
62-340

DOOR SCHEDULE

DR. NO.	SIZE	UNITS	DOORS TYPE	DOORS MATERIAL	DOORS GLASS	FRAMES ELEV.	FRAMES DETAILS	LOUVER ↔ OR UNDERCUT ↕	LINTELS	NAME PLATE	REMARKS	DR. NO.
B. 01	3'-0" x 6'-8" x 1 3/4"	SINGLE	A	H.M.	-	C	35/A-5		2-#5		C-LABEL	B. 01
101	2'-6" x 7'-10"	DBL	B	ALUM.	1/4" P.P.	A	2,3,4,5/A-5					101
102	2'-0" x 7'-10"	DBL	b	ALUM.	1/4" P.P.	A	3,4,5/A-5					102
103	3'-10" x 7'-10"	SINGLE	B	ALUM.		B	1, C/A-5					103
104	2'-6" x 7'-0" x 1 3/4"	DBL	A	H.M.		C	7, B/A-5	↔ FULL	2-#5 3-3x3x1/4 ∠ 2-#5 2-3x3x1/4 ∠		FILL LOUVER	104
105	2'-6" x 7'-0" x 1 3/4"	DBL	A	H.M.		C	7, B/A-5	↔ FULL	2-#5 6-3x3x1/4 ∠		FILL LOUVER	105
106	3'-0" x 7'-0" x 1 3/4"	SINGLE	A	H.M.		C	7, B/A-5					106
107	3'-0" x 7'-10"	SINGLE	B	ALUM.		D	1, C/A-5					107
108	3'-0" x 7'-0" x 1 3/4"	SINGLE	A	WOOD		C	9/A-5			PUBLIC HEALTH NURSE		108
109	3'-0" x 7'-0" x 1 3/4"	SINGLE	D	WOOD	WIRE GLASS	C	9/A-5					109
110	3'-0" x 7'-0" x 1 3/4"	SINGLE	A	WOOD		C	9/A-5			DIRECTOR OF NURSES		110
111	3'-0" x 7'-0" x 1 3/4"	SINGLE	A	WOOD		C	9/A-5					111
112	3'-0" x 7'-0" x 1 3/4"	SINGLE	A	WOOD		C	9/A-5					112
113	3'-0" x 7'-0" x 1 3/4"	SINGLE	A	WOOD		C	9/A-5			MEDICAL OFFICER IN CHARGE		113
114	3'-0" x 7'-0" x 1 3/4"	SINGLE	A	WOOD		C	9/A-5					114
115	3'-0" x 7'-0" x 1 3/4"	SINGLE	A	WOOD		C	9/A-5			SECRETARY		115
116	3'-0" x 7'-0" x 1 3/4"	SINGLE	A	WOOD		C	9/A-5			ASSISTANT ADMINISTRATOR		116
117	3'-0" x 7'-0" x 1 3/4"	SINGLE	A	WOOD		C	9/A-5					117
118	3'-0" x 7'-0" x 1 3/4"	SINGLE	D	WOOD	WIRE GLASS	C	9/A-5			FIELD HEALTH OFFICES		118
119	3'-0" x 7'-0" x 1 3/4"	SINGLE	A	WOOD		C	9/A-5	↔ 1"		SOILED LINEN		119
120	3'-0" x 7'-0" x 1 3/4"	SINGLE	A	WOOD		C	9/A-5			STORAGE		120
121	2'-6" x 7'-0" x 1 3/4"	DBL	A	H.M.		C	9/A-5			MECHANICAL EQUIP-SHOP	C LABEL	121
122	3'-0" x 7'-0" x 1 3/4"	SINGLE	A	WOOD		C	9/A-5			WOMENS LOUNGE		122
123	3'-0" x 7'-0" x 1 3/4"	SINGLE	A	WOOD		C	9/A-5	↔ 20"x12"				123
124	2'-0" x 7'-0" x 1 3/4"	SINGLE	A	WOOD		C	9/A-5					124
125	2'-6" x 7'-0" x 1 3/4"	SINGLE	A	WOOD		C	9/A-5	↔ 12"x12"				125
126	3'-0" x 7'-0" x 1 3/4"	SINGLE	D	WOOD	WIRE GLASS	C	9/A-5			CENTRAL LINEN		126
127	3'-0" x 7'-0" x 1 3/4"	SINGLE	D	WOOD	WIRE GLASS	C	9/A-5					127
128	2'-8" x 7'-0" x 1 3/4"	SINGLE	A	WOOD		C	9/A-5					128
129	3'-0" x 7'-0" x 1 3/4"	SINGLE	A	WOOD		C	9/A-5	↔ 1"		JANITOR		129
130	3'-0" x 7'-0" x 1 3/4"	SINGLE	A	WOOD		C	9/A-5			STORAGE		130
131	3'-0" x 7'-0" x 1 3/4"	SINGLE	A	WOOD		C	9/A-5			PATIENT CLOTHES		131
132	3'-0" x 7'-0" x 1 3/4"	SINGLE	A	WOOD		C	9/A-5			ITEMS LOCKER		132
133	2'-6" x 7'-0" x 1 3/4"	SINGLE	A	WOOD		C	9/A-5	↔ 12"x12"				133
134	2'-6" x 7'-0" x 1 3/4"	DBL	D	WOOD		C	34/A-5				C LABEL	134
135	3'-0" x 7'-0" x 1 3/4"	SINGLE	A	WOOD		C	9/A-5			EKG-BMR		135
136	3'-0" x 7'-0" x 1 3/4"	SINGLE	A	WOOD		C	9/A-5			LABORATORY		136
137	3'-0" x 7'-0" x 1 3/4"	SINGLE	A	WOOD		C	9/A-5					137
138	3'-0" x 7'-0" x 1 3/4"	SINGLE	A	WOOD		C	9/A-5	↔ 1"		SPECIMEN TOILET		138
139	3'-0" x 7'-0" x 1 3/4"	SINGLE	A	WOOD		C	9/A-5			BLOOD LETTING		139
140	3'-0" x 7'-0" x 1 3/4"	SINGLE	A	WOOD		C	9/A-5			STORAGE		140
141	3'-0" x 7'-0" x 1 3/4"	SINGLE	A	WOOD		C	9/A-5			STORAGE		141
142	3'-10" x 7'-0" x 1 3/4"	SINGLE	A	WOOD		C	9/A-5			X-RAY		142
143	3'-0" x 7'-0" x 1 3/4"	SINGLE	A	WOOD		C	9/A-5	↔ 1"		TOILET		143
144	3'-10" x 7'-0" x 1 3/4"	SINGLE	A	WOOD		C	10/A-5			X-RAY - NO ADMITTANCE	LEAD PROTECTION	144
145	2'-0" x 7'-0" x 1 3/4"	SINGLE	A	WOOD		C	9/A-5	↔ 12" x 12" LIGHT PROOF		DARK ROOM - NO ADMITTANCE		145
146	3'-0" x 7'-0" x 1 3/4"	SINGLE	A	WOOD		C	10/A-5			OFFICE & VIEWING	LEAD PROTECTION	146
147	2'-6" x 7'-0" x 1 3/4"	SINGLE	A	WOOD		C	9/A-5			FILM STORAGE		147
148	3'-0" x 7'-0" x 1 3/4"	SINGLE	A	WOOD		C	9/A-5			OFFICE		148
149	2'-10" x 7'-0" x 1 3/4"	SINGLE	A	WOOD		C	9/A-5	↔ 1"		JANITOR		149
150	2'-8" x 7'-0" x 1 3/4"	DBL	D	WOOD	WIRE GLASS	C	34/A-5				C-LABEL	150
151	3'-0" x 7'-0" x 1 3/4"	SINGLE	A	WOOD		C	9/A-5	↔ 1"		TOILET		151
152	2'-6" x 7'-0" x 1 3/4"	DBL	C	WOOD	WIRE GLASS	C	9/A-5			EMERGENCY - NO ADMITTANCE	DOUBLE ACTING	152
153	2'-0" x 7'-0" x 1 3/4"	DBL	A	WOOD		C	9/A-5					153
154	3'-0" x 7'-0" x 1 3/4"	SINGLE	A	WOOD		C	9/A-5					154
155	3'-0" x 7'-0" x 1 3/4"	SINGLE	A	WOOD		C	9/A-5			STORAGE		155
156	2'-6" x 7'-0" x 1 3/4"	DBL	A	WOOD		C	9/A-5			LINEN		156
157	3'-0" x 7'-0" x 1 3/4"	SINGLE	D	WOOD	WIRE GLASS	C	9/A-5	↔ 1"		UTILITY		157
158	3'-0" x 7'-0" x 1 3/4"	SINGLE	A	WOOD		C	9/A-5			OFFICE - EXAMINATION NO 1		158
159	2'-8" x 7'-0"	SINGLE	G	WOOD		-	14/A-5					159
160	3'-0" x 7'-0" x 1 3/4"	SINGLE	D	WOOD	WIRE GLASS	C	9/A-5			NURSE WORK ROOM		160
161	3'-0" x 7'-0" x 1 3/4"	SINGLE	A	WOOD		C	9/A-5			EXAMINATION NO 2		161
162	2'-8" x 7'-0"	SINGLE	G	WOOD		-	14/A-5					162
163	3'-0" x 7'-0" x 1 3/4"	SINGLE	A	WOOD		C	9/A-5			PHARMACY		163
164	3'-0" x 7'-0" x 1 3/4"	SINGLE	A	WOOD		C	9/A-5			MEDICAL RECORDS		164
165	3'-0" x 7'-0" x 1 3/4"	SINGLE	A	WOOD		C	9/A-5					165
166	2'-8" x 7'-0" x 1 3/4"	DBL	D	WOOD	WIRE GLASS	C	34/A-5			DIAGNOSTIC AREA		166
167	3'-8" x 7'-0" x 1 3/4"	SINGLE	C	WOOD	WIRE GLASS	C	12, 13/A-5		2-#5	STAIR	B-LABEL-1 1/2 HOUR	167
168	3'-0" x 7'-0" x 1 3/4"	SINGLE	A	WOOD		C	15/A-5			STORAGE		168
169	2'-4" x 7'-0" x 1 3/4"	SINGLE	A	WOOD		C	9/A-5	↔ 1"		MEN		169
170	2'-4" x 7'-0" x 1 3/4"	SINGLE	A	WOOD		C	9/A-5	↔ 1"		WOMEN		170
171	3'-0" x 7'-0" x 1 3/4"	SINGLE	D	WOOD	WIRE GLASS	C	9,11/A-5			FIELD HEALTH OFFICES	C-LABEL	171
172	3'-0" x 7'-0" x 1 3/4"	SINGLE	A	WOOD		C	9/A-5			STORAGE		172
173	2'-4" x 7'-0" x 1 3/4"	SINGLE	A	WOOD		C	9/A-5	↔ 1"		MEN STAFF		173
174	2'-4" x 7'-0" x 1 3/4"	SINGLE	A	WOOD		C	9/A-5	↔ 1"		WOMEN STAFF		174
175	3'-0" x 7'-0" x 1 3/4"	SINGLE	A	WOOD		C	9,11/A-5			CONFERENCE - LIBRARY	C-LABEL	175
176	3'-0" x 7'-0" x 1 3/4"	SINGLE	D	WOOD		C	9,11/A-5			DENTAL CLINIC	C-LABEL	176
177	3'-0" x 7'-0" x 1 3/4"	SINGLE	A	WOOD		C	9/A-5			OFFICE		177
178	3'-0" x 7'-0" x 1 3/4"	SINGLE	A	WOOD		C	10/A-5				LEAD PROTECTION	178
179	3'-0" x 7'-0" x 1 3/4"	SINGLE	A	WOOD		C	10/A-5			DENTAL CLINIC	LEAD PROTECTION	179
180	2'-0" x 7'-0" x 1 3/4"	SINGLE	A	WOOD		C	10/A-5	↔ 12"x12" LIGHT PROOF-LEAD LINED		DARK ROOM - NO ADMITTANCE	LEAD PROTECTION	180
181	2'-0" x 7'-0" x 1 3/4"	SINGLE	A	WOOD		C	9/A-5	↔ 1"		JANITOR		181
182	3'-0" x 7'-0" x 1 3/4"	SINGLE	A	WOOD		C	9/A-5			DENTAL STORAGE		182
183	3'-0" x 7'-0" x 1 3/4"	SINGLE	A	WOOD		C	9/A-5			CONFERENCE - LIBRARY		183
184	3'-0" x 7'-0" x 1 3/4"	SINGLE	A	WOOD		C	9/A-5			SANITATION ENGINEER		184
185	3'-0" x 7'-0" x 1 3/4"	SINGLE	A	WOOD		C	9/A-5					185
186	3'-0" x 7'-0" x 1 3/4"	SINGLE	A	WOOD		C	9/A-5			HEALTH EDUCATION OFFICER		186
187	3'-0" x 7'-0" x 1 3/4"	SINGLE	A	WOOD		C	9/A-5			FIELD HEALTH SECRETARY		187
188	3'-0" x 7'-0" x 1 3/4"	SINGLE	A	WOOD		C	9/A-5			MEDICAL SOCIAL WORKER		188
189	3'-0" x 7'-0" x 1 3/4"	SINGLE	A	WOOD		C	9/A-5			ADMITTING		189
190	2'-6" x 7'-0" x 1 3/4"	SINGLE	C	WOOD		C	10/A-5	↔ 12"x12" LEAD LINED		CONTROL	LEAD PROTECTION - 10"x10" LEAD GLASS VIEW WINDOW	190
CONSTRUCTION ALTERNATE B												
191	10'-0" x 8'-8"	SINGLE	I	WOOD	-	-	19,20/A-5		2-#5 L 4x4x3/8"			191
201	3'-10" x 7'-0" x 1 3/4"	SINGLE	B	ALUM.		B	1, C/A-5					201
202	3'-4" x 7'-0" x 1 3/4"	SINGLE	A	H.M.		C	16, 17/A-5			KITCHEN		202
203	3'-0" x 7'-0" x 1 3/4"	SINGLE	A	H.M.		C	16, 17, 18/A-5			ANESTHESIA		203
204	3'-0" x 7'-0" x 1 3/4"	SINGLE	A	H.M.		C	16, 17, 18/A-5			OXYGEN		204
205	3'-0" x 7'-0" x 1 3/4"	SINGLE	A	H.M.		C	16, 17, 18/A-5			TRASH		205
206	3'-0" x 7'-0" x 1 3/4"	SINGLE	A	WOOD		C	9, 12/A-5	↔ 24"x21"		BULK FOOD STORAGE		206
207	2'-6" x 7'-0" x 1 3/4"	SINGLE	A	WOOD		C	9/A-5			JANITOR		207
208	2'-6" x 7'-0" x 1 3/4"	SINGLE	A	WOOD		C	9/A-5			TOILET		208


DOOR SCHEDULE

DR. NO.	SIZE	UNITS	DOORS TYPE	DOORS MATERIAL	DOORS GLASS	FRAMES ELEV.	FRAMES DETAILS	LOUVER ↔ OR UNDERCUT ↕	LINTELS	NAME PLATE	REMARKS	DR. NO.
209	3'-4" x 7'-0" x 1 3/4"	SINGLE	F	H.M.		C	9/A-5					209
210	3'-0" x 7'-0" x 1 3/4"	SINGLE	A	WOOD		C	9/A-5	↔ 18"x12"				210
211	3'-0" x 7'-0" x 1 3/4"	SINGLE	A	WOOD		C	9/A-5			DINING		211
212	3'-0" x 7'-0" x 1 3/4"	SINGLE	H	WOOD	WIRE GLASS	C	9/A-5			DISHWASH	DOUBLE ACTING	212
213	2'-6" x 7'-0" x 1 3/4"	DBL	H	WOOD	WIRE GLASS	C	9,11/A-5			DIETARY AREA	DOUBLE ACTING C-LABEL	213
214	3'-0" x 7'-0" x 1 3/4"	SINGLE	D	WOOD	WIRE GLASS	C	9/A-5			FORMULA		214
215	3'-0" x 7'-0" x 1 3/4"	SINGLE	D	WOOD	WIRE GLASS	C	9/A-5			CLEAN FORMULA		215
216	3'-10" x 7'-0" x 1 3/4"	SINGLE	A	WOOD		C	9/A-5			TREATMENT		216
217	3'-0" x 7'-0" x 1 3/4"	SINGLE	D	WOOD	WIRE GLASS	C	9/A-5	↔ 1"		FLOOR KITCHEN		217
218	3'-0" x 7'-0" x 1 3/4"	SINGLE	A	WOOD		C	9/A-5			STORAGE		218
219	3'-0" x 7'-0" x 1 3/4"	SINGLE	A	WOOD		C	9/A-5			TREATMENT		219
220	2'-6" x 7'-0" x 1 3/4"	SINGLE	A	WOOD		C	9/A-5	↔ 1"		PUBLIC TOILET		220
221	3'-0" x 7'-0" x 1 3/4"	SINGLE	A	WOOD		C	9/A-5			SOILED WASH		221
222	2'-6" x 7'-0" x 1 3/4"	SINGLE	A	WOOD		C	9/A-5			JANITOR		222
223	3'-0" x 7'-0" x 1 3/4"	SINGLE	D	WOOD	WIRE GLASS	C	9/A-5			CENTRAL STERILIZING		223
224	2'-0" x 7'-0" x 1 3/4"	SINGLE	A	WOOD		C	9/A-5					224
225	3'-0" x 7'-0" x 1 3/4"	SINGLE	E	WOOD		C	9/A-5			CENTRAL STERILIZING	DITCH DOOR (A-4)	225
226	3'-0" x 7'-0" x 1 3/4"	SINGLE	A	WOOD		C	9/A-5	↔ 12"x12"				226
227	3'-0" x 7'-0" x 1 3/4"	SINGLE	A	WOOD		C	9/A-5	↔ 1"				227
228	3'-10" x 7'-0" x 1 3/4"	SINGLE	A	WOOD		C	9/A-5					228
229	3'-0" x 7'-0" x 1 3/4"	SINGLE	A	WOOD		C	9/A-5	↔ 1"				229
230	3'-10" x 7'-0" x 1 3/4"	SINGLE	A	WOOD		C	9/A-5					230
231	3'-0" x 7'-0" x 1 3/4"	SINGLE	A	WOOD		C	9/A-5	↔ 1"				231
232	3'-0" x 7'-0" x 1 3/4"	SINGLE	A	WOOD		C	9/A-5	↔ 1"		BATH	DOUBLE ACTING	232
233	3'-10" x 7'-0" x 1 3/4"	SINGLE	A	WOOD		C	9/A-5					233
234	3'-0" x 7'-0" x 1 3/4"	SINGLE	A	WOOD		C	9/A-5	↔ 1"			DOUBLE ACTING	234
235	3'-10" x 7'-0" x 1 3/4"	SINGLE	A	WOOD		C	9/A-5					235
236	3'-0" x 7'-0" x 1 3/4"	SINGLE	A	WOOD		C	9/A-5	↔ 1"				236
237	3'-0" x 7'-0" x 1 3/4"	SINGLE	A	WOOD		C	9/A-5	↔ 1"				237
238	3'-10" x 7'-0" x 1 3/4"	SINGLE	A	WOOD		C	9/A-5					238
239	3'-0" x 7'-0" x 1 3/4"	SINGLE	A	WOOD		C	9/A-5	↔ 1"				239
240	3'-0" x 7'-0" x 1 3/4"	SINGLE	D	WOOD	WIRE GLASS	C	9/A-5			SOILED UTILITY		240
241	3'-0" x 7'-0" x 1 3/4"	SINGLE	D	WOOD	WIRE GLASS	C	9/A-5			CLEAN UTILITY		241
242	3'-10" x 7'-0" x 1 3/4"	SINGLE	C	WOOD		C	9/A-5			ISOLATION		242
243	3'-10" x 7'-0" x 1 3/4"	SINGLE	C	WOOD		C	7/A-5					243
244	3'-0" x 7'-0" x 1 3/4"	SINGLE	A	WOOD		C	9/A-5					244
245	2'-0" x 7'-0" x 1 3/4"	DBL	A	WOOD		C	9/A-5			CLEAN LINEN		245
246	2'-6" x 7'-0" x 1 3/4"	SINGLE	D	WOOD	WIRE GLASS	C	9/A-5	↔ 1"		MEDICINE PREPARATION		246
247	3'-0" x 7'-0" x 1 3/4"	SINGLE	A	WOOD		C	7/A-5			SOILED LINEN		247
248	3'-8" x 7'-0" x 1 3/4"	SINGLE	C	WOOD	WIRE GLASS	C	12, 13/A-5		2-#5	STAIR	B-LABEL-1 1/2 HOUR	248
249	3'-6" x 7'-0" x 1 3/4"	DBL	D	WOOD	WIRE GLASS	C	34/A-5			OBSTETRICS AREA	C-LABEL	249
250	3'-0" x 7'-0" x 1 3/4"	SINGLE	D	WOOD	WIRE GLASS	C	9,11/A-5			NURSERY - NO ADMITTANCE	C-LABEL	250
251	3'-8" x 7'-0" x 1 3/4"	SINGLE	D	WOOD	WIRE GLASS	C	9/A-5					251
252	3'-0" x 7'-0" x 1 3/4"	SINGLE	D	WOOD	WIRE GLASS	C	7/A-5					252
253	3'-0" x 7'-0" x 1 3/4"	SINGLE	D	WOOD	WIRE GLASS	C	9/A-5					253
254	3'-10" x 7'-0" x 1 3/4"	SINGLE	A	WOOD		C	7/A-5					254
255	3'-0" x 7'-0" x 1 3/4"	SINGLE	A	WOOD		C	9/A-5	↔ 1"				255
256	3'-0" x 7'-0" x 1 3/4"	SINGLE	D	WOOD	WIRE GLASS	C	9/A-5			UTILITY		256
257	2'-8" x 7'-0" x 1 3/4"	SINGLE	A	WOOD		C	9/A-5			SHOWER	DOUBLE ACTING	257
258	2'-6" x 7'-0" x 1 3/4"	SINGLE	A	WOOD		C	9/A-5			STORAGE		258
259	3'-0" x 7'-0" x 1 3/4"	SINGLE	A	WOOD		C	9/A-5			LINEN		259
260	3'-10" x 7'-0" x 1 3/4"	SINGLE	A	WOOD		C	7/A-5					260
261	3'-0" x 7'-0" x 1 3/4"	SINGLE	A	WOOD		C	9/A-5	↔ 1"				261
262	2'-6" x 7'-0" x 1 3/4"	DBL	C	WOOD	WIRE GLASS	C	9/A-5			DELIVERY AREA - NO ADMITTANCE		262
263	2'-6" x 7'-0" x 1 3/4"	SINGLE	A	WOOD		C	9/A-5			DOCTORS		263
264	2'-6" x 7'-0" x 1 3/4"	SINGLE	A	WOOD		C	9/A-5			DOCTORS		264
265	2'-6" x 7'-0" x 1 3/4"	SINGLE	A	WOOD		C	9/A-5					265
266	2'-0" x 7'-0" x 1 3/4"	SINGLE	A	WOOD		C	9/A-5			STORAGE		266
267	2'-6" x 7'-0" x 1 3/4"	SINGLE	A	WOOD		C	7/A-5	↔ 1"		JANITOR		267
268	3'-0" x 7'-0" x 1 3/4"	SINGLE	D	WOOD	WIRE GLASS	C	9/A-5			CLEAN UP		268
269	2'-8" x 7'-0" x 1 3/4"	SINGLE	D	WOOD	WIRE GLASS	C	9/A-5			SUB STERILIZATION		269
270	2'-6" x 7'-0" x 1 3/4"	DBL	C	WOOD	WIRE GLASS	C	9/A-5			DELIVERY ROOM		270
271	2'-6" x 7'-0" x 1 3/4"	SINGLE	A	WOOD		C	9/A-5			NURSES		271
272	2'-0" x 1'-0" x 1 3/4"	SINGLE	A	WOOD		C	9/A-5			NURSES		272
273	2'-6" x 7'-0" x 1 3/4"	SINGLE	A	WOOD		C	9/A-5	↔ 20"x12"				273
												274
P-1	3'-0" x 7'-0" x 1 3/4"	SINGLE	A	H.M.		C	12, 13/A-5		2-#5		B-LABEL-1 1/2 HOUR	P-1
P-2	3'-0" x 7'-0" x 1 3/4"	SINGLE	A	H.M.		C	12, 13/A-5		2-#5		B-LABEL-1 1/2 HOUR	P-2

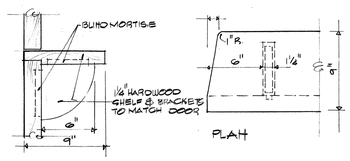

SECTION

DUTCH DOOR DETAILS (1 / A-4) 1 1/2" = 1'-0"

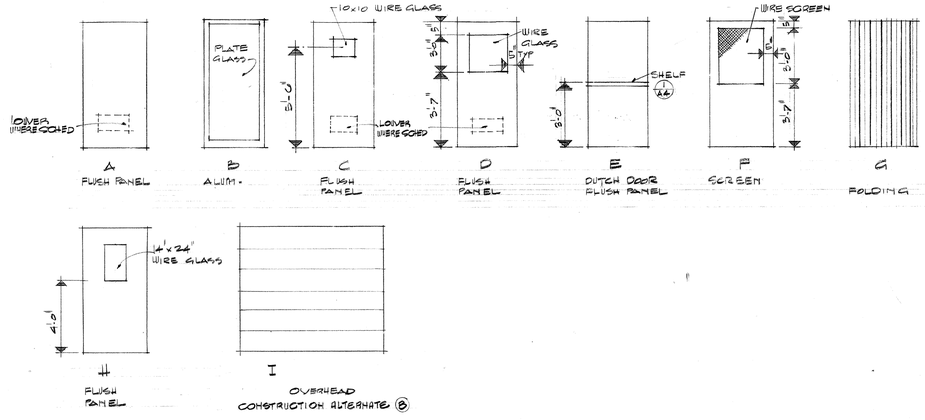

REVISION	DATE	BRIEF	BY

DEPARTMENT OF THE INTERIOR
BUREAU OF INDIAN AFFAIRS
BRANCH OF PLANT DESIGN AND CONSTRUCTION
ALBUQUERQUE, NEW MEXICO
RALPH W. MIZE, CHIEF

MESCALERO HOSPITAL
MESCALERO, NEW MEXICO

PROJECT NO: K56-PH 80

DEPARTMENT OF HEALTH EDUCATION AND WELFARE
PUBLIC HEALTH SERVICE
BUREAU OF MEDICAL SERVICES
DIVISION OF INDIAN HEALTH
WASHINGTON 25, D. C.

SHEET NO: A-4 OF 15 SHEETS

PREPARED BY	TRACED BY	CHECKED BY	DATE
R.C.	T.P.	D.P.S.	5/8/67

DOOR SCHEDULE & TYPES

DRAWING NO: J-1071

FERGUSON STEVENS MALLORY & PEARL
ARCHITECTS ENGINEERS
ALBUQUERQUE NEW MEXICO