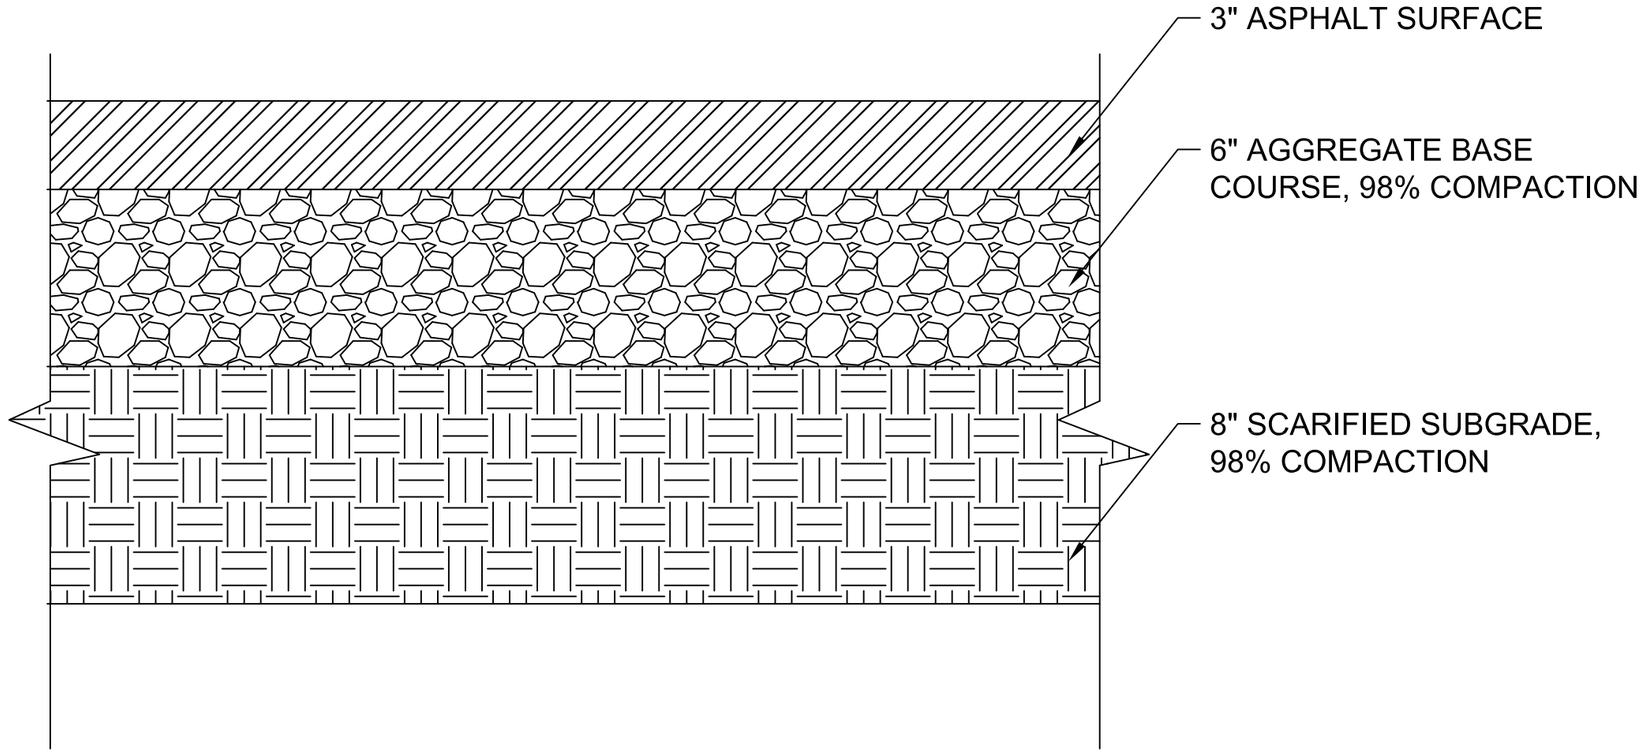


ASPHALT PAVING SECTION

UNITED STATES DEPARTMENT OF THE INTERIOR
U.S. FISH AND WILDLIFE SERVICE
DIVISION OF ENGINEERING

UVALDE NATIONAL FISH HATCHERY

UVALDE COUNTY TEXAS

ASPLALT REPAIRS HOLDING HOUSE & ADMIN

DETAILS

DESIGN: JOHNS	DRAWN: JOHNS	CHECK: DUNCAN
DRAWING FILENAME AND NUMBER ASPHALT_UVALDE2019 2F-TEX-184-49.0		DATE: 5/23/19 SHT. NO. 5 / SEQ. NO. 5 OF 5