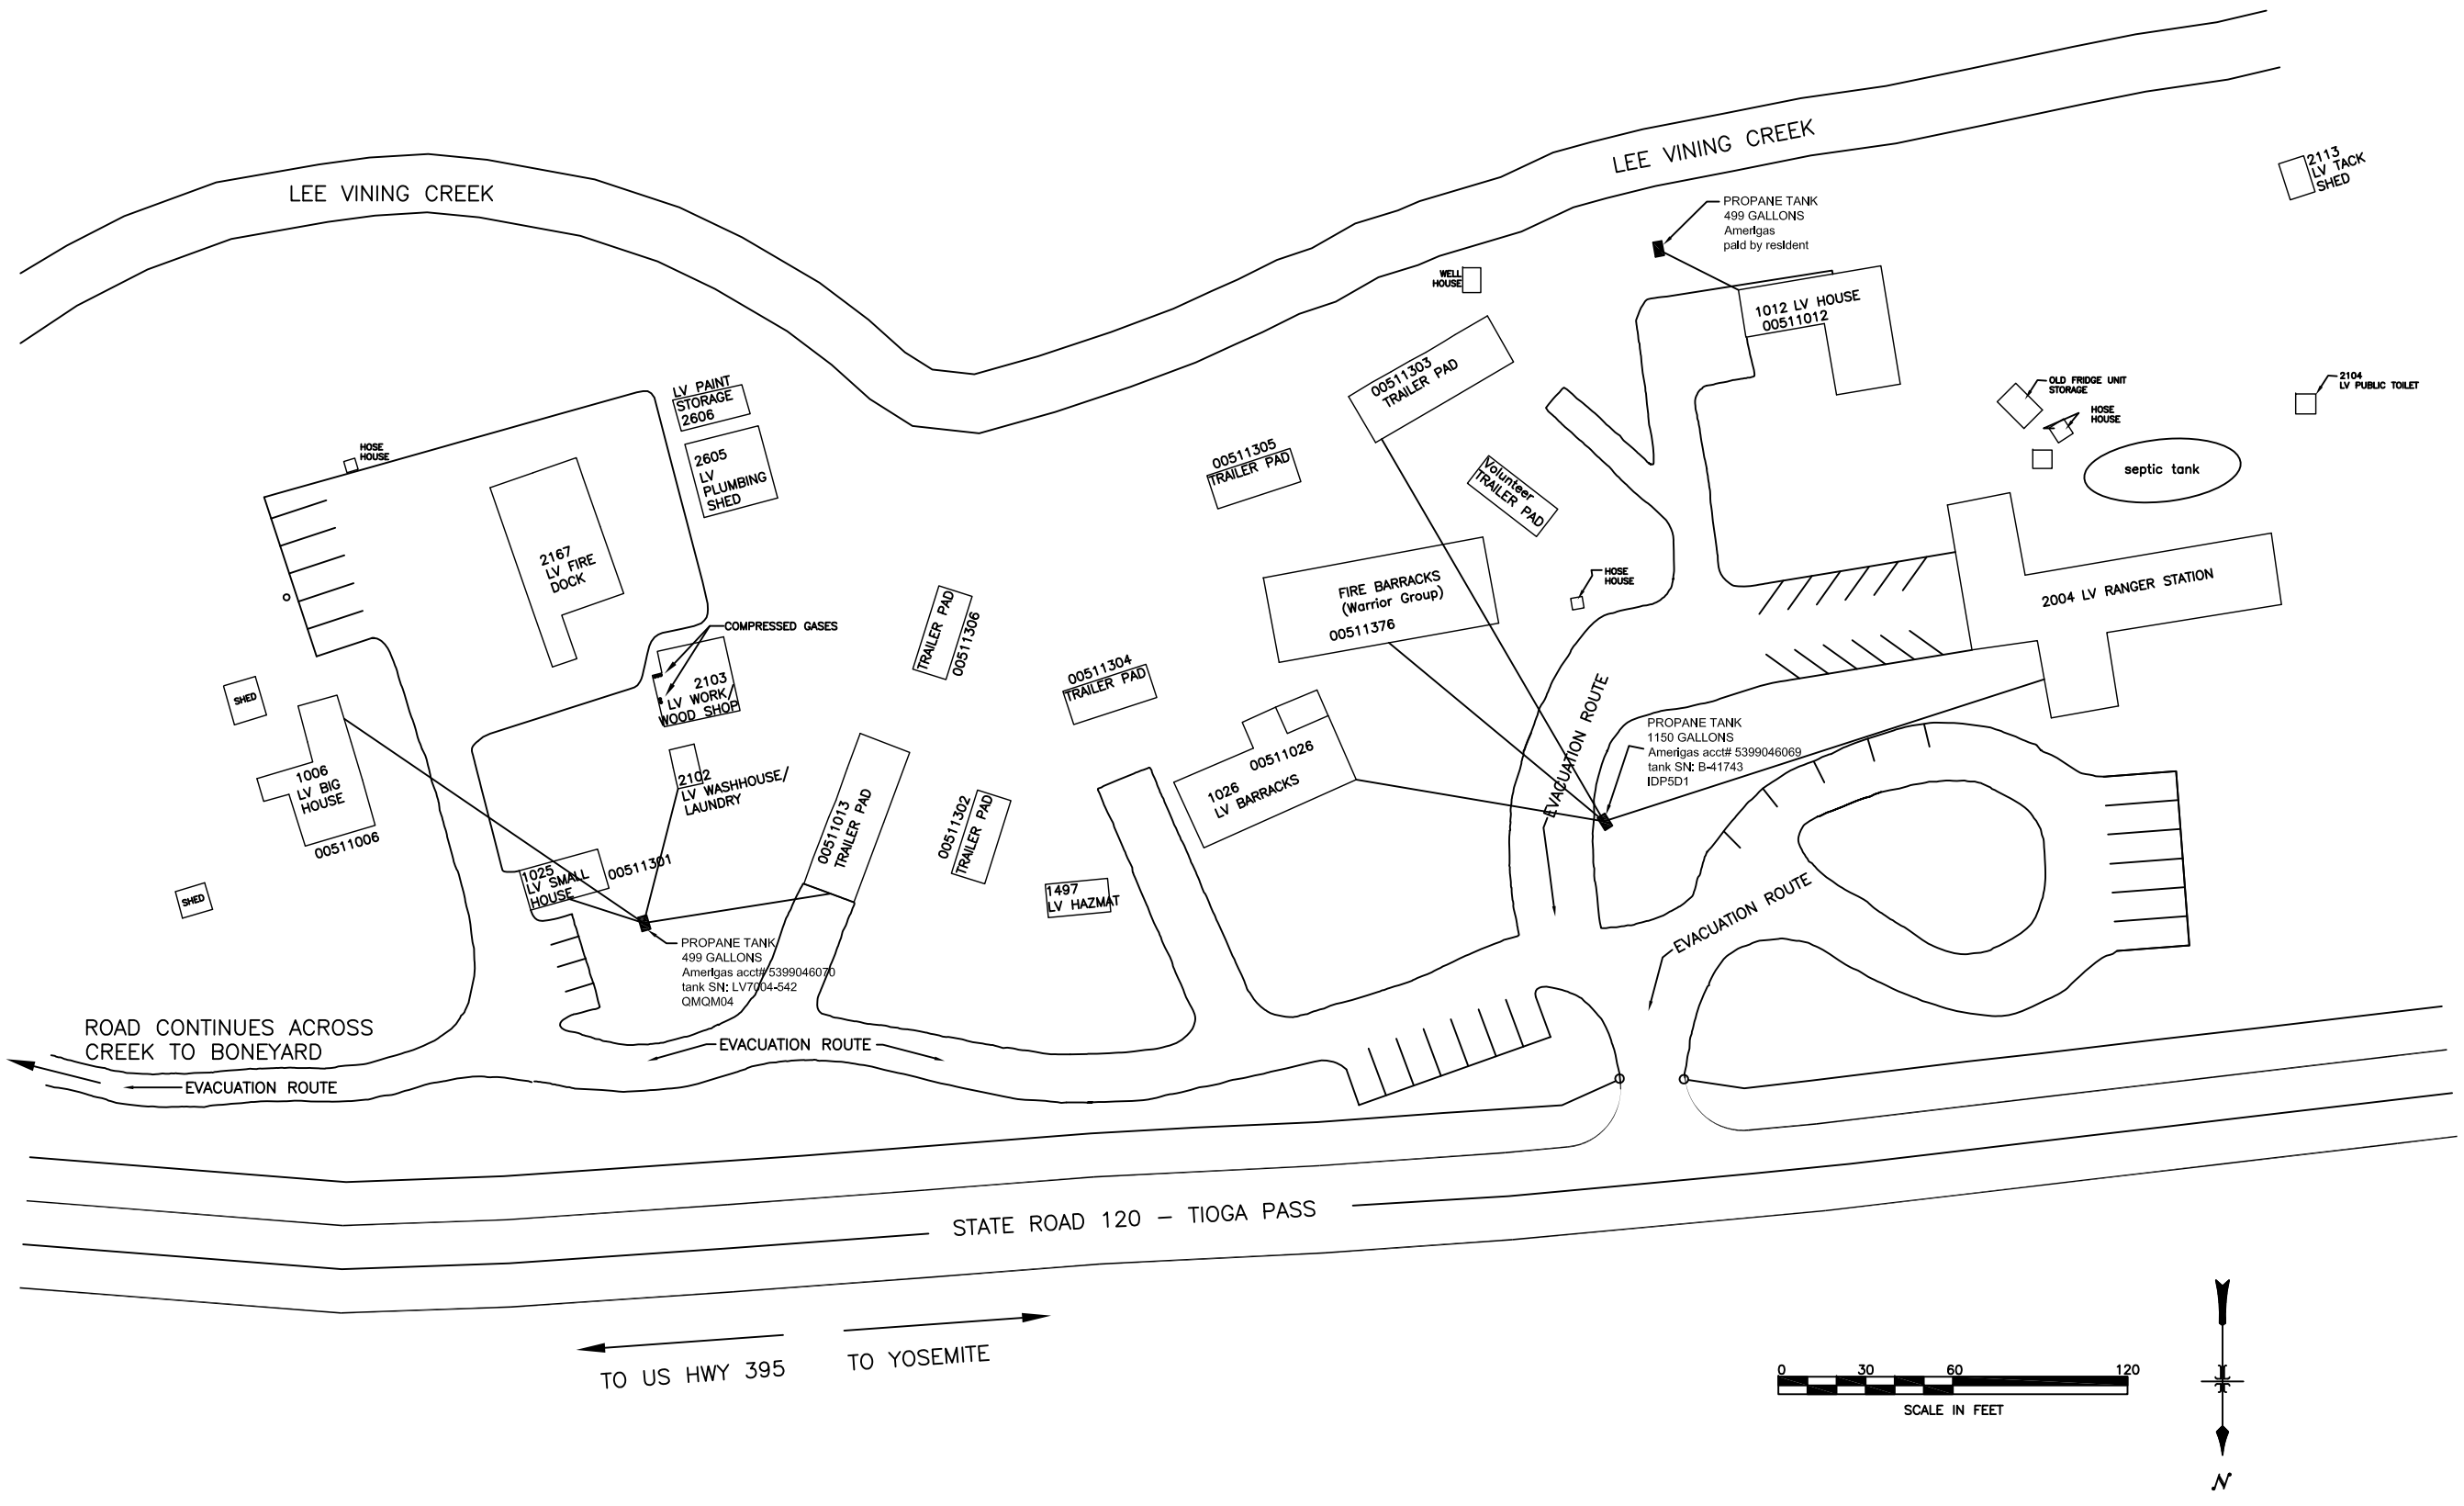


USFS-(11x17).dwg

USDA FOREST SERVICE

PACIFIC SOUTHWEST REGION R5

NO.	DATE
1	03/18/2012
2	06/13/2014
3	04/01/2015

FOREST: INYO NATIONAL FOREST

PROJECT NAME: LEE VINING RANGER STATION

DRAWING NAME: UTILITY SITE PLAN

INYO NATIONAL FOREST

MONO LAKE RANGER DISTRICT

PROJECT NO: --

DESIGNED BY: --

CHECKED BY: --

DRAWN BY: NG

SCALE: 1:60

DATE: 05/18/2010

DRAWING

SHEET 1 OF 1