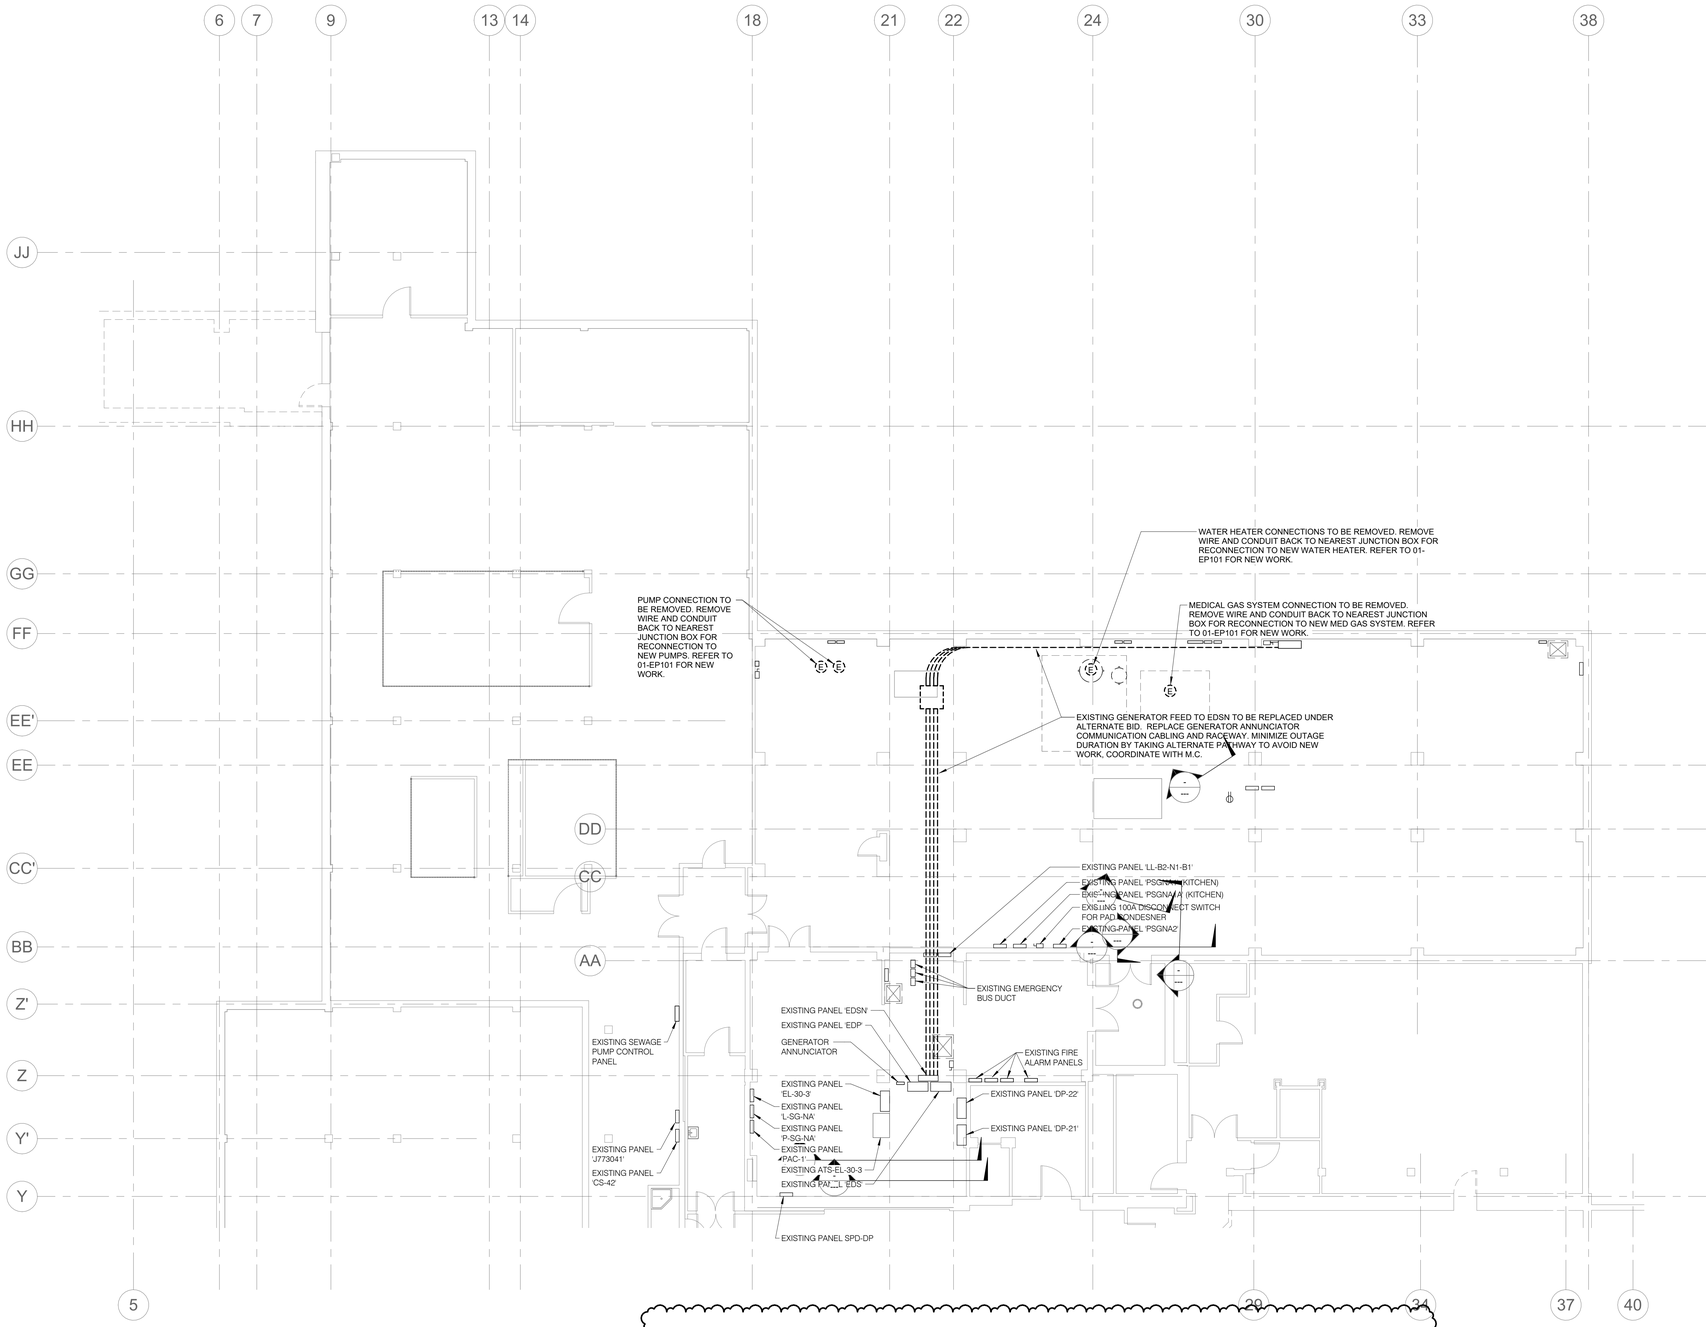


F4 DEMOLITION PLAN - SUB-BASEMENT 01 - POWER - OPTION BID 0005

1/8" = 1'-0"

BIDDING RFIS	09/23/2026
Revisions:	Date:

CONSTRUCTION AGENT

US Army Corps of Engineers ®

New England District

CONSULTANT

IMEG
The FUTURE. Built Smarter www.imegcorp.com
15 SUNNEN DRIVE
SUITE 104
ST. LOUIS, MO 63143
P: 314.645.1132 F: 314.645.1173
PROJECT #22000669.04

DESIGNER OF RECORD

A/E:
LEO A DALY JOINT VENTURE | Perkins&Will

STAMP

Office of Construction and Facilities Management

VA | U.S. Department of Veterans Affairs

Drawing Title
DEMOLITION PLAN - SUB-BASEMENT 01 - POWER - OPTION BID 0005

Approved:

Phase
READY TO ADVERTISE

FULLY SPRINKLERED

Project Title
CHILLED WATER PLANT REPLACEMENT AND SITE UTILITY IMPROVEMENTS PHASE A2

Location
950 Campbell Avenue,
West Haven, CT 06516

Issue Date	Checked	Drawn
2026-07-31	JEFMAN	CHABLO

Project Number
689-040


Building Number
01

Drawing Number
01-ED101

Autodesk Docs://1001-10210-001_Phase_A2/689_040_VAWH-BLDG-01_ET.rvt

10/8/2026 3:38:45 PM

VA FORM 08 - 6231

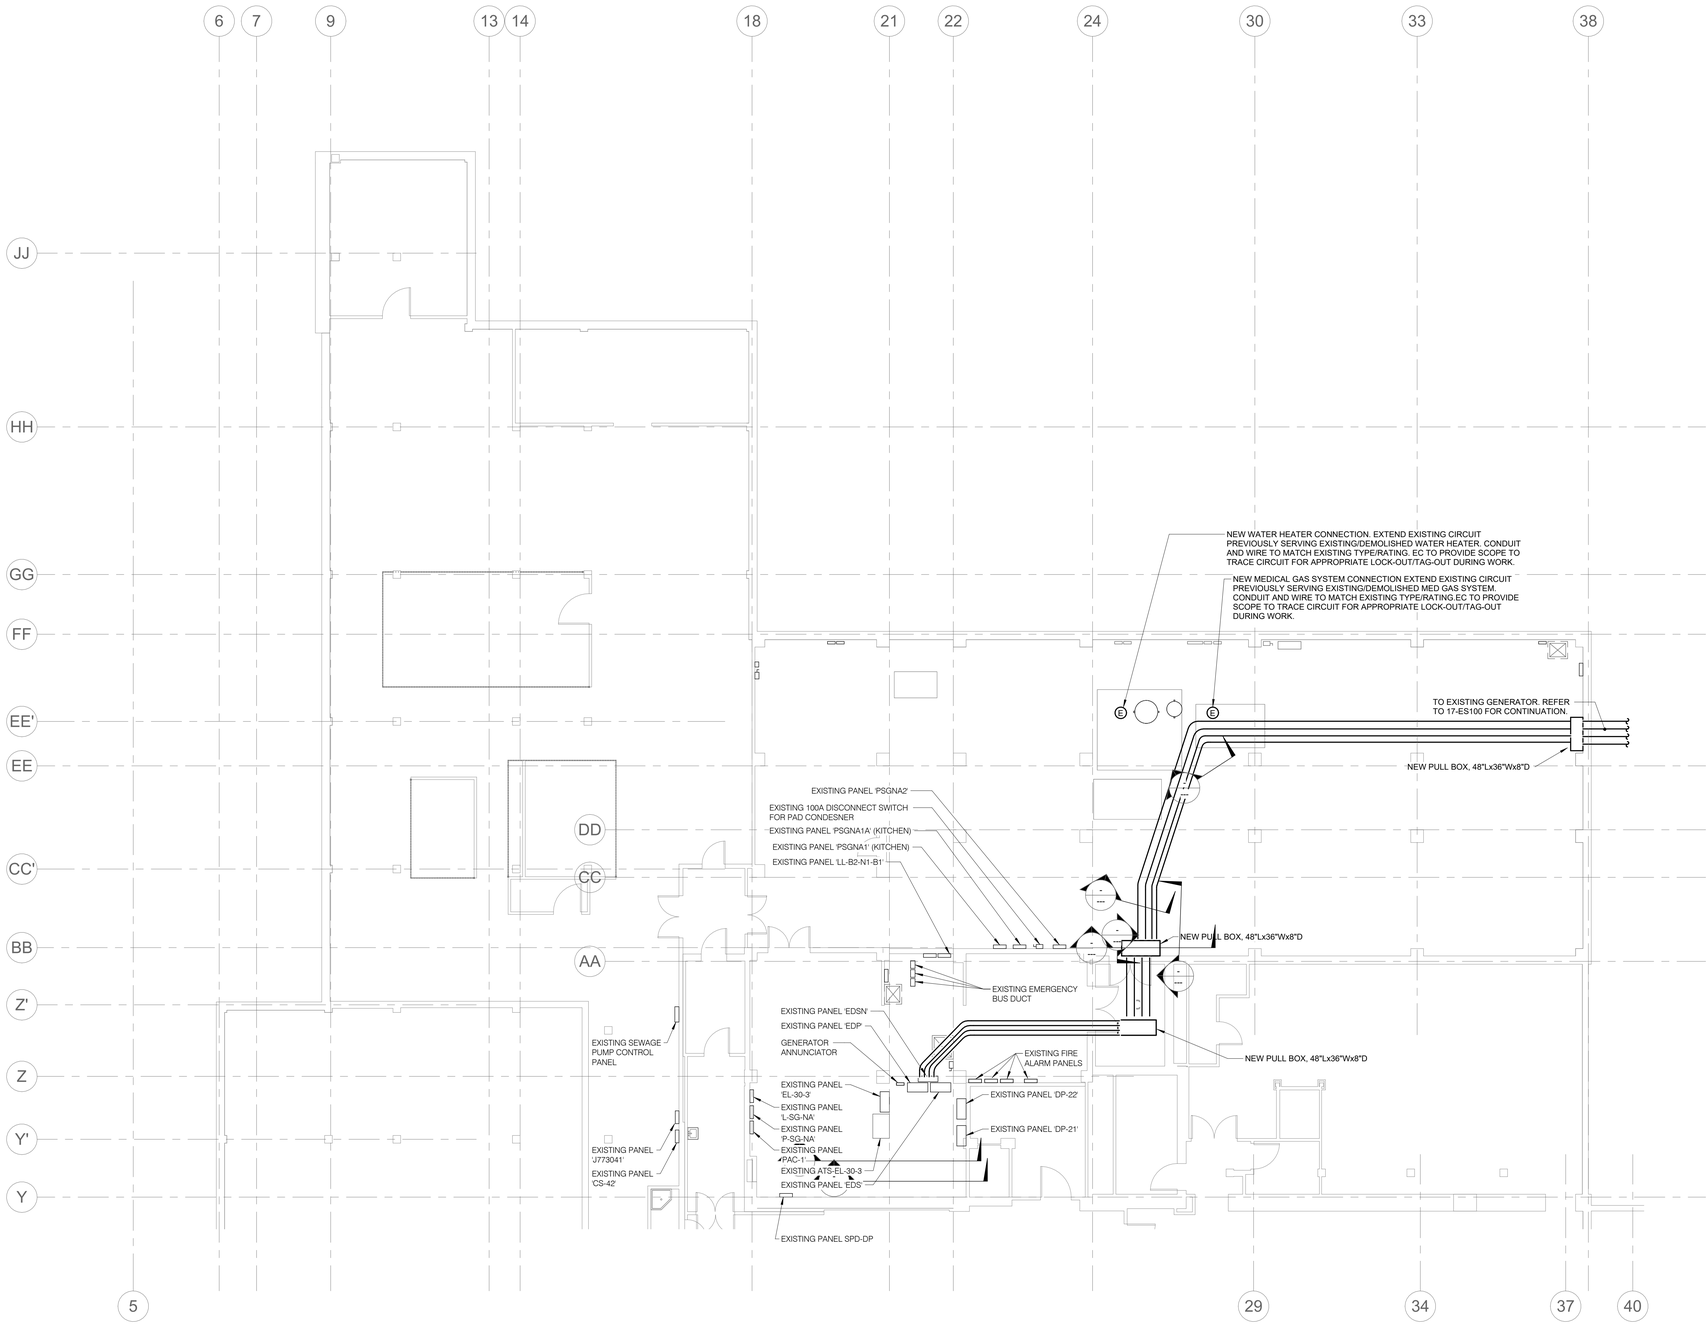

F4 FLOOR PLAN - SUB-BASEMENT 01 - POWER - OPTION BID 0005

1/8" = 1'-0"

BIDDING RFIS	09/23/2026
Revisions:	Date:

CONSTRUCTION AGENT

US Army Corps of Engineers ®

New England District

CONSULTANT

IMEG
The FUTURE. Built Smarter www.imegcorp.com
15 SUNNEN DRIVE
SUITE 104
ST. LOUIS, MO 63143
P: 314.645.1132 F: 314.645.1173
PROJECT #22000669.04

DESIGNER OF RECORD

A/E:
LEO A DALY JOINT VENTURE | Perkins&Will

STAMP

Office of Construction and Facilities Management

VA U.S. Department of Veterans Affairs

Drawing Title
FLOOR PLAN - SUB-BASEMENT 01 - POWER - OPTION BID 0005

Approved:

Phase
READY TO ADVERTISE

FULLY SPRINKLERED

Project Title
CHILLED WATER PLANT REPLACEMENT AND SITE UTILITY IMPROVEMENTS PHASE A2

Location
950 Campbell Avenue,
West Haven, CT 06516

Issue Date 2026-07-31
Checked JEFMAN
Drawn CHABLO

Project Number 689-040
Building Number 01
Drawing Number 01-EP101

Autodesk Docs://001-10210-001_Phase_A2/689_040_VAWH-BLDG-01_ET.rvt
10/8/2026 3:38:45 PM

VA FORM 08 - 6231