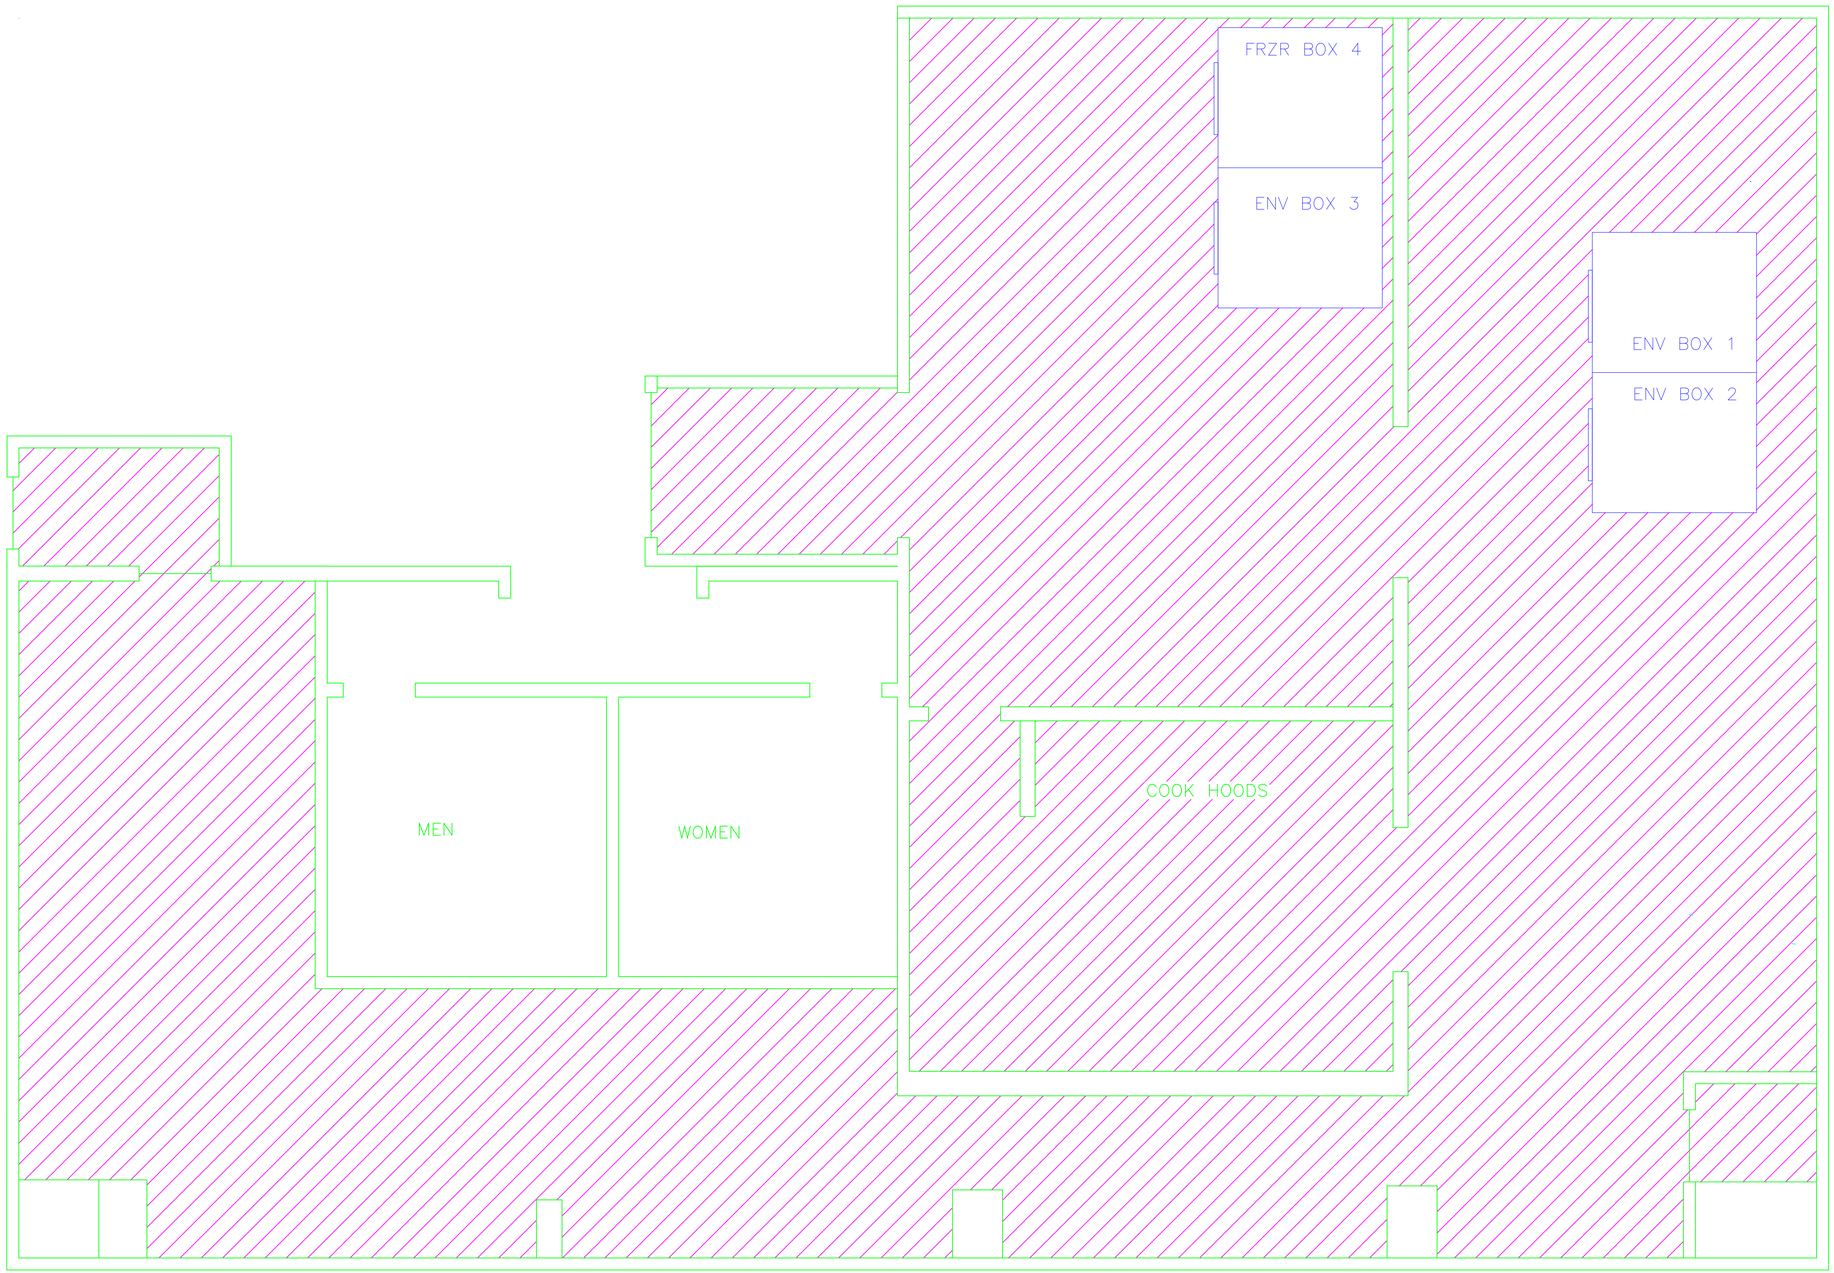

GENERAL NOTES

1. This drawing repairs and recoats Chemical resistant resinous coated concrete flooring in the Mechanical Services Building (MSB), second floor laboratory at Eastern Regional Research Center, 600 East Mermaid Lane, Wyndmoor Pa, 19454.
2. Areas shown thusly including existing cove base shall be repaired and recoated.
3. Areas shall be prepped for new material in accordance with manufacturers recommendations.
4. Treat cracks, control joints and expansion joints.
5. Apply base coat of pure epoxy and finish coat of chemical resistant polyaspartic including a texturing additive providing and non–skid surface.
6. The laboratory is use for biological work. Finishes must meet cleanroom requirements and be compatible with chlorinated cleaning solutions.

U.S. DEPARTMENT OF AGRICULTURE
AGRICULTURAL RESEARCH SERVICE
EASTERN REGIONAL RESEARCH CENTER
WYNDMOOR, PA. 19118

MSB FLOOR COATING REPAIRS
SECOND FLOOR PLAN VIEW

FACILITIES ENGINEERING

APPROVED	DRAWN GOLDBERG	DATE 08/10/2026
	CHECKED	
	SCALE	

REVISIONS

NO.	DATE	APPROVED