

DINO PMIS NO.: 310333

STATE	PROJECT	SHEET NUMBER
UT	FTNP DINO 10(3) & 100(2) GREEN RIVER RD & QUARRY ACCESS RD	T27

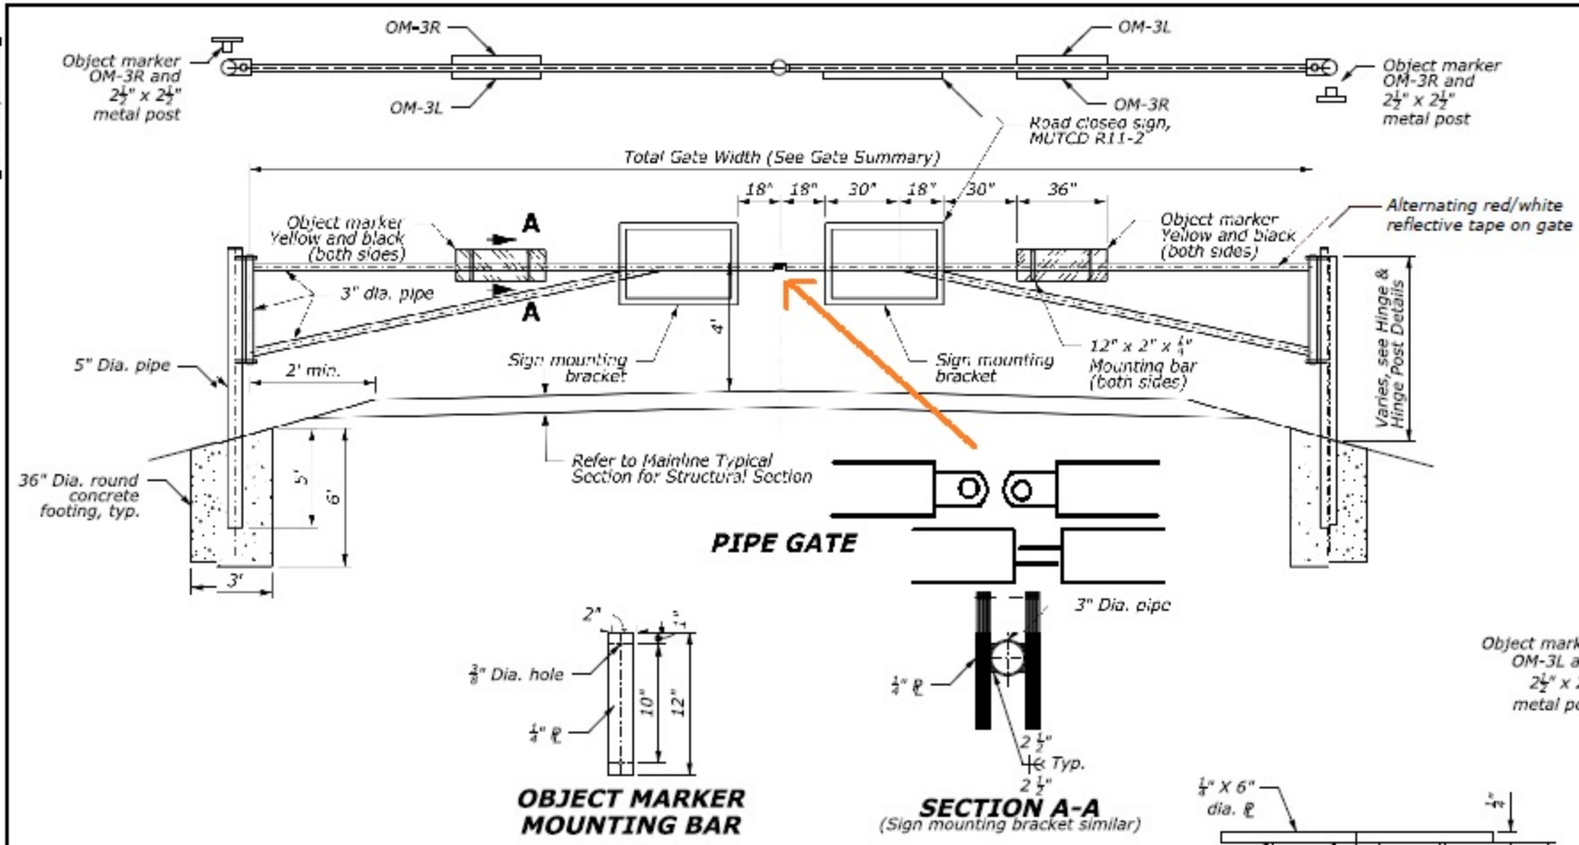


OBJECT MARKER MOUNTING BAR


SECTION A-A
(Sign mounting bracket similar)

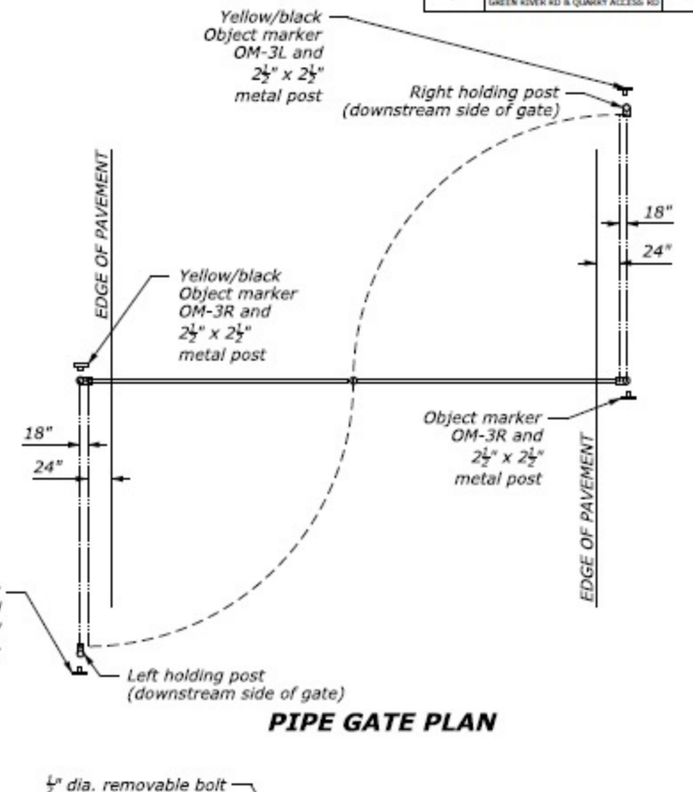


PIPE GATE PLAN

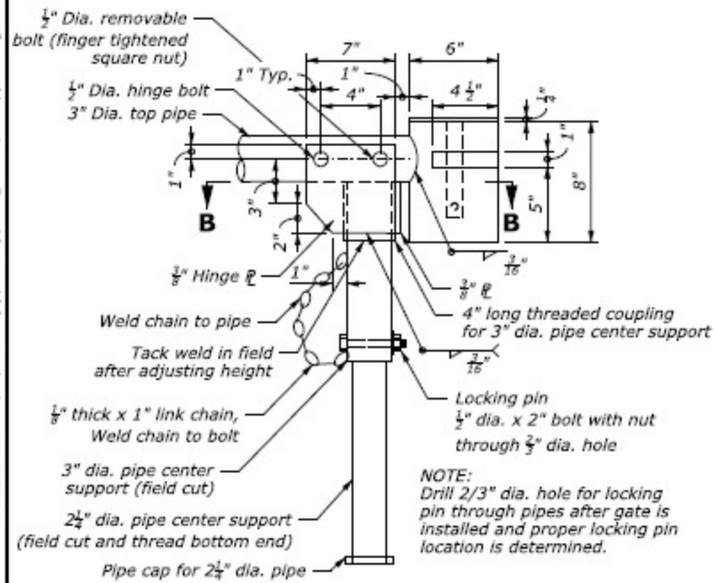

ELEVATION
LOCK & CENTER SUPPORT DETAILS

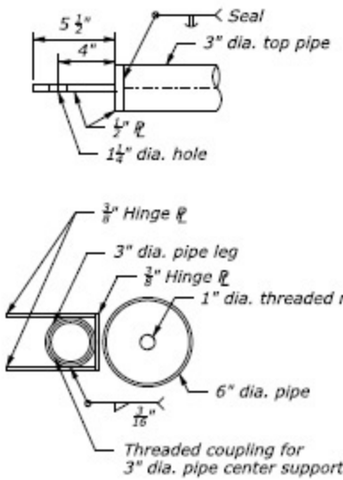


SECTION B-B

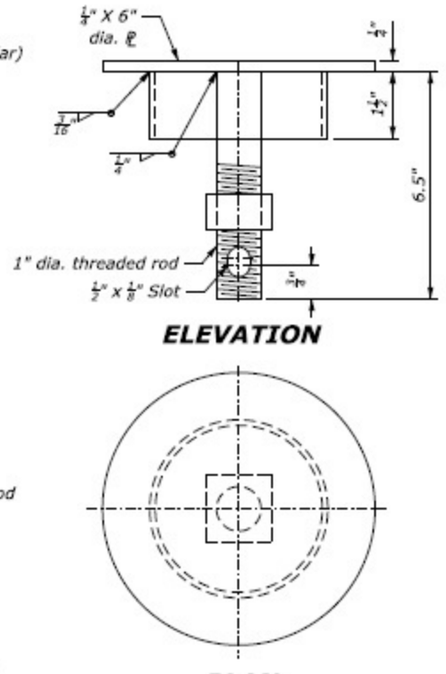

ELEVATION

PLAN
LOCK CAP DETAIL

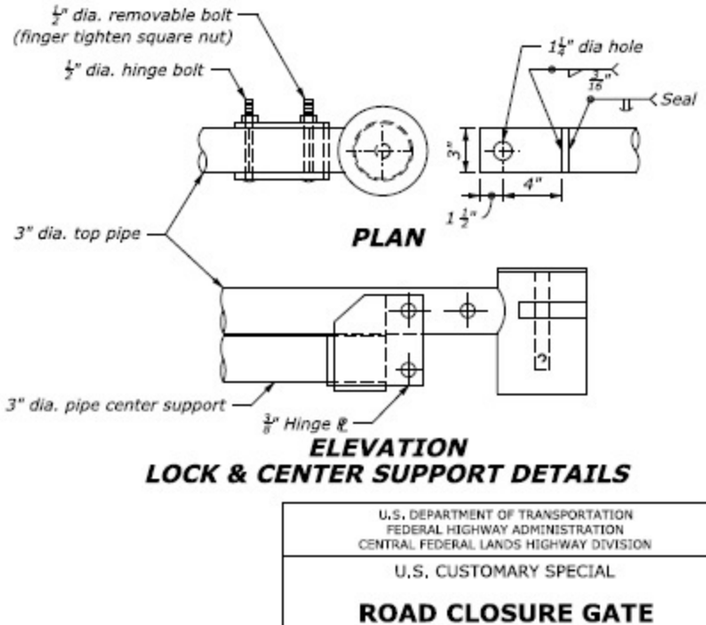

PLAN

ELEVATION
LOCK & CENTER SUPPORT DETAILS

U.S. DEPARTMENT OF TRANSPORTATION
FEDERAL HIGHWAY ADMINISTRATION
CENTRAL FEDERAL LANDS HIGHWAY DIVISION

U.S. CUSTOMARY SPECIAL

ROAD CLOSURE GATE

Sheet 1 of 2

NO SCALE

SPECIAL
619-B

User: Stacy.Dicicco
8:11:39 AM C:\CD\meve100(1)\Roadway\CADD_Sheets\T-600\spe619A.dgn
8/19/2020