
# U.S. FISH & WILDLIFE SERVICE

## NATIONAL ELK REFUGE

## ACCESS ROAD REPAIR

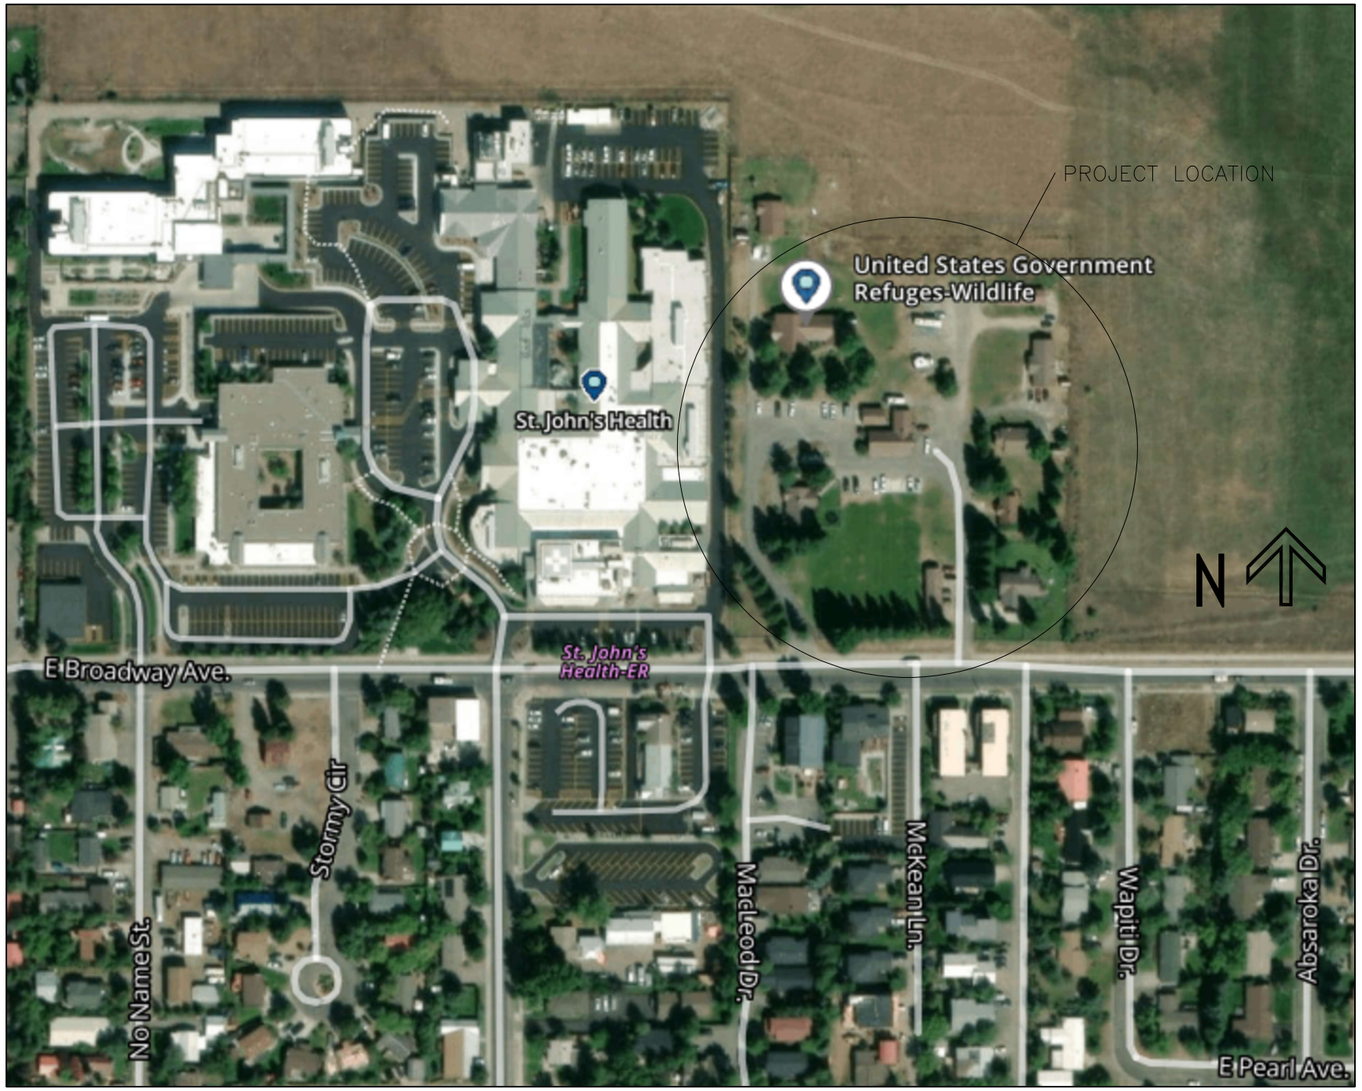


SITE PLAN
NOT TO SCALE

## DRAWING INDEX

| SHEET | TITLE | SHEET # |
|---|---|---|
| COVER | COVER SHEET, VICINITY MAP, LOCATION MAP | 1/3 |
| C10 | ELK REFUGE SITE PLAN | 2/3 |
| D10 | DETIALS | 3/3 |
| | | |
| | | |
| | | |
| | | |




VICINITY MAP
NO SCALE

## APPROVAL SIGNATURES

REGIONAL ENGINEER — DATE

PROGRAM SUPERVISOR — DATE

ASS'T. REGIONAL DIR. — DATE

FACILITIES — DATE

SAFETY/IND HYGIENIST — DATE

CULTURAL RESOURCES — DATE

NOTE TO BIDDERS:

ANY PRINT ACCOMPANYING THIS INVITATION TO BID MAY BE A REDUCED REPRODUCTION OF THE WORKING DRAWINGS. IF LINE BELOW DOES NOT MEASURE SIX INCHES IN LENGTH, THE INDICATED SCALES ARE TO BE ADJUSTED ACCORDINGLY.


UNITED STATES DEPARTMENT OF THE INTERIOR
FISH AND WILDLIFE SERVICE
REGION 6 ENGINEERING – DENVER, COLORADO

NATIONAL ELK REFUGE

TETON COUNTY — WYOMING

ACCESS ROAD REPAIR
VICINITY MAP AND
DRAWING INDEX

| DESIGNED: CL | DRAWN: CL | CHECKED: | |
|---|---|---|---|
| DATE: 09/10/25 | DRAWING NO. 6R-WY-074-25-042 | | SHEET 1 OF 3 |

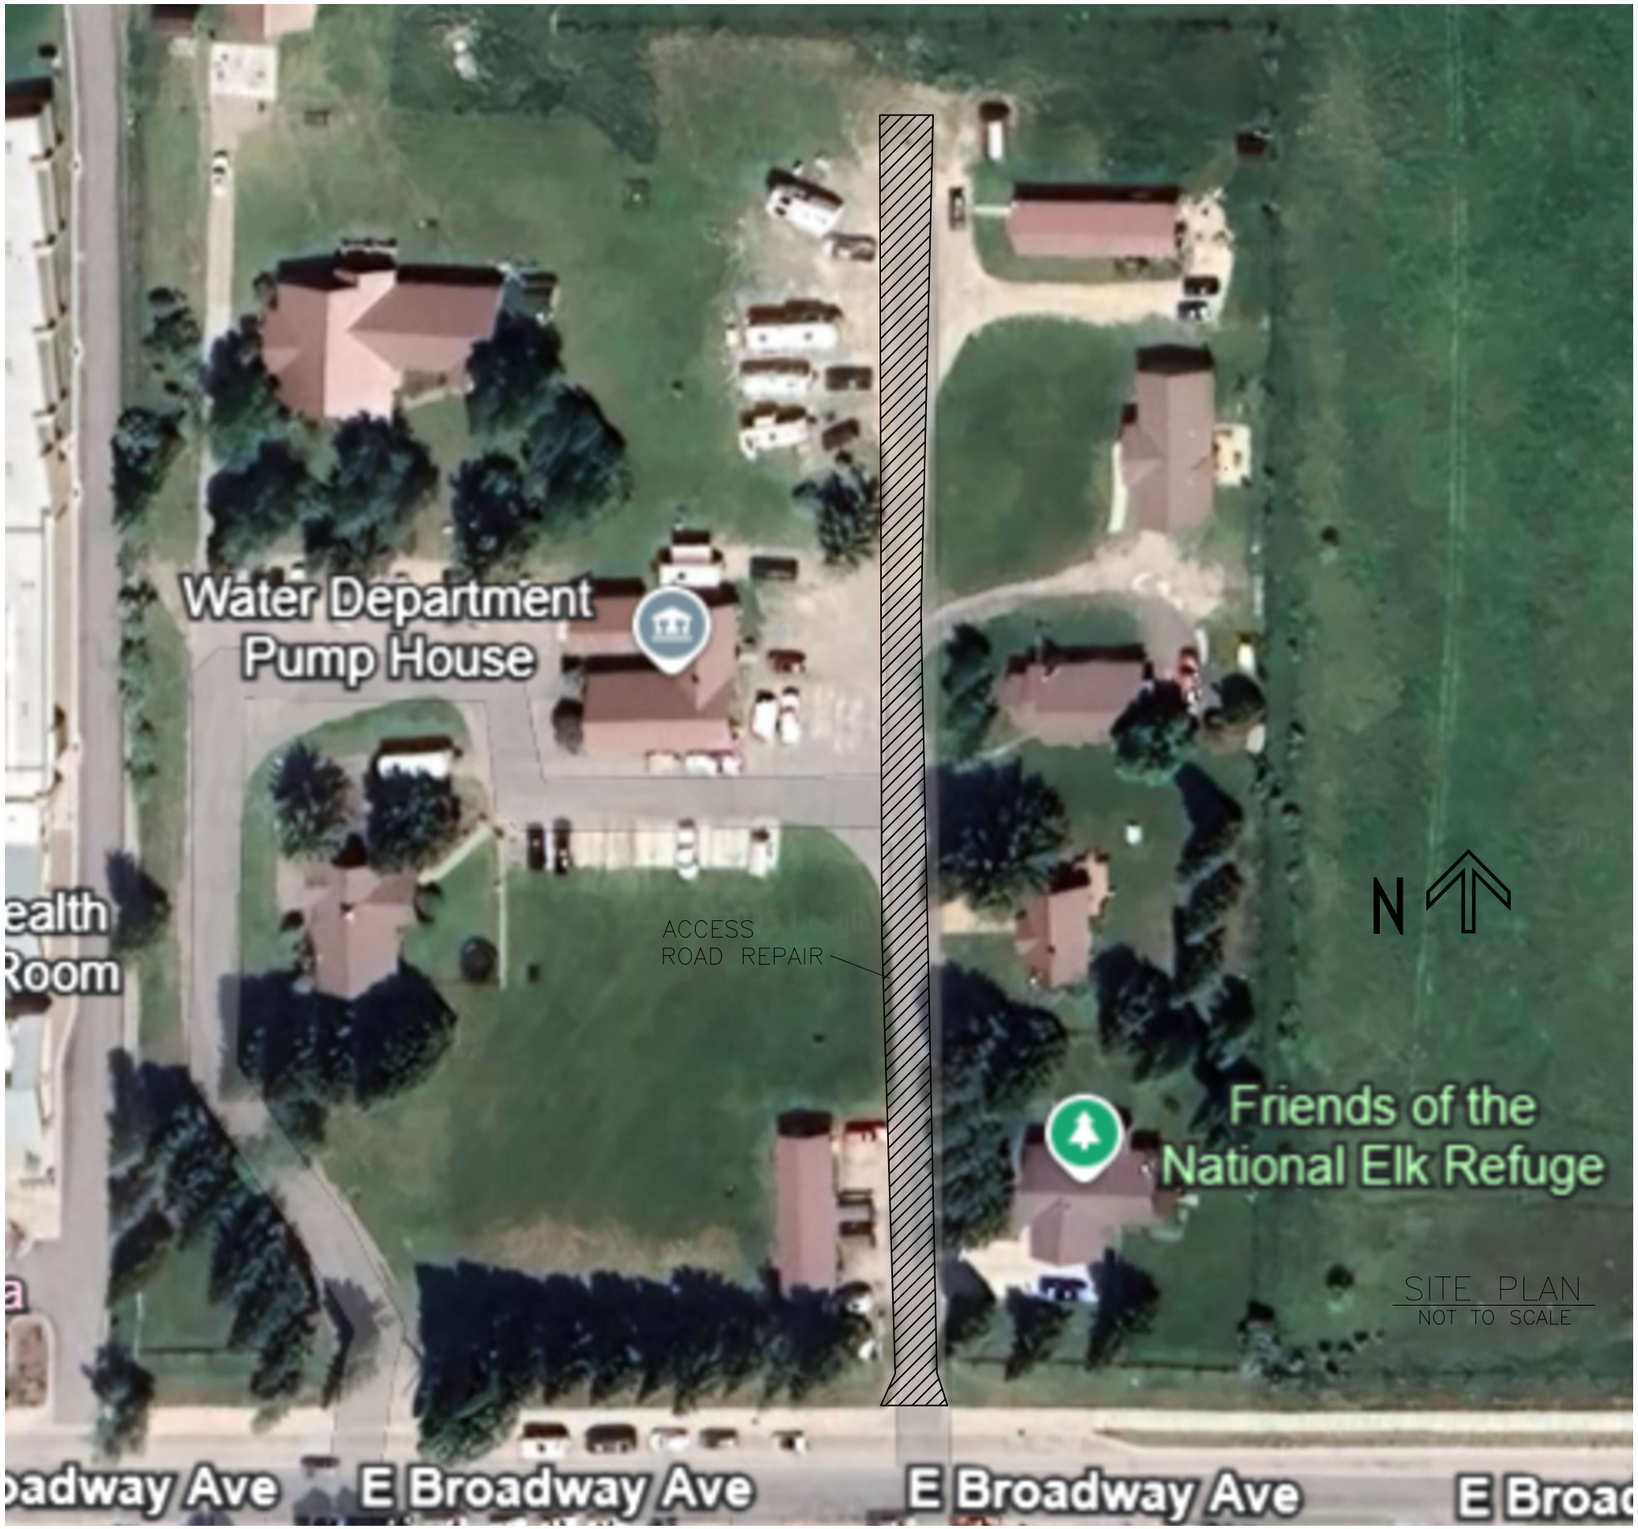


PROJECT NOTES:

1) CLEAN SURFACE AND REMOVE LOOSE DEBRIS
2) APPLY PRIME COAT TO SURFACE OF EXISITNG ROAD
3) PLACE A 3" LIFT OF ASPHALT CEMENT PAVEMENT.
4) ROLL AND COMPACT USING A STEEL DRUM ROLLER.

REPAIR CALCULATIONS

Perimeter
1,030 ft

Area
7,743 ft²


Advanced measurements

Elevation estimate
Min: 6,269 ft | Median: 6,273 ft | Max: 6,282 ft

NATIONAL ELK REFUGE
ELK REFUGE SITE PLAN
ACCESS ROAD REPAIR

SUB-SHEET C10

| DESIGNED | DRAWN | CHECKED | DATE | DRAWING NO. | SHEET |
|---|---|---|---|---|---|
| CL | | L | 09/10/2025 | 6R-WY-074-25-042 | 2 OF 3 |

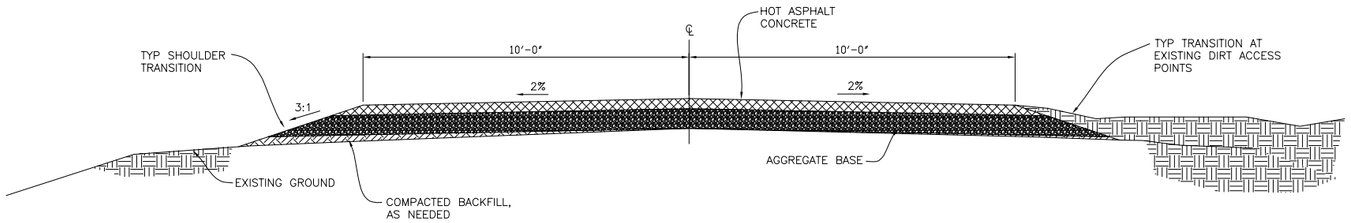


ROAD DETAIL
NOT TO SCALE

PROJECT NOTES:

1) CLEAN SURFACE AND REMOVE LOOSE DEBRIS
2) APPLY PRIME COAT TO SURFACE OF EXISITNG ROAD
3) PLACE A 3" LIFT OF ASPHALT CEMENT PAVEMENT.
4) ROLL AND COMPACT ASPHALT WITH A STEEL DRUM ROLLER.

REPAIR CALCULATIONS

**Perimeter**
1,030 ft

**Area**
7,743 ft²

**Advanced measurements**

**Elevation estimate**
Min: 6,269 ft | Median: 6,273 ft | Max: 6,282 ft

NATIONAL ELK REFUGE
ELK REFUGE SITE PLAN
ACCESS ROAD REPAIR

SUB-SHEET
D10

| DESIGNED | DRAWN | CHECKED | DATE | DRAWING NO. | SHEET |
|---|---|---|---|---|---|
| CL | | L | 09/10/2025 | 6R-WY-074-25-042 | 3 OF 3 |