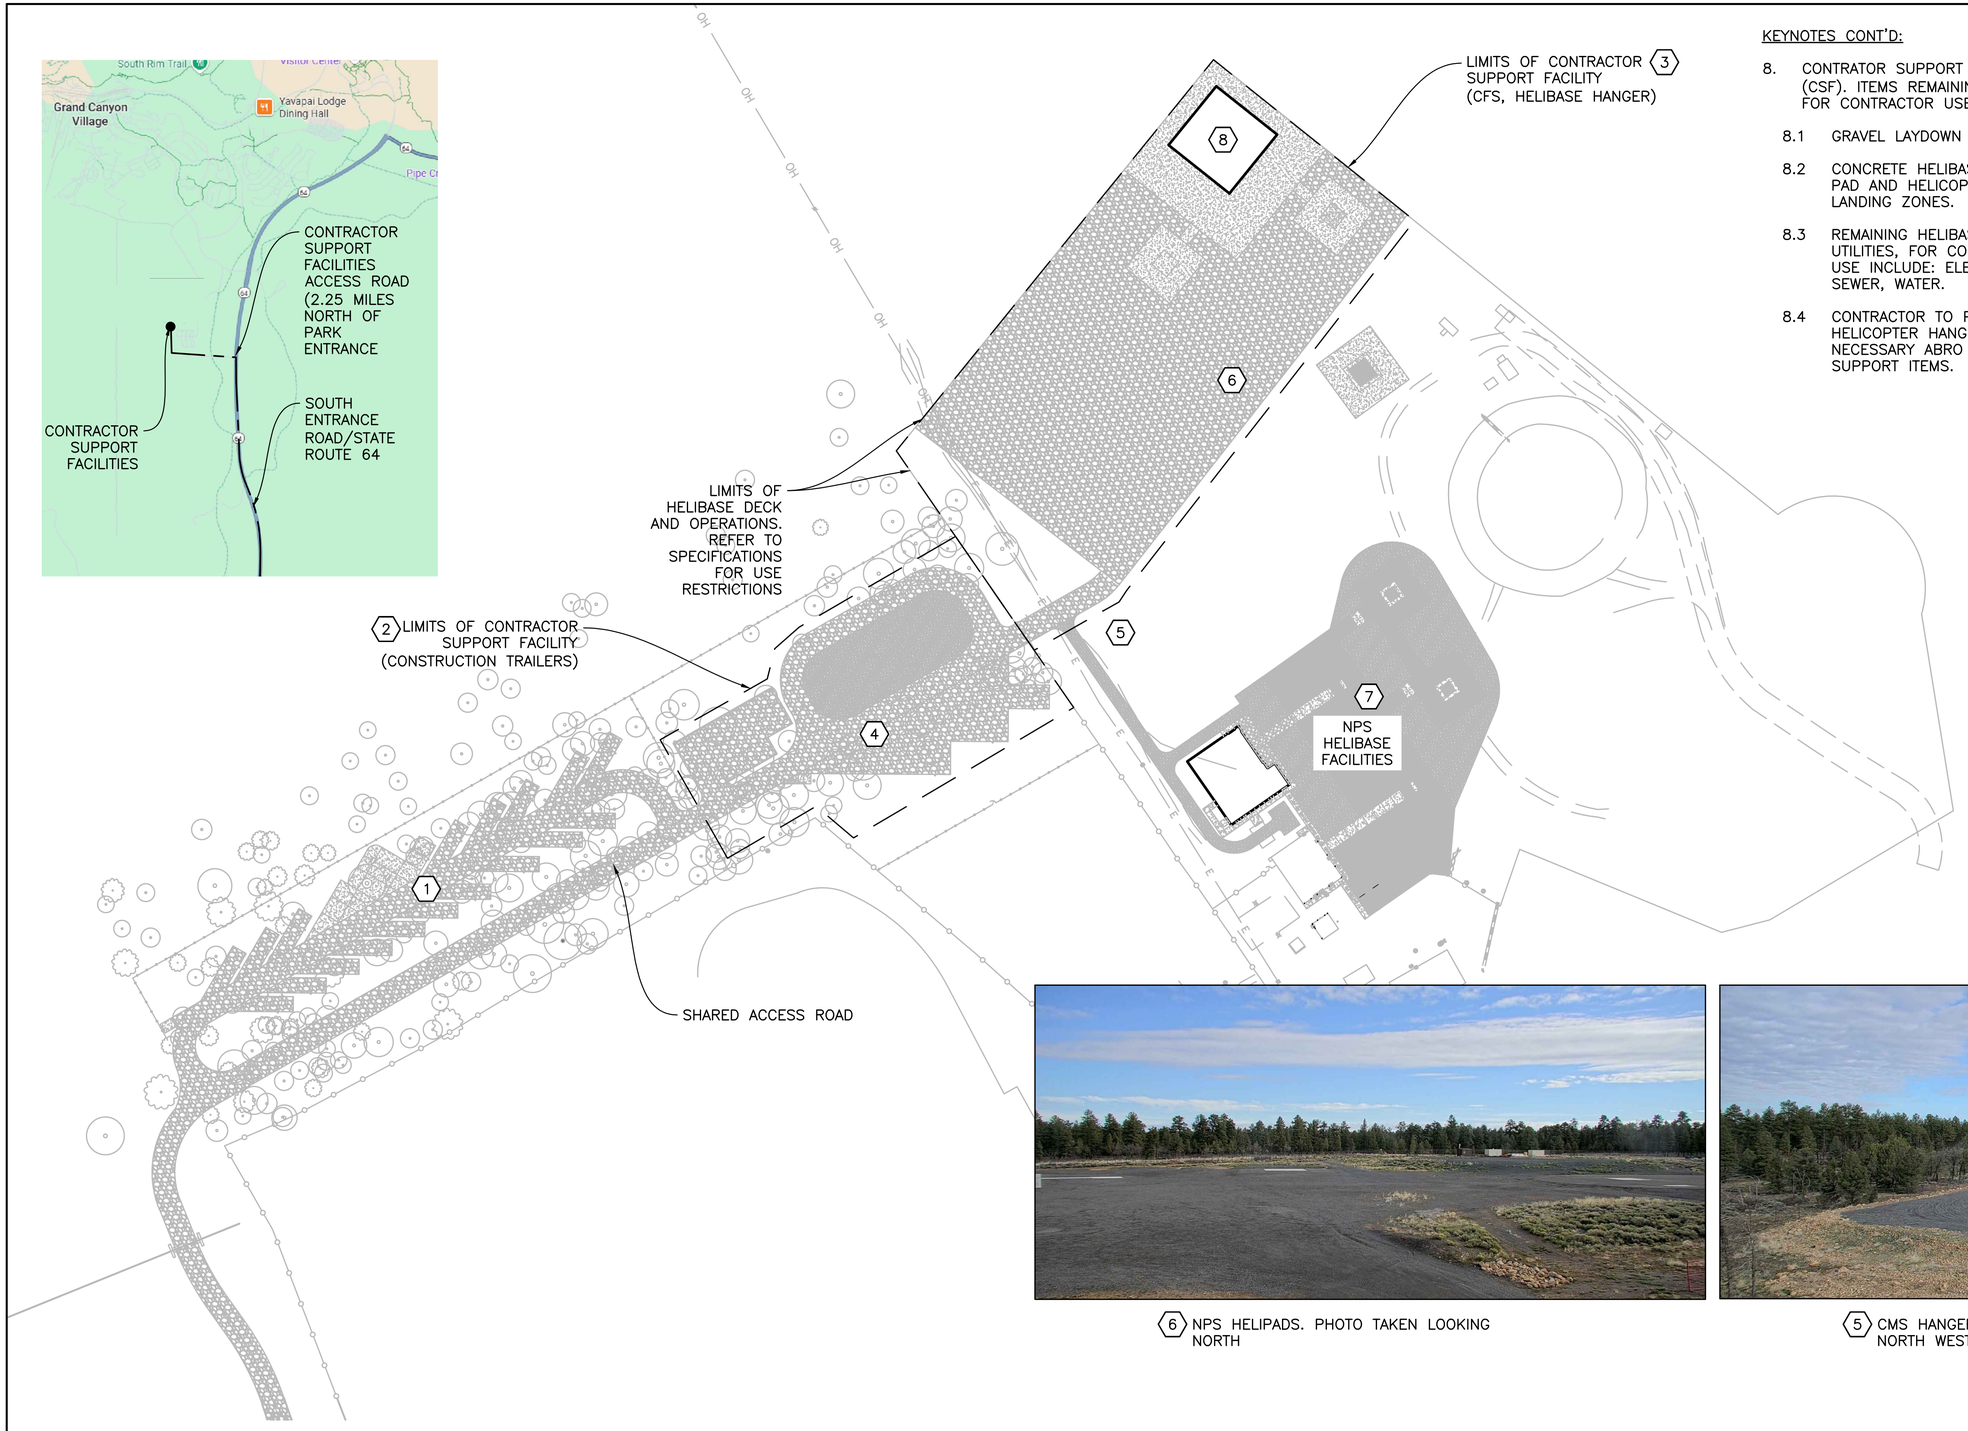


KEYNOTES CONT'D:

8. CONTRATOR SUPPORT FACILITIES (CSF). ITEMS REMAINING ON SITE FOR CONTRACTOR USE WILL BE:
   - 8.1 GRAVEL LAYDOWN YARDS.
   - 8.2 CONCRETE HELIBASE HANGER PAD AND HELICOPTER LANDING ZONES.
   - 8.3 REMAINING HELIBASE UTILITIES, FOR CONTRACTOR USE INCLUDE: ELECTRIC, SEWER, WATER.
   - 8.4 CONTRACTOR TO PROVIDE HELICOPTER HANGER AND ALL NECESSARY ABRO RELATED SUPPORT ITEMS.

KEYNOTES: (X)

1. RV SPOTS NOT IN CONTRACT
2. CONTRACTOR STAGING, HOUSING, JOB TRAILERS, AND GENERAL USE.
3. CONTRACTOR AVIATION OPERATIONS PER SPECIFICATION 01 65 50 – MATERIAL TRANSPORT – HELICOPTERS.
4. DRIVING DIRECTIONS TO THE CONTRACTOR SUPPORT FACILITY FROM TUSAYAN, AZ. CONTRACTOR SHALL REVERSE THESE DIRECTIONS TO BACK TO TUSAYAN, AZ:
   - 4.1. GO NORTH ON STATE ROUTE 64 UNTIL YOU REACH THE PARK'S SOUTH ENTRANCE STATION (1.5 MILES APPROX).
   - 4.2. CONTINUE NORTH, THOUGH THE SOUTH ENTRANCE STATION ON STATE ROUTE 64. (2.25 MILES APPROX.)
   - 4.3. TAKE A LEFT (WEST) ONTO THE GRAVEL ROAD CONSTRUCTED FOR THE CONTRACTOR SUPPORT FACILITIES.
   - 4.4. CONTINUE ON THIS ROAD UNTIL DEAD END AT THE CONTRACTOR CUPPORT FACILITIES (0.75 MILES APPROX.).
5. LOOKING NORTH–WEST.
6. LOCATION OF PHOTO, LOOKING NORTH.
7. NPS HELIBASE FACILITIES ARE NOT AVAILABLE FOR CONTRACTOR USE, NOT IN THE CONTRACT.

(6) NPS HELIPADS. PHOTO TAKEN LOOKING NORTH



(5) CMS HANGER. PHOTO TAKEN LOOKING NORTH WEST

80 0 80 160
SCALE OF FEET
1" = 80'

REGISTERED PROFESSIONAL ENGINEER (CIVIL) CERTIFICATE NO. 41859 RYAN RHOADES Date Signed 5-1-26 ARIZONA, U.S.A.

A/E FIRM PRIME: HDR ENGINEERING, INC. DENVER, CO 80202	DESIGNED: G. YOUNG CADD G. YOUNG TECH. REVIEW: M. GOUCH/R. RHODES DATE: MAY 2026	SUB SHEET NO. 000 G107	TITLE OF SHEET GENERAL NORTH RIM CSF HELICOPTER STAGING AREA (SOUTH RIM) NORTH RIM - GRAND CANYON NATIONAL PARK	DRAWING NO. 113 182752 PMIS/PKG NO. 318719 SHEET 10 OF 99

4/23/2026 Lynch, Nicole C:\Users\nlynch\DC\ACCDocs\HDR\10350545_NPS_GRCA_N_Rim_Utility_2026\Project Files\CAD_HDR\DRAWINGS\GEN\000-G107.dwg



GENERAL NOTES:

A. LINDBERGH HILL CONSTRUCTION CAMP REQUIRES SHUTTLE FOR ALL PERSONNEL TO AND FROM THE NORTH RIM CONSTRUCTION AREAS TO REDUCE AMOUNT OF TRAFFIC AND VEHICLES AT EACH WORK SITE ON THE NORTH RIM. STAGING AREA PARKING IS LIMITED.

B. CONTRACTOR SHALL BE RESPONSIBLE FOR ALL REQUIRED SNOW REMOVAL FROM SR 67 INTO THE CONSTRUCTION CAMP AREA.

KEYNOTES: (X)

1. YEAR ROUND CAMPING IS ACCEPTABLE AT THIS LOCATION. THE FOLLOWING RESTRICTIONS ARE APPLICABLE:
   1.1 UP TO 6 SELF CONTAINED CAMPING UNITS ARE ACCEPTABLE.
   1.2 SELF CONTAINED CAMPING UNITS SHALL BE NO LONGER THAN 40 FT IN LENGTH.
   1.3 ONLY ELECTRICAL HOOKUPS PROVIDED. NO WATER OR SEWER UTILITIES AVAILABLE.
   1.3 SEWER (GRAY & BLACK) MUST BE HAULED TO PROPER RV DUMP FACILITY.
2. CONTRACTOR RESPONSIBLE FOR MAINTAINING ROAD AND RETURNING ROAD TO EXISTING CONDITIONS OR BETTER POST CONSTRUCTION ACTIVITIES.
3. ACCESS TO OWNER FACILITIES TO BE MAINTAINED. FINAL LOCATION OF TRAILERS TO BE APPROVED BY CO.

50 0 50 100 1" = 50'
SCALE OF FEET

ARIZONA PROFESSIONAL ENGINEER CERTIFICATE NO. 41909 RYAN RHOADES United States 5-17-26 ARIZONA, U.S.A.

A/E FIRM	PRIME: HDR ENGINEERING, INC. DENVER, CO 80202
DESIGNED:	G. YOUNG
DRAWN:	G. YOUNG
TECH. REVIEW:	M.GOUGH/R. RHODES
DATE:	MAY 2026
SUB SHEET NO.	000 G108
TITLE OF SHEET	GENERAL NORTH RIM LINDBERGH HILL CONSTRUCTION CAMP NORTH RIM - GRAND CANYON NATIONAL PARK
DRAWING NO.	113 182752
PMIS/PKG NO.	318719
SHEET	11 OF 99

4/18/2026 Young, Gregory C:\Users\gryoung\DC\ACCDocs\HDR\10350545_NPS_GRCA_N_Rim_Utility_2022\Project Files\CAD_HDR\DRAWINGS\GEN\000-G108.dwg