GENERAL NOTES:

A. ENTIRE FACILITY, INCLUDING BUT NOT LIMITED TO THE NORTON COURT CAMPGROUND, CAMPING AREA, ETC., ARE SHARED USE WITH NPS. SEE SPECIFICATIONS FOR ADDITIONAL INFORMATION PERTAINING TO GENERAL USE RESTRICTIONS AND LIMITATIONS.

KEYNOTES: (X)

1. SEASONAL CAMPING IS ACCEPTABLE AT THIS LOCATION ALONG DUSTY ROAD. THE FOLLOWING RESTRICTIONS ARE APPLICABLE:
   1.1. 19 SITES AVAILABLE FOR USE. 3 OF THE SITES SHALL BE RESERVED FOR CMR (16 SPACES AVAILABLE FOR CONTRACTOR USE, 3 FOR CMR USE).
   1.2. FULL HOOKUPS ARE AVAILABLE MAY – OCTOBER.

40 0 40 80 1" = 40'
SCALE OF FEET

ARIZONA REGISTERED PROFESSIONAL ENGINEER CERTIFICATE NO. 41809 RYAN RHOADES Date Signed 5-1-26 ARIZONA, U.S.A.

A/E FIRM PRIME: HDR ENGINEERING, INC. DENVER, CO 80202	DESIGNED: G. YOUNG CADD G. GIORLANDO TECH. REVIEW: M. GOUGH/R. RHODES DATE: MAY 2026	SUB SHEET NO. 000 G111	TITLE OF SHEET GENERAL NORTH RIM NORTON CT CAMPGROUND CONSTRUCTION CAMP NORTH RIM - GRAND CANYON NATIONAL PARK
			DRAWING NO. 113 182752 PMIS/PKG NO. 318719 SHEET 14 OF 99

4/17/2026 Flansburg, Jade C:\Users\jflansburg\DC\ACCDocs\HDR\103505545_NPS_GRCA_N_Rim_Utility_2022\Project Files\CAD_HDR\DRAWINGS\GEN\000-G111.dwg

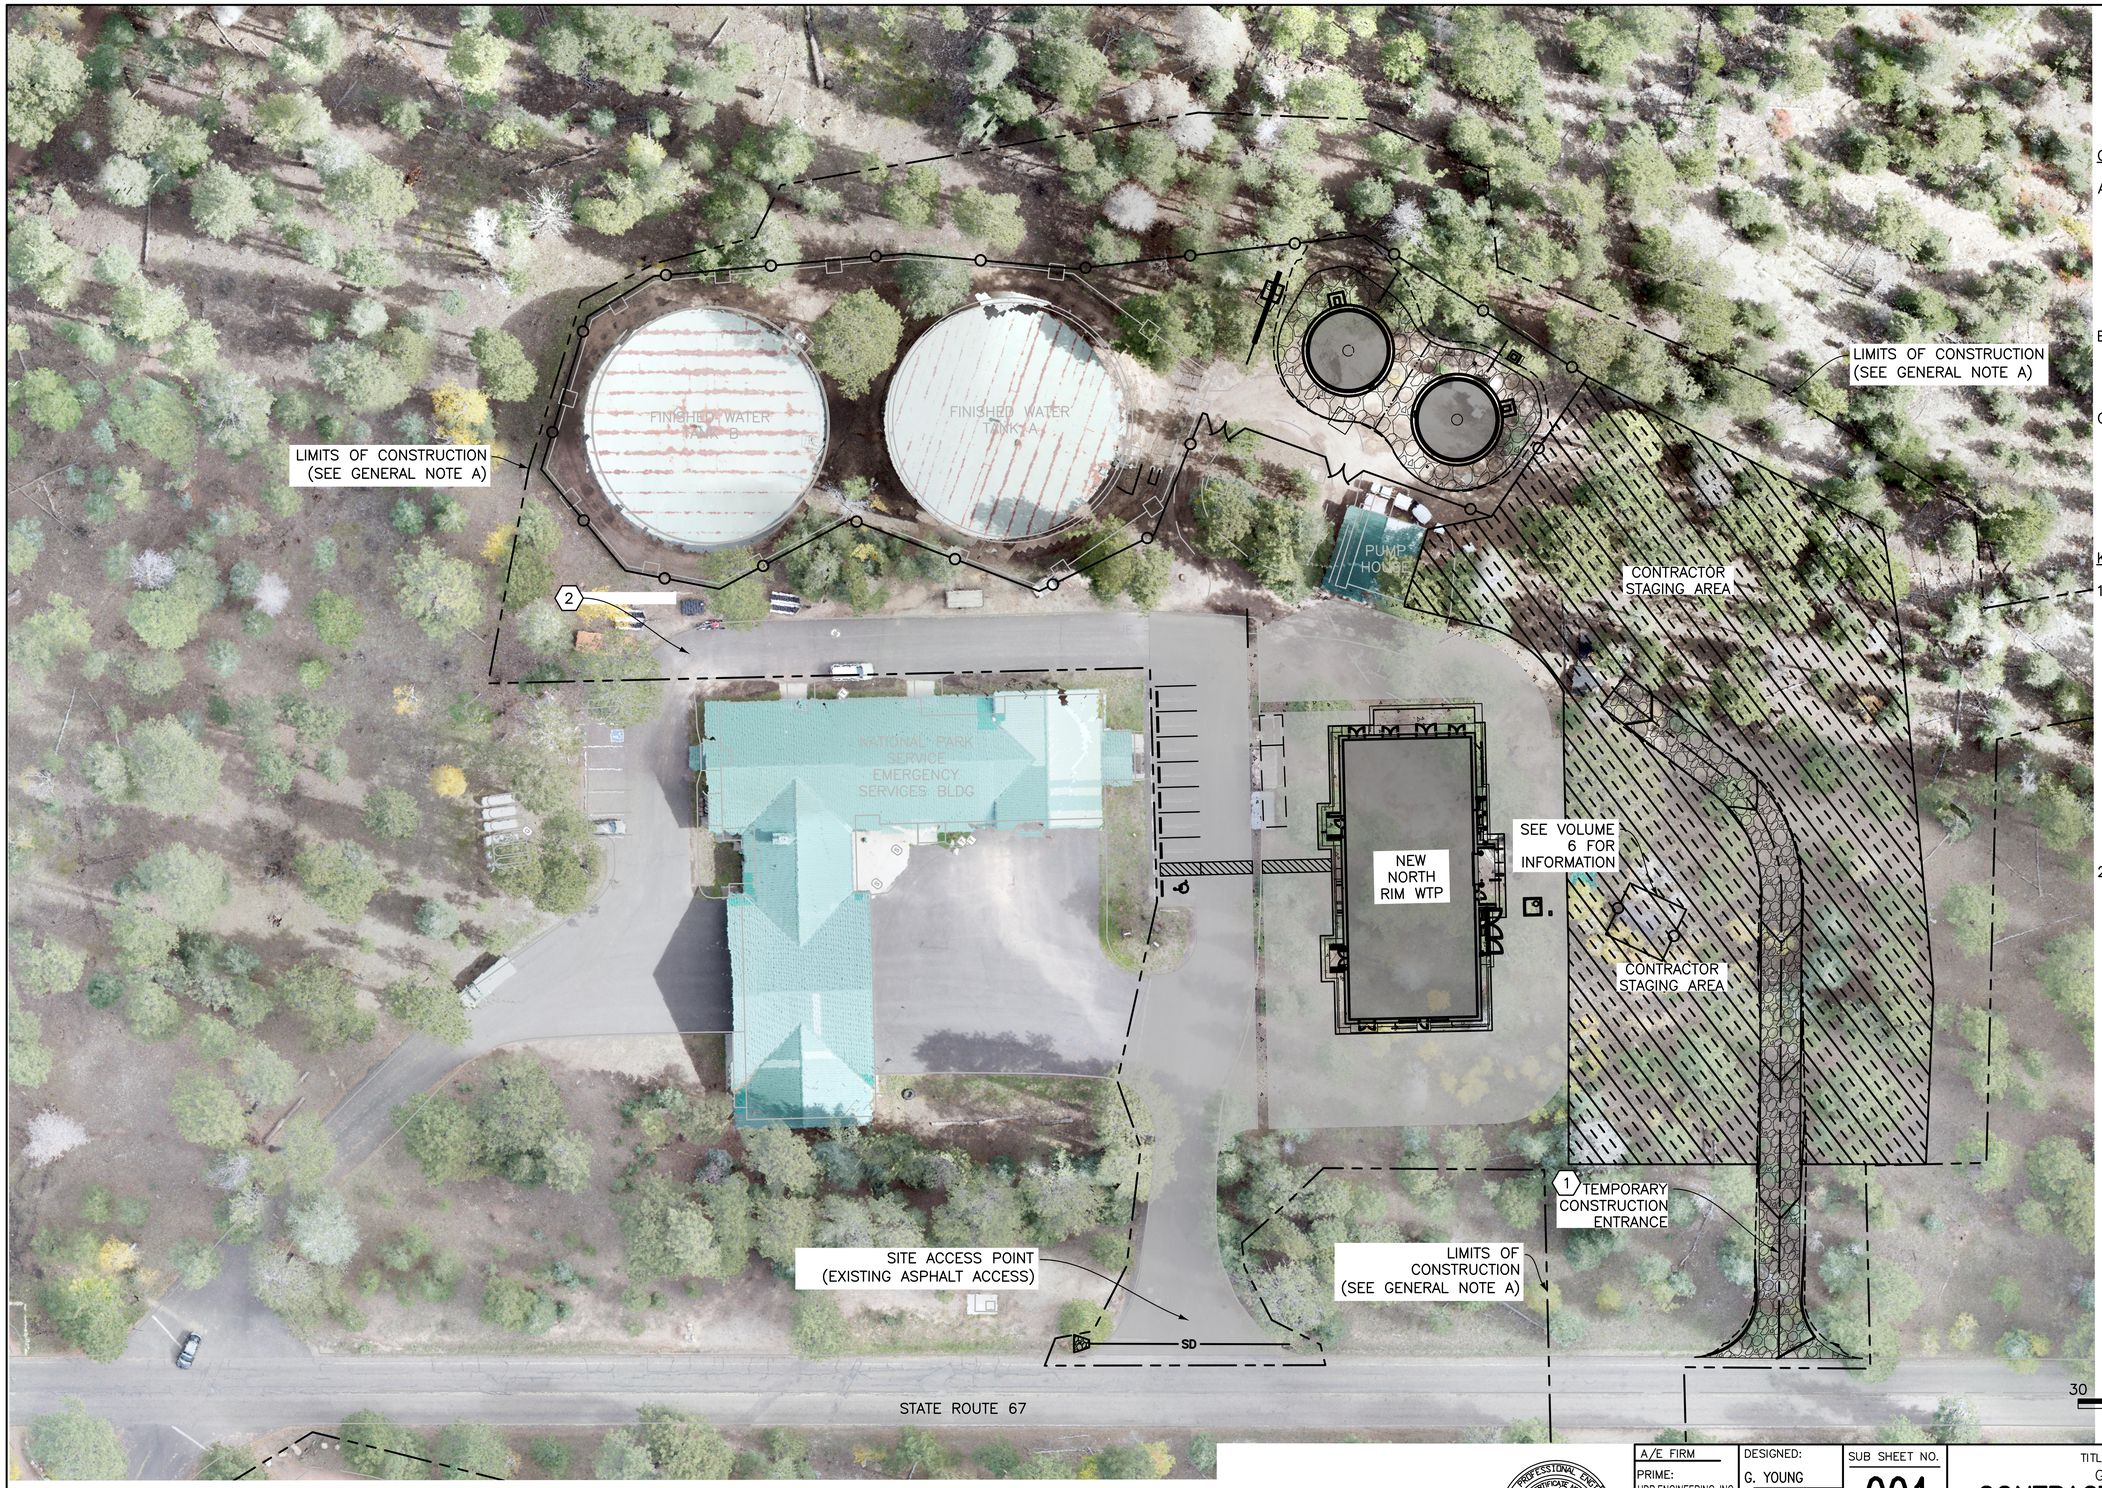

GENERAL NOTES:

A. LIMITS OF CONSTRUCTION:

A.A. LIMIT USE OF PREMISES TO AREAS WITHIN THE LIMITS OF CONSTRUCTION INDICATED ON DRAWINGS. DO NOT DISTURB PORTIONS OF THE SITE BEYOND THESE AREAS.

B. CONTRACTOR STAGING AREA TO SUPPORT CONSTRUCTION, CONSTRUCTION CAMP NOT AUTHORIZED.

C. CONTRACTOR WILL PROVIDE TRAFFIC ACCESS FOR NPS TRAFFIC ACCESS FOR NPS OPERATIONS DURING CONSTRUCTION ACTIVITIES ON ALL EXISTING PAVED AREAS AROUND THE EMS BUILDING.

KEYNOTES: (X)

1. APPROXIMATE LOCATION OF TEMPORARY CONSTRUCTION ENTRANCE. CONTRACTOR SHALL MINIMIZE DISTURBANCE TO ALL EXISTING TREES AND SHALL DEVELOP A TREE REMOVAL PLAN TO BE APPROVED BY THE CONTRACTING OFFICER PRIOR TO CONSTRUCTION. AGGREGATE QUANTITY = 200 TONS (APPROX.). TEMPORARY CONSTRUCTION ROAD AND ALL CONSTRUCTION STAGING AREAS SHALL BE REMOVED AND REHABILITATED PER THE SPECIFICATIONS AFTER CONSTRUCTION IS COMPLETED.

2. CONTRACTOR WILL PROVIDE TRAFFIC ACCESS FOR NPS OPERATIONS DURING CONSTRUCTION ACTIVITIES ON ALL EXISTING PAVED AREAS AROUND THE EMS BUILDING.

REGISTERED PROFESSIONAL ENGINEER — CERTIFICATE NO. 41809 — RYAN RHOADES — State Barred — ARIZONA, U.S.A. — 12-31-26

A/E FIRM PRIME: HDR ENGINEERING, INC. DENVER, CO 80202	DESIGNED: G. YOUNG CADD G. YOUNG TECH. REVIEW: M. GOUCH/R. RHODES DATE: JUNE 2026	SUB SHEET NO. 001 G120	TITLE OF SHEET GENERAL CONTRACTOR STAGING AND WTP ACCESS PLAN NORTH RIM - GRAND CANYON NATIONAL PARK	DRAWING NO. 113 182752 PMIS/PKG NO. 318719 SHEET 15 OF 99

8/17/2026 Green, Jake C:\Users\jgreen\DC\ACCDocs\HDR\10350545_NPS_GRCA_N_Rim_Utility_2022\Project Files\CAD_HDR\DRAWINGS\GEN\000-G120.dwg

GENERAL NOTES:

A. LIMITS OF CONSTRUCTION:

A.A. LIMIT USE OF PREMISES TO AREAS WITHIN THE LIMITS OF CONSTRUCTION INDICATED ON DRAWINGS. DO NOT DISTURB PORTIONS OF THE SITE BEYOND THESE AREAS.

B. CONTRACTOR STAGING AREA:

B.A. EQUIPMENT AND MATERIAL STAGING AREAS ARE INTENDED FOR DELIVERIES AND STORAGE OF TOOLS AND EQUIPMENT, MATERIAL STOCKPILING, CONSTRUCTION EQUIPMENT PARKING, CONSTRUCTION VEHICLE PARKING, CONSTRUCTION ADMINISTRATION TRAILERS, AND SIMILAR.

B.B. CONFINE STOCKPILING TO EQUIPMENT AND MATERIAL STAGING AREAS. SMALL STOCKPILES WITHIN LIMITS OF CONSTRUCTION FOR USE IN LOCALIZED TRENCHING WORK IS ACCEPTABLE.

B.C. AREAS WITHIN THE LIMITS OF CONSTRUCTION THAT ARE NOT DESIGNATED FOR EQUIPMENT AND MATERIAL STAGING SHALL NOT BE USED FOR THIS PURPOSE.

B.D. EQUIPMENT AND MATERIAL STAGING AREAS SHOULD NOT BE USED FOR CONSTRUCTION CAMPS INCLUDING CAMPING UNITS, TRAILER COMPLEXES FOR LIVING AREAS, PRIVATE VEHICLE PARKING, AND SIMILAR.

40 0 40 80 1" = 40'
SCALE OF FEET

REGISTERED PROFESSIONAL ENGINEER
CERTIFICATE NO. 41909
RYAN RHOADES
Date Signed 5-21-26
ARIZONA, U.S.A.

A/E FIRM PRIME: HDR ENGINEERING, INC. DENVER, CO 80202	DESIGNED: G. YOUNG CADD G. YOUNG TECH. REVIEW: M. GOUGH/R. RHODES DATE: JUNE 2026	SUB SHEET NO. 001 G122	TITLE OF SHEET SITEWORK CONTRACTOR STAGING AND ACCESS PLAN BALLFIELD SITE NORTH RIM - GRAND CANYON NATIONAL PARK	DRAWING NO. 113 182752 PMIS/PKG NO. 318719 SHEET 16 OF 99

8/17/2026 Green, Jake C:\Users\jgreen\DC\ACCDocs\HDR\10350545_NPS_GRCA_N_Rim_Utility_2022\Project Files\CAD_HDR\DRAWINGS\GEN\000-G122.dwg

CIVIL MAPPING SYMBOLOGY

- EMBANKMENT SLOPE (CUT)
- EMBANKMENT SLOPE (FILL)
- H:V EMBANKMENT SLOPE RIGHT ARROW RIGHT
- H:V EMBANKMENT SLOPE LEFT ARROW LEFT
- SURVEY BENCHMARK
- CP–X SURVEY CONTROL POINT
- CP–X EXIST SURVEY CONTROL POINT
- HORIZONTAL CONTROL POINT
- EXIST HORIZONTAL CONTROL POINT
- VERTICAL CONTROL POINT
- FLOW ARROW
- WATER LEVEL IN SECTION/PROFILE
- XXX INTERSTATE HIGHWAY SYMBOL
- XXX US HIGHWAY SYMBOL
- XXX STATE HIGHWAY SYMBOL
- POWER POLE
- EXIST POWER POLE
- POLE TRANSFORMER
- EXIST POLE TRANSFORMER
- E EXIST ELECTRICAL BOX
- EM EXIST ELECTRICAL METER
- T PAD TRANSFORMER
- T EXIST PAD TRANSFORMER
- J JUNCTION BOX
- J EXIST JUNCTION BOX
- SB # SPLICE BOX
- COMM EXIST COMMS BOX
- SIGN
- EXIST SIGN
- EXIST WOOD POST

- FIRE HYDRANT
- EXIST FIRE HYDRANT
- YARD HYDRANT
- EXIST YARD HYDRANT
- HB HOSE BIBB
- HB EXIST HOSE BIBB
- M WATER METER
- M EXIST WATER METER
- MANHOLE
- EXIST MANHOLE
- CULVERT W/END (WITH END SECTIONS–DBL LINE)
- EXIST CULVERT W/END (WITH END SECTIONS–DBL LINE)
- CULVERT W/END SECTIONS (SINGLE LINE)
- EXIST CULVERT W/END (SINGLE LINE)
- HEADWALL
- EXIST HEADWALL
- VALVE
- EXIST VALVE
- CONCENTRIC REDUCER
- EXIST CONCENTRIC REDUCER
- PIPE CAP
- POST INDICATOR VALVE
- IRRI EXIST IRRIGATION BOX
- EXIST POTABLE WATER SPIGOT
- SEWER CLEANOUT
- EXIST SEWER CLEANOUT
- FO FIBER OPTIC PULL BOX
- AIR RELIEF VALVE

WATER AND RAW WATER LINETYPE DESCRIPTIONS

W1	NORTH RIM POTABLE WATER DISTRIBUTION
W2	NOT USED
W3	SUPAI TUNNEL POTABLE WATER SUPPLY
W4	NOT USED
W5	INNER CANYON POTABLE WATER SUPPLY (HIGH PRESSURE)
W6	INNER CANYON POTABLE WATER SUPPLY (STANDARD PRESSURE)
RW1	NORTH RIM RAW WATER SUPPLY
RW2	NOT USED
RW3	NOT USED
RW4	RAW WATER SUPPLY FROM RS CAVE TO RSPH
RW5	RAW WATER FROM RSPH TO NORTH RIM (HIGH PRESSURE)

MATERIALS IN PLAN/SECTION

- ACOUSTICAL CEILING TILE (SECTION)
- ASPHALT (PLAN OR SMALL–SCALE SECTION)
- ASPHALT (LARGE–SCALE SECTION)
- EXISTING ASPHALT (PLAN OR SMALL–SCALE SECTION)
- BATT INSULATION (SECTION)
- BRICK MASONRY (PLAN AND/OR SECTION)
- CHECKERED PLATE (PLAN)
- CONCRETE (PLAN AND/OR SECTION)
- CONCRETE MASONRY (PLAN AND/OR SECTION)
- DEMOLITION (PLAN AND/OR SECTION)
- EARTH (SECTION)
- FILTER POINT MAT (PLAN)
- FINISHED WOOD (SECTION)
- GLULAM LUMBER (SECTION)
- GRANULAR FILL (SECTION)
- GRATING (SECTION)
- GRATING (PLAN)
- GROUT (SECTION)
- GYPSUM BOARD (SECTION)
- METAL (SECTION)
- ORIENTED STRAND BOARD (SECTION)
- PARTICLE BOARD (SECTION)
- PLYWOOD (LARGE–SCALE SECTION)
- PLYWOOD (SMALL–SCALE SECTION)
- PRECAST CONCRETE (PLAN AND/OR SECTION)
- RIGID INSULATION (SECTION)
- RIPRAP (PLAN AND/OR SECTION)
- SAND (SECTION)
- SOD (SECTION)
- WEEP JOINT MORTAR PROTECTION SYSTEM (SECTION)
- WOOD – CONTINUOUS (SECTION)
- WOOD BLOCKING (SECTION)
- DEMOLISH TREE

UTILITY/CIVIL LINE SYMBOLOGY

- W TREATED WATER PIPELINE
- RW RAW WATER PIPELINE
- LARGE PIPELINE
- RW FORCE MAIN
- UTILITY BENEATH STRUCTURE
- (SS) EXISTING SANITARY SEWER (GIS) (WITH IMAGE BEHIND)
- (UE) EXISTING UNDERGROUND ELECTRIC (GIS)(WITH IMAGE BEHIND)
- (W) EXISTING WATERLINE (GIS) (WITH IMAGE BEHIND)
- (OHE) EXISTING OVERHEAD ELECTRIC (GIS) (WITH IMAGE BEHIND)
- OHE OHE OHE EXISTING OVERHEAD ELECTRIC
- (IRR) EXISTING IRRIGATION (GIS) (WITH IMAGE BEHIND)
- (UT) EXISTING TELEPHONE (GIS) (WITH IMAGE BEHIND)
- UT EXISTING TELEPHONE (SURVEYED)
- (8"W) EXISTING (X"W) WATERLINE (GIS) (WITH IMAGE BEHIND)
- (SS) EXISTING SANITARY SEWER (GIS)
- ST ST ST EXISTING STORM DRAIN (GIS)
- (UE) EXISTING UNDERGROUND ELECTRIC (GIS)
- (W) EXISTING WATERLINE (GIS)
- (OHE) EXISTING OVERHEAD ELECTRIC (GIS)
- (IRR) EXISTING IRRIGATION (GIS)
- (UT) EXISTING TELEPHONE (GIS)
- (8"W) EXISTING (X"W) WATERLINE (GIS)
- W EXISTING WATER LINE (SURVEYED)
- X"W PROPOSED X"W WATERLINE
- XX"RW PROPOSED X"RW WATERLINE
- XX"OVF PROPOSED X"OVF OVER FLOW
- XX"PW PROPOSED X"PW POTABLE WATERLINE
- UE PROPOSED UNDERGROUND ELECTRIC
- CENTERLINE
- BOTTOM OF DITCH
- PROPERTY LINE
- EASEMENT
- LIMITS OF CONSTRUCTION
- LIMITS OF DISTURBANCE
- ROW
- EXISTING EDGE OF TRAIL
- EXISTING CONTOUR (MINOR)
- 25 EXISTING CONTOUR W/ELEVATION (MAJOR)
- EXISTING WOOD FENCE
- EXISTING FENCE
- EXISTING VEGETATION/BRUSH LINE
- FENCE – BARB WIRE
- FENCE – CHAIN LINK
- ABANDONMENT OF EXIST PIPE
- FO FO PROPOSED FIBER OPTIC

- FENCE – FIELD
- FENCE – OTHER
- FENCE – WOOD
- XX FENCE – WOVEN WIRE
- FLOOD LIMIT (10 YEAR)
- FLOOD LIMIT (100 YEAR)
- FLOOD LIMIT (500 YEAR)
- HIGHWAY GUARDRAIL
- LEVEE TOP
- LEVEE TOE
- 25 NEW CONTOUR (MAJOR)
- NEW CONTOUR (MINOR)
- EXIST ROCK WALL
- BOULDER
- TOE OF SLOPE
- TOP OF SLOPE
- FO FIBER OPTIC
- FUEL OIL
- NATURAL GAS
- INDUSTRIAL WASTE WATER
- DR DRAIN LINE
- PROPOSED DRAINAGE SWALE
- CONTRACTOR STAGING AREA/ INSERTION/PULL AREA/ MATERIAL STAGING AREA
- EXISTING BUILDING OUTLINE

GENERAL NOTES:

1. THIS IS A STANDARD CIVIL SYMBOLOGY SHEET. ALL SYMBOLS ARE NOT NECESSARILY USED ON THIS PROJECT.
2. SCREENING OR SHADING OF WORK IS USED TO INDICATE EXISTING COMPONENTS OR TO DE–EMPHASIZE PROPOSED IMPROVEMENTS TO HIGHLIGHT SELECTED TRADE WORK. REFER TO CONTEXT OF EACH SHEET FOR USAGE.

SURVEY NOTES:

Survey performed in the months of October & November, 2022, by Arizona Surveying, Inc.

Basis of Bearing and/or Coordinates:
All dimensions shown on this plat are measured and based on the following projection information.
Linear Unit: International Foot

Geodetic Datum: North American Datum of 1983(NAD83)
System: World Wide/UTM
Zone = 12 North
Projection: Transverse Mercator
Latitude of Grid Origin: N0°00'00.00000"
Longitude of Grid Origin: W111°00'00.00000"
Northing at Grid Origin: 0.000
Easting at Grid Origin: 1640419.948

Vertical Datum: NAVD 88
Geoid Model = Geoid18

The basis of bearings is true geodetic north. Grid bearings shown hereon do not equal geodetic bearings due to meridian convergence. All bearings shown are grid bearings.

This survey was conducted using GPS referenced to the National Spatial Refernce System. Coordinates for GPS control points were derived using the Nation Geodetic Survey's, Online Positioning User Service (OPUS)
REF FRAME: NAD_83(2011)(EPOCH: 2010.0000).

This is not a boundry survey.
Existing survey reference monuments found during the course of this survey were left undisturbed.

REGISTERED PROFESSIONAL ENGINEER – CERTIFICATE NO. 75262 – GREGORY YOUNG – ARIZONA, U.S.A. – DATE SIGNED 5/11/26

A/E FIRM	PRIME: HDR ENGINEERING, INC. DENVER, CO 80202
DESIGNED:	G. YOUNG
DRAWN:	C. WITTENMEIER
TECH. REVIEW:	M. GOUGH/R. RHODES
DATE:	MAY 2026
SUB SHEET NO.	002 C001

TITLE OF SHEET
GENERAL
GENERAL NOTES, ABBREVIATIONS, AND LEGEND CIVIL
NORTH RIM - GRAND CANYON NATIONAL PARK

DRAWING NO. 113 182752
PMIS/PKG NO. 318719
SHEET 17 OF 99

4/17/2026 Young, Gregory C:\Users\gryoung\DC\ACCDocs\HDR\10350545_NPS_GRCA_N_Rim_Utility_2022\Project Files\CAD_HDR\DRAWINGS\GEN\002-C000.dwg