



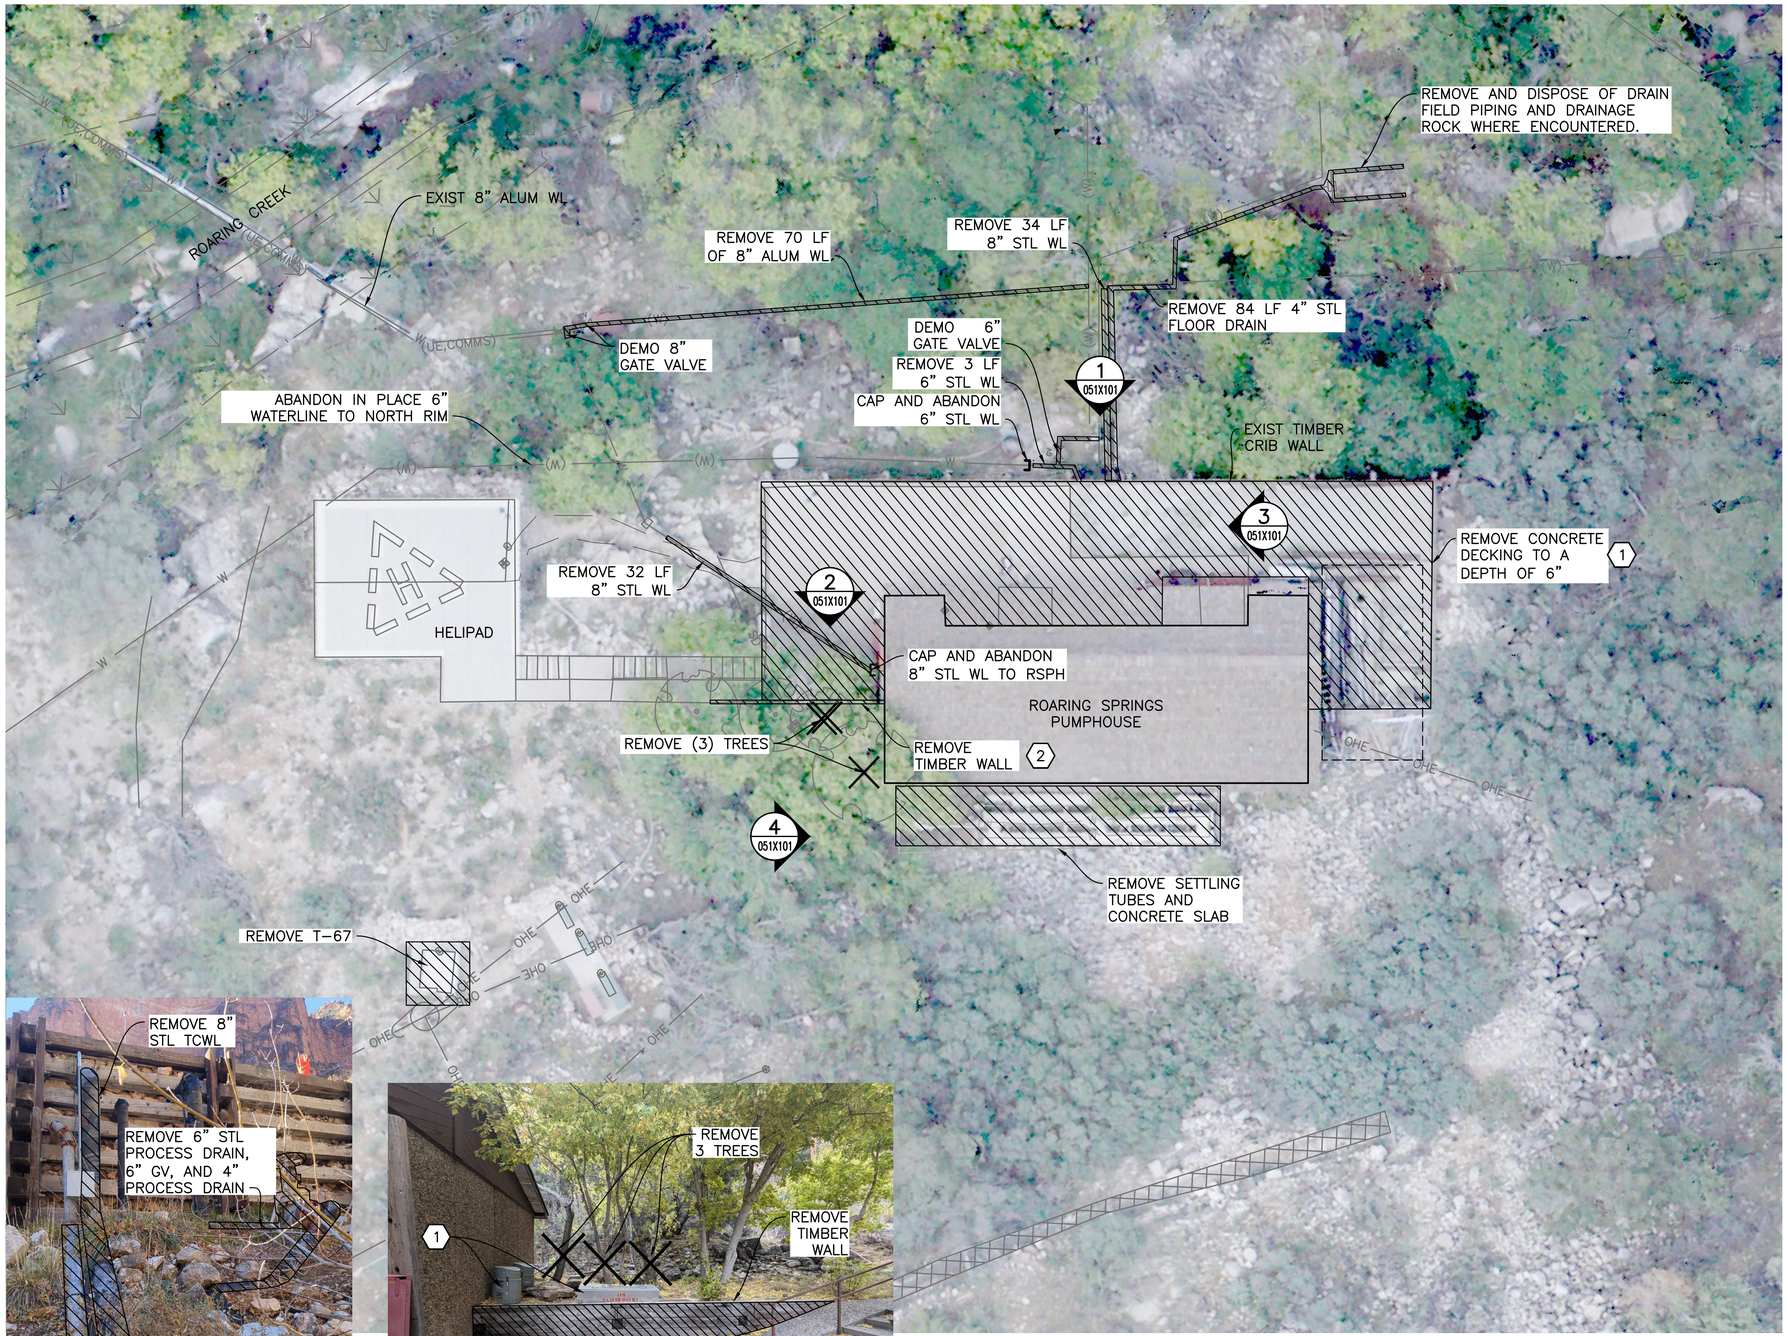

1 051X101 CRIB WALL YARD PIPING
NOT TO SCALE

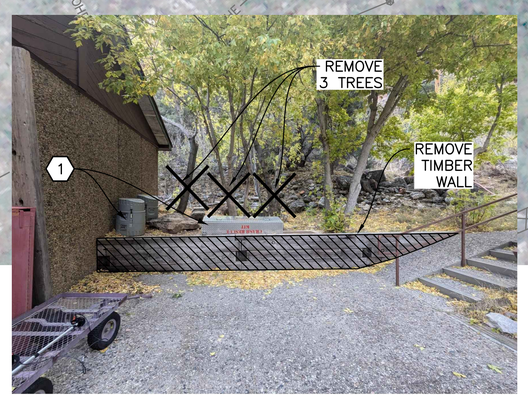

2 051X101 TIMBER WALL
NOT TO SCALE

GENERAL NOTES:

A. UPON REMOVAL OF CONCRETE SLAB AND SURFACE GRAVEL, EXPOSED PORTIONS OF TIMBER CRIB WALL SHALL BE SUBJECT TO INSPECTION BY COR.

B. CONTRACTOR TO RELOCATE ROCK/RIPRAP THAT HAS SETTLED BEYOND TOE OF SLOPE BEHIND RSPH. DISTRIBUTE ROCK/RIP-RAP WITHIN LIMITS OF SLOPE STABILIZATION. SEE SHEET 051C401.

C. MATERIALS REMOVED SHALL BE DISPOSED OF AT CONTRACTORS EXPENSE.

KEYNOTES: (X)

1. CONTRACTOR TO RELOCATE AND STORE DECKING SURFACE OF ANY MATERIAL OR EQUIPMENT PRIOR TO REMOVAL OF CONCRETE SLAB. COORDINATE TEMPORARY AND FINAL STORAGE LOCATIONS WITH COR.

2. CONTRACTOR WILL COORDINATE EQUIPMENT RELOCATION WITH CO.



3 051X101 CONCRETE SLAB
NOT TO SCALE



4 051X101 SETTLING TUBES
NOT TO SCALE

10 0 10 20
SCALE OF FEET
1" = 10'

Registered Professional Engineer (Civil) CERTIFICATE No. 76139 NICHOLAS HUMPHREY 5-1-2026 Date Signed ARIZONA, U.S.A.
Nicholas Humphrey

A/E FIRM PRIME: HDR ENGINEERING, INC. DENVER, CO 80202	DESIGNED: S. RACE CADD C. WITTENMEIER TECH. REVIEW: GOUGH/GLOVER DATE: MAY 2026	SUB SHEET NO. 051 X101	TITLE OF SHEET SITEWORK DEMOLITION PLAN NORTH RIM - GRAND CANYON NATIONAL PARK	DRAWING NO. 113 182752 PMIS/PKG NO. 318719 SHEET 10 OF 113

4/17/2026 Willyard, Lisa C:\Users\LWILLYARD\DC\ACCDocs\HDR\10350545_NPS_GRCA_N_Rim_Utility_2026\Project Files\CAD_HDR\DRAWINGS\CIVIL\051-X101.dwg