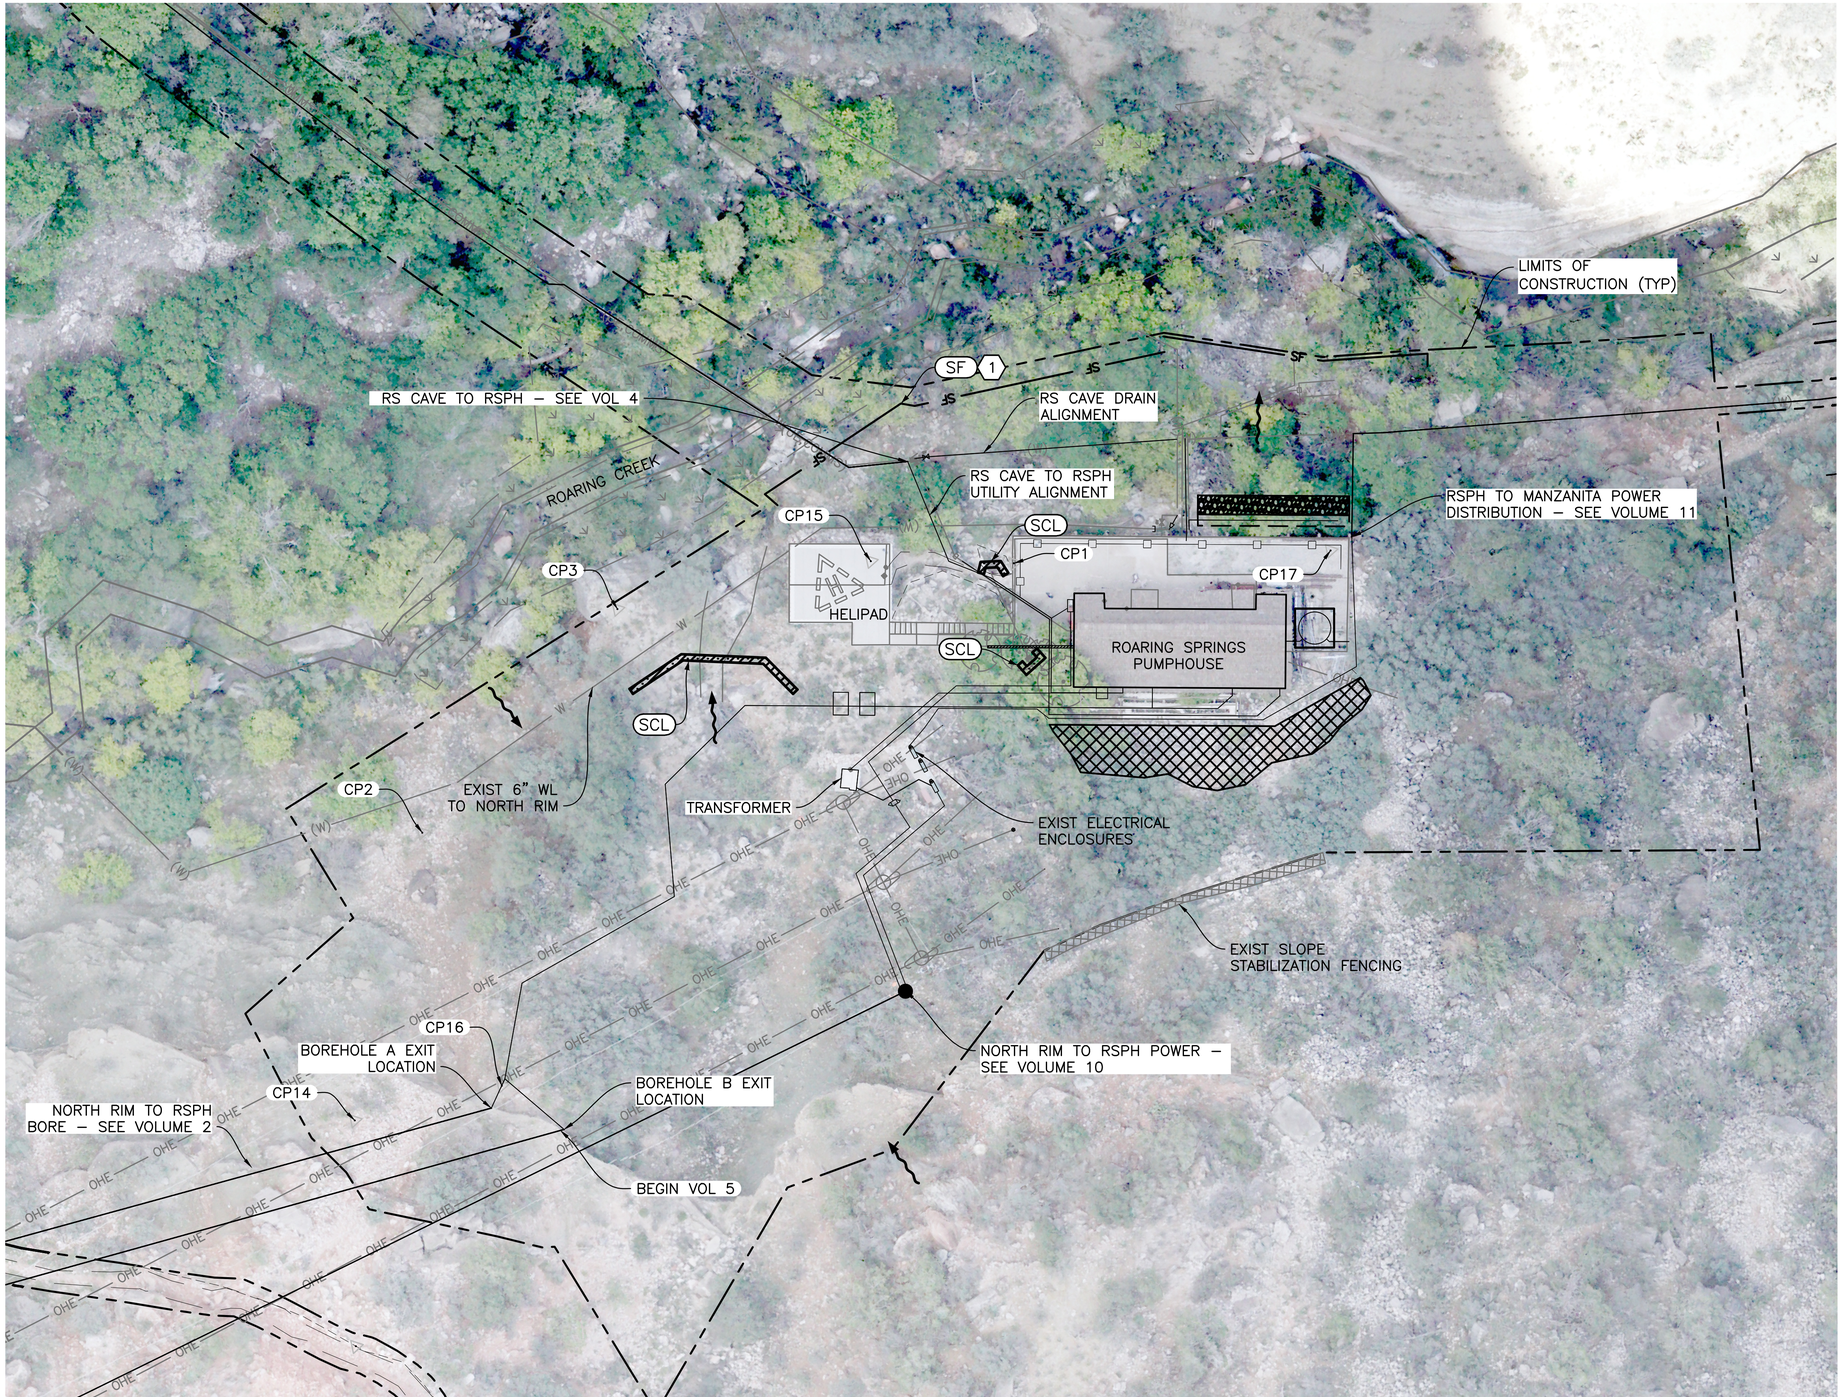

GENERAL NOTES:

A. FOR EROSION CONTROL NOTES AND DETAILS SEE VOLUME 0 SHEETS 002C507 – 002C509.

B. SURVEY CONTROL AND CONTROL POINT (CP) TABLE LOCATED IN VOLUME 0 SHEET 002C105.

KEY NOTES: (X)

1. SILT FENCE
   1.1. QUANTITY = 119 LF (VOLUME 5 TOTAL)

2. SEDIMENT CONTROL LOG
   2.1. QUANTITY = 95 LF (VOLUME 5 TOTAL)

LEGEND:

(SF) — SF — SILT FENCE. SEE VOLUME 0, 01/002C509

(SCL) — SEDIMENT CONTROL LOG VOLUME 0, 05/002C509

FLOW ARROW

20 0 20 40
SCALE OF FEET
1" = 20'

Registered Professional Engineer (Civil) CERTIFICATE NO. 76139 NICHOLAS HUMPHREY 10-9-2026 Date Signed ARIZONA, U.S.A.
Nicholas Humphrey

A/E FIRM PRIME: HDR ENGINEERING, INC. DENVER, CO 80202	DESIGNED: S. RACE CADD C. WITTENMEIER TECH. REVIEW: GOUGH/GLOVER DATE: JUNE 2026	SUB SHEET NO. 051 C101	TITLE OF SHEET SITEWORK GESC PLAN NORTH RIM - GRAND CANYON NATIONAL PARK	DRAWING NO. 113 182752 PMIS/PKG NO. 318719 SHEET 11 OF 113

10/12/2026 Green, Jake C:\Users\jgreen\DC\ACCDocs\HDR\10350545_NPS_GRCA_N_Rim_Utility_2022\Project Files\CAD_HDR\DRAWINGS\CIVIL\051-C101.dwg