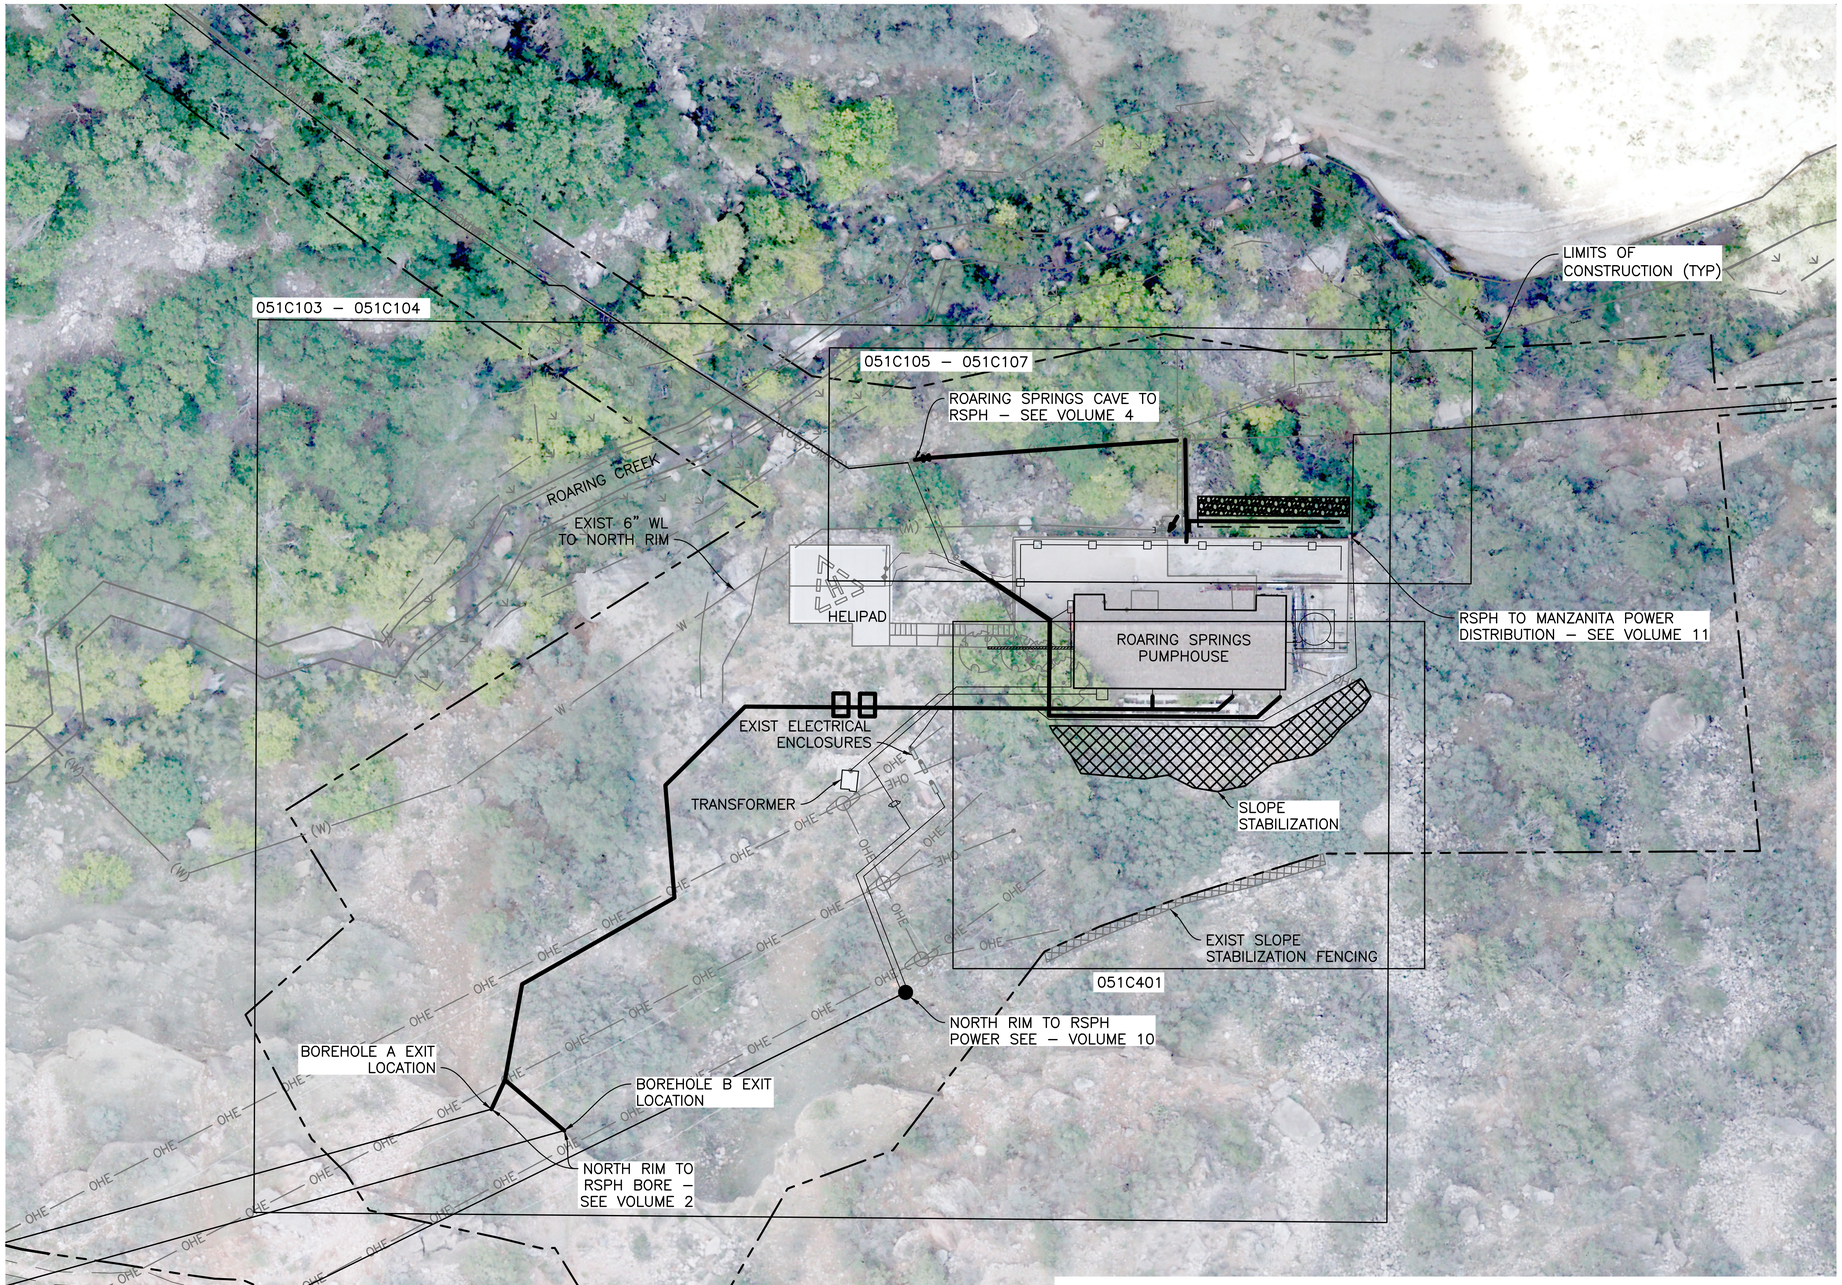

GENERAL NOTES:

A. ALL EQUIPMENT WILL NEED TO BE FLOWN INTO THE JOBSITE AREA.

20 0 20 40

SCALE OF FEET
1" = 20'

Registered Professional Engineer (Civil) CERTIFICATE NO. 76139 NICHOLAS HUMPHREY 10-9-2026 Date Signed ARIZONA, U.S.A.

Nicholas Humphrey

A/E FIRM PRIME: HDR ENGINEERING, INC. DENVER, CO 80202	DESIGNED: S. RACE CADD C. WITTENMEIER TECH. REVIEW: GOUGH/GLOVER DATE: JUNE 2026	SUB SHEET NO. 051 C102	TITLE OF SHEET SITEWORK CIVIL SHEET MAP NORTH RIM - GRAND CANYON NATIONAL PARK	DRAWING NO. 113 182752 PMIS/PKG NO. 318719 SHEET 12 OF 113

10/12/2026 Green, Jake C:\Users\jagreen\DC\ACCDocs\HDR\10350545_NPS_GRCA_N_Rim_Utility_2022\Project Files\CAD_HDR\DRAWINGS\CIVIL\051-C102.dwg