
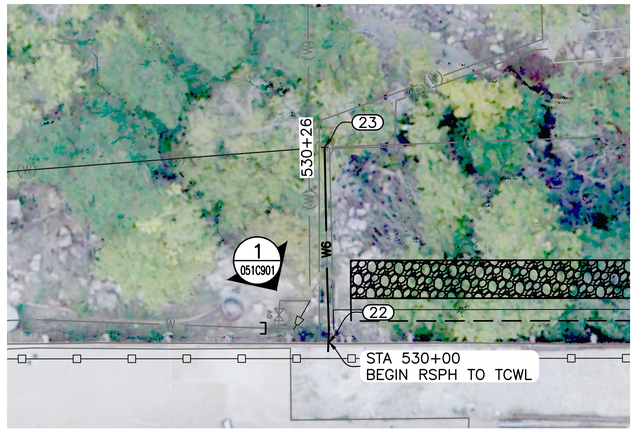


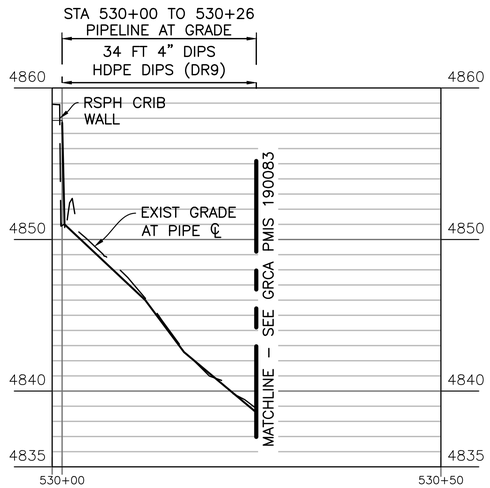

PROFILE D – TCWL CONNECTION PROFILE

WATERLINE FITTING TABLE – TCWL CONNECTION			
POINT NO.	NORTHING	EASTING	DESCRIPTION
22	13142718.08	1335432.01	INTERCEPT SLIPLINE W/ 3"x4" REDUCER AND REPLACE EXIST 8" TCWL WITH 4" HDPE
23	13142737.62	1335449.07	CONNECT TO TCWL

GENERAL NOTES:

A. AVAILABLE CONSTRUCTION WIDTH IS INTENDED TO DEFINE THE LIMITS OF CONSTRUCTION CONSIDERING SITE TOPOGRAPHY, INCLUDING TRAIL WIDTH, AND MAXIMUM ALLOWABLE DISTURBANCE.

B. LENGTHS OF PIPE SHOWN IN PROFILE REFLECT CALCULATED SLOPE LENGTH.

10 0 10 20 HORIZ.
5 0 5 10 VERT.
SCALE OF FEET
H: 1" = 10' V: 1" = 5'

Registered Professional Engineer (Civil) CERTIFICATE NO. 76139 NICHOLAS HUMPHREY 10-9-2026 Date Signed ARIZONA, U.S.A.

Nicholas Humphrey

A/E FIRM	DESIGNED:	SUB SHEET NO.	TITLE OF SHEET	DRAWING NO.
PRIME: HDR ENGINEERING, INC. DENVER, CO 80202	S. RACE CADD C. WITTENMEIER TECH. REVIEW: GOUGH/GLOVER DATE: JUNE 2026	051 C106	SITEWORK PLAN AND PROFILE D NORTH RIM - GRAND CANYON NATIONAL PARK	113 182752 PMIS/PKG NO. 318719 SHEET 16 OF 113

10/12/2026 Green, Jake C:\Users\jagreen\DC\ACCDocs\HDR\10350545_NPS_GRCA_N_Rim_Utility_2022\Project Files\CAD_HDR\DRAWINGS\CIVIL\051-C106.dwg