

GENERAL NOTES:

A. CONTRACTOR TO FIELD VERIFY CONNECTION TO EXISTING FLOOR DRAIN AT DECK.

B. PROTECT IN PLACE EXIST TCWL.

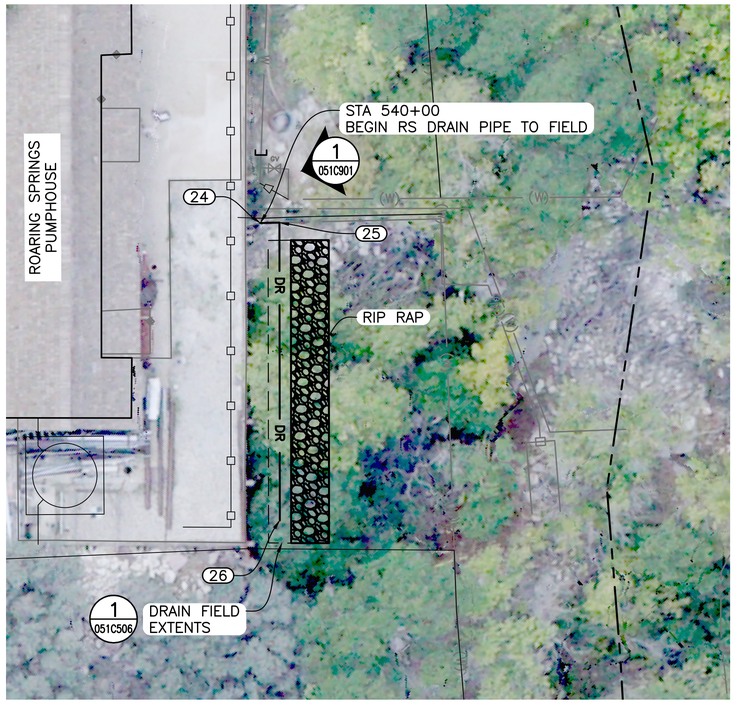

WATERLINE FITTING TABLE			
POINT NO.	NORTHING	EASTING	DESCRIPTION
24	13142719.04	1335433.91	CONNECT TO FLOOR DRAIN AT EXISTING MECH JOINT.
25	13142720.95	1335435.54	4" 90° BEND
26	13142694.66	1335464.71	4" 90° BEND

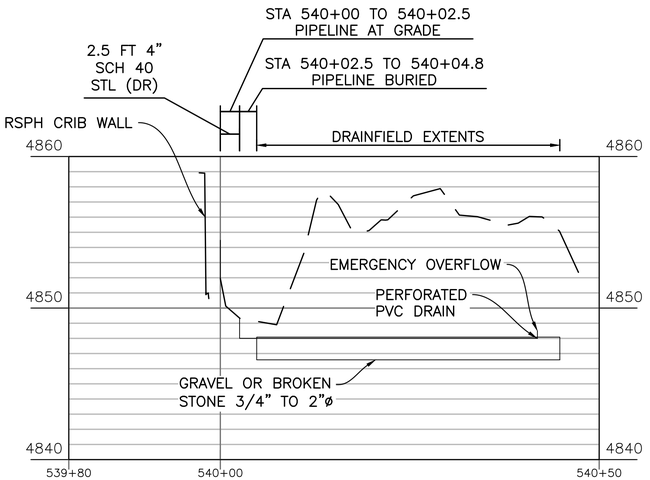

PROFILE E – RS DRAIN FIELD

10 0 10 20 HORIZ.
5 0 5 10 VERT.
SCALE OF FEET
H:1" = 10' V:1" = 5'

Registered Professional Engineer (Civil) CERTIFICATE NO. 76139 NICHOLAS HUMPHREY 10-9-2026 Date Signed ARIZONA, U.S.A.
Nicholas Humphrey

A/E FIRM PRIME: HDR ENGINEERING, INC. DENVER, CO 80202	DESIGNED: S. RACE DRAWN: T. MCCALLAN TECH. REVIEW: GOUGH/GLOVER DATE: JUNE 2026	SUB SHEET NO. 051 C107	TITLE OF SHEET SITEWORK PLAN AND PROFILE E NORTH RIM - GRAND CANYON NATIONAL PARK	DRAWING NO. 113 182752 PMIS/PKG NO. 318719 SHEET 17 OF 113

10/13/2026 Green, Jake C:\Users\jagreen\DC\ACCDocs\HDR\10350545_NPS_GRCA_N_Rim_Utility_2022\Project Files\CAD_HDR\DRAWINGS\CIVIL\051-C107.dwg