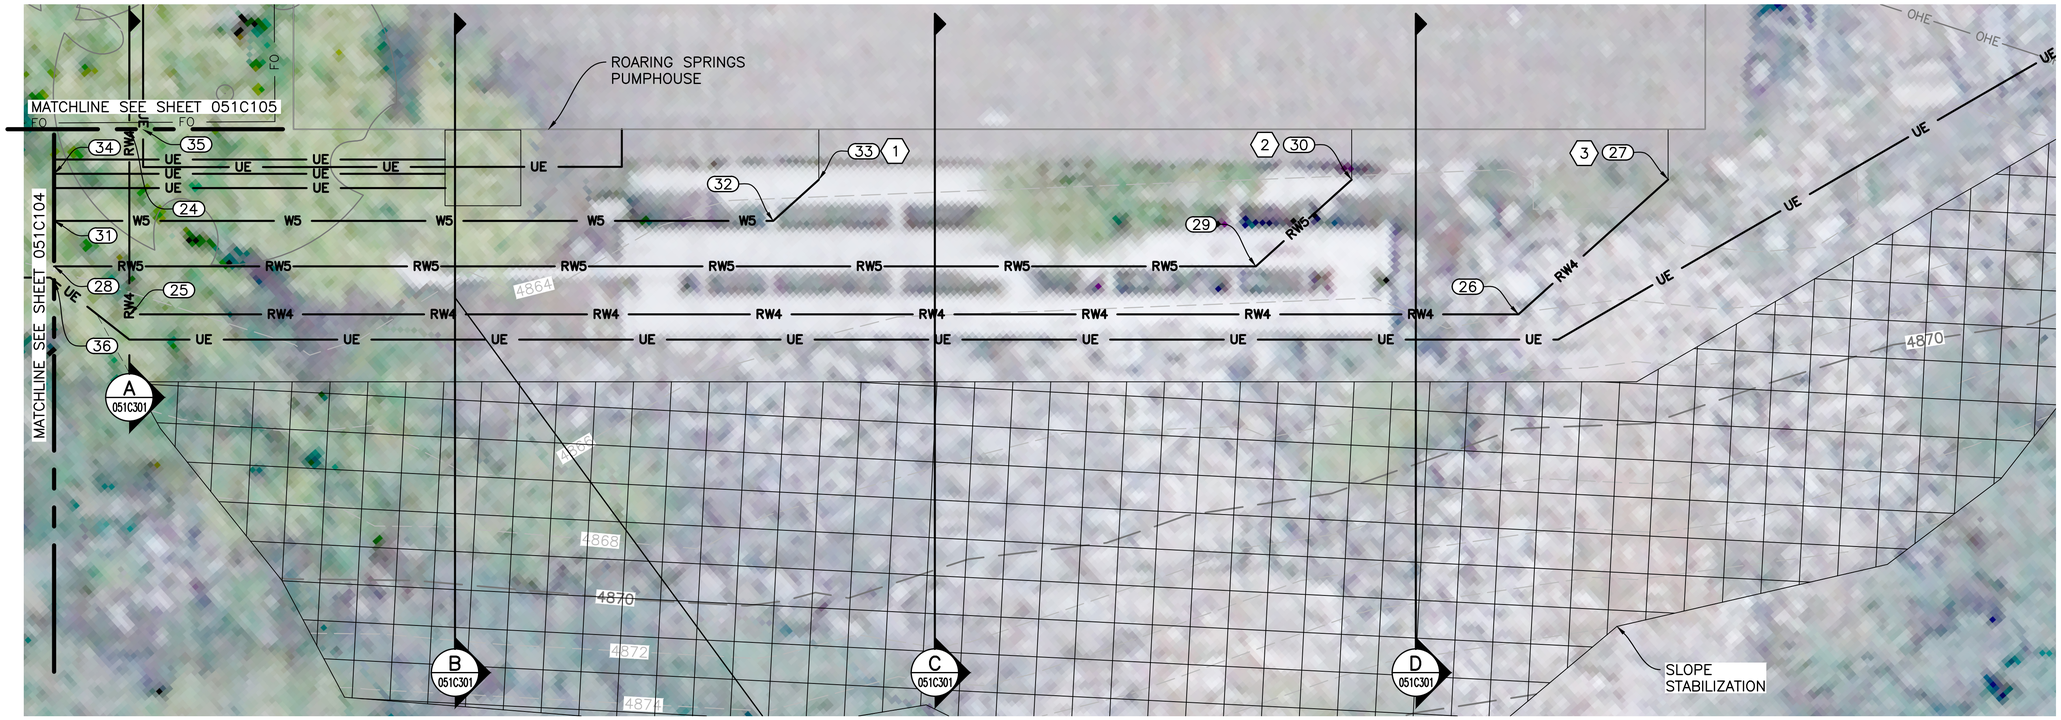

GENERAL NOTES:

A. RSPH PROCESS PIPING (SEE SPECIFICATION DIVISION 40) EXTENDS 2–FT FROM OUTSIDE WALL OF BUILDING. REFER TO SPECIFICATION DIVISION 33 FOR ALL OTHER PIPING OUTSIDE BUILDING.

KEY NOTES: (X)

1. CONNECT 2" W5 DISTRIBUTION PIPING TO RSPH PROCESS PIPING. INV = 4860.36 SEE SHEET 052D101.
2. CONNECT TO 4" RW5 DISTRIBUTION PIPING TO RSPH PROCESS PIPING. INV = 4861.8. SEE SHEET 052D101.
3. CONNECT 4" RW4 DISTRIBUTION PIPING TO RSPH PROCESS PIPING. INV = 4861.05 SEE SHEET 052D101.

WATERLINE FITTING TABLE

POINT NO.	NORTHING	EASTING	DESCRIPTION
24	13142712.64	1335378.65	BEGIN 72 LF 4" SCH 40 STL, FROM RS CAVE
25	13142707.23	1335373.74	4" 90 DEG BEND, SCH 40 STL
26	13142670.34	1335414.55	4" 45 DEG BEND, SCH 40 STL
27	13142670.33	1335422.52	4" 90 DEG VERT BEND (ROTATED), SCH 40 STL. CONNECT TO PROCESS PIPING (RW4), END RS CAVE TO RSPH
28	13142710.63	1335372.80	BEGIN 55 LF 4" SCH 80 STL, FROM RSPH
29	13142678.73	1335408.10	4" 45 DEG BEND, SCH 40 STL
30	13142678.73	1335413.22	4" 90 DEG VERT BEND (ROTATED), SCH 80 STL. CONNECT TO PROCESS PIPING (RW5), END RSPH TO BORE
31	13142711.97	1335374.01	BEGIN 33 LF 2" SCH 80 STL, FROM BORE
32	13142692.87	1335395.14	2" 45 DEG BEND, SCH 80 STL
33	13142692.87	1335397.57	2" 90 DEG VERT BEND (ROTATED), SCH 80 STL. CONNECT TO PROCESS PIPING (W5), END BORE TO RSPH
34	13142713.35	1335375.26	POWER TO RSPH
35	13142712.28	1335379.05	POWER TO CAVE
36	13142710.21	1335372.42	ARMORED 3PH POWER TO MANZANITA

3 0 3 6 HORIZ.
SCALE OF FEET
1" = 3'

Registered Professional Engineer (Civil) CERTIFICATE NO. 76139 NICHOLAS HUMPHREY 10-9-2026 Date Signed ARIZONA, U.S.A.

A/E FIRM PRIME: HDR ENGINEERING, INC. DENVER, CO 80202	DESIGNED: S. RACE DRAWN: C. WITTENMEIER TECH. REVIEW: J.GOUGH/GLOVER DATE: JUNE 2026	SUB SHEET NO. 051 C108	TITLE OF SHEET SITEWORK RSPH UTILITY CORRIDOR ENLARGED PLAN NORTH RIM - GRAND CANYON NATIONAL PARK	DRAWING NO. 113 182752 PMIS/PKG NO. 318719 SHEET 18 OF 113

10/13/2026 Green, Jake C:\Users\jgreen\DC\ACCDocs\HDR\10350545_NPS_GRCA_N_Rim_Utility_2022\Project Files\CAD_HDR\DRAWINGS\CIVIL\051-C108.dwg

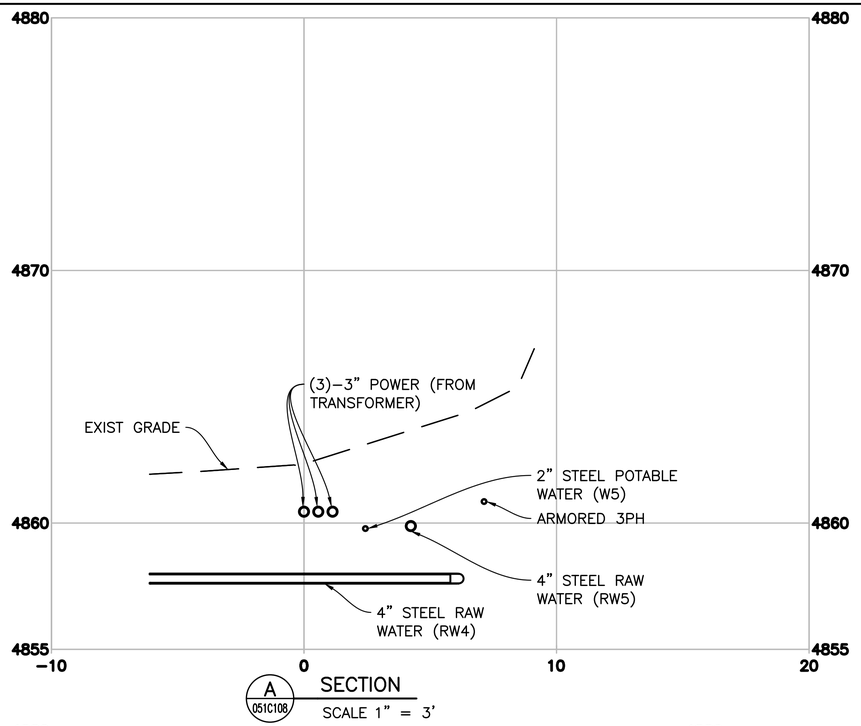

A 051C108 SECTION
SCALE 1" = 3'

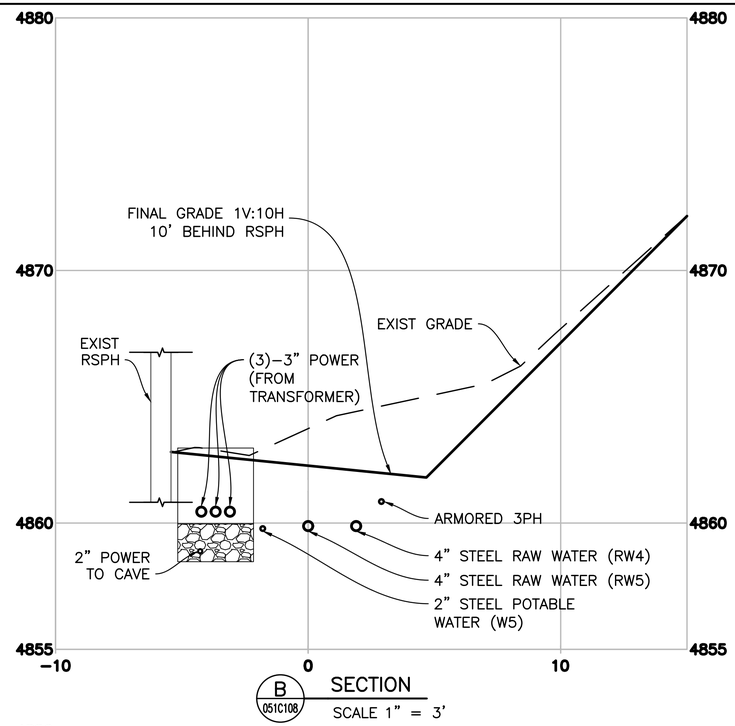

B 051C108 SECTION
SCALE 1" = 3'

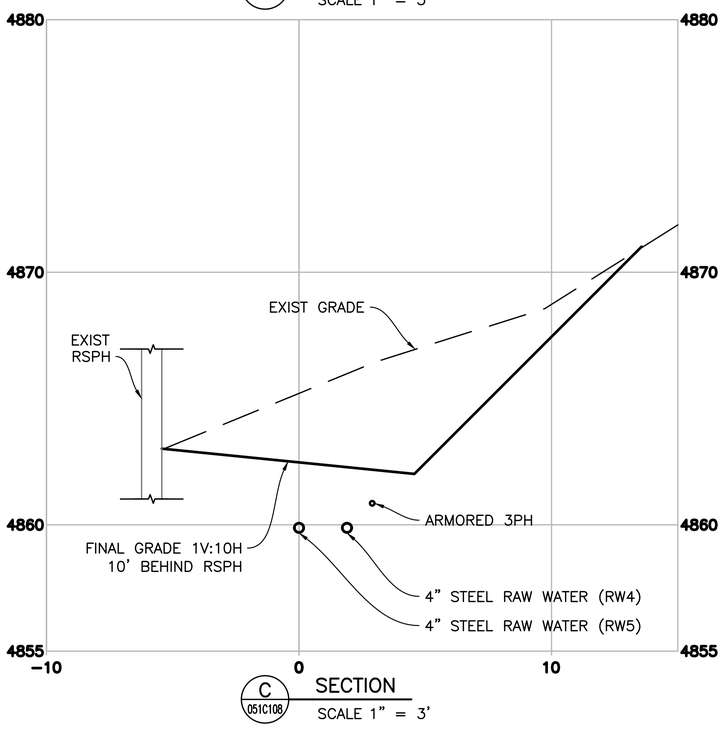

C 051C108 SECTION
SCALE 1" = 3'

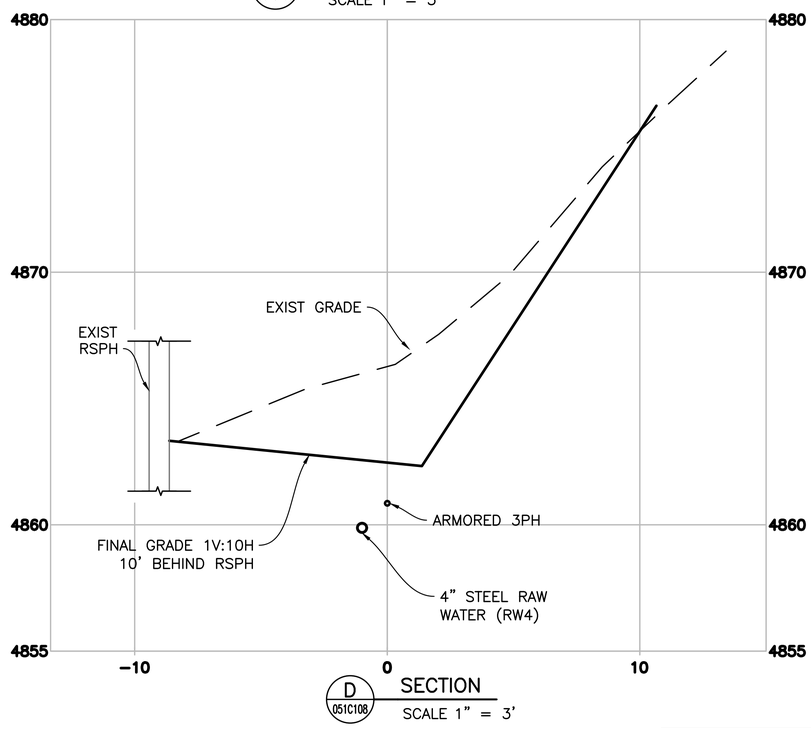

D 051C108 SECTION
SCALE 1" = 3'

3 0 3 6 HORIZ.
3 0 3 6 VERT.
SCALE OF FEET
H:1" = 3' V:1" = 3'

Registered Professional Engineer (Civil)
CERTIFICATE NO.
76139
NICHOLAS HUMPHREY
Date Signed 12-9-2025
ARIZONA, U.S.A.
Nicholas Humphrey

A/E FIRM PRIME: HDR ENGINEERING, INC. DENVER, CO 80202	DESIGNED: S. RACE CADD C. WITTENMEIER TECH. REVIEW: GOUGH/GLOVER DATE: JUNE 2026	SUB SHEET NO. 051 C301	TITLE OF SHEET SITEWORK RSPH UTILITY SECTIONS NORTH RIM - GRAND CANYON NATIONAL PARK	DRAWING NO. 113 182752 PMIS/PKG NO. 318719 SHEET 19 OF 113

10/12/2026 Green, Jake C:\Users\jagreen\DC\ACCDocs\HDR\10350545_NPS_GRCA_N_Rim_Utility_2022\Project Files\CAD_HDR\DRAWINGS\CIVIL\051-C301.dwg