National Park Service

EXPERIENCE YOUR AMERICA

Rehabilitate 4 Lazy F Ranch for Housing

GRTE 237343

Solicitation Number 140P2026R0098





Pre-Proposal Conference/Site Visit

October 29, 2026

EXPERIENCE YOUR AMERICA

AGENDA

9:00 to 10:00

- Introductions / Sign In
- Project Overview
- Contract Overview

10:15 to TBD - Site Walk






EXPERIENCE YOUR AMERICA


INTRODUCTIONS

- Tony Jasper Contracting Officer - NPS Denver Service Center
- Crissy Roe, Project Manager - NPS DSC
- Alex Thibadoux, Project Manager - GRTE
- Joel Holtrop, Project Specialist - NPS DSC
- NPS GRTE Staff
- Participants

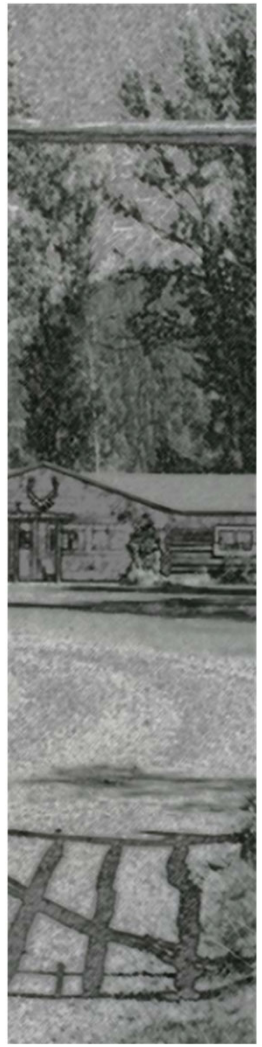

TODAY'S GOAL

- Provide offerors an opportunity to gain a better understanding of the project and the proposal submission/evaluation process.
- Provide potential offerors an opportunity for a thorough site investigation.
- Questions are encouraged. Any unanswered questions to be submitted formally to Contracting Officer

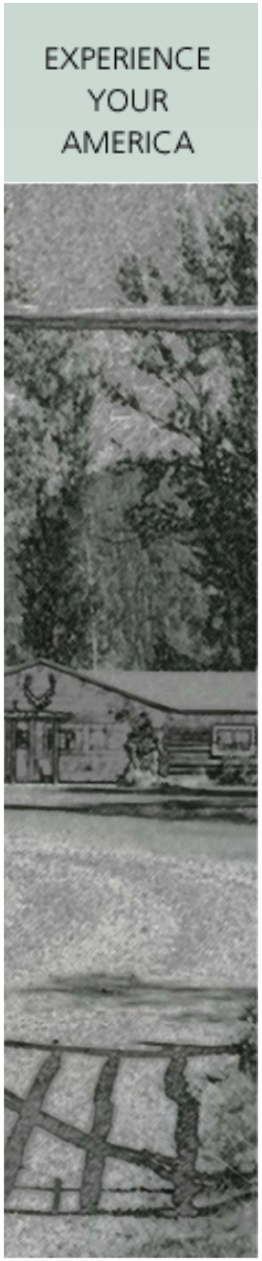

National Park Service

EXPERIENCE YOUR AMERICA

HISTORY

- 1914 Homestead - Bryant Mears
- 1927 4 Lazy F - William Frew



Figure 6. Front of the Lodge, probably 1980s. Note the climbing vine at each corner of the porch and the elk antlers nailed to the roof truss. Source: Collection of the Jackson Hole Historical Society and Museum, Jackson, Wyoming [1989.2293.001].



Figure 5. Looking northwest over the casting pond. Harry's Cabin (HS-410) visible beyond the pond. Source: Collection of the Jackson Hole Historical Society and Museum, Jackson, Wyoming [1989.2268.001].



Figure 1. Emily Frew on the porch of a cabin, probably at the Bar B C in 1926. Source: Collection of the Jackson Hole Historical Society and Museum, Jackson, Wyoming [C1.004.h 1958.1801.001].



Figure 3. Looking northwest towards the south and east walls of the Lodge, soon after completion. Collection of the Jackson Hole Historical Society and Museum, Jackson, Wyoming [1958.2031.01].



Figure 2. Looking east towards the front of the Lodge nearing completion. Note the well housing in front of the building. Source: Collection of the Jackson Hole Historical Society and Museum, Jackson, Wyoming [1958.1801.01N].



EXPERIENCE YOUR AMERICA

PROJECT OVERVIEW

- General Timeline
  - Proposals - November
  - Evaluations - December
  - Award - January/February
  - Submittals - February/March
  - Construction – April
- Utilities
- Buildings and Site




EXPERIENCE YOUR AMERICA

PROJECT SCOPE


- UTILITIES: Design, permitting and construction of new water distribution system, new sewer system (a lift station, force main & gravity main) and new buried telecommunications and underground power. Scope includes connections to proximate electrical, water, sanitary, and telecommunication service at each building.



National Park Service

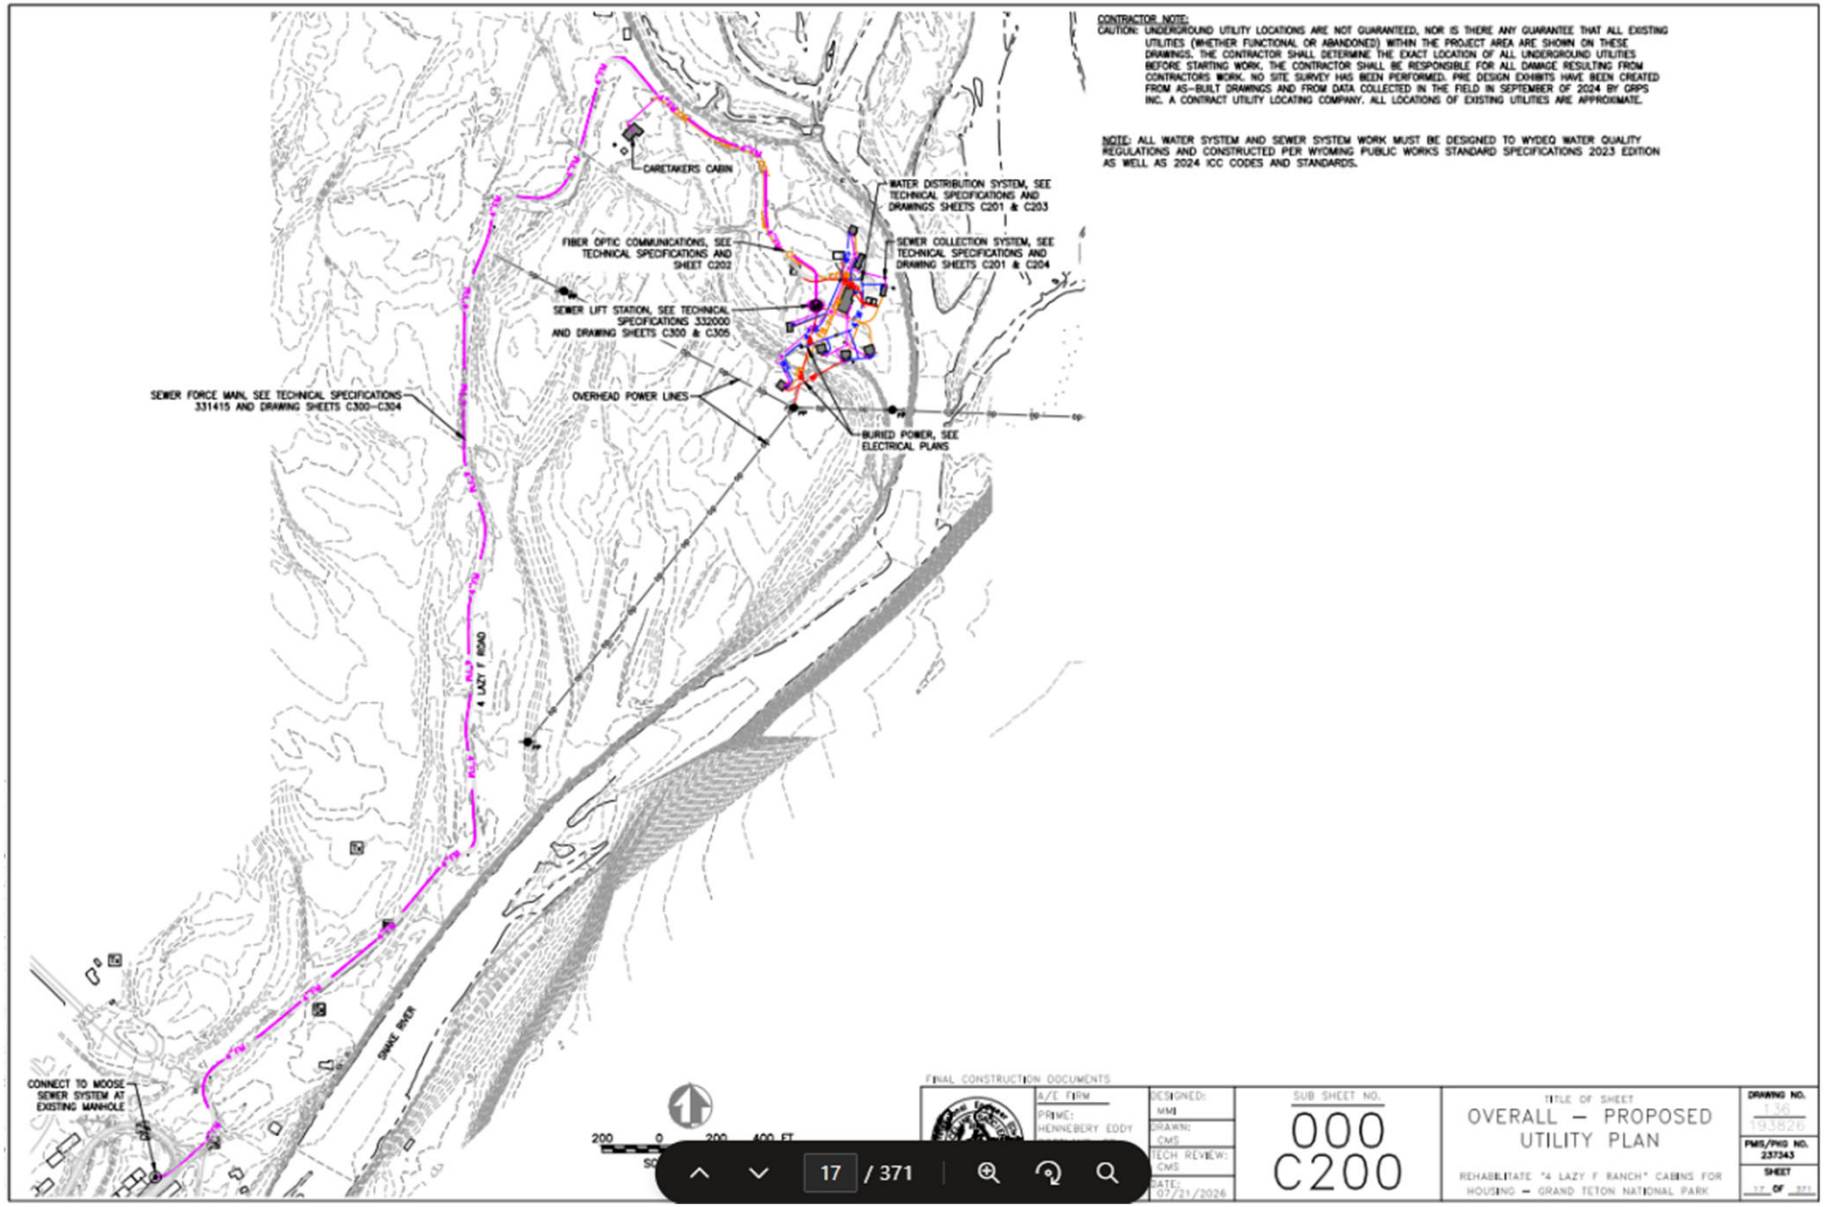

National Park Service

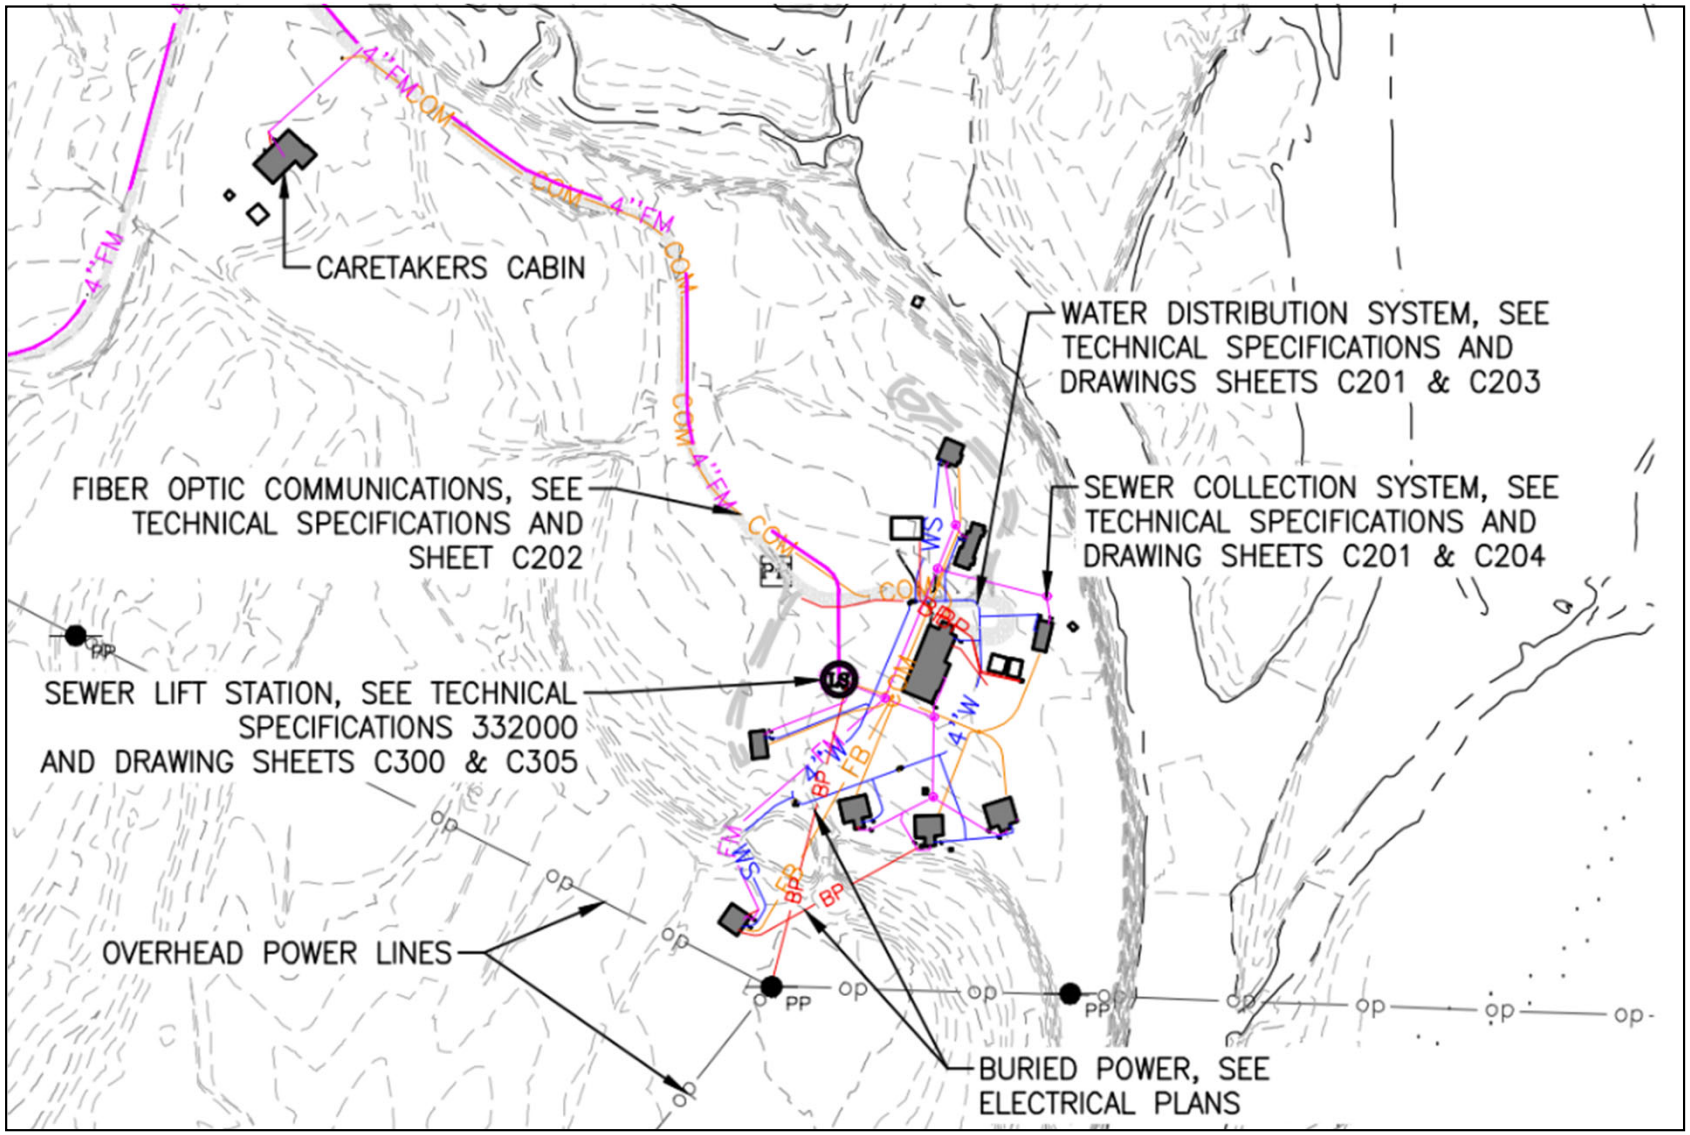


EXPERIENCE YOUR AMERICA

PROJECT SCOPE

- BUILDINGS & SITE: Rehabilitate the lodge, eight cabins, one garage, two outbuildings, and a water well structure. Scope includes roof replacement, foundation repair/replacement, structural upgrades, exterior log repairs and refurnishing, pest exclusion, historic window and door repairs, updating all building utilities to be code compliant, new fire suppression installation, and preservation work. Site work includes new parking spaces, maintaining in-kind access road, and pathway connections.



National Park Service

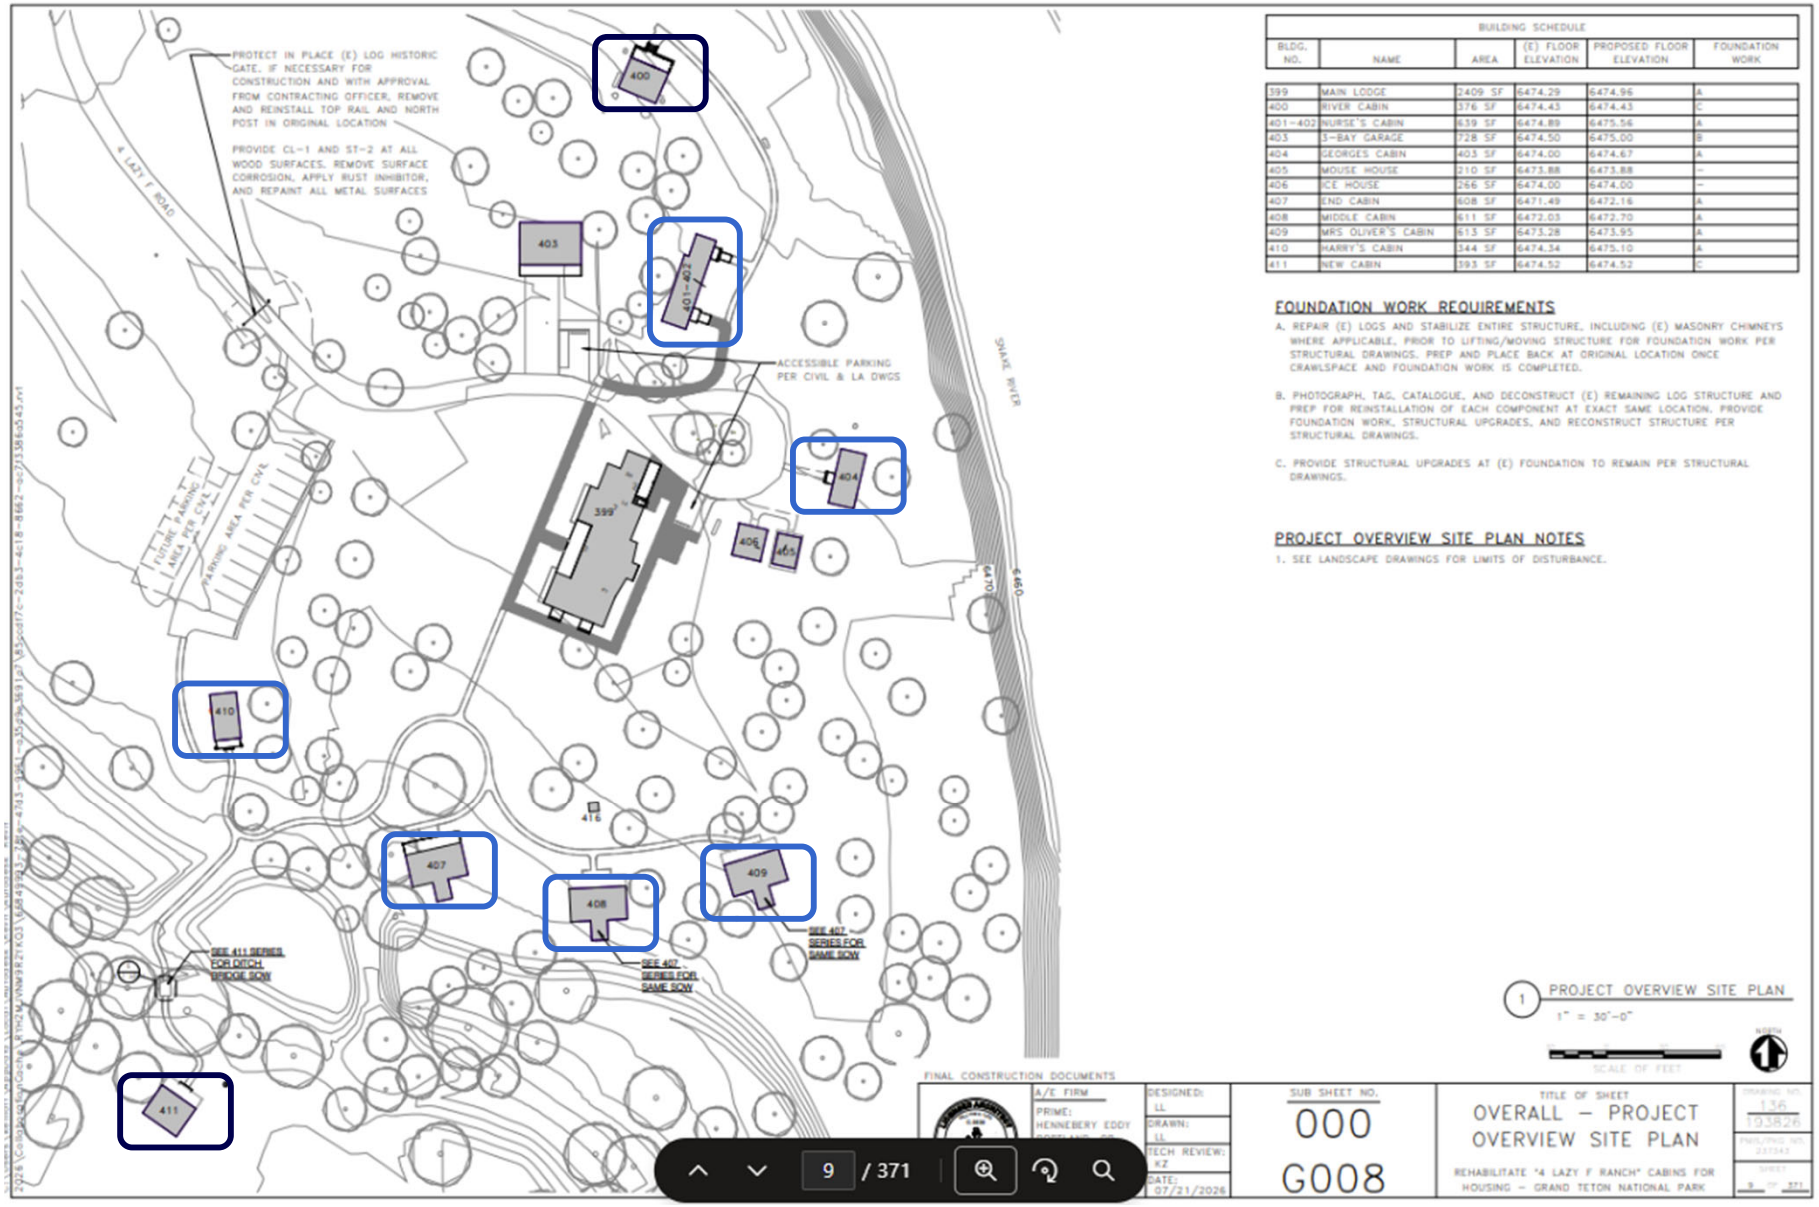

BUILDING SCHEDULE					
BLDG. NO.	NAME	AREA	(E) FLOOR ELEVATION	PROPOSED FLOOR ELEVATION	FOUNDATION WORK
399	MAIN LODGE	2409 SF	6474.29	6474.96	A
400	RIVER CABIN	576 SF	6474.43	6474.43	C
401-402	NURSE'S CABIN	639 SF	6474.89	6475.56	A
403	3-BAY GARAGE	728 SF	6474.50	6475.00	B
404	GEORGES CABIN	403 SF	6474.00	6474.67	A
405	MOUSE HOUSE	210 SF	6473.88	6473.88	–
406	ICE HOUSE	266 SF	6474.00	6474.00	–
407	END CABIN	608 SF	6471.49	6472.16	A
408	MIDDLE CABIN	611 SF	6472.03	6472.70	A
409	MRS OLIVER'S CABIN	613 SF	6473.28	6473.95	A
410	HARRY'S CABIN	344 SF	6474.34	6475.10	A
411	NEW CABIN	393 SF	6474.52	6474.52	C

FOUNDATION WORK REQUIREMENTS

A. REPAIR (E) LOGS AND STABILIZE ENTIRE STRUCTURE, INCLUDING (E) MASONRY CHIMNEYS WHERE APPLICABLE, PRIOR TO LIFTING/MOVING STRUCTURE FOR FOUNDATION WORK PER STRUCTURAL DRAWINGS. PREP AND PLACE BACK AT ORIGINAL LOCATION ONCE CRAWLSPACE AND FOUNDATION WORK IS COMPLETED.

B. PHOTOGRAPH, TAG, CATALOGUE, AND DECONSTRUCT (E) REMAINING LOG STRUCTURE AND PREP FOR REINSTALLATION OF EACH COMPONENT AT EXACT SAME LOCATION. PROVIDE FOUNDATION WORK, STRUCTURAL UPGRADES, AND RECONSTRUCT STRUCTURE PER STRUCTURAL DRAWINGS.

C. PROVIDE STRUCTURAL UPGRADES AT (E) FOUNDATION TO REMAIN PER STRUCTURAL DRAWINGS.

PROJECT OVERVIEW SITE PLAN NOTES

1. SEE LANDSCAPE DRAWINGS FOR LIMITS OF DISTURBANCE.

1 PROJECT OVERVIEW SITE PLAN
1" = 30'-0"
SCALE: 0 30' 60'

FINAL CONSTRUCTION DOCUMENTS

A/E FIRM
PRIME: HENNEBERY EDDY

DESIGNED: LL
DRAWN: LL
TECH REVIEW: KZ
DATE: 07/21/2026

SUB SHEET NO. 000 G008

TITLE OF SHEET: OVERALL – PROJECT OVERVIEW SITE PLAN

REHABILITATE "4 LAZY F RANCH" CABINS FOR HOUSING – GRAND TETON NATIONAL PARK

DRAWING NO. 136 19.38.26


PROJECT NO. 237043

SHEET 9 OF 371

National Park Service

EXPERIENCE YOUR AMERICA


DRAWING SET STRUCTURE

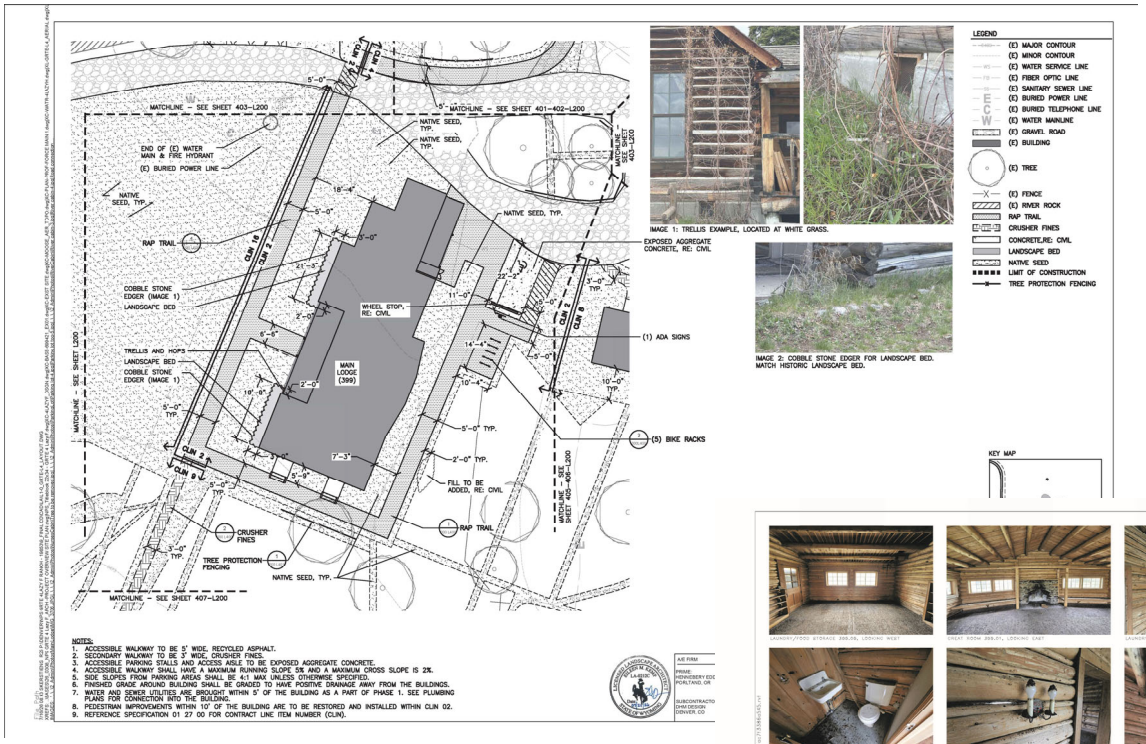






National Park Service

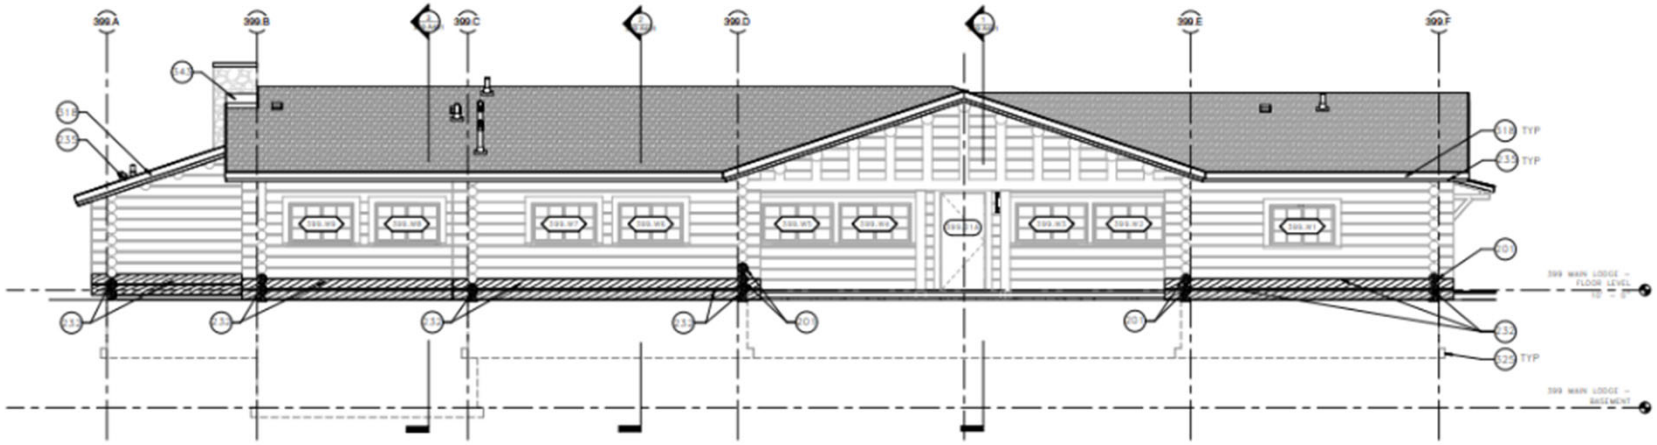

1 399 MAIN LODGE – WEST ELEVATIONS

1/4" = 1'-0"

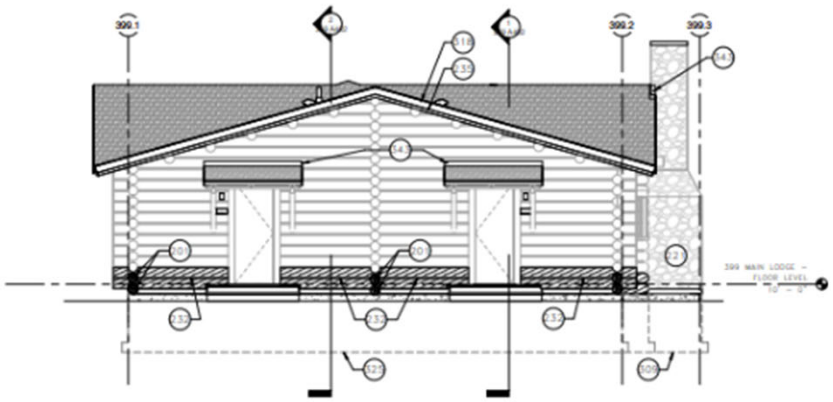

2 399 MAIN LODGE – SOUTH ELEVATIONS

1/4" = 1'-0"

EXTERIOR ELEVATION LEGEND

NOTE: NOT ALL ITEMS MAY BE USED

- (E) LOG OR LOG SIDING WALL
- LOG OR LOG SIDING TO MATCH (E)
- (E) BOARD & BATTEN SIDING
- BOARD & BATTEN SIDING
- ROOFING
- WINDOW TAG
- (E) RIVER ROCK CHIMNEY
- KEYNOTE TAG

KEYNOTES

201 LOG DUTCHMAN REPAIR
221 RESTORE (E) CHIMNEY BOTH INSIDE AND OUT
232 REPLACE DETERIORATED LOG
235 REPLACE (E) WOOD FASCIA
309 PROVIDE CONCRETE PAD FOOTING PER STRUCTURAL
318 PROVIDE SECONDARY WOOD FASCIA
325 PROVIDE FOUNDATION WALL AND FOOTING PER STRUCTURAL
343 SM FLASHING; SEE BUILDING SECTIONS AND DETAILS

EXTERIOR ELEVATION NOTES

1. SEE "000 GENERAL" SERIES FOR GENERAL INFORMATION APPLICABLE TO ALL STRUCTURES, INCLUDING GENERAL NOTES, SYMBOLS, ASSEMBLIES, AND DETAILS.
2. SEE 000 G008 FOR EXISTING VS PROPOSED FLOOR ELEVATIONS FOR EACH STRUCTURE.
3. GRADE LINES INDICATED ARE APPROXIMATE AND SHOWN FOR REFERENCE ONLY. SEE CIVIL AND LANDSCAPE DRAWINGS FOR GRADING INFORMATION.
4. LINE OF FOUNDATIONS (SHOWN DASHED OR GRAYED OUT WHERE OCCURS) ARE APPROXIMATE AND SHOWN FOR REFERENCE ONLY.
5. DIMENSIONS ARE SHOWN TO DIMENSION POINT OF REFERENCED DETAIL WHERE APPLICABLE.
6. ALIGN MATERIAL, CONTROL AND EXPANSION JOINTS VERTICALLY AND HORIZONTALLY WITH ADJACENT JOINTS AND DOOR, WINDOW AND LOUVER HEADS/JAMBS/SILLS. VERIFY DIMENSIONS WITH DETAIL CONDITIONS. VERIFY LOCATION AND ALIGNMENT WITH CONTRACTING OFFICER.
7. MOUNTING LOCATION OF DEVICES AS INDICATED ON DRAWINGS, VERIFY WITH CONTRACTING OFFICER IF NOT INDICATED.
8. COORDINATE WORK HIDDEN FROM VIEW ON EXTERIOR ELEVATIONS WITH PLAN VIEW DRAWINGS.
9. GENERAL CLEANING (CL-1) AT 100% OF EXTERIOR SURFACES.
10. BIOGROWTH CLEANING (CL-2) AT 30% OF EXTERIOR SURFACES.
11. REPAIR ALL (E) BOARD & BATTEN SIDING TO REMAIN. ASSUME 25% IN-KIND REPLACEMENT.
12. ST-2 AT 100% OF EXTERIOR LOG SURFACES; EXTERIOR BOARD & BATTEN SURFACES; WOOD DECKING/RAILING; AND EXPOSED ROOF ASSEMBLY WOOD COMPONENTS, UON.

SCALE 0 1 2 4 8 SCALE OF FEET

FINAL CONSTRUCTION DOCUMENTS

	A/E FIRM PRIME: HENNEBERY EDDY PORTLAND, OR	DESIGNED: LL DRAWN: LL TECH REVIEW: KZ DATE: 07/21/2026	SUB SHEET NO. 399 A301	TITLE OF SHEET MAIN LODGE – EXTERIOR ELEVATIONS REHABILITATE "4 LAZY F RANCH" CABINS FOR HOUSING – GRAND TETON NATIONAL PARK	DRAWING NO. 136 19326 PROJECT NO. 237343 SHEET 107 OF 371

EXPERIENCE YOUR AMERICA

Special Considerations

- Site Access: 1 Apr - 15 Dec (01 11 00)
  - Work hours are 8am-6pm but can vary (01 11 00 and 01 57 19.12)
- Maintain Driveway Access for Govt. Employees (01 11 00)
- Environmental/Wildlife Protections - Eagles, Migratory Bids, Sage Grouse (01 11 00) (01 35 13.05); Elk Parturition 15 May - 30 Jun
- Tree Removal Limited to Fall - October Preferred (01 35 13.05)
- Bat Exclusion (01 35 13.05) Initial 1 Apr - 15 Apr Window
  - Lodge Primary Roost (1 Apr –15 Apr)
  - Seasonal Exclusion Required (1 Oct Departure – Mid Apr Arrival)
- Government Furnished Materials
  - Windows and Screens (01 11 00)
- Communications – Local Provider Coordination (27 00 00)
  - Site (conduit and handholes provided)
  - Facilities (contractor to establish pathway
- Government Furnished Permit
  - WYDEQ is secured and to be provided to Contractor. All other permits are responsibility of the Contractor (01-31-00)



EXPERIENCE YOUR AMERICA

SOLICITATION KEY POINTS

- Released to SAM.gov on September 21st
- Procurement is being conducted as a Total Small Business Set-Aside under NAICS 237110
- Period of Performance varies based upon the exercised options
- One Firm-Fixed-Price contract will be awarded
- Source selection will be made using Best Value/Tradeoff method (see FAR 15.101-1)
- Proposals are currently due November 20th – NPS does not intend to extend beyond this date



National Park Service

CLIN	CONTRACT LINE ITEM (CLIN) TITLE	QTY	UM	UNIT PRICE	TOTAL PRICE
001A	Sitework – Sewer System	1	LS		
001B	Sitework – Water System	1	LS		
001C	Sitework – Buried Power	1	LS		
001D	Sitework – Fiber Optic Communications	1	LS		
TOTAL BASE PRICE (Contract Line-Item Number 1A through 1D)					
002	OPTION 1 - B - (HS) 399 4 Lazy F Dude Ranch Main Lodge	1	LS		
003	OPTION 2 - B - (HS) 404 4 Lazy F Dude Ranch George's Cabin	1	LS		
004	OPTION 3 - B - (HS) 409 4 Lazy F Dude Ranch Mrs. Oliver's Cabin	1	LS		
005	OPTION 4 - B - (HS) 408 4 Lazy F Dude Ranch Middle Cabin	1	LS		
006	OPTION 5 - B - (HS) 407 4 Lazy F Dude Ranch End Cabin	1	LS		
007	OPTION 6 - B - (HS) 401-402 4 Lazy F Dude Ranch Nurse's Cabin	1	LS		
008	OPTION 7 - B - (HS) 400 4 Lazy F Dude Ranch (River) Cabin	1	LS		
009	OPTION 8 - B - (HS) 410 4 Lazy F Dude Ranch Harry's Cabin	1	LS		
010	OPTION 9 - B - (HS) 411 4 Lazy F New Cabin	1	LS		
011	OPTION 10 - Sitework – Parking Lot	1	LS		
012	OPTION 11 - Sitework – Roadway and Staging Area Restoration	1	LS		
013	OPTION 12 - B - (HS) 406 4 Lazy F Dude Ranch Ice House	1	LS		
014	OPTION 13 - B - (HS) 405 4 Lazy F Dude Ranch Mouse House	1	LS		
015	OPTION 14 - B - (HS) 403 3-Bay Garage 4 Lazy F	1	LS		
016	OPTION 15 B - (HS) 416 Well House 4 Lazy F	1	LS		

EXPERIENCE YOUR AMERICA



EXPERIENCE YOUR AMERICA

Period of Performance

Base Scope: 303 Calendar Days

Base Scope plus any six CLINs: 669 Calendar Days

Base plus any seven CLINs or more: 1,034 Calendar Days



Key Solicitation Clauses

EXPERIENCE YOUR AMERICA

- Special Requirement 2 – Performance of Work by the Contractor (Must self perform at least 15% of TCV)
- Special Requirement 3 – Option for Additional Services (NPS has 120 days after award to exercise the options)
- Liquidated Damages ($1,714/day)
- Davis Bacon Wage Requirements apply. Certified payrolls are due weekly.



EXPERIENCE YOUR AMERICA

PROPOSAL INSTRUCTIONS

- Please read Section L thoroughly
- Email submissions to CO on or before 5pm ET, November 20th, 2026
  - anthony_jasper@ios.doi.gov, and CS_DSC_Proposal_Submission@nps.gov
- Make sure you verify receipt from NPS
- Pay attention to detailed page limitation requirements
- Pay attention to attachment size limitations
- Offer Guarantee/Bid Bond is required – valid for 90 days
- Please submit your proposal as two separate pdf files – Volume 1: Technical; Volume 2: Price



EXPERIENCE YOUR AMERICA

PROPOSAL EVALUATION - Basis of Award

- NPS will award a contract to the offeror who submits a proposal that conforms to solicitation requirements; offers fair and reasonable pricing; and provides the best value to the government considering all evaluation factors
- The Government may accept other than the lowest priced proposal when the perceived benefits of a higher priced proposal merit the price differential.
- All evaluation factors other than price (Factors 1-4), when combined are approximately equally important to price.
- NPS intends to award a contract **without entering into discussions**. In the event that NPS chooses to enter into discussions, a competitive range will be established and the process described under FAR 15.306 will be followed.



EXPERIENCE YOUR AMERICA

PROPOSAL CONTENTS (Technical Volume)

- Technical Volume must contain the following five sections pertaining to each evaluation factor. These are listed in descending order of importance

  Factor 1 – Technical Approach
  Factor 2 – Project Experience
  Factor 3 – Schedule
  Factor 4 – Past Performance



EXPERIENCE YOUR AMERICA

PROPOSAL CONTENTS (Technical Volume)

Factor 1 – Technical Approach: 10 page max narrative discussing your approach to this project

Factor 2 – Project Experience – up to 3 relevant projects completed or close to completion. Use Project Experience Questionnaire form attached to the solicitation

Factor 3 – Schedule: Gantt Chart format schedule with NTP of February 1st, 2027. NO NARRATIVE IS REQUIRED but project phasing should be discussed under your Technical Approach

Factor 4 – Past Performance: Past performance info for the projects submitted under Factor 2.



EXPERIENCE YOUR AMERICA

PROPOSAL CONTENTS

Volume 2 – Business and Price Proposal

- Signed SF1442
- Acknowledgement of Amendments
- Completed Contract Price Schedule
- Bid Bond
- Section K: Reps & Certs
- General References
- Proposed Substitutions
- Subcontracting Percentage Worksheet (to track required 15% self performance)



EXPERIENCE YOUR AMERICA

USE OF AI TOOLS IN PROPOSAL WRITING

- NPS does not restrict offerors in any way in using AI tools or software to assist in the proposal writing and submission process
- **Remember - Substance is everything!**



EXPERIENCE YOUR AMERICA

REMINDERS

- Questions are due to the Contracting Officer by **November 6th, 2026**. It is the Offeror's responsibility to take notes and submit questions in writing by the deadline.
- Submit questions only to Anthony_jasper@ios.doi.gov. Please do NOT reach out to the park directly or any other NPS staff other than the CO.
- Email proposals on or before **November 20, 2026**
- Solicitation and project documents are only changed with a formal amendment.



EXPERIENCE YOUR AMERICA

QUESTIONS?





Thank you for your interest in this project!

National Park Service

SITE WALK

- Parking
- Safety

