
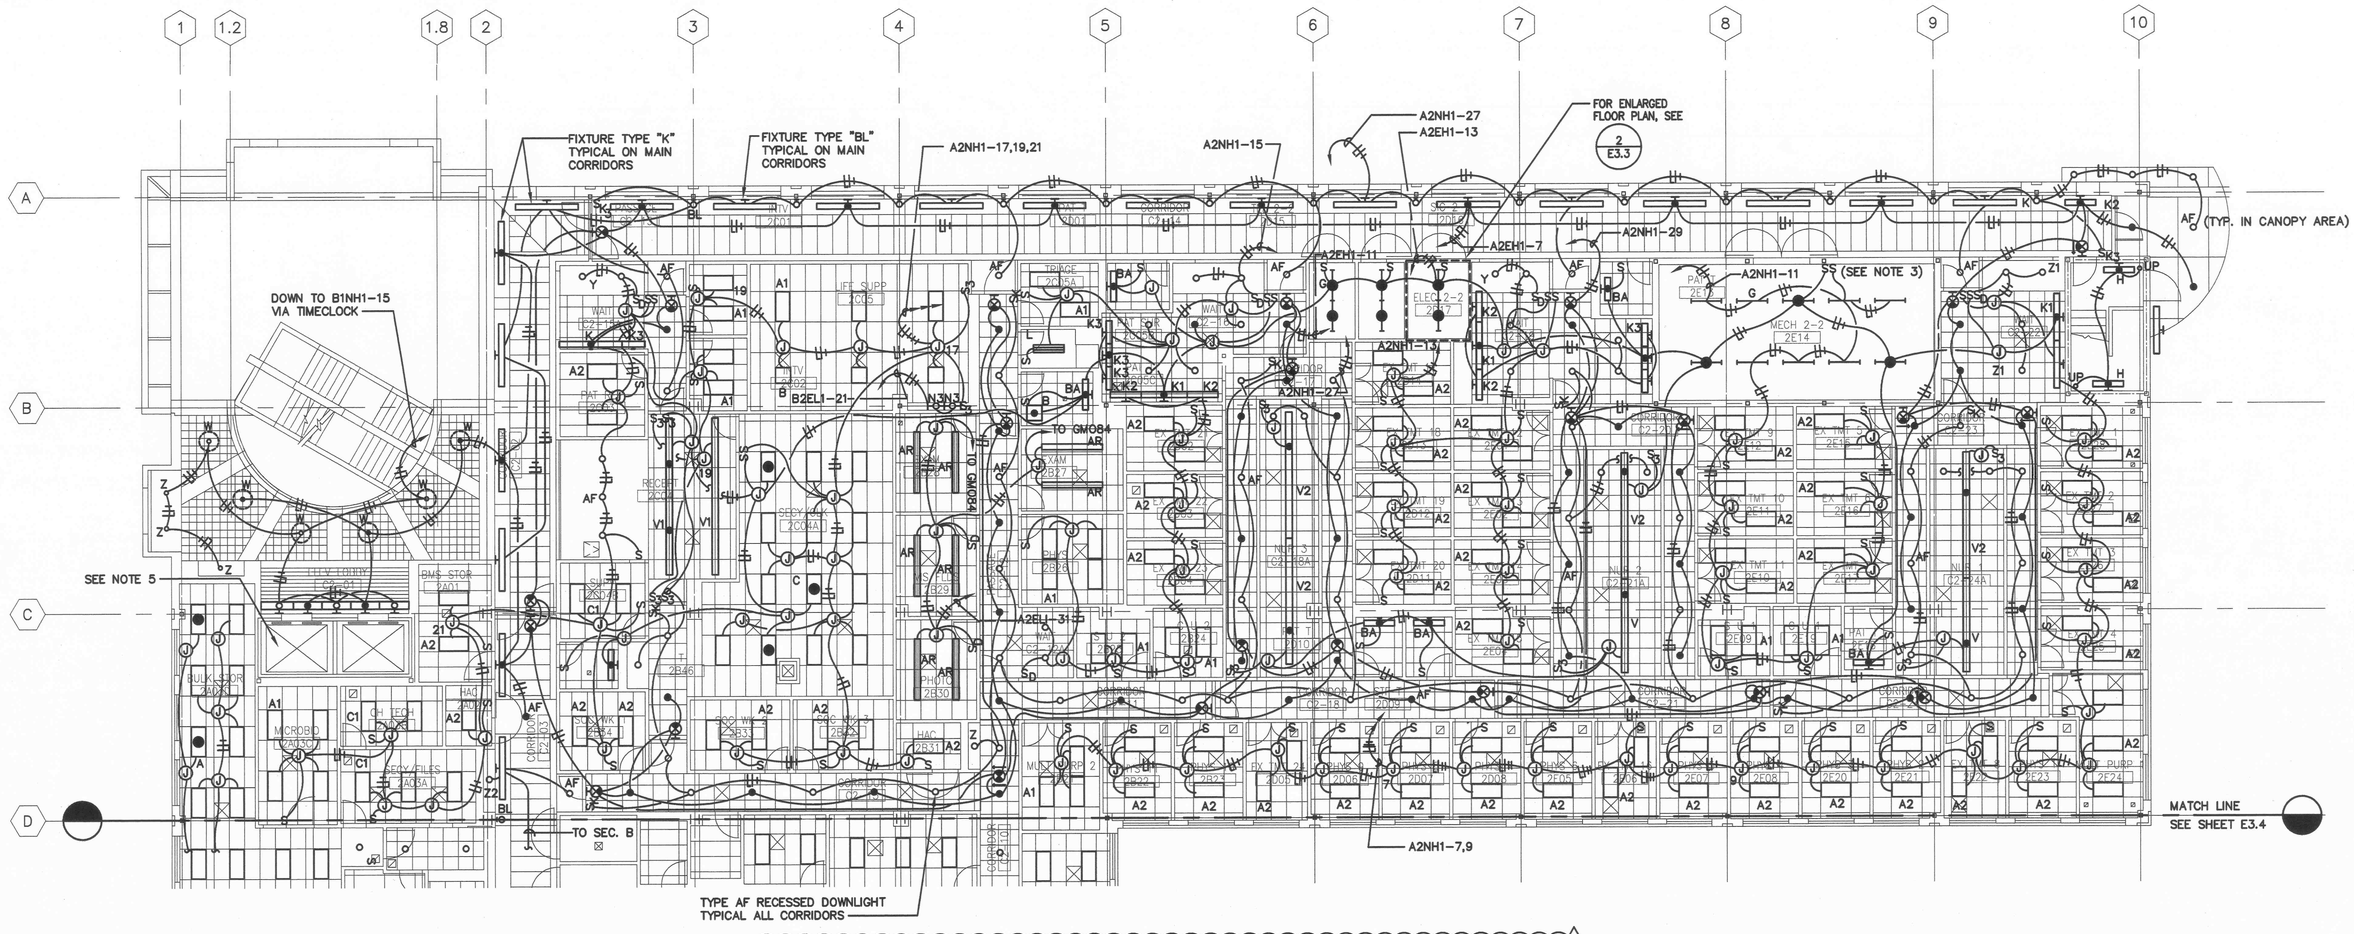


1/E3.3 PARTIAL LIGHTING PLAN - LEVEL 2 - AREA A

SCALE: 1/8" = 1'-0"


NOTES:

1. FIXTURE TYPE INDICATED IN ROOM IS TYPICAL FOR ALL LIGHT FIXTURES IN THAT ROOM.
2. A SHALLOW JUNCTION BOX (1-1/2" DEPTH) SHALL BE USED FOR MOUNTING LIGHT FIXTURE TYPE "BL" WHERE STRUCTURAL STEEL COLUMNS OCCUR.
3. COORDINATE WITH STRUCTURAL AND MECHANICAL CONTRACTORS FOR PLACEMENT OF LIGHT FIXTURES IN ELEC., MECH., AND SIGNAL ROOMS.
4. THE DIMMABLE TRACK LIGHTING IN EXAM ROOMS 2B27 AND 2B28 SHALL BE CONNECTED TO THE LUMBART INSTRUMENT CONTROL PANEL. (CONNECT TO CONNECTION POINT #5 AND INSTALL PER MANUFACTURER'S REQUIREMENTS.
5. ELEVATOR LOBBY LIGHTS-TYPE "S". FOUR (4)-4' AND ONE (1)-3' TO SPAN TOTAL LENGTH OF LOBBY.

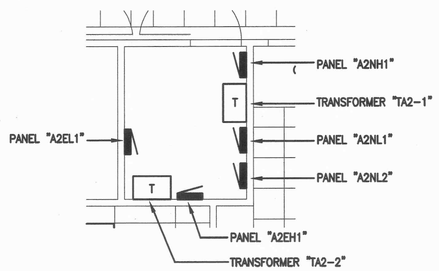

2/E3.3 ELECTRIC ROOM NO. 2-2

SCALE: 1/4" = 1'-0"

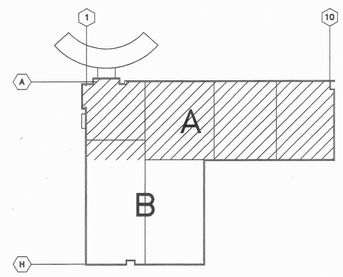

KEY PLAN
NO SCALE

N PROJECT NORTH

GRAPHIC SCALE
1/8"=1'-0" 4' 0 4' 8' 12' 16' 20'
scale feet

DVM JOB No.: 95150
CAD FILE No.: 30C-2ALP

AMENDMENT DRAWING - AMEND SHT. E3.3

Revisions	Date
⚠1 AMENDMENT #1	4/4/97

DOUGLAS V. MACMAHON LTD.
REGISTERED PROFESSIONAL ENGINEERS
1131 KAPAHULU AVENUE
HONOLULU, HAWAII 96816

ARCHITECTS HAWAII LIMITED
Pacific Tower, Suite 300
1001 Bishop Street
Honolulu, Hawaii 96813
Telephone: (808) 523-9636
FAX: (808) 521-3280

This work was prepared by me or under my supervision and construction of this project will be under my supervision.
Signature
NOTE: Contractor to check and verify all dimensions at job before proceeding with work.

ALBERT F. KILBURG JR. LICENSED PROFESSIONAL ENGINEER No. 3183-E HAWAII, U.S.A.

Drawing Title: PARTIAL LIGHTING PLAN LEVEL 2 - AREA A
Approved: Area Project Manager


Project Title: AMBULATORY CARE AND RENOVATE E-WING PHASE I, AMBULATORY CARE CLINIC
Building Number: 30
Checked: TB
Drawn: TY
Location: VAMROC, HONOLULU, HAWAII


Date: MAR. 20, 1997
Project No.: 459-002A
Drawing No.: E3.3 R1
Dwg. 275 of 346

Department of Veterans Affairs

VA FORM, 08-6231A, JAN 1990


★U.S. GOVERNMENT PRINTING OFFICE: 1984-440-487

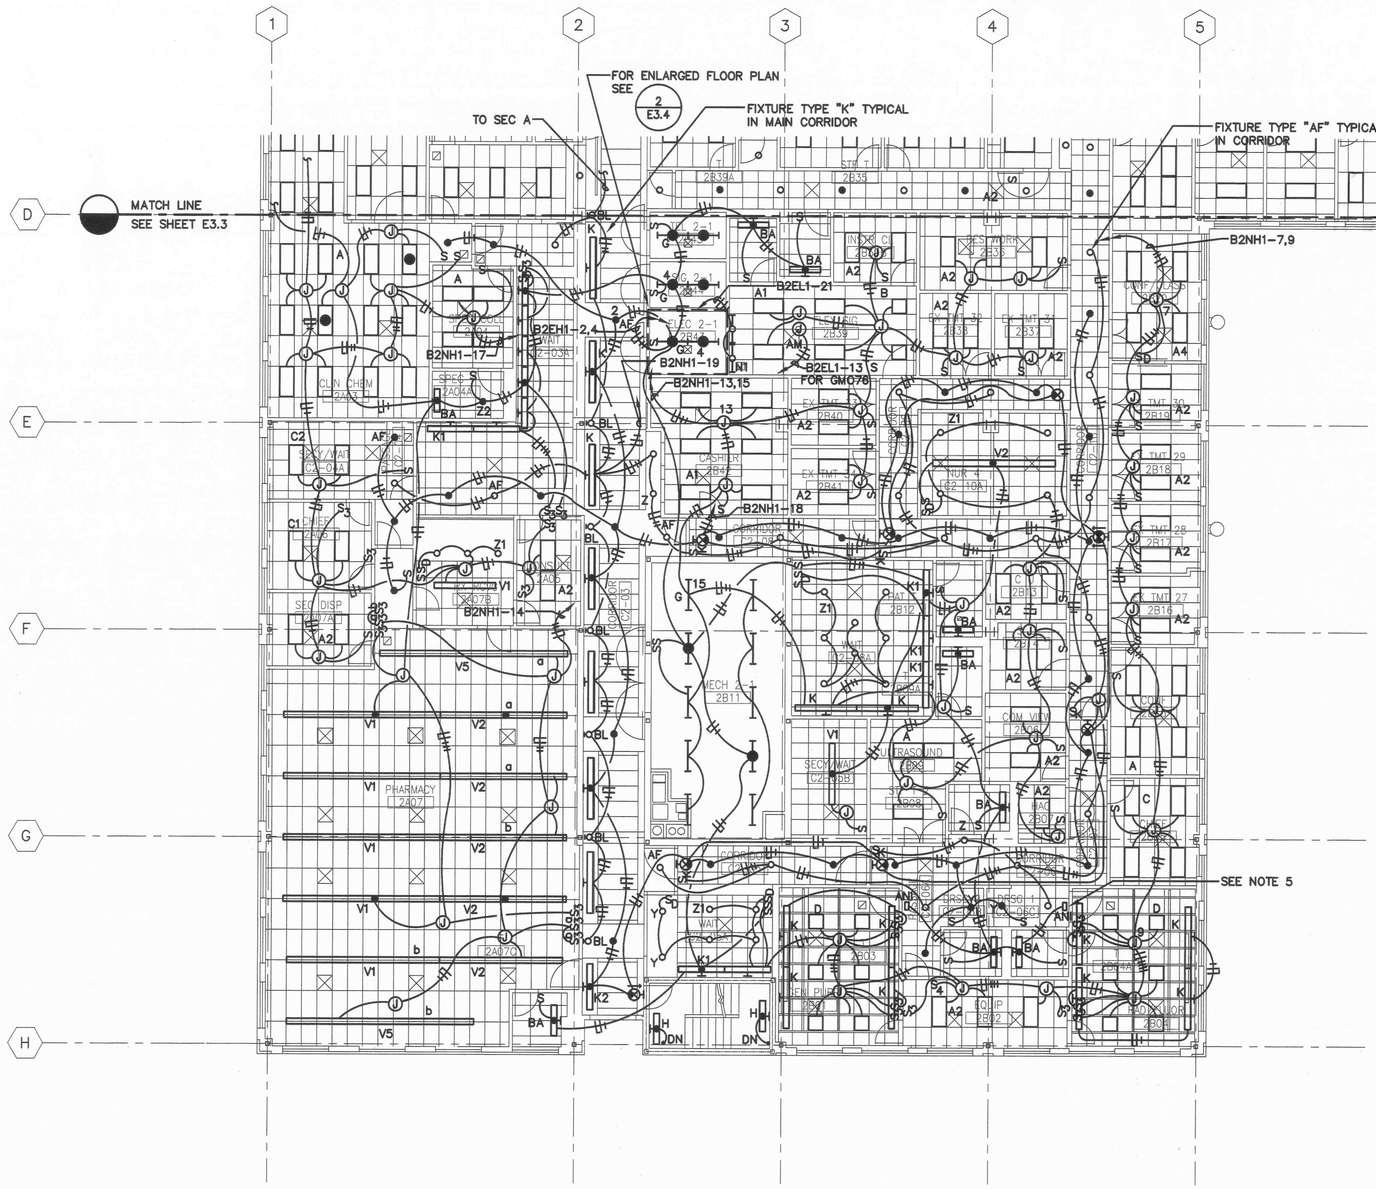

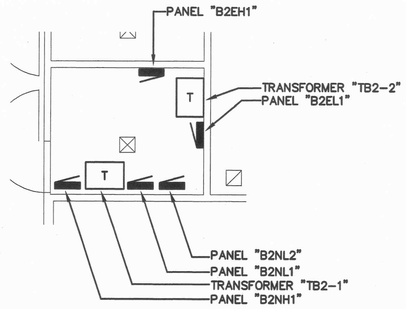

2/E3.4 ELECTRIC ROOM NO. 2-1
SCALE: 1/4" = 1'-0"

1/E3.4 PARTIAL LIGHTING PLAN - LEVEL 2 - AREA B
SCALE: 1/8" = 1'-0"

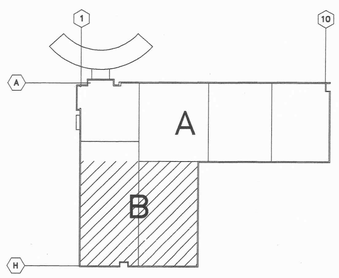

KEY PLAN
NO SCALE

N PROJECT NORTH

GRAPHIC SCALE
1/8"=1'-0"
4' 0 4' 8' 12' 16' 20'
scale feet

NOTES:

1. FIXTURE TYPE INDICATED IN ROOM IS TYPICAL FOR ALL LIGHT FIXTURES IN THAT ROOM.
2. A SHALLOW JUNCTION BOX SHALL BE USED FOR MOUNTING LIGHT FIXTURE TYPE "BL". (1-1/2" DEPTH).
3. COORDINATE WITH STRUCTURAL AND MECHANICAL CONTRACTORS FOR PLACEMENT OF LIGHT FIXTURES IN MECH., ELEC., AND SIGNAL.
4. EXAM LIGHT (GM076) IN ROOM 2B39 IS CONTRACTOR FURNISHED CONTRACTOR INSTALLED. SEE SPECS SECTION 16515.
5. PROVIDE CONTROL CIRCUIT TO X-RAY GENERATOR CONTACTS SUCH THAT "X-RAY IN USE" SIGN TURNS ON WHEN X-RAY MACHINE IS IN USE.

DVM JOB No.: 95150
CAD FILE No.: 30C-2BLP/MASADA

AMENDMENT DRAWING - AMEND SHT. E3.4

Revisions	Date
1 AMENDMENT #1	4/4/97

VA FORM, 08-6231A, JAN 1990

DOUGLAS V. MACMAHON LTD.
REGISTERED PROFESSIONAL ENGINEERS
1121 KAPAHULU AVENUE
HONOLULU, HAWAII 96816

ARCHITECTS HAWAII LIMITED
Pacific Tower, Suite 300
1001 Bishop Street
Honolulu, Hawaii 96813
Telephone: (808) 523-9636
FAX: (808) 521-3280

This work was prepared by me or under my supervision and construction of this project will be under my supervision.

Signature

NOTE: Contractor to check and verify all dimensions at job before proceeding with work.

ALBERT F. KILBURG, JR. LICENSED PROFESSIONAL ENGINEER No. 3183-E HAWAII, U.S.A.

Drawing Title: PARTIAL LIGHTING PLAN LEVEL 2 - AREA B

Approved: Area Project Manager

Project Title: AMBULATORY CARE AND RENOVATE E-WING PHASE I, AMBULATORY CARE CLINIC

Date: MAR. 20, 1997

Project No.: 459-002A

Building Number: 30 | Checked: TS | Drawn: TY

Location: VAMROC, HONOLULU, HAWAII

Drawing No.: E3.4R1

Dwg. 216 of 368

Department of Veterans Affairs

U.S. GOVERNMENT PRINTING OFFICE: 1986-440-487