LEGEND

2'x4' ACOUS PANEL

2'x2' ACOUS PANEL

1'x1' ACOUS PANEL

ACOUS WOOD

GYPSUM BD UNLESS OTHERWISE NOTED.

CEILING MATERIAL INDICATIONS

LIGHT FIXTURES (SEE ELEC DWGS)

CUBICLE CURTAIN TRACK


MECHANICAL REGISTERS, GRILLES, ETC (SEE MECH DWGS)

CEILING BRACE


NOTES:

1. CEILING HEIGHTS ARE 9'-0", UNLESS OTHERWISE NOTED.
   SOFFIT HEIGHTS ARE 8'-0", UNLESS OTHERWISE NOTED.
2. CEILING MATERIALS AND FINISHES ARE INDICATED IN SPECIFICATIONS SECTION 09050 – COLOR DESIGN.
3. SEE 8/8.2 FOR MAIN CORRIDOR LAYOUT
   TYPICAL FOR CORRIDORS C1-01, C1-02, C2-02, C2-03, C2-14, C3-02, C3-03, C3-10
4. SOFFIT MATERIAL TO BE GYPSUM BOARD, INDICATED ON REFLECTED CEILING PLANS AS "GWB".
5. EXPOSED STRUCTURE INDICATED AS ⟨EXP⟩.
6. NOT ALL ACCESS PANELS ARE SHOWN. SEE MECHANICAL AND ELECTRICAL

2A01	BUILDING MANAGEMENT STORAGE
2A02	HOUSEKEEPING AIDS CLOSET
2A03A	SECRETARY/FILES
2A03B	CHIEF TECHNICIAN
2A03C	MICROBIOLOGY
2A03D	BULK STORAGE
2B21	MULTI-PURPOSE 2
2B22	PHYSICIAN 11
2B23	PHYSICIAN 10
2B24	CLEAN UTILITY 2
2B25	SOILED UTILITY 2
2B26	PHYSICIAN
2B27	EXAM
2B28	EXAM
2B29	VISUAL FIELDS
2B30	PHOTOGRAPHY
2B31	HOUSEKEEPING AIDS CLOSET
2B32	SOCIAL WORKER 3
2B33	SOCIAL WORKER 2
2B34	SOCIAL WORKER 1
2C01	INTERVIEW
2C02	INTERVIEW
2C03	PATIENT REPRESENTATIVE
2C04	RECEPTION
2C04A	SECRETARY/CLERK
2C04B	SUPERVISOR
2C05	LIFE SUPPORT
2C05A	TRIAGE
2C05B	PATIENT SHOWER
2C05C	PATIENT TOILET
2C07	LIFE SUPPORT
2D01	PATIENT TOILET
2D02	EXAM/TREATMENT 21
2D03	EXAM/TREATMENT 22
2D05	EXAM/TREATMENT 24
2D06	PHYSICIAN 9
2D07	PHYSICIAN 8
2D08	PHYSICIAN 7
2D09	STAFF TOILET
2D10	PATIENT TOILET
2D11	EXAM/TREATMENT 20
2D12	EXAM/TREATMENT 19
2D13	EXAM/TREATMENT 18
2D14	EXAM/TREATMENT 17
2D15	TELEPHONE 2-2
2D16	SIGNAL 2-2
2D17	ELECTRICAL 2-2
2E01	EXAM/TREATMENT 12
2E02	EXAM/TREATMENT 13
2E03	EXAM/TREATMENT 14
2E04	EXAM/TREATMENT 15
2E05	PHYSICIAN 6
2E06	EXAM/TREATMENT 16
2E07	PHYSICIAN 5
2E08	PHYSICIAN 4
2E09	SOILED UTILITY 1
2E10	EXAM/TREATMENT 11
2E11	EXAM/TREATMENT 10
2E12	EXAM/TREATMENT 9
2E13	PATIENT TOILET
2E14	MECHANICAL 2-2
2E15	EXAM/TREATMENT 5
2E16	EXAM/TREATMENT 6
2E17	EXAM/TREATMENT 7
2E18	PATIENT TOILET
2E19	CLEAN UTILITY 1
2E20	PHYSICIAN 3
2E21	PHYSICIAN 2
2E22	EXAM/TREATMENT 8
2E23	PHYSICIAN 1
2E24	MULTI-PURPOSE 1
2E25	EXAM/TREATMENT 4
2E26	EXAM/TREATMENT 3
2E27	EXAM/TREATMENT 2
2E28	EXAM/TREATMENT 1
C2-01	ELEVATOR LOBBY
C2-02	CORRIODR
C2-03	CORRIDOR
C2-10	CORRIDOR
C2-11	CORRIDOR
C2-12	PASSAGE
C2-13	CORRIDOR
C2-14	CORRIDOR
C2-15	PASSAGE
C2-15A	WAITING
C2-16	WAITING
C2-17	CORRIDOR
C2-18	CORRIDOR
C2-18A	NURSE STATION
C2-19	WAITING
C2-20	CORRIDOR
C2-21	CORRIDOR
C2-21A	NURSE STATION
C2-22	WAITING
C2-23	CORRIDOR
C2-24	CORRIDOR
C2-24A	NURSE STATION

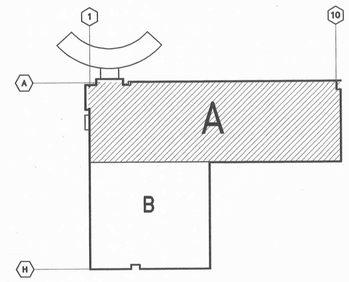

KEY PLAN
NO SCALE

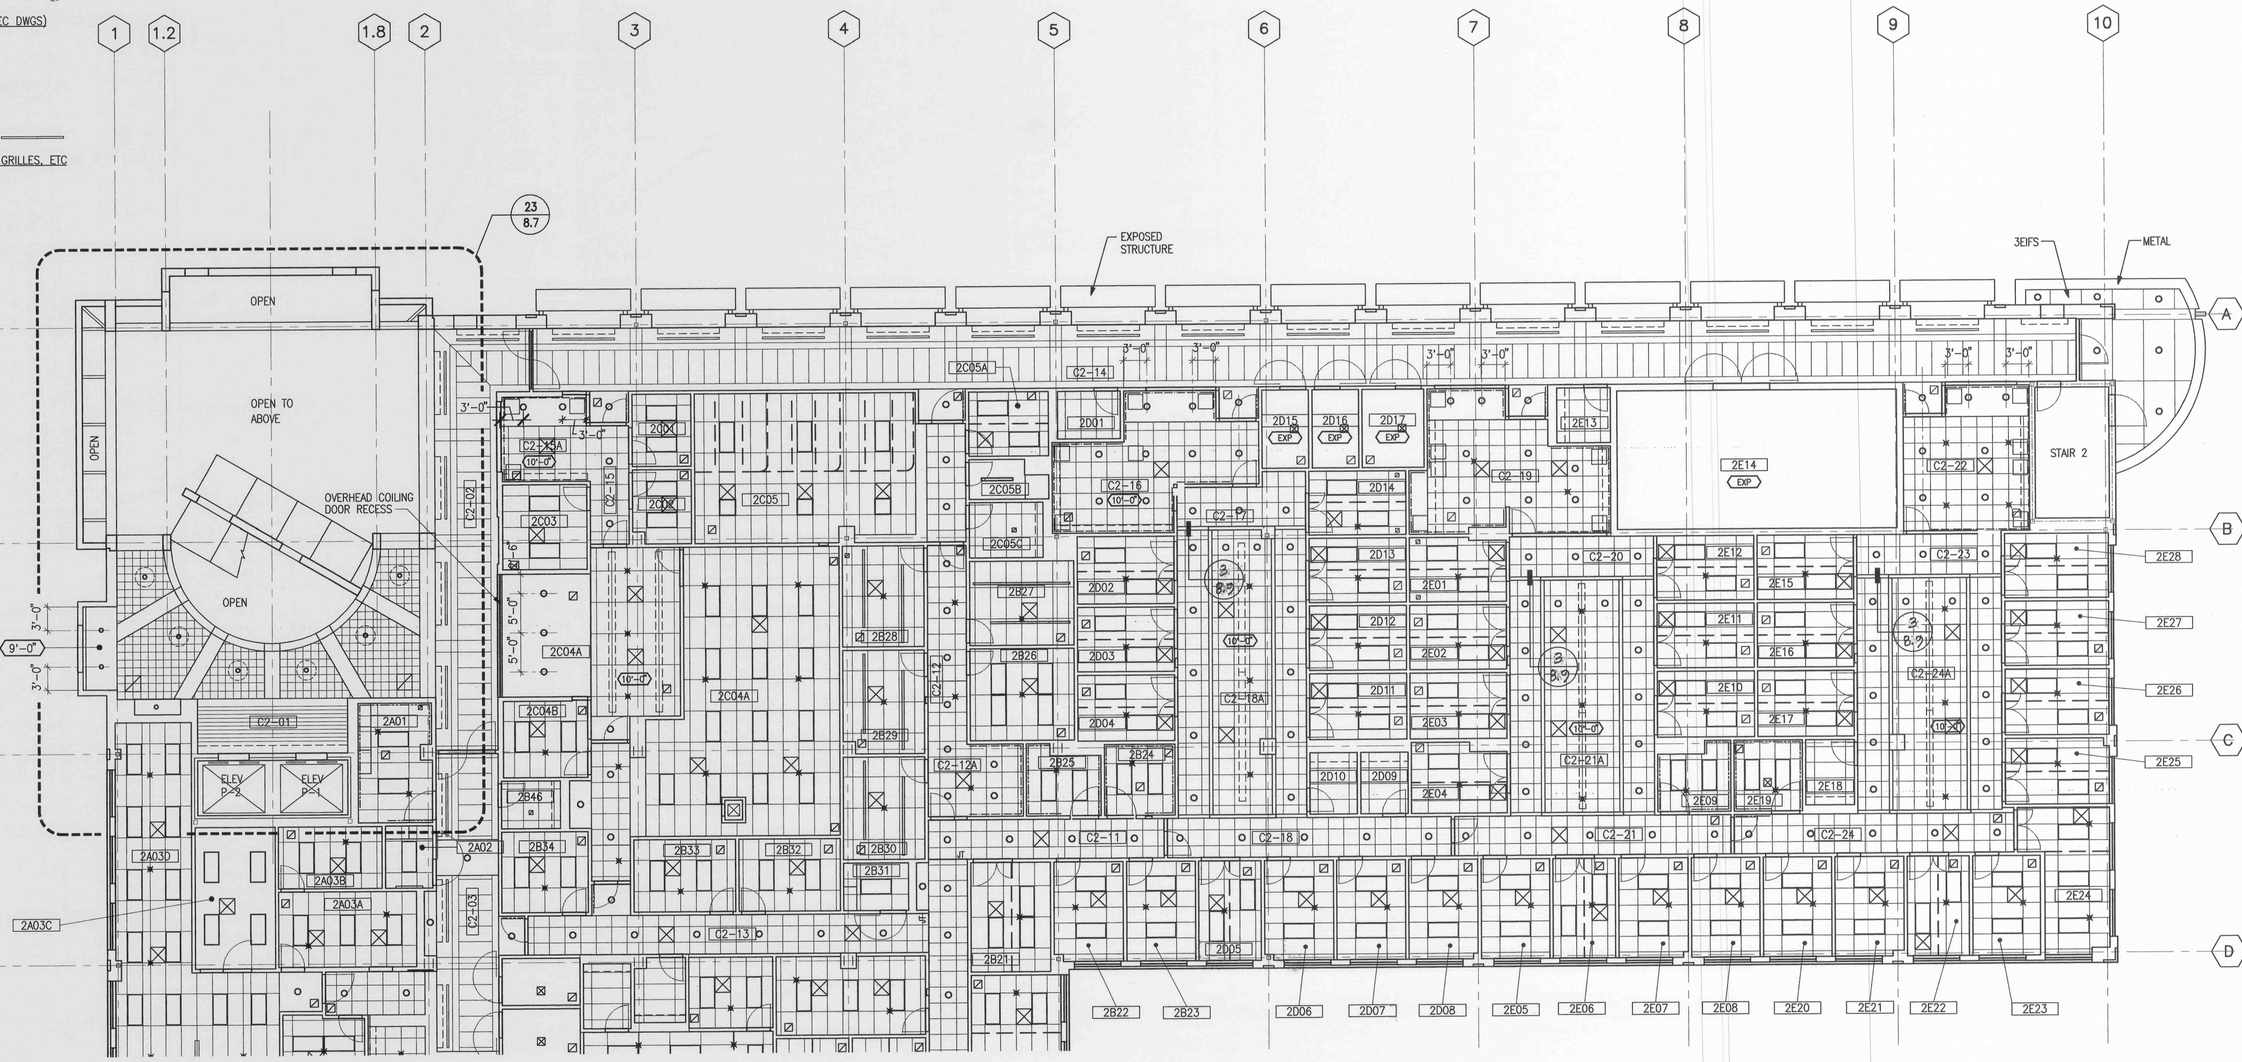

VA AMBULATORY CARE CLINIC
PARTIAL REFLECTED CEILING PLAN
LEVEL 2 - AREA A

SCALE: 1/8"=1'-0"

FULLY SPRINKLERED

Revisions	Date

ARCHITECTS HAWAII LIMITED
1001 Bishop Street, Pacific 300
Honolulu, Hawaii 96813
Telephone: (808) 523-9636
FAX: (808) 521-3280

This work was prepared by me or under my supervision and construction of this project will be under my supervision.

Signature

NOTE: Contractor to check and verify all dimensions at job before proceeding with work.

WALTER H. MURAOKA LICENSED PROFESSIONAL ARCHITECT No. 5035 HAWAII, U.S.A.

Drawing Title: PARTIAL REFL CLG PLAN LEVEL 2 - AREA A

Approved: Area Project Manager

Project Title: AMBULATORY CARE AND RENOVATE E-WING PHASE I, AMBULATORY CARE CLINIC

Building Number: 30 | Checked: | Drawn: CKT

Location: VAMROC, HONOLULU, HAWAII

Date: MAR 20, 1997

Project No.: 459-002A

Drawing No.: 8.3

Dwg. 106 Of 366

Department of Veterans Affairs

PLAN/PF2RC-A.DWG

VA FORM, 08-6231A, JAN 1990

© U.S. GOVERNMENT PRINTING OFFICE: 1984-440-467