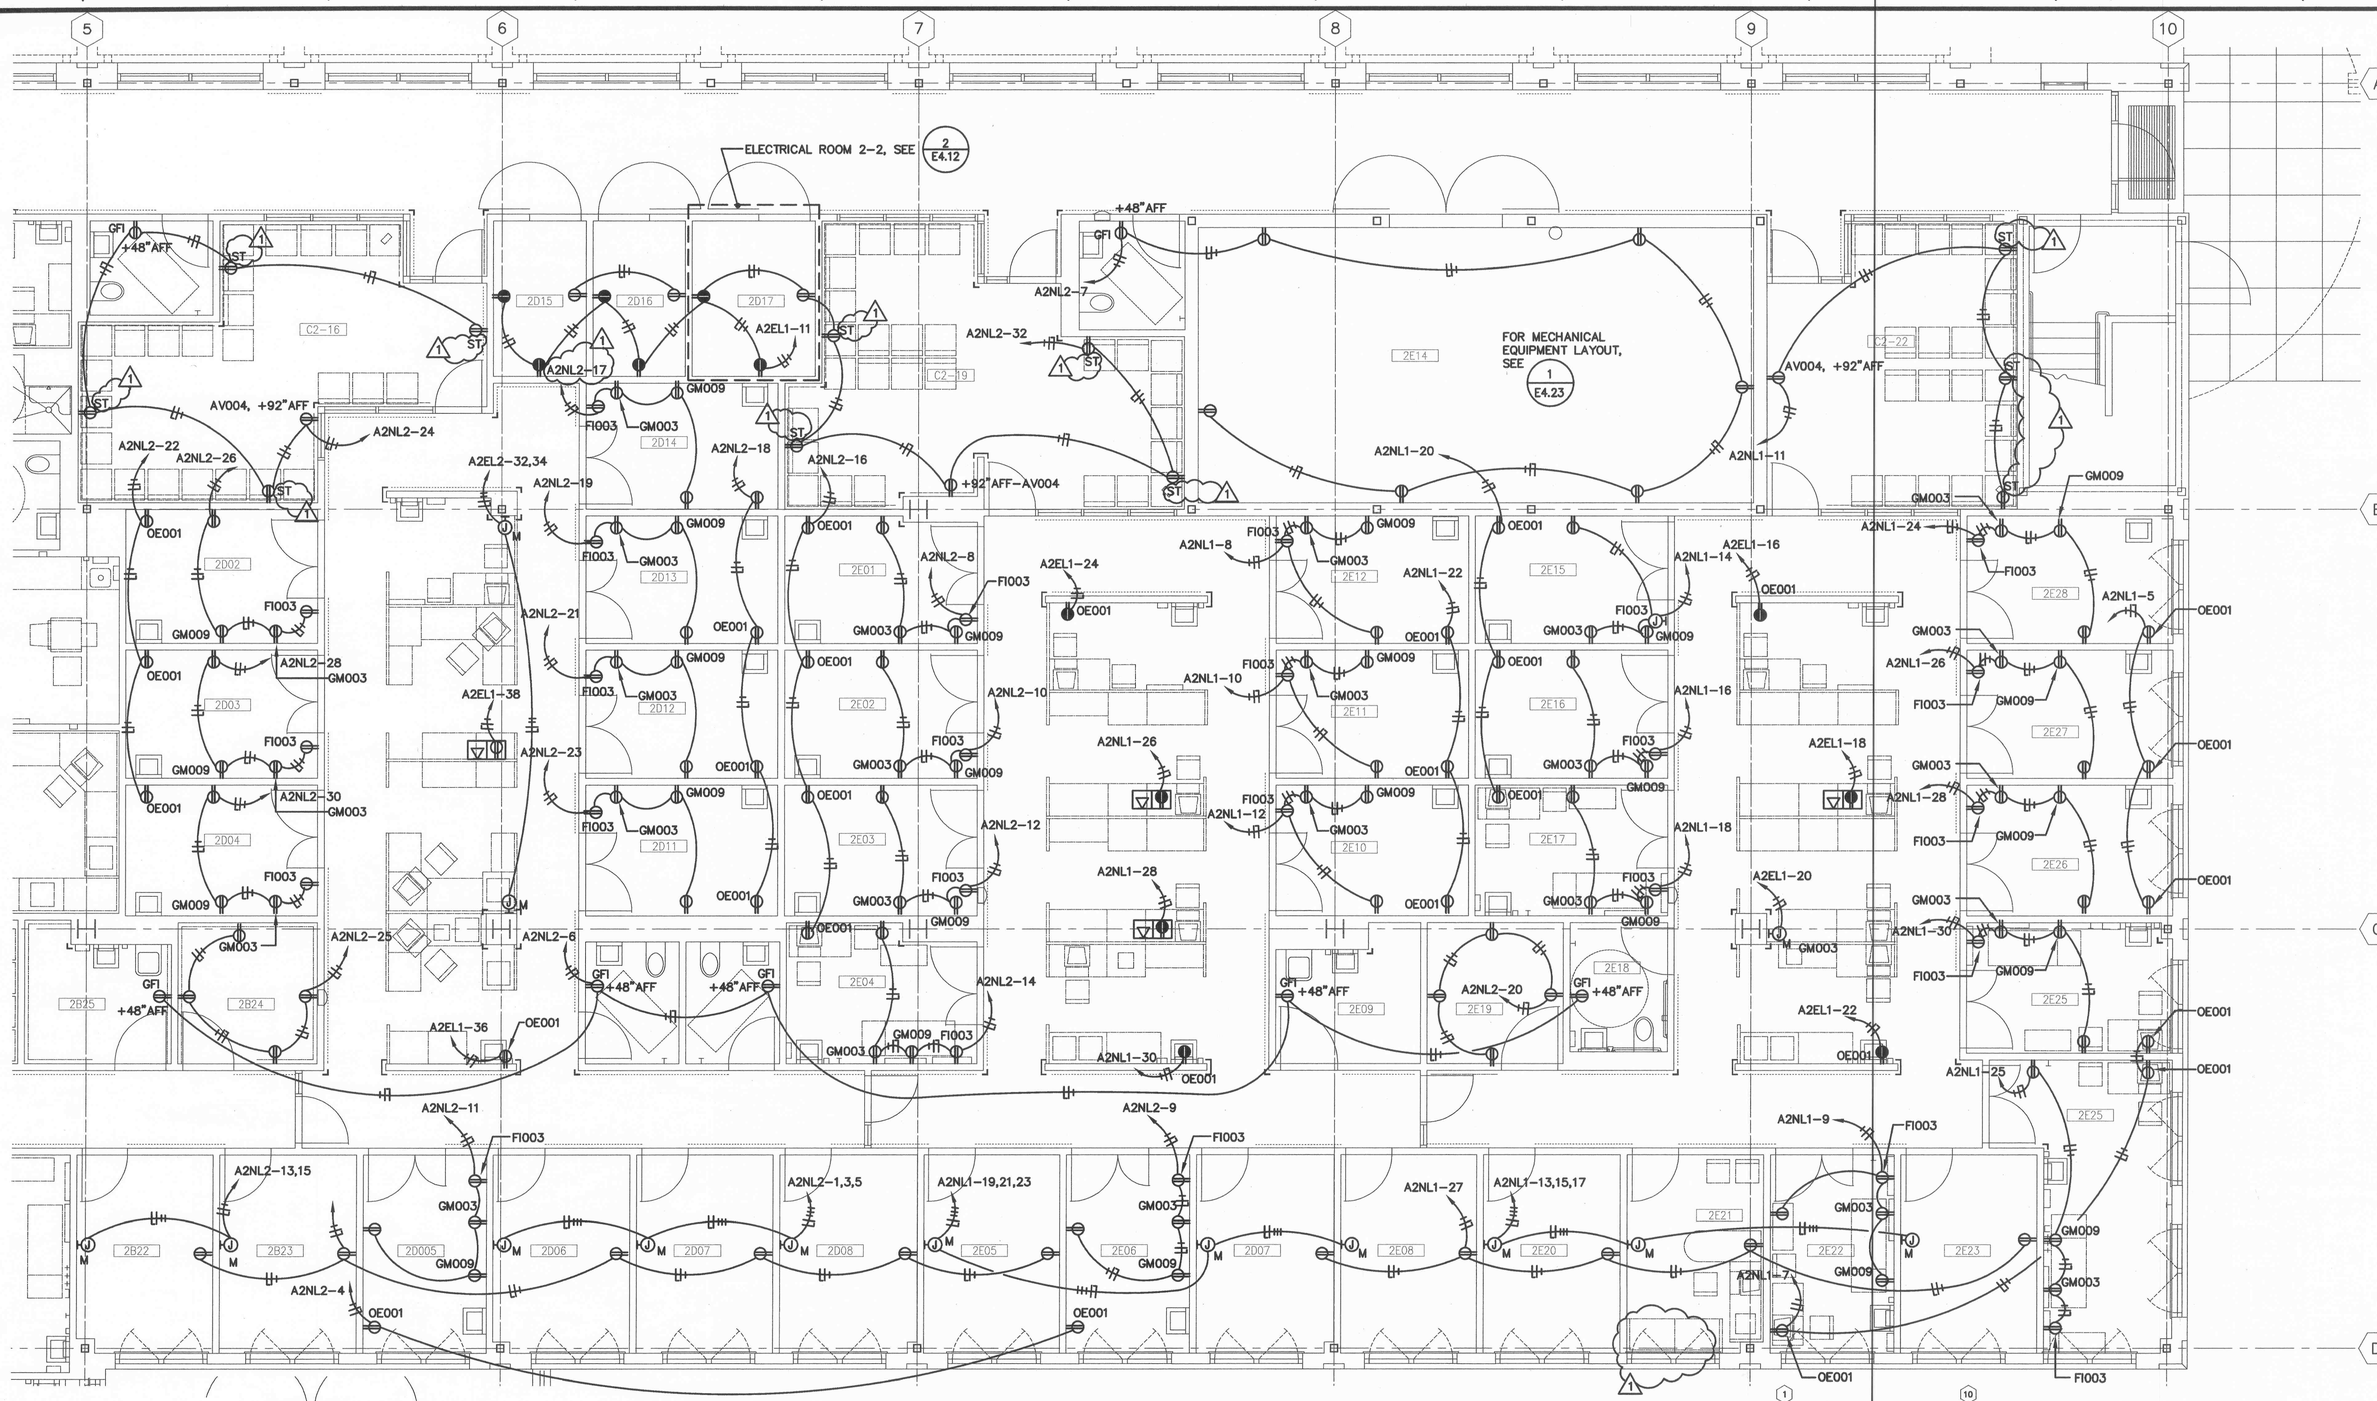


NOTE:

1. FOR ELECTRICAL REQUIREMENTS OF EQUIPMENT SHOWN, SEE SHEET E4.27.

DVM JOB No.: 95150
CAD FILE No.: 30C-2BEP

(2/E4.12) ELECTRIC ROOM NO. 2-2

SCALE: 1/4" = 1'-0"

(1/E4.12) PARTIAL EQUIPMENT OUTLETS PLAN - LEVEL 2 - AREA B

SCALE: 1/4" = 1'-0"

Revisions	Date
⚠ AMENDMENT #1	4/4/97

DOUGLAS V. MACMAHON LTD.
REGISTERED PROFESSIONAL ENGINEERS
1131 KAPAHULU AVENUE
HONOLULU, HAWAII 96816

ARCHITECTS HAWAII LIMITED
Pacific Tower, Suite 300
1001 Bishop Street
Honolulu, Hawaii 96813
Telephone: (808) 523-9636
FAX: (808) 521-3280

This work was prepared by me or under my supervision and construction of this project will be under my supervision.
Signature
NOTE: Contractor to check and verify all dimensions at job before proceeding with work.

ALBERT F. KILBURG, JR. LICENSED PROFESSIONAL ENGINEER No. 3183-E HAWAII, U.S.A.

Drawing Title: PARTIAL EQUIPMENT OUTLETS PLAN LEVEL 2 - AREA B

Approved: Area Project Manager

Project Title: AMBULATORY CARE AND RENOVATE E-WING PHASE I, AMBULATORY CARE CLINIC

Building Number: 30 | Checked: TB/DM | Drawn: PCS

Location: VAMROC, HONOLULU, HAWAII

Date: MAR. 20, 1997

Project No.: 459-002A

Drawing No.: E4.12R1


Dwg. 299 of 360 Dwgs.

Department of Veterans Affairs

AMENDMENT DRAWING feet AMEND SHT. E4.12


VA FORM, 08-6231A, JAN 1990

★U.S. GOVERNMENT PRINTING OFFICE: 1984-440-487

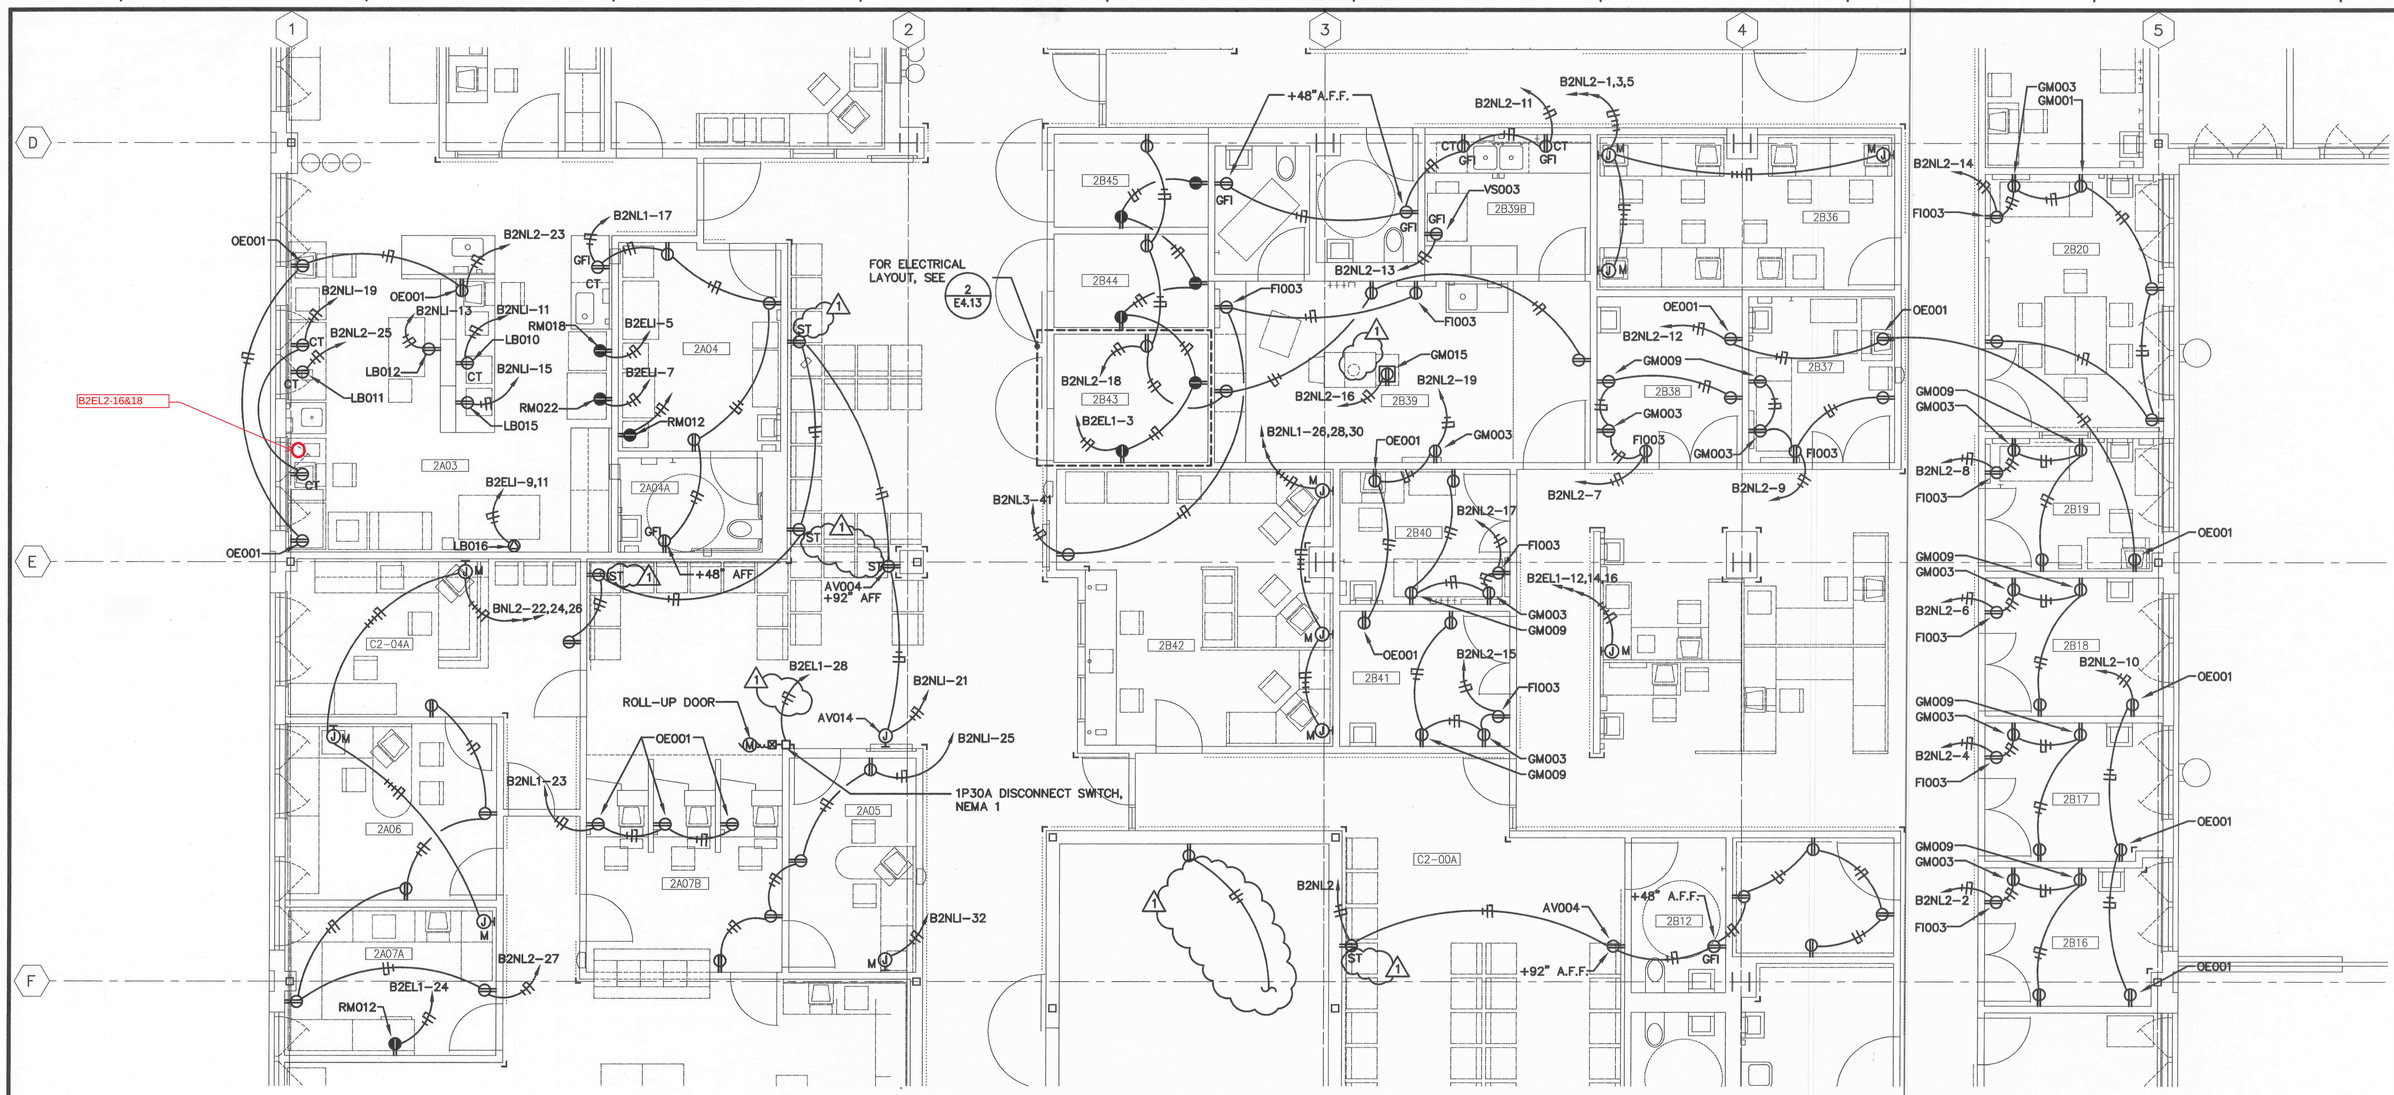


NOTE:

1. FOR ELECTRICAL REQUIREMENTS OF EQUIPMENT SHOWN, SEE SHEET E4.27.

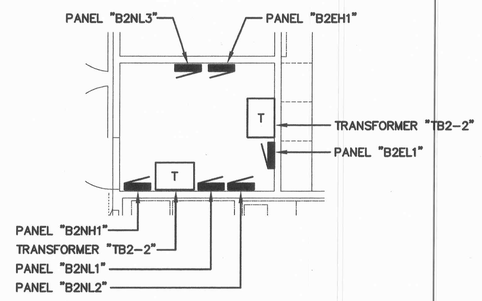

2/E4.13 ELECTRIC ROOM NO. 2-1

SCALE: 1/4" = 1'-0"

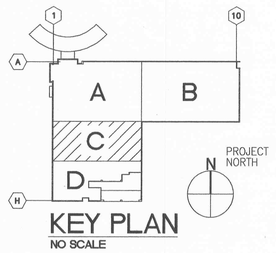

1/E4.13 PARTIAL EQUIPMENT OUTLETS PLAN - LEVEL 2 - AREA C

SCALE: 1/4" = 1'-0"

DVM JOB No.: 95150
CAD FILE No.: 30C-2CEP

GRAPHIC SCALE
1/4"=1'-0" 2' 0 2' 4' 6' 8' 10'
scale AMENDMENT DRAWING feet AMEND SHT. E4.13

Revisions	Date
⚠1 AMENDMENT #1	4/4/97

DOUGLAS V. MACMAHON LTD.
REGISTERED PROFESSIONAL ENGINEERS
1131 KAPAHULU AVENUE
HONOLULU, HAWAII 96816

ARCHITECTS HAWAII LIMITED
Pacific Tower, Suite 300
1001 Bishop Street
Honolulu, Hawaii 96813
Telephone: (808) 523-9636
FAX: (808) 521-3280

This work was prepared by me or under my supervision and construction of this project will be under my supervision.
Signature
NOTE: Contractor to check and verify all dimensions at job before proceeding with work.

ALBERT F. KILBURG, JR. LICENSED PROFESSIONAL ENGINEER No. 3183-E HAWAII, U.S.A.

Drawing Title: PARTIAL EQUIPMENT OUTLETS PLAN LEVEL 2 - AREA C

Approved: Area Project Manager

Project Title: AMBULATORY CARE AND RENOVATE E-WING PHASE I, AMBULATORY CARE CLINIC

Building Number: 30 | Checked: TB/DM | Drawn: PCS


Location: VAMROC, HONOLULU, HAWAII

Date: MAR. 20, 1997
Project No.: 459-002A
Drawing No.: E4.13R1
Dwg.300 Of 346

Department of Veterans Affairs

VA FORM, 08-6231A, JAN 1990

★U.S. GOVERNMENT PRINTING OFFICE: 1984-448-497

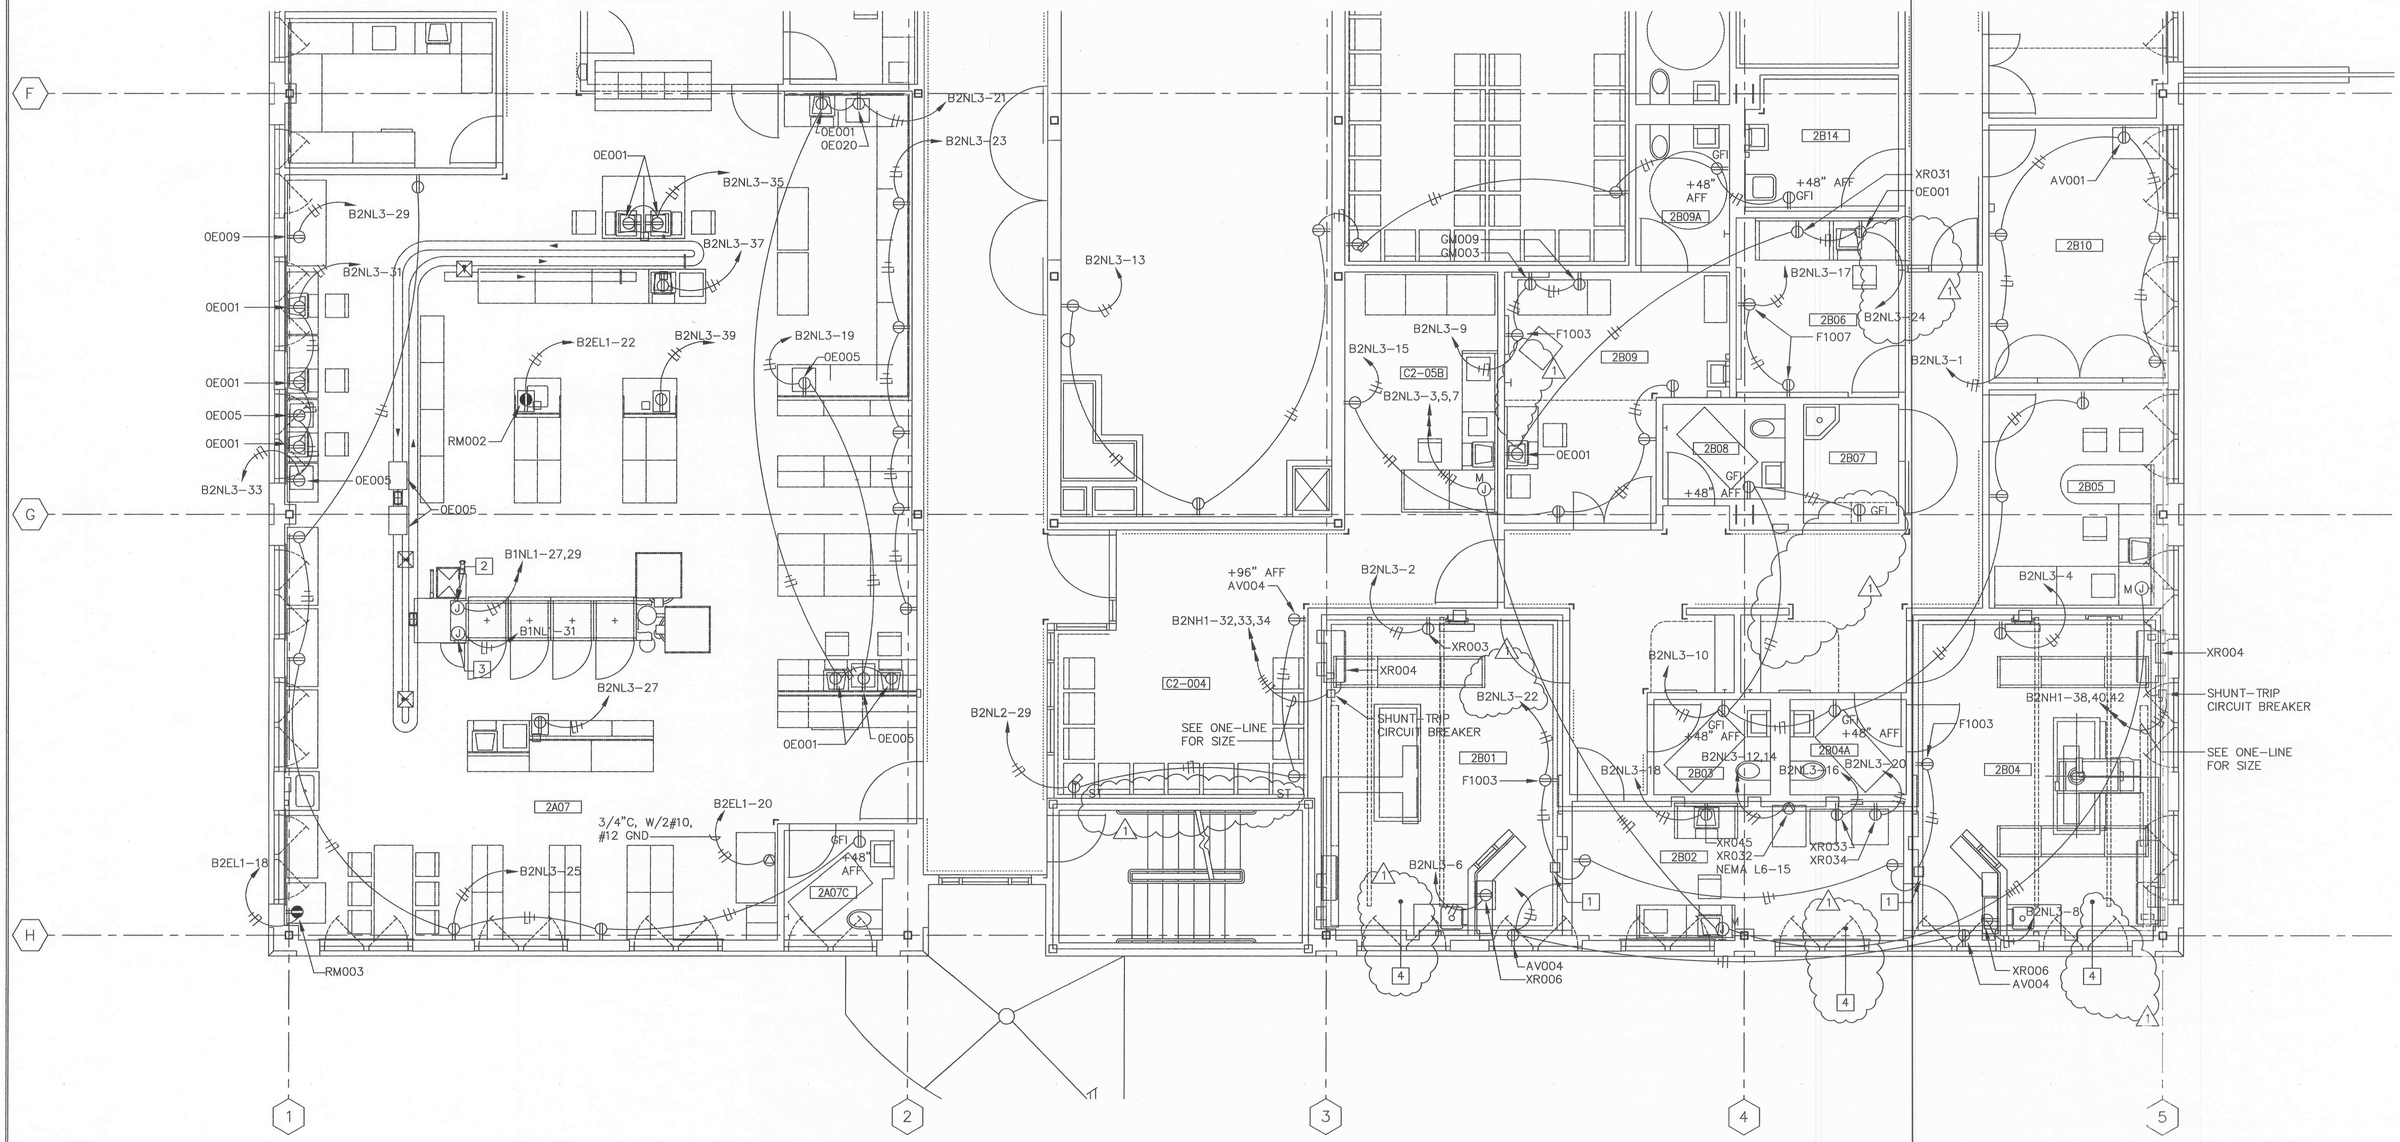


1/E4.14 PARTIAL EQUIPMENT OUTLETS PLAN - LEVEL 2 - AREA D

SCALE: 1/4" = 1'-0"


WORK NOTES:

1. PROVIDE PUSH-BUTTON TO ACTIVATE SHUNT-TRIP CIRCUIT BRAKERS MOUNT PUSH-BUTTON AT 5'-6" AFF. PROVIDE NAMEPLATE: "X-RAY SHUTOFF".
2. PROVIDE JUNCTION BOX IN CEILING AND CONNECT TO DISPENSER PER MANUFACTURER'S RECOMMENDATION. ROUTE 1" CONDUIT WITH 2#10, #12 GROUND TO PANEL B2NL1-27,29.
3. PROVIDE JUNCTION BOX IN CEILING AND CONNECT TO DISPENSER FOR POWER TO 0E005.
4. PROVIDE WALL DUCT, FLOOR TRENCH, & WIREWAYS AS REQUIRED FOR A COMPLETE RACEWAY INSTALLATION FOR ROOMS 2B01, 2B02, & 2B03. SEE ARCHITECTURAL DWG 6-13 FOR RACEWAY ISOMETRIC AND RACEWAY SECTION AND TRANSISTION DETAILS. RACEWAYS SHALL ALL BE OF SAME MANUFACTURER AND SHALL BE MANUFACTURED FROM 14 GAUGE STEEL AND SHALL HAVE REMOVABLE COVERPLATES. FIELD CUT RACEWAYS TO MATCH ISOMETRIC AND PROVIDE PARTITIONS AND HANGARS AS REQUIRED FOR A COMPLETE INSTALLATION.

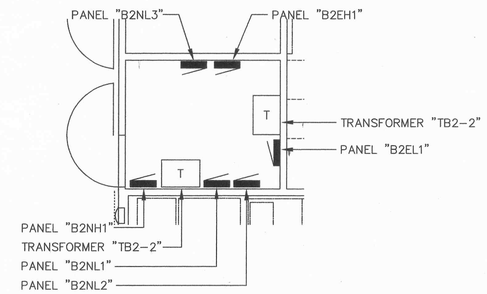

2/E4.14 ELECTRIC ROOM No. 2-1

SCALE: 1/4" = 1'-0"

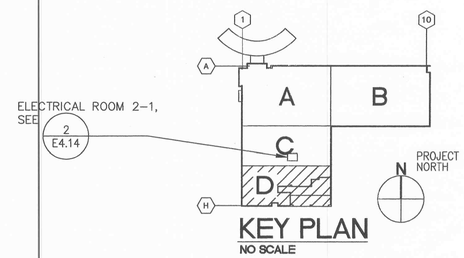

KEY PLAN
NO SCALE

DVM JOB No.: 95150
CAD FILE No.: 30C-2DEP

GRAPHIC SCALE
1/4"=1'-0" scale
2' 0 2' 4' 6' 8' 10' feet

AMENDMENT DRAWING AMEND SHT. E4.14

Revisions	Date
⚠ AMENDMENT #1	4/4/97

DOUGLAS V. MACMAHON LTD.
REGISTERED PROFESSIONAL ENGINEERS
1131 KAPAHULU AVENUE
HONOLULU, HAWAII 96816

ARCHITECTS HAWAII LIMITED
Pacific Tower, Suite 300
1001 Bishop Street
Honolulu, Hawaii 96813
Telephone: (808) 523-9636
FAX: (808) 521-3280

This work was prepared by me or under my supervision and construction of this project will be under my supervision.

Signature

NOTE: Contractor to check and verify all dimensions at job before proceeding with work.

ALBERT F. KILBURG JR. LICENSED PROFESSIONAL ENGINEER No. 3183-E HAWAII, U.S.A.

Drawing Title: PARTIAL EQUIPMENT OUTLETS PLAN LEVEL 2- AREA D

Approved: Area Project Manager

Project Title: AMBULATORY CARE AND RENOVATE E-WING PHASE I, AMBULATORY CARE CLINIC

Building Number: 30 | Checked: TS/DM | Drawn: PCS

Location: VAMROC, HONOLULU, HAWAII

Date: MAR. 20, 1997

Project No.: 459-002A

Drawing No.: E4.14R1

Dwg. 301 of 368

Department of Veterans Affairs

VA FORM, 08-6231A, JAN 1990

☆U.S. GOVERNMENT PRINTING OFFICE: 1984-440-467