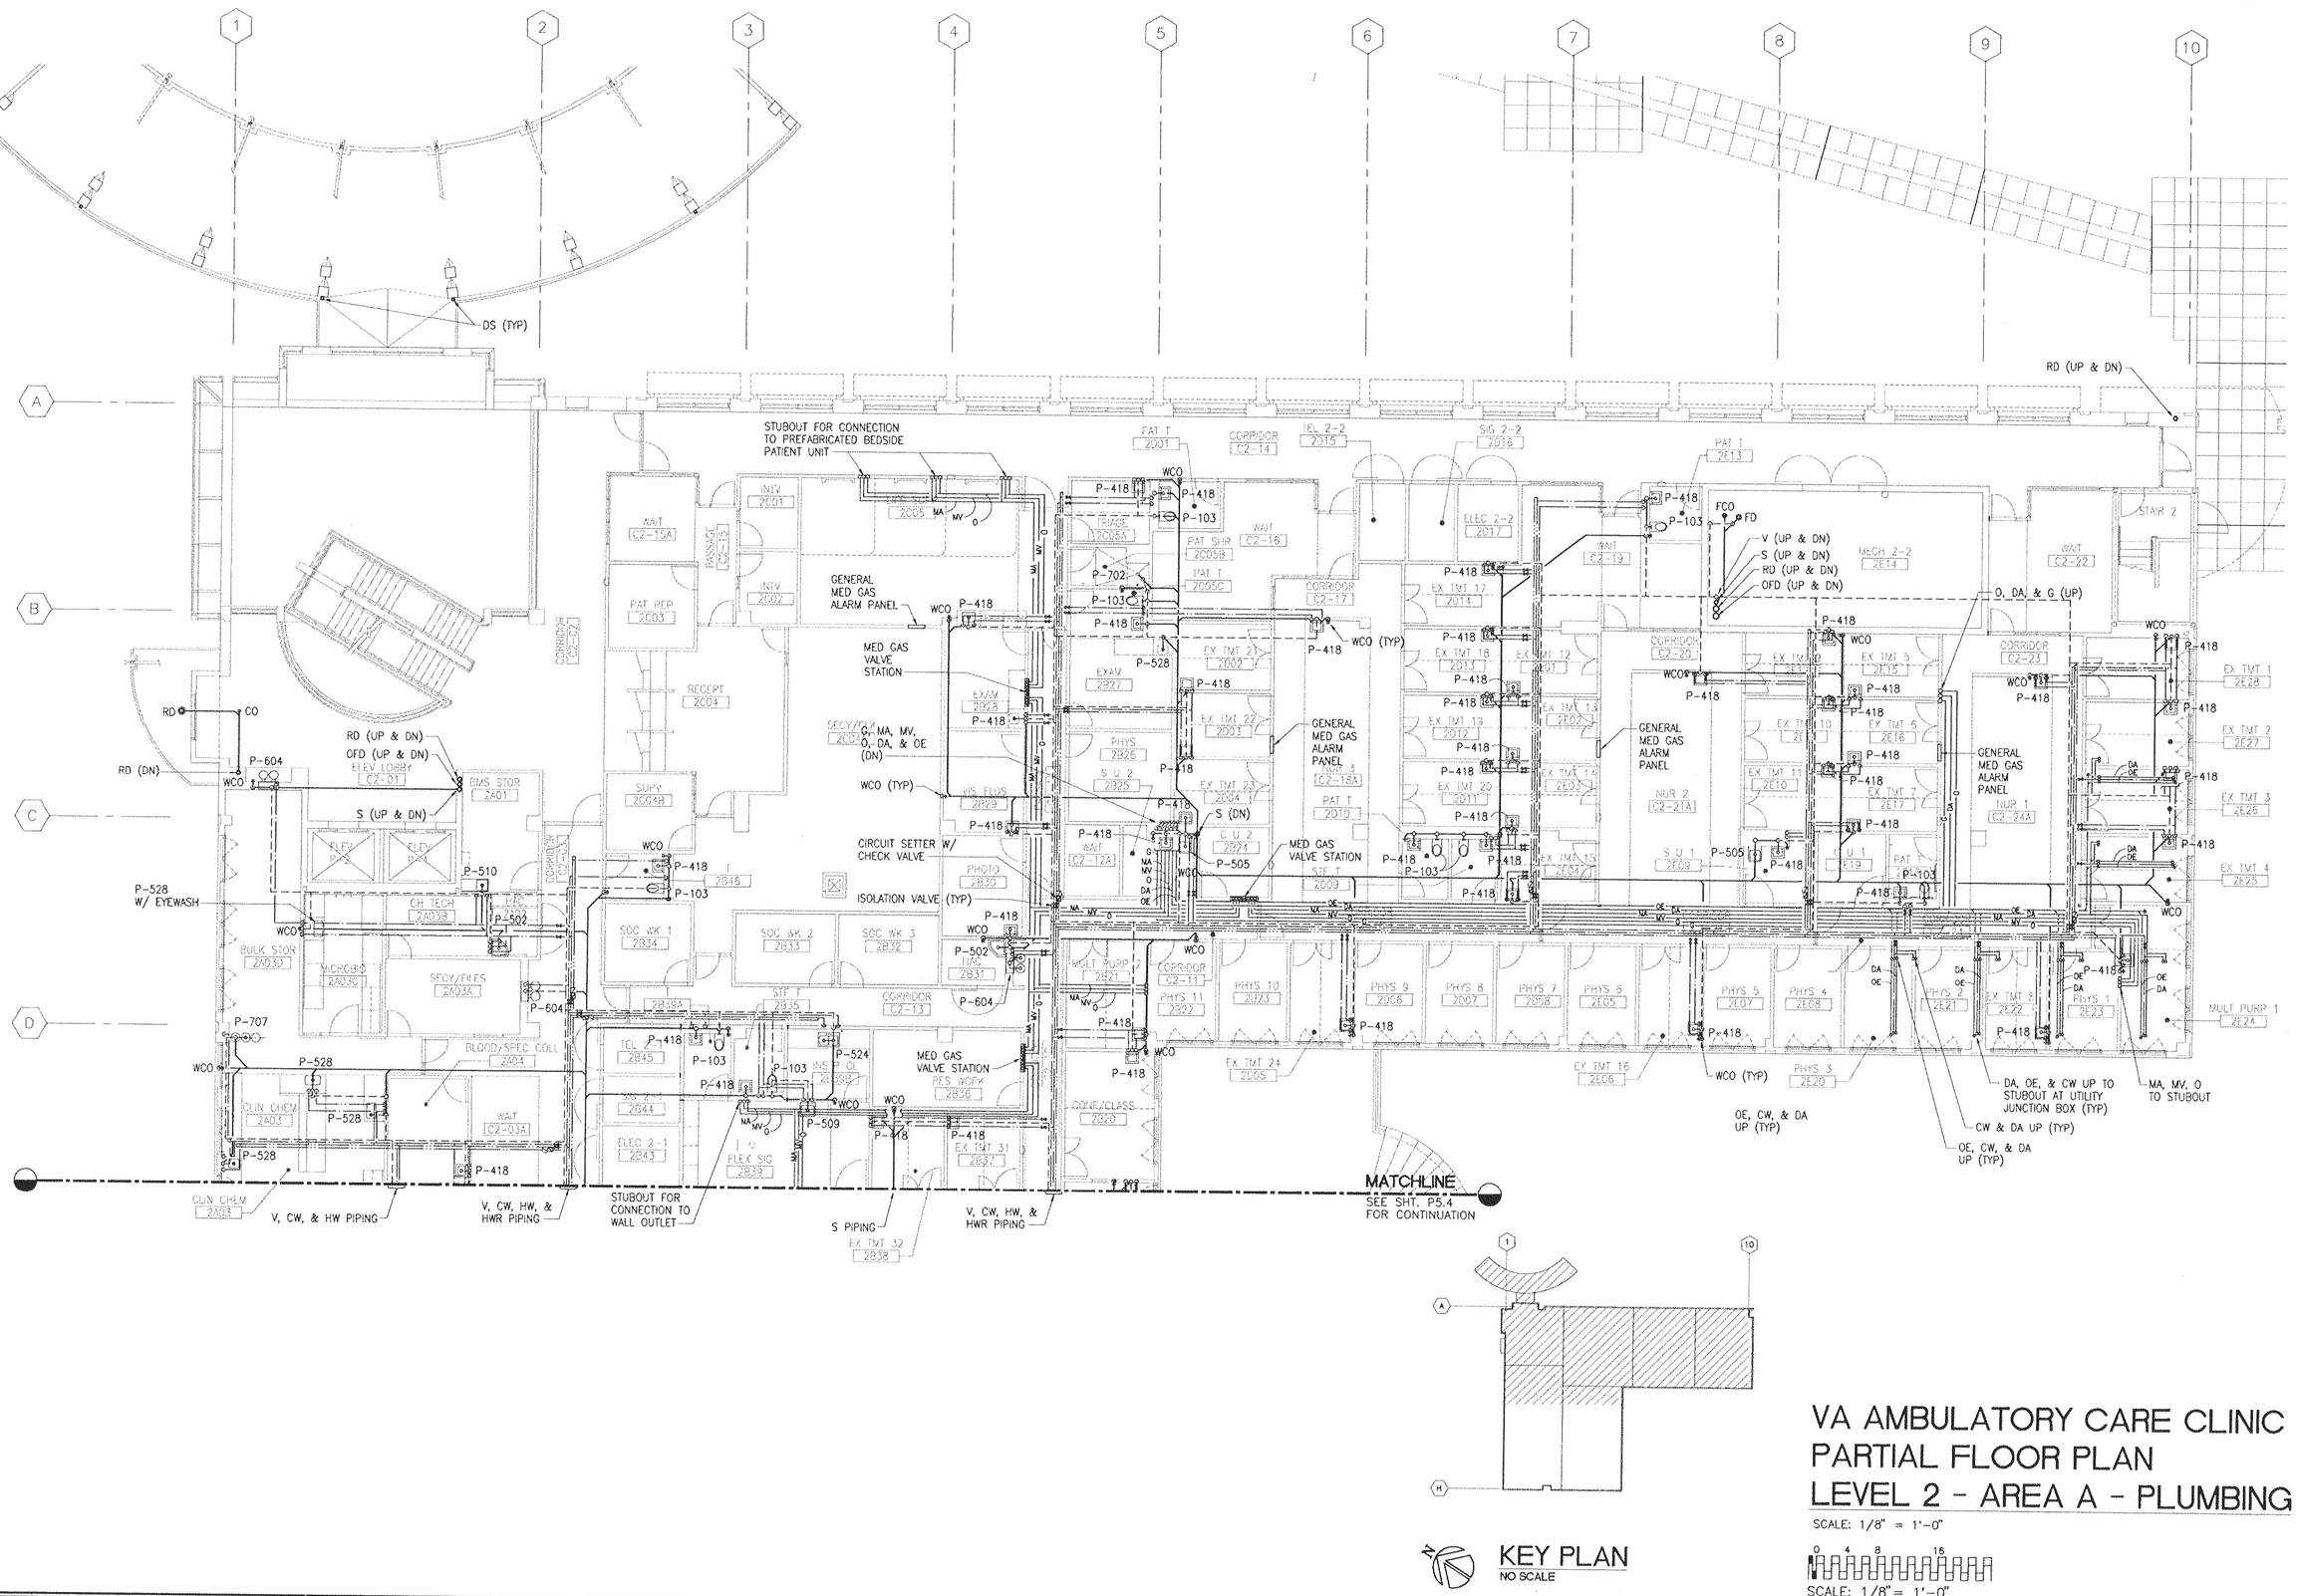


KEY PLAN
NO SCALE

VA AMBULATORY CARE CLINIC
PARTIAL FLOOR PLAN
LEVEL 2 - AREA A - PLUMBING

SCALE: 1/8" = 1'-0"

0 4 8 16

SCALE: 1/8" = 1'-0"

Revisions	Date

ARCHITECTS HAWAII LIMITED
1001 Bishop Street, Pacific 300
Honolulu, Hawaii 96813
Telephone: (808) 523-9636
FAX: (808) 521-3280

This work was prepared by me or under my supervision and construction of this project will be under my supervision.

Signature

NOTE: Contractor to check and verify all dimensions at job before proceeding with work.

JOEL P. YUEN LICENSED PROFESSIONAL ENGINEER No. 5805-M HAWAII, U.S.A.

Drawing Title: LEVEL 2 AREA A PLUMBING PLAN

Approved: Area Project Manager

Project Title: AMBULATORY CARE AND RENOVATE E-WING PHASE I, AMBULATORY CARE CLINIC

Building Number: 30 | Checked: | Drawn:

Location: VAMROC, HONOLULU, HAWAII

Date: DEC 23, 1996

Project No.: 459-002A

Drawing No.: P5.3

Dwg. Of

Department of Veterans Affairs