US Army Corps of Engineers ®

GMHILL | Michael Baker INTERNATIONAL JOINT VENTURE

MAINTENANCE AND RENOVATION ARMY RESERVE B56767- ECS
ARMY RESERVE CENTER
NORTH CAVAZOS, TX

PN: 096397

P2 #: 515198

26 March 2025

W912QR25RA013

25-02-10


SCHEDULE - SHEET INDEX

Sheet Information	
Number	**Name**
GENERAL	
G-001	COVER SHEET
CIVIL	
V-100	OVERALL EXISTING CONDITIOINS PLAN
V-101	EXISTING CONDITIONS PLAN
V-102	EXISTING CONDITIONS PLAN
V-103	EXISTING CONDITIONS PLAN
V-104	EXISTING CONDITIONS PLAN
V-105	EXISTING CONDITIONS PLAN
V-106	EXISTING CONDITIONS PLAN
V-107	EXISTING CONDITIONS PLAN
V-401	EXISTING CONDITIONS PLAN ENLARGED AREAS
V-402	EXISTING CONDITIONS PLAN ENLARGED AREAS
C-101	WATERLINE BID OPTION
C-105	PROPOSED UTILITY PLAN
C-401	ENLARGED SITE PLAN
C-402	ENLARGED SITE PLAN
ARCHITECTURE	
A-001	ABBREVIATIONS
AD101	DEMOLITION PLAN
A-101	OVERALL FLOOR PLAN
A-102	FLOOR PLAN - AREA A
A-103	FLOOR PLAN - AREA B
A-104	ENLARGED FLOOR PLAN - AREA C
A-201	EXTERIOR ELEVATIONS
INTERIORS	
IF110	COMPREHENSIVE FURNITURE FLOOR PLAN - AREA A
IF112	COMPREHENSIVE FURNITURE FLOOR PLAN - AREA B

SITE LOCATION

VICINITY MAP

PROJECT LOCATION:
ECS 64
200 PARK AVE.
GATESVILLE, TX 76528

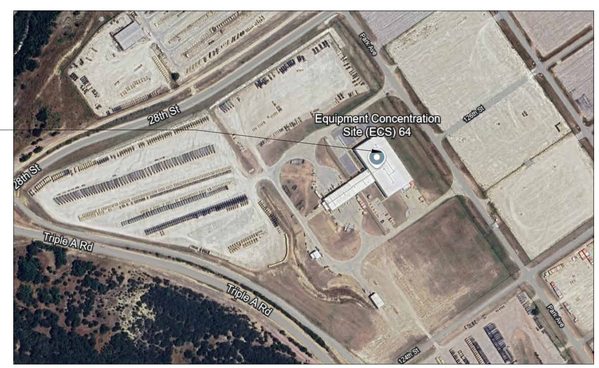

LOCATION MAP

US Army Corps of Engineers ®

ISSUE DATE:	25-02-10
SOLICITATION NO.:	
CONTRACT NO.:	
PLOT DATE:	2/7/2025 12:12:54 PM
FILENAME:	US-XXXXXA-G-001
DESIGNED BY:	KHR
DRAWN BY:	KHR
CHECKED BY:	TED
SUBMITTED BY:	NAB
SIZE:	ANSI D

US ARMY CORPS OF ENGINEERS
LOUISVILLE DISTRICT
600 DR MARTIN LUTHER KING JR PL.
LOUISVILLE, KY 40202

GMHILL | Michael Baker INTERNATIONAL JOINT VENTURE

MAINTENANCE AND REPAIR ARMY RESERVE (ECS)
NORTH CAVAZOS, TX
BUILDING B56767

COVER SHEET


SHEET ID

G-001

MARK	DESCRIPTION	DATE

File Path: C:\Users\Karen.Rutter\Documents\Ft Cavazos_Karen.rutter4VW2G1.rvt

PHASE 1 ADVERTISEMENT W912QR25RA013_Plans_Ph1-0000

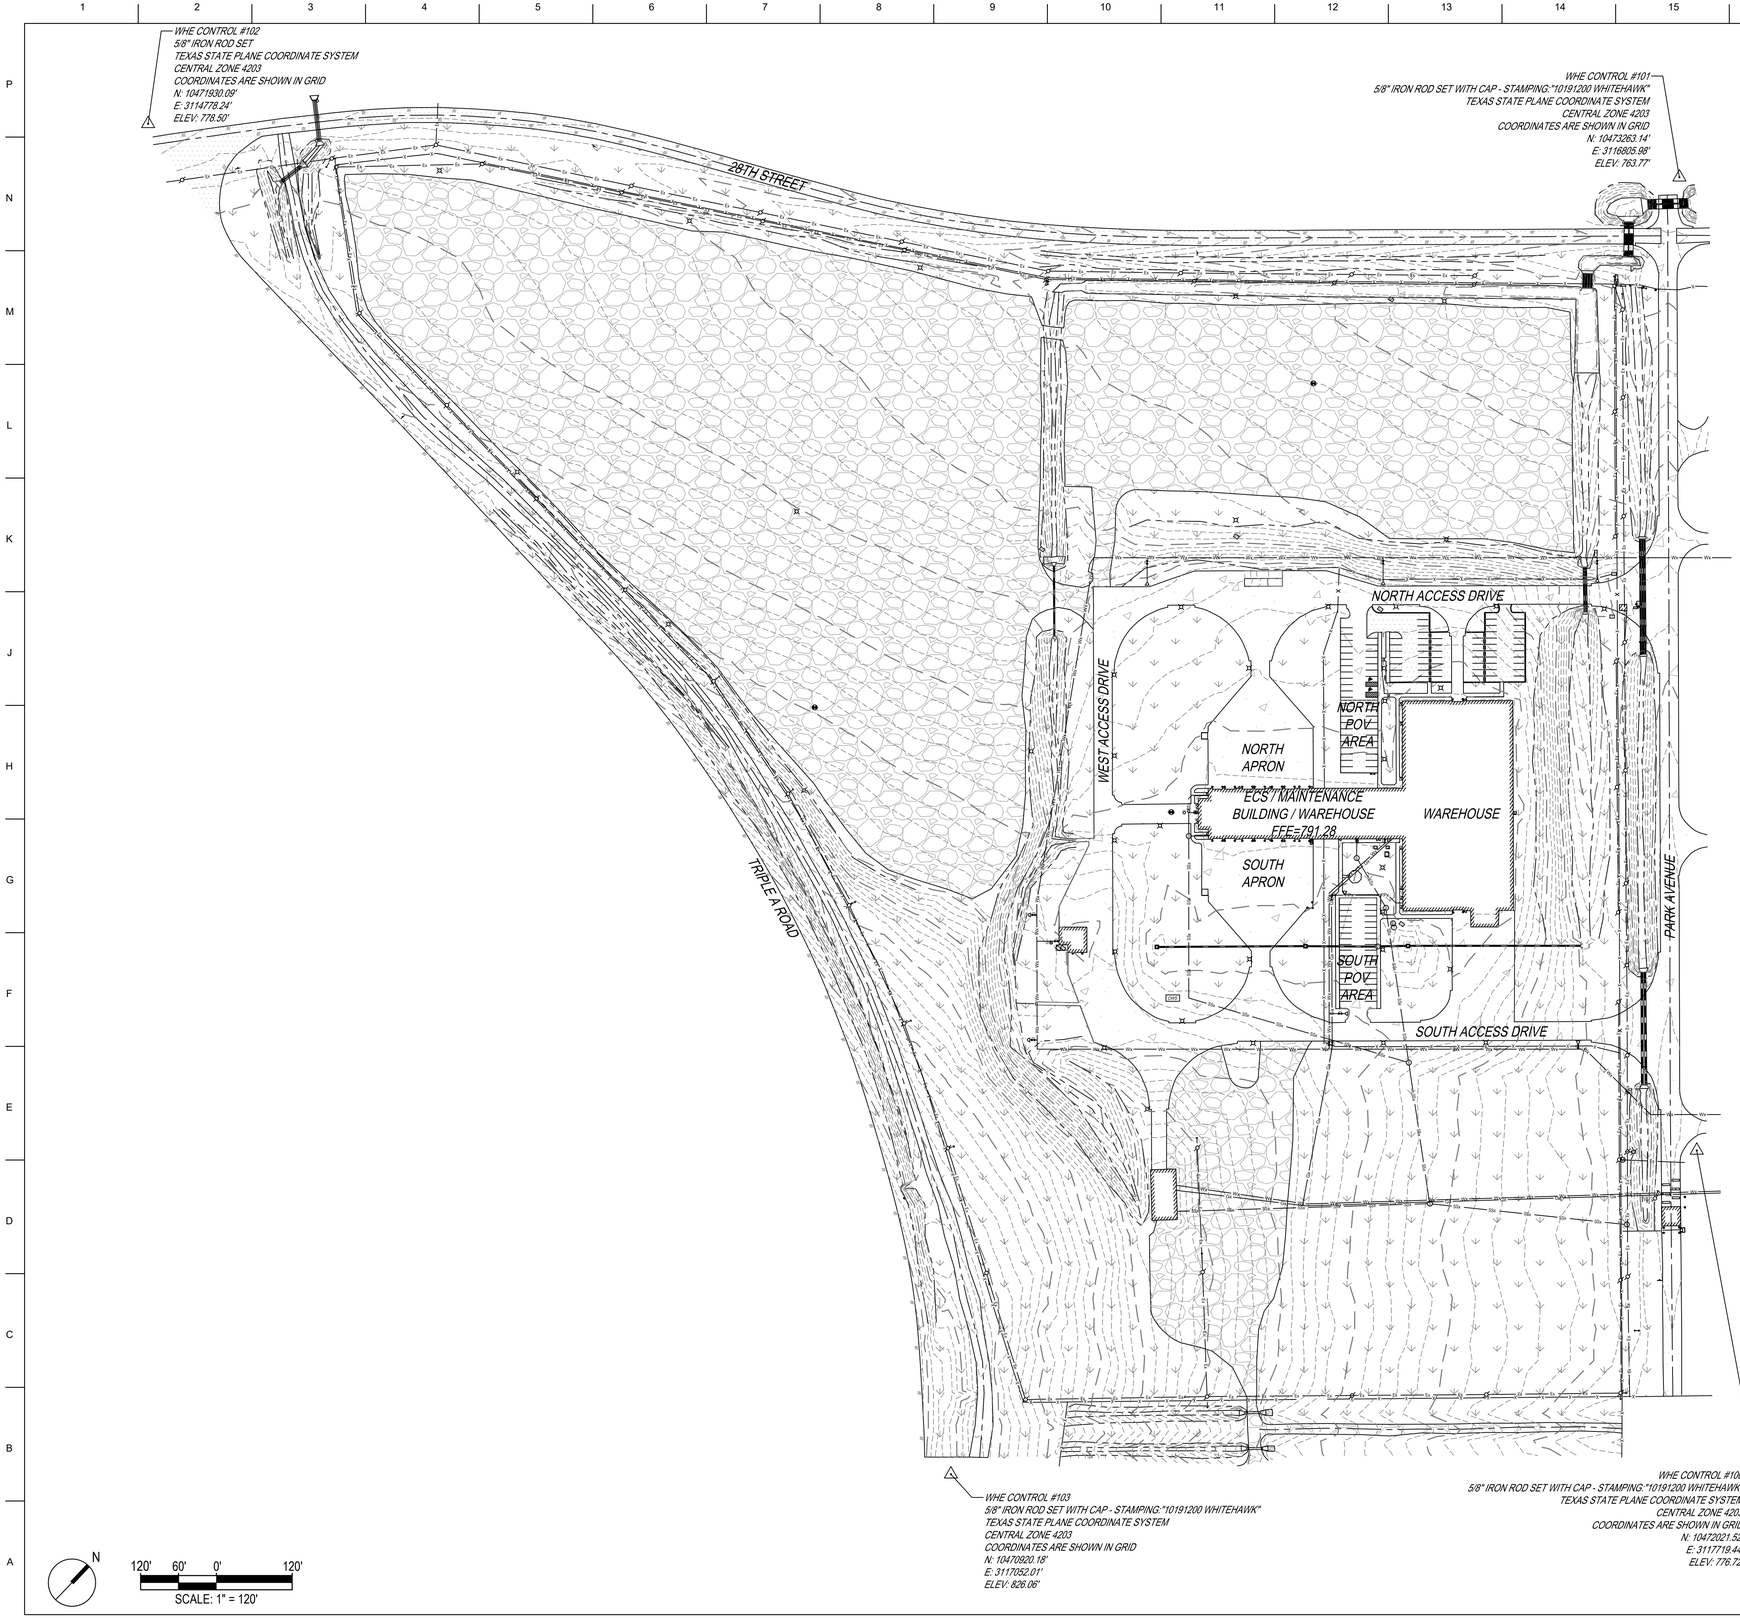

EXISTING LEGEND

- MAJOR CONTOURS
- MINOR CONTOURS
- FENCE
- AIR CONDITIONER
- LIGHT POLE
- SIGN
- FIRE HYDRANT
- WATER VALVE
- SECURITY CAMERA
- SECURITY KEYPAD
- BOLLARD
- PULLBOX
- POWER POLE
- VAULT
- UTILITY MARKER
- REFLECTOR
- FIBER OPTICS METER
- SANITARY SEWER MANHOLE
- TRANSFORMER
- CLEAN OUT
- GATE CONTROL BOX
- TELEPHONE PEDESTAL
- OVERHEAD UTILITY
- SANITARY SEWER
- GAS METER
- GAS VALVE
- GUY ANCHOR
- UNKNOWN MANHOLE
- 2' X 2' STORM SEWER INLET
- STORM MANHOLE
- ELECTRIC MANHOLE
- TELEPHONE MANHOLE
- BORE HOLE
- SURVEY CONTROL POINT
- STORM SEWER LINE
- GRAVEL
- RIP RAP
- NATURAL GROUND
- CONCRETE
- ASPHALT
- GAS LINE
- WATER LINE
- FIRE PROTECTION LINE

GENERAL NOTES

1. THE INFORMATION ON THIS DRAWING IS PRELIMINARY AND NOT TO BE USED FOR CONSTRUCTION. THE CONTRACTOR WILL BE RESPONSIBLE FOR ALL WORK ASSOCIATED WITH THE FINAL PROJECT SCOPE AND IT'S DESIGN AND CONSTRUCTION REQUIREMENTS. THIS DOCUMENT IS NOT INTENDED TO CONVEY AN DESIGN; RATHER, ONLY SCOPE AND PRELIMINARY COST ESTIMATING. THE CONTRACTOR IS RESPONSIBLE TO CONFIRM ALL FIELD CONDITIONS AND IS RESPONSIBLE FOR THE COMPLETE DESIGN AND CONSTRUCTION OF THE PROJECT.
2. EXISTING CONDITIONS INFORMATION SHOWN ON THESE DRAWINGS ARE BASED ON AVAIALBLE A SURVEY PERFORMED BY WHITE HAWK ENGINEERS PROVIDED ON JANUARY 13, 2025, AND ON AERIAL IMAGERY AND DOCUMENTATION PROVIDED IN THE REQUEST FOR PROPOSAL ATTACHMENTS OR PUBLICALLY AVAILABLE INFORMATION

US Army Corps of Engineers ®

MARK	DESCRIPTION	DATE

DESIGNED BY: J. PRITCHARD
DRAWN BY: R.DOYLE
CHECKED BY: J. PRITCHARD-SHEFFER
SUBMITTED BY: R. PARRISH
SIZE: ANSI D
ISSUE DATE: 25-02-10
SOLICITATION NO.:
CONTRACT NO.:
PLOT DATE: 2/6/2025 11:17 AM
FILENAME: 204020_V-10X.DWG

US ARMY CORPS OF ENGINEERS
LOUISVILLE DISTRICT
MICHAEL J. SMITH FEDERAL BUILDING
600 DR. MARTIN LUTHER KING JR. PL.
LOUISVILLE, KY 40202

GMHILL Michael Baker INTERNATIONAL

FORT CAVAZOV, TX
ECS / MAINTENANCE BUILDING / WAREHOUSE

OVERALL EXISTING CONDITIONS PLAN


SHEET ID
V-100

PHASE 1 ADVERTISEMENT W912QR25RA013_Plans_Ph1-0000

GENERAL NOTES

1. THE INFORMATION ON THIS DRAWING IS PRELIMINARY AND NOT TO BE USED FOR CONSTRUCTION. THE CONTRACTOR WILL BE RESPONSIBLE FOR ALL WORK ASSOCIATED WITH THE FINAL PROJECT SCOPE AND IT'S DESIGN AND CONSTRUCTION REQUIREMENTS. THIS DOCUMENT IS NOT INTENDED TO CONVEY AN DESIGN; RATHER, ONLY SCOPE AND PRELIMINARY COST ESTIMATING. THE CONTRACTOR IS RESPONSIBLE TO CONFIRM ALL FIELD CONDITIONS AND IS RESPONSIBLE FOR THE COMPLETE DESIGN AND CONSTRUCTION OF THE PROJECT.


2. EXISTING CONDITIONS INFORMATION SHOWN ON THESE DRAWINGS ARE BASED ON AVAIALBLE A SURVEY PERFORMED BY WHITE HAWK ENGINEERS PROVIDED ON JANUARY 13, 2025, AND ON AERIAL IMAGERY AND DOCUMENTATION PROVIDED IN THE REQUEST FOR PROPOSAL ATTACHMENTS OR PUBLICALLY AVAILABLE INFORMATION

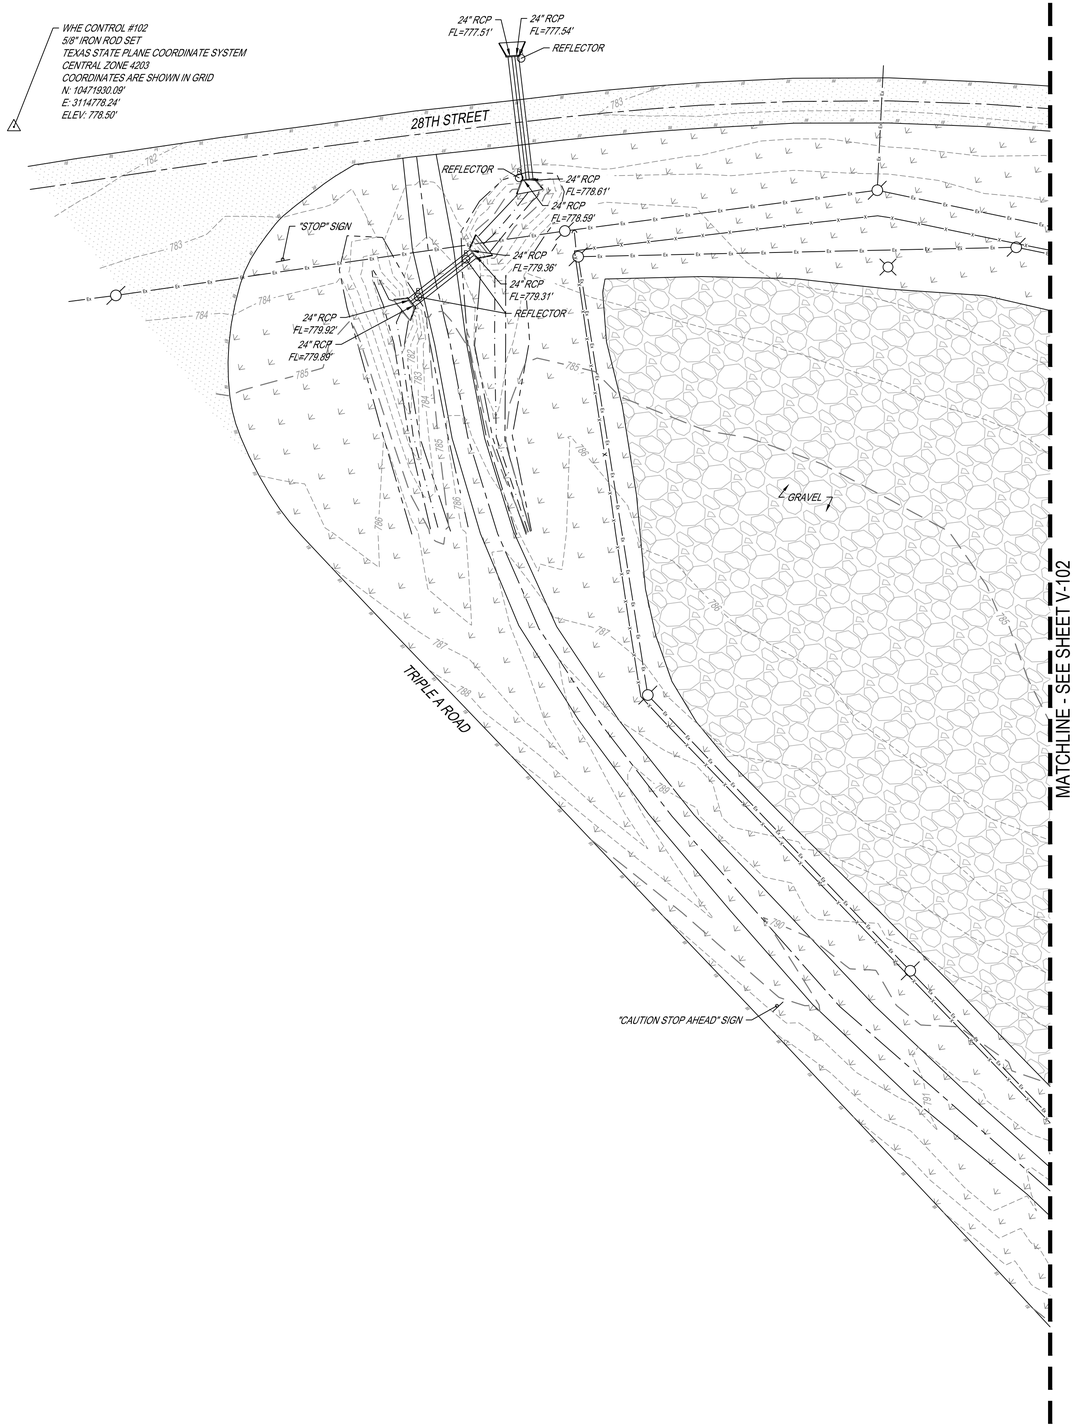

EXISTING LEGEND

- MAJOR CONTOURS
- MINOR CONTOURS
- FENCE
- AIR CONDITIONER
- LIGHT POLE
- SIGN
- FIRE HYDRANT
- WATER VALVE
- SECURITY CAMERA
- SECURITY KEYPAD
- BOLLARD
- PULLBOX
- POWER POLE
- VAULT
- UTILITY MARKER
- REFLECTOR
- FIBER OPTICS METER
- SANITARY SEWER MANHOLE
- TRANSFORMER
- CLEAN OUT
- GATE CONTROL BOX
- TELEPHONE PEDESTAL
- OVERHEAD UTILITY
- SANITARY SEWER
- GAS METER
- GAS VALVE
- GUY ANCHOR
- UNKNOWN MANHOLE
- 2' X 2' STORM SEWER INLET
- STORM MANHOLE
- ELECTRIC MANHOLE
- TELEPHONE MANHOLE
- BORE HOLE
- SURVEY CONTROL POINT
- STORM SEWER LINE
- GRAVEL
- RIP RAP
- NATURAL GROUND
- CONCRETE
- ASPHALT
- GAS LINE
- WATER LINE
- FIRE PROTECTION LINE

KEY PLAN

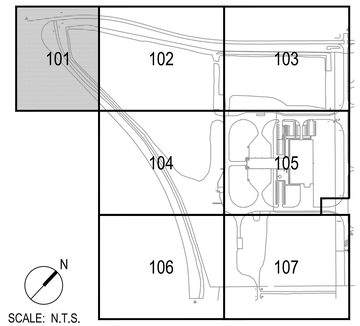

SCALE: N.T.S.

N

40' 20' 0' 40'

SCALE: 1" = 40'

US Army Corps of Engineers ®

MARK	DESCRIPTION	DATE

US ARMY CORPS OF ENGINEERS
LOUISVILLE DISTRICT
MICHAEL J. SLAVEN FEDERAL BUILDING
600 DR. MARTIN LUTHER KING JR. PL.
LOUISVILLE, KY 40202

GM HILL Michael Baker INTERNATIONAL

DESIGNED BY: J. PRITCHARD	ISSUE DATE: 25-02-10
DRAWN BY: R.DOYLE	SOLICITATION NO.:
CHECKED BY: B. CHESTERFER	CONTRACT NO.:
SUBMITTED BY: R. PARRISH	PLOT DATE: 2/6/2026 11:17 AM
SIZE: ANSI D	FILENAME: 204020_V-10X.DWG

FORT CAVAZZOV, TX
ECS / MAINTENANCE BUILDING / WAREHOUSE

EXISTING CONDITIONS PLAN


SHEET ID

V-101

PHASE 1 ADVERTISEMENT W912QR25RA013_Plans_Ph1-0000

GENERAL NOTES


1. THE INFORMATION ON THIS DRAWING IS PRELIMINARY AND NOT TO BE USED FOR CONSTRUCTION. THE CONTRACTOR WILL BE RESPONSIBLE FOR ALL WORK ASSOCIATED WITH THE FINAL PROJECT SCOPE AND IT'S DESIGN AND CONSTRUCTION REQUIREMENTS. THIS DOCUMENT IS NOT INTENDED TO CONVEY AN DESIGN; RATHER, ONLY SCOPE AND PRELIMINARY COST ESTIMATING. THE CONTRACTOR IS RESPONSIBLE TO CONFIRM ALL FIELD CONDITIONS AND IS RESPONSIBLE FOR THE COMPLETE DESIGN AND CONSTRUCTION OF THE PROJECT.
2. EXISTING CONDITIONS INFORMATION SHOWN ON THESE DRAWINGS ARE BASED ON AVAIALBLE A SURVEY PERFORMED BY WHITE HAWK ENGINEERS PROVIDED ON JANUARY 13, 2025, AND ON AERIAL IMAGERY AND DOCUMENTATION PROVIDED IN THE REQUEST FOR PROPOSAL ATTACHMENTS OR PUBLICALLY AVAILABLE INFORMATION

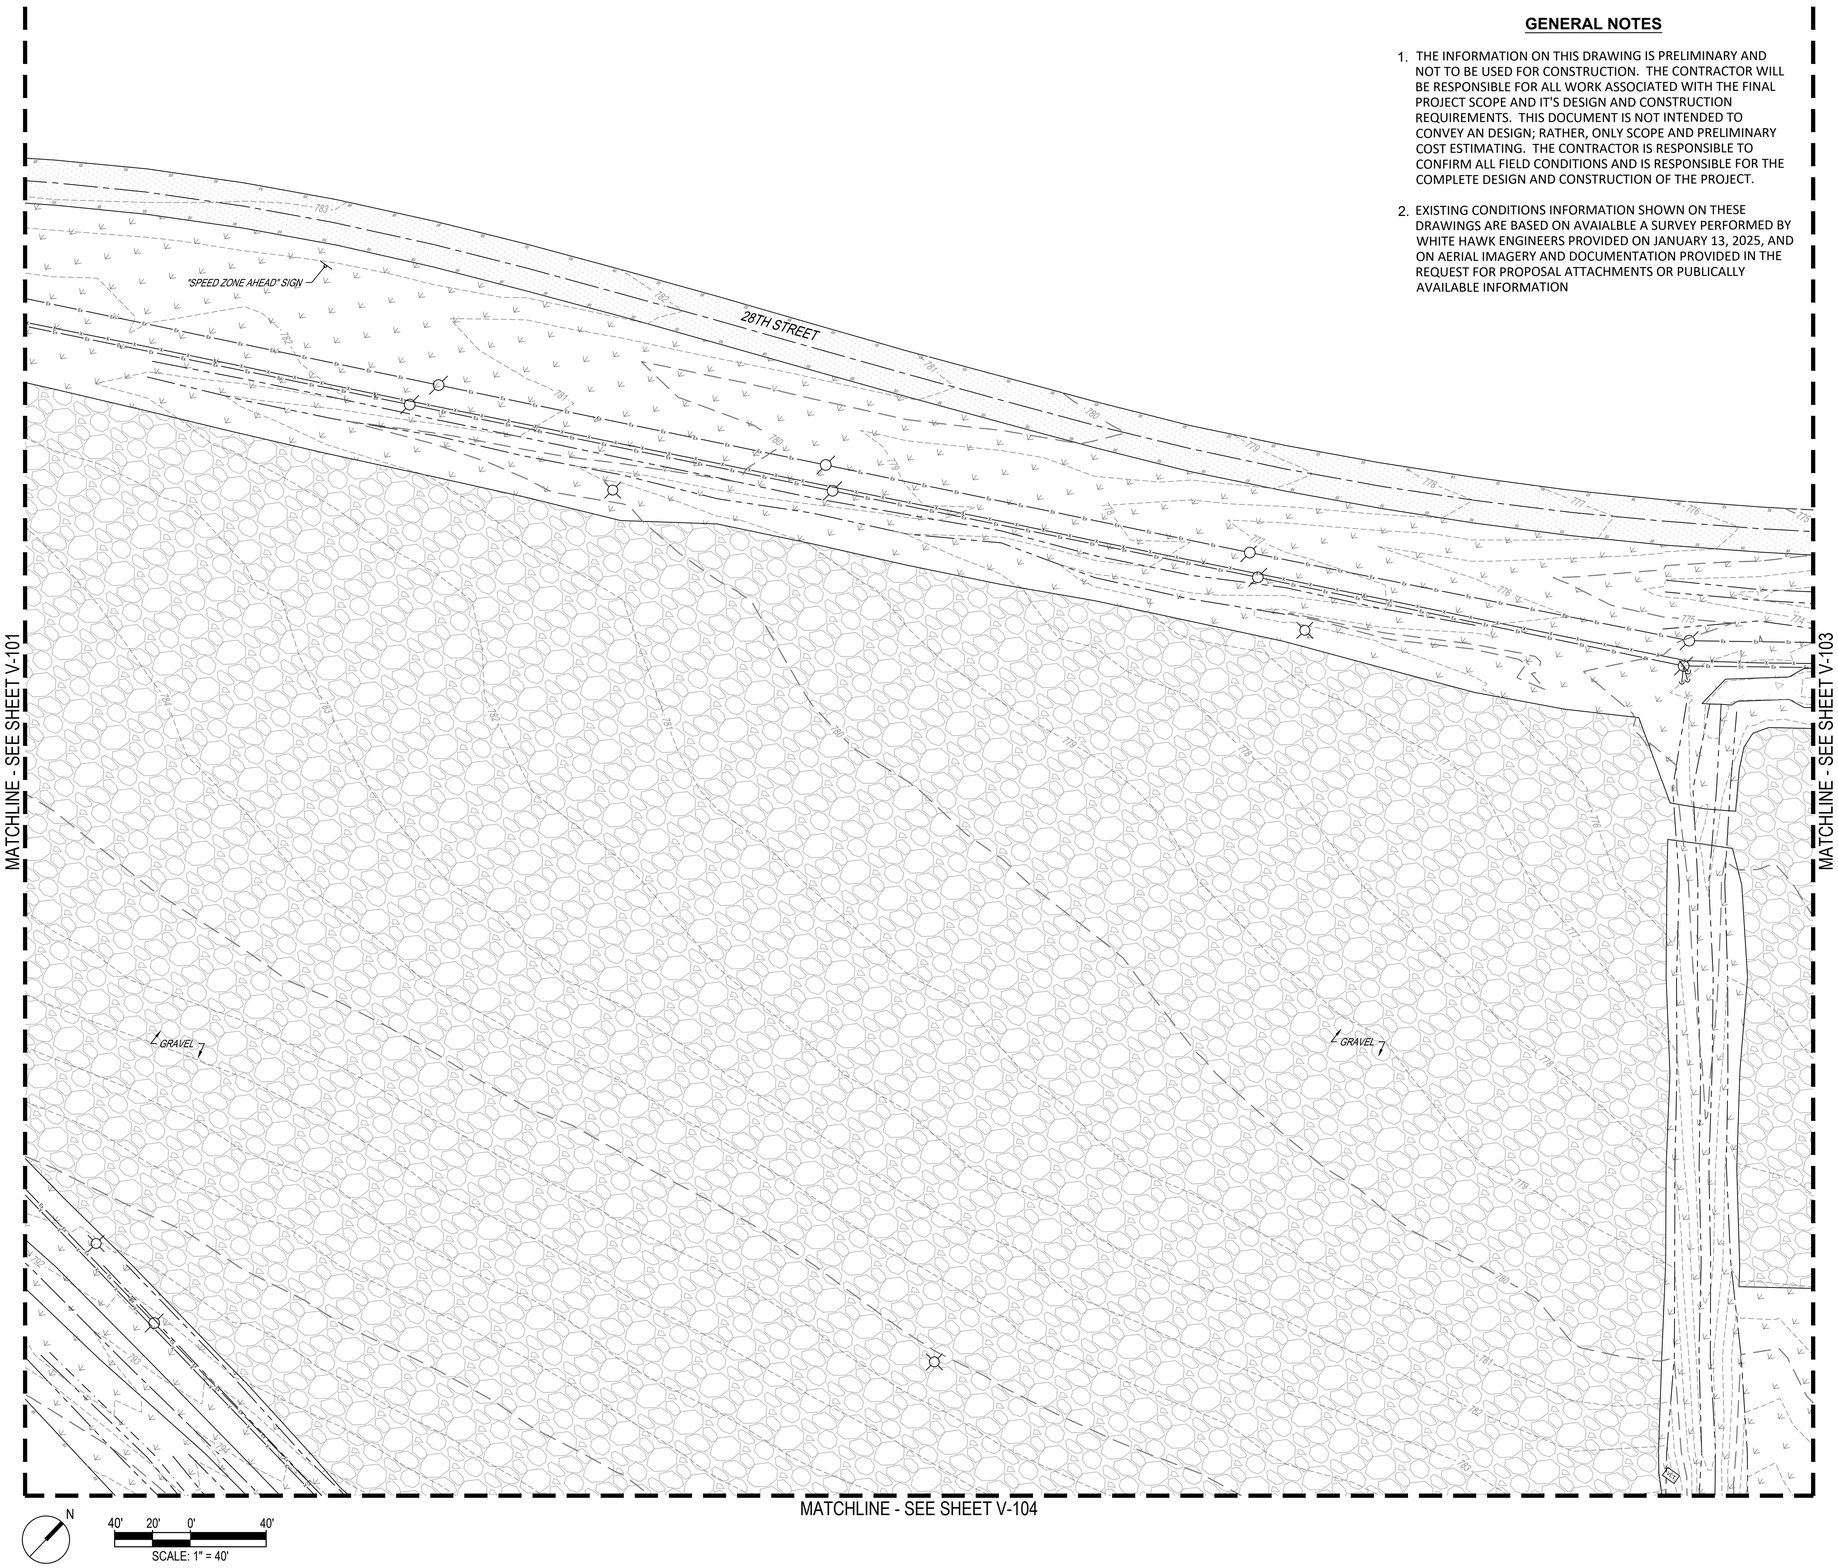

EXISTING LEGEND

- MAJOR CONTOURS
- MINOR CONTOURS
- FENCE
- AIR CONDITIONER
- LIGHT POLE
- SIGN
- FIRE HYDRANT
- WATER VALVE
- SECURITY CAMERA
- SECURITY KEYPAD
- BOLLARD
- PULLBOX
- POWER POLE
- VAULT
- UTILITY MARKER
- REFLECTOR
- FIBER OPTICS METER
- SANITARY SEWER MANHOLE
- TRANSFORMER
- CLEAN OUT
- GATE CONTROL BOX
- TELEPHONE PEDESTAL
- OVERHEAD UTILITY
- SANITARY SEWER
- GAS METER
- GAS VALVE
- GUY ANCHOR
- UNKNOWN MANHOLE
- 2' X 2' STORM SEWER INLET
- STORM MANHOLE
- ELECTRIC MANHOLE
- TELEPHONE MANHOLE
- BORE HOLE
- SURVEY CONTROL POINT
- STORM SEWER LINE
- GRAVEL
- RIP RAP
- NATURAL GROUND
- CONCRETE
- ASPHALT
- GAS LINE
- WATER LINE
- FIRE PROTECTION LINE

KEY PLAN

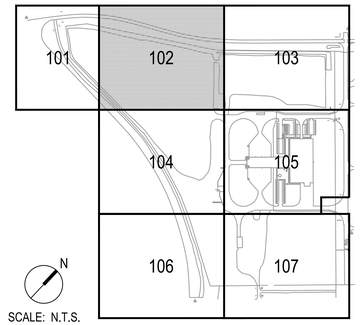

US Army Corps of Engineers ®

MARK	DESCRIPTION	DATE

ISSUE DATE:	25-02-10
SOLICITATION NO.:	
CONTRACT NO.:	
PLOT DATE:	2/6/2025 11:17 AM
FILENAME:	204020_V-10X.DWG
DESIGNED BY:	J. PRITCHARD
DRAWN BY:	R.DOYLE
CHECKED BY:	C. HEFFERNAN/J. PERFER
SUBMITTED BY:	R. PARRISH
SIZE:	ANSI D

US ARMY CORPS OF ENGINEERS
LOUISVILLE DISTRICT
600 DR. MARTIN LUTHER KING JR. PL.
LOUISVILLE, KY 40202

GM HILL Michael Baker INTERNATIONAL

FORT CAVAZOV, TX
ECS / MAINTENANCE BUILDING / WAREHOUSE


EXISTING CONDITIONS PLAN

SHEET ID
V-102

PHASE 1 ADVERTISEMENT W912QR25RA013_Plans_Ph1-0000

GENERAL NOTES


1. THE INFORMATION ON THIS DRAWING IS PRELIMINARY AND NOT TO BE USED FOR CONSTRUCTION. THE CONTRACTOR WILL BE RESPONSIBLE FOR ALL WORK ASSOCIATED WITH THE FINAL PROJECT SCOPE AND IT'S DESIGN AND CONSTRUCTION REQUIREMENTS. THIS DOCUMENT IS NOT INTENDED TO CONVEY AN DESIGN; RATHER, ONLY SCOPE AND PRELIMINARY COST ESTIMATING. THE CONTRACTOR IS RESPONSIBLE TO CONFIRM ALL FIELD CONDITIONS AND IS RESPONSIBLE FOR THE COMPLETE DESIGN AND CONSTRUCTION OF THE PROJECT.
2. EXISTING CONDITIONS INFORMATION SHOWN ON THESE DRAWINGS ARE BASED ON AVAIALBLE A SURVEY PERFORMED BY WHITE HAWK ENGINEERS PROVIDED ON JANUARY 13, 2025, AND ON AERIAL IMAGERY AND DOCUMENTATION PROVIDED IN THE REQUEST FOR PROPOSAL ATTACHMENTS OR PUBLICALLY AVAILABLE INFORMATION

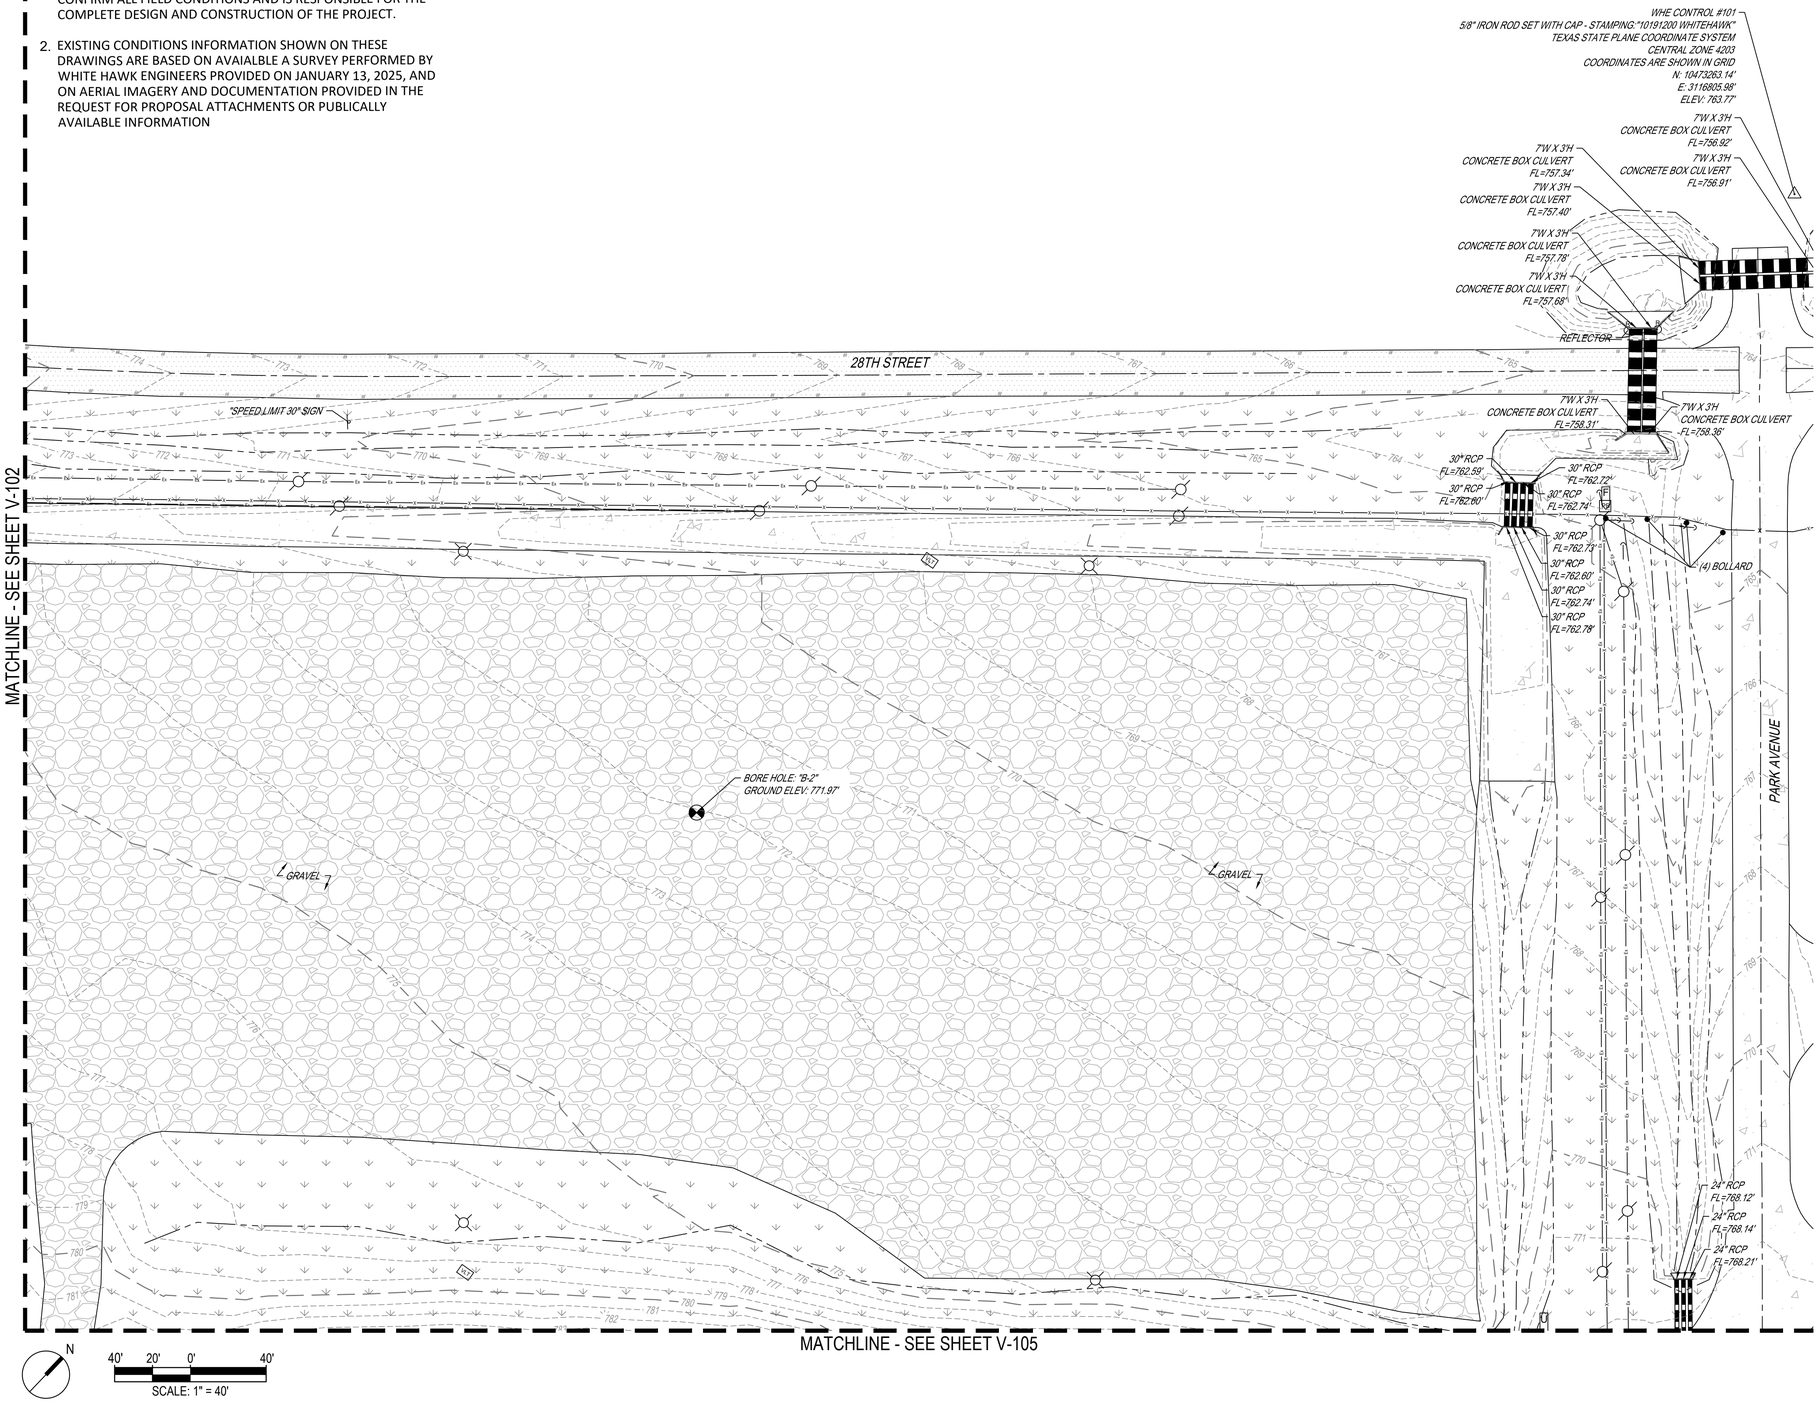

EXISTING LEGEND

- MAJOR CONTOURS
- MINOR CONTOURS
- FENCE
- AIR CONDITIONER
- LIGHT POLE
- SIGN
- FIRE HYDRANT
- WATER VALVE
- SECURITY CAMERA
- SECURITY KEYPAD
- BOLLARD
- PULLBOX
- POWER POLE
- VAULT
- UTILITY MARKER
- REFLECTOR
- FIBER OPTICS METER
- SANITARY SEWER MANHOLE
- TRANSFORMER
- CLEAN OUT
- GATE CONTROL BOX
- TELEPHONE PEDESTAL
- OVERHEAD UTILITY
- SANITARY SEWER
- GAS METER
- GAS VALVE
- GUY ANCHOR
- UNKNOWN MANHOLE
- 2' X 2' STORM SEWER INLET
- STORM MANHOLE
- ELECTRIC MANHOLE
- TELEPHONE MANHOLE
- BORE HOLE
- SURVEY CONTROL POINT
- STORM SEWER LINE
- GRAVEL
- RIP RAP
- NATURAL GROUND
- CONCRETE
- ASPHALT
- GAS LINE
- WATER LINE
- FIRE PROTECTION LINE

KEY PLAN

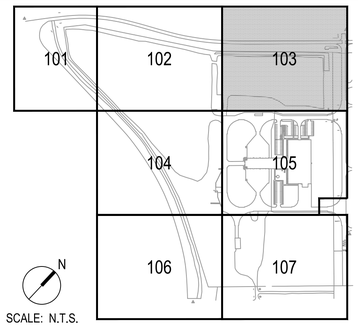

US Army Corps of Engineers ®

MARK	DESCRIPTION	DATE

DESIGNED BY: J. PRITCHARD
DRAWN BY: R.DOYLE
CHECKED BY: R. CHRISTOFFER
SUBMITTED BY: R. PARRISH
SIZE: ANSI D
ISSUE DATE: 25-02-10
SOLICITATION NO.:
CONTRACT NO.:
PLOT DATE: 2/6/2025 11:17 AM
FILENAME: 204020_V-10X.DWG

US ARMY CORPS OF ENGINEERS
LOUISVILLE DISTRICT
MISSISSIPPI VALLEY DIVISION
600 DR. MARTIN LUTHER KING JR. PL.
LOUISVILLE, KY 40202


Michael Baker INTERNATIONAL
GMHILL

FORT CAVAZOV, TX
ECS / MAINTENANCE BUILDING / WAREHOUSE

EXISTING CONDITIONS PLAN

SHEET ID
V-103

PHASE 1 ADVERTISEMENT W912QR25RA013_Plans_Ph1-0000

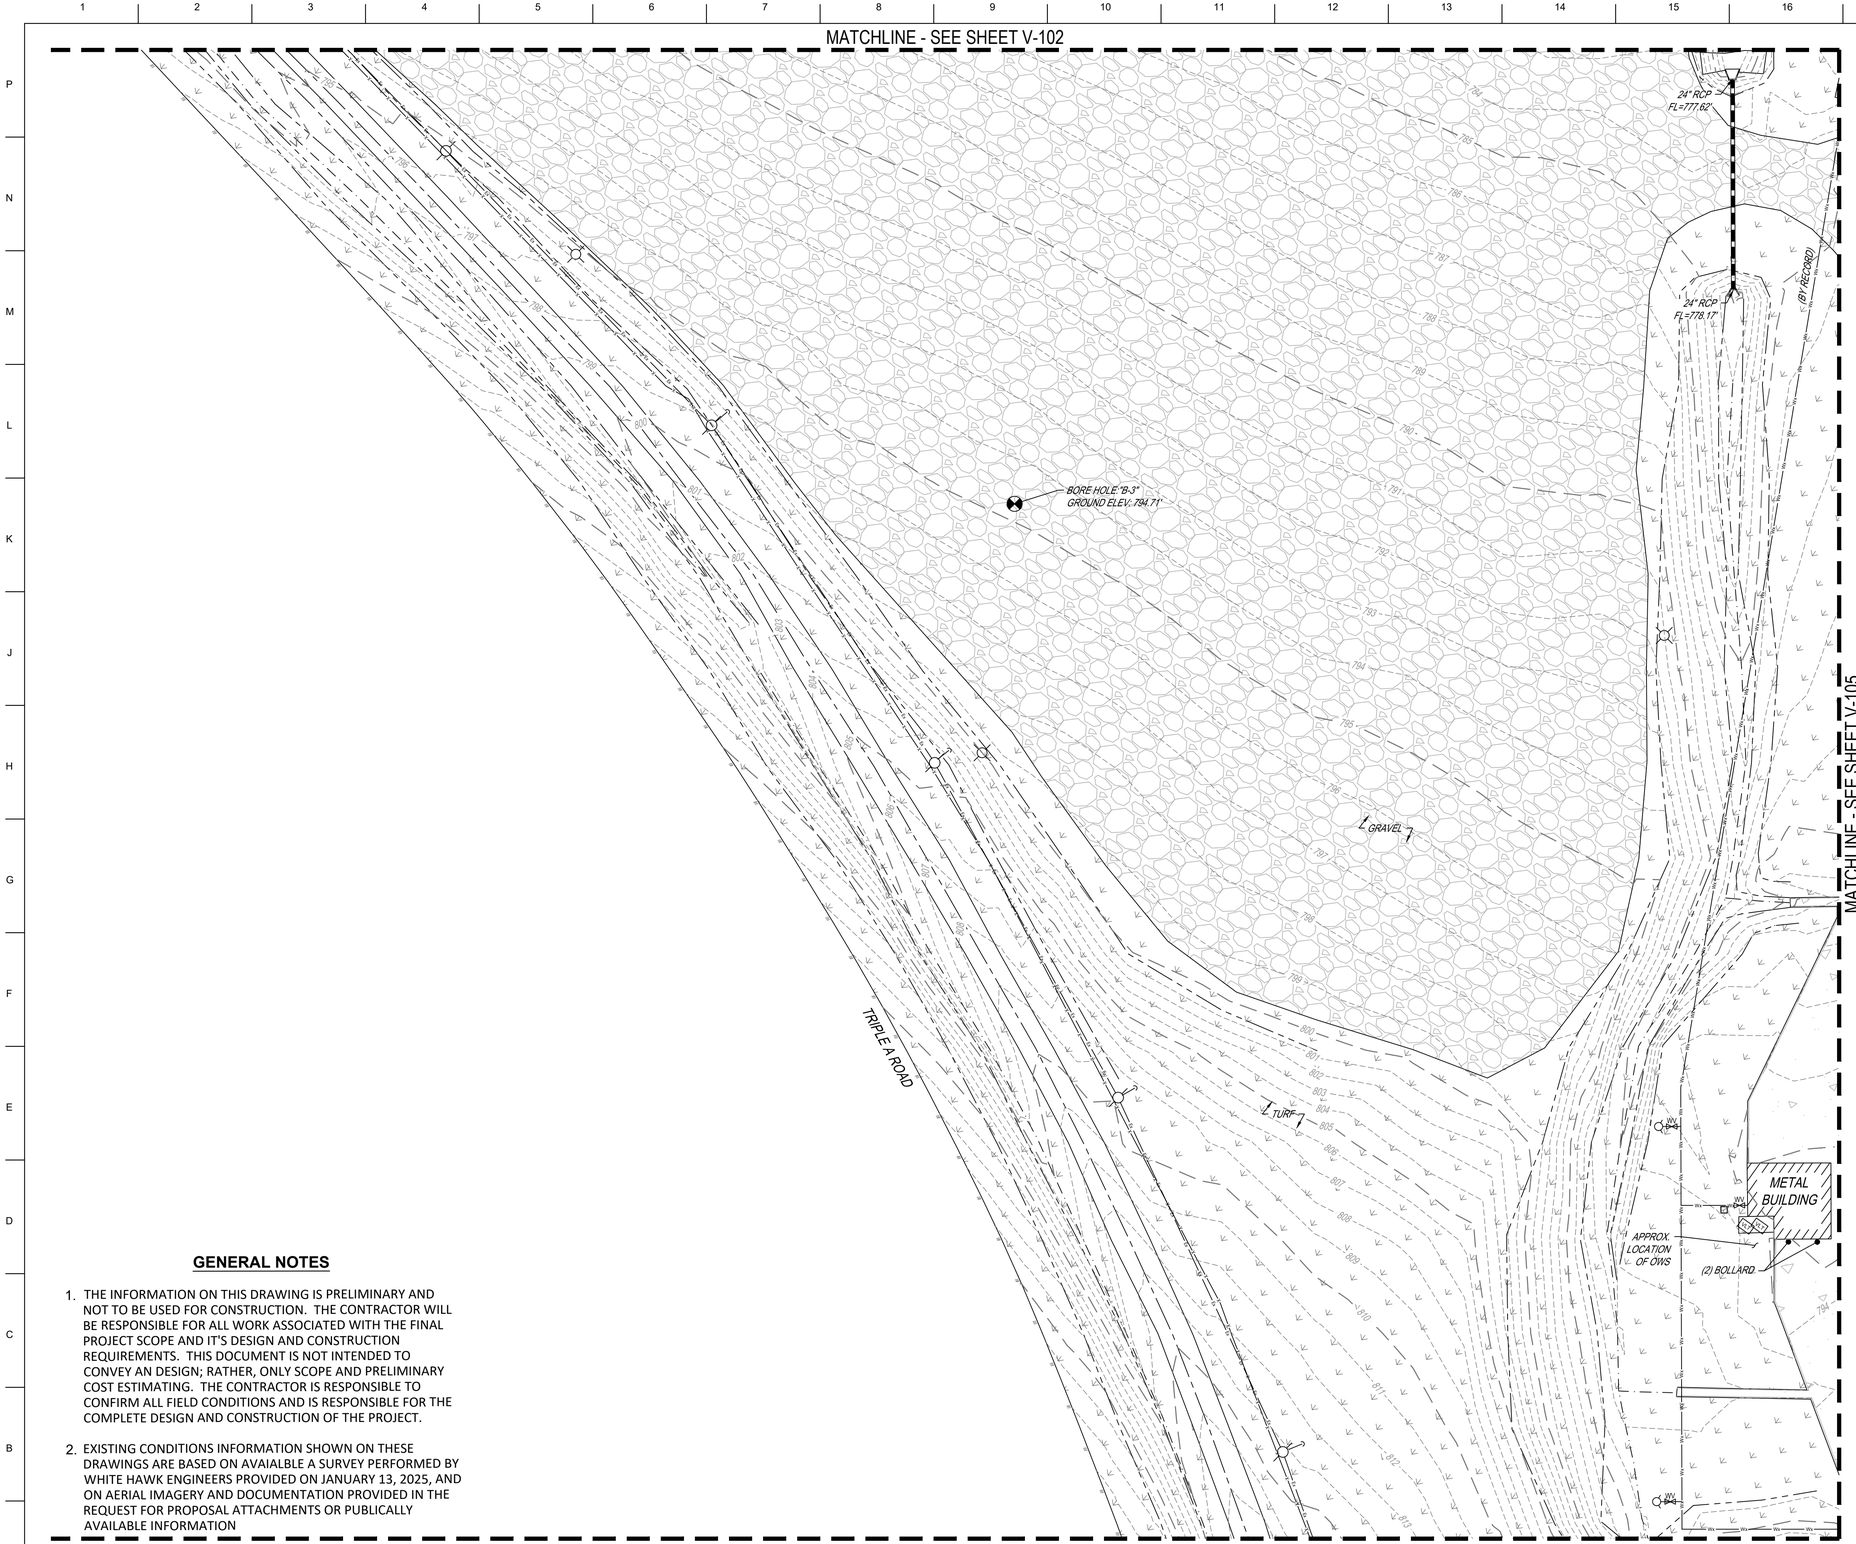

GENERAL NOTES


1. THE INFORMATION ON THIS DRAWING IS PRELIMINARY AND NOT TO BE USED FOR CONSTRUCTION. THE CONTRACTOR WILL BE RESPONSIBLE FOR ALL WORK ASSOCIATED WITH THE FINAL PROJECT SCOPE AND IT'S DESIGN AND CONSTRUCTION REQUIREMENTS. THIS DOCUMENT IS NOT INTENDED TO CONVEY AN DESIGN; RATHER, ONLY SCOPE AND PRELIMINARY COST ESTIMATING. THE CONTRACTOR IS RESPONSIBLE TO CONFIRM ALL FIELD CONDITIONS AND IS RESPONSIBLE FOR THE COMPLETE DESIGN AND CONSTRUCTION OF THE PROJECT.
2. EXISTING CONDITIONS INFORMATION SHOWN ON THESE DRAWINGS ARE BASED ON AVAIALBLE A SURVEY PERFORMED BY WHITE HAWK ENGINEERS PROVIDED ON JANUARY 13, 2025, AND ON AERIAL IMAGERY AND DOCUMENTATION PROVIDED IN THE REQUEST FOR PROPOSAL ATTACHMENTS OR PUBLICALLY AVAILABLE INFORMATION

N
40' 20' 0' 40'
SCALE: 1" = 40'

EXISTING LEGEND

- MAJOR CONTOURS
- MINOR CONTOURS
- FENCE
- AIR CONDITIONER
- LIGHT POLE
- SIGN
- FIRE HYDRANT
- WATER VALVE
- SECURITY CAMERA
- SECURITY KEYPAD
- BOLLARD
- PULLBOX
- POWER POLE
- VAULT
- UTILITY MARKER
- REFLECTOR
- FIBER OPTICS METER
- SANITARY SEWER MANHOLE
- TRANSFORMER
- CLEAN OUT
- GATE CONTROL BOX
- TELEPHONE PEDESTAL
- OVERHEAD UTILITY
- SANITARY SEWER
- GAS METER
- GAS VALVE
- GUY ANCHOR
- UNKNOWN MANHOLE
- 2' X 2' STORM SEWER INLET
- STORM MANHOLE
- ELECTRIC MANHOLE
- TELEPHONE MANHOLE
- BORE HOLE
- SURVEY CONTROL POINT
- STORM SEWER LINE
- GRAVEL
- RIP RAP
- NATURAL GROUND
- CONCRETE
- ASPHALT
- GAS LINE
- WATER LINE
- FIRE PROTECTION LINE

KEY PLAN

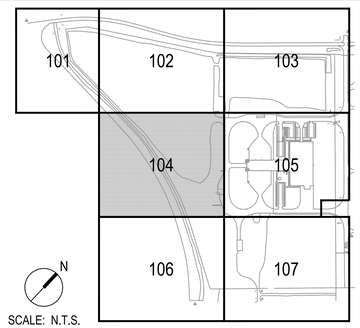

US Army Corps of Engineers ®

MARK	DESCRIPTION	DATE

ISSUE DATE:	25-02-10
SOLICITATION NO.:	
CONTRACT NO.:	
PLOT DATE:	2/6/2025 11:17 AM
FILENAME:	204020_V-10X.DWG
DESIGNED BY:	J. PRITCHARD
DRAWN BY:	R.DOYLE
CHECKED BY:	R. KEEFER
SUBMITTED BY:	R. PARRISH
SIZE:	ANSI D

US ARMY CORPS OF ENGINEERS
LOUISVILLE DISTRICT
MICHAEL J. HOGAN FEDERAL JR PL.
600 DR MARTIN LUTHER KING JR PL.
LOUISVILLE, KY 40202

Michael Baker INTERNATIONAL
GMHILL

FORT CAVAZOV, TX
ECS / MAINTENANCE BUILDING / WAREHOUSE

EXISTING CONDITIONS PLAN

SHEET ID
V-104

PHASE 1 ADVERTISEMENT W912QR25RA013_Plans_Ph1-0000

MATCHLINE - SEE SHEET V-103

MATCHLINE - SEE SHEET V-104

MATCHLINE - SEE SHEET V-107

NORTH ACCESS DRIVE

CONCRETE LOADING RAMP

TURF

NORTH APRON

WEST ACCESS DRIVE

NORTH POV AREA

NORTH WAREHOUSE ACCESS DRIVE

ASPHALT

ABA PARKING SIGN

(2) BOLLARD

"US ARMY RESERVE EQUIPMENT CONCENTRATION SITE 64" SIGN

(14) BOLLARD (TYP)

(BY RECORD)

BORE HOLE "B-1"
GROUND ELEV. 790.50'

ECS / MAINTENANCE BUILDING / WAREHOUSE
FFE=791.28

SEE ENLARGED PLAN (A1/V-402)

SEE ENLARGED PLAN (A1/V-401)

WAREHOUSE

MH-SANITARY SEWER
RIM=791.30'
FULL OF WATER - INVERT SIZE/TYPE COULD NOT BE DETERMINED

(14) BOLLARD (TYP (BY RECORD))

MH-SANITARY SEWER
RIM=790.50'
6"PVC PIPE-NORTHWEST FL=785.55'
6"PVC PIPE-SOUTHEAST FL=785.34'

UTILITY TRANSFORMER

GAZEBO

SEE ENLARGED PLAN (H9/V-402)

MH-SANITARY SEWER
RIM=789.34'
6"PVC PIPE-NORTHWEST FL=785.10'
8"PVC PIPE-SOUTHEAST FL=784.96'

SOUTH APRON

(3) BOLLARD

SHED

(3) BOLLARD

24" RCP FL=788.88'

24" RCP FL=788.98'

24" RCP FL=769.50'

24" RCP FL=769.49'

24" RCP FL=769.24'

24" RCP FL=769.35'

24" RCP FL=769.28'

24" RCP FL=783.65'

24" RCP FL=781.44'

24" RCP FL=781.38'

24" RCP FL=779.50'

24" RCP FL=779.02'

24" RCP FL=778.94'

24" RCP FL=777.54'

36" CMP FL=771.94'

36" CMP FL=772.12'

SOUTH POV AREA

SOUTH WAREHOUSE ACCESS DRIVE

SOUTH ACCESS DRIVE

PARK AVENUE

OWS

OIL/WATER SEPARATOR (BY RECORD)

N

40' 20' 0' 40'

SCALE: 1" = 40'


GENERAL NOTES

1. THE INFORMATION ON THIS DRAWING IS PRELIMINARY AND NOT TO BE USED FOR CONSTRUCTION. THE CONTRACTOR WILL BE RESPONSIBLE FOR ALL WORK ASSOCIATED WITH THE FINAL PROJECT SCOPE AND IT'S DESIGN AND CONSTRUCTION REQUIREMENTS. THIS DOCUMENT IS NOT INTENDED TO CONVEY AN DESIGN; RATHER, ONLY SCOPE AND PRELIMINARY COST ESTIMATING. THE CONTRACTOR IS RESPONSIBLE TO CONFIRM ALL FIELD CONDITIONS AND IS RESPONSIBLE FOR THE COMPLETE DESIGN AND CONSTRUCTION OF THE PROJECT.
2. EXISTING CONDITIONS INFORMATION SHOWN ON THESE DRAWINGS ARE BASED ON AVAILABLE A SURVEY PERFORMED BY WHITE HAWK ENGINEERS PROVIDED ON JANUARY 13, 2025, AND ON AERIAL IMAGERY AND DOCUMENTATION PROVIDED IN THE REQUEST FOR PROPOSAL ATTACHMENTS OR PUBLICALLY AVAILABLE INFORMATION

EXISTING LEGEND

- MAJOR CONTOURS
- MINOR CONTOURS
- FENCE
- AIR CONDITIONER
- LIGHT POLE
- SIGN
- FIRE HYDRANT
- WATER VALVE
- SECURITY CAMERA
- SECURITY KEYPAD
- BOLLARD
- PULLBOX
- POWER POLE
- VAULT
- UTILITY MARKER
- REFLECTOR
- FIBER OPTICS METER
- SANITARY SEWER MANHOLE
- TRANSFORMER
- CLEAN OUT
- GATE CONTROL BOX
- TELEPHONE PEDESTAL
- OVERHEAD UTILITY
- SANITARY SEWER
- GAS METER
- GAS VALVE
- GUY ANCHOR
- UNKNOWN MANHOLE
- 2' X 2' STORM SEWER INLET
- STORM MANHOLE
- ELECTRIC MANHOLE
- TELEPHONE MANHOLE
- BORE HOLE
- SURVEY CONTROL POINT
- STORM SEWER LINE
- GRAVEL
- RIP RAP
- NATURAL GROUND
- CONCRETE
- ASPHALT
- GAS LINE
- WATER LINE
- FIRE PROTECTION LINE

KEY PLAN

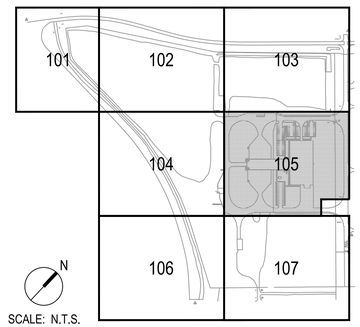

SCALE: N.T.S.

US Army Corps of Engineers ®

MARK	DESCRIPTION	DATE

US ARMY CORPS OF ENGINEERS
LOUISVILLE DISTRICT
600 DR. MARTIN LUTHER KING JR. PL.
LOUISVILLE, KY 40202

GMHILL Michael Baker INTERNATIONAL

DESIGNED BY: J. PRITCHARD
DRAWN BY: R.DOYLE
CHECKED BY: J. BECKMEYER-HEFFER
SUBMITTED BY: R. PARRISH
SIZE: ANSI D
ISSUE DATE: 25-02-10
SOLICITATION NO.:
CONTRACT NO.:
PLOT DATE: 2/6/2026 11:17 AM
FILENAME: 204020_V-10X.DWG

FORT CAVAZOS, TX
ECS / MAINTENANCE BUILDING / WAREHOUSE

EXISTING CONDITIONS PLAN


SHEET ID
V-105

PHASE 1 ADVERTISEMENT W912QR25RA013_Plans_Ph1-0000

MATCHLINE - SEE SHEET V-104

GENERAL NOTES

1. THE INFORMATION ON THIS DRAWING IS PRELIMINARY AND NOT TO BE USED FOR CONSTRUCTION. THE CONTRACTOR WILL BE RESPONSIBLE FOR ALL WORK ASSOCIATED WITH THE FINAL PROJECT SCOPE AND IT'S DESIGN AND CONSTRUCTION REQUIREMENTS. THIS DOCUMENT IS NOT INTENDED TO CONVEY AN DESIGN; RATHER, ONLY SCOPE AND PRELIMINARY COST ESTIMATING. THE CONTRACTOR IS RESPONSIBLE TO CONFIRM ALL FIELD CONDITIONS AND IS RESPONSIBLE FOR THE COMPLETE DESIGN AND CONSTRUCTION OF THE PROJECT.
2. EXISTING CONDITIONS INFORMATION SHOWN ON THESE DRAWINGS ARE BASED ON AVAIALBLE A SURVEY PERFORMED BY WHITE HAWK ENGINEERS PROVIDED ON JANUARY 13, 2025, AND ON AERIAL IMAGERY AND DOCUMENTATION PROVIDED IN THE REQUEST FOR PROPOSAL ATTACHMENTS OR PUBLICALLY AVAILABLE INFORMATION

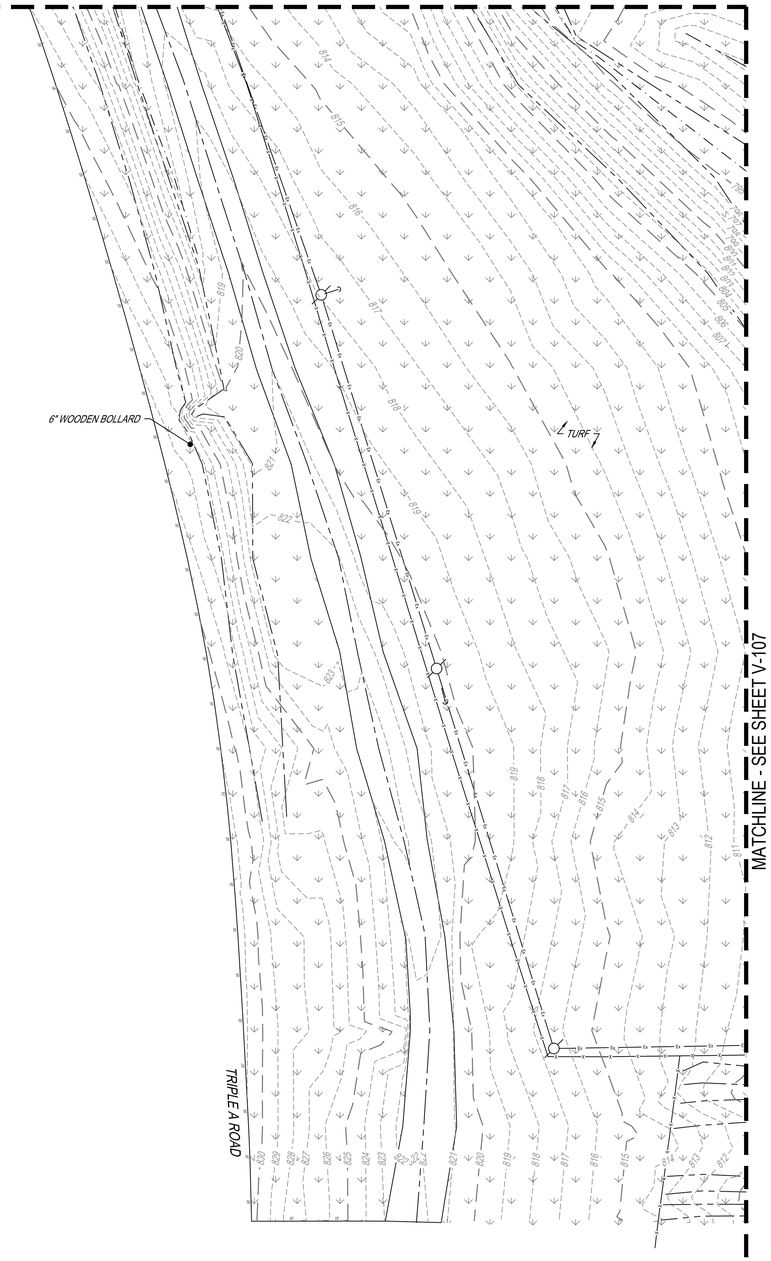


WHE CONTROL #103
5/8" IRON ROD SET WITH CAP - STAMPING:"10191200 WHITEHAWK"
TEXAS STATE PLANE COORDINATE SYSTEM
CENTRAL ZONE 4203
COORDINATES ARE SHOWN IN GRID
N: 10470920.18'
E: 3117052.01'
ELEV: 828.08'

EXISTING LEGEND

- MAJOR CONTOURS
- MINOR CONTOURS
- FENCE
- AIR CONDITIONER
- LIGHT POLE
- SIGN
- FIRE HYDRANT
- WATER VALVE
- SECURITY CAMERA
- SECURITY KEYPAD
- BOLLARD
- PULLBOX
- POWER POLE
- VAULT
- UTILITY MARKER
- REFLECTOR
- FIBER OPTICS METER
- SANITARY SEWER MANHOLE
- TRANSFORMER
- CLEAN OUT
- GATE CONTROL BOX
- TELEPHONE PEDESTAL
- OVERHEAD UTILITY
- SANITARY SEWER
- GAS METER
- GAS VALVE
- GUY ANCHOR
- UNKNOWN MANHOLE
- 2' X 2' STORM SEWER INLET
- STORM MANHOLE
- ELECTRIC MANHOLE
- TELEPHONE MANHOLE
- BORE HOLE
- SURVEY CONTROL POINT
- STORM SEWER LINE
- GRAVEL
- RIP RAP
- NATURAL GROUND
- CONCRETE
- ASPHALT
- GAS LINE
- WATER LINE
- FIRE PROTECTION LINE

KEY PLAN

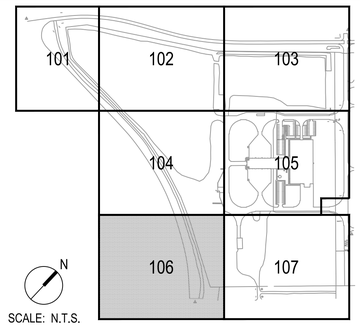

SCALE: N.T.S.

N

40' 20' 0' 40'

SCALE: 1" = 40'

US Army Corps of Engineers ®

MARK	DESCRIPTION	DATE

DESIGNED BY: J. PRITCHARD	ISSUE DATE: 25-02-10
DRAWN BY: R.DOYLE	SOLICITATION NO.:
CHECKED BY: J. BUTCHKOSKI-PERFER	CONTRACT NO.:
SUBMITTED BY: R. PARRISH	PLOT DATE: 2/6/2026 11:17 AM
SIZE: ANSI D	FILENAME: 204020_V-10X.DWG

US ARMY CORPS OF ENGINEERS
LOUISVILLE DISTRICT
600 DR. MARTIN LUTHER KING JR. PL.
LOUISVILLE, KY 40202

GM HILL Michael Baker INTERNATIONAL

FORT CAVAZOV, TX
ECS / MAINTENANCE BUILDING / WAREHOUSE

EXISTING CONDITIONS PLAN

SHEET ID

V-106

PHASE 1 ADVERTISEMENT W912QR25RA013_Plans_Ph1-0000

MATCHLINE - SEE SHEET V-105

MATCHLINE - SEE SHEET V-106

METAL BUILDING

TURF

GRAVEL

RIPRAP

SS MH 1A (BY RECORD)

(BY RECORD)

MH-SANITARY SEWER
RIM=786.41'
8"PVC PIPE-NORTHWEST FL=782.17'
3"PVC PIPE-SOUTHWEST FL=781.96'
6"PVC PIPE-NORTHEAST FL=781.80'

MH-SANITARY SEWER
RIM=779.06'
6"PVC PIPE-SOUTHWEST FL=774.27'
6"PVC PIPE-NORTHEAST FL=774.23'

36" CMP
FL=773.09'
36" CMP
FL=773.24'
6" PVC PIPE
FL=775.38'
(BY RECORD)

SPEED BUMP

GATE ENTRANCE

"SPEED LIMIT" SIGN

SIGN

PARK AVENUE

3'W X 1'H CONCRETE BOX CULVERT FL=793.02'

3'W X 1'H CONCRETE BOX CULVERT FL=793.21'

3'W X 1'H CONCRETE BOX CULVERT FL=792.09'

3'W X 1'H CONCRETE BOX CULVERT FL=792.59'

N

40' 20' 0' 40'

SCALE: 1" = 40'


EXISTING LEGEND

- MAJOR CONTOURS
- MINOR CONTOURS
- FENCE
- AIR CONDITIONER
- LIGHT POLE
- SIGN
- FIRE HYDRANT
- WATER VALVE
- SECURITY CAMERA
- SECURITY KEYPAD
- BOLLARD
- PULLBOX
- POWER POLE
- VAULT
- UTILITY MARKER
- REFLECTOR
- FIBER OPTICS METER
- SANITARY SEWER MANHOLE
- TRANSFORMER
- CLEAN OUT
- GATE CONTROL BOX
- TELEPHONE PEDESTAL
- OVERHEAD UTILITY
- SANITARY SEWER
- GAS METER
- GAS VALVE
- GUY ANCHOR
- UNKNOWN MANHOLE
- 2' X 2' STORM SEWER INLET
- STORM MANHOLE
- ELECTRIC MANHOLE
- TELEPHONE MANHOLE
- BORE HOLE
- SURVEY CONTROL POINT
- STORM SEWER LINE
- GRAVEL
- RIP RAP
- NATURAL GROUND
- CONCRETE
- ASPHALT
- GAS LINE
- WATER LINE
- FIRE PROTECTION LINE

GENERAL NOTES

1. THE INFORMATION ON THIS DRAWING IS PRELIMINARY AND NOT TO BE USED FOR CONSTRUCTION. THE CONTRACTOR WILL BE RESPONSIBLE FOR ALL WORK ASSOCIATED WITH THE FINAL PROJECT SCOPE AND IT'S DESIGN AND CONSTRUCTION REQUIREMENTS. THIS DOCUMENT IS NOT INTENDED TO CONVEY AN DESIGN; RATHER, ONLY SCOPE AND PRELIMINARY COST ESTIMATING. THE CONTRACTOR IS RESPONSIBLE TO CONFIRM ALL FIELD CONDITIONS AND IS RESPONSIBLE FOR THE COMPLETE DESIGN AND CONSTRUCTION OF THE PROJECT.
2. EXISTING CONDITIONS INFORMATION SHOWN ON THESE DRAWINGS ARE BASED ON AVAIALBLE A SURVEY PERFORMED BY WHITE HAWK ENGINEERS PROVIDED ON JANUARY 13, 2025, AND ON AERIAL IMAGERY AND DOCUMENTATION PROVIDED IN THE REQUEST FOR PROPOSAL ATTACHMENTS OR PUBLICALLY AVAILABLE INFORMATION

KEY PLAN

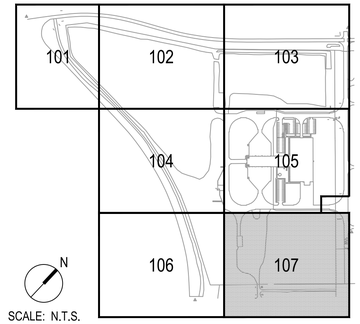

N

SCALE: N.T.S.

US Army Corps of Engineers ®

MARK	DESCRIPTION	DATE

ISSUE DATE: 25-02-10
SOLICITATION NO.:
CONTRACT NO.:
PLOT DATE: 2/6/2025 11:17 AM

DESIGNED BY: J. PRITCHARD
DRAWN BY: R.DOYLE
CHECKED BY: J. BUSSEMER
SUBMITTED BY: R. PARRISH
SIZE: ANSI D
FILENAME: 204020_V-10X.DWG

US ARMY CORPS OF ENGINEERS
LOUISVILLE DISTRICT
600 DR. MARTIN LUTHER KING JR PL.
LOUISVILLE, KY 40202


Michael Baker INTERNATIONAL
GMHILL

FORT CAVAZOV, TX
ECS / MAINTENANCE BUILDING / WAREHOUSE

EXISTING CONDITIONS PLAN

SHEET ID
V-107

PHASE 1 ADVERTISEMENT W912QR25RA013_Plans_Ph1-0000

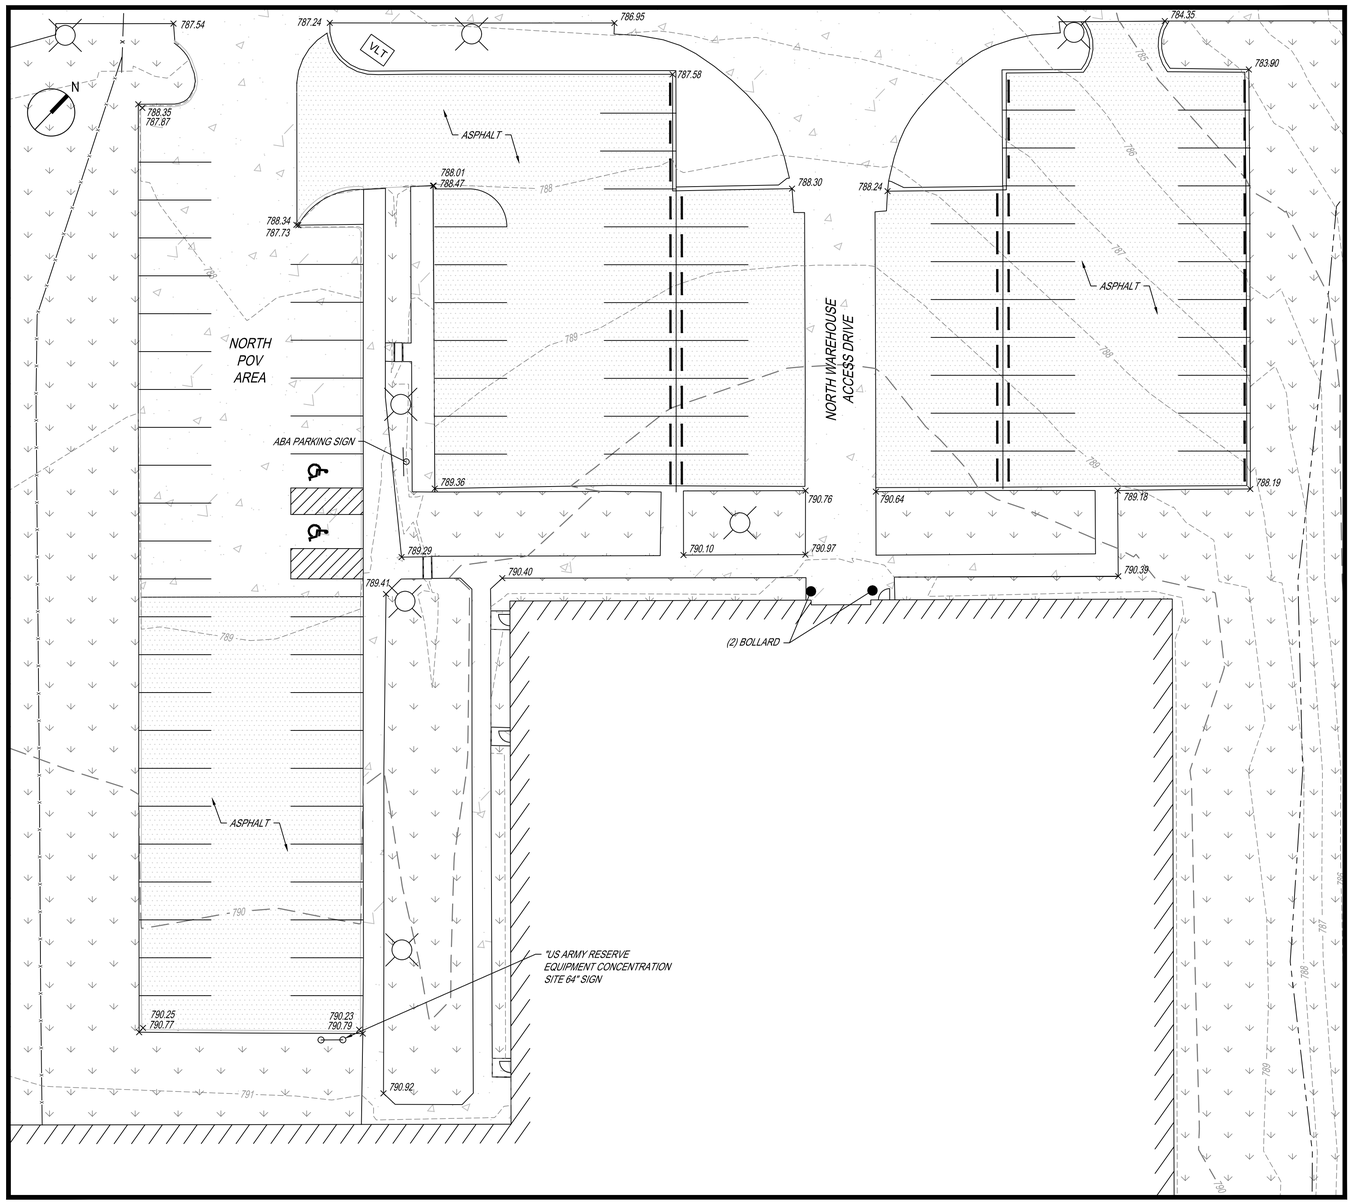

A1 ENLARGED PLAN
SCALE: 1" = 20'


EXISTING LEGEND

- MAJOR CONTOURS
- MINOR CONTOURS
- FENCE
- AIR CONDITIONER
- LIGHT POLE
- SIGN
- FIRE HYDRANT
- WATER VALVE
- SECURITY CAMERA
- SECURITY KEYPAD
- BOLLARD
- PULLBOX
- POWER POLE
- VAULT
- UTILITY MARKER
- REFLECTOR
- FIBER OPTICS METER
- SANITARY SEWER MANHOLE
- TRANSFORMER
- CLEAN OUT
- GATE CONTROL BOX
- TELEPHONE PEDESTAL
- OVERHEAD UTILITY
- SANITARY SEWER
- GAS METER
- GAS VALVE
- GUY ANCHOR
- UNKNOWN MANHOLE
- 2' X 2' STORM SEWER INLET
- STORM MANHOLE
- ELECTRIC MANHOLE
- TELEPHONE MANHOLE
- BORE HOLE
- SURVEY CONTROL POINT
- STORM SEWER LINE
- GRAVEL
- RIP RAP
- NATURAL GROUND
- CONCRETE
- ASPHALT
- GAS LINE
- WATER LINE
- FIRE PROTECTION LINE

GENERAL NOTES

1. THE INFORMATION ON THIS DRAWING IS PRELIMINARY AND NOT TO BE USED FOR CONSTRUCTION. THE CONTRACTOR WILL BE RESPONSIBLE FOR ALL WORK ASSOCIATED WITH THE FINAL PROJECT SCOPE AND IT'S DESIGN AND CONSTRUCTION REQUIREMENTS. THIS DOCUMENT IS NOT INTENDED TO CONVEY AN DESIGN; RATHER, ONLY SCOPE AND PRELIMINARY COST ESTIMATING. THE CONTRACTOR IS RESPONSIBLE TO CONFIRM ALL FIELD CONDITIONS AND IS RESPONSIBLE FOR THE COMPLETE DESIGN AND CONSTRUCTION OF THE PROJECT.
2. EXISTING CONDITIONS INFORMATION SHOWN ON THESE DRAWINGS ARE BASED ON AVAIALBLE A SURVEY PERFORMED BY WHITE HAWK ENGINEERS PROVIDED ON JANUARY 13, 2025, AND ON AERIAL IMAGERY AND DOCUMENTATION PROVIDED IN THE REQUEST FOR PROPOSAL ATTACHMENTS OR PUBLICALLY AVAILABLE INFORMATION

KEY PLAN

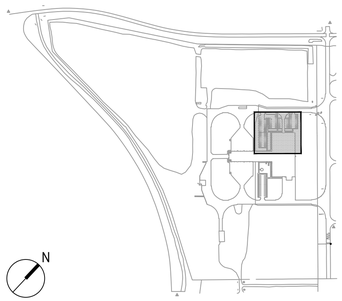

SCALE: N.T.S.

US Army Corps of Engineers ®

MARK	DESCRIPTION	DATE

ISSUE DATE:	25-02-10
SOLICITATION NO.:	
CONTRACT NO.:	
PLOT DATE:	2/6/2025 11:17 AM
DESIGNED BY:	J. PRITCHARD
DRAWN BY:	R.DOYLE
CHECKED BY:	J. PRITCHARD/R.PEFER
SUBMITTED BY:	R. PARRISH
SIZE:	ANSI D
FILENAME:	204020_V-10X.DWG

US ARMY CORPS OF ENGINEERS
LOUISVILLE DISTRICT
600 DR. MARTIN LUTHER KING, JR PL.
LOUISVILLE, KY 40202


GMHILL Michael Baker INTERNATIONAL

FORT CAVAZOV, TX
ECS / MAINTENANCE BUILDING / WAREHOUSE


EXISTING CONDITIONS PLAN ENLARGED AREAS

SHEET ID
V-401

PHASE 1 ADVERTISEMENT W912QR25RA013_Plans_Ph1-0000

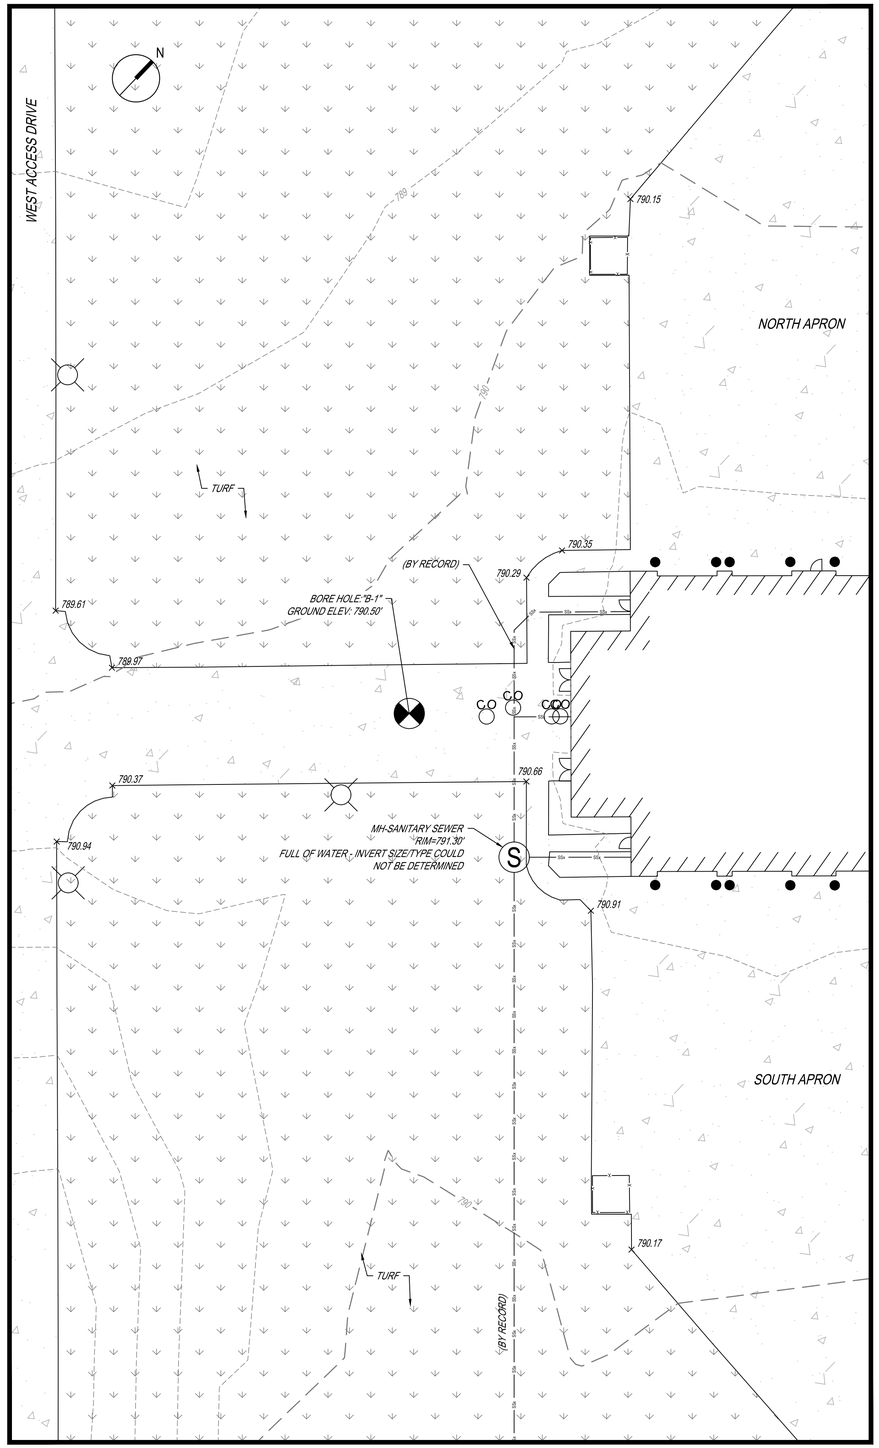

A1 ENLARGED PLAN
SCALE: 1" = 20'

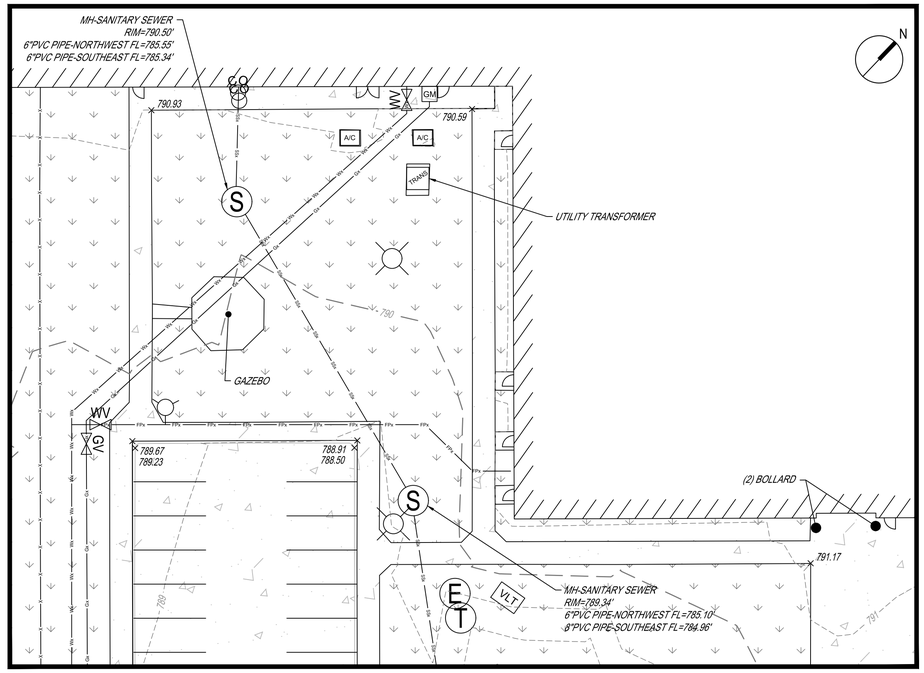

H9 ENLARGED PLAN
SCALE: 1" = 20'


GENERAL NOTES

1. THE INFORMATION ON THIS DRAWING IS PRELIMINARY AND NOT TO BE USED FOR CONSTRUCTION. THE CONTRACTOR WILL BE RESPONSIBLE FOR ALL WORK ASSOCIATED WITH THE FINAL PROJECT SCOPE AND IT'S DESIGN AND CONSTRUCTION REQUIREMENTS. THIS DOCUMENT IS NOT INTENDED TO CONVEY AN DESIGN; RATHER, ONLY SCOPE AND PRELIMINARY COST ESTIMATING. THE CONTRACTOR IS RESPONSIBLE TO CONFIRM ALL FIELD CONDITIONS AND IS RESPONSIBLE FOR THE COMPLETE DESIGN AND CONSTRUCTION OF THE PROJECT.
2. EXISTING CONDITIONS INFORMATION SHOWN ON THESE DRAWINGS ARE BASED ON AVAIALBLE A SURVEY PERFORMED BY WHITE HAWK ENGINEERS PROVIDED ON JANUARY 13, 2025, AND ON AERIAL IMAGERY AND DOCUMENTATION PROVIDED IN THE REQUEST FOR PROPOSAL ATTACHMENTS OR PUBLICALLY AVAILABLE INFORMATION

EXISTING LEGEND

- MAJOR CONTOURS
- MINOR CONTOURS
- FENCE
- AIR CONDITIONER
- LIGHT POLE
- SIGN
- FIRE HYDRANT
- WATER VALVE
- SECURITY CAMERA
- SECURITY KEYPAD
- BOLLARD
- PULLBOX
- POWER POLE
- VAULT
- UTILITY MARKER
- REFLECTOR
- FIBER OPTICS METER
- SANITARY SEWER MANHOLE
- TRANSFORMER
- CLEAN OUT
- GATE CONTROL BOX
- TELEPHONE PEDESTAL
- OVERHEAD UTILITY
- SANITARY SEWER
- GAS METER
- GAS VALVE
- GUY ANCHOR
- UNKNOWN MANHOLE
- 2' X 2' STORM SEWER INLET
- STORM MANHOLE
- ELECTRIC MANHOLE
- TELEPHONE MANHOLE
- BORE HOLE
- SURVEY CONTROL POINT
- STORM SEWER LINE
- GRAVEL
- RIP RAP
- NATURAL GROUND
- CONCRETE
- ASPHALT
- GAS LINE
- WATER LINE
- FIRE PROTECTION LINE

KEY PLAN

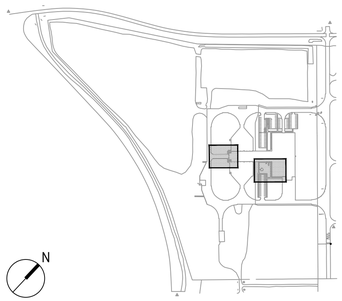

SCALE: N.T.S.

US Army Corps of Engineers ®

MARK	DESCRIPTION	DATE

ISSUE DATE:	25-02-10
SOLICITATION NO.:	
CONTRACT NO.:	
PLOT DATE:	2/6/2025 11:17 AM
FILENAME:	204020_V-10X.DWG
SIZE:	ANSI D
SUBMITTED BY:	R. PARRISH
CHECKED BY:	J. LUCKETT/J. REFER
DRAWN BY:	R.DOYLE
DESIGNED BY:	J. PRITCHARD

US ARMY CORPS OF ENGINEERS
LOUISVILLE DISTRICT
600 DR. MARTIN LUTHER KING, JR PL.
LOUISVILLE, KY 40202


GMHILL Michael Baker INTERNATIONAL

FORT CAVAZOV, TX
ECS / MAINTENANCE BUILDING / WAREHOUSE

EXISTING CONDITIONS PLAN ENLARGED AREAS

SHEET ID
V-402

PHASE 1 ADVERTISEMENT W912QR25RA013_Plans_Ph1-0000

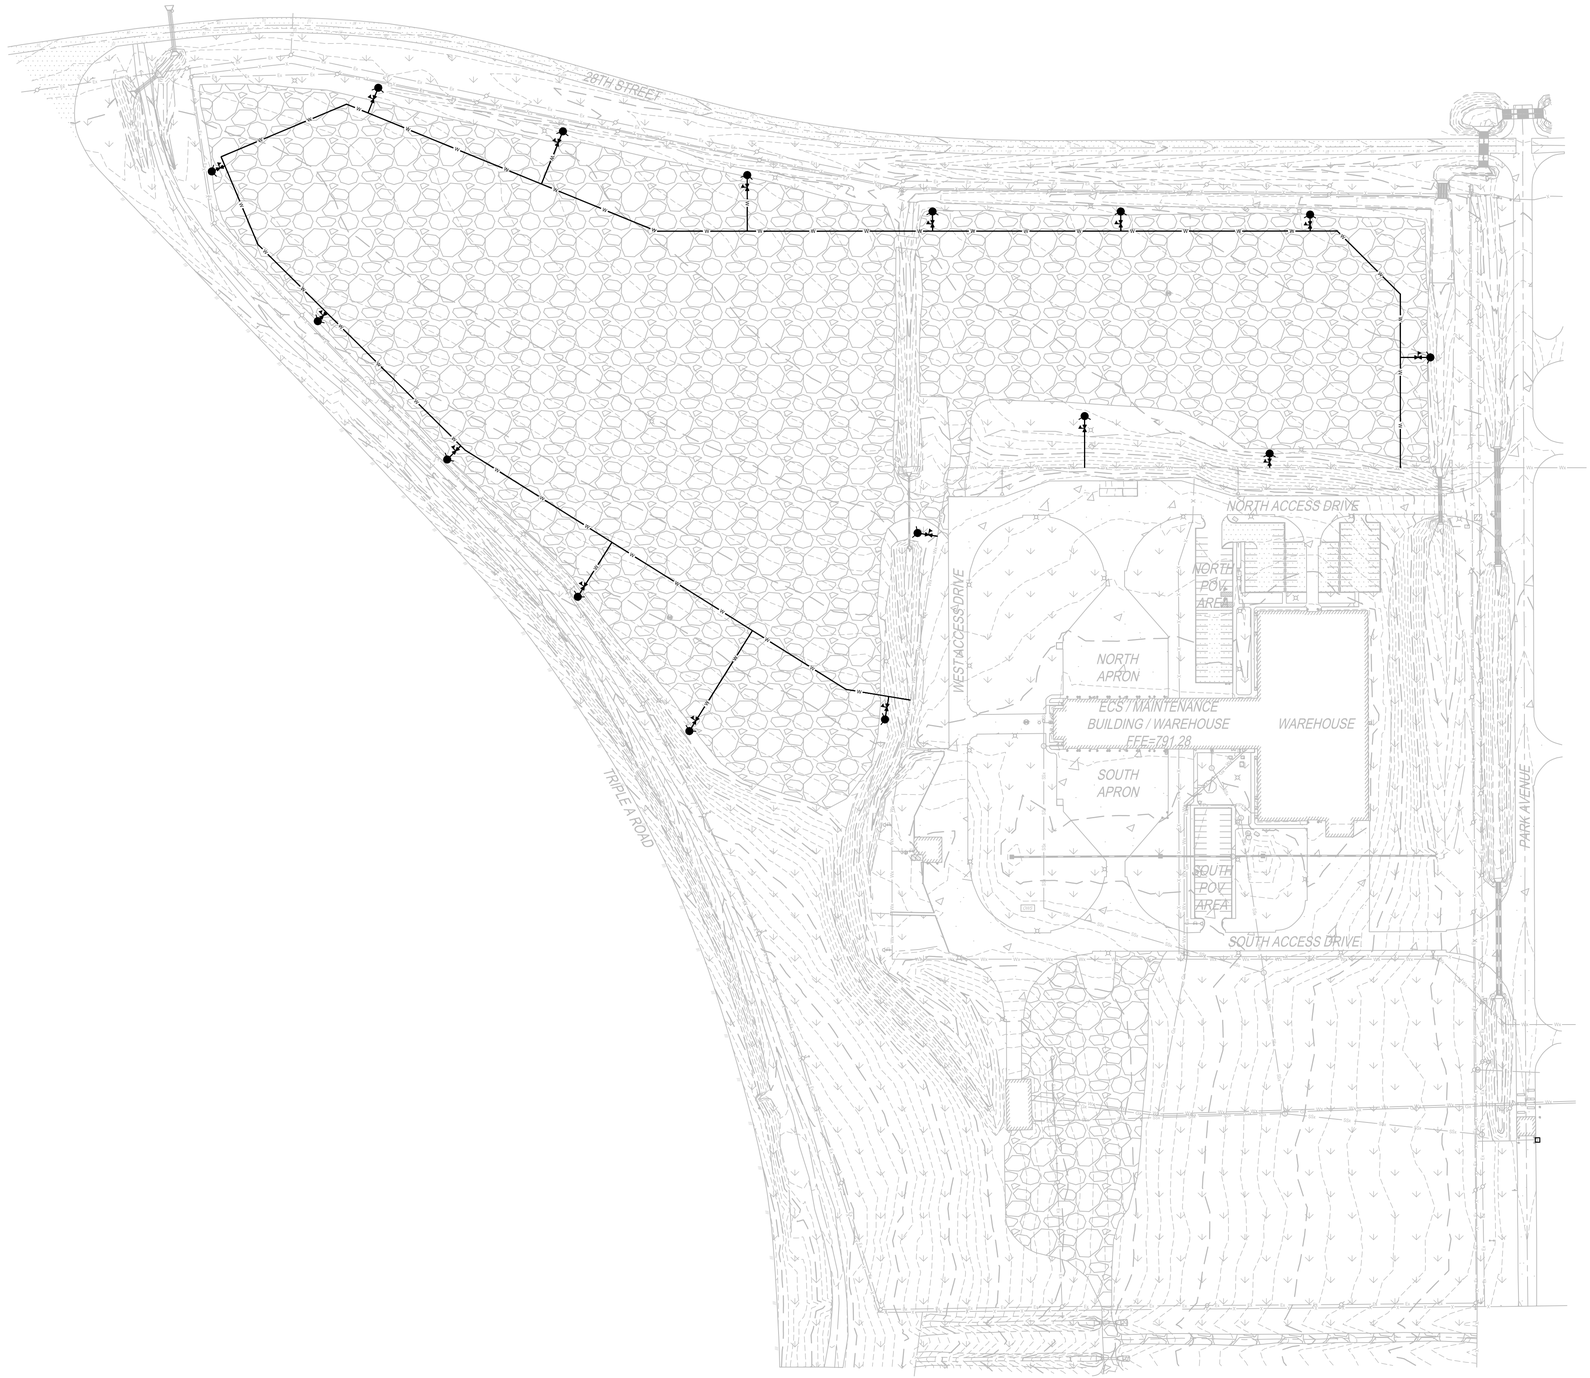

N

120' 60' 0' 120'

SCALE: 1" = 120'

WATERLINE BID OPTION LEGEND

- WATER LINE
- FIRE HYDRANT
- WATER VALVE

GENERAL NOTES

1. THE INFORMATION ON THIS DRAWING IS PRELIMINARY AND NOT TO BE USED FOR CONSTRUCTION. THE CONTRACTOR WILL BE RESPONSIBLE FOR ALL WORK ASSOCIATED WITH THE FINAL PROJECT SCOPE AND IT'S DESIGN AND CONSTRUCTION REQUIREMENTS. THIS DOCUMENT IS NOT INTENDED TO CONVEY AN DESIGN; RATHER, ONLY SCOPE AND PRELIMINARY COST ESTIMATING. THE CONTRACTOR IS RESPONSIBLE TO CONFIRM ALL FIELD CONDITIONS AND IS RESPONSIBLE FOR THE COMPLETE DESIGN AND CONSTRUCTION OF THE PROJECT.
2. EXISTING CONDITIONS INFORMATION SHOWN ON THESE DRAWINGS ARE BASED ON AVAIALBLE A SURVEY PERFORMED BY WHITE HAWK ENGINEERS PROVIDED ON JANUARY 13, 2025, AND ON AERIAL IMAGERY AND DOCUMENTATION PROVIDED IN THE REQUEST FOR PROPOSAL ATTACHMENTS OR PUBLICALLY AVAILABLE INFORMATION

US Army Corps of Engineers ®

MARK	DESCRIPTION	DATE

DESIGNED BY:	J. PRITCHARD
DRAWN BY:	R.DOYLE
CHECKED BY:	J. BLOCHBERGER
SUBMITTED BY:	R. PARRISH
SIZE:	ANSI D
ISSUE DATE:	25-02-10
SOLICITATION NO.:	
CONTRACT NO.:	
PLOT DATE:	2/6/2025 11:17 AM
FILENAME:	204020 C-10X.DWG

US ARMY CORPS OF ENGINEERS
LOUISVILLE DISTRICT
600 DR MARTIN LUTHER KING JR PL.
LOUISVILLE, KY 40202

GMHILL — Michael Baker INTERNATIONAL


FORT CAVAZOV, TX
ECS / MAINTENANCE BUILDING / WAREHOUSE

WATERLINE BID OPTION

SHEET ID

C-101

PHASE 1 ADVERTISEMENT W912QR25RA013_Plans_Ph1-0000

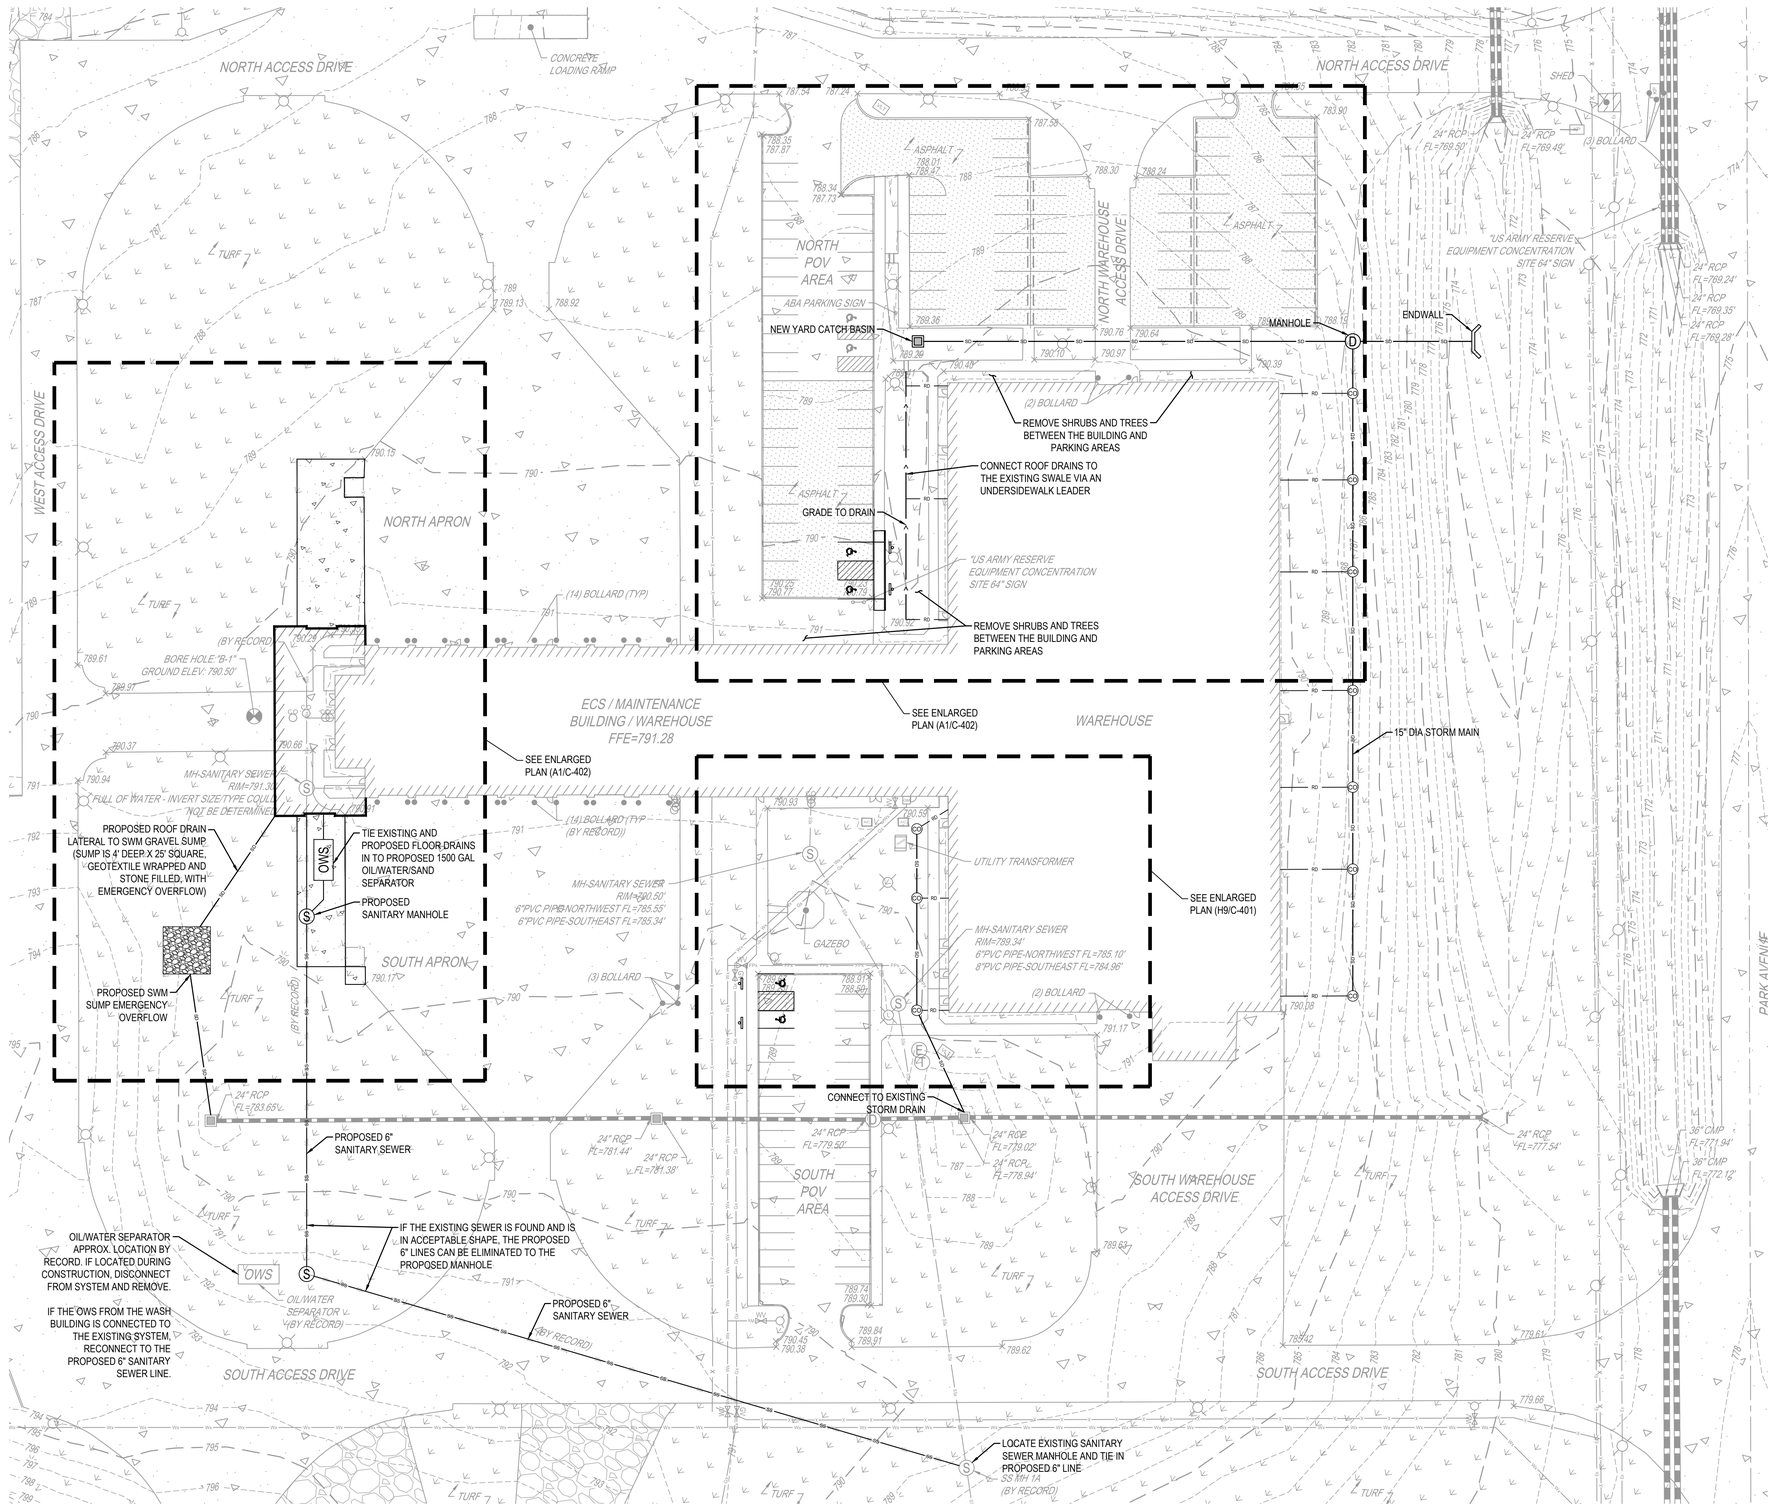


PROPOSED LEGEND

- BUILDING ADDITION FOOTPRINT
- SANITARY SEWER LINE
- SANITARY SEWER MANHOLE
- STORM SEWER LINE
- ROOF DRAIN
- DRAINAGE DITCH
- STORM SEWER MANHOLE
- CATCH BASIN
- CLEAN OUT
- OWS — 1500 GAL OIL/WATER/SAND SEPARATOR
- ENDWALL
- CONCRETE PAVEMENT
- ABA PARKING SIGN
- ABA PARKING STALL
- ABA CURB RAMP

GENERAL NOTES

1. THE INFORMATION ON THIS DRAWING IS PRELIMINARY AND NOT TO BE USED FOR CONSTRUCTION. THE CONTRACTOR WILL BE RESPONSIBLE FOR ALL WORK ASSOCIATED WITH THE FINAL PROJECT SCOPE AND IT'S DESIGN AND CONSTRUCTION REQUIREMENTS. THIS DOCUMENT IS NOT INTENDED TO CONVEY AN DESIGN; RATHER, ONLY SCOPE AND PRELIMINARY COST ESTIMATING. THE CONTRACTOR IS RESPONSIBLE TO CONFIRM ALL FIELD CONDITIONS AND IS RESPONSIBLE FOR THE COMPLETE DESIGN AND CONSTRUCTION OF THE PROJECT.
2. EXISTING CONDITIONS INFORMATION SHOWN ON THESE DRAWINGS ARE BASED ON AVAILABLE A SURVEY PERFORMED BY WHITE HAWK ENGINEERS PROVIDED ON JANUARY 13, 2025, AND ON AERIAL IMAGERY AND DOCUMENTATION PROVIDED IN THE REQUEST FOR PROPOSAL ATTACHMENTS OR PUBLICALLY AVAILABLE INFORMATION

KEY PLAN

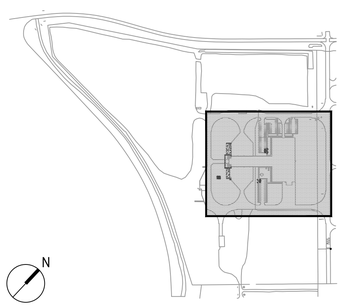

US Army Corps of Engineers ®

MARK	DESCRIPTION	DATE

ISSUE DATE:	25-02-10
SOLICITATION NO.:	
CONTRACT NO.:	
PLOT DATE:	2/6/2025 11:17 AM
FILENAME:	20420 C-10X.DWG
SIZE:	ANSI D
DESIGNED BY:	J. PRITCHARD
DRAWN BY:	R.DOYLE
CHECKED BY:	J. BLACKSHEFFER
SUBMITTED BY:	R. PARRISH

US ARMY CORPS OF ENGINEERS
LOUISVILLE DISTRICT
600 DR MARTIN LUTHER KING JR PL.
LOUISVILLE, KY 40202


Michael Baker INTERNATIONAL
GMHILL

FORT CAVAZOV, TX
ECS / MAINTENANCE BUILDING / WAREHOUSE

SITE PLAN

SHEET ID
C-105

PHASE 1 ADVERTISEMENT W912QR25RA013_Plans_Ph1-0000

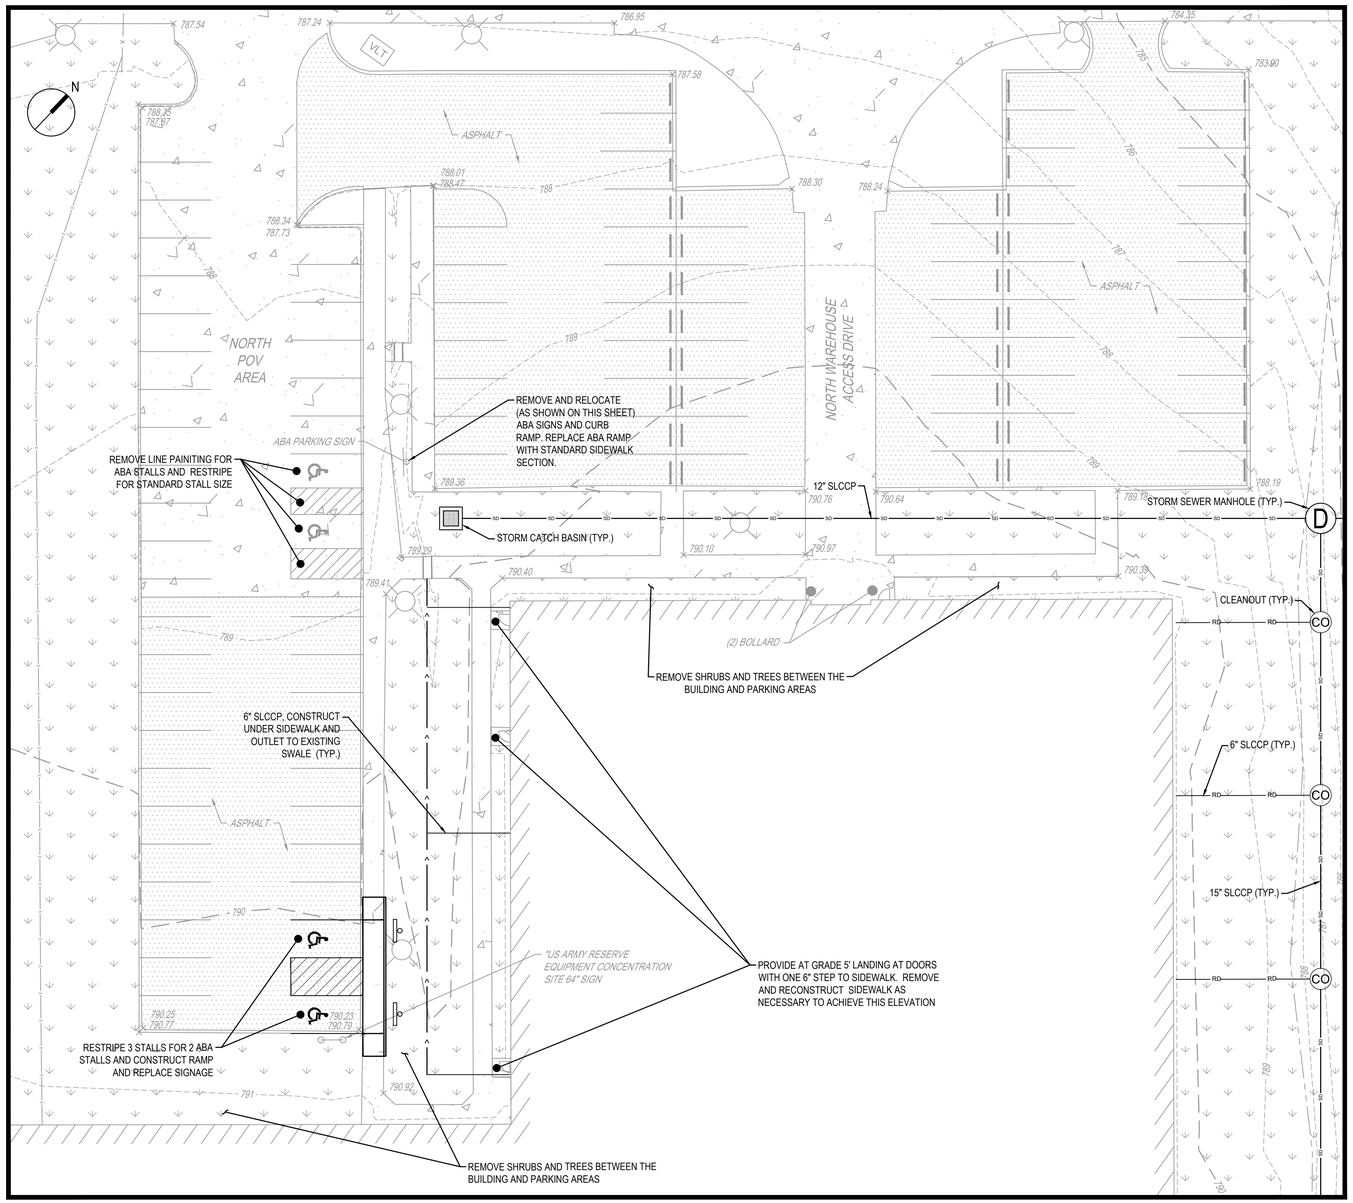

A1 ENLARGED PLAN
SCALE: 1" = 20'


PROPOSED LEGEND

- BUILDING ADDITION FOOTPRINT
- SANITARY SEWER LINE
- SANITARY SEWER MANHOLE
- STORM SEWER LINE
- ROOF DRAIN
- DRAINAGE DITCH
- STORM SEWER MANHOLE
- CATCH BASIN
- CLEAN OUT
- OWS — 1500 GAL OIL/WATER/SAND SEPARATOR
- ENDWALL
- CONCRETE PAVEMENT
- ABA PARKING SIGN
- ABA PARKING STALL
- ABA CURB RAMP

GENERAL NOTES

1. THE INFORMATION ON THIS DRAWING IS PRELIMINARY AND NOT TO BE USED FOR CONSTRUCTION. THE CONTRACTOR WILL BE RESPONSIBLE FOR ALL WORK ASSOCIATED WITH THE FINAL PROJECT SCOPE AND IT'S DESIGN AND CONSTRUCTION REQUIREMENTS. THIS DOCUMENT IS NOT INTENDED TO CONVEY AN DESIGN; RATHER, ONLY SCOPE AND PRELIMINARY COST ESTIMATING. THE CONTRACTOR IS RESPONSIBLE TO CONFIRM ALL FIELD CONDITIONS AND IS RESPONSIBLE FOR THE COMPLETE DESIGN AND CONSTRUCTION OF THE PROJECT.
2. EXISTING CONDITIONS INFORMATION SHOWN ON THESE DRAWINGS ARE BASED ON AVAIALBLE A SURVEY PERFORMED BY WHITE HAWK ENGINEERS PROVIDED ON JANUARY 13, 2025, AND ON AERIAL IMAGERY AND DOCUMENTATION PROVIDED IN THE REQUEST FOR PROPOSAL ATTACHMENTS OR PUBLICALLY AVAILABLE INFORMATION

KEY PLAN

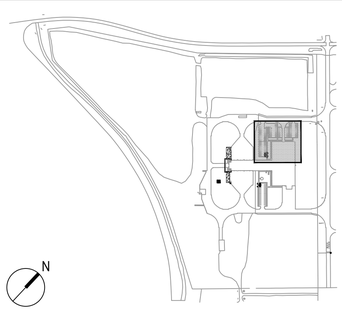

SCALE: N.T.S.

US Army Corps of Engineers ®

MARK	DESCRIPTION	DATE

DESIGNED BY: J. PRITCHARD
DRAWN BY: R.DOYLE
CHECKED BY: B. MCCLOSKEY
SUBMITTED BY: R. PARRISH
SIZE: ANSI D
ISSUE DATE: 25-02-10
SOLICITATION NO.:
CONTRACT NO.:
PLOT DATE: 2/6/2025 11:17 AM
FILENAME: 204020_C-10X.DWG

US ARMY CORPS OF ENGINEERS
LOUISVILLE DISTRICT
MUHAMMAD ALI-JOE FRAZIER JR PL.
600 DR. MARTIN LUTHER KING JR. PL.
LOUISVILLE, KY 40202


GMHILL Michael Baker INTERNATIONAL

FORT CAVAZOV, TX
ECS / MAINTENANCE BUILDING / WAREHOUSE


ENLARGED SITE PLAN

SHEET ID
C-401

PHASE 1 ADVERTISEMENT W912QR25RA013_Plans_Ph1-0000

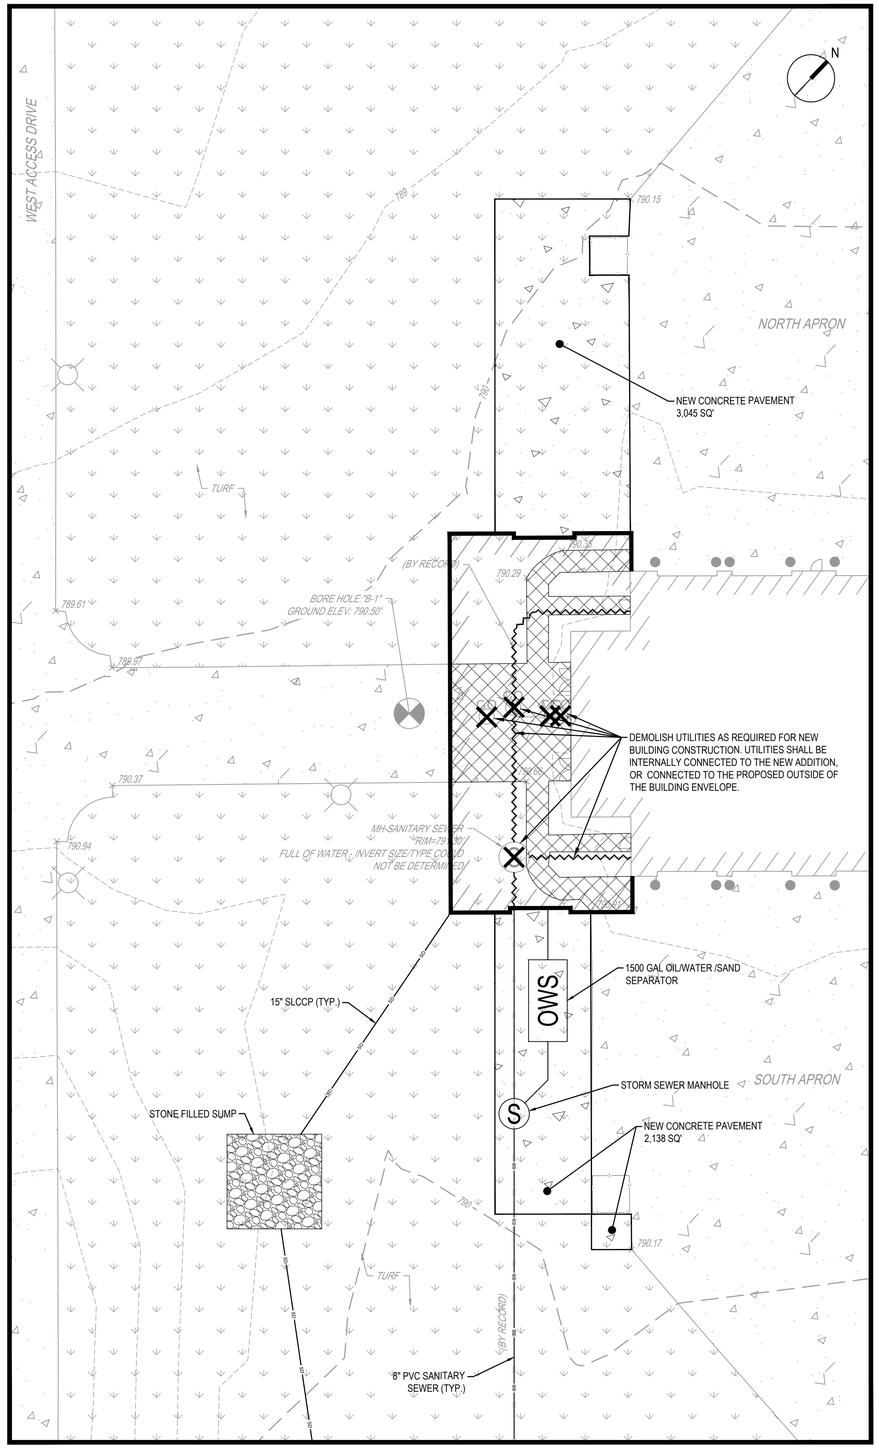

A1 ENLARGED PLAN
SCALE: 1" = 20'

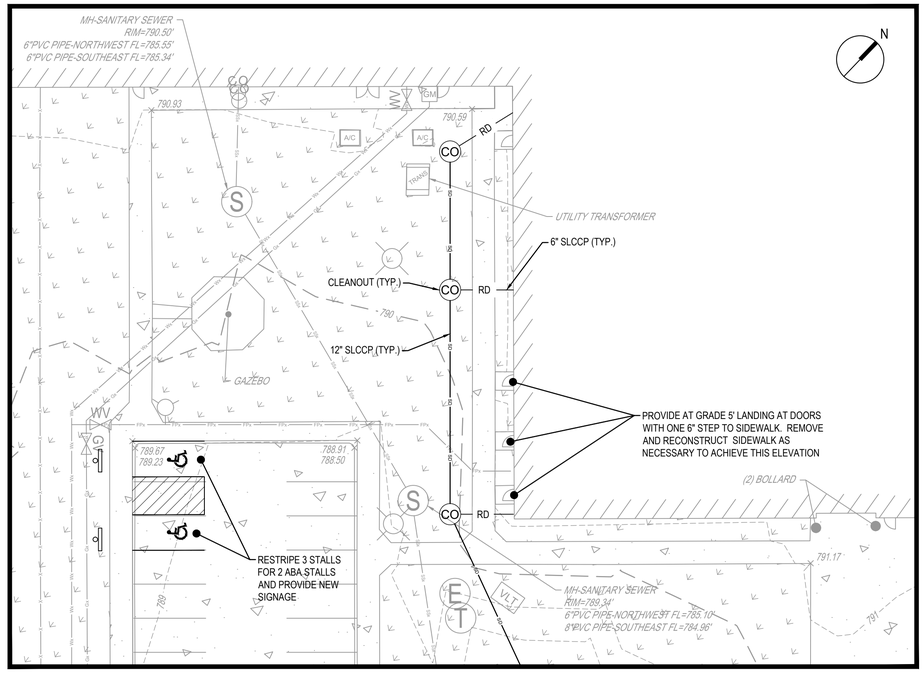

H9 ENLARGED PLAN
SCALE: 1" = 20'


PROPOSED LEGEND

- BUILDING ADDITION FOOTPRINT
- SANITARY SEWER LINE
- SANITARY SEWER MANHOLE
- STORM SEWER LINE
- ROOF DRAIN
- DRAINAGE DITCH
- STORM SEWER MANHOLE
- CATCH BASIN
- CLEAN OUT
- OWS — 1500 GAL OIL/WATER/SAND SEPARATOR
- ENDWALL
- CONCRETE PAVEMENT
- ABA PARKING SIGN
- ABA PARKING STALL
- ABA CURB RAMP
- CONCRETE TO BE DEMOLISHED
- UTILITY TO BE DEMOLISHED
- UTILITY / SITE FEATURE TO BE DEMOLISHED

GENERAL NOTES

1. THE INFORMATION ON THIS DRAWING IS PRELIMINARY AND NOT TO BE USED FOR CONSTRUCTION. THE CONTRACTOR WILL BE RESPONSIBLE FOR ALL WORK ASSOCIATED WITH THE FINAL PROJECT SCOPE AND IT'S DESIGN AND CONSTRUCTION REQUIREMENTS. THIS DOCUMENT IS NOT INTENDED TO CONVEY AN DESIGN; RATHER, ONLY SCOPE AND PRELIMINARY COST ESTIMATING. THE CONTRACTOR IS RESPONSIBLE TO CONFIRM ALL FIELD CONDITIONS AND IS RESPONSIBLE FOR THE COMPLETE DESIGN AND CONSTRUCTION OF THE PROJECT.
2. EXISTING CONDITIONS INFORMATION SHOWN ON THESE DRAWINGS ARE BASED ON AVAIALBLE A SURVEY PERFORMED BY WHITE HAWK ENGINEERS PROVIDED ON JANUARY 13, 2025, AND ON AERIAL IMAGERY AND DOCUMENTATION PROVIDED IN THE REQUEST FOR PROPOSAL ATTACHMENTS OR PUBLICALLY AVAILABLE INFORMATION

KEY PLAN

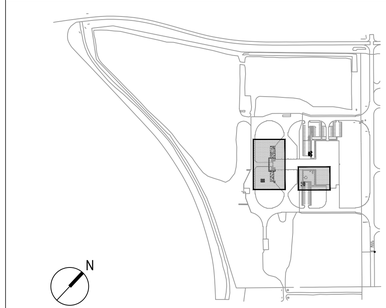

SCALE: N.T.S.

US Army Corps of Engineers ®

MARK	DESCRIPTION	DATE

ISSUE DATE:	25-02-10
SOLICITATION NO.:	
CONTRACT NO.:	
PLOT DATE:	2/6/2025 11:17 AM
FILENAME:	204020_C-10X.DWG
SIZE:	ANSI D
DESIGNED BY:	J. PRITCHARD
DRAWN BY:	R.DOYLE
CHECKED BY:	J. BUCKINGHAM-REFER
SUBMITTED BY:	R. PARRISH

US ARMY CORPS OF ENGINEERS
LOUISVILLE DISTRICT
600 DR. MARTIN LUTHER KING, JR PL.
LOUISVILLE, KY 40202

Michael Baker INTERNATIONAL
GMHILL

FORT CAVAZOV, TX
ECS / MAINTENANCE BUILDING / WAREHOUSE

ENLARGED SITE PLAN

SHEET ID
C-402

PHASE 1 ADVERTISEMENT W912QR25RA013_Plans_Ph1-0000

(Master) Abbreviations

Abbreviation	Description
_____ A _____	
&	AND
<	ANGLE
@	AT
A/	ABOVE
ACP	ACOUSTIC CEILING PANEL
ADJ	ADJACENT, ADJUSTABLE
AED	AUTOMATED EXTERNAL DEFIBRILLATOR
AFF	ABOVE FINISHED FLOOR
AP	ACCESS PANEL
APPROX	APPROXIMATE(LY)
ARCH	ARCHITECT OR ARCHITECTURAL
ASTM	AMERICAN SOCIETY FOR TESTING MATERIAL
ATTEN	ATTENUATE, ATTENUATION
AVG	AVERAGE
_____ B _____	
B/	BOTTOM OF
B/C	BOTTOM OF CURB
BC	BASE CABINET
BD	BOARD
BIT	BITUMINOUS
BLDG	BUILDING
BSMT	BASEMENT
_____ C _____	
[	CHANNEL
C/	CENTER OF
CAB	CABINET
CC	CENTER TO CENTER
CG	CORNER GUARD
CJ	CORNER JOINT
CL	CENTER LINE
CLG	CEILING
CLG HT	CEILING HEIGHT
CLO	CLOSET
CLR	CLEAR
CMU	CONCRETE MASONRY UNIT
CO	CLEAN OUT
COL	COLUMN
CONC	CONCRETE
CONT	CONTINUOUS
CORR	CORRIDOR
CP	COPIER
CT	CERAMIC TILE
CY	CUBIC YARD
_____ D _____	
DF	DRINKING FOUNTAIN
DIA	DIAMETER
DIM	DIMENSION
DN	DOWN
DW	DISHWASHER
DWG	DRAWING
_____ E _____	
E	EAST
EA	EACH
EB	EDGE BANDING
EIFS	EXTERIOR INSULATION FINISH SYSTEM
EJ	EXPANSION JOINT
ELEC	ELECTRICAL
ELEV	ELEVATOR
EMER	EMERGENCY
ENCL	ENCLOSE(URE)
EP	ELECTRICAL PANEL
EQ	EQUAL
EQUIP	EQUIPMENT
EWC	ELECTRIC WATER COOLER
EXIST	EXISTING
EXP BLT	EXPANSION BOLT
EXT	EXTERIOR
_____ F _____	
<	FABRIC
F/F	FACE TO FACE

(Master) Abbreviations

Abbreviation	Description
FAX	FACSIMILE
FE	FIRE EXTINGUISHER
FEC	FIRE EXTINGUISHER CABINET
FHC	FIRE HOSE CABINET
FL	FLOOR
FL CO	FLOOR CLEANOUT
FP	FIRE PROTECTION
FPRF	FIREPROOF(ING)
FR	FIRE RATED OR FRAME
FT	FOOT/FEET
_____ G _____	
GA	GAUGE
GL	GLASS OR GLAZING
GRD	GROUND
GWB	GYPSUM WALL BOARD
_____ H _____	
HB	HOSE BIBB
HC	HANDICAP(PED)
HDW	HARDWARE
HM	HOLLOW METAL
HOR	HORIZONTAL
HP	HIGH POINT
HTR	HEATER
_____ I _____	
ID	INSIDE DIAMETER
IN	INCH(ES)
INT	INTERIOR
_____ J _____	
JB	JAMB
JST	JOIST
JT	JOINT
_____ L _____	
LAM	LAMINATE
LAN	LOCAL AREA NETWORK CONNECTION
LAV	LAVATORY
LB	POUND
LF	LINEAL FOOT
LP	LOW POINT
LTL	LINTEL
_____ M _____	
m	METERS
MAS	MASONRY
MAX	MAXIMUM
MDF	MEDIUM DENSITY FIBERBOARD
MECH	MECHANICAL
MEZZ	MEZZANINE
MFR	MANUFACTURE
MH	MANHOLE
MICRO	MICROWAVE
MIN	MINIMUM
MISC	MISCELLANEOUS
mm	MILLIMETERS
MO	MASONRY OPENING
MTD	MOUNTED EL
MTL	METAL
_____ N _____	
N	NORTH
NFPA	NATIONAL FIRE PROTECTION ASSOCIATION
NIC	NOT IN CONTRACT
NOM	NOMINAL
NTS	NOT TO SCALE
_____ O _____	
OC	ON CENTER
OD	OUTSIDE DIAMETER
OFF	OFFICE
OPNG	OPENING
OPP	OPPOSITE
_____ P _____	
PART	PARTITION
PL	PLATE

(Master) Abbreviations

Abbreviation	Description
PLAM	PLASTIC LAMINATE
PLAS	PLASTER
PLYWD	PLYWOOD
PNL	PANEL
POS	POINT OF SALE
PR	PAIR
PRCST	PRECAST
PREFAB	PREFABRICATED
PROP	PROPERTY
PSI	POUNDS PER SQUARE INCH
PSIG	POUNDS PER SQUARE INCH GAUGE
PT	POINT
PTD	PAINTED
_____ Q _____	
QTY	QUANTITY
_____ R _____	
R	RISER OR RADIUS
RCP	REFLECTED CEILING PLAN
RD	ROOF DRAIN
REF	REFER / REFERENCE
REG	REGISTER
REINF	REINFORCING
REQ'D	REQUIRED
RFG	REFRIGERATOR
RG	RANGE
RM	ROOM
RO	ROUGH OPENING
RTS	RUBBER TRANSITION STRIP
RWC	RAIN WATER CONDUCTOR
_____ S _____	
S	SOUTH
SAN	SANITARY
SCHD	SCHEDULE
SEC	SECTION
SF	SQUARE FOOT
SIM	SIMILAR
SPKLR	SPRINKLER
SQ	SQUARE
SQ FT	SQUARE FOOT
SS	STAINLESS STEEL
STD	STANDARD
STL	STEEL
STN	STAINED
STOR	STORAGE
SUSP	SUSPEND, SUSPENDED, OR SUSPENSION
SYS	SYSTEM
_____ T _____	
"T"	TEE (BAR OR W)
T	TREAD
T/	TOP OF
T/C	TOP OF CURB
TB	TACKBOARD
TC	TERRA COTTA
TEL	TELEPHONE
TEMP	TEMPERED OR TEMPERATURE
TERM	TERMINATE / TERMINAL
THRESH	THRESHOLD
TLT	TOILET
TV	TELEVISION
TYP	TYPICAL
_____ U _____	
UH	UNIT HEATER
UL	UNDERWRITER'S LABORATORY
UMCT	UNGLAZED MOSAIC CERAMIC TILE
UNO	UNLESS NOTED OTHERWISE
_____ V _____	
VEST	VESTIBULE
VIF	VERIFY IN FIELD
_____ W _____	
W	WEST
W/	WITH
W/O	WITHOUT
WC	WATER CLOSET
WIN	WINDOW
WP	WATERPROOF(ING)
WSCT	WAINSCOT
WT	WEIGHT
WWF	WELDED WIRE REINFORCEMENT

SECTIONS/ SECTIONAL DETAILS

- CONCRETE BLOCK
- CAST-IN-PLACE-CONCRETE
- STRUCTURAL/MISCELLANEO US STEEL
- EARTH
- GRAVEL/ENGINEERED FILL
- STONE, OR NATURAL BUILDING STONE
- PLASTER OR GYPSUM BOARD, OR EXTERIOR SHEATHING
- BATT INSULATION
- ROOF, TAPERED, CAVITY OR RIGID INSULATION
- FINISHED WOOD TRIM
- PLYWOOD
- CAVITY DRAINAGE MATERIAL

SYMBOLS

- # VIEW TITLE / SCALE: — VIEW CALLOUT
- INTERIOR / EXTERIOR — ELEVATIONS
- BUILDING SECTION
- WALL SECTION
- INTERIOR SECTION
- DETAIL SECTION
- CALLOUT PLAN, SECTION OR DETAIL
- COLUMN GRID LABEL - NEW
- COLUMN GRID LABEL - EXISTING
- REVISION
- ROOM NAME / ### — ROOM TAG
- #X#.# — PARTITION TYPE
- DOOR TAG - SEE SCHEDULE
- ##.## — KEYNOTE
- WINDOW TYPE
- TOILET ROOM ACCESSORIES
- ELEVATION MARK
- DENOTES ABOVE, BELOW, OR BEHIND
- ACCESSIBLE TOILET STALL
- RECYCLING COLLECTION AREA
- PLAN NORTH / N — NORTH ARROW
- CENTER LINE
- FLOOR TRANSITION
- SLOPE — ROOF SLOPE ARROW
- LEVEL LINE
- SPOT ELEVATION

US Army Corps of Engineers ®

MARK	DESCRIPTION	DATE

File Path: C:\Users\Karen.Rutter\Documents\Ft Cavazos_Karen.rutter4.rvt:201.rvt

DESIGNED BY: KHR
DRAWN BY: KHR
CHECKED BY: TED
SUBMITTED BY:
SIZE: ANSI D
ISSUE DATE: 25-02-10
SOLICITATION NO.:
CONTRACT NO.:
PLOT DATE: 27/2/2025 12:12:53 PM
FILENAME: US-XXXXXXA-001

US ARMY CORPS OF ENGINEERS
LOUISVILLE DISTRICT
600 DR MARTIN LUTHER KING JR PL,
LOUISVILLE, KY 40202

GMHILL — Michael Baker INTERNATIONAL — JOINT VENTURE


MAINTENANCE AND REPAIR ARMY RESERVE (ECS)
NORTH CAVAZOS, TX
BUILDING B56767

ABBREVIATIONS

SHEET ID

A-001

PHASE 1 ADVERTISEMENT W912QR25RA013_Plans_Ph1-0000

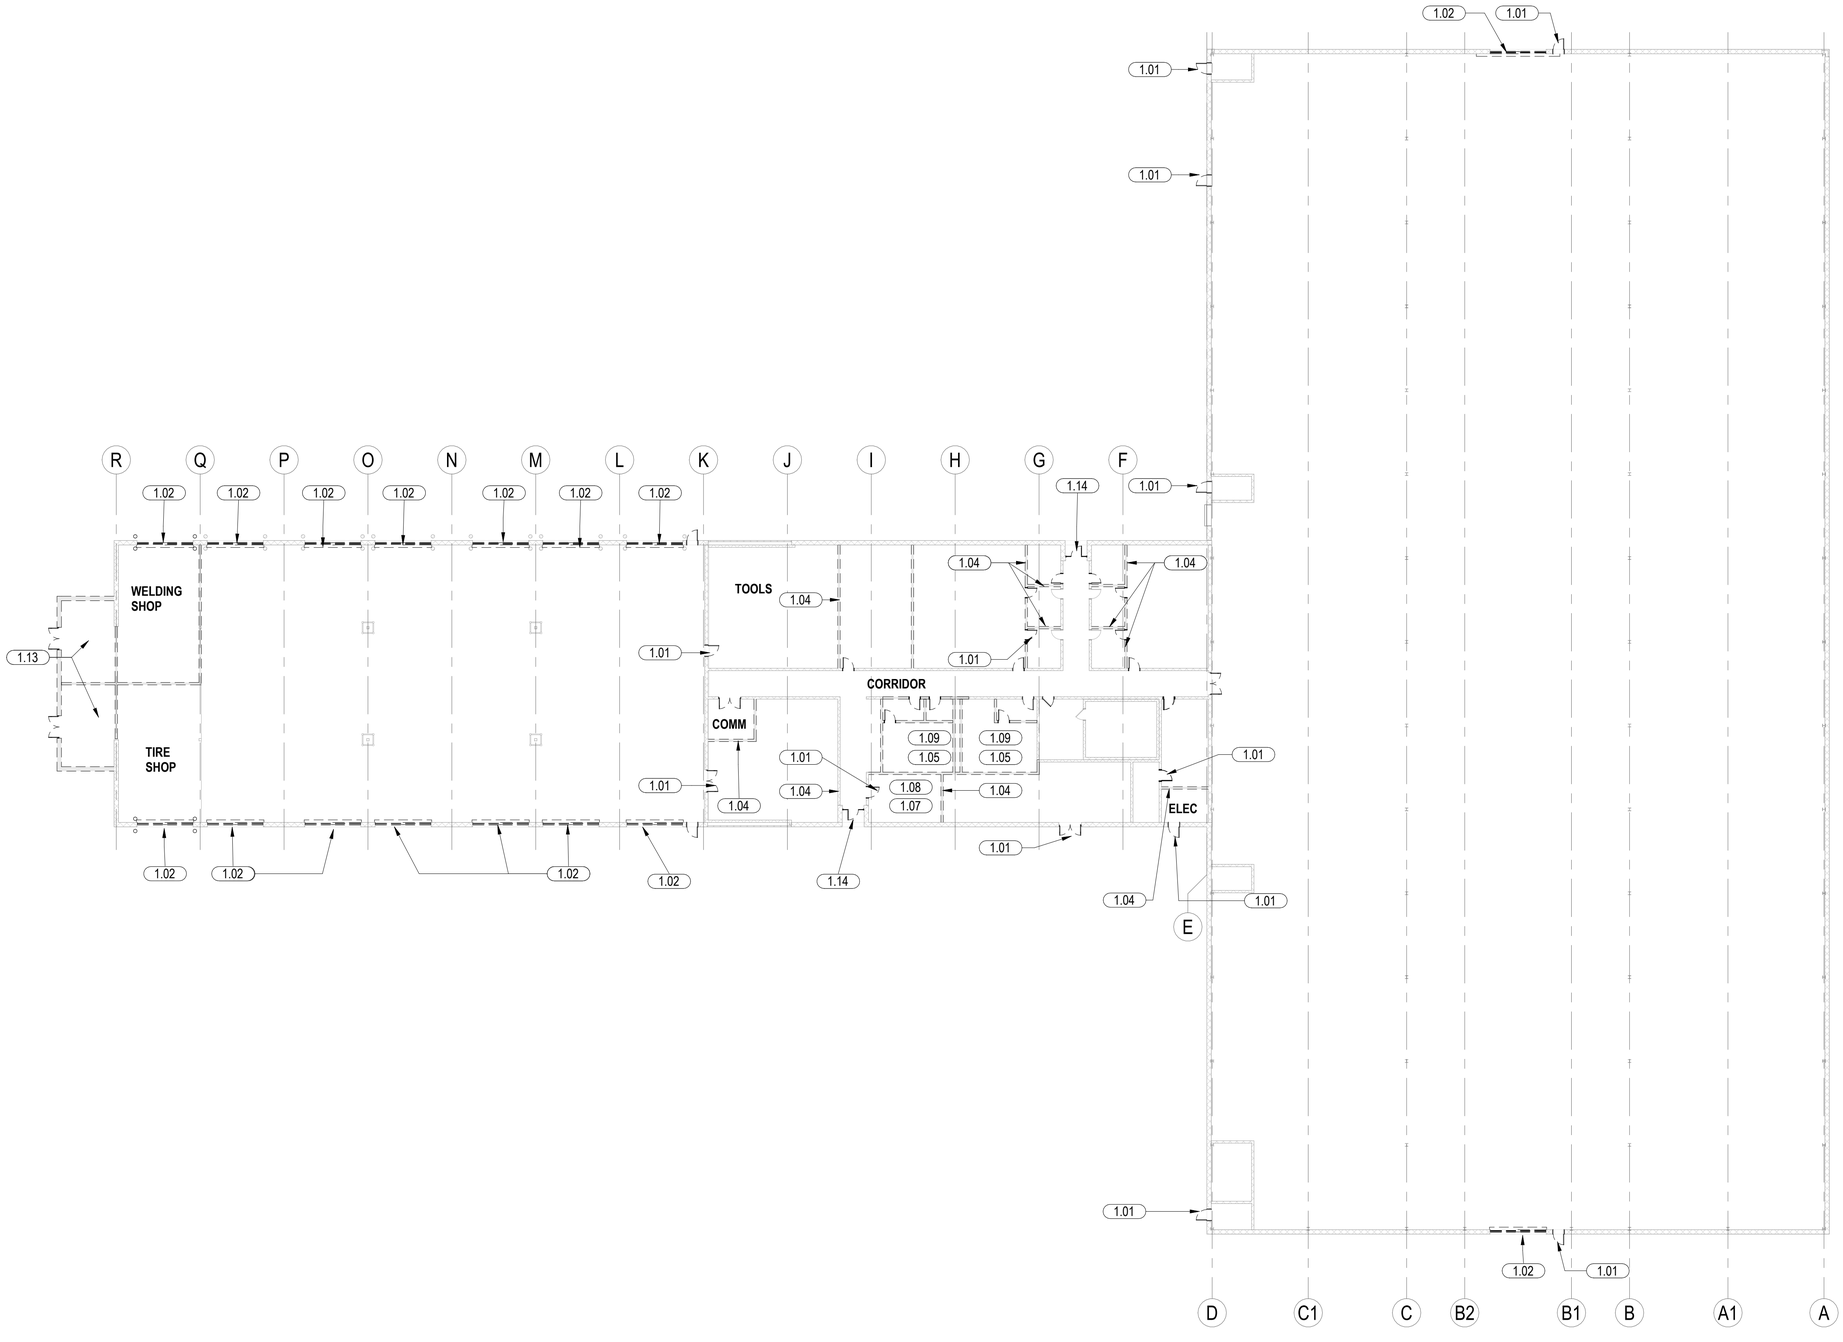

1 PRELIMINARY DEMOLITION PLAN
SCALE: 3/64" = 1'-0"

KEYNOTES

1.01	REMOVE EXISTING METAL DOOR AND FRAME
1.02	REMOVE EXISTING OVERHEAD DOOR
1.04	REMOVE WALL TO LIMITS SHOWN
1.05	DEMOLISH TOILET, SHOWER, AND VANITY AND REMOVE LOCKERS.
1.07	REMOVE CABINETRY AND SINK
1.08	REMOVE FLOORING, WALL BASE, AND ACOUSTIC CEILING TILE
1.09	REMOVE FLOORING AND WALL FINISH
1.13	DEMOLISH BATTERY STORAGE AND FLAMMABLE STORAGE IN ITS ENTIRETY
1.14	REMOVE STOREFRONT DOOR

NOTES - FLOOR PLANS

1 THE PRELIMINARY DEMOLITION PLAN , FLOOR PLANS AND ELEVATIONS ARE FOR PROGRAMMATIC DISCUSSIONS ONLY. THESE DRAWINGS REPRESENT A POSSIBLE SOLUTION BUT ARE NOT INTENDED FOR CONSTRUCTION, NOR DO THEY INCLUDE ENGINEERING DESIGNS.

DEMOLITION LEGEND

- EXISTING DOOR AND/OR FRAME TO REMAIN
- EXISTING DOOR AND/OR FRAME TO BE REMOVED
- EXISTING WALL TO REMAIN
- EXISTING WALL TO BE REMOVED

PLAN NORTH

0 16'-0" 32'-0" 64'-0"
SCALE: 3/64" = 1'-0"

US Army Corps of Engineers ®

MARK	DESCRIPTION	DATE

File Path: C:\Users\Karen.Rutter\Documents\Ft Cavazos_karen.rutter4VW2G.rvt

DESIGNED BY:	KHR
DRAWN BY:	KHR
CHECKED BY:	TED
SUBMITTED BY:	SHEET
SIZE:	ANSI D
ISSUE DATE:	25-02-10
SOLICITATION NO.:	
CONTRACT NO.:	
PLOT DATE:	2/6/2025 5:12:33 PM
FILENAME:	US-XXXXXXA-AD101

US ARMY CORPS OF ENGINEERS
LOUISVILLE DISTRICT
600 DR MARTIN LUTHER KING JR PL.
LOUISVILLE, KY 40202

GMHILL — Michael Baker INTERNATIONAL
JOINT VENTURE

MAINTENANCE AND REPAIR ARMY RESERVE (ECS)
NORTH CAVAZOS, TX
BUILDING B56767


DEMOLITION PLAN

SHEET ID
AD101

PHASE 1 ADVERTISEMENT W912QR25RA013_Plans_Ph1-0000

BUILDING AREA LEGEND

- ADMINISTRATION
- CIRCULATION
- PERSONNEL SUPPORT
- STORAGE EXISTING
- WEAPON
- WORK BAY EXISTING
- WORK BAY SUPPORT
- WORK BAY SUPPORT ADDITION
- BUILDING SUPPORT
- WORK BAYS ADDITION

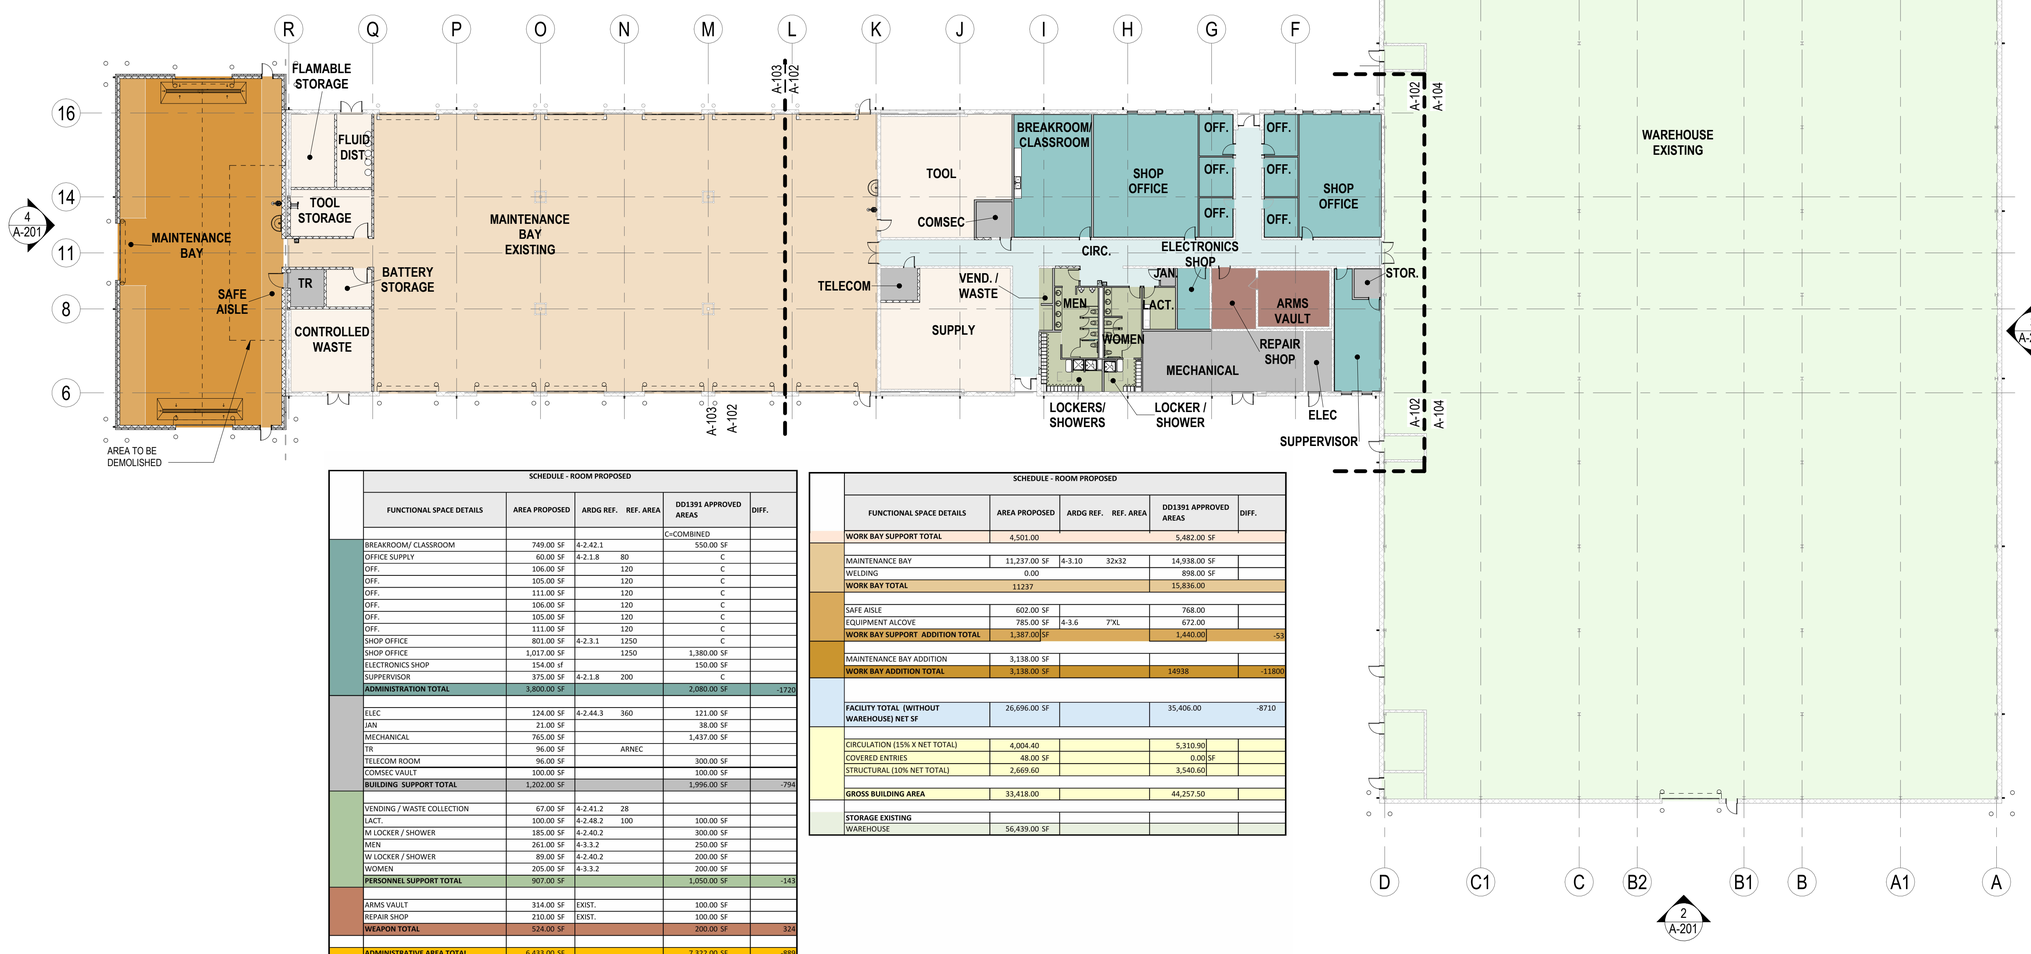

SCHEDULE - ROOM PROPOSED						
	FUNCTIONAL SPACE DETAILS	AREA PROPOSED	ARDG REF.	REF. AREA	DD1391 APPROVED AREAS	DIFF.
					C=COMBINED	
	BREAKROOM/ CLASSROOM	749.00 SF	4-2.42.1		550.00 SF	
	OFFICE SUPPLY	60.00 SF	4-2.1.8	80	C	
	OFF.	106.00 SF		120	C	
	OFF.	105.00 SF		120	C	
	OFF.	111.00 SF		120	C	
	OFF.	106.00 SF		120	C	
	OFF.	105.00 SF		120	C	
	OFF.	111.00 SF		120	C	
	SHOP OFFICE	801.00 SF	4-2.3.1	1250	C	
	SHOP OFFICE	1,017.00 SF		1250	1,380.00 SF	
	ELECTRONICS SHOP	154.00 sf			150.00 SF	
	SUPPERVISOR	375.00 SF	4-2.1.8	200	C	
	ADMINISTRATION TOTAL	3,800.00 SF			2,080.00 SF	-1720
	ELEC	124.00 SF	4-2.44.3	360	121.00 SF	
	JAN	21.00 SF			38.00 SF	
	MECHANICAL	765.00 SF			1,437.00 SF	
	TR	96.00 SF		ARNEC		
	TELECOM ROOM	96.00 SF			300.00 SF	
	COMSEC VAULT	100.00 SF			100.00 SF	
	BUILDING SUPPORT TOTAL	1,202.00 SF			1,996.00 SF	-794
	VENDING / WASTE COLLECTION	67.00 SF	4-2.41.2	28		
	LACT.	100.00 SF	4-2.48.2	100	100.00 SF	
	M LOCKER / SHOWER	185.00 SF	4-2.40.2		300.00 SF	
	MEN	261.00 SF	4-3.3.2		250.00 SF	
	W LOCKER / SHOWER	89.00 SF	4-2.40.2		200.00 SF	
	WOMEN	205.00 SF	4-3.3.2		200.00 SF	
	PERSONNEL SUPPORT TOTAL	907.00 SF			1,050.00 SF	-143
	ARMS VAULT	314.00 SF	EXIST.		100.00 SF	
	REPAIR SHOP	210.00 SF	EXIST.		100.00 SF	
	WEAPON TOTAL	524.00 SF			200.00 SF	324
	ADMINISTRATIVE AREA TOTAL	6,433.00 SF			7,322.00 SF	-889
	BATTERY STORAGE	133.00	4-3.7		70.00 SF	
	CONTROLLED WASTE STORAGE	532.00 SF	4-3.9		636.00 SF	
	EQUIPMENT ALCOVE	785.00 SF	4-3.6	7'XL	672.00 SF	
	FLAMMABLE STORAGE	254.00 SF	4-3.8		420.00 SF	
	FLUID DISTRIBITION	201.00 SF			228.00 SF	
	SUPPLY (PARTS)	1,145.00 SF	4-3.5	96/WA	1,728.00 SF	
	TOOLS	1,150.00 SF	4-3.4	96/WA		
	TOOLS STORAGE	301.00 SF	4-3.4		1,728.00 SF	

SCHEDULE - ROOM PROPOSED						
	FUNCTIONAL SPACE DETAILS	AREA PROPOSED	ARDG REF.	REF. AREA	DD1391 APPROVED AREAS	DIFF.
	WORK BAY SUPPORT TOTAL	4,501.00			5,482.00 SF	
	MAINTENANCE BAY	11,237.00 SF	4-3.10	32x32	14,938.00 SF	
	WELDING	0.00			898.00 SF	
	WORK BAY TOTAL	11237			15,836.00	
	SAFE AISLE	602.00 SF			768.00	
	EQUIPMENT ALCOVE	785.00 SF	4-3.6	7'XL	672.00	
	WORK BAY SUPPORT ADDITION TOTAL	1,387.00 SF			1,440.00	-53
	MAINTENANCE BAY ADDITION	3,138.00 SF				
	WORK BAY ADDITION TOTAL	3,138.00 SF			14938	-11800
	FACILITY TOTAL (WITHOUT WAREHOUSE) NET SF	26,696.00 SF			35,406.00	-8710
	CIRCULATION (15% X NET TOTAL)	4,004.40			5,310.90	
	COVERED ENTRIES	48.00 SF			0.00 SF	
	STRUCTURAL (10% NET TOTAL)	2,669.60			3,540.60	
	GROSS BUILDING AREA	33,418.00			44,257.50	
	STORAGE EXISTING					
	WAREHOUSE	56,439.00 SF				

PLAN NORTH

0 16'-0" 32'-0" 64'-0"

SCALE: 3/64" = 1'-0"

1 PROPOSED OVERALL PLAN

SCALE: 3/64" = 1'-0"

NOTE:

THE PRELIMINARY DEMOLITION PLAN, PRELIMINARY FLOOR PLANS, AND PRELIMINARY ELEVATIONS ARE FOR PROGRAMMATIC DISCUSSIONS ONLY. THESE DRAWINGS REPRESENT A POSSIBLE SOLUTION BUT ARE NOT INTENDED FOR CONSTRUCTION, NOR DO THEY INCLUDE ENGINEERING DESIGNS.

US Army Corps of Engineers ®

MARK	DESCRIPTION	DATE

File Path: C:\Users\Karen.Rutter\Documents\Ft Cavazos_Karen.rutter4-WX2G.rvt

DESIGNED BY: KHR	ISSUE DATE: 25-02-10
DRAWN BY: KHR	SOLICITATION NO.:
CHECKED BY: TED	CONTRACT NO.:
SUBMITTED BY: TED	PLOT DATE: 2/6/2025 5:12:22 PM
SIZE: ANSI D	FILENAME: US-XXXXXXA-A-101

US ARMY CORPS OF ENGINEERS
LOUISVILLE DISTRICT
600 DR MARTIN LUTHER KING JR PL.
LOUISVILLE, KY 40202

Michael Baker INTERNATIONAL
JOINT VENTURE
GMHILL


MAINTENANCE AND REPAIR ARMY RESERVE (ECS)
NORTH CAVAZOS, TX
BUILDING B5B767

OVERALL FLOOR PLAN

SHEET ID

A-101

PHASE 1 ADVERTISEMENT W912QR25RA013_Plans_Ph1-0000

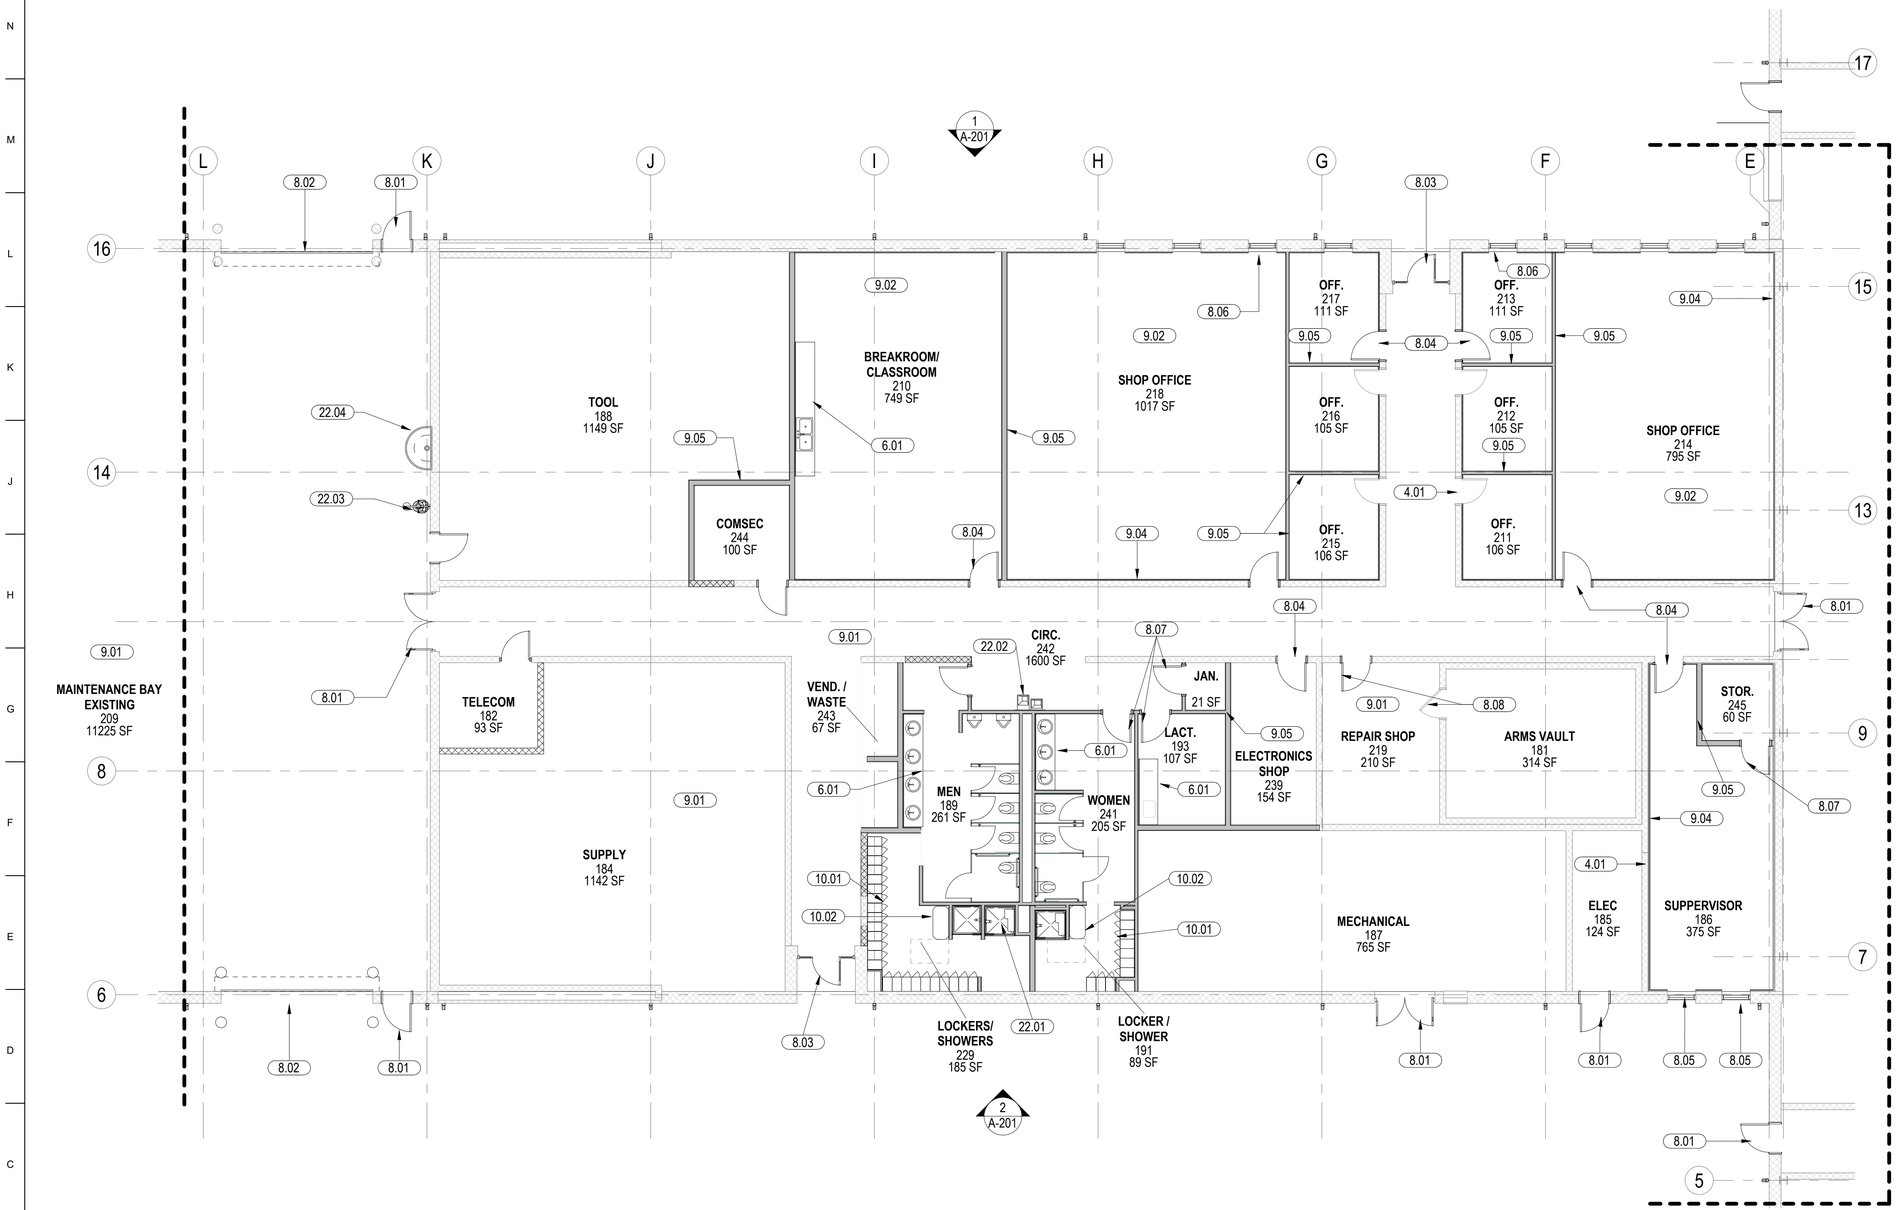

1 1ST FLOOR PLAN - AREA A
SCALE: 1/8" = 1'-0"

KEYNOTES


4.01	INFILL CMU WALL MATCH WITH EXISTING
6.01	ACCESSIBLE CABINETRY AND SINK
8.01	INSULATED HOLLOW METAL DOOR AND FRAME
8.02	INSULATED OVERHEAD COILING DOOR
8.03	ALUMINUM STOREFRONT ENTRY DOOR
8.04	WOOD DOOR AND HOLLOW METAL FRAME
8.05	ALUMINUM WINDOW MATCH WITH EXISTING
8.06	WINDOW TREATMENT
8.07	HOLLOW METAL DOOR AND FRAME
8.08	EXISTING DOOR TO REMAIN
9.01	CLEAN, PATCH AND REPAIR WALLS - PAINT
9.02	INSTALL FLOORING, WALL BASE, AND ACOUSTIC CEILING TILE
9.04	GYPSUM BOARD FURRING
9.05	METAL STUD ACOUSTIC DRYWALL SYSTEM
10.01	LOCKER
10.02	ACCESSIBLE BENCH AND CLEARANCE
22.01	SHOWER
22.02	DRINKING FOUNTAIN
22.03	SAFETY SHOWER AND EYEWASH
22.04	HANDWASH FOUNTAIN

NOTES - FLOOR PLANS

1 THE PRELIMINARY DEMOLITION PLAN , FLOOR PLANS AND ELEVATIONS ARE FOR PROGRAMMATIC DISCUSSIONS ONLY. THESE DRAWINGS REPRESENT A POSSIBLE SOLUTION BUT ARE NOT INTENDED FOR CONSTRUCTION, NOR DO THEY INCLUDE ENGINEERING DESIGNS.

WALL LEGEND

- NEW METAL STUD WALL WITH GYPUSM WALLBOARD EACH SIDE
- NEW INTERIOR NON-LOAD BEARING 8" CMU PARTITION
- NEW INTERIOR LOAD BEARING 8" CMU WALL
- NEW EXTERIOR WALL (4" VENEER AIRSPACE WITH INSULATION ON STRUCTURAL 8" MASONRY WALL TO 8' WITH INSULATED METAL WALL PANELS FROM 8' TO EAVE) TO MATCH EXISTING
- EXISTING INTERIOR MASONRY WALL 8" TO REMAIN
- EXISTING EXTERIOR WALL (4" VENEER AIRSPACE WITH INSULATION ON STRUCTURAL 8" MASONRY WALL TO 8' WITH INSULATED METAL WALL PANELS FROM 8' TO EAVE) TO REMAIN
- EXISTING FORMED IN PLACE REINFORCED CONCRETE INTERIOR VAULT WALL TO REMAIN

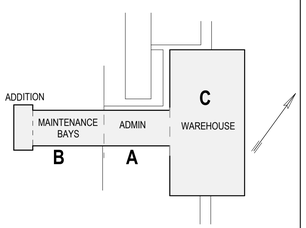

PLAN NORTH

0 4' - 0" 8' - 0" 16' - 0"
SCALE: 1/8" = 1' - 0"

US Army Corps of Engineers ®

MARK	DESCRIPTION	DATE

File Path: C:\Users\Karen.Rutter\Documents\Ft Cavazos_karen.rutter4.rvt

ISSUE DATE: 25-02-10
SOLICITATION NO.:
CONTRACT NO.:
PLOT DATE: 2/6/2025 5:12:23 PM

DESIGNED BY: KHR
DRAWN BY: KHR
CHECKED BY: TED
SUBMITTED BY: SUBMITTER
SIZE: ANSI D
FILENAME: US-XXXXXXA-A-102

US ARMY CORPS OF ENGINEERS
LOUISVILLE DISTRICT
600 DR MARTIN LUTHER KING JR PL.
LOUISVILLE, KY 40202


Michael Baker INTERNATIONAL
GMHILL
JOINT VENTURE

MAINTENANCE AND REPAIR ARMY RESERVE (ECS)
NORTH CAVAZOS, TX
BUILDING B56767

FLOOR PLAN - AREA A

SHEET ID
A-102

PHASE 1 ADVERTISEMENT W912QR25RA013_Plans_Ph1-0000

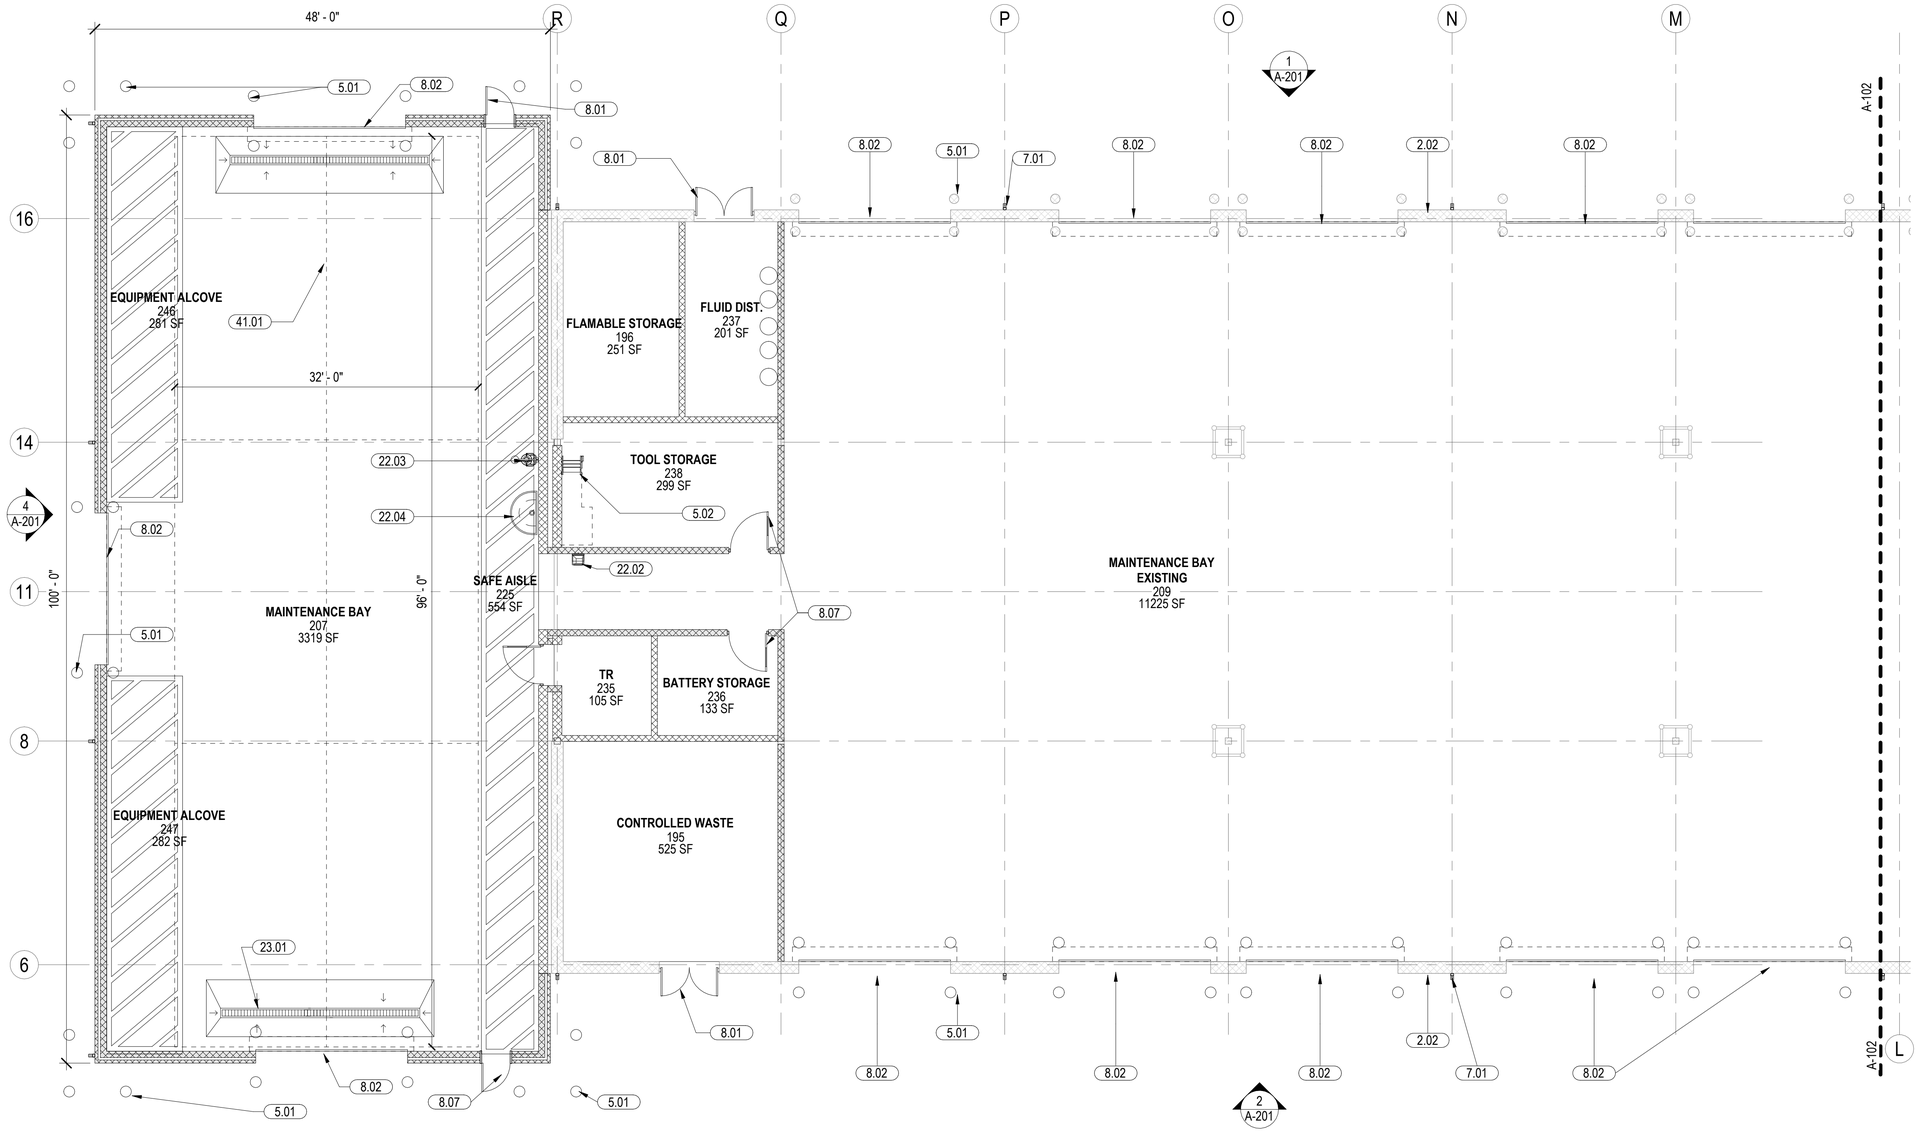


1 1ST FLOOR PLAN - AREA B
SCALE: 1/8" = 1'-0"

KEYNOTES

2.02	SURVEY, DOCUMENT, AND REPAIR VEHICLE IMPACT DAMAGE TO EXTERIOR WALL(MASONRY) WITH MATCHING MATERIALS
5.01	BOLLARDS
5.02	SHIP LADDER - ROOF PERMANENT ACCESS
7.01	REPLACE EXISTING GUTTERS AND DOWNSPOUTS
8.01	INSULATED HOLLOW METAL DOOR AND FRAME
8.02	INSULATED OVERHEAD COILING DOOR
8.07	HOLLOW METAL DOOR AND FRAME
22.02	DRINKING FOUNTAIN
22.03	SAFETY SHOWER AND EYEWASH
22.04	HANDWASH FOUNTAIN
23.01	TRENCH DRAIN
41.01	BRIDGE CRANE ABOVE

NOTES - FLOOR PLANS

1 THE PRELIMINARY DEMOLITION PLAN , FLOOR PLANS AND ELEVATIONS ARE FOR PROGRAMMATIC DISCUSSIONS ONLY. THESE DRAWINGS REPRESENT A POSSIBLE SOLUTION BUT ARE NOT INTENDED FOR CONSTRUCTION, NOR DO THEY INCLUDE ENGINEERING DESIGNS.

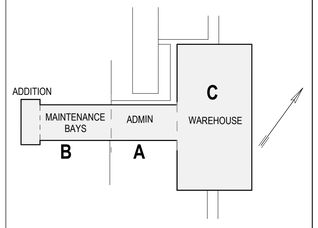

WALL LEGEND

- NEW METAL STUD WALL WITH GYPUSM WALLBOARD EACH SIDE
- NEW INTERIOR NON-LOAD BEARING 8" CMU PARTITION
- NEW INTERIOR LOAD BEARING 8" CMU WALL
- NEW EXTERIOR WALL (4" VENEER AIRSPACE WITH INSULATION ON STRUCTURAL 8" MASONRY WALL TO 8' WITH INSULATED METAL WALL PANELS FROM 8' TO EAVE) TO MATCH EXISTING
- EXISTING INTERIOR MASONRY WALL 8" TO REMAIN
- EXISTING EXTERIOR WALL (4" VENEER AIRSPACE WITH INSULATION ON STRUCTURAL 8" MASONRY WALL TO 8' WITH INSULATED METAL WALL PANELS FROM 8' TO EAVE) TO REMAIN
- EXISTING FORMED IN PLACE REINFORCED CONCRETE INTERIOR VAULT WALL TO REMAIN

PLAN NORTH

0 4' - 0" 8' - 0" 16' - 0"
SCALE: 1/8" = 1' - 0"

US Army Corps of Engineers ®

MARK	DESCRIPTION	DATE

File Path: C:\Users\Karen.Rutter\Documents\Ft Cavazos_Karen.rutter4VW2G.rvt

ISSUE DATE: 25-02-10
SOLICITATION NO.:
CONTRACT NO.:
PLOT DATE: 2/6/2025 5:12:25 PM
DESIGNED BY: KHR
DRAWN BY: KHR
CHECKED BY: TED
SUBMITTED BY: WEB
SIZE: ANSI D
FILENAME: US-XXXXXXA-A-103

US ARMY CORPS OF ENGINEERS
LOUISVILLE DISTRICT
600 DR MARTIN LUTHER KING JR PL.
LOUISVILLE, KY 40202


GMHILL
Michael Baker INTERNATIONAL
JOINT VENTURE

MAINTENANCE AND REPAIR ARMY RESERVE (ECS)
NORTH CAVAZOS, TX
BUILDING B5676?

FLOOR PLAN - AREA B

SHEET ID
A-103

PHASE 1 ADVERTISEMENT W912QR25RA013_Plans_Ph1-0000

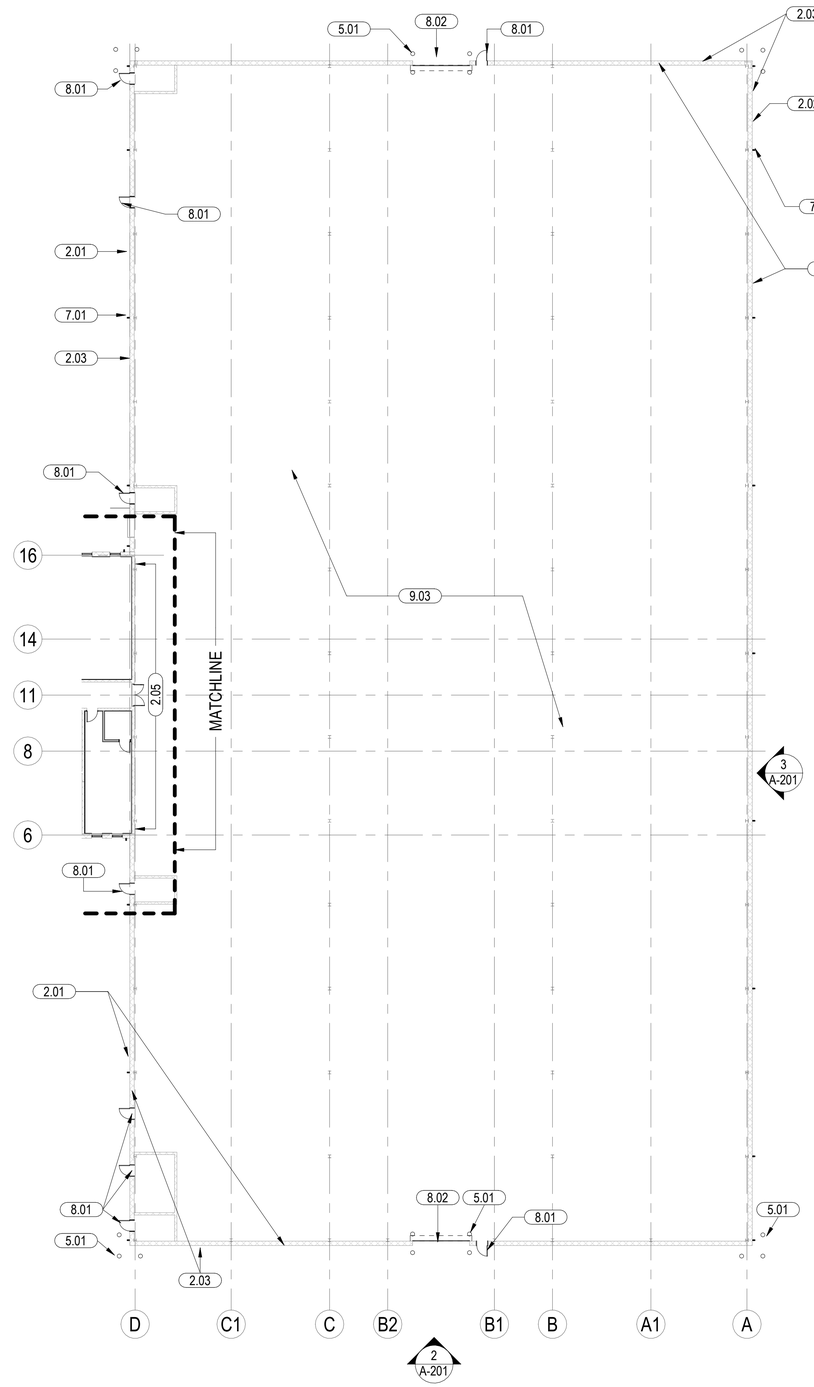


1 WAREHOUSE FLOOR PLAN
SCALE: 3/64" = 1'-0"

KEYNOTES

Key Value	Keynote Text
2.01	CLEAN EXTERIOR WALLS, REMOVE ORGANIC AND INORGANIC MATERIAL
2.02	SURVEY, DOCUMENT, AND REPAIR VEHICLE IMPACT DAMAGE TO EXTERIOR WALL(MASONRY) WITH MATCHING MATERIALS
2.03	COAT EXISTING MASONRY WALLS WITH PROTECTIVE ANTIMICROBIAL HYDROPHOBIC CLEAR COAT
2.05	INSPECT JOINT BETWEEN LOWER ROOF AND EXISTING WALL PANELS TO DETERMINE SOURCE OF WATER INTRUSION FOR REPAIR
5.01	BOLLARDS
7.01	REPLACE EXISTING GUTTERS AND DOWNSPOUTS
8.01	INSULATED HOLLOW METAL DOOR AND FRAME
8.02	INSULATED OVERHEAD COILING DOOR
9.03	CLEAN, REPAIR, PRIME AND PAINT UNDERSIDE OF METAL DECK

NOTES - FLOOR PLANS

1 THE PRELIMINARY DEMOLITION PLAN , FLOOR PLANS AND ELEVATIONS ARE FOR PROGRAMMATIC DISCUSSIONS ONLY. THESE DRAWINGS REPRESENT A POSSIBLE SOLUTION BUT ARE NOT INTENDED FOR CONSTRUCTION, NOR DO THEY INCLUDE ENGINEERING DESIGNS.

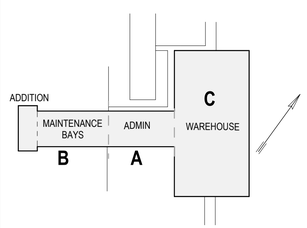

PLAN NORTH

0 16'-0" 32'-0" 64'-0"

SCALE: 3/64" = 1'-0"

US Army Corps of Engineers ®

MARK	DESCRIPTION	DATE

File Path: C:\Users\Karen.Rutter\Documents\Ft Cavazos_karen.rutter4VW2G.rvt

ISSUE DATE:	25-02-10
SOLICITATION NO.:	
CONTRACT NO.:	
PLOT DATE:	2/6/2025 5:12:25 PM
DESIGNED BY:	KHR
DRAWN BY:	KHR
CHECKED BY:	TED
SUBMITTED BY:	WBP2
SIZE:	ANSI D
FILENAME:	US-XXXXXXA-A-104

US ARMY CORPS OF ENGINEERS
LOUISVILLE DISTRICT
600 DR MARTIN LUTHER KING JR PL,
LOUISVILLE, KY 40202

GMHILL | Michael Baker INTERNATIONAL JOINT VENTURE


MAINTENANCE AND REPAIR ARMY RESERVE (ECS)
NORTH CAVAZOS, TX
BUILDING B56767

ENLARGED FLOOR PLAN - AREA C

SHEET ID


A-104

PHASE 1 ADVERTISEMENT W912QR25RA013_Plans_Ph1-0000

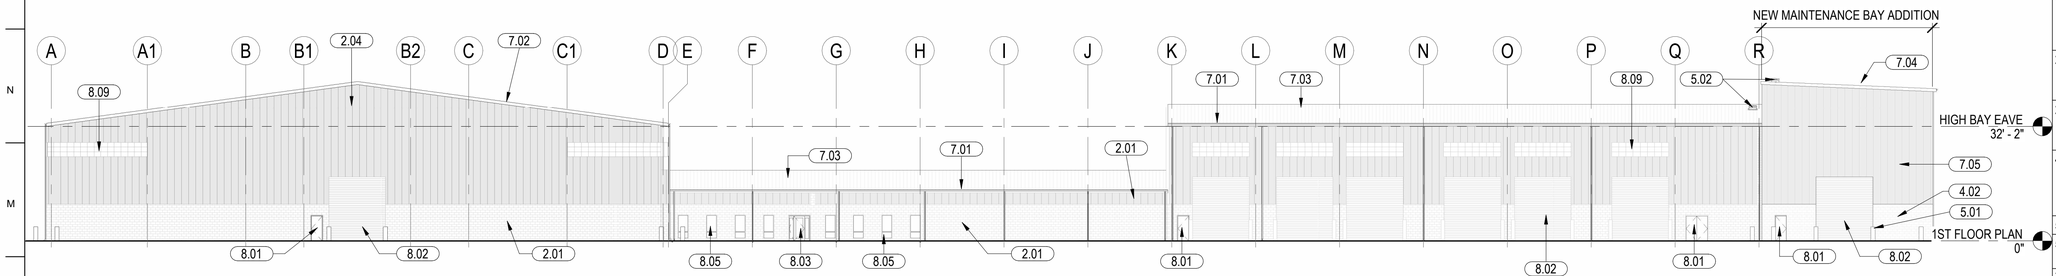


1 NORTH ELEVATION

SCALE: 3/64" = 1'-0"

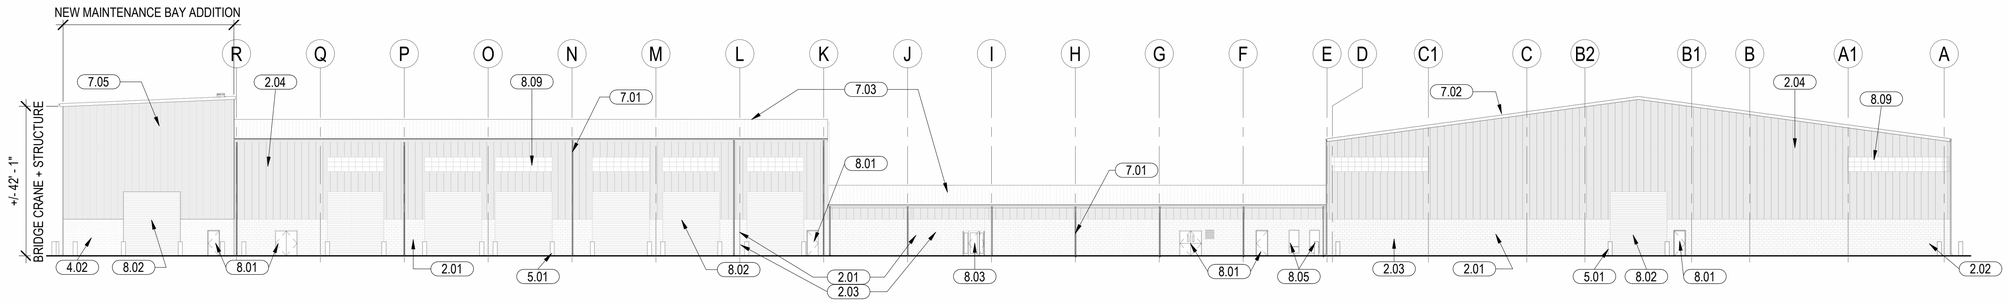


2 SOUTH ELEVATION

SCALE: 3/64" = 1'-0"

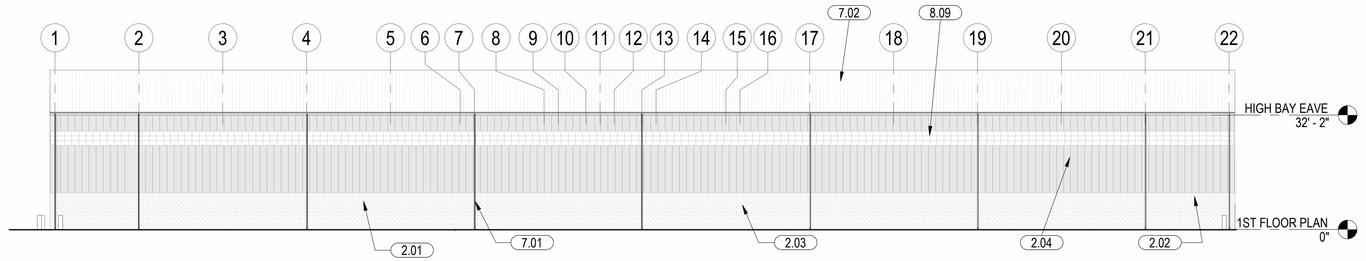

3 EAST ELEVATION

SCALE: 3/64" = 1'-0"

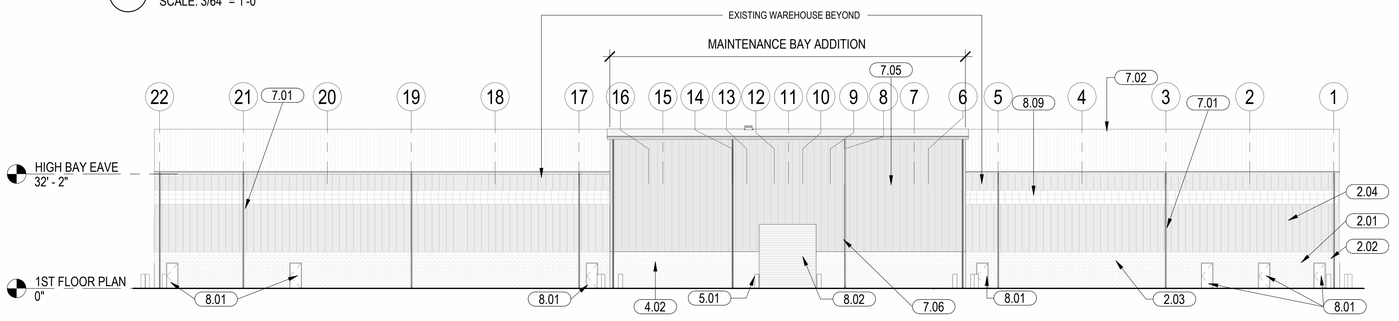

4 WEST ELEVATION

SCALE: 3/64" = 1'-0"

KEYNOTES

2.01	CLEAN EXTERIOR WALLS, REMOVE ORGANIC AND INORGANIC MATERIAL
2.02	SURVEY, DOCUMENT, AND REPAIR VEHICLE IMPACT DAMAGE TO EXTERIOR WALL(MASONRY) WITH MATCHING MATERIALS
2.03	COAT EXISTING MASONRY WALLS WITH PROTECTIVE ANTIMICROBIAL HYDROPHOBIC CLEAR COAT
2.04	CLEAN EXISTING METAL WALL PANELS, SURVEY AND DOCUMENT DAMAGE FOR REPAIR
4.02	MASONRY WALL- MATCH EXISTING VENEER INCLUDE AIRSPACE WATERPROOFING INSUALTION AND STRUCTURAL MASONRY WALL
5.01	BOLLARDS
5.02	SHIP LADDER - ROOF PERMANENT ACCESS
7.01	REPLACE EXISTING GUTTERS AND DOWNSPOUTS
7.02	CLEAN, PRIME, AND COAT EXISTING STANDING SEAM ROOF COVERING WITH FLUID APPLIED ACRYLIC ROOF MEMBRANE
7.03	REPLACE EXISTING ROOF COVERING AND INSULATION WITH NEW STANDING SEAM METAL ROOFING AND UNDERLAMENT OVER NEW INSULATION
7.04	STANDING SEAM METAL ROOFING, UNDERLAMENT, INSULATION ON STRUCTURAL STEEL DECK
7.05	INSULATED METAL WALL PANELS - MATCH EXISTING PATTERN AND COLOR
7.06	GUTTERS AND DOWNSPOUTS
8.01	INSULATED HOLLOW METAL DOOR AND FRAME
8.02	INSULATED OVERHEAD COILING DOOR
8.03	ALUMINUM STOREFRONT ENTRY DOOR
8.05	ALUMINUM WINDOW MATCH WITH EXISTING
8.09	EXISTING TRANSLUCENT RESIN DAYLIGHTING PANEL SYSTEM TO REMAIN

NOTES - FLOOR PLANS

1 THE PRELIMINARY DEMOLITION PLAN , FLOOR PLANS AND ELEVATIONS ARE FOR PROGRAMMATIC DISCUSSIONS ONLY. THESE DRAWINGS REPRESENT A POSSIBLE SOLUTION BUT ARE NOT INTENDED FOR CONSTRUCTION, NOR DO THEY INCLUDE ENGINEERING DESIGNS.

0 16'-0" 32'-0" 64'-0"

SCALE: 3/64" = 1'-0"

US Army Corps of Engineers ®

MARK	DESCRIPTION	DATE

File Path: C:\Users\Karen.Rutter\Documents\Ft Cavazos_karen.rutter4-WX2G1.rvt

DESIGNED BY: KHR
DRAWN BY: KHR
CHECKED BY: TED
SUBMITTED BY: KHR
SIZE: ANSI D
ISSUE DATE: 25-02-10
SOLICITATION NO.:
CONTRACT NO.:
PLOT DATE: 2/7/2025 5:07:36 AM
FILENAME: US-XXXXXXA-A-201

US ARMY CORPS OF ENGINEERS
LOUISVILLE DISTRICT
600 DR MARTIN LUTHER KING JR PL.
LOUISVILLE, KY 40202

GMHILL
Michael Baker INTERNATIONAL
JOINT VENTURE

MAINTENANCE AND REPAIR ARMY RESERVE (ECS)
NORTH CAVAZOS, TX
BUILDING B56767

EXTERIOR ELEVATIONS

SHEET ID


A-201

PHASE 1 ADVERTISEMENT W912QR25RA013_Plans_Ph1-0000

FURNITURE SCHEDULE		
MARK	TYPE	COUNT
CH-1	TASK CHAIR	37
CH-2	GUEST CHAIR W/ARMS	18
CH-3	STACKING CHAIR	30
CH-5	MOTHERS ROOM RECLINER	1
CH-6	TASK CHAIR - STOOL	3
D-1	WORKSTATION - 6' X 6'	10
D-2	DESK - 6' X 6'	6
D-3	DESK - 9' X 10' W/ CREDENZA	1
D-4	WORKSTATION - W/ MOBILE PED	20
LN-1	LECTERN	1
SC-1	STORAGE CABINET 36"X 72"	1
ST-1	SIDE TABLE	1
T-1	TRAINING TABLE	15
T-2	TABLE - 36" ROUND	2
T-6	WORKBENCH	3

FURNITURE SCHEDULE		
MARK	TYPE	COUNT
CH-1	TASK CHAIR	37
CH-2	GUEST CHAIR W/ARMS	18
CH-3	STACKING CHAIR	30
CH-5	MOTHERS ROOM RECLINER	1
CH-6	TASK CHAIR - STOOL	3
D-1	WORKSTATION - 6' X 6'	10
D-2	DESK - 6' X 6'	6
D-3	DESK - 9' X 10' W/ CREDENZA	1
D-4	WORKSTATION - W/ MOBILE PED	20
LN-1	LECTERN	1
SC-1	STORAGE CABINET 36"X 72"	1
ST-1	SIDE TABLE	1
T-1	TRAINING TABLE	15
T-2	TABLE - 36" ROUND	2
T-6	WORKBENCH	3

SPECIALTY EQUIPMENT SCHEDULE		
MARK	TYPE	COUNT
EQ-1	REFRIGERATOR	1
EQ-6	SNACK MACHINE	1
EQ-7	BEVERAGE MACHINE	2
EQ-9	<varies>	30
EQ-10	72" Shelf	3
R-2	RECYCLING BIN 23GAL	1
R-3	WASTE BIN - 64 GAL	1
W-2	TRASH BIN 23GAL	1
W-3	WASTE BIN - 64 GAL	2

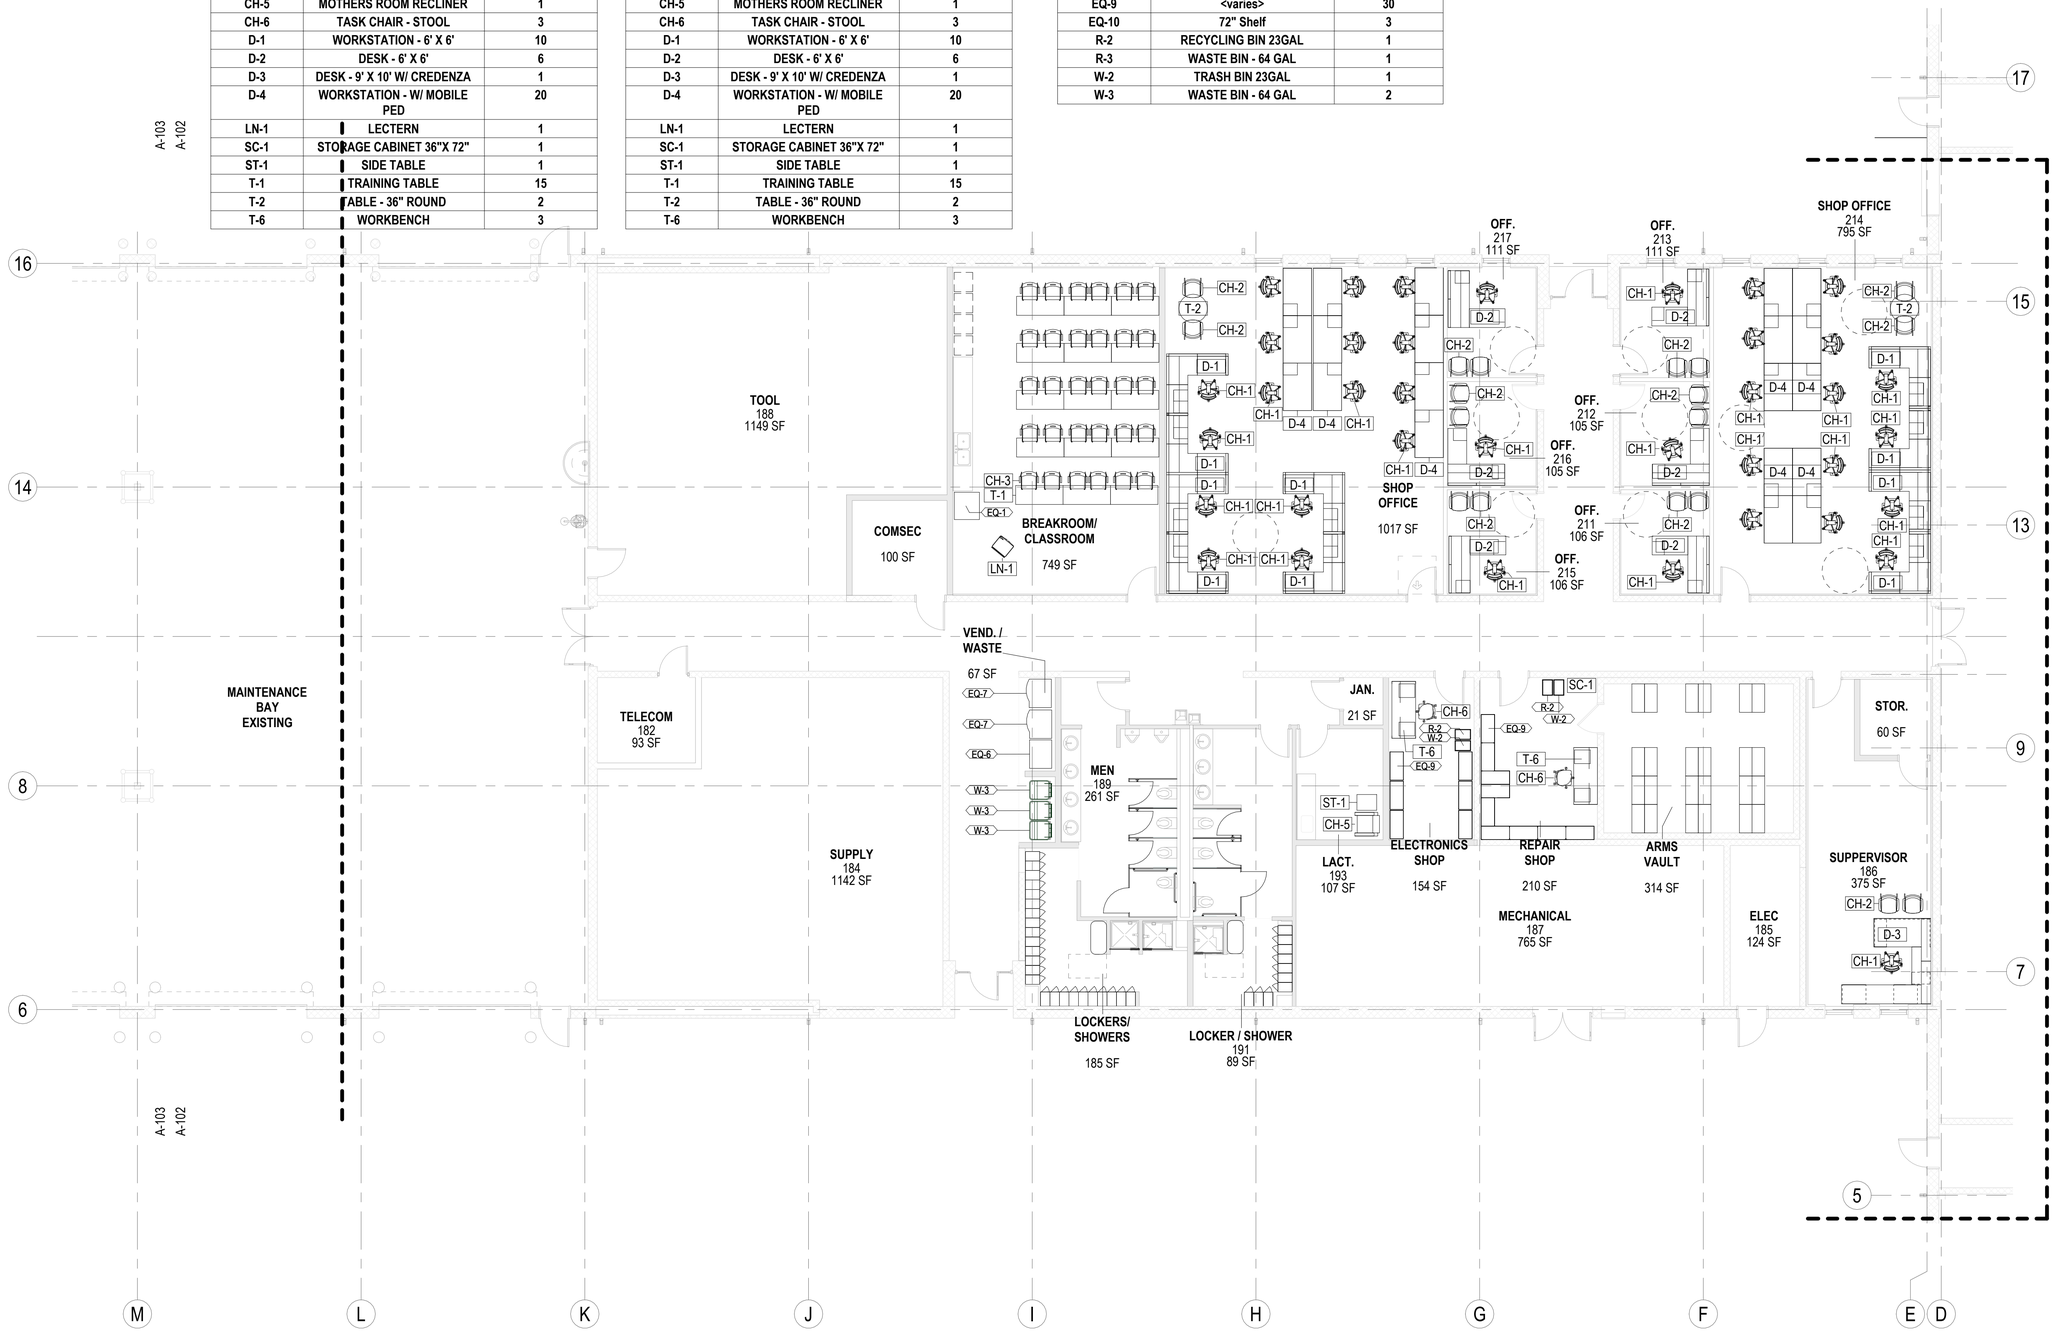

1 COMPREHENSIVE FURNITURE FLOOR PLAN - AREA A
SCALE: 1/8" = 1'-0"

PLAN NORTH N

0 4' - 0" 8' - 0" 16' - 0"
SCALE: 1/8" = 1' - 0"

US Army Corps of Engineers ®

MARK	DESCRIPTION	DATE

File Path: C:\Users\Karen.Rutter\Documents\Ft Cavazos_karen.rutter4VW2G.rvt

ISSUE DATE: 25-02-10
SOLICITATION NO.:
CONTRACT NO.:
PLOT DATE: 2/6/2025 5:12:37 PM
DESIGNED BY: JLF
DRAWN BY: JLF
CHECKED BY: TED
SUBMITTED BY:
VARIES
SIZE: ANSI D
FILENAME: US-XXXXXXA-IF110

US ARMY CORPS OF ENGINEERS
LOUISVILLE DISTRICT
600 DR MARTIN LUTHER KING JR PL.
LOUISVILLE, KY 40202


GMHILL
Michael Baker INTERNATIONAL
JOINT VENTURE

MAINTENANCE AND REPAIR ARMY RESERVE (ECS)
NORTH CAVAZOS, TX
BUILDING B56767

COMPREHENSIVE FURNITURE FLOOR PLAN - AREA A

SHEET ID
IF110

PHASE 1 ADVERTISEMENT W912QR25RA013_Plans_Ph1-0000

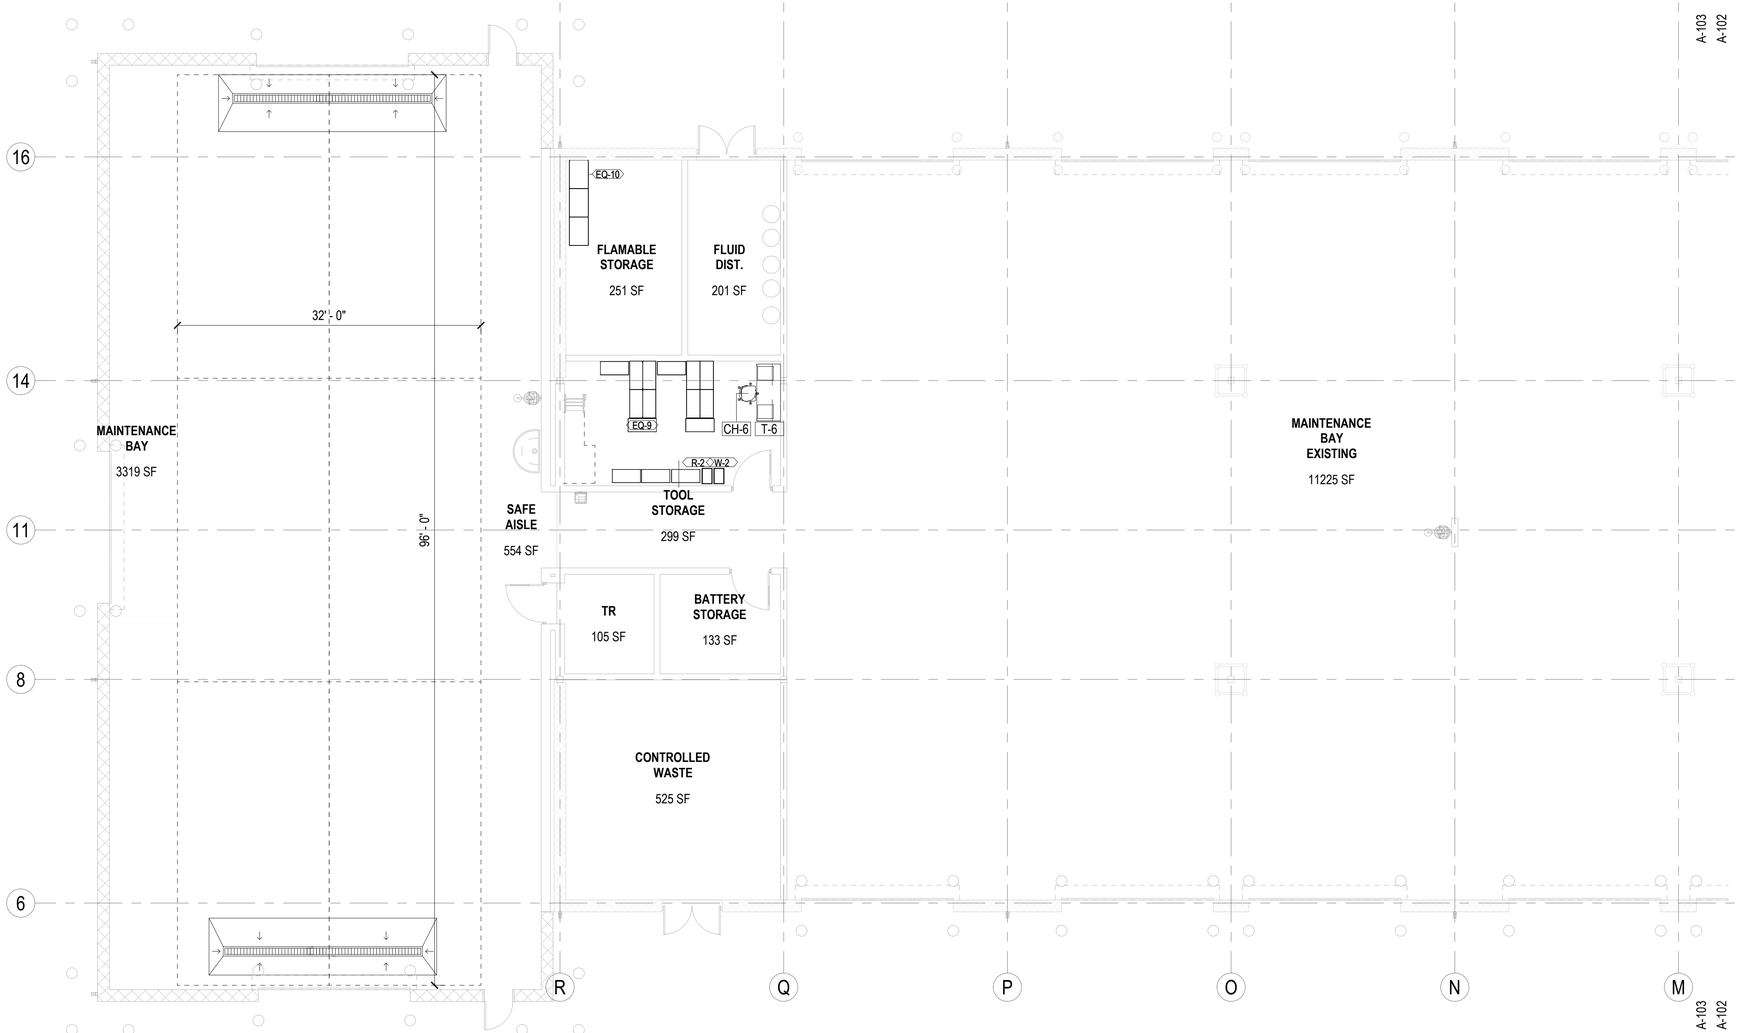

1 COMPREHENSIVE FURNITURE FLOOR PLAN - AREA B
SCALE: 1/8" = 1'-0"

FURNITURE SCHEDULE

MARK	TYPE	COUNT
CH-1	TASK CHAIR	37
CH-2	GUEST CHAIR W/ARMS	18
CH-3	STACKING CHAIR	30
CH-5	MOTHERS ROOM RECLINER	1
CH-6	TASK CHAIR - STOOL	3
D-1	WORKSTATION - 6' X 6'	10
D-2	DESK - 6' X 6'	6
D-3	DESK - 9' X 10' W/ CREDENZA	1
D-4	WORKSTATION - W/ MOBILE PED	20
LN-1	LECTERN	1
SC-1	STORAGE CABINET 36"X 72"	1
ST-1	SIDE TABLE	1
T-1	TRAINING TABLE	15
T-2	TABLE - 36" ROUND	2
T-6	WORKBENCH	3

SPECIALTY EQUIPMENT SCHEDULE

MARK	TYPE	COUNT
EQ-1	REFRIGERATOR	1
EQ-6	SNACK MACHINE	1
EQ-7	BEVERAGE MACHINE	2
EQ-9	<varies>	30
EQ-10	72" Shelf	3
R-2	RECYCLING BIN 23GAL	1
R-3	WASTE BIN - 64 GAL	1
W-2	TRASH BIN 23GAL	1
W-3	WASTE BIN - 64 GAL	2

PLAN NORTH
N

0 4' - 0" 8' - 0" 16' - 0"
SCALE: 1/8" = 1' - 0"

US Army Corps of Engineers ®

MARK	DESCRIPTION	DATE

File Path: C:\Users\Karen.Rutter\Documents\Ft Cavazos_Karen.rutter4VW2G.rvt

ISSUE DATE: 25-02-10
SOLICITATION NO.:
CONTRACT NO.:
PLOT DATE: 2/6/2025 5:12:38 PM
DESIGNED BY: JLF
DRAWN BY: JLF
CHECKED BY: TED
SUBMITTED BY:
SIZE: ANSI D
FILENAME: US-XXXXXXA-IF112

US ARMY CORPS OF ENGINEERS
LOUISVILLE DISTRICT
600 DR MARTIN LUTHER KING JR PL,
LOUISVILLE, KY 40202

GMHILL
Michael Baker INTERNATIONAL
JOINT VENTURE

MAINTENANCE AND REPAIR ARMY RESERVE (ECS)
NORTH CAVAZOS, TX
BUILDING B56767

COMPREHENSIVE FURNITURE FLOOR PLAN - AREA B

SHEET ID
IF112

PHASE 1 ADVERTISEMENT W912QR25RA013_Plans_Ph1-0000