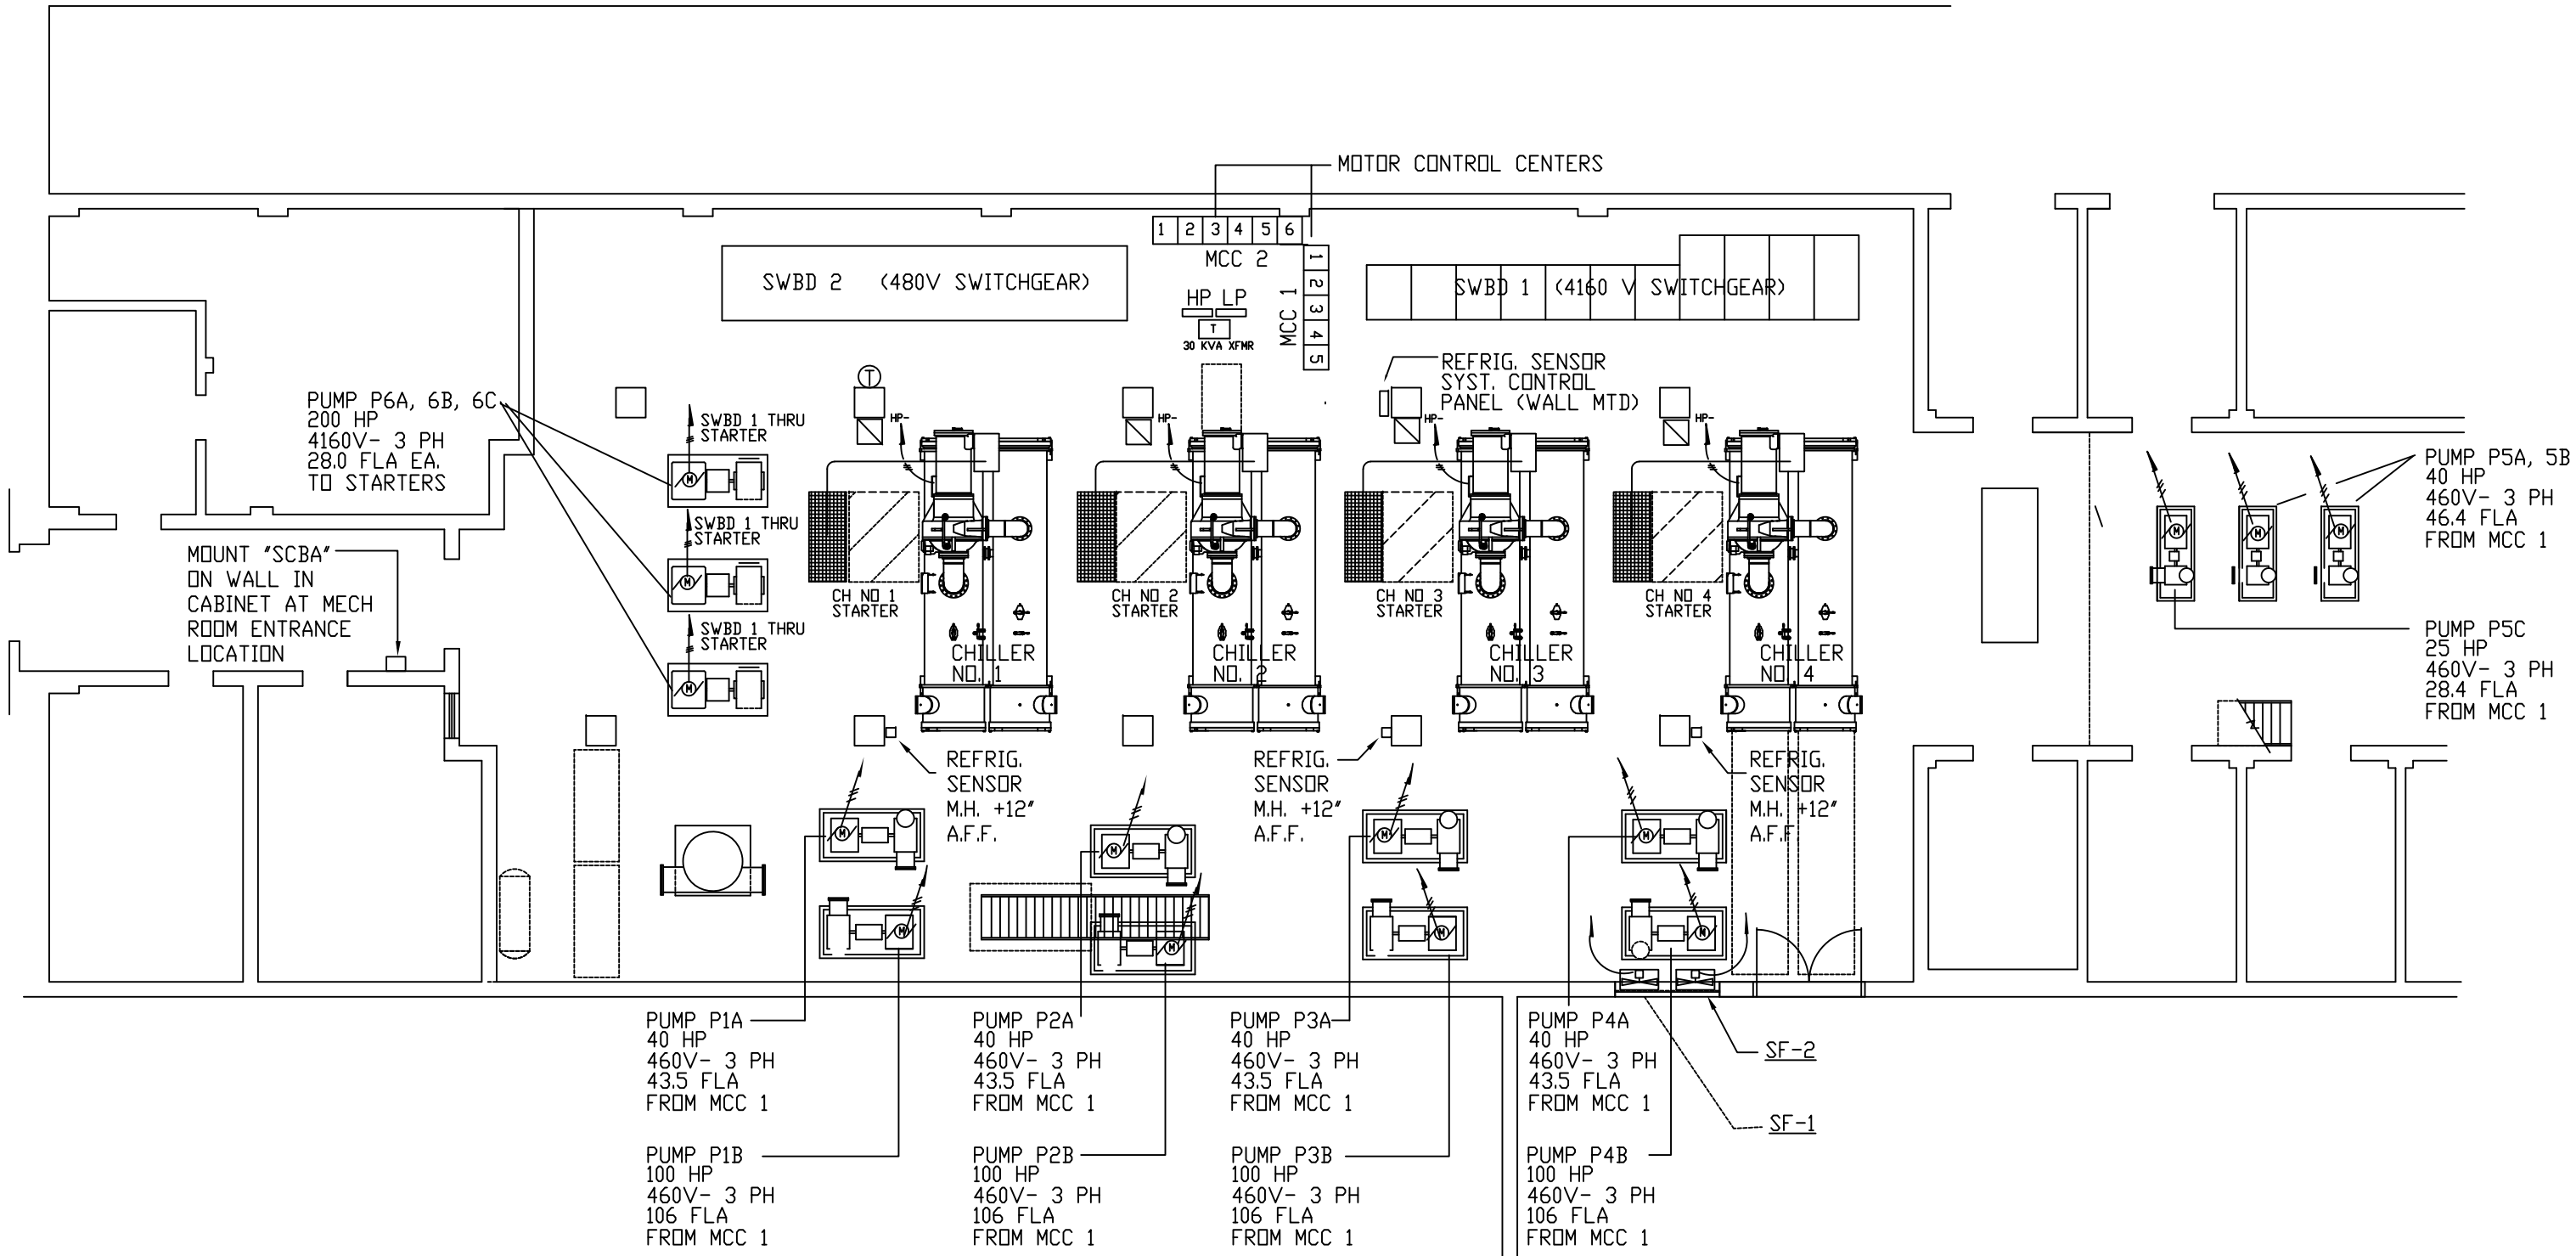


CHILLER PLANT FLOOR PLAN (BSMT) - ELECTRICAL - POWER

SCALE: 1/8"=1'-0"

\\bepfiles\ofs$\FACILITY_MASTER_DRAWINGS\Chilled_Water_Plant\BEP-E1R613.DWG, 7/21/2026 12:24:08 PM, Adobe PDF