
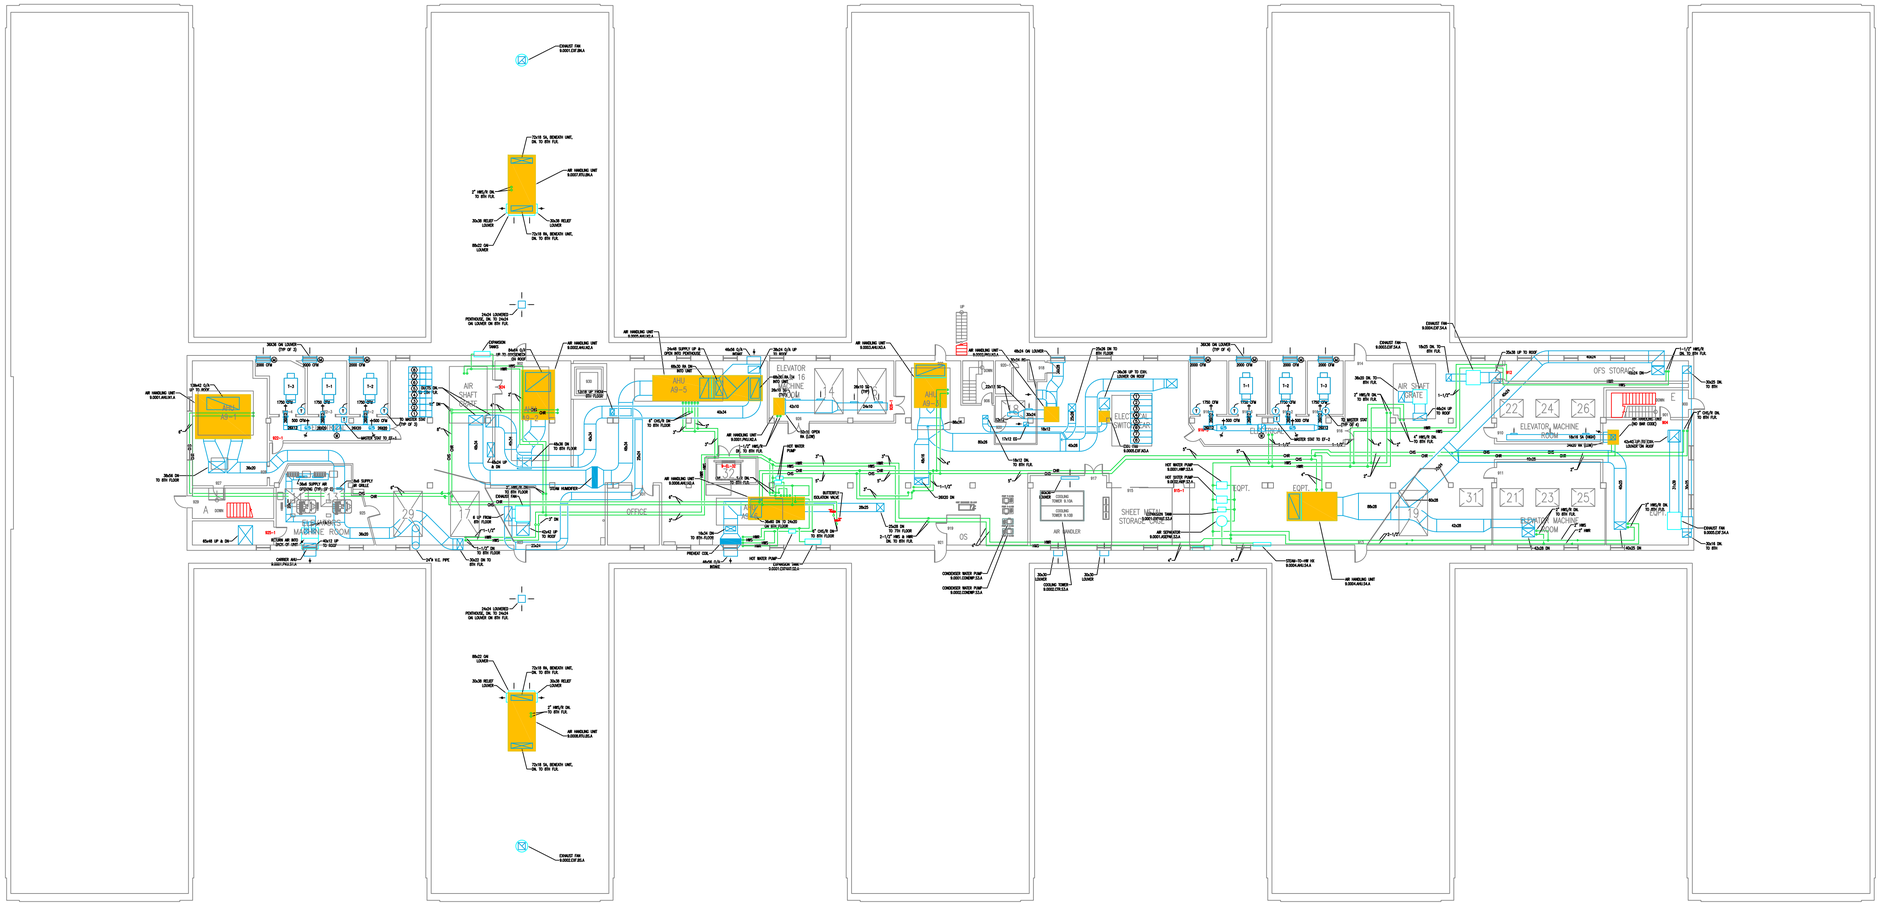


EQUIPMENT DESIGNATIONS

- (A.) MITSUBISHI "MR. SLIM" HI-WALL A/C UNIT WITH 1/2" REFRIGERANT LINE.
- (B.) FRIEDRICH RESIDENTIAL-TYPE WINDOW A/C UNIT, MOUNTED IN WALL.
- (C.) CEILING-MOUNTED, UNDUCTED FAN COIL UNIT.
- (D.) CEILING-MOUNTED STEAM HUMIDIFIER.
- (E.) FLOOR-MOUNTED FAN COIL UNIT.
- (F.) FLOOR-MOUNTED RADIATOR.

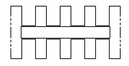

9TH FLOOR ANNEX BUILDING
KEYPLAN

0 10' 20' 40'
SCALE: 1" = 20'-0"

DEPARTMENT OF THE TREASURY
BUREAU OF ENGRAVING AND PRINTING

HVAC MASTER
ANNEX BUILDING
NINTH FLOOR

DRAWN BY: EM	DATE: 08/21/14
CHECKED BY:	DATE:
DATE OF ISSUE: 10/28/24	
SHEET: 15 OF: 15	DWG. NO. 1001023
SCALE: 1" = 20'-0"	