RENOVATE SURGICAL SUITE PHASE II

DEPARTMENT OF VETERANS AFFAIRS PROJECT NO. 658-19-103

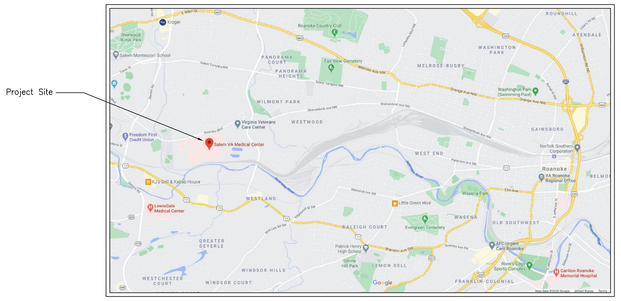

LOCATION MAP
SCALE: NTS

SALEM VA MEDICAL CENTER
1970 ROANOKE BOULEVARD
SALEM, VIRGINIA 24153

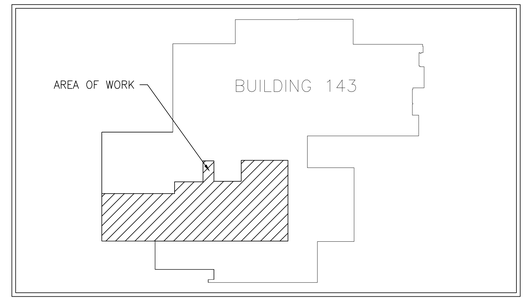

BUILDING KEY PLAN
SCALE: NTS

ACTUAL NORTH
PLAN NORTH

PROJECT CONSULTANTS

ENGINEER OF RECORD	ARCHITECT	CIVIL ENGINEER	FIRE & LIFE SAFETY	PHYSICAL SECURITY	COST ESTIMATOR
MILLER-REMICK, LLC 856-429-4000 WWW.MILLER-REMICK.COM	PF&A DESIGN, P.C. 757-471-0537 WWW.PFA-ARCHITECT.COM	LABELLA ASSOCIATES 301-835-0543 WWW.LABELLAPC.COM	STANTON ENGINEERING SERVICES, LLC 410-290-9301 WWW.STANTONENGINEERING.COM	FORCE PROTECT SECURITY CONSULTANTS 502-836-4232 WWW.FORCE-PROTECT.COM	PREFERRED CONSTRUCTION MANAGEMENT 973-853-6060 PCMCOMPANY.COM

DRAWING INDEX

DRAWING No.	DRAWING TITLE
	GENERAL
GI001	COVER SHEET
GI002	BUILDING REGULATION DATA & ICRA NOTES
GI003	LIFE SAFETY PLAN - FIRST FLOOR - OVERALL
GI004	LIFE SAFETY PLAN - BID DEDUCT
GI005	SMOKE COMPARTMENT & SUITE PLANS - FIRST FLOOR
GI006	OCCUPANT LOAD PLAN - FIRST FLOOR
	CIVIL
C-100	EXISITNG CONDITIONS
C-110	DEMOLITION & EROSION CONTROL PLANS
C-200	SITE LAYOUT & WATERLINE PROFILE
C-400	EROSION & SEDIMENT CONTROL NOTES
C-401	EROSION & SEDIMENT CONTROL DETAILS
C-402	EROSION & SEDIMENT CONTROL DETAILS
C-500	CONSTRUCTION DETAILS
C-501	CONSTRUCTION DETAILS
	STRUCTURAL
S-001	ABBREVIATIONS & NOTES
S-002	NOTES
SS101	SITE PLAN
SS501	SECTIONS & DETAILS
P1-SF101	BASEMENT PLAN - PHASE 1
P1-SF111	FRAMING PLAN - 1ST FLOOR, PHASE 1
P1-SF121	FRAMING PLAN - ROOF, PHASE 1
P1-SF123	DUNNAGE FRAMING PLAN - ROOF, PHASE 1
P2-SF122	FRAMING PLAN - 2ND FLOOR, PHASE 2
SF151	FRAMING PLAN - 5TH FLOOR ROOF
S-501	SECTIONS & DETAILS
S-502	SECTIONS & DETAILS
S-503	SECTIONS & DETAILS
S-504	SECTIONS & DETAILS
S-505	SECTIONS & DETAILS
	ARCHITECTURAL
A-001	ABBREVIATIONS, SYMBOLS, LEGENDS, NOTES & WALL TYPE SCHEDULE
A-010	PHASING PLANS - FIRST FLOOR - OVERALL
A-011	ICRA PLAN - FIRST FLOOR - PHASE 1
A-012	ICRA PLAN - FIRST FLOOR - PHASE 2
A-013	ICRA PLAN - FIRST FLOOR - PHASE 3

DRAWING No.	DRAWING TITLE
	ARCHITECTURAL (CONTINUED)
A-014	ICRA PLAN - FIRST FLOOR - PHASE 4
AD100	DEMOLITION PLAN - BASEMENT
AE100	NEW WORK PLAN - FIRST FLOOR - OVERALL
AC100	REFLECTED CEILING PLAN - FIRST FLOOR - OVERALL
AI100	FINISH PLAN - FIRST FLOOR - OVERALL
AE110	DEMOLITION, NEW WORK, & RELFECTED CEILING PLANS - FIRST FLOOR - BID DEDUCT
AE111	FINISH PLAN & SCHEDULE - FIRST FLOOR - BID DEDUCT
P1-AD100	DEMOLITION PLANS - FIRST FLOOR - PHASE 1
P1-AE100	NEW WORK PLAN - FIRST FLOOR - PHASE 1
P1-AC100	REFLECTED CEILING PLAN - FIRST FLOOR - PHASE 1
P1-AQ100	EQUIPMENT PLAN - FIRST FLOOR - PHASE 1
P1-AI100	FINISH PLAN - FIRST FLOOR - PHASE 1
P2-AD100	DEMOLITION PLANS - FIRST FLOOR - PHASE 2
P2-AE100	NEW WORK PLAN - FIRST FLOOR - PHASE 2
P2-AE101	NEW WORK PLAN - FIRST FLOOR - PHASE 2 (NORTH)
P2-AC100	REFLECTED CEILING PLAN - FIRST FLOOR - PHASE 2
P2-AC101	REFLECTED CEILING PLAN - FIRST FLOOR - PHASE 2 (NORTH)
P2-AQ100	EQUIPMENT PLAN - FIRST FLOOR - PHASE 2
P2-AQ101	EQUIPMENT PLAN - FIRST FLOOR - PHASE 2 (NORTH)
P2-AI100	FINISH PLAN - FIRST FLOOR - PHASE 2
P2-AI101	FINISH PLAN - FIRST FLOOR - PHASE 2 (NORTH)
P3-AD100	DEMOLITION PLAN - FIRST FLOOR - PHASE 3
P3-AE100	NEW WORK PLAN - FIRST FLOOR - PHASE 3
P3-AC100	REFLECTED CEILING PLAN - FIRST FLOOR - PHASE 3
P3-AQ100	EQUIPMENT PLAN - FIRST FLOOR - PHASE 3
P3-AI100	FINISH PLAN - FIRST FLOOR - PHASE 3
P4-AD100	DEMOLITION PLAN - FIRST FLOOR - PHASE 4
P4-AE100	NEW WORK PLAN - FIRST FLOOR - PHASE 4
P4-AC100	REFLECTED CEILING PLAN - FIRST FLOOR - PHASE 4
P4-AQ100	EQUIPMENT PLAN - FIRST FLOOR - PHASE 4
P4-AI100	FINISH PLAN - FIRST FLOOR - PHASE 4
AE300	NEW WORK / ROOF PLAN - SECOND FLOOR
AE301	OVERALL ROOF & PENTHOUSE FLOOR PLAN
AE400	ELEVATIONS
AE500	BULDING SECTION & CEILING DETAILS
AE510	SECTIONS & DETAILS
AE600	DOOR & WINDOW ELEVATIONS, DOOR SCHEDULES & DETAILS
AE610	FINISH LEGEND & INTERIOR DETAILS
AI800	INTERIOR ELEVATIONS
AI801	INTERIOR ELEVATIONS
AI810	CASEWORK DETAILS
AI811	CASEWORK DETAILS

DRAWING No.	DRAWING TITLE
	FIRE SUPPRESSION
FX001	COVER SHEET
FX101	NEW WORK PLAN - GENERATOR BUILDING
P1-FK101	DEMOLITION PLAN - FIRST FLOOR - PHASE 1
P1-FX101	NEW WORK PLAN - FIRST FLOOR - PHASE 1
P2-FK101	DEMOLITION PLAN - FIRST FLOOR - PHASE 2
P2-FX101	NEW WORK PLAN - FIRST FLOOR - PHASE 2
P3-FK101	DEMOLITION PLAN - FIRST FLOOR - PHASE 3
P3-FX101	NEW WORK PLAN - FIRST FLOOR - PHASE 3
P4-FK101	DEMOLITION PLAN - FIRST FLOOR - PHASE 4
P4-FX101	NEW WORK PLAN - FIRST FLOOR - PHASE 4
FX501	DETAILS
	PLUMBING
P-001	ABBREVIATIONS, NOTES & SYMBOLS
P1-PD111	DEMOLITION PLAN - 1ST FLOOR, PHASE 1
P1-P-111	NEW WORK PLAN - 1ST FLOOR, PHASE 1
P1-P-112	NEW WORK PLAN - 1ST FLOOR, PHASE 1
P1-P-113	NEW WORK PLAN - MECHANICAL ROOM, PHASE 1
P2-PD111	DEMOLITION PLAN - 1ST FLOOR, PHASE 2 (SOUTH)
P2-PD112	DEMOLITION PLAN - 1ST FLOOR, PHASE 2 (NORTH)
P2-P-111	NEW WORK PLAN - 1ST FLOOR, PHASE 2 (SOUTH)
P2-P-112	NEW WORK PLAN - 1ST FLOOR, PHASE 2 (NORTH)
P3-PD111	DEMOLITION PLAN - 1ST FLOOR, PHASE 3
P3-P-111	NEW WORK PLAN - 1ST FLOOR, PHASE 3
P4-PD111	DEMOLITION PLAN - 1ST FLOOR, PHASE 4
P4-P-111	NEW WORK PLAN - 1ST FLOOR, PHASE 4
P-501	DETAILS
P-502	DETAILS
P-601	ISOMETRIC DIAGRAM MEDICAL GAS
P-602	ISOMETRIC DIAGRAM DOMESTIC WATER
P-603	ISOMETRIC DIAGRAM SANITARY & VENT
P-701	SCHEDULES
	MECHANICAL
M-001	ABBREVIATIONS, NOTES & SYMBOLS
MD601	DEMOLITION - CHILLED WATER FLOW DIAGRAM
P1-MD100	PIPING DEMOLITION PLAN - SUB BASEMENT, PHASE 1
P1-MD101	DEMOLITION PLAN - BASEMENT, PHASE 1
P1-MD102	DEMOLITION PLAN - BASEMENT GENERATOR, PHASE 1
P1-MD103	DEMOLITION PLAN - BASEMENT, PHASE 1

DRAWING No.	DRAWING TITLE
	MECHANICAL (CONTINUED)
P1-MD111	DEMOLITION DUCTWORK PLAN - 1ST FLOOR, PHASE 1
P1-MD112	DEMOLITION PLAN - MECHANICAL ROOM, PHASE 1
P1-MD121	DEMOLITION ROOF PLAN, PHASE 1
P1-MH101	DUCTWORK PLAN - BASEMENT, PHASE 1
P1-MH111	DUCTWORK PLAN - 1ST FLOOR, PHASE 1
P1-MH112	DUCTWORK PLAN - MECHANICAL ROOM, PHASE 1
P1-MH121	DUCTWORK PLAN - ROOF, PHASE 1
P1-MP100	PIPING PLAN - SUB-BASEMENT
P1-MP102	PIPING PLAN - BASEMENT GENERATOR, PHASE 1
P1-MP103	PIPING PLAN - BASEMENT CHILLER, PHASE 1
P1-MP111	PIPING PLAN - 1ST FLOOR, PHASE 1
P1-MP112	PIPING PLAN - MECHANICAL ROOM, PHASE 1
P2-MD111	DEMOLITION DUCTWORK PLAN - 1ST FLOOR, PHASE 2
P2-MD112	DEMOLITION DUCKWORK PLAN - 1ST FLOOR, PHASE 2 (NORTH)
P2-MD113	DEMOLITION PLAN - MECHANICAL ROOM, PHASE 2
P2-MH111	DUCTWORK PLAN - 1ST FLOOR, PHASE 2 (SOUTH)
P2-MH112	DUCTWORK PLAN - 1ST FLOOR, PHASE 2 (NORTH)
P2-MH113	DUCTWORK PLAN - MECHANICAL ROOM, PHASE 2
P2-MH121	DUCTWORK PLAN - ROOF, PHASE 2
P2-MP111	PIPING PLAN - 1ST FLOOR, PHASE 2 (SOUTH)
P2-MP112	PIPING PLAN - 1ST FLOOR, PHASE 2 (NORTH)
P2-MP113	PIPING PLAN - MECHANICAL ROOM, PHASE 2
P3-MD111	DEMOLITION DUCTWORK PLAN - 1ST FLOOR, PHASE 3
P3-MH111	DUCTWORK PLAN - 1ST FLOOR, PHASE 3
P3-MH112	DUCTWORK PLAN - MECHANICAL ROOM, PHASE 3
P3-MH121	DUCTWORK PLAN - ROOF, PHASE 3
P3-MP111	PIPING PLAN - 1ST FLOOR, PHASE 3
P3-MP112	PIPING PLAN - MECHANICAL ROOM, PHASE 3
P4-MD111	DEMOLITION DUCTWORK PLAN - 1ST FLOOR, PHASE 4
P4-MD112	DEMOLITION PLAN - MECHANICAL ROOM, PHASE 4
P4-MH111	DUCTWORK PLAN - 1ST FLOOR, PHASE 4
P4-MH121	DUCTWORK PLAN - ROOF, PHASE 4
P4-MP111	PIPING PLAN - 1ST FLOOR, PHASE 4
M-301	SECTIONS
M-501	DETAILS
M-502	DETAILS
M-503	DETAILS
M-504	DETAILS
M-601	AIR FLOW DIAGRAM - PHASE 1
M-602	AIR FLOW DIAGRAM - PHASES 2 & 3
M-603	AIR FLOW DIAGRAM - PHASE 4
M-604	CHILLED WATER FLOW DIAGRAM

DRAWING No.	DRAWING TITLE
	MECHANICAL (CONTINUED)
M-605	CHILLED WATER FLOW DIAGRAM
M-606	NO. 2 FUEL OIL FLOW DIAGRAM - GENERATORS
M-701	SCHEDULES
M-702	SCHEDULES
M-703	SCHEDULES
M-704	SCHEDULES
M-801	CONTROLS
M-802	AHU FOR SURGICAL SUITE (VAV) DIAGRAM
M-803	AHU FOR SURGICAL SUITE (VAV) POINTS SUMMARY
M-804	CONTROLS DIAGRAMS
M-805	ISOLATION PATIENT ROOM & EXHAUST FAN CONTROL DIAGRAM
M-806	AIR COOLED CHILLER & CHILLED WATER CONTROL DIAGRAM
M-807	AIR TERMINAL UNIT CONTROL DIAGRAM
	ELECTRICAL
E-001	ABBREVIATIONS & SYMBOLS
E-002	NOTES
ES101	SITE PLAN
ED111	DEMOLITION PLAN - MECHANICAL ROOM
EP111	POWER PLAN - MECHANICAL ROOM
EP121	POWER PLAN - ROOF
P1-ED101	DEMOLITION PLAN - BASEMENT, PHASE 1
P1-ED111	DEMOLITION PLAN - 1ST FLOOR, PHASE 1
P1-EL111	LIGHTING PLAN - 1ST FLOOR, PHASE 1
P1-EP100	POWER PLAN - SUB-BASEMENT, PHASE 1
P1-EP101	POWER PLAN - BASEMENT, PHASE 1
P1-EP102	POWER PLAN - BASEMENT, PHASE 1
P1-EP111	POWER PLAN - 1ST FLOOR, PHASE 1
P1-EY111	SYSTEMS PLAN - 1ST FLOOR, PHASE 1
P2-ED111	DEMOLITION PLAN - 1ST FLOOR, PHASE 2 (SOUTH)
P2-ED112	DEMOLITION PLAN - 1ST FLOOR, PHASE 2 (NORTH)
P2-EL111	LIGHTING PLAN - 1ST FLOOR, PHASE 2 (SOUTH)
P2-EL112	LIGHTING PLAN - 1ST FLOOR, PHASE 2 (NORTH)
P2-EP111	POWER PLAN - 1ST FLOOR, PHASE 2 (SOUTH)
P2-EP112	POWER PLAN - 1ST FLOOR, PHASE 2 (NORTH)
P2-EY111	SYSTEMS PLAN - 1ST FLOOR, PHASE 2 (SOUTH)
P2-EY112	SYSTEMS PLAN - 1ST FLOOR, PHASE 2 (NORTH)
P3-ED111	DEMOLITION PLAN - 1ST FLOOR, PHASE 3
P3-EL111	LIGHTING PLAN - 1ST FLOOR, PHASE 3
P3-EP111	POWER PLAN - 1ST FLOOR, PHASE 3
P3-EY111	SYSTEMS PLAN - 1ST FLOOR, PHASE 3

DRAWING No.	DRAWING TITLE
	ELECTRICAL (CONTINUED)
P4-ED111	DEMOLITION PLAN - 1ST FLOOR, PHASE 4
P4-EL111	LIGHTING PLAN - 1ST FLOOR, PHASE 4
P4-EP111	POWER PLAN - 1ST FLOOR, PHASE 4
P4-EY111	SYSTEMS PLAN - 1ST FLOOR, PHASE 4
E-501	DETAILS
E-502	DETAILS
E-503	O.R. DETAILS
E-504	HYBRID O.R. DETAILS
E-505	HYBRID O.R. DETAILS
E-506	HYBRID O.R. DETAILS
E-507	HYBRID O.R. DETAILS
E-601	DEMOLITION - SINGLE LINE DIAGRAM
E-602	NEW WORK - SINGLE LINE DIAGRAM
E-603	TELE/DATA RISER DIAGRAM
E-701	PANEL SCHEDULES
E-702	PANEL SCHEDULES
E-703	ISOLATION PANEL SCHEDULES
E-704	SCHEDULES & LIGHTING CONTROL RISER DIAGRAM
E-705	RELAY PANEL SCHEDULES
	FIRE ALARM
FA001	COVER SHEET
FA101	NEW WORK PLAN - GENERATOR BUILDING
P1-FD101	DEMOLITION PLAN - FIRST FLOOR - PHASE 1
P1-FA101	NEW WORK PLAN - FIRST FLOOR - PHASE 1
P2-FD101	DEMOLITION PLAN - FIRST FLOOR - PHASE 2
P2-FA101	NEW WORK PLAN - FIRST FLOOR - PHASE 2
P3-FD101	DEMOLITION PLAN - FIRST FLOOR - PHASE 3
P3-FA101	NEW WORK PLAN - FIRST FLOOR - PHASE 3
P4-FD101	DEMOLITION PLAN - FIRST FLOOR - PHASE 4
P4-FA101	NEW WORK PLAN - FIRST FLOOR - PHASE 4
FA501	DETAILS

PRINTS OF THIS DRAWING SHALL NOT BE USED FOR ANY PURPOSE WHATSOEVER WITHOUT THE SEAL AND SIGNATURE OF THE PROFESSIONAL ENGINEER.

NO.	DESCRIPTION	DATE

CONSULTANTS

Architecture:	Civil Engineering:	Fire & Life Safety:
PF&A DESIGN, P.C.	LABELLA ASSOCIATES	STANTON ENGINEERING SERVICES, LLC

ENGINEER OF RECORD

MILLER-REMICK
A Service-Disabled Veteran-Owned Small Business
(856) 429-4000 • Miller-Remick.com
M-R PROJECT NO 0499-0136

MILLER-REMICK LLC
PROFESSIONAL ENGINEER

COMMONWEALTH OF VIRGINIA
ANTHONY DANIEL PACARO JR.
Lic. No. 402055079
PROFESSIONAL ENGINEER
12.30.2025

Office of Construction and Facilities Management

VA U.S. Department of Veterans Affairs

Drawing Title: GENERAL COVER SHEET	Phase: BID DOCUMENTS	Project Title: RENOVATE SURGICAL SUITE PHASE II	VA Drawing Number: 2617
Approved by: Jon Manninen, COR	FULLY SPRINKLERED	Project Number: 658-19-103	Building Number: 143
		Location: SALEM VA MEDICAL CENTER	Drawing Number: GI001
		Issue Date: 2025-12-30 / Checked: DJ / Drawn: MC/VR	

VA FORM 08-6231

P:\0499_DVA\0499-0136 Salem Renovate Surgical Suite\4_Drawings\1_Cad\1_Current Submittal Phase\0_Cover Sheet\GI001.dwg 12-30-25 10:00:30 AM vroot

Infection Control Risk Mitigation Recommendations Matrix of Precautions for Construction and Renovation

Type of Construction / Project Activity Table

TYPE A	Inspection and Non-Invasive Activities Includes, but is not limited to: -Removal of ceiling tiles for visual inspection limited to 20 Ln Ft tile per 160 sq. ft. space. -Painting (but not sanding). -Wall covering, electrical trim work, minor plumbing, and activities which do not generate dust or require cutting of walls or access to ceilings other than for visual inspection. -Patching walls - not exceeding 8 sq. ft.
TYPE B	Small scale, short duration activities which create minimal dust. Includes, but is not limited to: -Installation of telephone and computer cabling. -Access to chase spaces. -Cutting of walls or ceiling where dust migration can be controlled. -Patching walls - exceeding 8 sq. ft.
TYPE C	Work that generates a moderate to high level of dust or requires demolition or removal of any fixed building components and assemblies or new construction. Includes, but is not limited to: -Sanding of walls for painting or wall covering exceeding 32 sq. ft., or vacant areas. -Removal of floor coverings, ceiling tiles and casework. -New wall construction -Uncontained duct, HVAC or electrical work above ceilings. -Major cabling activities. -Any other project where high levels of dust are generated.
TYPE D	Major demolition and construction projects Includes, but is not limited to: -Activities that require consecutive work shifts -Requires heavy demolition or removal of a complete cabling system. -New Construction.

PATIENT RISK GROUP TABLE

GROUP 1 LOW RISK	GROUP 2 MEDIUM RISK	GROUP 3 HIGH RISK	GROUP 4 HIGHEST RISK
- ADMINISTRATIVE OFFICES - PUBLIC CORRIDORS - ELEVATORS - DAY ROOMS - CANTEEN RETAIL STORE - VACANT WARDS OR VACANT ICU'S ETC.	- OUTPATIENT, URGENT CARE & PRIMARY CARE CLINICS - LABORATORY - CARDIOLOGY - ECHOCARDIOGRAPHY - ENDOSCOPY - FOOD SERVICES - INTERIM CARE & MEDICAL UNITS - NUCLEAR MEDICINE - PHARMACY - PHYSICAL THERAPY - RADIOLOGY & NUCLEAR MEDICINE - RESPIRATORY THERAPY	- CCU - EMERGENCY ROOM - LABORATORY - OUTPATIENT SURGERY - PHARMACY - POST ANESTHESIA CARE UNIT - SURGICAL UNITS	- ANY AREA CARING FOR IMMUNICOMPROMISED PATIENTS - SPD STORAGE / STERILIZATION - INTENSIVE CARE UNITS - TB NEGATIVE PRESSURE ISOLATION ROOMS -OPERATING ROOM

INFECTION CONTROL MATRIX - CLASS OF PRECAUTIONS: CONSTRUCTION PROJECT BY PATIENT RISK

PATIENT RISK GROUP	CONSTRUCTION PROJECT TYPE			
	TYPE A	TYPE B	TYPE C	TYPE D
LOW RISK GROUP 1	I	II	II	III/IV
MEDIUM RISK GROUP 2	I	II	II	IV
HIGH RISK GROUP 3	I	II	III/IV	IV
HIGHEST RISK GROUP 4	II	III/IV	III/IV	IV

NOTE: INFECTION CONTROL APPROVAL WILL BE REQUIRED WHEN THE CONSTRUCTION ACTIVITY AND RISK LEVEL INDICATE THAT CLASS III OR CLASS IV CONTROL PROCEDURES ARE NECESSARY.

IT IS THE CONTRACTOR'S RESPONSIBILITY TO PROVIDE THE FOLLOWING INFECTION CONTROL PRECAUTIONS DEPENDING UPON THE AREA CLASS DESIGNATION

	DURING CONSTRUCTION PROJECT	UPON COMPLETION OF PROJECT
CLASS I	1. EXECUTE WORK BY METHODS TO MINIMIZE RAISING DUST FROM CONSTRUCTION OPERATIONS. 2. IMMEDIATELY REPLACE A CEILING TILE DISPLACED FOR VISUAL INSPECTIONS.	
CLASS II	1. PROVIDE ACTIVE MEANS TO PREVENT AIRBORNE DUST FROM DISPERSING INTO ATMOSPHERE. 2. WATER MIST WORK SURFACES TO CONTROL DUST WHILE CUTTING. 3. SEAL UNUSED DOORS WITH DUCT TAPE. 4. BLOCK OFF AND SEAL AIR VENTS. 5. PLACE DUST MAT AT ENTRANCE AND EXIT OF WORK AREA. 6. REMOVE OR ISOLATE HVAC SYSTEM IN AREAS WHERE WORK IS BEING PERFORMED.	1. WIPE WORK SURFACES WITH DISINFECTANT. 2. CONTAIN CONSTRUCTION WASTE BEFORE TRANSPORT IN TIGHTLY COVERED CONTAINERS. 3. WIPE WORK SURFACES WITH DISINFECTANT, WET MOP AND/OR VACUUM WITH HEPA VACUUM BEFORE LEAVING WORK AREA. 4. REMOVE ISOLATION OF HVAC.

	DURING CONSTRUCTION PROJECT	UPON COMPLETION OF PROJECT
CLASS III	1. REMOVE OR ISOLATE HVAC SYSTEM IN AREA WHERE WORK IS BEING DONE TO PREVENT CONTAMINATION OF DUCT SYSTEM. 2. COMPLETE ALL CRITICAL BARRIERS, I.E., SHEETROCK, PLYWOOD, PLASTIC, TO SEAL AREA FROM NON-WORK AREA OR IMPLEMENT CONTROL CUBE METHOD (CART WITH PLASTIC COVERING AND SEALED CONNECTION TO WORK SITE WITH HEPA VACUUM FOR VACUUMING PRIOR TO EXIT) BEFORE CONSTRUCTION BEGINS. 3. MAINTAIN NEGATIVE AIR PRESSURE WITHIN WORK SITE UTILIZING HEPA EQUIPPED AIR FILTRATION UNITS. 4. CONTAIN CONSTRUCTION WASTE BEFORE TRANSPORT IN TIGHTLY COVERED CONTAINERS. 5. COVER TRANSPORT RECEPTACLES OR CARTS. TAPE COVERING UNLESS SOLID LID.	1. DO NOT REMOVE BARRIERS FROM WORK AREA UNTIL COMPLETED PROJECT IS INSPECTED BY THE ENVIRONMENTAL HEALTH AND SAFETY AND INFECTION CONTROL AND THOROUGHLY CLEANED BY ENVIRONMENTAL SANITATION SECTION. 2. REMOVE BARRIER MATERIALS CAREFULLY TO MINIMIZE SPREADING OF DIRT AND DEBRIS ASSOCIATED WITH CONSTRUCTION. 3. VACUUM WORK AREA WITH HEPA FILTERED VACUUMS. 4. WET MOP AREA WITH DISINFECTANT. 5. REMOVE ISOLATION OF HVAC SYSTEM IN AREAS WHERE WORK IS BEING PERFORMED.
CLASS IV	1. OBTAIN INFECTION CONTROL PERMIT BEFORE CONSTRUCTION BEGINS. 2. ISOLATE HVAC SYSTEM IN AREA WHERE WORK IS BEING DONE TO PREVENT CONTAMINATION OF DUCT SYSTEM. 3. COMPLETE ALL CRITICAL BARRIERS OR IMPLEMENT CONTROL CUBE METHOD BEFORE CONSTRUCTION BEGINS. 4. MAINTAIN NEGATIVE AIR PRESSURE WITHIN WORK SITE UTILIZING HEPA EQUIPPED AIR FILTRATION UNITS. 5. SEAL HOLES, PIPES, CONDUITS AND PUNCTURES APPROPRIATELY. 6. CONSTRUCT ANTEROOM AND REQUIRE ALL PERSONNEL TO PASS THROUGH THIS ROOM SO THEY CAN BE VACUUMED USING A HEPA VACUUM CLEANER BEFORE LEAVING WORK SITE OR THEY CAN WEAR CLOTH OR PAPER COVERALLS THAT ARE REMOVED EACH TIME THEY LEAVE THE WORK SITE. 7. ALL PERSONNEL ENTERING WORK SITE ARE REQUIRED TO WEAR SHOE COVERS.	1. DO NOT REMOVE BARRIERS FROM WORK AREA UNTIL COMPLETED PROJECT IS THOROUGHLY CLEANED BY ENVIRONMENTAL MANAGEMENT. 2. VACUUM WORK AREA WITH HEPA FILTERED VACUUMS. 3. WET MOP AREA WITH DISINFECTANT. 4. REMOVE BARRIER MATERIALS CAREFULLY TO MINIMIZE SPREADING OF DIRT AND DEBRIS ASSOCIATED WITH CONSTRUCTION. 5. CONTAIN CONSTRUCTION WASTE BEFORE TRANSPORT IN TIGHTLY COVERED CONTAINERS. 6. COVER TRANSPORT RECEPTACLES OR CARTS. TAPE COVERING. 7. REMOVE ISOLATION OF HVAC SYSTEM IN AREAS WHERE WORK IS BEING PERFORMED.

ALL WORK ON 1ST FLOOR IS CONSTRUCTION TYPE D, RISK GROUP 4, CLASS DESIGNATION IV
ALL WORK IN THE BASEMENT IS CONSTRUCTION TYPE C, RISK GROUP 1,CLASS DESIGNATION II

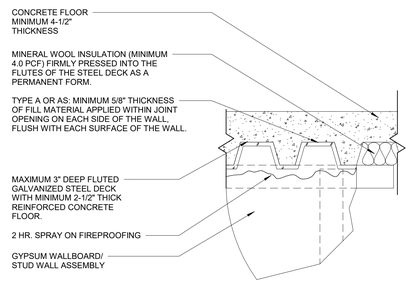

UL SYSTEM HW-D-0262
FOR FLUTED STEEL DECK/
CONCRETE FLOOR ASSEMBLY
AND GYPSUM WALLBOARD WALL
1 &2 HR. RATING
JOINT WIDTH: 1" MAXIMUM

1 GI002 FIRE STOPPING DETAIL
1 1/2" = 1'-0"

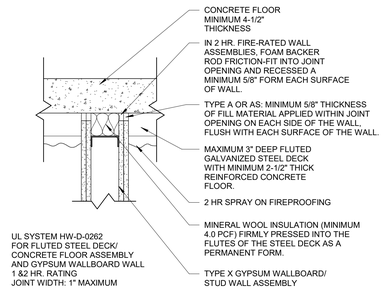

UL SYSTEM HW-D-0262
FOR FLUTED STEEL DECK/
CONCRETE FLOOR ASSEMBLY
AND GYPSUM WALLBOARD WALL
1 &2 HR. RATING
JOINT WIDTH: 1" MAXIMUM

2 GI002 FIRE STOPPING DETAIL - TOP OF WALL
1 1/2" = 1'-0"

FIRE RATINGS

CONSTRUCTION TYPE		TYPE I (3,3,2)
CONSTRUCTION ELEMENTS		HOURS
BEARING WALLS	EXTERIOR	
	SUPPORTING MORE THAN ONE FLOOR, COLUMNS, OR OTHER BEARING WALLS	3
	SUPPORTING ONE FLOOR ONLY	3
	SUPPORTING A ROOF ONLY	3
	INTERIOR	
	SUPPORTING MORE THAN ONE FLOOR, COLUMNS, OR OTHER BEARING WALLS	3
	SUPPORTING ONE FLOOR ONLY	2
	SUPPORTING A ROOF ONLY	2
COLUMNS	SUPPORTING MORE THAN ONE FLOOR, COLUMNS, OR OTHER BEARING WALLS	3
	SUPPORTING ONE FLOOR ONLY	2
	SUPPORTING A ROOF ONLY	2
BEAMS, GIRDERS, TRUSSES AND ARCHES	SUPPORTING MORE THAN ONE FLOOR, COLUMNS, OR OTHER BEARING WALLS	3
	SUPPORTING ONE FLOOR ONLY	2
	SUPPORTING A ROOF ONLY	2
FLOOR / CEILING ASSEMBLIES		2
ROOF / CEILING ASSEMBLIES		1 1/2
INTERIOR NONBEARING WALLS		0
EXTERIOR NONBEARING WALLS		0

GENERAL NOTES:

1) ALL RATED INTERIOR PARTITION SHOULD BE CONSTRUCTED IN ACCORDANCE WITH THE RATED PARTITION SCHEDULE UNLESS NOTED OTHERWISE ON THE FLOOR PLANS

CODE REQUIREMENTS

APPLICABLE CODES:

- NFPA-10 STANDARD FOR PORTABLE FIRE EXTINGUISHERS, 2018
- NFPA-70 NATIONAL ELECTRICAL CODE, 2008
- NFPA-99 HEALTHCARE FACILITIES CODE, 2021
- NFPA 101 LIFESAFETY CODE, 2021
- NFPA-220 STANDARD TYPE OF BUILDING CONSTRUCTION, 2021
- PG 18-12 -SURGICAL AND ENDOVASCULAR SERVICES DESIGN GUIDE APRIL 2016 (REV 08/23)
- PG 18-14 -ROOM FINISHES, DOOR & HARDWARE SCHEDULE
- VA FIRE PROTECTION DESIGN MANUAL 9TH EDITION NOVEMBER 2023

APPLICABLE CODE EXCERPTS :

1. ALL REQUIRED HANDRAILS, GUARDS, AND GRAB BARS SHALL BE DESIGNED AND CONSTRUCTIED TO THE STRUCTURAL LOADING CONDITIONS IN SECTION 4.4 OF ACSE 7.

	NFPA 101
BUILDING OCCUPANCY CLASSIFICATION	HEALTHCARE (EXISTING)
TYPE OF CONSTRUCTION	TYPE I (3, 3, 2)
FIRE SUPPRESSION SYSTEM	NFPA 13 SPRINKLER SYSTEM
FIRE EXTINGUISHER	
TYPE	2-A (TABLE 6.2.1.1)
TRAVEL DISTANCE	75 FT. (TABLE 6.2.1.1)
BUILDING HEIGHT	30'-4" (ETR)
BUILDING STORIES	UNLIMITED
BUILDING AREA	22,920 DGSF
EXITS - MINIMUM NUMBER REQUIRED	2 REQ < 500 OCCUPANTS. (NFPA 101, 7.4.1.1)
SEPARATION DISTANCE OF EXITS (OVERALL DIAGONAL OF THE AREA SERVED)	1/3 L - SPRINKLERED (NFPA 101,7.5.1.3.3) 1/2 L - NON-SPRINKLERED (NFPA 101,7.5.1.3.2)
AREA OF REFUGE	N/A
STAIRWAY WIDTH	N/A
STAIR CLEAR WIDTH (1005.3.1)	N/A
CORRIDOR WIDTH	CORRIDORS I-2 BED MOVEMENT = 96 INCHES CORRIDOR ACCESS (MIN.) = 60 INCHES
EGRESS CLEAR WIDTH NFPA 101, 7.3.3.1 (1005.3.2)	164" 2=33" , 36" MINIMUM APPLIES - APPEARS TO BE 168" PROVIDED
DEAD END CORRIDOR	30 FT. SPRINKLED (NFPA 101,18.2.5.2)
COMMON PATH OF TRAVEL	100 FT. SPRINKLED (NFPA 101,18.2.5.3)
TRAVEL DISTANCE	200 FT. SPRINKLED (NFPA 101,18.2.6.2.1)
OCCUPANT LOAD SEE SHEET GI006 FOR OCCUPANT LOAD PLAN	• AMBULATORY (100 SF/OCC) - 20,728 NSF - 208 OCCUPANT • UNCONCENTRATED ASSEMBLY (15 SF/OCC) - 185 NSF - 13 OCCUPANT • STORAGE AND MECHANICAL (300 SF/OCC) - 1,876 NSF - 7 OCCUPANT • **TOTAL OCCUPANT LOAD = 228 OCCUPANTS** (TABLE 7.3.1.2)
PLUMBING FIXTURES	
INTERIOR FINISHES	NFPA 101, 18.3.3.2
INTERIOR WALL AND CEILING REQUIREMENTS	CLASS B NFPA 101, 10.2.8.1 CLASS B OR C = SPACES < 4 PEOPLE FINISHES 48"H MAX AFF NFPA 101, 10.2.8.1
INTERIOR FLOOR REQUIREMENTS	CLASS II OR A MINIMUM CRITICAL RADIANT FLUX OF 0.1 W/SQ CM (NFPA 101,10.2.8.2)
SMOKE COMPARTMENTS	
SIZE	CAN BE UP TO 40,000 SF MAX SINCE NO PATIENT SLEEPING ROOMS ARE IN THE RENOVATION SMOKE ZONE - 22,500 SF MAX (NFPA 101, 18.3.7.1.3)
TRAVEL DISTANCE	200 FT. (NFPA 101,18.2.6.2.1)
ASSEMBLY RATINGS: WALLS, DOORS, GLAZING	WALL - "SMOKE BARRIER" 1 HOUR DOOR - 1/3 HOUR (PROVIDE CLOSER 18.3.7.8.1) GLAZING - 3/4 HOUR (NFPA 101,TABLE 8.3.3.2.2)
SUITES	
SIZE	
SLEEPING	10,000 SF MAX - SMOKE DEDECTION (18.2.5.7.2.3.C)
NON-SLEEPING	15,000 SF MAX - SMOKE DEDECTION (NFPA 101, 18.2.5.7.2.3.2.B)
NUMBER OF EXITS	
SLEEPING	2 REQUIRED ≥ 1000 SF (NFPA 101,18.2.5.7.2.2.B)
NON-SLEEPING	2 REQUIRED ≥ 2500 SF (NFPA 101,18.2.5.7.3.2.B)
TRAVEL DISTANCE	100 FT. TO SUITE EXIT ACCESS DOOR (NFPA 101, 18.2.5.7.2.4.A AND 18.2.5.7.3.3.A)
ASSEMBLY RATINGS: WALLS, DOORS, GLAZING	• WALL - "SMOKE PARTITION" (NFPA 101, 18.2.5.7.1.2 AND 18.3.6.2) • DOOR - CLOSER **NOT** REQUIRED (NFPA 101, 18.3.6.3) *SEAL ASSEMBLIES TO LIMIT PASSAGE OF SMOKE
FIRE WALL LABELING	

PRINTS OF THIS DRAWING SHALL NOT BE USED FOR ANY PURPOSE WHATSOEVER WITHOUT THE SEAL AND SIGNATURE OF THE PROFESSIONAL ENGINEER

Revisions: | Date:

CONSULTANT

Architecture:	Civil Engineering:	Fire Protection:
PF&A DESIGN, P.C.	LABELLA ASSOCIATES	STANTON ENGINEERING SERVICES, LLC

ENGINEER OF RECORD

MILLER•REMICK
A Service-Disabled Veteran-Owned Small Business
(856) 429-4000 Miller-Remick.com
M-R PROJECT NO: 04990-0136

PF&A DESIGN, P.C.
REGISTERED ARCHITECT
COMMONWEALTH OF VIRGINIA
JOSEPH H. TROST
NO. 7843
2025-12-30
REGISTERED ARCHITECT

Office of Construction and Facilities Management

VA U.S. Department of Veterans Affairs

Drawing Title: GENERAL INFORMATION
BUILDING REGULATION DATA & ICRA NOTES

Approved by: Jon Manninen, COR

Phase: BID DOCUMENTS

FULLY SPRINKLERED

Project Title: RENOVATE SURGICAL SUITE PHASE II
Project Number: 658-19-103

Location: SALEM VA MEDICAL CENTER

Issue Date: 2025-12-30 | Checked: DJP | Drawn: MAT

VA Drawing Number: 2617
Building Number: 143
Drawing Number: GI002

12/29/2025 1:41:12 AM

VA FORM 08 - 6231

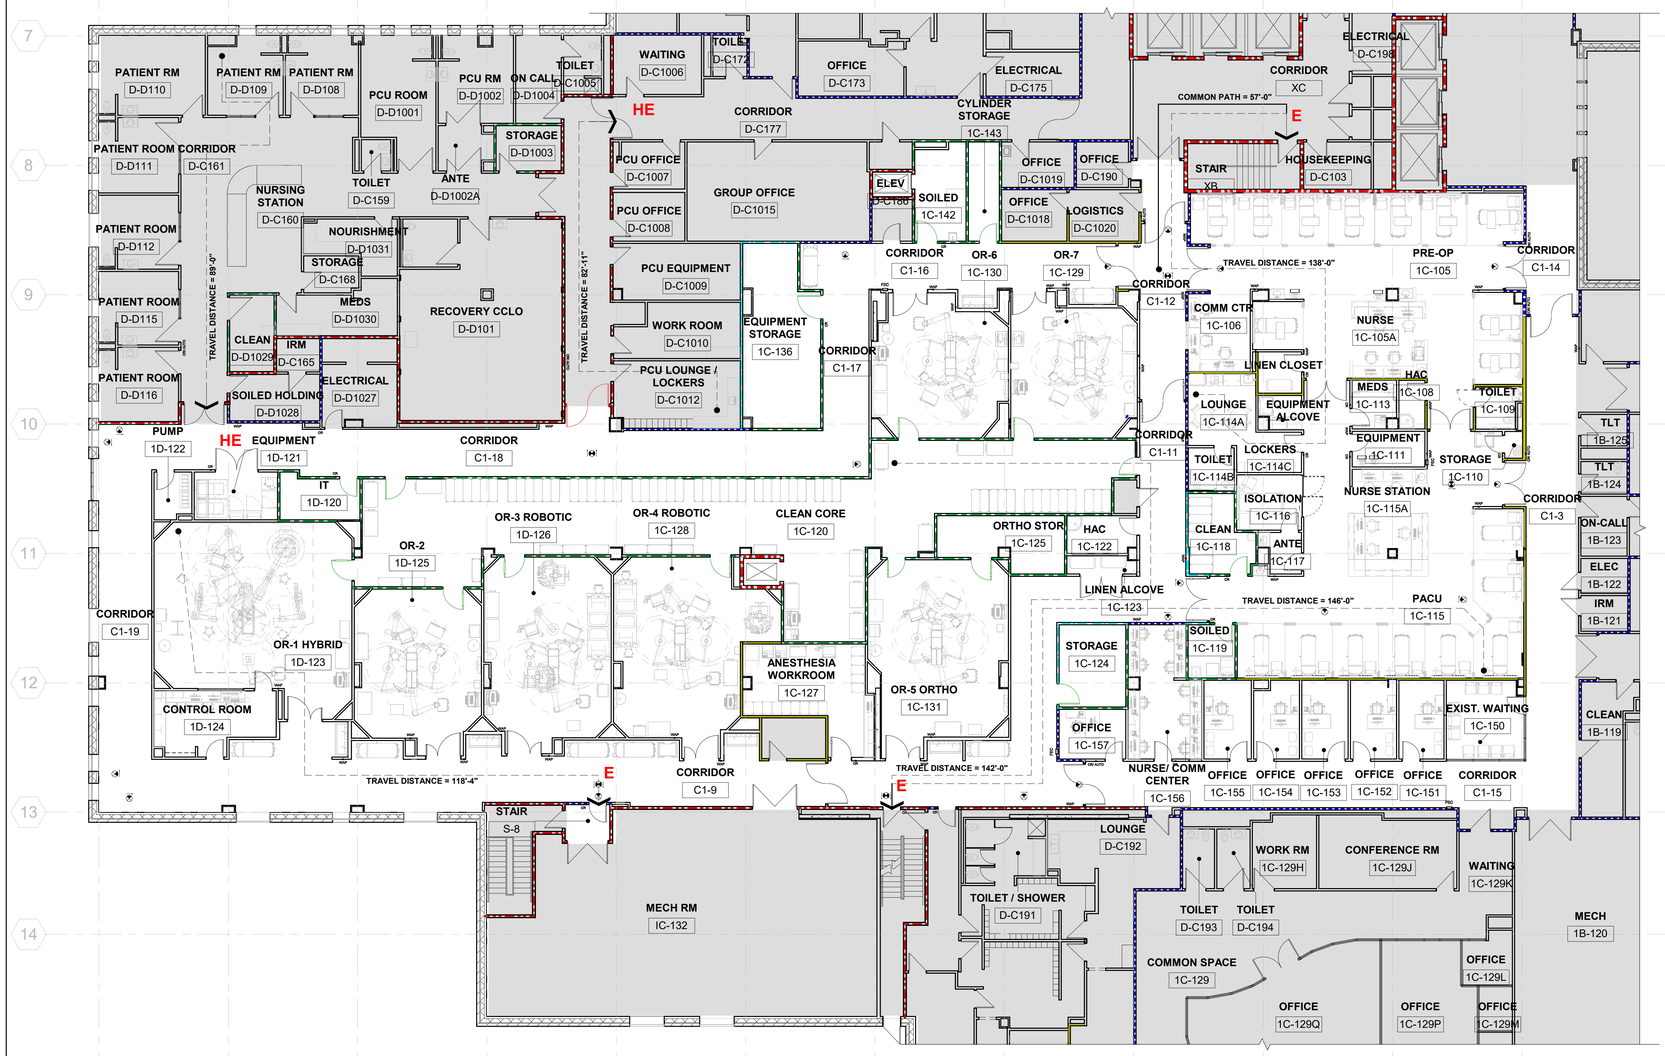

WALL LEGEND

- SMOKE PARTITION
- 1 HR. FIRE BARRIER
- SMOKE BARRIER
- 1 HR FIRE BARRIER AND SMOKE BARRIER (BOTH WALL TYPES APPLY)
- 2 HR.FIRE BARRIER

LIFE SAFETY LEGEND

- HORIZONTAL EXIT — HE
  **HORIZONTAL EXIT LOCATIONS BASED ON RECORD DRAWINGS RECEIVED FROM VA
- REQUIRED EXIT — E
- TRAVEL DISTANCE — X' - X" MAX TRAVEL DISTANCE 200'
- COMMON PATH — X' - X" MAX TRAVEL DISTANCE 100'
- FIRE EXTINGUISHER CABINET — FEC
- EXIT SIGN
- ** SEE ELECTRICAL PLANS FOR EXIT SIGN ORIENTATION**

1 FIRST FLOOR PLAN - LIFE SAFETY

SCALE: 3/32" = 1'-0"

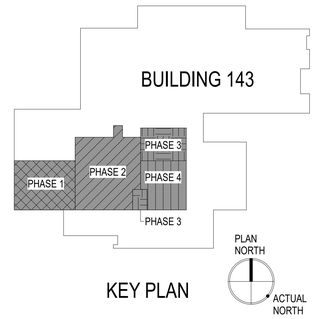

KEY PLAN

PRINTS OF THIS DRAWING SHALL NOT BE USED FOR ANY PURPOSE WHATSOEVER WITHOUT THE SEAL AND SIGNATURE OF THE PROFESSIONAL ENGINEER

Revisions:	Date:

CONSULTANT

Architecture:	Civil Engineering:	Fire Protection:
PF&A DESIGN, P.C.	LABELLA ASSOCIATES	STANTON ENGINEERING SERVICES, LLC

ENGINEER OF RECORD

MILLER•REMICK
A Service-Disabled Veteran-Owned Small Business
(856) 429-4000 • Miller-Remick.com
M-R PROJECT NO. 04/09-0136

PF&A DESIGN, P.C. REGISTERED ARCHITECT

COMMONWEALTH OF VIRGINIA — JOSEPH D. PRICE — NO. 7843 — 2025-12-50

Office of Construction and Facilities Management

U.S. Department of Veterans Affairs

Drawing Title GENERAL INFORMATION LIFE SAFETY PLAN FIRST FLOOR - OVERALL	**Phase** BID DOCUMENTS	**Project Title** RENOVATE SURGICAL SUITE PHASE II	**VA Drawing Number** 2617
Approved by: Jon Manninen, COR	FULLY SPRINKLERED	**Project Number** 658-19-103	**Building Number** 143
		Location SALEM VA MEDICAL CENTER	**Drawing Number** GI003
		Issue Date 2025-12-30 / **Checked** DJP / **Drawn** MAT / SKC	

VA FORM 08 - 6231

12/29/2025 1:41:35 AM

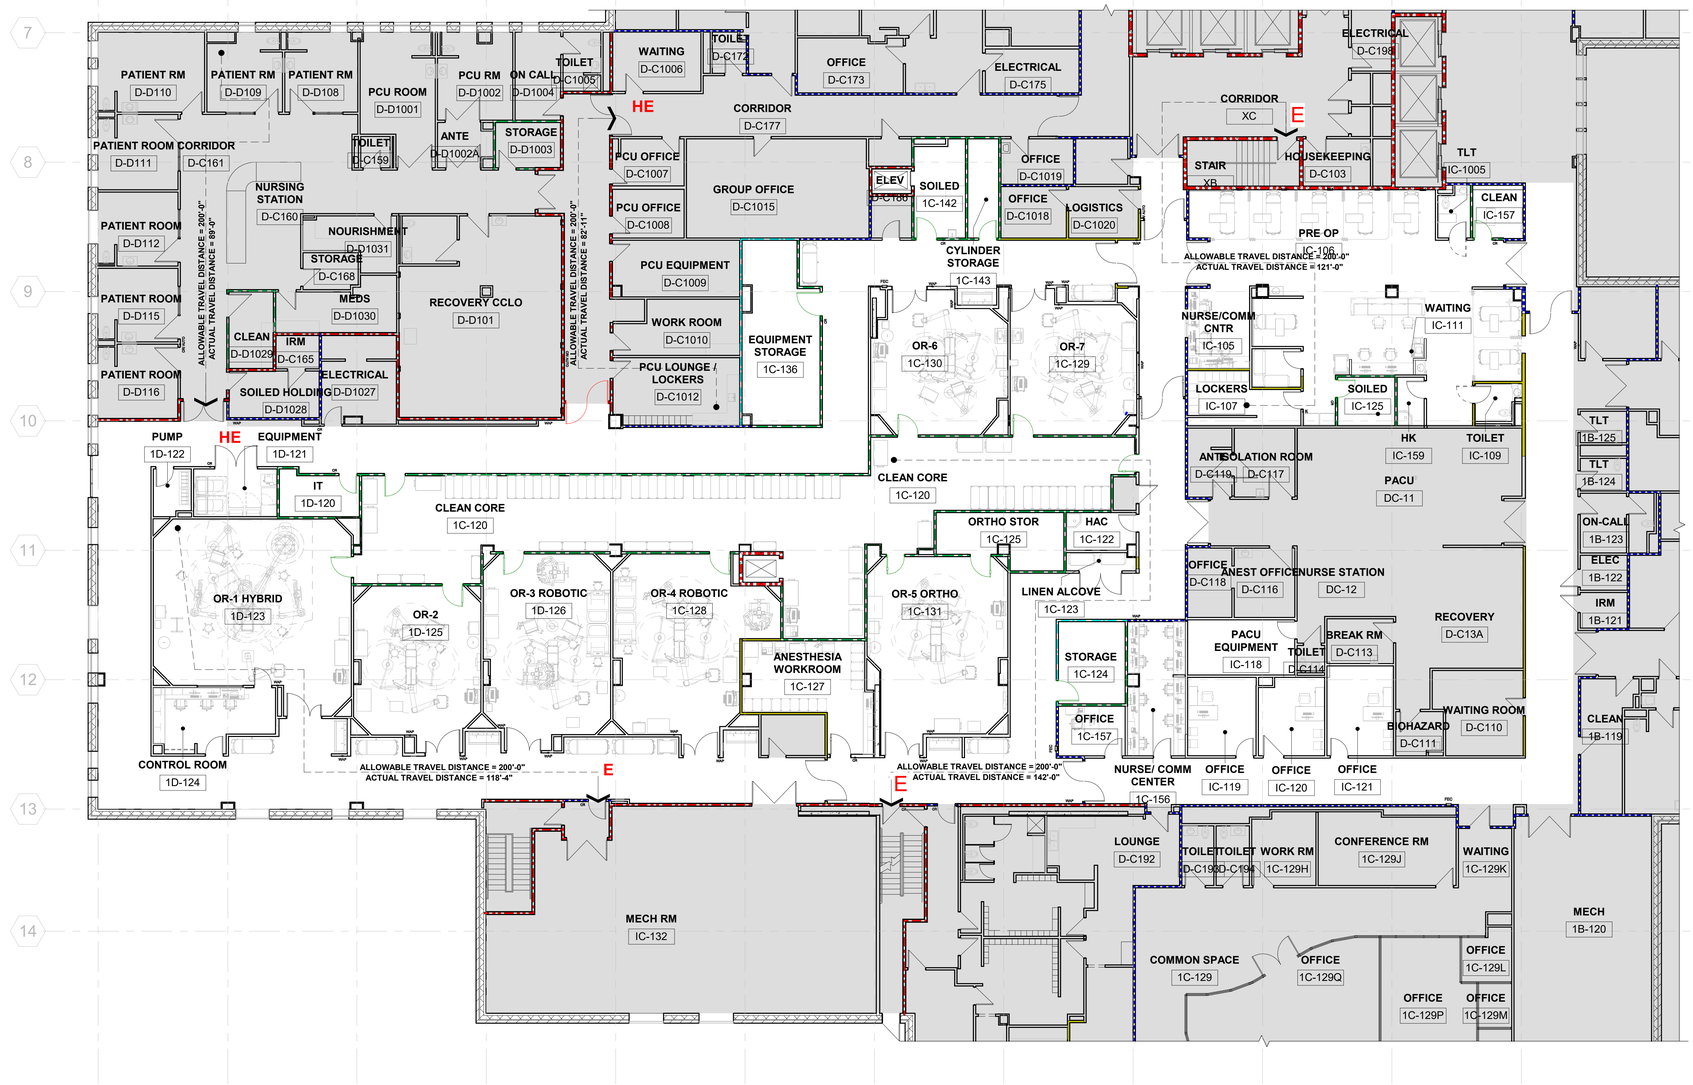

1 FIRST FLOOR PLAN - LIFE SAFETY - BID DEDUCT

SCALE: 3/32" = 1'-0"

WALL LEGEND

- SMOKE PARTITION
- 1 HR. FIRE BARRIER
- SMOKE BARRIER
- 1 HR FIRE BARRIER AND SMOKE BARRIER (BOTH WALL TYPES APPLY)
- 2 HR.FIRE BARRIER

LIFE SAFETY LEGEND

HORIZONTAL EXIT — HE

**HORIZONTAL EXIT LOCATIONS BASED ON RECORD DRAWINGS RECEIVED FROM VA

REQUIRED EXIT — E

TRAVEL DISTANCE — X' - X" / MAX TRAVEL DISTANCE 200'

COMMON PATH — X' - X" / MAX TRAVEL DISTANCE 100'

FIRE EXTINGUISHER CABINET — FEC

EXIT SIGN

** SEE ELECTRICAL PLANS FOR EXIT SIGN ORIENTATION**

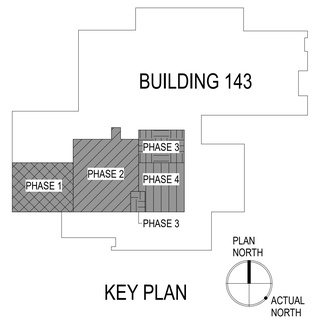

KEY PLAN

PRINTS OF THIS DRAWING SHALL NOT BE USED FOR ANY PURPOSE WHATSOEVER WITHOUT THE SEAL AND SIGNATURE OF THE PROFESSIONAL ENGINEER

Revisions: | Date:

CONSULTANT

Architecture:	Civil Engineering:	Fire Protection:
PF&A DESIGN, P.C.	LABELLA ASSOCIATES	STANTON ENGINEERING SERVICES, LLC

ENGINEER OF RECORD

MILLER•REMICK
A Service-Disabled Veteran-Owned Small Business
(856) 429-4000 • Miller-Remick.com
MR PROJECT NO. 0499-0138

PF&A DESIGN, P.C.
REGISTERED ARCHITECT
COMMONWEALTH OF VIRGINIA
JOSEPH M. PRESTI
No. 7843
2025-12-30
REGISTERED ARCHITECT

Office of Construction and Facilities Management

VA U.S. Department of Veterans Affairs

Drawing Title	GENERAL INFORMATION LIFE SAFETY PLAN - BID DEDUCT
Phase	BID DOCUMENTS
Approved by:	Jon Manninen, COR
	FULLY SPRINKLERED

Project Title	RENOVATE SURGICAL SUITE PHASE II		
Project Number	658-19-103		
Location	SALEM VA MEDICAL CENTER		
Issue Date	2025-12-30	Checked: DJP	Drawn: MAT / SKC

VA Drawing Number	2617
Building Number	143
Drawing Number	GI004

VA FORM 08 - 6231

02/28/2025 1:41:47 AM

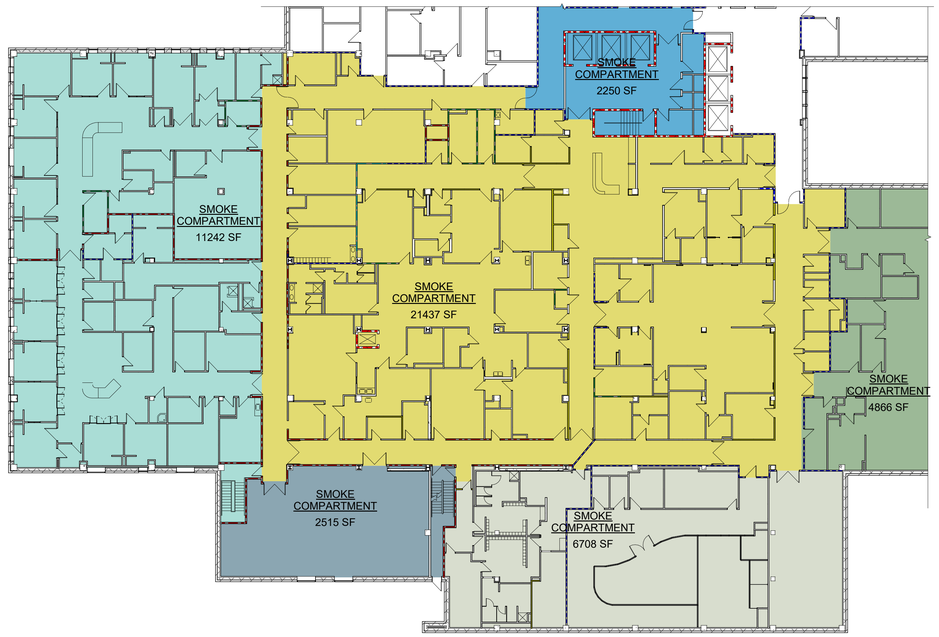

1 FIRST FLOOR EXISTING SMOKE COMPARTMENT PLANS
SCALE: 1" = 20'-0"

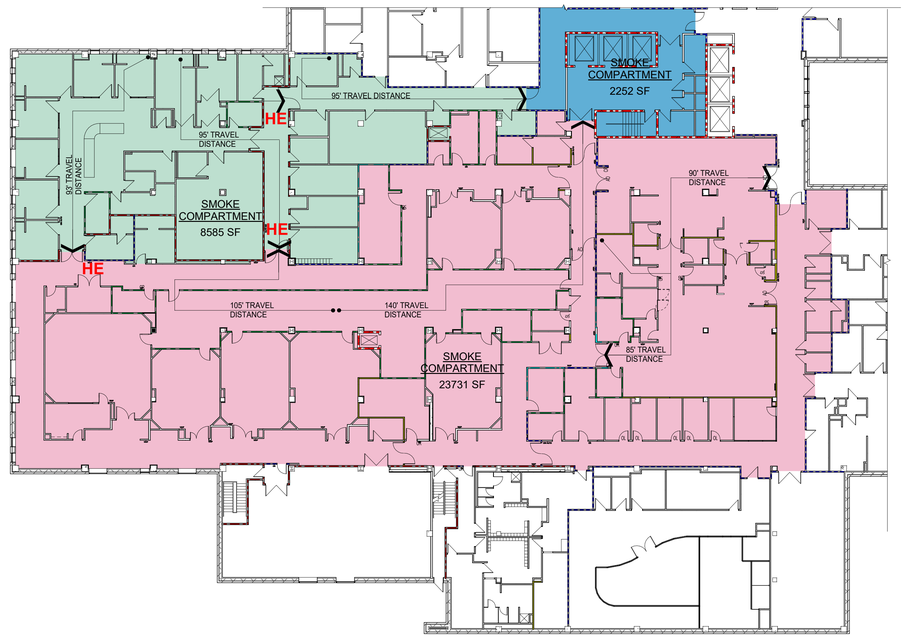

2 FIRST FLOOR NEW SMOKE COMPARTMENT PLAN
SCALE: 1" = 20'-0"

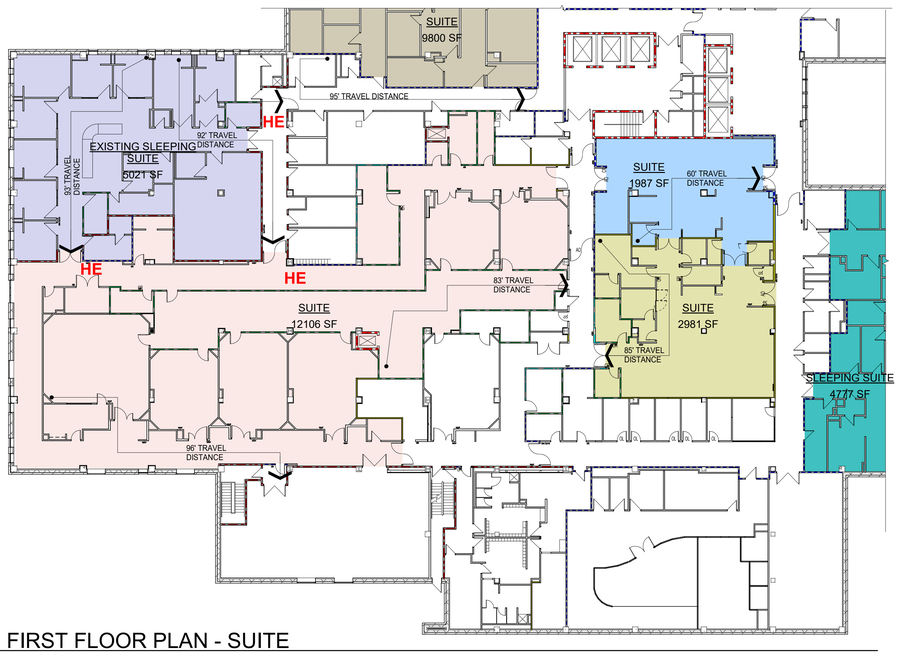

3 FIRST FLOOR PLAN - SUITE
SCALE: 1" = 20'-0"

SUITES INFORMATION

SUITES 18.2.5.7.1

SUITE SEPARATION SHALL BE CONSTRUCTED IN ACCORDANCE IN 18.3.6.2 - CORRIDOR WALLS.

PATIENT CARE NON SLEEPING SUITES MAXIMUM SIZE 12,500 SF. (18.2.5.7.3)

NON SLEEPING SUITES REQUIRE 2 EXIT ACCESS DOORS IF MORE THAN 2500 SF (18.2.5.7.3.2)

ONE MEANS OF EGRESS SHALL BE DIRECT TO A CORRIDOR OR AN EXIT STAIR.

ONE MEANS OF EGRESS SHALL BE PERMITTED TO BE INTO ANOTHER SUITE.

TRAVEL DISTANCE WITHIN A NON SLEEPING TO AN EXIT ACCESS SHALL NOT EXCEED 100 FEET (18.2.5.7.3.4A)

TRAVEL DISTANCE WITHIN A NON SLEEPING SUITE TO AN EXIT SHALL NOT EXCEED 200 FEET (18.2.5.7.3.4.B)

WALL LEGEND

- SMOKE PARTITION
- 1 HR. FIRE BARRIER
- SMOKE BARRIER
- 1 HR FIRE BARRIER AND SMOKE BARRIER (BOTH WALL TYPES APPLY)
- 2 HR.FIRE BARRIER

LIFE SAFETY LEGEND

- HORIZONTAL EXIT — HE
  **HORIZONTAL EXIT LOCATIONS BASED ON RECORD DRAWINGS RECEIVED FROM VA
- REQUIRED EXIT — E
- TRAVEL DISTANCE — X' - X" MAX TRAVEL DISTANCE 200'
- COMMON PATH — X' - X" MAX TRAVEL DISTANCE 100'
- FIRE EXTINGUISHER CABINET — FEC
- EXIT SIGN

** SEE ELECTRICAL PLANS FOR EXIT SIGN ORIENTATION**

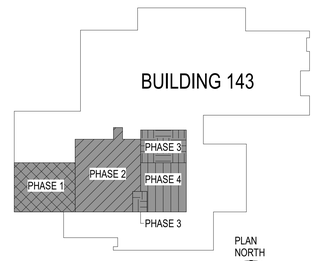

KEY PLAN
PLAN NORTH
ACTUAL NORTH

PRINTS OF THIS DRAWING SHALL NOT BE USED FOR ANY PURPOSE WHATSOEVER WITHOUT THE SEAL AND SIGNATURE OF THE PROFESSIONAL ENGINEER

Revisions:	Date:

CONSULTANT

Architecture:	Civil Engineering:	Fire Protection:
PF&A DESIGN, P.C.	LABELLA ASSOCIATES	STANTON ENGINEERING SERVICES, LLC

ENGINEER OF RECORD

MILLER•REMICK
A Service-Disabled Veteran-Owned Small Business
(856) 429-4000 ● Miller-Remick.com
M-R PROJECT NO. 0459-0130

PF&A DESIGN, P.C. REGISTERED ARCHITECT

COMMONWEALTH OF VIRGINIA
JOSEPH H. TROST
NO. 28463
2025-12-30
REGISTERED ARCHITECT

Office of Construction and Facilities Management

VA U.S. Department of Veterans Affairs

Drawing Title	GENERAL INFORMATION SMOKE COMPARTMENT & SUITE PLANS FIRST FLOOR
Approved by:	Jon Manninen, COR
Phase	BID DOCUMENTS
	FULLY SPRINKLERED
Project Title	RENOVATE SURGICAL SUITE PHASE II
Project Number	658-19-103
Location	SALEM VA MEDICAL CENTER
Issue Date	2025-12-30
Checked	DJP
Drawn	MAT / SKC
VA Drawing Number	2617
Building Number	143
Drawing Number	GI005

VA FORM 08 - 6231

12/29/2025 1:41:53 AM

OCCUPANT LOAD LEGEND

- (MES) MECHANICAL, ELECTRICAL AND STORAGE
- AMBULATORY HEALTHCARE
- UNCONCENTRATED ASSEMBLY

1 FIRST FLOOR PLAN - OCCUPANT LOAD
SCALE: 3/32" = 1'-0"

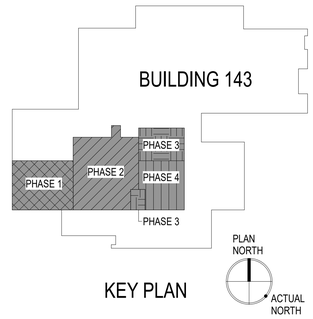

KEY PLAN

PRINTS OF THIS DRAWING SHALL NOT BE USED FOR ANY PURPOSE WHATSOEVER WITHOUT THE SEAL AND SIGNATURE OF THE PROFESSIONAL ENGINEER

Revisions: | Date:

CONSULTANT

Architecture:	Civil Engineering:	Fire Protection:
PF&A DESIGN, P.C.	LABELLA ASSOCIATES	STANTON ENGINEERING SERVICES, LLC

ENGINEER OF RECORD

MILLER•REMICK
A Service-Disabled Veteran-Owned Small Business
(856) 429-4000 ▪ Miller-Remick.com
M-R PROJECT NO: 0499-0136

PF&A DESIGN, P.C.
REGISTERED ARCHITECT
COMMONWEALTH OF VIRGINIA
JOSEPH H. TROST
NO. 7843
2025-12-30
ARCHITECT

Office of Construction and Facilities Management

VA U.S. Department of Veterans Affairs

Drawing Title: GENERAL INFORMATION
OCCUPANT LOAD PLAN
FIRST FLOOR

Approved by: Jon Manninen, COR

Phase: BID DOCUMENTS

FULLY SPRINKLERED

Project Title: RENOVATE SURGICAL SUITE
PHASE II
Project Number: 658-19-103

Location: SALEM VA MEDICAL CENTER

Issue Date: 2025-12-30 | Checked: DJP | Drawn: MAT / SKC

VA Drawing Number: 2617
Building Number: 143
Drawing Number: GI006

12/29/2025 1:41:55 AM

VA FORM 08 - 6231

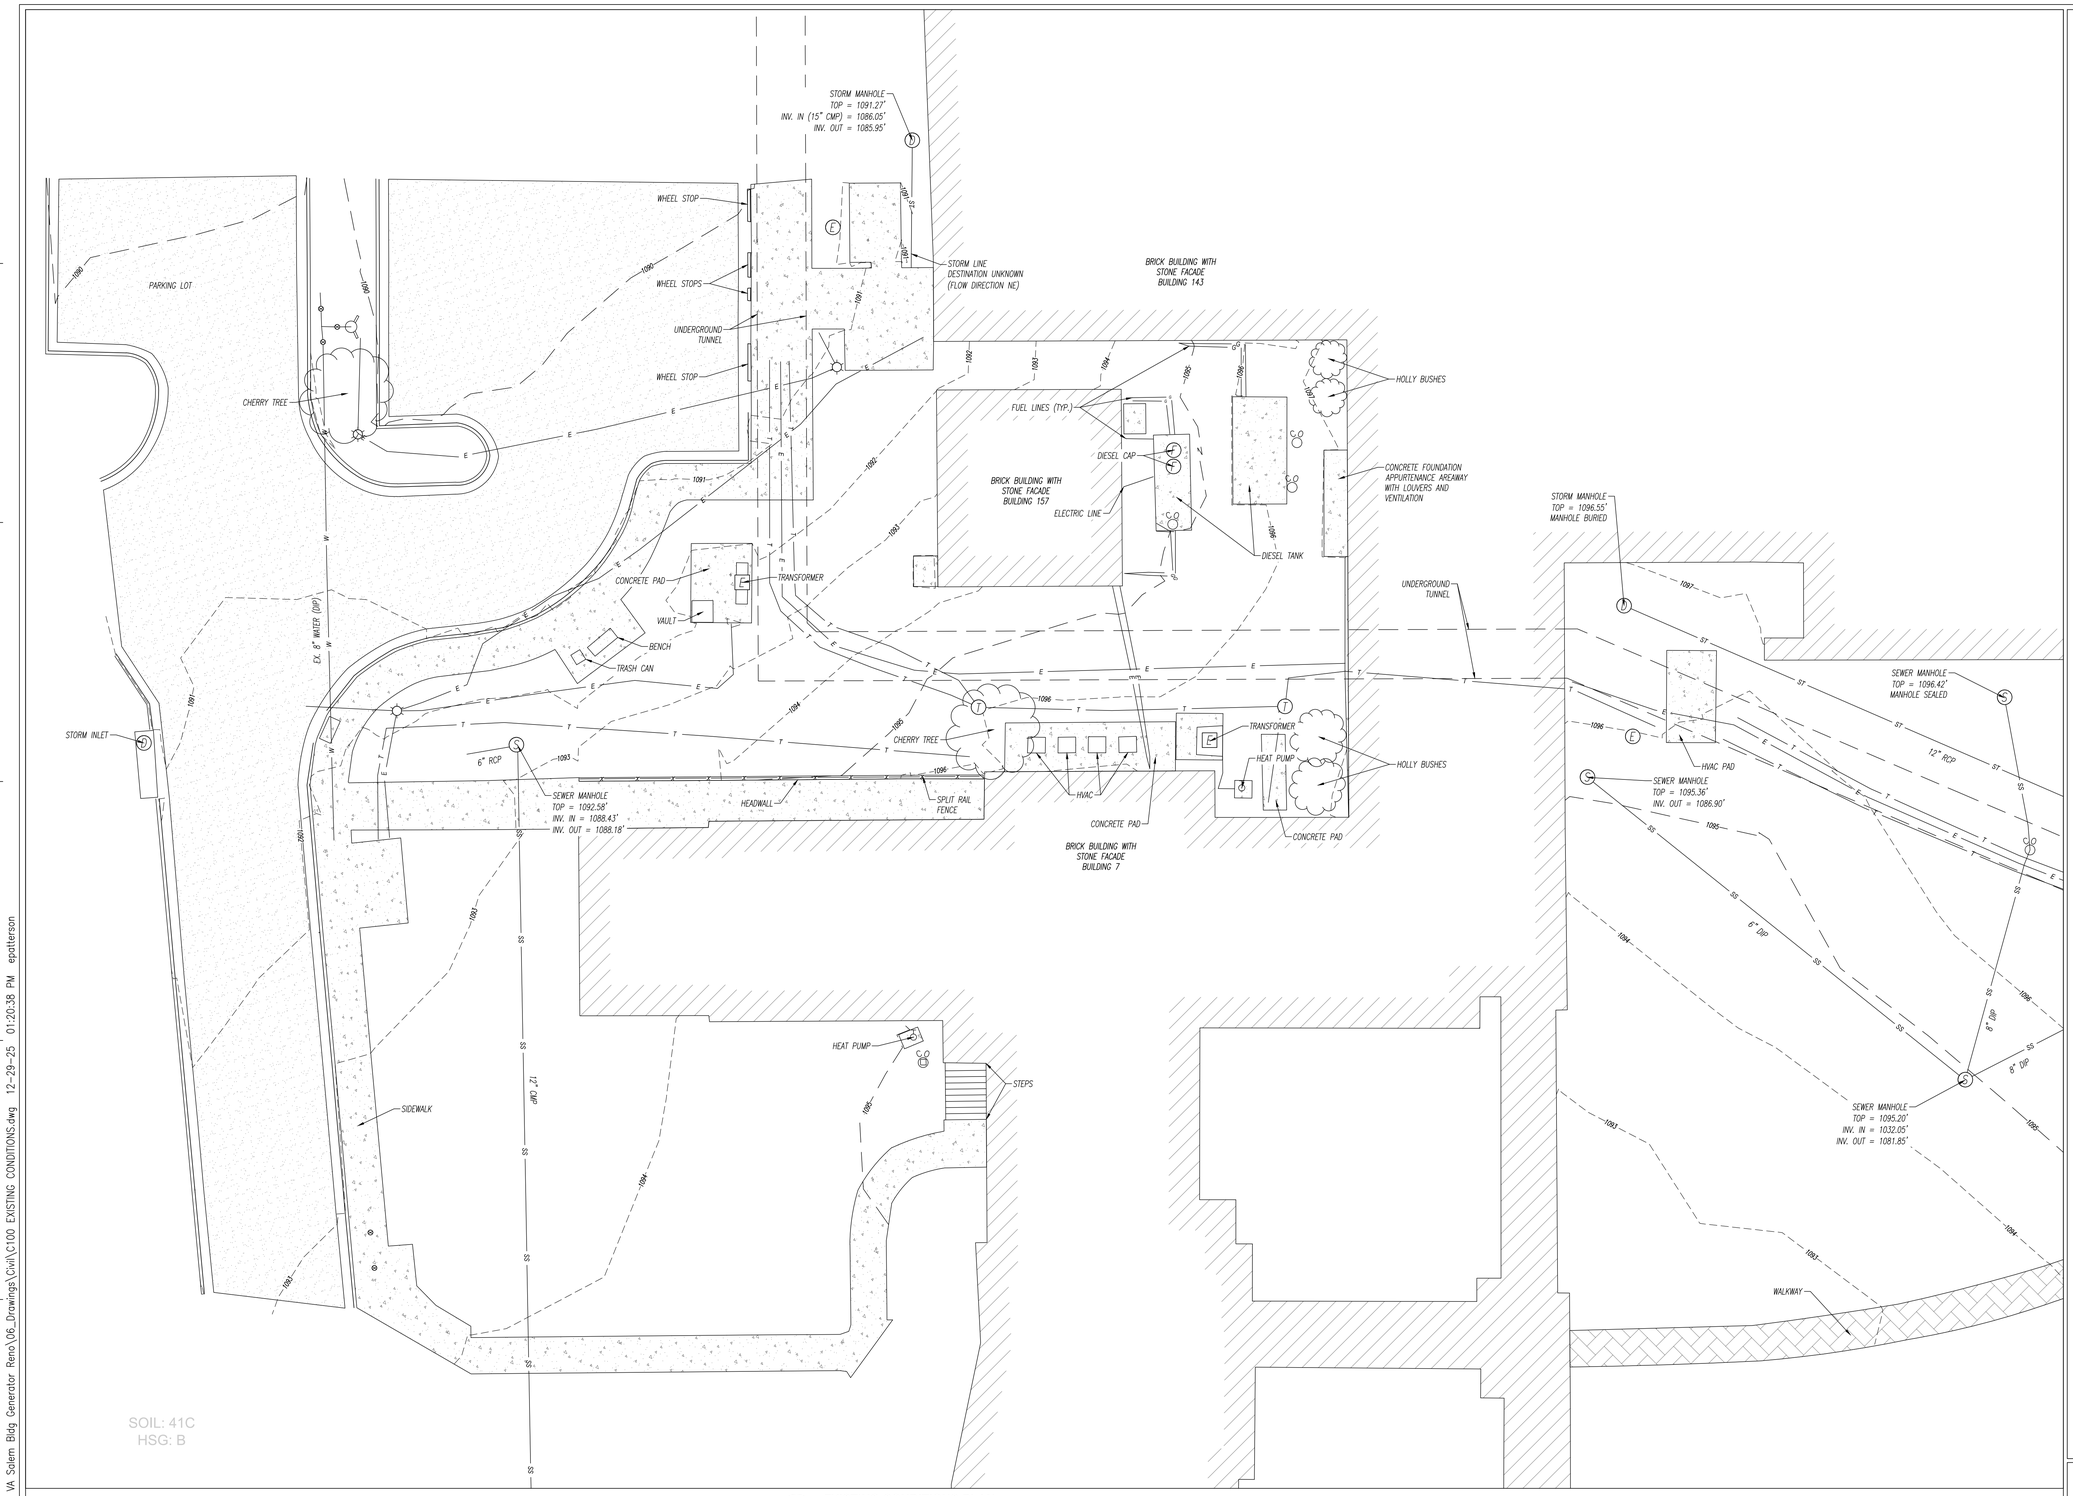

1 C-100 EXISTING CONDITIONS PLAN

SCALE: 1" = 10'

LEGEND

EXISTING CONDITIONS:

- PROPERTY LINE NO PHYSICAL BOUNDS
- ADJACENT PROPERTY LINE
- EXISTING MAJOR CONTOUR
- EXISTING MINOR CONTOUR
- EXISTING BUILDING
- EXISTING CONCRETE
- EXISTING WALKWAY
- EXISTING ASPHALT
- EXISTING CURB
- EXISTING FENCE
- EXISTING WATER LINE
- EXISTING GAS LINE
- EXISTING UNDERGROUND ELECTRIC LINE
- EXISTING UNDERGROUND COMMUNICATIONS LINE
- EXISTING UNDERGROUND SEWER LINE (8"SW)
- EXISTING UNDERGROUND STORM LINE (15"RCP)

SYMBOLS:

- EXISTING SANITARY MANHOLE
- EXISTING CLEANOUT/VENT
- EXISTING DRAINAGE MANHOLE
- EXISTING CATCH BASIN
- EXISTING ELECTRIC MANHOLE
- EXISTING ELECTRIC TRANSFORMER
- EXISTING LIGHT POLE
- EXISTING AIR CONDITION COMPRESSOR
- EXISTING HYDRANT
- EXISTING WATER VALVE
- EXISTING TELEPHONE MANHOLE
- EXISTING HEAT PUMP

EXISTING CONDITIONS AS SHOWN BY FIELD SURVEY COMPLETED BY ACCUPOINT SURVEYING & DESIGN, LLC DATED 10/07/2025. SUBSURFACE RADAR SURVEY COMPLETED BY AMERIMARK LOCATE DATED 10/06/2025.

0' 10' 20' 30'

SCALE 1" = 10'

PLAN NORTH

ACTUAL NORTH

PRINTS OF THIS DRAWING SHALL NOT BE USED FOR ANY PURPOSE WHATSOEVER WITHOUT THE SEAL AND SIGNATURE OF THE PROFESSIONAL ENGINEER.

NO.	DESCRIPTION	DATE

CONSULTANTS

Architecture:	Civil Engineering:	Fire & Life Safety:
PF&A DESIGN, P.C.	LABELLA ASSOCIATES	STANTON ENGINEERING SERVICES, LLC

ENGINEER OF RECORD

MILLER•REMICK

A Service-Disabled Veteran-Owned Small Business

(856) 429-4000 ★ Miller-Remick.com

M-R PROJECT NO: 0499-0136

LABELLA ASSOCIATES
PROFESSIONAL ENGINEER

COMMONWEALTH OF VIRGINIA
JARED J. PAPPELLA
No. 063378
PROFESSIONAL ENGINEER

12/30/2025

Office of Construction and Facilities Management

VA U.S. Department of Veterans Affairs

Drawing Title: CIVIL EXISTING CONDITIONS	Phase: BID DOCUMENTS
Approved by: Jon Manninen, COR	FULLY SPRINKLERED

Project Title: RENOVATE SURGICAL SUITE PHASE II		VA Drawing Number: 2617
Project Number: 658-19-103		Building Number: 143
Location: SALEM VA MEDICAL CENTER		Drawing Number: C-100
Issue Date: 2025-12-30	Checked: JJP	Drawn: EBP

VA FORM 08-6231

B:\GLOBAL\Projects\Miller-Remick\22548877 - VA Salem Bldg Generator Reno\06_Drawings\Civil\C100 EXISTING CONDITIONS.dwg 12-29-25 01:20:38 PM epatterson

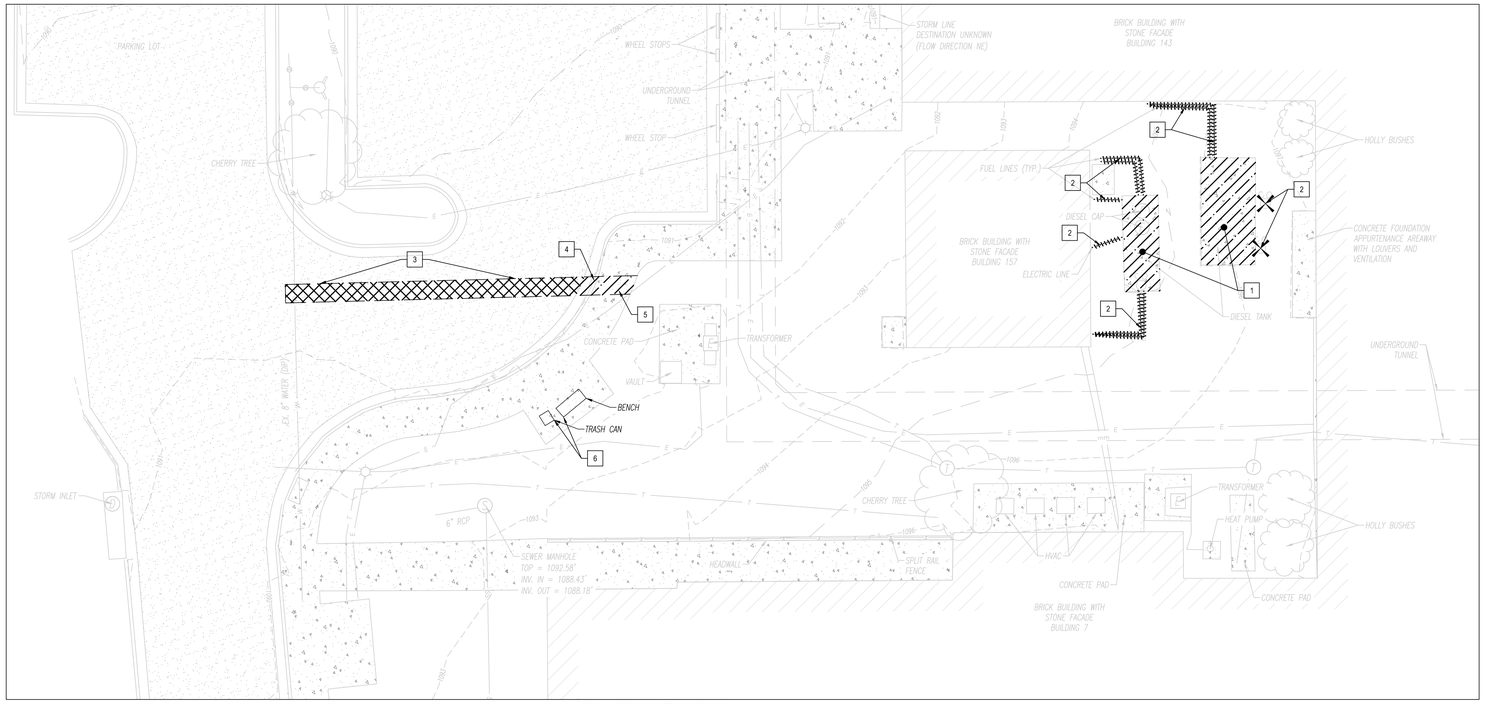

1 C-110 **DEMOLITION PLAN**

SCALE: 1" = 10'

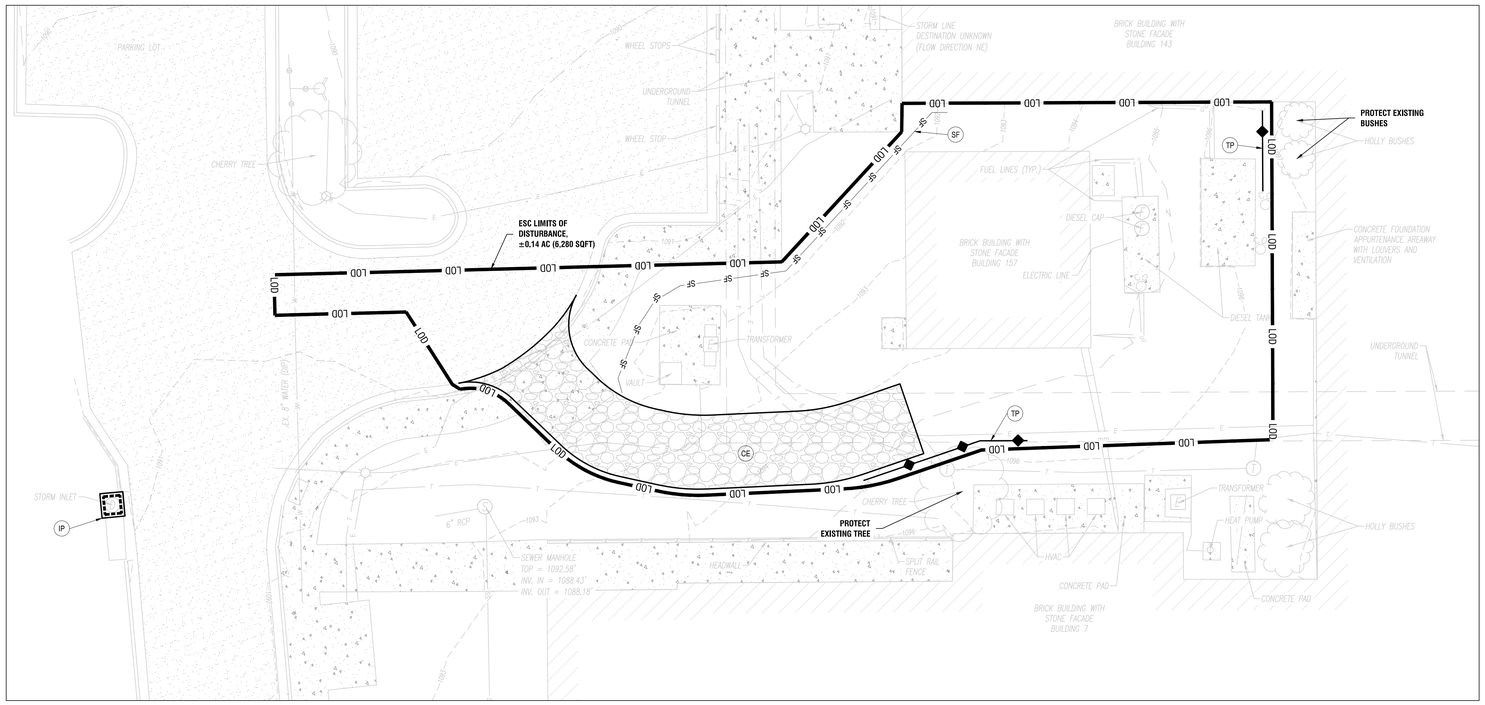

2 C-110 **EROSION CONTROL PLAN**

SCALE: 1" = 10'

DEMOLITION KEY NOTES & LEGEND

1. REMOVE AND DISPOSE OF EXISTING CONCRETE SLABS AND UNDERGROUND FUEL TANKS. IN THE EVENT OF A SUPPOSED LEAK OR FUEL DISCHARGE, NOTIFY PROJECT ENVIRONMENTAL INSPECTOR IMMEDIATELY.
2. REMOVE AND DISPOSE OF ASSOCIATED UNDERGROUND PIPING, VENTS, AND ELECTRICAL LINES.
3. FULL-DEPTH ASPHALT SAWCUT LIMITS. REMOVE AND DISPOSE OF EXISTING ASPHALT PAVEMENT.
4. REMOVE AND DISPOSE OF EXISTING CONCRETE CURB AND GUTTER AT NEAREST JOINT LINES.
5. REMOVE AND DISPOSE OF EXISTING CONCRETE SIDEWALK AT NEAREST JOINT LINES. SAWCUT AT CRACK CONTROL LINES IF NECESSARY.
6. SALVAGE AND PROTECT EXISTING TRASH CAN AND BENCH AND RETURN TO OWNER. REPLACE AT THE OWNER'S DISCRETION AFTER CONSTRUCTION IS COMPLETED.

LINETYPE/BLOCK	DESCRIPTION
×	EXISTING SITE FEATURE TO BE REMOVED
— — — —	APPROX. SAWCUT LIMITS
~~	REMOVE UNDERGROUND UTILITY
	REMOVE ASPHALT PAVEMENT MATERIAL
	REMOVE CONCRETE PAVEMENT MATERIAL

EROSION CONTROL LEGEND

LINETYPE/BLOCK		DESCRIPTION
LOD	LOD	LIMITS OF DISTURBANCE
SF SF	SF	SILT FENCE
	TP	TREE PROTECTION FENCE
	IP	INLET PROTECTION
	CE	TEMPORARY CONSTRUCTION ENTRANCE

0' 10' 20' 30'

SCALE 1" = 10'

PLAN NORTH

ACTUAL NORTH

PRINTS OF THIS DRAWING SHALL NOT BE USED FOR ANY PURPOSE WHATSOEVER WITHOUT THE SEAL AND SIGNATURE OF THE PROFESSIONAL ENGINEER.

NO.	DESCRIPTION	DATE

CONSULTANTS

Architecture:	Civil Engineering:	Fire & Life Safety:
PF&A DESIGN, P.C.	LABELLA ASSOCIATES	STANTON ENGINEERING SERVICES, LLC

ENGINEER OF RECORD

MILLER•REMICK

A Service-Disabled Veteran-Owned Small Business

(856) 429-6000 • Miller-Remick.com

M–R PROJECT NO: 0499–0136

LABELLA ASSOCIATES PROFESSIONAL ENGINEER

COMMONWEALTH OF VIRGINIA JARED J. PAPARELLA Lic. No. 043378 PROFESSIONAL ENGINEER

12/30/2025

Office of Construction and Facilities Management

VA U.S. Department of Veterans Affairs

Drawing Title	CIVIL DEMOLITION & EROSION CONTROL PLANS
Approved by:	Jon Manninen, COR
Phase	BID DOCUMENTS
	FULLY SPRINKLERED
Project Title	RENOVATE SURGICAL SUITE PHASE II
Project Number	658-19-103
Location	SALEM VA MEDICAL CENTER
Issue Date	2025-12-30
Checked	JJP
Drawn	EBP
VA Drawing Number	2617
Building Number	143
Drawing Number	C-110

VA FORM 08-6231

B:\GLOBAL\Projects\Miller-Remick\2254877 – VA Salem Bldg Generator Reno\06_Drawings\Civil\C110 DEMO PLAN.dwg 12-29-25 01:20:39 PM epatterson

three inches = one foot; one and one half inches = one foot; one inch = one foot; three quarters inch = one foot; one half inch = one foot; three eighths inch = one foot; one quarter inch = one foot; one eighth inch = one foot

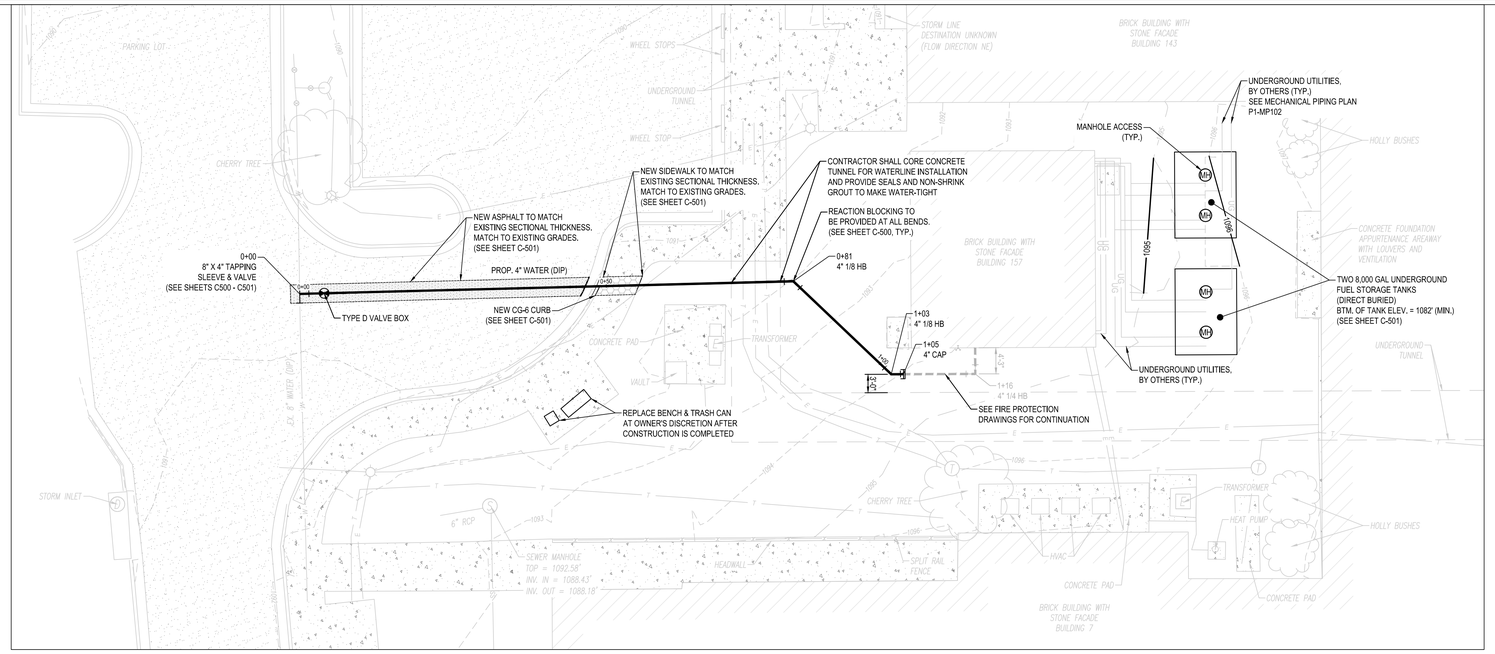

1 C-200 SITE LAYOUT PLAN
SCALE: 1" = 10'

2 C-200 WATERLINE PROFILE
SCALE: H: 1" = 20'
V: 1" = 2'

LEGEND

EXISTING	PROPOSED	DESCRIPTION
		SUBJECT PROPERTY LINE
		ADJACENT PROPERTY LINE
1090	1090	MAJOR CONTOUR
1089	1089	MINOR CONTOUR
		BUILDING
		CONCRETE PAVEMENT
		WALKWAY
		ASPHALT PAVEMENT
		CURB
X X		FENCE
W		WATERLINE
		WATERLINE, BY OTHERS
G		GAS LINE
E		U/G ELECTRIC LINE
T		U/G COMMUNICATIONS LINE
SS 8"SN		U/G SEWER LINE
ST 15"RCP		U/G STORM LINE
	UG	U/G UTILITY LINE, BY OTHERS
		SANITARY MANHOLE
		CLEANOUT/VENT
		DRAINAGE MANHOLE
		CATCH BASIN
		ELECTRIC MANHOLE
		ELECTRIC TRANSFORMER
		LIGHT POLE
		AIR CONDITION COMPRESSOR
		HYDRANT
		WATER VALVE
		TELEPHONE MANHOLE
		HEAT PUMP
		TANK ACCESS MANHOLE
		FIRE DEPARTMENT CONNECTION
		WATER LINE CAP

SITE PLAN NOTES:

1. CONTRACTOR SHALL TEST PIT FOR EXISTING UTILITIES PRIOR TO CONSTRUCTION.
2. SEE SHEETS C-500 - C-501 FOR SITE DETAILS.

0' 10' 20' 30'
SCALE 1" = 10'

PLAN NORTH
ACTUAL NORTH

PRINTS OF THIS DRAWING SHALL NOT BE USED FOR ANY PURPOSE WHATSOEVER WITHOUT THE SEAL AND SIGNATURE OF THE PROFESSIONAL ENGINEER.

NO.	DESCRIPTION	DATE

CONSULTANTS

Architecture:	Civil Engineering:	Fire & Life Safety:
PF&A DESIGN, P.C.	LABELLA ASSOCIATES	STANTON ENGINEERING SERVICES, LLC

ENGINEER OF RECORD

MILLER•REMICK
A Service-Disabled Veteran-Owned Small Business
(856) 429-6000 • Miller-Remick.com
M–R PROJECT NO: 0499–0136

LABELLA ASSOCIATES PROFESSIONAL ENGINEER
COMMONWEALTH OF VIRGINIA
JARED J. PAGNELLA
No. 061328
PROFESSIONAL ENGINEER
12/30/2025

Office of Construction and Facilities Management

VA U.S. Department of Veterans Affairs

Drawing Title	CIVIL SITE LAYOUT & WATERLINE PROFILE
Approved by:	Jon Manninen, COR
Phase	BID DOCUMENTS
	FULLY SPRINKLERED
Project Title	RENOVATE SURGICAL SUITE PHASE II
Project Number	658-19-103
Location	SALEM VA MEDICAL CENTER
Issue Date	2025-12-30
Checked	JJP
Drawn	EBP
VA Drawing Number	2617
Building Number	143
Drawing Number	C-200

VA FORM 08-6231

B:\GLOBAL\Projects\Miller-Remick\2254877 – VA Salem Bldg Generator Reno\06_Drawings\Civil\C200 SITE PLAN.dwg 12-29-25 01:20:40 PM epotterson

EROSION & SEDIMENT CONTROL MINIMUM STANDARDS

MS-1 PERMANENT OR TEMPORARY SOIL STABILIZATION SHALL BE APPLIED TO DENUDED AREAS WITHIN SEVEN DAYS AFTER FINAL GRADE IS REACHED ON ANY PORTION OF THE SITE. TEMPORARY SOIL STABILIZATION SHALL BE APPLIED WITHIN SEVEN DAYS TO DENUDED AREAS THAT MAY NOT BE AT FINAL GRADE BUT WILL REMAIN DORMANT FOR LONGER THAN 14 DAYS. PERMANENT STABILIZATION SHALL BE APPLIED TO AREAS THAT ARE TO BE LEFT DORMANT FOR MORE THAN ONE YEAR.
TEMPORARY AND PERMANENT SEEDING ARE REQUIRED FOR THIS PROJECT AND ARE SHOWN ON THE PLANS.

MS-2 DURING CONSTRUCTION OF THE PROJECT, SOIL STOCK PILES AND BORROW AREAS SHALL BE STABILIZED OR PROTECTED WITH SEDIMENT TRAPPING MEASURES. THE APPLICANT IS RESPONSIBLE FOR THE TEMPORARY PROTECTION AND PERMANENT STABILIZATION OF ALL SOIL STOCKPILES ON SITE AS WELL AS BORROW AREAS AND SOIL INTENTIONALLY TRANSPORTED FROM THE PROJECT SITE.
STABILIZE WITH TEMPORARY SEEDING & ENCLOSE BORROW OR STOCKPILE AREAS WITH SILT FENCE.

MS-3 A PERMANENT VEGETATIVE COVER SHALL BE ESTABLISHED ON DENUDED AREAS NOT OTHERWISE PERMANENTLY STABILIZED. PERMANENT VEGETATION SHALL NOT BE CONSIDERED ESTABLISHED UNTIL A GROUND COVER IS ACHIEVED THAT IS UNIFORM, MATURE ENOUGH TO SURVIVE AND WILL INHIBIT EROSION.
ADEQUATE SYMBOLS, DETAILS, AND NOTES ARE PROVIDED ON THE PLAN FOR DIRECTION.

MS-4 SEDIMENT BASINS AND TRAPS, PERIMETER DIKES, SEDIMENT BARRIERS AND OTHER MEASURES INTENDED TO TRAP SEDIMENT SHALL BE CONSTRUCTED AS A FIRST STEP IN ANY LAND-DISTURBING ACTIVITY AND SHALL BE MADE FUNCTIONAL BEFORE UP-SLOPE LAND DISTURBANCE TAKES PLACE.
PERIMETER SILT FENCE AND 2 SEDIMENT TRAPS ARE SHOWN ON THE PLAN AND SHALL BE INSTALLED PRIOR TO ANY ADDITIONAL GRADING.

MS-5 STABILIZATION MEASURES SHALL BE APPLIED TO EARTHEN STRUCTURES SUCH AS DAMS, DIKES AND DIVERSIONS IMMEDIATELY AFTER INSTALLATION.
APPLY SEEDING TO DAM SECTION IMMEDIATELY AFTER CONSTRUCTION.

MS-6 SEDIMENT TRAPS AND SEDIMENT BASINS SHALL BE DESIGNED AND CONSTRUCTED BASED UPON THE TOTAL DRAINAGE AREA TO BE SERVED BY THE TRAP OR BASIN. THE MINIMUM STORAGE CAPACITY OF A SEDIMENT TRAP SHALL BE 134 CUBIC YARDS PER ACRE OF DRAINAGE AREA AND THE TRAP SHALL ONLY CONTROL DRAINAGE AREAS LESS THAN THREE ACRES. SURFACE RUNOFF FROM DISTURBED AREAS THAT IS COMPRISED OF FLOW FROM DRAINAGE AREAS GREATER THAN OR EQUAL TO THREE ACRES SHALL BE CONTROLLED BY A SEDIMENT BASIN. THE MINIMUM STORAGE CAPACITY OF A SEDIMENT BASIN SHALL BE 134 CUBIC YARDS PER ACRE OF DRAINAGE AREA. THE OUTFALL SYSTEM SHALL AT A MINIMUM, MAINTAIN THE STRUCTURAL INTEGRITY OF THE BASIN DURING A 25-YEAR STORM OF 24-HOUR DURATION. RUNOFF COEFFICIENTS USED IN RUNOFF CALCULATIONS SHALL CORRESPOND TO A BARE EARTH CONDITION OR THOSE CONDITIONS EXPECTED TO EXIST WHILE THE SEDIMENT BASIN IS UTILIZED.
INSTALL SEDIMENT TRAPS PRIOR TO ANY ADDITIONAL GRUBBING OR LAND DISTURBANCE.

MS-7 CUT- AND FILL-SLOPES SHALL BE DESIGNED AND CONSTRUCTED IN A MANNER THAT WILL MINIMIZE EROSION. SLOPES THAT ARE FOUND TO BE ERODING EXCESSIVELY WITHIN ONE-YEAR OF PERMANENT STABILIZATION SHALL BE PROVIDED WITH ADDITIONAL SLOPE STABILIZING MEASURES UNTIL THE PROBLEM IS CORRECTED.
SLOPE STABILIZING MEASURES ARE DETAILED FOR USE THE PLANS, SPECIFICALLY BLANKET MATTING SHALL BE APPLIED TO ALL SLOPES 2:1 OR STEEPER.

MS-8 CONCENTRATED RUNOFF SHALL NOT FLOW DOWN CUT- OR FILL-SLOPES UNLESS CONTAINED WITHIN AN ADEQUATE TEMPORARY OR PERMANENT CHANNEL, FLUME OR SLOPE DRAIN STRUCTURE.
ALL CONCENTRATED RUNOFF FROM THIS RE-DEVELOPMENT AREA SHALL BE DIRECTED IN THE PROPOSED STORM WATER MANAGEMENT FACILITIES AND CONVEYED INTO THE EXISTING BMP, AS IF A NATURAL CHANNEL; THE EXISTING CONTROLLING RELEASE STRUCTURE, RISER AND DETENTION SYSTEM LOCATED AT THE EXISTING SITE OUTFALL IS TO REMAIN UNCHANGED.

MS-9 WHENEVER WATER SEEPS FROM A SLOPE FACE, ADEQUATE DRAINAGE OR OTHER PROTECTION SHALL BE PROVIDED.
SHOULD THIS BECOME EVIDENT ONSITE, CONTRACTOR SHALL INSTALL RIP-RAP APRON TO CONVEY SEEPAGE DOWNGRADE TO THE EXISTING ROADWAY.

MS-10 ALL STORM SEWER INLETS THAT ARE MADE OPERABLE DURING CONSTRUCTION SHALL BE PROTECTED SO THAT SEDIMENT-LADEN WATER CANNOT ENTER THE CONVEYANCE SYSTEM WITHOUT FIRST BEING FILTERED OR OTHERWISE TREATED TO REMOVE SEDIMENT.
INLET & CULVERT INLET PROTECTION IS SHOWN ON THE PLANS FOR EXISTING INLETS AND SHALL BE ADDED TO EACH NEW INLET AS IT IS CONSTRUCTED. INLET & CULVERT PROTECTIONS SHALL BE ADDED TO ALL EXISTING INLETS & CULVERTS WITHIN THE PHASE 1 LOW DURING ESC PHASE 1 OPERATIONS.

MS-11 BEFORE NEWLY CONSTRUCTED STORMWATER CONVEYANCE CHANNELS OR PIPES ARE MADE OPERATIONAL, ADEQUATE OUTLET PROTECTION AND ANY REQUIRED TEMPORARY OR PERMANENT CHANNEL LINING SHALL BE INSTALLED IN BOTH THE CONVEYANCE CHANNEL AND RECEIVING CHANNEL.
THERE IS ONE PROPOSED STORMWATER CONVEYANCE CHANNEL TO ROUTE WATER THROUGH THE CURB CUT AND INTO RR POND #1. REFER TO ESC PHASE 3 (SHEET C404).

MS-12 WHEN WORK IN A LIVE WATERCOURSE IS PERFORMED, PRECAUTIONS SHALL BE TAKEN TO MINIMIZE ENCROACHMENT, CONTROL SEDIMENT TRANSPORT AND STABILIZE THE WORK AREA TO THE GREATEST EXTENT POSSIBLE DURING CONSTRUCTION. NON-ERODIBLE MATERIAL SHALL BE USED FOR THE CONSTRUCTION OF CAUSEWAYS AND COFFERDAMS. EARTHEN FILL MAY BE USED FOR THESE STRUCTURES IF ARMORED BY NON-ERODIBLE COVER MATERIALS.
NOT APPLICABLE.

MS-13 WHEN A LIVE WATERCOURSE MUST BE CROSSED BY CONSTRUCTION VEHICLES MORE THAN TWICE IN ANY SIX-MONTH PERIOD, A TEMPORARY VEHICULAR STREAM CROSSING CONSTRUCTED OF NON-ERODIBLE MATERIAL SHALL BE PROVIDED.
NOT APPLICABLE.

MS-14 ALL APPLICABLE FEDERAL, STATE AND LOCAL REQUIREMENTS PERTAINING TO WORKING IN OR CROSSING LIVE WATERCOURSES SHALL BE MET.
NOT APPLICABLE.

MS-15 THE BED AND BANKS OF A WATERCOURSE SHALL BE STABILIZED IMMEDIATELY AFTER WORK IN THE WATERCOURSE IS COMPLETED.
NOT APPLICABLE.

MS-16 UNDERGROUND UTILITY LINES SHALL BE INSTALLED IN ACCORDANCE WITH THE FOLLOWING STANDARDS IN ADDITION TO OTHER APPLICABLE CRITERIA:
- a. NO MORE THAN 500 LINEAR FEET OF TRENCH MAY BE OPENED AT ONE TIME.
- b. EXCAVATED MATERIAL SHALL BE PLACED ON THE UPHILL SIDE OF TRENCHES.
- c. EFFLUENT FROM DEWATERING OPERATIONS SHALL BE FILTERED OR PASSED THROUGH AN APPROVED SEDIMENT TRAPPING DEVICE, OR BOTH, AND DISCHARGED IN A MANNER THAT DOES NOT ADVERSELY AFFECT FLOWING STREAMS OR OFF-SITE PROPERTY.
- d. MATERIAL USED FOR BACKFILLING TRENCHES SHALL BE PROPERLY COMPACTED IN ORDER TO MINIMIZE EROSION AND PROMOTE STABILIZATION.
- e. RESTABILIZATION SHALL BE ACCOMPLISHED IN ACCORDANCE WITH THIS CHAPTER.
- f. APPLICABLE SAFETY REQUIREMENTS SHALL BE COMPLIED WITH.

THIS APPLIES TO THE ALL PRIVATE UTILITIES, SANITARY SEWER, WATERLINE OR STORM SEWER PIPE INSTALLATIONS.

MS-17 WHERE CONSTRUCTION VEHICLE ACCESS ROUTES INTERSECT PAVED OR PUBLIC ROADS, PROVISIONS SHALL BE MADE TO MINIMIZE THE TRANSPORT OF SEDIMENT BY VEHICULAR TRACKING ONTO THE PAVED SURFACE. WHERE SEDIMENT IS TRANSPORTED ONTO A PAVED OR PUBLIC ROAD SURFACE, THE ROAD SURFACE SHALL BE CLEANED THOROUGHLY AT THE END OF EACH DAY. SEDIMENT SHALL BE REMOVED FROM THE ROADS BY SHOVELING OR SWEEPING AND TRANSPORTED TO A SEDIMENT CONTROL DISPOSAL AREA. STREET WASHING SHALL BE ALLOWED ONLY AFTER SEDIMENT IS REMOVED IN THIS MANNER. THIS PROVISION SHALL APPLY TO INDIVIDUAL DEVELOPMENT LOTS AS WELL AS TO LARGER LAND-DISTURBING ACTIVITIES.
THE TWO CONSTRUCTION ENTRANCES ARE LOCATED INTERNALLY WITHIN THE LOD AND DO NOT DIRECTLY INTERSECT WITH THE PUBLIC ROAD (OLD STAGE ROAD), CONTRACTOR SHALL KEEP THE ROADS FREE FROM SEDIMENT, DEBRIS AND MUD AT ALL TIMES DURING CONSTRUCTION.

MS-18 ALL TEMPORARY EROSION AND SEDIMENT CONTROL MEASURES SHALL BE REMOVED WITHIN 30-DAYS AFTER FINAL SITE STABILIZATION OR AFTER THE TEMPORARY MEASURES ARE NO LONGER NEEDED, UNLESS OTHERWISE AUTHORIZED BY THE VA ESCP AUTHORITY. TRAPPED SEDIMENT AND THE DISTURBED SOIL AREAS RESULTING FROM THE DISPOSITION OF TEMPORARY MEASURES SHALL BE PERMANENTLY STABILIZED TO PREVENT FURTHER EROSION AND SEDIMENTATION.
CONTRACTOR SHALL FOLLOW MS-18 ONCE FINAL GRADES ARE MET AND OBTAIN APPROVAL FROM ENVIRONMENTAL INSPECTOR.

MS-19 PROPERTIES AND WATERWAYS DOWNSTREAM FROM DEVELOPMENT SITES SHALL BE PROTECTED FROM SEDIMENT DEPOSITION, EROSION AND DAMAGE DUE TO INCREASES IN VOLUME, VELOCITY AND PEAK FLOW RATE OF STORMWATER RUNOFF FOR THE STATED FREQUENCY STORM OF 24-HOUR DURATION IN ACCORDANCE WITH THE FOLLOWING STANDARDS AND CRITERIA. STREAM RESTORATION AND RELOCATION PROJECTS THAT INCORPORATE NATURAL CHANNEL DESIGN CONCEPTS ARE NOT MAN-MADE CHANNELS AND SHALL BE EXEMPT FROM ANY FLOW RATE CAPACITY AND VELOCITY REQUIREMENTS FOR NATURAL OR MAN-MADE CHANNELS:
- a. CONCENTRATED STORMWATER RUNOFF LEAVING A DEVELOPMENT SITE SHALL BE DISCHARGED DIRECTLY INTO AN ADEQUATE NATURAL OR MANMADE RECEIVING CHANNEL, PIPE OR STORM SEWER SYSTEM, FOR THOSE SITES WHERE RUNOFF IS DISCHARGED INTO A PIPE OR PIPE SYSTEM, DOWNSTREAM STABILITY ANALYSES AT THE OUTFALL OF THE PIPE OR PIPE SYSTEM SHALL BE PERFORMED,
- b. ADEQUACY OF ALL CHANNELS AND PIPES SHALL BE VERIFIED IN THE FOLLOWING MANNER:
  - (1) THE APPLICANT SHALL DEMONSTRATE THAT THE TOTAL DRAINAGE AREA TO THE POINT OF ANALYSIS WITHIN THE CHANNEL IS ONE HUNDRED TIMES GREATER THAN THE CONTRIBUTING DRAINAGE AREA OF THE PROJECT IN QUESTION; OR
  - (2)(a) NATURAL CHANNELS SHALL BE ANALYZED BY THE USE OF A TWO-YEAR STORM TO VERIFY THAT STORMWATER WILL NOT OVERTOP CHANNEL BANKS NOR CAUSE EROSION OF CHANNEL BED OR BANKS;
  - (2)(b) ALL PREVIOUSLY CONSTRUCTED MAN-MADE CHANNELS SHALL BE ANALYZED BY THE USE OF A 10-YEAR STORM TO VERIFY THAT STORMWATER WILL NOT OVERTOP ITS BANKS AND BY THE USE OF A TWO-YEAR STORM TO DEMONSTRATE THAT STORMWATER WILL NOT CAUSE EROSION OF CHANNEL BED OR BANKS; AND
  - (2)(c) PIPES AND STORM SEWER SYSTEMS SHALL BE ANALYZED BY THE USE OF A 10-YEAR STORM TO VERIFY THAT STORMWATER WILL BE CONTAINED WITHIN THE PIPE OR SYSTEM.
  - (2)(d) IF EXISTING NATURAL RECEIVING CHANNELS OR PREVIOUSLY CONSTRUCTED MAN-MADE CHANNELS OR PIPES ARE NOT ADEQUATE, THE APPLICANT SHALL:
  - (3) IMPROVE THE CHANNELS TO A CONDITION WHERE A 10-YEAR STORM WILL NOT OVERTOP THE BANKS AND A TWO-YEAR STORM WILL NOT CAUSE EROSION TO THE CHANNEL, THE BED, OR THE BANKS; OR
  - (4) IMPROVE THE PIPE OR PIPE SYSTEM TO A CONDITION WHERE THE 10-YEAR STORM IS CONTAINED WITHIN THE APPURTENANCES;
  - (5) DEVELOP A SITE DESIGN THAT WILL NOT CAUSE THE PRE-DEVELOPMENT PEAK RUNOFF RATE FROM A TWO-YEAR STORM TO INCREASE WHEN RUNOFF OUTFALLS INTO A NATURAL CHANNEL OR WILL NOT CAUSE THE PRE-DEVELOPMENT PEAK RUNOFF RATE FROM A 10-YEAR STORM TO INCREASE WHEN RUNOFF OUTFALLS INTO A MAN-MADE CHANNEL; OR
  - (6) PROVIDE A COMBINATION OF CHANNEL IMPROVEMENT, STORMWATER DETENTION OR OTHER MEASURES WHICH IS SATISFACTORY TO THE VESCP AUTHORITY TO PREVENT DOWNSTREAM EROSION.
- c. THE APPLICANT SHALL PROVIDE EVIDENCE OF PERMISSION TO MAKE THE IMPROVEMENTS.
- d. ALL HYDROLOGIC ANALYSES SHALL BE BASED ON THE EXISTING WATERSHED CHARACTERISTICS AND THE ULTIMATE DEVELOPMENT CONDITION OF THE SUBJECT PROJECT.
- e. IF THE APPLICANT CHOOSES AN OPTION THAT INCLUDES STORMWATER DETENTION, HE SHALL OBTAIN APPROVAL FROM THE VESCP OF A PLAN FOR MAINTENANCE OF THE DETENTION FACILITIES. THE PLAN SHALL SET FORTH THE MAINTENANCE REQUIREMENTS OF THE FACILITY AND THE PERSON RESPONSIBLE FOR PERFORMING THE MAINTENANCE.
- f. OUTFALL FROM A DETENTION FACILITY SHALL BE DISCHARGED TO A RECEIVING CHANNEL, AND ENERGY DISSIPATORS SHALL BE PLACED AT THE OUTFALL OF ALL DETENTION FACILITIES AS NECESSARY TO PROVIDE A STABILIZED TRANSITION FROM THE FACILITY TO THE RECEIVING CHANNEL.
- g. ALL ON-SITE CHANNELS MUST BE VERIFIED TO BE ADEQUATE.
- h. INCREASED VOLUMES OF SHEET FLOWS THAT MAY CAUSE EROSION OR SEDIMENTATION ON ADJACENT PROPERTY SHALL BE DIVERTED TO A STABLE OUTLET, ADEQUATE CHANNEL, PIPE OR PIPE SYSTEM, OR TO A DETENTION FACILITY.
- i. IN APPLYING THESE STORMWATER MANAGEMENT CRITERIA, INDIVIDUAL LOTS OR PARCELS IN A RESIDENTIAL, COMMERCIAL OR INDUSTRIAL DEVELOPMENT SHALL NOT BE CONSIDERED TO BE SEPARATE DEVELOPMENT PROJECTS. INSTEAD, THE DEVELOPMENT, AS A WHOLE, SHALL BE CONSIDERED TO BE A SINGLE DEVELOPMENT PROJECT. HYDROLOGIC PARAMETERS THAT REFLECT THE ULTIMATE DEVELOPMENT CONDITION SHALL BE USED IN ALL ENGINEERING CALCULATIONS.
- j. ALL MEASURES USED TO PROTECT PROPERTIES AND WATERWAYS SHALL BE EMPLOYED IN A MANNER WHICH MINIMIZES IMPACTS ON THE PHYSICAL, CHEMICAL AND BIOLOGICAL INTEGRITY OF RIVERS, STREAMS AND OTHER WATERS OF THE STATE.
- k. ALL MEASURES APPROVED PRIOR TO JULY 1, 2014, THAT PROVIDES FOR STORMWATER MANAGEMENT THAT ADDRESSES ANY FLOW RATE CAPACITY AND VELOCITY REQUIREMENTS FOR NATURAL OR MAN-MADE CHANNELS SHALL SATISFY THE FLOW RATE CAPACITY AND VELOCITY REQUIREMENTS FOR NATURAL OR MAN-MADE CHANNELS IF THE PRACTICES ARE DESIGNED TO (I) DETAIN THE WATER QUALITY VOLUME AND TO RELEASE IT OVER 48 HOURS; (II) DETAIN AND RELEASE OVER A 24-HOUR PERIOD THE EXPECTED RAINFALL RESULTING FROM THE ONE YEAR, 24-HOUR STORM; AND (III) REDUCE THE ALLOWABLE PEAK FLOW RATE RESULTING FROM THE 1.5, 2, AND 10-YEAR, 24-HOUR STORMS TO A LEVEL THAT IS LESS THAN OR EQUAL TO THE PEAK FLOW RATE FROM THE SITE ASSUMING IT WAS IN A GOOD FORESTED CONDITION, ACHIEVED THROUGH MULTIPLICATION OF THE FORESTED PEAK FLOW RATE BY A REDUCTION FACTOR THAT IS EQUAL TO THE RUNOFF VOLUME FROM THE SITE WHEN IT WAS IN A GOOD FORESTED CONDITION DIVIDED BY THE RUNOFF VOLUME FROM THE SITE IN ITS PROPOSED CONDITION, AND SHALL BE EXEMPT FROM ANY FLOW RATE CAPACITY AND VELOCITY REQUIREMENTS FOR NATURAL OR MAN-MADE CHANNELS AS DEFINED IN ANY REGULATIONS PROMULGATED PURSUANT TO § 62.1-44.15:54 OR 62.1-44.15:65 OF THE ACT.
- l. FOR PLANS APPROVED ON AND AFTER JULY 1, 2014, THE FLOW RATE CAPACITY AND VELOCITY REQUIREMENTS OF § 62.1-44.15:52 A OF THE ACT AND THIS SUBSECTION SHALL BE SATISFIED BY COMPLIANCE WITH WATER QUANTITY REQUIREMENTS IN THE STORMWATER MANAGEMENT ACT (§ 62.1-44.15:24 ET SEQ. OF THE CODE OF VIRGINIA) AND ATTENDANT REGULATIONS, UNLESS SUCH LAND-DISTURBING ACTIVITIES ARE IN ACCORDANCE WITH 9VAC25-870-48 OF THE VIRGINIA STORMWATER MANAGEMENT PROGRAM (VSMP) REGULATION OR ARE EXEMPT PURSUANT TO SUBDIVISION C 7 OF § 62.1-44.15:34 OF THE ACT.
- m. COMPLIANCE WITH THE WATER QUANTITY MINIMUM STANDARDS SET OUT IN 9VAC25-870-66 OF THE VIRGINIA STORMWATER MANAGEMENT PROGRAM (VSMP) REGULATION SHALL BE DEEMED TO SATISFY THE REQUIREMENTS OF THIS SUBDIVISION 19.

EROSION & SEDIMENT CONTROL NARRATIVE

PROJECT DESCRIPTION
THE PURPOSE OF THIS PROJECT IS TO REPLACE UNDERGROUND FUEL TANKS AT A HOSPITAL AND TO ADD A SPRINKLER SYSTEM TO AN EXISTING BUILDING. ACCESS TO THIS SITE IS LOCATED AT AN EXISTING PARKING LOT OFF OF PATRIOTS CIRCLE. WATER QUALITY WILL BE PROVIDED FOR THE 0.08 AC LAND DISTURBANCE WHICH INCLUDES REPLACING CONCRETE PADS WITH TURF TO CONTROL RUNOFF. SANITARY SEWER WILL NOT BE CONSTRUCTED FOR THIS PROJECT. NUTRIENT CREDITS SHALL NOT BE REQUIRED; THIS SITE PLAN PROPOSES 2.24 ACRES OF IMPERVIOUS COVER, REPLACING EXISTING MANAGED TURF.

EXISTING CONDITIONS
THE SITE IS CURRENTLY DEVELOPED WITH A HOSPITAL. THE DISTURBANCE AREA PRIMARILY CONSISTS OF MANAGED TURF AND IMPERVIOUS COVER (PAVED).

ADJACENT PROPERTY
ADJOINING OWNERS ARE NOT SHOWN ON THE PLANS, AS THEY ARE FAR FROM THE AFFECTED AREAS. NO OTHER PROPERTIES ARE AFFECTED. THE PROPERTIES AROUND THE DEVELOPMENT ARE ZONED AS RESIDENTIAL SINGLE FAMILY, HEAVY MANUFACTURING, HIGHWAY BUSINESS, AND COMMUNITY BUSINESS DISTRICTS.

OFFSITE AREAS
THIS PROJECT ANTICIPATES THAT CERTAIN SITE MATERIALS MAY NEED TO BE WASTED OFFSITE. THE LOCATIONS OF OFF-SITE BORROW OR WASTE AREAS SHOULD BE PROVIDED TO THE GOVERNING AUTHORITY. EROSION CONTROL PLANS OR MEASURES MAY BE REQUIRED FOR THE OFF-SITE LOCATIONS. THE DEMOLITION ITEMS SHALL BE DISPOSED IN ACCORDANCE WITH LOCAL REQUIREMENTS. PRIOR TO COMMENCING LAND DISTURBING ACTIVITIES IN AREAS OTHER THAN INDICATED ON THESE PLANS (INCLUDING, BUT NOT LIMITED TO, OFF-SITE BORROW OR WASTE AREAS), THE CONTRACTOR SHALL SUBMIT A SUPPLEMENTARY EROSION CONTROL PLAN TO THE OWNER FOR REVIEW AND APPROVAL BY THE PLAN APPROVING AUTHORITY.

SOILS
AS IDENTIFIED BY THE U.S. DEPARTMENT OF AGRICULTURE, NRCS, THE CHARACTERISTICS ARE SHOWN BELOW:
- SEE SOIL MAP

CRITICAL EROSION AREAS
STEEP SLOPES MAY REQUIRE MATTING WHERE DISTURBED IN ORDER TO STABILIZE. IF AREAS DO NOT STABILIZE WITHIN 14 DAYS, PLACE STABILIZATION MATTING OR HYDRO-SEED AS APPLICABLE TO PREVENT TRANSPORT OF SEDIMENT OFFSITE. THE PLANNED EROSION AND SEDIMENT CONTROL (E&SC) MEASURES ARE INTENDED TO MINIMIZE ANY POTENTIAL PROBLEMS AND PROMOTE STABILIZATION.

EROSION AND SEDIMENT CONTROL MEASURES
TEMPORARY CONSTRUCTION ENTRANCE (3.02) - A STONE PAD, LOCATED AT POINTS OF VEHICULAR INGRESS AND EGRESS ON A CONSTRUCTION SITE, TO REDUCE THE SOIL TRANSPORTED ONTO PUBLIC ROADS AND OTHER PAVED AREAS. A *TEMPORARY CONSTRUCTION ENTRANCE HAS BEEN INCLUDED IN THIS PROJECT AND IS SHOWN ON THE DRAWINGS.*

SILT FENCE (3.05) - A TEMPORARY SEDIMENT BARRIER CONSTRUCTED OF POSTS, FILTER FABRIC AND, IN SOME CASES, A WIRE SUPPORT FENCE, PLACED ACROSS OR AT THE TOE OF A SLOPE OR IN A MINOR DRAINAGE WAY TO INTERCEPT AND DETAIN SEDIMENT AND DECREASE FLOW VELOCITIES FROM DRAINAGE AREAS OF LIMITED SIZE; APPLICABLE WHERE SHEET AND RILL EROSION OR SMALL CONCENTRATED FLOWS MAY BE A PROBLEM. MAXIMUM EFFECTIVE LIFE OF 6 MONTHS. *SILT FENCE WILL BE USED ON THIS PROJECT AND IS SHOWN ON THE DRAWINGS.*

STORM DRAIN INLET PROTECTION (3.07) - THE INSTALLATION OF VARIOUS KINDS OF SEDIMENT TRAPPING MEASURES AROUND DROP INLETS OR CURB INLET STRUCTURES PRIOR TO PERMANENT STABILIZATION OF THE DISTURBED AREA; LIMITED TO DRAINAGE AREAS NOT EXCEEDING ONE ACRE, AND NOT INTENDED TO CONTROL LARGE, CONCENTRATED STORMWATER FLOWS. *STORM DRAIN INLET PROTECTION WILL BE USED ON THIS PROJECT AND IS SHOWN ON THE DRAWINGS.*

CULVERT INLET PROTECTION (3.08) - A SEDIMENT FILTER LOCATED AT THE INLET TO STORM SEWER CULVERTS WHICH PREVENTS SEDIMENT FROM ENTERING, ACCUMULATING IN AND BEING TRANSFERRED BY THE CULVERT. IT ALSO PROVIDES EROSION CONTROL AT CULVERTS DURING THE PHASE OF A PROJECT WHERE ELEVATIONS AND DRAINAGE PATTERNS ARE CHANGING, CAUSING ORIGINAL CONTROL MEASURES TO BE INEFFECTIVE.

TEMPORARY DIVERSION DIKE (3.09) - A RIDGE OF COMPACTED SOIL CONSTRUCTED AT THE TOP OR BASE OF A SLOPING DISTURBED AREA WHICH DIVERTS OFF-SITE RUNOFF AWAY FROM UNPROTECTED SLOPES AND TO A STABILIZED OUTLET, OR TO DIVERT SEDIMENT-LADEN RUNOFF TO A SEDIMENT TRAPPING STRUCTURE. MAXIMUM EFFECTIVE LIFE IS 18 MONTHS.

OUTLET PROTECTION (3.18) - THE INSTALLATION OF RIPRAP CHANNEL SECTIONS AND/OR STILLING BASINS BELOW STORM DRAIN OUTLETS TO REDUCE EROSION AND UNDER-CUTTING FROM SCOURING AT OUTLETS AND TO REDUCE FLOW VELOCITIES BEFORE STORMWATER ENTERS RECEIVING CHANNELS BELOW THESE OUTLETS.

TOPSOILING (3.30) - PRESERVING AND USING TOPSOIL TO PROVIDE A SUITABLE GROWTH MEDIUM FOR VEGETATION USED TO STABILIZE DISTURBED AREAS. APPLICABLE WHERE PRESERVATION OR IMPORTATION OF TOPSOIL IS MOST COST-EFFECTIVE METHOD OF PROVIDING A SUITABLE GROWTH MEDIUM; NOT RECOMMENDED FOR SLOPES STEEPER THAN 2:1 UNLESS ADDITIONAL MEASURES ARE TAKEN TO PREVENT SLOUGHING AND EROSION. TOPSOIL MAY BE STOCKPILED, PROTECTED FROM EROSION, AND THEN REDISTRIBUTED FOR LAWN/GRASSED AREAS. EXACT LOCATION SHALL BE DETERMINED BY THE CONTRACTOR.

TEMPORARY SEEDING (3.31) - ESTABLISHMENT OF TEMPORARY VEGETATIVE COVER ON DISTURBED AREAS THAT WILL NOT BE BROUGHT TO FINAL GRADE FOR PERIODS OF 30 DAYS TO ONE YEAR. BY SEEDING WITH APPROPRIATE RAPIDLY-GROWING PLANTS. *TEMPORARY SEEDING IS PLANNED FOR THIS DEVELOPMENT.*

PERMANENT SEEDING (3.32) - ESTABLISHMENT OF PERENNIAL VEGETATIVE COVER BY PLANTING SEED ON ROUGH-GRADED AREAS THAT WILL NOT BE BROUGHT TO FINAL GRADE FOR A YEAR OR MORE OR WHERE PERMANENT, LONG-LIVED VEGETATIVE COVER IS NEEDED ON FINE-GRADED AREAS. *PERMANENT SEEDING WILL BE USED ON ALL FINISHED AREAS.*

MULCHING (3.35) - APPLICATION OF PLANT RESIDUES OR OTHER SUITABLE MATERIALS TO DISTURBED SURFACES TO PREVENT EROSION AND REDUCE OVERLAND FLOW VELOCITIES. FOSTERS PLAN GROWTH BY INCREASING AVAILABLE MOISTURE AND PROVIDING INSULATION AGAINST EXTREME HEAT OR COLD. SHOULD BE APPLIED TO ALL SEEDING OPERATIONS, THEMSELVES, AND BARE AREAS WHICH CANNOT BE SEEDED DUE TO THE SEASON BUT WHICH STILL NEED PROTECTION TO PREVENT SOIL LOSS.

SOIL STABILIZATION BLANKETS AND MATTING (3.36) - THE INSTALLATION OF A PROTECTIVE BLANKET (TREATMENT 1) OR A SOIL STABILIZATION MAT (TREATMENT 2) ON A PREPARED PLANTING OF A STEEP SLOPE, CHANNEL OR SHORELINE. MAINTENANCE INCLUDES: 1) INSPECT PERIODICALLY AND AFTER RAIN EVENTS FOR EROSION OR UNDERMINING; 2) REPAIR ANY DISLOCATION OR FAILURE; 3) REINSTALL AFTER REPAIRING DAMAGE FROM WASHOUTS OR BREAKAGE; 4) INSPECT UNTIL PERMANENTLY STABILIZED THEN INSPECT ANNUALLY.

TREE PRESERVATION AND PROTECTION (3.38) - PROTECTING EXISTING TREES FROM MECHANICAL AND OTHER INJURY DURING LAND-DISTURBING AND CONSTRUCTION ACTIVITY TO ENSURE THE SURVIVAL OF DESIRABLE TREES WHERE THEY WILL BE EFFECTIVE FOR EROSION AND SEDIMENT CONTROL AND PROVIDE OTHER AESTHETIC BENEFITS.

DUST CONTROL (3.39) - REDUCING SURFACE AND AIR MOVEMENT OF DUST DURING LAND DISTURBANCE, DEMOLITION OR CONSTRUCTION ACTIVITIES IN AREAS SUBJECT TO DUST PROBLEMS IN ORDER TO PREVENT SOIL LOSS AND REDUCE THE PRESENCE OF POTENTIALLY HARMFUL AIRBORNE SUBSTANCE. DUST CONTROL WILL BE PRACTICED TO KEEP DUST GENERATION TO REASONABLE LEVELS.

VEGETATIVE PRACTICES AND PERMANENT STABILIZATION
ALL DISTURBED AREAS SHALL RECEIVE PERMANENT STABILIZATION ACCORDANCE WITH THE "VIRGINIA EROSION AND SEDIMENT CONTROL HANDBOOK" (VA ESCH), STD AND SPEC. 3.32 WITHIN SEVEN (7) DAYS OF REACHING FINAL GRADE. FOR PERMANENT SEEDING MIXTURE SEE THE E&SC DETAIL SHEET. THE CONTRACTOR SHALL CHECK PERIODICALLY FOR ERODED OR DENUDED AREAS AND REAPPLY PERMANENT SEEDING WHERE NECESSARY. IN ERODING AREAS, BLANKET MATTING OR OTHER MEASURE MAY BE REQUIRED TO HELP ESTABLISH THE PERMANENT STABILIZATION. TEMPORARY SOIL STABILIZATION SHALL BE APPLIED WITHIN SEVEN (7) DAYS TO DENUDED AREAS THAT MAY NOT BE AT FINAL GRADE BUT WILL REMAIN DORMANT (UNDISTURBED) FOR LONGER THAN 14 DAYS. PERMANENT SEEDING SHALL BE USED ON ALL AREAS THAT ARE NOT AT FINAL GRADE AND THAT WILL BE LEFT DORMANT FOR A PERIOD OF MORE THAN ONE (1) YEAR.

PERMANENT VEGETATION SHALL NOT BE CONSIDERED ESTABLISHED UNTIL A GROUND COVER IS ACHIEVED THAT IS UNIFORM AND MATURE ENOUGH TO SURVIVE AND WILL INHIBIT EROSION. NEW VEGETATION SHALL BE MAINTAINED AT A MINIMUM OF ONE FULL YEAR AFTER PLANTING. NEW SEEDING SHALL BE SUPPLIED WITH ADEQUATE MOISTURE, ESPECIALLY LATE IN THE SEASON, AND IN ABNORMALLY HOT OR DRY WEATHER. STABILIZATION PRACTICES SHALL BE ACCOMPLISHED IN ACCORDANCE WITH THE APPROPRIATE VESCH STANDARD AND SPECIFICATION AND THE EROSION AND SEDIMENT CONTROL PLAN.

CONSTRUCTION SEQUENCING
SEE E&SC ADMINISTRATIVE NOTES FOR ITEMS TO BE COMPLETED PRIOR TO OBTAINING PERMITS.
1. THE OWNER IS REQUIRED TO GIVE CHESTERFIELD COUNTY INSPECTOR 48 HOURS NOTIFICATION TO SCHEDULE AN ON-SITE PRE-CONSTRUCTION MEETING FOR THE ISSUANCE OF A LAND DISTURBANCE PERMIT. A PRE-CONSTRUCTION CONFERENCE SHALL BE SCHEDULED WITH THE COUNTY OF CHESTERFIELD, TO BE HELD AT LEAST 48 HRS PRIOR TO ANY CONSTRUCTION. VSMP CONSTRUCTION ACTIVITY OPERATOR AND THE ENVIRONMENTAL INSPECTOR (OR AUTHORIZED REPRESENTATIVE) MUST ATTEND THE PRE-CONSTRUCTION MEETING. THE "CERTIFIED RESPONSIBLE LAND DISTURBER" (CRLD) MUST ALSO ATTEND THE PRE-CONSTRUCTION MEETING.
2. CONTRACTOR OR SITE OPERATOR SHALL HAVE AN ON-SITE EMPLOYEE CERTIFIED AS THE CRLD BY THE COMMONWEALTH OF VIRGINIA, DEPARTMENT OF ENVIRONMENTAL QUALITY, WHO WILL INSPECT EROSION AND SILTATION CONTROL DEVICES AND MEASURES FOR PROPER INSTALLATION. THIS EMPLOYEE SHALL ALSO INSPECT FOR DEFICIENCIES IMMEDIATELY AFTER EACH RAINFALL, AT LEAST DAILY DURING PROLONGED RAINFALL, AND AT LEAST EVERY OTHER WEEK WHEN NO RAINFALL OCCURS. PRIOR TO RECEIVING A

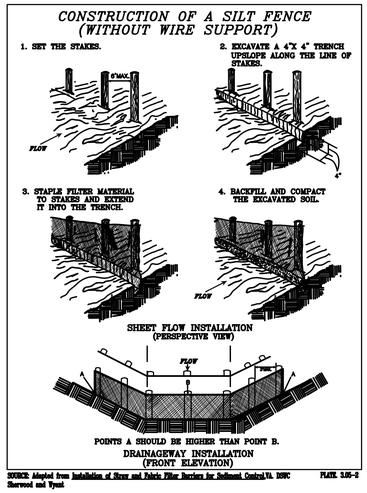

1 C-401 SILT FENCE INSTALLATION

N.T.S.

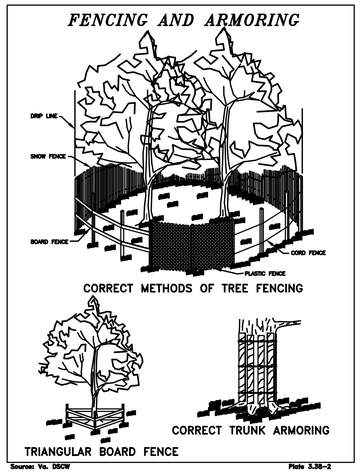

3 C-401 TREE FENCE/ARMOR INSTALLATION

N.T.S.

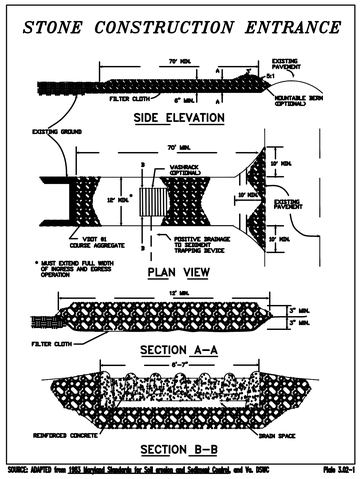

4 C-401 STONE CONSTRUCTION ENTRANCE (SCE)

N.T.S.

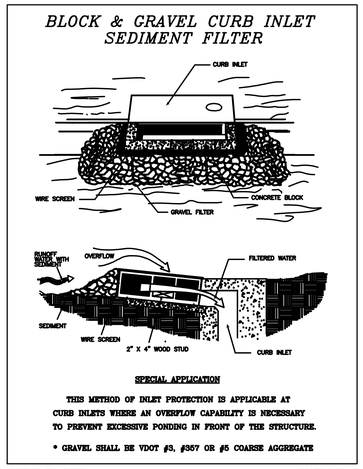

5 C-401 BLOCK & GRAVEL CURB INLET SEDIMENT FILTER

N.T.S.

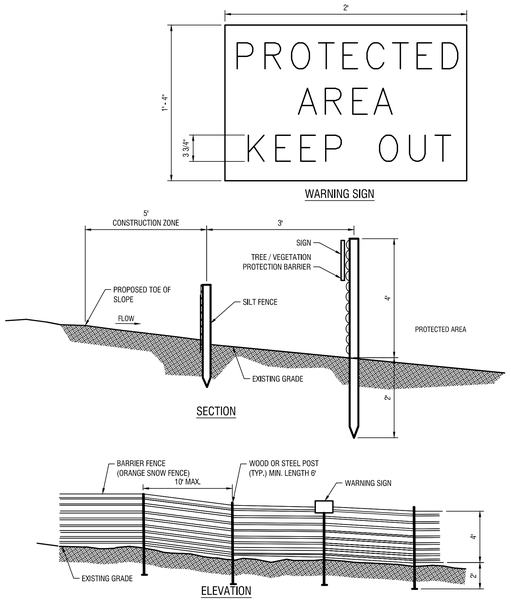

2 C-401 SAFETY FENCE

N.T.S.

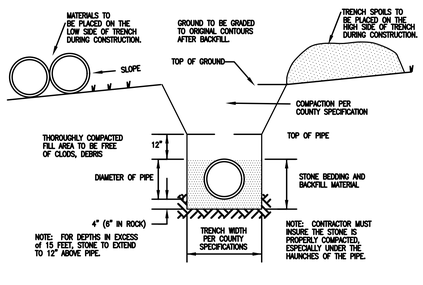

6 C-401 BEDDING, BACKFILL, AND TRENCH SPOIL PLACEMENT

N.T.S.

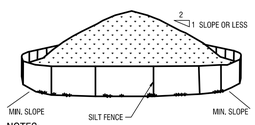

NOTES:

1. AREA CHOSEN FOR STOCKPILING OPERATIONS SHALL BE DRY AND STABLE. REFER TO SHEET C403 FOR PROPOSED/RECOMMENDED STOCKPILE LOCATIONS).
2. MAXIMUM SLOPE OF STOCKPILE SHALL BE 1V:2H.
3. UPON COMPLETION OF SOIL STOCKPILING, EACH PILE SHALL BE SURROUNDED WITH SILT FENCING, THEN STABILIZED WITH VEGETATION OR COVERED.
4. SEE SPECIFICATIONS AND DETAIL FOR INSTALLATION OF SILT FENCE ABOVE (SHEET C406).

7 C-401 TEMPORARY SOIL STOCKPILE

N.T.S.

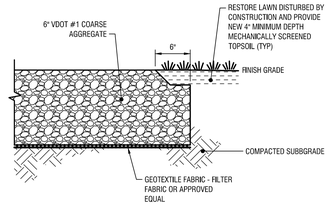

8 C-401 TEMPORARY CONSTRUCTION STAGING AREA

N.T.S.

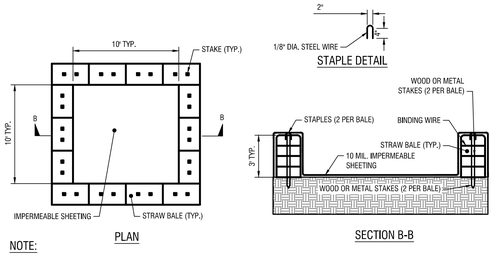

NOTE:

1. CAN BE TWO STACKED BALES OR PARTIALLY EXCAVATED TO REACH 3 FT DEPTH

CONSTRUCTION SPECIFICATIONS

1. CONCRETE TRUCKS WILL ONLY WASH OUT, DISCHARGE SURPLUS CONCRETE, OR DRUM WASH WATER AT APPROVED LOCATIONS IN ACCORDANCE WITH FEDERAL, STATE, AND LOCAL REGULATIONS. ALL CONCRETE MIXER TRUCKS AND CHUTES WILL BE DISCHARGED INTO THE WASHOUT AREA OR HAULED OFF-SITE FOR DISPOSAL. SMALLER EQUIPMENT SUCH AS WHEELBURROWS AND HAND TOOLS ALSO WILL BE WASHED DOWN AT THE TEMPORARY CONCRETE WASHOUT.
2. THE TEMPORARY CONCRETE WASHOUT AREA WILL BE CONSTRUCTED BEFORE ANY CONCRETE POURS ACCUR AT THE SITE.
3. CONCRETE POURS WILL NOT BE CONDUCTED DURIONG OR PRIOR TO AN ANTICIPATED STORM EVENT.
4. LOCATE WASHOUT STRUCTURE A MINIMUM OF 100 FEET AWAY FROM OPEN CHANNELS, STORM DRAIN INLETS, SENSITIVE AREAS, WETLANDS, BUFFERS AND WATER COURSES AND AWAY FROM CONSTRUCTION TRAFFIC.
5. SIZE WASHOUT STRUCTURE FOR VOLUME NECESSARY TO CONTAIN WASH WATER AND SOLIDS AND MAINTAIN AT LEAST 4 INCHES OF FREEBOARD. TYPICAL DIMENSIONS ARE 10 FEET X 10 FEET X 3 FEET DEEP.
6. PREPARE SOIL BASE FREE OF ROCKS OR OTHER DEBRIS THAT MAY CAUSE TEARS OR HOLES IN THE LINER. FOR LINER, USE 10 MIL OR THICKER UV RESISTANT, IMPERMEABLE SHEETING, FREE OF HOLES AND TEARS OR OTHER DEFECTS THAT COMPROMISE IMPERMEABILITY OF THE MATERIAL.
7. PROVIDE A SIGN FOR THE WASHOUT IN CLOSE PROXIMITY TO THE FACILITY TO ENSURE THAT CONCRETE EQUIPMENT OPERATORS USE THE PROPER FACILITY.
8. KEEP CONCRETE WASHOUT STRUCTURE WATER TIGHT, REPLACE IMPERMEABLE LINER IF DAMAGED (E.G., RIPPED OR PUNCTURED), EMPTY OR REPLACE WASHOUT STRUCTURE THAT IS 75 PERCENT FULL, AND DISPOSE OF ACCUMULATED MATERIAL PROPERLY. DO NOT REUSE PLASTIC LINER. WET-VACUUM STORED LIQUIDS THAT HAVE NOT EVAPORATED AND DISPOSE OF IN AN APPROVED MANNER. PRIOR TO FORECASTED RAINSTORMS, REMOVE LIQUIDS OR COVER STRUCTURE TO PREVENT OVERFLOWS, REMOVE HARDENED SOLIDS, WHOLE OR BROKEN UP, FOR DISPOSAL OR RECYCLING. MAINTAIN RUNOFF DIVERSION AROUND EXCAVATED WASHOUT STRUCTURE UNTIL STRUCTURE IS REMOVED.
9. THE WASHOUT AREA WILL BE INSPECTED DAILY AND AFTER HEAVY RAINS TO ENSURE THAT ALL CONCRETE WASHING IS BEING DISCHARGED INTO THE WASHOUT AREA, THAT THERE ARE NO LEAKS OR TEARS PRESENT, AND TO IDENTIFY IF THE WASHOUT HAS REACHED 75% OF ITS HOLDING CAPACITY.
10. BEFORE HEAVY RAINS, THE WASHOUT CONTAINERS LIQUID LEVEL SHOULD BE LOWERED OR THE CONTAINER SHOULD BE COVERED TO AVOID AN OVERFLOW DURING THE STORM EVENT.

9 C-401 CONCRETE WASHOUT AREA ABOVE-GRADE CONTAMINANT AREA WITH STRAW BALES

N.T.S.

PRINTS OF THIS DRAWING SHALL NOT BE USED FOR ANY PURPOSE WHATSOEVER WITHOUT THE SEAL AND SIGNATURE OF THE PROFESSIONAL ENGINEER.

NO.	DESCRIPTION	DATE

CONSULTANTS

Architecture:	Civil Engineering:	Fire & Life Safety:
PF&A DESIGN, P.C.	LABELLA ASSOCIATES	STANTON ENGINEERING SERVICES, LLC

ENGINEER OF RECORD

MILLER•REMICK
A Service-Disabled Veteran-Owned Small Business
(856) 429-4000 • Miller-Remick.com
M–R PROJECT NO. 0499–0136

LABELLA ASSOCIATES
PROFESSIONAL ENGINEER
COMMONWEALTH OF VIRGINIA
JARED J. POPIELLA
Lic. No. 043328
PROFESSIONAL ENGINEER
12/30/2025

Office of Construction and Facilities Management

VA U.S. Department of Veterans Affairs

Drawing Title: CIVIL EROSION & SEDIMENT CONTROL DETAILS

Approved by: Jon Manninen, COR

Phase: BID DOCUMENTS

FULLY SPRINKLERED

Project Title: RENOVATE SURGICAL SUITE PHASE II

Project Number: 658-19-103

Location: SALEM VA MEDICAL CENTER

Issue Date: 2025-12-30

Checked: JJP

Drawn: EBP

VA Drawing Number: 2617

Building Number: 143

Drawing Number: C-401

B:\GLOBAL\Projects\Miller-Remick\22548877 – VA Salem Bldg Generator Reno\06_Drawings\Civil\C405 ESC DETAILS.dwg 12-29-25 01:21:00 PM epatterson

VA FORM 08-6231

1. Liming: An evaluation should be conducted to determine if lime is necessary for temporary seeding. In most soils, it takes up to 6 months for a pH adjustment to occur following the application of lime. Therefore, it may be difficult to justify the cost of liming a temporary site, especially when the soil will later be moved and regraded. The following table may be used to determine the actual need along with suggested application rates.

TABLE 3.31-A

LIMING REQUIREMENTS FOR TEMPORARY SITES

pH Test	Recommended Application of Agricultural Limestone
below 4.2	3 tons per acre
4.2 to 5.2	2 tons per acre
5.2 to 6	1 ton per acre

Source: Va. DSWC

2. Fertilizer: Shall be applied as 600 lbs./acre of 10-20-10 (14 lbs./1,000 sq. ft.) or equivalent nutrients. Lime and fertilizer shall be incorporated into the top 2 to 4 inches of the soil if possible.

3. Surface Roughening: If the area has been recently loosened or disturbed, no further roughening is required. When the area is compacted, crusted, or hardened, the soil surface shall be loosened by discing, raking, harrowing, or other acceptable means (see SURFACE ROUGHENING, Std. & Spec. 3.29).

4. Tracking: Tracking with bulldozer cleats is most effective on sandy soils. This practice often causes undue compaction of the soil surface, especially in clayey soils, and does not aid plant growth as effectively as other methods of surface roughening.

Seeding

Seed shall be evenly applied with a broadcast seeder, drill, cultipacker seeder or hydroseeder. Small grains shall be planted no more than 1½ inches deep. Small seeds, such as Kentucky Bluegrass, should be planted no more than 1/4 inch deep. Other Grasses and Legumes should be planted from 1/4 inch to 1/2 inch deep.

Mulching

1. Seedings made in fall for winter cover and during hot and dry summer months shall be mulched according to MULCHING, Std. & Spec. 3.35, except that hydromulches (fiber mulch) will not be considered adequate. Straw mulch should be used during these periods.

2. Temporary seedings made under favorable soil and site conditions during optimum spring and fall seeding dates may not require mulch.

Re-seeding

Areas which fail to establish vegetative cover adequate to prevent rill erosion will be re-seeded as soon as such areas are identified.

TABLE 3.31-B

ACCEPTABLE TEMPORARY SEEDING PLANT MATERIALS

"QUICK REFERENCE FOR ALL REGIONS"

Planting Dates	Species	Rate (lbs./acre)
Sept. 1 - Feb. 15	50/50 Mix of Annual Ryegrass (Lolium multi-florum) & Cereal (Winter) Rye (Secale cereale)	50 - 100
Feb. 16 - Apr. 30	Annual Ryegrass (Lolium multi-florum)	60 - 100
May 1 - Aug 31	German Millet (Setaria italica)	50

Source: Va. DSWC

TABLE 3.31-C

TEMPORARY SEEDING PLANT MATERIALS, SEEDING RATES, AND DATES

SPECIES	SEEDING RATE		NORTH[a]			SOUTH[b]			PLANT CHARACTERISTICS
	Acre	1000 ft²	3/1 to 4/30	5/1 to 8/15	8/15 to 11/1	2/15 to 4/30	5/1 to 9/1	9/1 to 11/15	
OATS (Avena sativa)	3 bs. (up to 100 lbs., not less than 50 lbs.)	2 lbs.	X	-	-	X	-	-	Use spring varieties (e.g., Noble).
RYE[d] (Secale cereale)	2 bs. (up to 110 lbs., not less than 50 lbs.)	2.5 lbs.	X	-	X	X	-	X	Use for late fall seedings, winter cover. Tolerates cold and low moisture.
GERMAN MILLET (Setaria italica)	50 lbs.	approx. 1 lb.	-	X	-	-	X	-	Warm-season annual. Dies at first frost. May be added to summer mixes.
ANNUAL RYEGRASS[e] (Lolium multi-florum)	60 lbs.	1½ lbs.	X	-	X	X	-	X	May be added in mixes. Will snow out of most stands.
WEEPING LOVEGRASS (Eragrostis curvula)	15 lbs.	5½ ozs.	-	X	-	-	X	-	Warm-season perennial. May bunch. Tolerates hot, dry slopes and acid, infertile soils. May be added to mixes.
KOREAN LESPEDEZA[c] (Lespedeza stipulacea)	25 lbs.	approx. 1½ lbs.	X	X	-	X	X	-	Warm season annual legume. Tolerates acid soils. May be added to mixes.

[a] Northern Piedmont and Mountain region. See Plates 3.22-1 and 3.22-2.
[b] Southern Piedmont and Coastal Plain.
[c] May be used as a cover crop with spring seeding.
[d] May be used as a cover crop with fall seeding.
X May be planted between these dates.
- May not be planted between these dates.

1 C-402 SOIL LIME TREATMENT & TEMPORARY SEEDING SPECIFICATIONS 3.31 - APPALACHIAN / MOUNTAIN AREA

N.T.S.

Seedbed Requirements

Vegetation should not be established on slopes that are unsuitable due to inappropriate soil texture, poor internal structure or internal drainage, volume of overland flow, or excessive steepness, until measures have been taken to correct these problems.

To maintain a good stand of vegetation, the soil must meet certain minimum requirements as a growth medium. The existing soil must have these characteristics:

1. Enough fine-grained material to maintain adequate moisture and nutrient supply.

2. Sufficient pore space to permit root penetration. A bulk density of 1.2 to 1.5 indicates that sufficient pore space is present. A fine granular or crumb-like structure is also favorable.

3. Sufficient depth of soil to provide an adequate root zone. The depth to rock or impermeable layers such as hardpans shall be 12 inches or more, except on slopes steeper than 2:1 where the addition of soil is not feasible.

4. A favorable pH range for plant growth. If the soil is so acidic that a pH range of 6.0-7.0 cannot be attained by addition of pH-modifying materials, then the soil is considered an unsuitable environment for plant roots and further soil modification would be required.

5. Freedom from toxic amounts of materials harmful to plant growth.

6. Freedom from excessive quantities of roots, branches, large stones, large clods of earth, or trash of any kind. Clods and stones may be left on slopes steeper than 3:1 if they do not significantly impede good seed soil contact.

If any of the above criteria cannot be met, i.e., if the existing soil is too coarse, dense, shallow, acidic, or contaminated to foster vegetation, then topsoil shall be applied in accordance with TOPSOILING, Std. & Spec. 3.30.

Necessary structural erosion and sediment control practices will be installed prior to seeding. Grading will be carried out according to the approved plan.

Surfaces will be roughened in accordance with SURFACE ROUGHENING, Std. & Spec. 3.29.

Soil Conditioners

In order to modify the texture, structure, or drainage characteristics of a soil, the following materials may be added to the soil:

TABLE 3.32-C

SITE SPECIFIC SEEDING MIXTURES FOR APPALACHIAN/MOUNTAIN AREA

	Total Lbs. Per Acre
Minimum Care Lawn	
- Commercial or Residential	200-250 lbs.
- Kentucky 31 or Turf-Type Tall Fescue	90-100%
- Improved Perennial Ryegrass *	0-10%
- Kentucky Bluegrass	0-10%
High-Maintenance Lawn	
Minimum of three (3) up to five (5) varieties of bluegrass from approved list for use in Virginia.	125 lbs.
General Slope (3:1 or less)	
- Kentucky 31 Fescue	128 lbs.
- Red Top Grass	2 lbs.
- Seasonal Nurse Crop **	20 lbs.
	150 lbs.
Low-Maintenance Slope (Steeper than 3:1)	
- Kentucky 31 Fescue	108 lbs.
- Red Top Grass	2 lbs.
- Seasonal Nurse Crop **	20 lbs.
- Crownvetch ***	20 lbs.
	150 lbs.

* Perennial Ryegrass will germinate faster and at lower soil temperatures than fescue, thereby providing cover and erosion resistance for seedbed.

** Use seasonal nurse crop in accordance with seeding dates as stated below:
March, April through May 15th ..... Annual Rye
May 16th through August 15th ..... Foxtail Millet
August 16th through September, October ..... Annual Rye
November through February ..... Winter Rye

*** If Flatpea is used, increase to 30 lbs./acre. All legume seed must be properly inoculated. Weeping Lovegrass may also be included in any slope or low-maintenance mixture during warmer seeding periods; add 10-20 lbs/acre in mixes.

2 C-402 PERMANENT SEEDING SPECIFICATIONS 3.32 - APPALACHIAN / MOUNTAIN AREA

N.T.S.

PRINTS OF THIS DRAWING SHALL NOT BE USED FOR ANY PURPOSE WHATSOEVER WITHOUT THE SEAL AND SIGNATURE OF THE PROFESSIONAL ENGINEER.

NO.	DESCRIPTION	DATE

CONSULTANTS

Architecture:	Civil Engineering:	Fire & Life Safety:
PF&A DESIGN, P.C.	LABELLA ASSOCIATES	STANTON ENGINEERING SERVICES, LLC

ENGINEER OF RECORD

MILLER•REMICK
A Service-Disabled Veteran-Owned Small Business
(856) 429-4000 ★ Miller-Remick.com
M+R PROJECT NO: 0499--0136

LABELLA ASSOCIATES PROFESSIONAL ENGINEER

COMMONWEALTH OF VIRGINIA JARED J. PAGNOTTA Lic. No. 063378 PROFESSIONAL ENGINEER

12/30/2025

Office of Construction and Facilities Management

VA U.S. Department of Veterans Affairs

Drawing Title: CIVIL EROSION & SEDIMENT CONTROL DETAILS

Approved by: Jon Manninen, COR

Phase: BID DOCUMENTS

FULLY SPRINKLERED

Project Title: RENOVATE SURGICAL SUITE PHASE II

Project Number: 658-19-103

Location: SALEM VA MEDICAL CENTER

Issue Date: 2025-12-30

Checked: JJP

Drawn: EBP

VA Drawing Number: 2617

Building Number: 143

Drawing Number: C-402

VA FORM 08-6231

B:\GLOBAL\Projects\Miller-Remick\2254877 - VA Salem Bldg Generator Reno\06_Drawings\Civil\C405 ESC DETAILS.dwg 12-29-25 01:21:03 PM epatterson

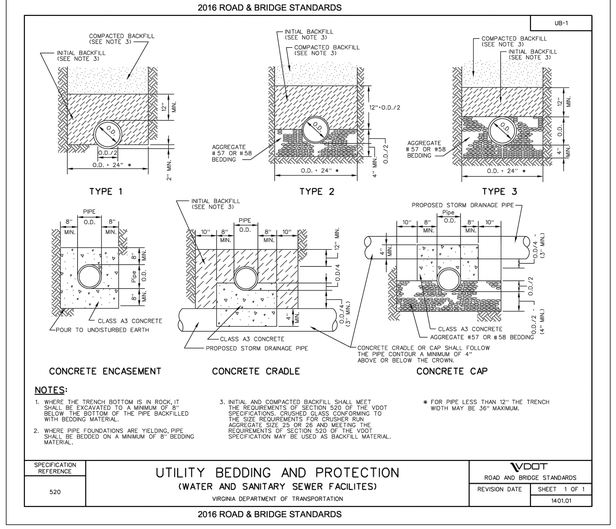

1 C-500 UTILITY BEDDING AND PROTECTION
N.T.S.

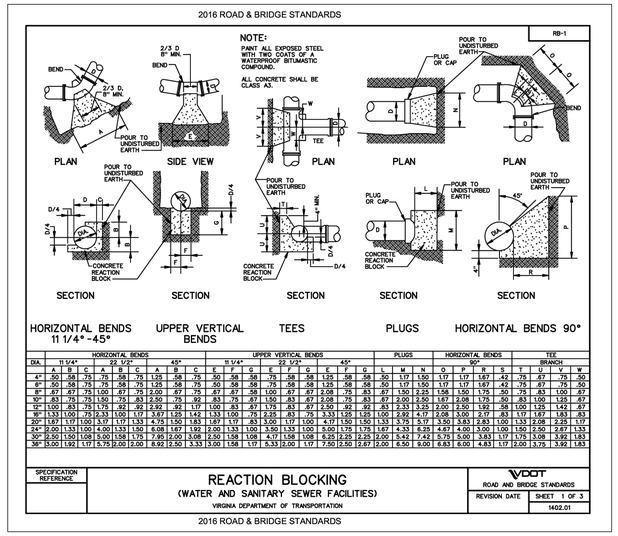

DIA.	HORIZONTAL BENDS 11 1/4°						22 1/2°						45°					
	A	B	C	A	B	C	A	B	C	A	B	C
4"	.50	.58	.75	.75	.58	.75	1.25	.58	.75	.50	.58	.75	.50	.58	.75	.75	.58	.75
6"	.50	.58	.75	.75	.58	.75	1.25	.58	.75	.50	.58	.75	.50	.58	1.25	.58	.58	.75
8"	.67	.67	.75	1.00	.67	.75	2.00	.67	.75	.67	.67	.75	.67	.58	1.00	.67	.67	.75
10"	.83	.75	.75	1.50	.75	.83	2.50	.75	.92	.83	.75	.67	1.50	.83	.67	2.08	.75	.83
12"	1.00	.83	.75	1.75	.92	.92	2.92	.92	1.17	1.00	.83	.67	1.75	.83	.67	2.50	.92	.92
16"	1.33	1.00	.75	2.33	1.00	1.17	3.67	1.25	1.42	1.33	1.00	.75	2.25	.83	.75	3.33	1.25	1.25
20"	1.67	1.17	1.00	3.17	1.17	1.33	4.75	1.50	1.83	1.67	1.17	.83	3.00	1.07	1.00	4.17	1.50	1.50
24"	2.00	1.33	1.00	4.00	1.33	1.50	6.08	1.67	1.92	2.00	1.33	1.00	3.50	1.33	1.00	5.00	1.75	1.75
30"	2.50	1.50	1.08	5.00	1.58	1.75	7.95	2.00	2.08	2.50	1.58	1.08	4.17	1.58	1.08	6.25	2.25	2.25
36"	3.00	1.92	1.17	5.75	2.00	2.00	8.92	2.50	3.33	3.00	1.58	1.17	5.33	2.00	1.17	7.50	2.50	2.67

DIA.	UPPER VERTICAL BENDS 11 1/4°						22 1/2°						45°					
	E	F	G	E	F	G	E	F	G	E	F	G
4"	.50	.58	.58	.75	.58	.58	1.25	.58	.58	.50	.58	.58
6"	.50	.58	.58	.75	.58	.58	1.25	.58	.58	.50	.58	.58
8"	.67	.67	.67	1.00	.67	.67	2.08	.75	.83	.67	1.00	.67
10"	.83	.75	.67	1.50	.83	.67	2.08	.75	.83	.67	2.00	2.50
12"	1.00	.83	.67	1.75	.83	.67	2.50	.92	.92	.83	2.33	3.25
16"	1.33	1.00	.75	2.25	.83	.75	3.33	1.25	1.25	1.00	2.92	4.17
20"	1.67	1.17	1.00	3.17	.83	1.00	4.17	1.50	1.50	1.33	3.75	5.17
24"	2.00	1.33	1.00	4.00	1.33	1.00	5.00	1.75	1.75	1.67	4.33	6.33
30"	2.50	1.50	1.08	5.00	1.58	1.08	6.25	2.25	2.25	2.00	5.42	7.42
36"	3.00	1.92	1.17	5.75	2.00	1.17	7.50	2.50	2.67	2.00	6.50	9.00

DIA.	PLUGS			HORIZONTAL BENDS 90°						TEE BRANCH					
	L	M	N	O	P	R	S	T	U	V	W
4"	.50	1.17	1.50	1.17	1.17	1.67	.42	.75	.67	.75	.50
6"	.50	1.17	1.50	1.17	1.17	1.67	.42	.75	.67	.75	.50
8"	.67	1.50	2.25	1.58	1.50	1.75	.50	.75	.83	1.00	.67
10"	.83	1.67	2.08	2.08	1.75	.50	.83	1.00	1.25	1.42	.67
12"	.83	2.33	3.25	2.00	2.50	1.92	.58	1.00	1.25	1.42	.67
16"	1.00	2.92	4.17	2.08	3.00	2.17	.83	1.17	1.67	1.83	.83
20"	1.33	3.75	5.17	3.50	3.83	2.83	1.00	1.33	2.08	2.25	1.17
24"	1.67	4.33	6.33	4.67	4.00	3.00	1.00	1.50	2.50	2.67	1.33
30"	2.00	5.42	7.42	5.75	5.00	3.83	1.17	1.75	3.08	3.92	1.83
36"	2.00	6.50	9.00	6.83	6.00	4.83	1.17	2.00	3.75	3.92	1.83

2 C-500 REACTION BLOCKING (WATER AND SANITARY SEWER FACILITIES)
N.T.S.

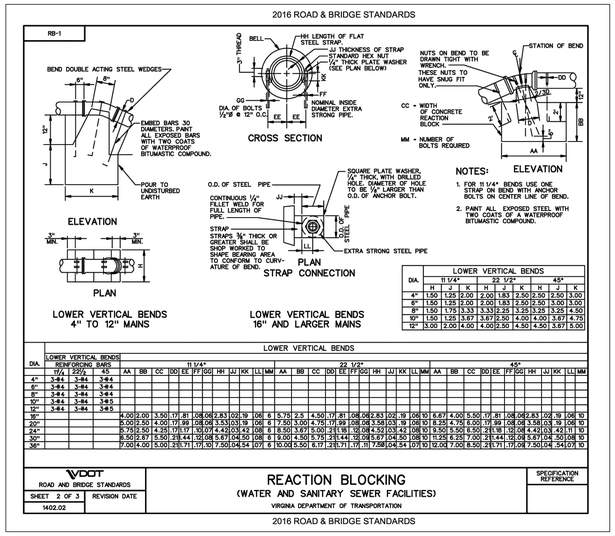

DIA.	LOWER VERTICAL BENDS 11 1/4°						22 1/2°						45°					
	H	J	K	H	J	K	H	J	K
4"	1.50	1.25	2.00	2.00	1.83	2.50	2.50	2.50	3.00
6"	1.50	1.25	2.00	2.00	1.83	2.50	2.50	3.00	3.00
8"	1.50	1.75	3.33	3.33	3.25	3.25	4.50		
10"	1.50	1.25	3.67	3.67	2.50	4.00	4.00	3.67	4.75
12"	3.00	2.00	4.00	4.00	2.50	4.50	4.50	3.67	5.00

3 C-500 REACTION BLOCKING (WATER AND SANITARY SEWER FACILITIES)
N.T.S.

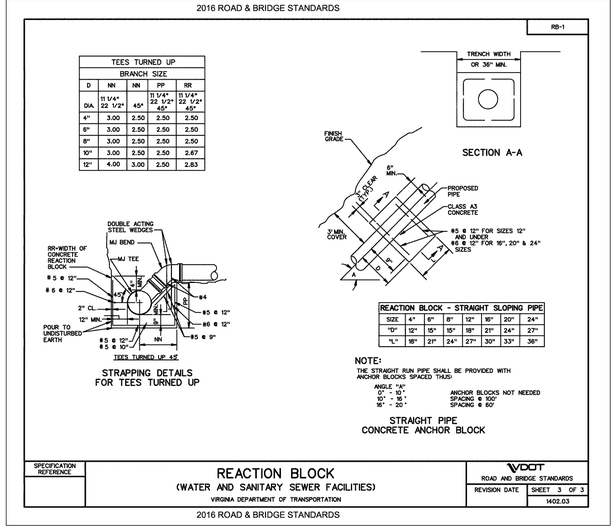

4 C-500 REACTION BLOCK (WATER AND SANITARY SEWER FACILITIES)
N.T.S.

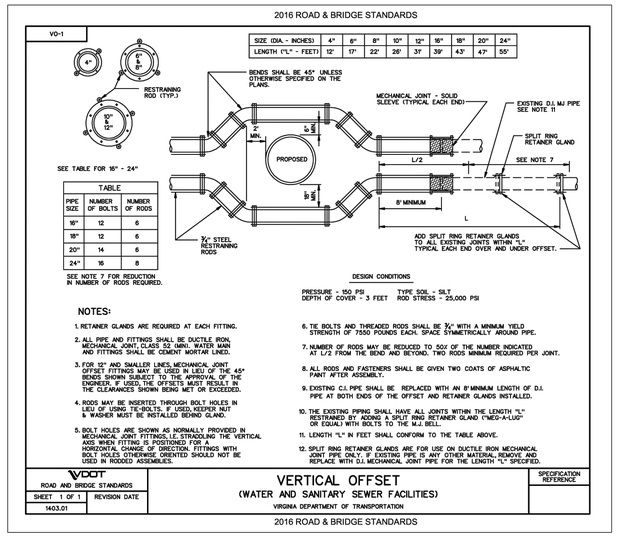

5 C-500 VERTICAL OFFSET (WATER AND SANITARY SEWER FACILITIES)
N.T.S.

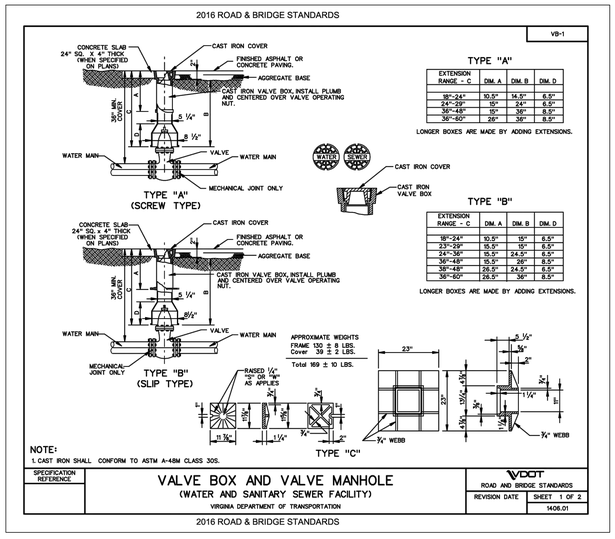

6 C-500 VALVE BOX AND VALVE MANHOLE
N.T.S.

PRINTS OF THIS DRAWING SHALL NOT BE USED FOR ANY PURPOSE WHATSOEVER WITHOUT THE SEAL AND SIGNATURE OF THE PROFESSIONAL ENGINEER.

NO.	DESCRIPTION	DATE

CONSULTANTS

Architecture:	Civil Engineering:	Fire & Life Safety:
PF&A DESIGN, P.C.	LABELLA ASSOCIATES	STANTON ENGINEERING SERVICES, LLC

ENGINEER OF RECORD

MILLER•REMICK
A Service-Disabled Veteran-Owned Small Business
(856) 429-4000 ■ Miller-Remick.com
M–R PROJECT NO: 0499–0136

LABELLA ASSOCIATES PROFESSIONAL ENGINEER
COMMONWEALTH OF VIRGINIA
JARED J. PAPPALLA
No. 063328
PROFESSIONAL ENGINEER
12/30/2025

Office of Construction and Facilities Management

VA U.S. Department of Veterans Affairs

Drawing Title: CIVIL CONSTRUCTION DETAILS	Phase: BID DOCUMENTS	Project Title: RENOVATE SURGICAL SUITE PHASE II Project Number: 658-19-103	VA Drawing Number: 2617
Approved by: Jon Manninen, COR	FULLY SPRINKLERED	Location: SALEM VA MEDICAL CENTER Issue Date: 2025-12-30 / Checked: JJP / Drawn: EBP	Building Number: 143 Drawing Number: C-500

VA FORM 08-6231

B:\GLOBAL\Projects\Miller-Remick\22548877 - VA Salem Bldg Generator Reno\06_Drawings\Civil\C-500 CONSTRUCTION DETAILS.dwg 12-29-25 01:21:11 PM epatterson

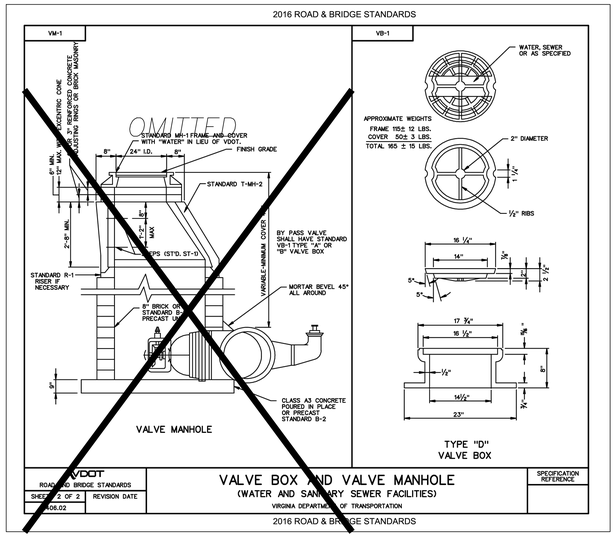

5 C-501 VALVE BOX AND VALVE MANHOLE
N.T.S.

NOTES:

1. VERTICALLY SAW CUT ALL ASPHALT FULL DEPTH.
2. BLOW CLEAN AND APPLY TACK COAT 0.050 GAL/SY AT ALL ASPHALT TO ASPHALT SURFACES.
3. REFER TO HEAVY DUTY PAVEMENT DETAIL SECTION FOR COURSE THICKNESS.

1 C-501 HEAVY DUTY PAVEMENT JOINT
N.T.S.

NOTES:

1. THIS ITEM MAY BE PRECAST OR CAST IN PLACE.
2. CONCRETE TO BE CLASS A3 IF CAST IN PLACE, 4000 PSI IF PRECAST.
3. CURB HAVING A RADIUS OF 300 FEET OR LESS (ALONG FACE OF CURB) WILL BE PAID FOR AS RADIAL CURB.
4. THE DEPTH OF CURB MAY BE REDUCED AS MUCH AS 3" (15° DEPTH) OR INCREASED AS MUCH AS 3" (21° DEPTH) IN ORDER THAT THE BOTTOM OF CURB WILL COINCIDE WITH THE TOP OF A COURSE OF THE PAVEMENT SUBSTRUCTURE. OTHERWISE, THE DEPTH IS TO BE 18" AS SHOWN. NO ADJUSTMENT IN THE PRICE BID IS TO BE MADE FOR A DECREASE OR AN INCREASE IN DEPTH.
5. CG-2 IS TO BE USED ON ROADWAYS MEETING THE REQUIREMENTS FOR CG-6 AS SHOWN IN APPENDIX A OF THE VDOT ROAD DESIGN MANUAL, IN THE SECTION ON GS URBAN STANDARDS.

3 C-501 COMBINATION 6" CURB AND GUTTER

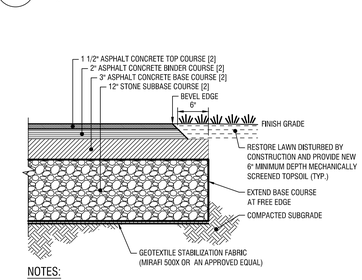

NOTES:

1. PROVIDE ADDITIONAL SUBBASE MATERIAL WHERE FILL IS REQUIRED TO OBTAIN PROPER SUBGRADE ELEVATION, OR TO REPLACE UNSUITABLE SUBGRADE MATERIAL.
2. CONTRACTOR SHALL INSTALL SPECIFIED THICKNESSES OR EXISTING SECTIONAL THICKNESSES, WHICHEVER IS GREATER.

2 C-501 HEAVY DUTY ASPHALT PAVEMENT
N.T.S.

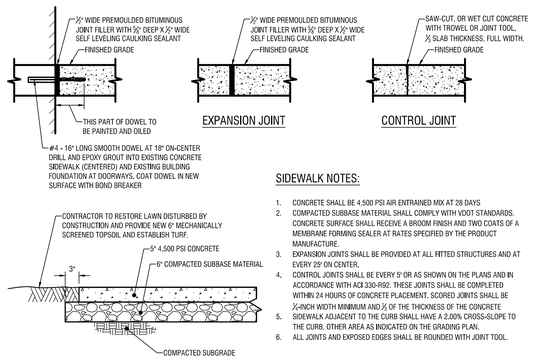

SIDEWALK NOTES:

1. CONCRETE SHALL BE 4,500 PSI AIR ENTRAINED MIX AT 28 DAYS
2. COMPACTED SUBBASE MATERIAL SHALL COMPLY WITH VDOT STANDARDS. CONCRETE SURFACE SHALL RECEIVE A BROOM FINISH AND TWO COATS OF A MEMBRANE FORMING SEALER AT RATES SPECIFIED BY THE PRODUCT MANUFACTURE.
3. EXPANSION JOINTS SHALL BE PROVIDED AT ALL FITTED STRUCTURES AND AT EVERY 25' ON CENTER.
4. CONTROL JOINTS SHALL BE EVERY 5' OR AS SHOWN ON THE PLANS AND IN ACCORDANCE WITH ACI 330-R92. THESE JOINTS SHALL BE COMPLETED WITHIN 24 HOURS OF CONCRETE PLACEMENT. SCORED JOINTS SHALL BE ¼-INCH WIDTH MINIMUM AND ¼ OF THE THICKNESS OF THE CONCRETE
5. SIDEWALK ADJACENT TO THE CURB SHALL HAVE A 2.00% CROSS-SLOPE TO THE CURB. OTHER AREA AS INDICATED ON THE GRADING PLAN.
6. ALL JOINTS AND EXPOSED EDGES SHALL BE ROUNDED WITH JOINT TOOL.

4 C-501 CONCRETE SIDEWALK
N.T.S.

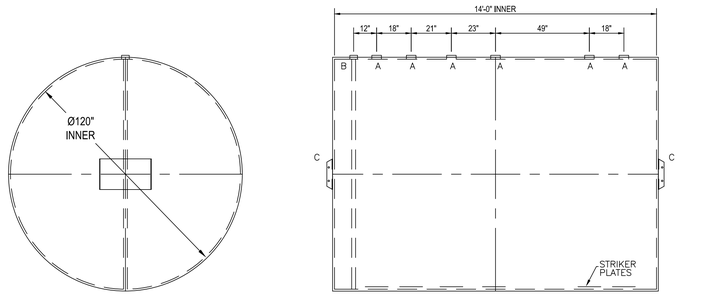

DESIGN DATA
CAPACITY – 8,000 GALLONS
TYPE – DOUBLE WALL, UNDERGROUND
NO. REQ. – –
OPERATING PRESSURE – ATMOSPHERIC
TANK MATERIAL – MILD CARBON STEEL
THICKNESS INNER –HEADS: 1/4 GA, SHELL: 1/4" THICKNESS OUTER –HEADS: 1/4", SHELL: 10 GA *GA THK. BASED ON 60" MAX. BURIAL DEPTH
CONSTRUCTION – INNER TANK LAP WELD OUTSIDE ONLY OUTER TANK LAP WELD OUTSIDE ONLY
TANK TEST – INNER – 5 PSIG OUTER – 2 PSIG AND FULL VACUUM
INT. FINISH – NONE –
EXT. FINISH – SP6 BLAST, 75 MILS POLYURETHANE –
LABEL – UL–1746 PART IV

LEGEND	
A	4" FITTING
B	2" INTERNAL MONITOR PIPE
C	HTM SPIN BRKT - MFG USE ONLY - NOT TO BE USED FOR FIELD INSTALLATION
D	-
E	-
F	-

NOTES:
1) 15,000 VOLT SPARK TEST PROVIDED AT FACTORY.
2) SHOP TO INSTALL 1/4"x12"x12" STRIKER PLATES, ROLLED AND SEAL WELD TO THE TANK.

UNLESS NOTED, TOLERANCES ARE +/- 1"

8,000 GAL 120"Ø DOUBLE WALL

CUSTOMER:

PROJECT:

QUOTE NO: CHK'D BY:

SCALE: 3/8"=1'-0" DATE: DWG. BY: DWG. NO.

6 C-501 8,000 GALLON 12" Ø DOUBLE WALL
N.T.S.

PRINTS OF THIS DRAWING SHALL NOT BE USED FOR ANY PURPOSE WHATSOEVER WITHOUT THE SEAL AND SIGNATURE OF THE PROFESSIONAL ENGINEER.

NO.	DESCRIPTION	DATE

CONSULTANTS

Architecture:	Civil Engineering:	Fire & Life Safety:
PF&A DESIGN, P.C.	LABELLA ASSOCIATES	STANTON ENGINEERING SERVICES, LLC

ENGINEER OF RECORD

MILLER•REMICK
A Service-Disabled Veteran-Owned Small Business
(856) 429-6000 • Miller-Remick.com
M–R PROJECT NO: 0499–0136

LABELLA ASSOCIATES PROFESSIONAL ENGINEER

COMMONWEALTH OF VIRGINIA JARED J. MONTELLA Lic. No. 043378 PROFESSIONAL ENGINEER
12/30/2025

Office of Construction and Facilities Management

VA U.S. Department of Veterans Affairs

Drawing Title: CIVIL CONSTRUCTION DETAILS

Approved by: Jon Manninen, COR

Phase: BID DOCUMENTS

FULLY SPRINKLERED

Project Title: RENOVATE SURGICAL SUITE PHASE II
Project Number: 658-19-103

Location: SALEM VA MEDICAL CENTER

Issue Date: 2025-12-30
Checked: JJP
Drawn: EBP

VA Drawing Number: 2617
Building Number: 143
Drawing Number: C-501

VA FORM 08-6231

three inches = one foot
one and one half inches = one foot
one inch = one foot
three quarters inch = one foot
one half inch = one foot
three eighths inch = one foot
one quarter inch = one foot
one eighth inch = one foot

B:\GLOBAL\Projects\Miller-Remick\2254877 – VA Salem Bldg Generator Reno\06_Drawings\Civil\C-500 CONSTRUCTION DETAILS.dwg 12-29-25 01:21:14 PM epatterson

ABBREVIATIONS

AB	ANCHOR BOLT
ADDL	ADDITIONAL
AFF	ABOVE FINSIHED FLOOR
ALT	ALTERNATE
ARCH	ARCHITECT
BCE	BOTTOM CHORD EXTENSION
BO	BOTTOM OF
BLDG	BUILDING
BM	BEAM
BOTT	BOTTOM
BRG	BEARING
BSMT	BASEMENT
BP	BEARING PLATE
BTWN	BETWEEN
BS	BOTH SIDES
CL	CENTERLINE
CANT	CANTILEVER
CMU	CONCRETE MASONRY UNIT
CNTR	CENTER/CENTERED
COL	COLUMN
CONC	CONCRETE
CONN	CONNECTION
CONT	CONTINUOUS
COORD	COORDINATE
Ø / DIA	DIAMETER
DWG	DRAWING
(E)	EXISTING
EA	EACH
EF	EACH FACE
EL	ELEVATION
ELECT	ELECTRICAL
ELEV	ELEVATOR
EMBED	EMBEDMENT
EOD	EDGE OF DECK
EOS	EDGE OF SLAB
EQ	EQUAL
EQUIP	EQUIPMENT
EW	EACH WAY
EWB	EACH WAY BOTTOM
EWT	EACH WAY TOP
EXIST	EXISTING
EXP	EXPANSION
EXT	EXTERIOR
FDN	FOUNDATION
FF	FINISHED FLOOR
FIN	FINISH
FLR	FLOOR
FT	FEET
FTG	FOOTING
GA	GAGE
GALV	GALVANIZED
GB	GRADE BEAM
(H)	HIGH
HP	HIGH POINT
HORIZ	HORIZONTAL
IF	INSIDE FACE
IJ	ISOLATION JOINT
IN	INCHES
INFO	INFORMATION
INT	INTERIOR
IS	INSIDE
JT	JOINT
k	KIP
k-ft	KIP-FEET
(L)	LOW
LP	LOW POINT
LW	LIGHT WEIGHT
LLH	LONG LEG HORIZONTAL
LLV	LONG LEG VERTICAL
LTS	LAP TENSION SPLICE
MEP	MECHANICAL ELECTRICAL PLUMBING
MST	METAL STUD TRUSS
MAX	MAXIMUM
MECH	MECHANICAL
MEZZ	MEZZANINE
MFR	MANUFACTURER
MIN	MINIMUM
MISC	MISCELLANEOUS
MP	MASONRY
(N)	NEW
NTS	NOT TO SCALE
NW	NORMAL WEIGHT
OC	ON CENTER
OH	OPPOSITE HAND
OS	OUTSIDE
PAF	POWEDER ACTUATED FASTENER
PL	PLATE
PLUMB	PLUMBING
PC	PILE CAP
P/C	PRECAST
PSF	POUNDS PER SQUARE FOOT
PSI	POUNDS PER SQUARE INCH
REINF	REINFORCEMENT
REQ'D	REQUIRED
SF	STEP FOOTING
SOG	SLAB ON GRADE
SCHED	SCHEDULE
SECT	SECTION
SIM	SIMILAR
SPECS	SPECIFICATIONS
SST	STAINLESS STEEL
STL	STEEL
STIFF	STIFFENER
STRUCT	STRUCTURAL
T&B	TOP AND BOTTOM
T	TOP
T/	TOP OF
TOC	TOP OF CONCRETE
TOS	TOP OF STEEL
TS	THICKENED SLAB
TDS	TURNED DOWN SLAB
THK	THICK OR THICKENED
TYP	TYPICAL
UNO	UNLESS NOTED OTHERWISE
VIF	VERIFY IN FIELD
VERT	VERTICAL
W/	WITH
WP	WALL PLATE
WWF	WELDED WIRE FABRIC

GENERAL STRUCTURAL & CONSTRUCTION NOTES

THE FOLLOWING GENERAL STRUCTURAL NOTES ARE APPLICABLE TO THE STRUCTURAL DRAWINGS ONLY. THESE NOTES ARE PROVIDED FOR CONVENIENCE AND ARE SUPPLEMENTAL TO THE SPECIFICATIONS.

GENERAL

1. ALL WORK SHALL CONFORM TO THE:
   - A. 2021 INTERNATIONAL BUILDING CODE
   - B. VA DESIGN MANUALS
   - C. AND TO ALL OTHER APPLICABLE FEDERAL, STATE, AND LOCAL REGULATIONS.
2. IN CASE OF CONFLICT BETWEEN THE GENERAL NOTES, SPECIFICATIONS, AND DETAILS, THE MOST RIGID REQUIREMENTS SHALL GOVERN.
3. WORK NOT INDICATED ON A PART OF THE DRAWINGS BUT REASONABLY IMPLIED TO BE SIMILAR TO THAT SHOWN IN CORRESPONDING PLACES SHALL BE REPEATED.
4. JOB SITE SAFETY AND CONSTRUCTION PROCEDURES ARE THE SOLE RESPONSIBILITY OF THE CONTRACTOR.
5. PROVIDE FOR DEWATERING AS REQUIRED DURING EXCAVATION AND CONSTRUCTION. REFER TO SPECIFICATIONS FOR ADDITIONAL INFORMATION.
6. COORDINATE OPENINGS, SLEEVES, CONCRETE HOUSEKEEPING PADS, INSERTS AND DEPRESSIONS SHOWN ON THE ARCHITECTURAL, STRUCTURAL, MECHANICAL, ELECTRICAL, AND PLUMBING DRAWINGS.
7. SEE ARCHITECTURAL DRAWINGS FOR LOCATIONS OF MASONRY AND DRYWALL NON-LOAD BEARING PARTITIONS. PROVIDE SLIP CONNECTIONS THAT ALLOW VERTICAL MOVEMENT AT THE HEADS OF ALL SUCH PARTITIONS. CONNECTIONS SHALL BE DESIGNED TO SUPPORT THE TOP OF THE WALLS LATERALLY FOR THE CODE-REQUIRED LATERAL LOAD.
8. ALL COSTS OF INVESTIGATION AND/OR REDESIGN DUE TO CONTRACTOR IMPROPER INSTALLATION OF STRUCTURAL ELEMENTS OR OTHER ITEMS NOT IN CONFORMANCE WITH THE CONTRACT DOCUMENTS SHALL BE AT THE CONTRACTOR'S EXPENSE.
9. THE STRUCTURAL DRAWINGS SHALL BE USED IN CONJUNCTION WITH THE SPECIFICATIONS, ARCHITECTURAL, MECHANICAL, ELECTRICAL, AND PLUMBING DRAWINGS. IF THERE IS A DISCREPANCY BETWEEN DRAWINGS, IT IS THE CONTRACTOR'S RESPONSIBILITY TO NOTIFY THE COR PRIOR TO PERFORMING THE WORK.
10. COORDINATE NEW EQUIPMENT STRUCTURES SHOWN ON THE CONTRACT DRAWINGS WITH MANUFACTURER'S APPROVED SHOP DRAWINGS. ALL DIMENSIONS, DETAILS AND STRUCTURAL DESIGN REVISIONS REQUIRED TO ACCOMMODATE APPROVED EQUIPMENT SHALL BE MADE BY THE CONTRACTOR AT NO COST TO THE OWNER.
11. SUBMIT, FOR REVIEW, DRAWINGS AND CALCULATIONS FOR ALL PERFORMANCE ASSEMBLIES IDENTIFIED IN THE GENERAL NOTES AND LISTED BELOW. THE DESIGN OF THESE ASSEMBLIES IS THE RESPONSIBILITY OF THE CONTRACTOR'S ENGINEER REGISTERED IN THE PROJECT'S JURISDICTION. ALL SUBMITTALS SHALL BEAR THIS ENGINEER'S SEAL AND SIGNATURE. REVIEW SHALL BE FOR GENERAL CONFORMANCE WITH THE PROJECT REQUIREMENTS AS INDICATED ON THE DRAWINGS AND IN THE GENERAL NOTES:
    - A. METAL STAIRS AND METAL RAILINGS - DESIGNS SHALL TAKE INTO ACCOUNT ALL VERTICAL AND LATERAL LOADS REQUIRED BY APPLICABLE BUILDING CODES. WHERE HEADERS OR OTHER TYPES OF STRUCTURAL MEMBERS HAVE BEEN DESIGNATED BY THE STRUCTURAL ENGINEER OF RECORD TO SUPPORT THE STAIRS, THE CONNECTIONS FROM THE STAIRS SHALL BE DESIGNED SO THAT NO ECCENTRIC OR TORSIONAL FORCES ARE INDUCED IN THESE STRUCTURAL MEMBERS. THE CONTRACTOR SHALL BE RESPONSIBLE FOR FURNISHING AND INSTALLING HARDWARE AS REQUIRED BY THE STAIR DESIGN.
12. SHOP DRAWINGS FOR ALL STRUCTURAL MATERIALS TO BE SUBMITTED TO COR FOR REVIEW PRIOR TO THE START OF FABRICATION OR COMMENCEMENT OF WORK.
    - A. REPRODUCTION OF ANY PORTION OF THE STRUCTURAL CONTRACT DRAWINGS FOR RESUBMITTAL AS SHOP DRAWINGS IS PROHIBITED. SHOP DRAWINGS PRODUCED IN SUCH A MANNER WILL BE REJECTED AND RETURNED.
    - B. SHOP DRAWINGS SHALL BEAR THE CONTRACTOR'S STAMP OF APPROVAL, WHICH SHALL CONSTITUTE CERTIFICATION THAT THE CONTRACTOR HAS VERIFIED ALL CONSTRUCTION CRITERIA, MATERIALS AND SIMILAR DATA AND HAS CHECKED EACH DRAWING FOR COMPLETENESS, COORDINATION AND COMPLIANCE WITH THE CONTRACT DOCUMENTS.
    - C. THE SHOP DRAWINGS SHALL INCLUDE ALL COORDINATED DIMENSIONS.

SPECIAL INSPECTIONS

1. INSPECTION IS REQUIRED OF ALL CONSTRUCTION DELINEATED ON THE STRUCTURAL DRAWINGS AND/OR SPECIFICATIONS. THE CONTRACTOR SHALL ENGAGE A TESTING AGENCY TO PROVIDE TESTING SERVICES AS INDICATED IN EACH SECTION OF THESE GENERAL NOTES. THE TESTING AGENCY SHALL PROVIDE PERSONNEL CERTIFIED BY INSTITUTE OF CERTIFIED ENGINEERING TECHNICIANS, OR OTHER RECOGNIZED COMPARABLE ORGANIZATION. THE WORK SPECIFICALLY REQUIRING SPECIAL INSPECTIONS AS FOLLOWS:
   - A. STRUCTURAL CONCRETE INSPECTION
   - B. STRUCTURAL STEEL INSPECTION
   - C. SEISMIC RESTRAINT OF NON-STRUCTURAL COMPONENTS

   SUBMIT PERIODIC REPORTS WITHIN ONE (1) BUSINESS DAY AFTER RECEIPT BY THE CONTRACTOR TO COR DURING CONSTRUCTION. SUBMIT FINAL INSPECTION REPORT SUMMARY FOR EACH DIVISION OF WORK, CERTIFIED BY A LICENSED PROFESSIONAL ENGINEER, THAT INSPECTIONS WERE PERFORMED AND THAT WORK WAS PERFORMED IN ACCORDANCE WITH CONTRACT DOCUMENTS.

EXISTING CONDITIONS

1. ALL DIMENSIONS, ELEVATIONS, AND PHYSICAL CONDITIONS SHOWN ON THE DRAWINGS FOR EXISTING STRUCTURES ARE BASED ON LIMITED FIELD OBSERVATIONS OR OTHER AVAILABLE SOURCES. SUCH DEPICTIONS OF EXISTING CONSTRUCTION ARE INTENDED TO BE GENERAL, APPROXIMATE, AND LIMITED TO THOSE AREAS FOR WHICH WORK IS REQUIRED. THESE DEPICTIONS ARE PROVIDED ONLY FOR THE CONVENIENCE OF THE CONTRACTOR. PRIOR TO BIDDING, CONDUCT A CAREFUL AND THOROUGH EXAMINATION OF EXISTING CONDITIONS AT THE SITE APPLICABLE TO THE WORK.
2. THE EXACT EXTENT OF THE CONSTRUCTION WORK CANNOT BE NECESSARILY OR ACCURATELY DETERMINED PRIOR TO THE COMMENCEMENT OF WORK. ACTUAL FIELD CONDITIONS MAY REQUIRE MODIFICATIONS TO THE CONSTRUCTION DETAILS, MATERIAL QUANTITIES, AND EXTENT OF THE MODIFICATION WORK SHOWN ON CONTRACT DRAWINGS. PERFORM THE WORK TO MEET FIELD CONDITIONS ENCOUNTERED.
3. VERIFY ALL EXISTING BUILDING AND SITE INFORMATION SHOWN (DIMENSIONS, ELEVATIONS, ETC.) AND NOTIFY THE COR OF ANY DISCREPANCIES PRIOR TO FABRICATION OF ANY STRUCTURAL COMPONENT. IF THE EXISTING FIELD CONDITIONS DO NOT PERMIT THE INSTALLATION OF THE WORK IN ACCORDANCE WITH THE DETAILS SHOWN, THE CONTRACTOR SHALL NOTIFY THE COR IMMEDIATELY AND PROVIDE A SKETCH OF THE CONDITION WITH HIS PROPOSED MODIFICATION OF THE DETAILS GIVEN ON THE CONTRACT DOCUMENTS. DO NOT COMMENCE WORK UNTIL CONDITION IS RESOLVED AND THE COR APPROVES MODIFICATION. FAILURE TO NOTIFY COR OF UNSATISFACTORY CONDITIONS CONSTITUTES ACCEPTANCE OF UNSATISFACTORY CONDITIONS.
4. INCORPORATE ACTUAL FIELD CONDITIONS AND DIMENSIONS IN THE WORK AND INDICATE CHANGES AND ADJUSTMENTS ON SUBMITTED DRAWING
5. WHERE ALTERATIONS INVOLVE THE EXISTING SUPPORTING STRUCTURE, EXISTING STRUCTURAL COMPONENTS (MASONRY WALLS, FAÇADE PANELS, ETC.), ADJACENT CONSTRUCTION, AND/OR ADJACENT UTILITY LINES, PROVIDE SHORING AND PROTECTION REQUIRED TO MAINTAIN STRUCTURAL INTEGRITY AND PREVENT ANY LATERAL OR VERTICAL MOVEMENTS OF ALL EXISTING AND ADJACENT SITE STRUCTURES AND UTILITIES.
   - A. BRACING, SHEETING, SHORING, UNDERPINNING, ETC., REQUIRED TO ENSURE THE STRUCTURAL INTEGRITY OF THE EXISTING BUILDINGS OR NEW CONSTRUCTION, SIDEWALKS, UTILITIES, ETC., SHALL BE DESIGNED BY A PROFESSIONAL ENGINEER ENGAGED BY THE CONTRACTOR. DETAILED SIGNED AND SEALED SHOP DRAWINGS SHALL BE PREPARED INDICATING ALL WORK TO BE PERFORMED, SUBMIT THE SHOP DRAWINGS IN ACCORDANCE WITH THE CONTRACT REQUIREMENTS.
   - B. THE CONTRACTOR IS RESPONSIBLE TO DETERMINE ALLOWABLE CONSTRUCTION LOADS AND TO PROVIDE DESIGN AND CONSTRUCTION OF FALSEWORK, FORMWORK, STAGINGS, BRACING, SHEETING AND SHORING, ETC.
6. HEAVY EQUIPMENT IS NOT PERMITTED TO BE CLOSER THAN 8'-0" FROM ANY FOUNDATION WALL. IF IT IS NECESSARY TO OPERATE SUCH EQUIPMENT CLOSER THAN 8'-0" TO THE WALL, THE CONTRACTOR IS THE SOLE RESPONSIBLE PARTY AND, AT HIS OWN EXPENSE, SHALL PROVIDE ADEQUATE SUPPORTS OR BRACE THE WALL TO WITHSTAND THE ADDITIONAL LOADS SUPERIMPOSED FROM SUCH EQUIPMENT.

CONSTRUCTION OPERATIONS

1. NOTIFY THE COR OF ANY CONFLICT ON CONTRACT DOCUMENTS DURING BID. IN CASE OF CONFLICT IN THE CONTRACT DRAWINGS OR THE PROJECT SPECIFICATIONS, THE MOST STRINGENT REQUIREMENT SHALL APPLY.
2. AFTER THE AWARD OF THE CONTRACT, THE CONTRACTOR MAY NOT SUBMIT ANY CLAIM ALLEGING INSUFFICIENT DATA, INCORRECTLY ASSUMED CONDITIONS, OR MISUNDERSTANDING WITH REGARD TO MATTERS FOR WHICH NO SUCH CLARIFICATION WAS SOUGHT DURING THE BIDDING PHASE OF THE PROJECT, AS DESCRIBED FURTHER IN THE GENERAL CONDITION CONTRACT.
3. ASSUME AN ABSOLUTE OBLIGATION TO PROTECT EXISTING STRUCTURES AND EQUIPMENT, NEW WORK AND THE GENERAL PUBLIC FROM DAMAGE, LOSS OR INJURY RESULTING FROM THE CONTRACTOR'S OPERATIONS. IN THE EVENT OF SUCH DAMAGE OR LOSS, PROMPTLY REPLACE OR RESTORE THE WORK TO AN EQUIVALENT QUALITY TO THE SATISFACTION OF THE COR AND AT NO EXPENSE TO THE OWNER.
4. REMOVE TO THE EXTENT INDICATED AND PROPERLY DISPOSE OF EXISTING STRUCTURES AND MATERIALS TO BE DEMOLISHED IN ACCORDANCE WITH THE SPECIFICATIONS.
5. ALL WORK SPECIFIED HEREIN SHALL BE INSPECTED IN ACCORDANCE WITH THE BUILDING CODE AND ALL LOCAL ORDINANCES. THE COR MAY VISIT THE SITE TO ASCERTAIN GENERAL CONFORMANCE WITH THE CONTRACT DOCUMENTS. SUCH SITE VISITS ARE NOT TO BE CONSTRUED AS MEETING ANY INSPECTION REQUIREMENTS UNLESS THE COR SPECIFICALLY SO STATES IN WRITING.
6. RFI & RFC ARE REQUIRED TO BE COMMUNICATED FORMALLY AND IN WRITING TO THE COR AS PROVIDED IN THIS GENERAL NOTES. THE PURPOSE OF THIS POLICY IS TO AVOID COMMUNICATION WITH UNAUTHORIZED PERSONS AND TO MINIMIZE MISINFORMATION AND SPECULATION. THE COR WILL NOT RECOGNIZE AND CANNOT BE OBLIGATED TO ANY REQUEST THAT HAS NOT BEEN COMMUNICATED IN THE MANNER SET FORTH ABOVE. THE COR CANNOT BE RESPONSIBLE FOR ANY MISCOMMUNICATION OR MISINFORMATION OBTAINED IN VIOLATION OF THIS POLICY AND RESERVES THE RIGHT TO REJECT ANY REQUEST IN THE EVENT THAT ANY PERSON FAILS TO ADHERE TO THIS POLICY.
7. ALL MATERIALS SHALL BE STORED TO PROTECT THEM FROM EXPOSURE TO THE ELEMENTS.

SELECTIVE DEMOLITION

1. CONDUCT DEMOLITION OPERATIONS TO PREVENT INJURY TO PERSONS AND DAMAGE TO ADJACENT STRUCTURES, FACILITIES AND SITE IMPROVEMENTS TO REMAIN. ENSURE SAFE PASSAGE OF PERSONS AROUND SELECTIVE DEMOLITION AREA. LOCATE AND RE-ROUTE ANY EXISTING UTILITY PRIOR TO STARTING THE WORK.
2. DEMOLISH AND REMOVE EXISTING CONSTRUCTION TO THE EXTENT INDICATED ON THE DRAWINGS, OR AS OTHERWISE NECESSARY TO ACCOMMODATE NEW CONSTRUCTION. USE METHODS REQUIRED TO COMPLETE WORK WITHIN LIMITATIONS OF GOVERNING REGULATIONS.
3. PROMPTLY PATCH AND REPAIR DAMAGED SURFACES IN ADJOINING CONSTRUCTION TO REMAIN, WHICH ARE CAUSED BY SELECTIVE DEMOLITION OPERATIONS.
4. THE OWNER WILL USE AND OCCUPY PORTIONS OF THE FACILITY AND SITE IMMEDIATELY ADJACENT TO SELECTIVE DEMOLITION AREA. CONDUCT SELECTIVE DEMOLITION SO THAT OWNER'S OPERATIONS WILL NOT BE DISRUPTED. PROVIDE NOT LESS THAN SEVEN (7) CALENDAR DAYS NOTICE TO THE COR OF ACTIVITIES THAT WILL AFFECT OWNER'S OPERATIONS.
5. THE OWNER ASSUMES NO RESPONSIBILITY FOR ACTUAL CONDITIONS OF COMPONENTS AND SITE ELEMENTS TO BE SELECTIVELY DEMOLISHED.
6. PROMPTLY DISPOSE OF DEMOLISHED MATERIALS OFF-SITE. DO NOT PERMIT DEMOLISHED MATERIALS TO ACCUMULATE ON-SITE. TRANSPORT DEMOLISHED MATERIALS OFF THE OWNER'S PROPERTY AND DISPOSE OF IN A SAFE AND LAWFUL MANNER.

EARTHWORK

1. THE CONTRACTOR SHALL RETAIN THE SERVICES OF A PROFESSIONAL GEOTECHNICAL ENGINEER, SUBJECT TO THE APPROVAL OF THE COR, TO PERFORM SOIL TESTING AND INSPECTION. THE CONTRACTOR'S ENGINEER SHALL INSPECT THE SUBGRADE TO VERIFY GEOTECHNICAL ENGINEERING DESIGN RECOMMENDATIONS. INSPECTION REPORTS SHALL BE SUBMITTED TO THE COR OUTLINING THE WORK PERFORMED AND TEST RESULTS.
2. PROVIDE SHEETING, SHORING, AND UNDERPINNING AS REQUIRED. REFER TO GENERAL NOTES BELOW.
3. EXCAVATION SHALL BE PERFORMED SO AS NOT TO DISTURB EXISTING ADJACENT BUILDINGS, STREETS AND UTILITY LINES. VERIFY LOCATION OF ALL UTILITIES PRIOR TO COMMENCEMENT OF WORK. INFORM AND OBTAIN REQUIRED PERMITS FROM OWNERS OF UTILITIES, AND COORDINATE WITH COR PRIOR TO WORK. HAND EXCAVATE AROUND UTILITIES AS REQUIRED.
4. STORM WATER CONDITIONS AT THE SITE AND TAKE THE NECESSARY PRECAUTIONS TO ENSURE THAT THE FOUNDATION EXCAVATIONS ARE PROTECTED AND REMAIN DRY DURING CONSTRUCTION. ANY SHEETING OR SHORING REQUIRED FOR DEWATERING IS THE RESPONSIBILITY OF THE CONTRACTOR. PROVIDE SUFFICIENT DEWATERING MEASURES TO MAINTAIN GROUND WATER IF ENCOUNTERED AT LEAST 2 FEET BELOW WORKING SUBGRADE.
5. REMOVE EXISTING VEGETATION, TOPSOIL AND UNSATISFACTORY SOIL MATERIALS. PROOF ROLL SUBGRADE TO OBTAIN UNIFORMLY DENSIFIED SUBSTRATA PRIOR TO PLACING FILL.
6. SATISFACTORY FILL MATERIALS ARE THOSE COMPLYING WITH ASTM D2487, GROUPS GW, GP, GM, SM, SW AND SP. ON SITE BORROW MATERIAL SHALL BE TESTED TO DETERMINE SUITABILITY FOR USE AS FILL MATERIAL.
7. ENGINEERED (CONTROLLED COMPACTED) FILL WITHIN THE BUILDING AREA SHALL BE CONSTRUCTED PRIOR TO FOOTING (OR PILE CAP) EXCAVATION. SEE SPECIFICATIONS FOR REQUIREMENTS ENGINEERED FILL.
8. PLACE FILL MATERIAL EVENLY IN 8" THICK (MAXIMUM) LAYERS AND COMPACTING TO REQUIRED DENSITY. COMPACT SOIL TO NOT LESS THAN THE FOLLOWING PERCENTAGES OF MAXIMUM DENSITY OF MODIFIED PROCTOR (ASTM D1557):
   - A. UNDER BUILDING FOUNDATIONS: 98%
   - B. UNDER BUILDING SLABS, STEPS PAVEMENTS: 95%
9. BACKFILL SHALL BE BROUGHT UP SIMULTANEOUSLY ON EACH SIDE OF WALLS AND GRADE BEAMS, WITH A GRADE DIFFERENCE NOT TO EXCEED 2'-0" AT ANY TIME.

FOUNDATIONS

1. FOUNDATIONS HAVE BEEN DESIGNED AND FOOTING ELEVATIONS ESTABLISHED ON THE BASIS OF EXISTING DRAWINGS.
2. ALLOWABLE BEARING CAPACITY: THE FOUNDATIONS ARE DESIGNED AND SHALL BEAR ON COMPACTED SUBGRADE CAPABLE OF SAFELY SUPPORTING 4,000 PSF BASED ON EXISTING DRAWINGS.
3. PRIOR TO FOOTING CONCRETE PLACEMENT, THE FOOTING SUBGRADE SHALL BE APPROVED BY THE INSPECTING GEOTECHNICAL ENGINEER. IF CONDITIONS PROVE TO BE UNACCEPTABLE AT THE WORKING ELEVATIONS, INSPECTING GEOTECHNICAL ENGINEER SHALL PROVIDE RECOMMENDATIONS TO ACHIEVE THE SPECIFIED DESIGN BEARING CAPACITY, SUBJECT TO THE APPROVAL OF THE COR.
4. THE BOTTOM OF EXTERIOR FOOTINGS SHALL BE A MINIMUM OF THREE (3'-0") FEET BELOW FINISHED GRADE, OR AS REQUIRED BY LOCAL BUILDING CODES.
5. THE BEARING ELEVATIONS OF NEW FOOTINGS ADJACENT TO EXISTING FOOTINGS ARE TO MATCH THE ADJACENT EXISTING FOOTING BEARING ELEVATIONS UNLESS INDICATED OTHERWISE ON PLANS.
6. SLABS ON GRADE SHALL BEAR ON MECHANICALLY COMPACTED SOIL CAPABLE OF SUPPORTING 150 PSF. DRAINAGE FILL UNDER SLABS SHALL BE COMPACTED GRAVEL OF CRUSHED STONE.
7. CONCRETE FOR FOUNDATIONS SHALL BE POURED ON THE SAME DAY THE SUBGRADE IS APPROVED BY THE GEOTECHNICAL ENGINEER.
8. UTILITY LINES SHALL NOT BE PLACED THROUGH OR BELOW FOUNDATIONS WITHOUT THE COR'S APPROVAL.
9. THE CONTRACTOR SHALL OBSERVE WATER CONDITIONS AT THE SITE AND TAKE THE NECESSARY PRECAUTIONS TO ENSURE THAT THE FOUNDATION EXCAVATIONS REMAIN DRY DURING CONSTRUCTION. ANY SHEETING OR SHORING REQUIRED FOR DEWATERING SHALL BE THE RESPONSIBILITY OF THE CONTRACTOR.
10. THE CONTRACTOR SHALL BE RESPONSIBLE FOR COORDINATING THE NEED TO USE FOUNDATION REBAR AS A GROUNDING ELECTRODE SYSTEM AND SHALL BE RESPONSIBLE FOR INSTALLING THE BONDING CLAP PRIOR TO PLACEMENT OF THE CONCRETE PER NEC 250-50.

SHEETING AND SHORING

1. SHEETING, SHORING AND ASSOCIATED EXCAVATION SHALL BE PERFORMED IN ACCORDANCE WITH OSHA GUIDELINES.
2. STRUCTURAL STEEL SOLDIER PILES AND RELATED MISCELLANEOUS FRAMING SHALL HAVE A MINIMUM YIELD STRESS OF 36,000 PSI. WELDING ELECTRODES SHALL BE E70.
3. CONCRETE SHALL HAVE A MINIMUM COMPRESSIVE STRENGTH OF 3,000 PSI AT 28 DAYS.

CAST-IN-PLACE CONCRETE

1. CONCRETE SHALL BE DESIGNED AND DETAILED IN ACCORDANCE WITH THE BUILDING CODE REQUIREMENTS FOR STRUCTURAL CONCRETE (ACI 318-19), AND CONSTRUCTED IN ACCORDANCE WITH THE CRSI MANUAL OF STANDARD PRACTICE.
2. CONCRETE SHALL HAVE MINIMUM COMPRESSIVE 28 DAY STRENGTH (F'C) AS FOLLOWS:
   - A. FOOTINGS: 5,000 PSI
   - B. SITE CONCRETE: 5,000 PSI
3. AIR ENTRAINMENT SHALL BE:
   - A. FOOTINGS: 6%
   - B. SITE CONCRETE: 6%
4. MAXIMUM WATER/CEMENT RATIOS:
   - A. FOOTINGS: 0.40
   - B. SITE CONCRETE: 0.40
5. ALL CONCRETE SHALL BE NORMAL WEIGHT CONCRETE (144 PCF +) UNLESS NOTED OTHERWISE.
6. ALL CEMENT CONFORMING TO ASTM C150, TYPE I.
7. MAXIMUM AGGREGATE SIZE SHALL BE 1 1/2" FOR FOOTINGS AND 3/4" FOR WALLS AND SLABS, CONFORMING TO ASTM C33.
8. REINFORCING STEEL: ASTM A615, GRADE 60.
9. WELDED WIRE REINFORCEMENT: (WWR) ASTM A-185, GRADE 65.
10. LEVELING GROUT SHALL BE NON-SHRINK, NON-METALLIC TYPE, FACTORY PRE-MIXED GROUT IN ACCORDANCE WITH CE-CRD-C621 OR ASTM C109, WITH A MINIMUM COMPRESSIVE 28 DAY STRENGTH OF 5,000 PSI.
11. REINFORCING STEEL CLEAR COVER SHALL BE AS FOLLOWS UNLESS NOTED OTHERWISE:
    - A. CONCRETE CAST AGAINST AND PERMANENTLY EXPOSED TO EARTH: 3"
    - B. CONCRETE EXPOSED TO EARTH OR WEATHER: 2"
    - C. CONCRETE NOT EXPOSED TO WEATHER OR IN CONTACT WITH GROUND:
      SLABS, WALLS & JOISTS #11 BARS AND SMALLER: 0.75"
      BEAMS AND COLUMNS: 1-1/2"
12. PRIOR TO PLACING BARS, SUBMIT TO COR REINFORCING STEEL SHOP DRAWINGS FOR APPROVAL.
13. ALL REINFORCEMENT SHALL BE SECURELY HELD IN PLACE WHILE PLACING CONCRETE. PROVIDE PLASTIC TIPPED BOLSTERS AND CHAIRS AT ALL LOCATIONS WHERE THE CONCRETE SURFACE IN CONTACT WITH THE BOLSTERS OF CHAIRS IS EXPOSED. IF REQUIRED, ADDITIONAL BARS, STIRRUPS OR CHAIRS SHALL BE PROVIDED BY THE CONTRACTOR TO FURNISH SUPPORT FOR ALL BARS.
14. SPLICES IN REINFORCING BARS SHALL BE LAPPED A MINIMUM OF 50 BAR DIAMETERS, UNLESS SHOWN OTHERWISE ON THE DRAWINGS OR CALCULATED IN ACCORDANCE WITH ACI 318 AND APPROVED BY THE COR.
15. LAP WELDED WIRE REINFORCEMENT TWO (2) FULL WIRE SPACES AT SPLICES AND WIRE TOGETHER.
16. ADHESIVE SHALL BE USED WHERE DOWELS ARE TO BE INSTALLED INTO EXISTING CONCRETE. ADHESIVE SHALL BE HILTI HIT-HY 200 OR APPROVED EQUAL.
17. PLACING OF CONCRETE SHALL NOT START UNTIL THE PLACEMENT OF REINFORCING HAS BEEN APPROVED BY THE THIRD-PARTY INSPECTION AGENCY.
18. PRIOR TO PLACING CONCRETE, SUBMIT THE FOLLOWING TO THE COR FOR REVIEW:
    - A. CONCRETE POUR SCHEDULE SHOWING THE LOCATION OF ALL PROPOSED CONSTRUCTION JOINTS AND WATERSTOPS.
    - B. CONCRETE MIX DESIGNS PREPARED IN ACCORDANCE WITH THE SPECIFICATION AND REQUIREMENTS INDICATED IN THE GENERAL NOTES.
19. BONDING AGENT SHALL BE USED WHERE NEW CONCRETE IS PLACED AGAINST EXISTING CONCRETE.
20. NO SLEEVE SHALL BE PLACED THOUGH ANY CONCRETE ELEMENT UNLESS SHOWN ON THE APPROVED SHOP DRAWINGS OR SPECIFICALLY AUTHORIZED IN WRITING BY THE COR. THE CONTRACTOR SHALL VERIFY DIMENSIONS AND LOCATIONS OF ALL SLOTS, PIPE SLEEVES, ETC. AS REQUIRED FOR MEP TRADES BEFORE CONCRETE IS PLACED.
21. PIPES OR CONDUITS PLACED IN SLABS SHALL NOT HAVE AN OUTSIDE DIAMETER LARGER THAN 1/3 THE SLAB THICKNESS AND SHALL NOT BE SPACED CLOSER THAN THREE (3) DIAMETERS ON CENTER. ALUMINUM CONDUITS SHALL NOT BE PLACED IN CONCRETE. NO CONDUITS SHALL BE PLACED IN SLABS WITHIN 12" OF COLUMN FACE OR FACE OF BEARING WALL. NO CONDUITS MAY BE PLACED IN EXTERIOR SLABS OR SLABS SUBJECTED TO FLUIDS.
22. CONCRETE SHALL NOT BE PUMPED THROUGH ALUMINUM PIPES AND SHALL NOT BE PLACED IN CONTACT WITH ALUMINUM FORMS, MIXING DRUMS, BUGGIES, CHUTES, CONVEYORS OR OTHER EQUIPMENT MADE OF ALUMINUM.
23. ALL INSERTS AND SLEEVES SHALL BE CAST-IN-PLACE WHENEVER FEASIBLE. DRILLED OR POWDER DRIVEN FASTENERS WILL BE PERMITTED WHEN PROVEN TO THE SATISFACTION OF THE COR THAT THE FASTENERS WILL NOT SPALL THE CONCRETE AND HAVE THE SAME CAPACITY AS CAST-IN-PLACE INSERTS.
24. WHEN INSTALLING EXPANSION BOLTS OR ADHESIVE ANCHORS, THE CONTRACTOR SHALL TAKE MEASURES TO AVOID DRILLING OR CUTTING OF ANY EXISTING REINFORCING AND DESTRUCTION OF CONCRETE. HOLES SHALL BE BLOWN CLEAN PRIOR TO PLACING BOLTS OR ADHESIVE ANCHORS.
25. PROVIDE 3/4" CHAMFER ALL EXPOSED CONCRETE CORNERS UNLESS NOTED OTHERWISE ON ARCHITECTURAL DRAWINGS.
26. THE CONCRETE SLABS SHALL BE FINISHED FLAT AND LEVEL WITHIN TOLERANCE, TO THE ELEVATION INDICATED ON THE DRAWINGS. THE CONTRACTOR SHALL PROVIDE ADDITIONAL CONCRETE REQUIRED DUE TO FORMWORK, METAL DECK AND FRAMING DEFLECTION TO ACHIEVE THIS FINISHED TOP OF SLAB ELEVATION.
27. CONSTRUCTION JOINTS FOR MILD-REINFORCED CONCRETE SHALL BE LOCATED WITHIN THE MIDDLE THIRD OF SPAN. PROPOSED CONSTRUCTION JOINT LOCATIONS SHALL BE SHOWN ON REINFORCING STEEL SHOP DRAWINGS. ANY STOP IN CONCRETE WORK MUST BE MADE WITH VERTICAL BULKHEADS AND HORIZONTAL KEYS, UNLESS OTHERWISE SHOWN. ALL REINFORCING IS TO BE CONTINUOUS THROUGH JOINTS.
28. EARLY DRYING OUT OF CONCRETE, ESPECIALLY DURING THE FIRST 24 HOURS, SHALL BE CAREFULLY GUARDED AGAINST. ALL SURFACES SHALL BE MOIST CURED OR PROTECTED USING A MEMBRANE CURING AGENT APPLIED AS SOON AS FORMS ARE REMOVED. IF MEMBRANE CURING AGENT IS USED, EXERCISE CARE NOT TO DAMAGE COATING.
29. CONCRETE PLACEMENT IS IN ACCORDANCE WITH ACI-301. IN ADDITION TO ACI-301, COLD WEATHER CONCRETING SHALL BE IN ACCORDANCE WITH ACI-306 AND HOT WEATHER CONCRETING SHALL BE IN ACCORDANCE WITH ACI-305R.
30. THROUGHOUT CONSTRUCTION, THE CONCRETE WORK SHALL BE ADEQUATELY PROTECTED AGAINST DAMAGE DUE TO EXCESSIVE LOADING, CONSTRUCTION EQUIPMENT, MATERIALS OR METHODS, ICE, RAIN, SNOW, EXCESSIVE HEAT AND FREEZING TEMPERATURES.
31. CONTRACTOR SHALL RETAIN TESTING AGENCY TO PROVIDE FIELD AND LABORATORY TESTING SERVICES. TESTING AGENCY SHALL PROVIDE TESTS AS OUTLINED. RESULTS OF ALL TESTS SHALL BE REPORTED TO COR IN TIMELY MANNER:
    ON-SITE, SAMPLE FRESH CONCRETE IN ACCORDANCE WITH ASTM C172:
    - A. SLUMP PER ASTM C143L
    - B. AIR CONTENT PER ASTM C231 OR C173
    - C. TEMPERATURE PER ASTM C1064
    - D. CONCRETE TEST CYLINDERS PER ASTM C31.

GENERAL STRUCTURAL & CONSTRUCTION NOTES

STRUCTURAL STEEL

1. FABRICATION AND ERECTION OF STRUCTURAL STEEL SHALL CONFORM TO "THE MANUAL OF STEEL CONSTRUCTION", FIFTEENTH EDITION, 2017, AMERICAN INSTITUTE OF STEEL CONSTRUCTION INCLUDING SPECIFICATIONS FOR STRUCTURAL STEEL BUILDINGS.
2. ALL WELDING SHALL BE PERFORMED BY CERTIFIED WELDERS AND SHALL CONFORM TO "STRUCTURAL WELDING CODE ANSI/AWS D1.1", AMERICAN WELDING SOCIETY.
3. WIDE FLANGE SHAPES: ASTM A992, GRADE 50
4. STRUCTURAL SHAPES & PLATES: ASTM A36, A572
5. STEEL PIPE: ASTM A53, GRADE B
6. STEEL TUBING: ASTM A500, GRADE B
7. GALVANIZED STRUCTURAL STEEL:
   A. STRUCTURAL SHAPES AND RODS: ASTM A123.
   B. BOLTS, FASTENERS AND HARDWARE: ASTM F2329.
8. ALL BOLTED CONNECTIONS SHALL BE WITH ASTM F3125, GRADE A325 HIGH STRENGTH BOLTS 3/4" MINIMUM DIAMETER, UNLESS NOTED OTHERWISE.
9. ALL BOLTED CONNECTIONS ON WIND BRACING MEMBERS AND COLUMNS SHALL BE SLIP CRITICAL CONNECTIONS.
10. ANCHOR RODS SHALL CONFORM TO ASTM F1554, GRADE 55, HOT-DIP GALVANIZED, UNLESS NOTED OTHERWISE.
11. WELDING ELECTRODES SHALL BE E70XX FOR MANUAL ARC WELDING AND F7X-EXXX FOR SUBMERGED ARC WELDING. ALL WELDERS SHALL BE CERTIFIED BY THE AWS. MINIMUM WELD SIZE SHALL BE 3/16" UNLESS NOTED OTHERWISE.
12. WELDING OF REINFORCING BARS TO OTHER BARS OR STRUCTURAL STEEL: E90-XX ELECTRODE.
13. CUTS, HOLES, COPING, ETC. REQUIRED FOR OTHER TRADES OF FIELD CONDITIONS SHALL BE SHOWN ON THE SHOP DRAWINGS AND MADE IN THE SHOP. CUTTING OR BURNING OF MAIN STRUCTURAL MEMBERS IN THE FIELD WILL NOT BE PERMITTED.
14. SUBMIT SHOP DRAWINGS FOR FABRICATION AND ERECTION OF STRUCTURAL STEEL. CLEARLY INDICATE COORDINATED DIMENSIONS OF MECHANICAL UNIT AND ROOF PENETRATION SIZES. SHOP AND ERECTION DRAWINGS MUST SHOW ALL SHOP/FLOOR AND FIELD WELDS. INITIAL SHOP DRAWING SUBMITTAL SHALL INCLUDE PROPOSED CONNECTION DETAILS AND JOB STANDARDS. PROVIDE SIGNED AND SEALED CALCULATIONS FOR ALL NON-STANDARD CONNECTION DETAILS SHOWING DESIGN CAPACITIES.
15. STEEL MEMBERS SHOWN ON PLAN SHALL BE EQUALLY SPACED UNLESS NOTED OTHERWISE.
16. CAMBER INDICATED ON THESE DRAWINGS IS THE REQUIRED CAMBER AFTER FINAL ERECTION AND INCLUDES ALL MILL TOLERANCES.
17. ALL CONNECTIONS SHALL BE "FRAMED BEAM CONNECTIONS" DESIGNED IN ACCORDANCE WITH THE AISC MANUAL AND THE ENDS REACTIONS FROM THE "UNIFORM LOAD TABLES", BUT NOT LESS THAN 6 KIPS. PROVIDE DOUBLE ANGLE CONNECTIONS OR KNIFE PLATES CONNECTIONS FULL DEPTH OF SUPPORTING BEAM, UNLESS OTHERWISE APPROVED. MINIMUM TWO (2) BOLTS PER CONNECTION. UNLESS OTHERWISE NOTED, COMPOSITE BEAMS TO BE DESIGNED 80% OF THE "TOTAL" UNIFORM LOAD CAPACITY. SINGLE ANGLE OF SHEAR TAB CONNECTIONS ARE NOT ACCEPTABLE. ALL BEAM TO COLUMN CONNECTIONS SHALL BE DESIGNED FOR THE MINIMUM SHEAR REACTION INDICATED ABOVE IN COMBINATION WITH A 10 KIP AXIAL FORCE (ACTING IN BOTH TENSION AND COMPRESSION).
18. ALTERNATE CONNECTION DETAILS MAY BE USED IF SUCH DETAILS ARE SUBMITTED TO THE COR FOR REVIEW AND APPROVAL. HOWEVER, THE COR SHALL BE THE SOLE JUDGE OF ACCEPTANCE AND THE CONTRACTOR'S BID SHALL ANTICIPATE THE USE OF THOSE DETAILS THAT HE PROPOSES.
19. FIELD-WELDED SURFACES WITHIN FOUR (4) INCHES OF WELD SHALL BE CLEANED AND GROUND SMOOTH. AFTER WELDING COAT THE EXPOSED AREA WITH APPROPRIATE PRIMER, PAINTS, AND/OR FIREPROOFING AS SPECIFIED.
20. FIELD-WELDED GALVANIZED SURFACES WITHIN FOUR (4) INCHES OF WELD SHALL BE CLEANED AND GROUND SMOOTH. AFTER WELDING COAT THE EXPOSED AREA WITH GALVANIZING REPAIR PAINT. GALVANIZING REPAIR PAINT SHALL BE A HIGH ZINC DUST CONTENT PAINT COMPLYING WITH FEDERAL SPECIFICATIONS DOD-P-21035A OR SSPC-PAINT-20, COLD GALVANIZING COMPOUND BY ZRC PRODUCTS CO. OR EQUAL.
21. ALL BRACING OR TRUSS CONNECTIONS, WHICH HAVE NOT BEEN SPECIFICALLY DETAILED, SHALL BE DESIGNED BY A PROFESSIONAL ENGINEER REGISTERED IN THE PROJECT'S JURISDICTION FOR THE FORCES NOTED ON THE ELEVATIONS AND DETAILS. THIS SHALL INCLUDE ALL GUSSET PLATES, FILLER PLATES, ANGLES, STIFFENERS, BOLTS OR WELDS, OR OTHER MATERIAL REQUIRED FOR THE CONNECTION. STAMPED CALCULATIONS FOR THE CONNECTION DESIGN SHALL BE SUBMITTED ALONG WITH THE SHOP DRAWINGS FOR REVIEW BY THE COR.
22. GUSSET PLATE CONNECTIONS SHALL BE SIZED FOR 100% OF THE AXIAL FORCE CAPACITY OF THE BRACING MEMBER. DESIGN ALL GUSSET PLATES AND CONNECTORS AS REQUIRED FOR COMPLIANCE WITH AISC. PROVIDE STIFFENER PLATES AS REQUIRED AT THE GUSSET PLATE CONNECTIONS.
23. THE NET AREA (REFER TO AISC SECTION B2 AND B3) AT THE CONNECTION OF ANY BRACING MEMBER SHALL NOT BE LESS THAN 85 PERCENT OF THE GROSS CROSS SECTIONAL AREA OF THE MEMBER. ADDITIONAL PLATES SHALL BE ADDED AS NECESSARY TO MAINTAIN THE MINIMUM NET CROSS SECTIONAL AREA. SUCH PLATES SHALL EXTEND A MINIMUM DISTANCE EQUAL TO THE DEPTH OF THE MEMBER PAST THE LAST ROW IF BOLTS.
24. ALL CONNECTIONS SHALL BE SYMMETRICAL ABOUT THE AXIS OF THE MEMBER CONNECTED. PROVIDE ONLY ONE GRADE OF BOLT FOR EACH BOLT DIAMETER TO BE USED IN THE CONNECTIONS. DO NOT MIX GRADE OF BOLTS.
25. BEAMS AND GIRDERS SHALL HAVE BEAM WEB HOLES AS INDICATED ON THE STRUCTURAL DRAWINGS. ALL HOLES SHALL BE CENTERED AT MID-DEPTH OF THE BEAM UNLESS OTHERWISE NOTED. ALL RECTANGULAR WEB HOLES SHALL HAVE A MINIMUM CORNER RADIUS OF 5/8" OR TWICE THE THICKNESS OF THE BEAM WEB, WHICHEVER IS GREATER. ALL WEB OPENINGS SHALL BE MACHINE OXYGEN CUT. MANUAL CUTTING OR BURNING IS NOT PERMITTED. COORDINATE LOCATION AND SIZE OF HOME WITH MECHANICAL CONTRACTOR PRIOR TO REVIEW BY THE COR.
26. STEEL ANGLES AND PLATES ALONG WITH BOLTS AND WASHERS, IN DIRECT CONTACT WITH EXTERIOR FINISH MASONRY AND ALL EXTERIOR EXPOSED STRUCTURAL STEEL, SHALL BE HOT-DIPPED GALVANIZED PER ASTM A123.
27. ALL GUARDRAILS, CHAINS, AND SAFETY GATES SHALL BE PAINTED SAFETY YELLOW.
28. ALL EXTERIOR EXPOSED STRUCTURAL STEEL SHALL BE HOT-DIPPED GALVANIZED PER ASTM A123.
29. ALL DISSIMILAR METALS SHALL BE TREATED OR PROPERLY SEPARATED TO PREVENT GALVANIC AND/OR CORROSIVE EFFECTS.
30. MAIN SUPPORT MEMBERS FOR THE METAL GRATING ARE SHOWN. DURING PREPARATION, SUBMISSION AND REVIEW OF SHOP DRAWINGS, ANY ADDITIONAL ANGLES OR MISCELLANEOUS ATTACHMENT DETAILS REQUIRED TO SUPPORT THE METAL GRATING AT THE REQUIRED ELEVATION SHALL BE PROVIDED BY THE STRUCTURAL STEEL CONTRACTOR.
31. THE GENERAL CONTRACTOR AND STEEL ERECTOR SHALL NOTIFY THE COR OF ANY FABRICATION OR ERECTION ERRORS OR DEVIATIONS AND RECEIVE WRITTEN APPROVAL BEFORE ANY FIELD CORRECTIONS ARE MADE.
32. VISUALLY INSPECT ALL FIELD WELDS. 10% OF ALL FIELD FILLET WELDS IN PRIMARY CONNECTIONS AND MULTI-PASS WELDS SHALL BE TESTED BY THE MAGNETIC PARTICLE METHOD, COMPLYING WITH E109, PERFORMED ON THE ROOT PASS AND ON THE FINISHED WELD.
33. 100% OF FULL PENETRATION WELDS SHALL HAVE ULTRASONIC INSPECTION, COMPLYING WITH ASTM E164.
34. 100% OF WELDS IN BEAM AND COLUMN MOMENT CONNECTIONS SHALL HAVE ULTRASONIC INSPECTION, COMPLYING WITH ASTM E164.
35. FIELD TEST BOLTED CONNECTIONS IN ACCORDANCE WITH AISC.

STEEL GRATING

1. STEEL GRATING SHALL BE MANUFACTURED IN ACCORDANCE WITH THE METAL BAR GRATING MANUAL BY THE NATIONAL ASSOCIATION OF ARCHITECTURAL METAL MANUFACTURERS AND SHALL CONFORM TO FEDERAL SPECIFICATION RR-G-661E, TYPE 1, CLASS 1. STEEL FOR GRATING SHALL BE ASTM A569. ALL GRATING SHALL BE GALVANIZED AND ATTACHED WITH REMOVABLE TYPE FASTENERS.

BEARING PADS

1. ELASTOMERIC PADS: AASHTO M251, PLAIN, VULCANIZED, 100 PERCENT POLYCHLOROPRENE (NEOPRENE) ELASTOMER, MOLDED TO SIZE OR CUT FROM A MOLDED SHEET, 50 TO 70 SHORE A DUROMETER ACCORDING TO ASTM D2240, MINIMUM TENSILE STRENGTH 15.5 MPA (2250 PSI) PER ASTM D412.
2. RANDOM-ORIENTED, FIBER-REINFORCED ELASTOMERIC PADS: PREFORMED, RANDOMLY ORIENTED SYNTHETIC FIBERS SET IN ELASTOMER. SURFACE HARDNESS OF 70 TO 90 SHORE A DUROMETER ACCORDING TO ASTM D2240. CAPABLE OF SUPPORTING A COMPRESSIVE STRESS OF 20.7 MPA (3000 PSI) WITH NO CRACKING, SPLITTING OR DELAMINATING IN THE INTERNAL PORTIONS OF THE PAD. TEST ONE SPECIMEN FOR EACH 200 PADS USED IN THE PROJECT. SUBMIT TEST RESULTS.
3. COTTON-DUCK-FABRIC-REINFORCED ELASTOMERIC PADS: PREFORMED, HORIZONTALLY LAYERED COTTON-DUCK FABRIC BONDED TO AN ELASTOMER. SURFACE HARDNESS OF 80 TO 100 SHORE A DUROMETER ACCORDING TO ASTM D2240. CONFORMING TO DIVISION II, SECTION 18.10.2 OF AASHTO LRFD, OR MIL-C-882E.
4. FRICTIONLESS PADS: TETRAFLUOROETHYLENE (TEFLON), GLASS-FIBER REINFORCED, BONDED TO STAINLESS OR MILD-STEEL PLATES, OF TYPE REQUIRED FOR IN-SERVICE STRESS.
5. HIGH-DENSITY PLASTIC: MULTIMONOMER, NONLEACHING, PLASTIC STRIP.

MEP EQUIPMENT

1. ALL NEW MECHANICAL EQUIPMENT SHALL BE BOLTED TO THE CONCRETE PADS OR STEEL SUPPORTS IN ACCORDANCE WITH THE MANUFACTURER'S RECOMMENDATION BUT NOT LESS THAN 5/ 8" DIAMETER BOLTS AT 30" ON CENTER MAXIMUM.
2. CONTRACTOR SHALL SUBMIT SHOP DRAWINGS INDICATING COORDINATION BETWEEN FINAL MEP EQUIPMENT SELECTION AND PROPOSED SUPPORTING STRUCTURE. SHOP DRAWINGS SHALL SHOW LOCATION AND SIZE OF ALL ANCHOR BOLTS, CENTERLINES OF BEAMS, AND UNIT DIMENSIONS INCLUDING OVERALL DIMENSIONS AND CENTERLINES OF ATTACHMENT POINTS.

DESIGN DATA

1. GOVERNING CODES
   A. 2021 INTERNATIONAL BUILDING CODE
   B. ACI BUILDING CODE REQUIREMENTS FOR STRUCTURAL CONCRETE - ACI318
   C. AISC MANUAL OF STEEL CONSTRUCTION
   D. AWS STEEL WELDING CODES - AWS D1.1
   E. STEEL DECK INSTITUTE MANUAL
   F. DEPARTMENT OF VETERANS AFFAIRS PROGRAM GUIDE PG-18-15
   G. DEPARTMENT OF VETERANS AFFAIRS STRUCTURAL DESIGN MANUAL
   H. DEPARTMENT OF VETERANS AFFAIRS SEISMIC DESIGN REQUIREMENTS H-18-8
2. DESIGN DATA
   RISK CATEGORY: IV
3. FLOOR LIVE LOAD
   NURSING AND OUTPATIENT AREAS: 60 PSF (1988 DRAWINGS)
   OPERATING ROOM AREAS: 80 PSF
   SUPPORT AREAS: 100 PSF (1988 DRAWINGS)
   LOBBIES: 100 PSF (1988 DRAWINGS)
   STAIRS: 100 PSF (1988 DRAWINGS)
   LIGHT STORAGE: 150 PSF (1988 DRAWINGS)
   MECHANICAL: 150 PSF (1988 DRAWINGS)
   PARTITIONS (ALL AREAS): 25 PSF (1988 DRAWINGS)
   MEP & CEILING: 15 PSF
4. ROOF LIVE LOAD
   MINIMUM LIVE LOAD: 20 PSF
   ROOF LIVE LOAD: 30 PSF (1988 DRAWINGS)
   SNOW LOAD
   PG (GROUND SNOW LOAD): 30 PSF
   CE (SNOW EXPOSURE FACTOR): 0.9
   I (SNOW LOAD IMPORTANCE FACTOR): 1.2
   CT (THERMAL FACTOR): 1.0
   PF (FLAT SNOW LOAD): 24 PSF (ROOF)
   PF (FLAT SNOW LOAD): 27 PSF (UNITS)
5. WIND LOAD
   BASIC WIND SPEED: 121 MPH
   WIND EXPOSURE: B
6. EARTHQUAKE DESIGN DATA
   SITE CLASSIFICATION: D (ASSUMED)
   SS: 0.197
   STAIRS: 0.210
   S1: 0.064
   SD1: 0.102
   SEISMIC DESIGN CATEGORY: C

PRINTS OF THIS DRAWING SHALL NOT BE USED FOR ANY PURPOSE WHATSOEVER WITHOUT THE SEAL AND SIGNATURE OF THE PROFESSIONAL ENGINEER

Revisions:	Date:

CONSULTANT

Architecture:	Civil Engineering:	Fire Protection:
PF&A DESIGN, P.C.	LABELLA ASSOCIATES	STANTON ENGINEERING SERVICES, LLC

ENGINEER OF RECORD

MILLER-REMICK

A Service-Disabled Veteran-Owned Small Business

(856) 429-4000 • Miller-Remick.com

MILLER-REMICK LLC
PROFESSIONAL ENGINEER

COMMONWEALTH OF VIRGINIA
ANTHONY DANIEL PACARO JR.
Lic. No. 402055020
PROFESSIONAL ENGINEER

12 30 2025

Office of Construction and Facilities Management

VA U.S. Department of Veterans Affairs

Drawing Title: STRUCTURAL NOTES	Phase: BID DOCUMENTS	Project Title: RENOVATE SURGICAL SUITE PHASE II	VA Drawing Number: 2617
Approved by: Jon Manninen, COR	FULLY SPRINKLERED	Project Number: 658-19-103	Building Number: 143
		Location: SALEM VA MEDICAL CENTER	Drawing Number: S-002
		Issue Date: 2025-12-30 / Checked: FL / Drawn: DS	

12/29/2025 1:05:15 PM

VA FORM 08 - 6231

GENERAL SHEET NOTES:

1. FOR GENERAL STRUCTURAL NOTES SEE DRAWING S-001 AND S-002.
2. COORDINATE EQUIPMENT PADS WITH MECH AND ELEC DRAWINGS.
3. ALL DIMENSIONS FOR CONCRETE EQUIPMENT PADS AND FOUNDATIONS ARE APPROXIMATE. VERIFY WITH FINAL UNIT SELECTIONS. SEE 1,2/SS501.
4. FOR CONCRETE WORK, REFER TO SPECIFICATIONS SECTION 03-30-53.

PLAN NOTES:

1. REMOVE EXISTING CONCRETE EQUIPMENT PAD TO A SMOOTH SURFACE TO MATCH EXISTING, VIF.
2. ANCHOR EQUIPMENT PER MFR REQUIREMENT; ANCHOR 3 1/2" MAX EMBEDMENT INTO EXIST SLAB UNLESS APPROVED BY EOR.
3. CONTRACTOR TO VERIFY IN THE FIELD POSSIBLE CLASH BETWEEN CHILLER FOUNDATION AND (E) UTILITY TUNNEL. IF CONFLICT EXIST NOTIFY COR/EOR PRIOR TO COMMENCEMENT OF WORK.

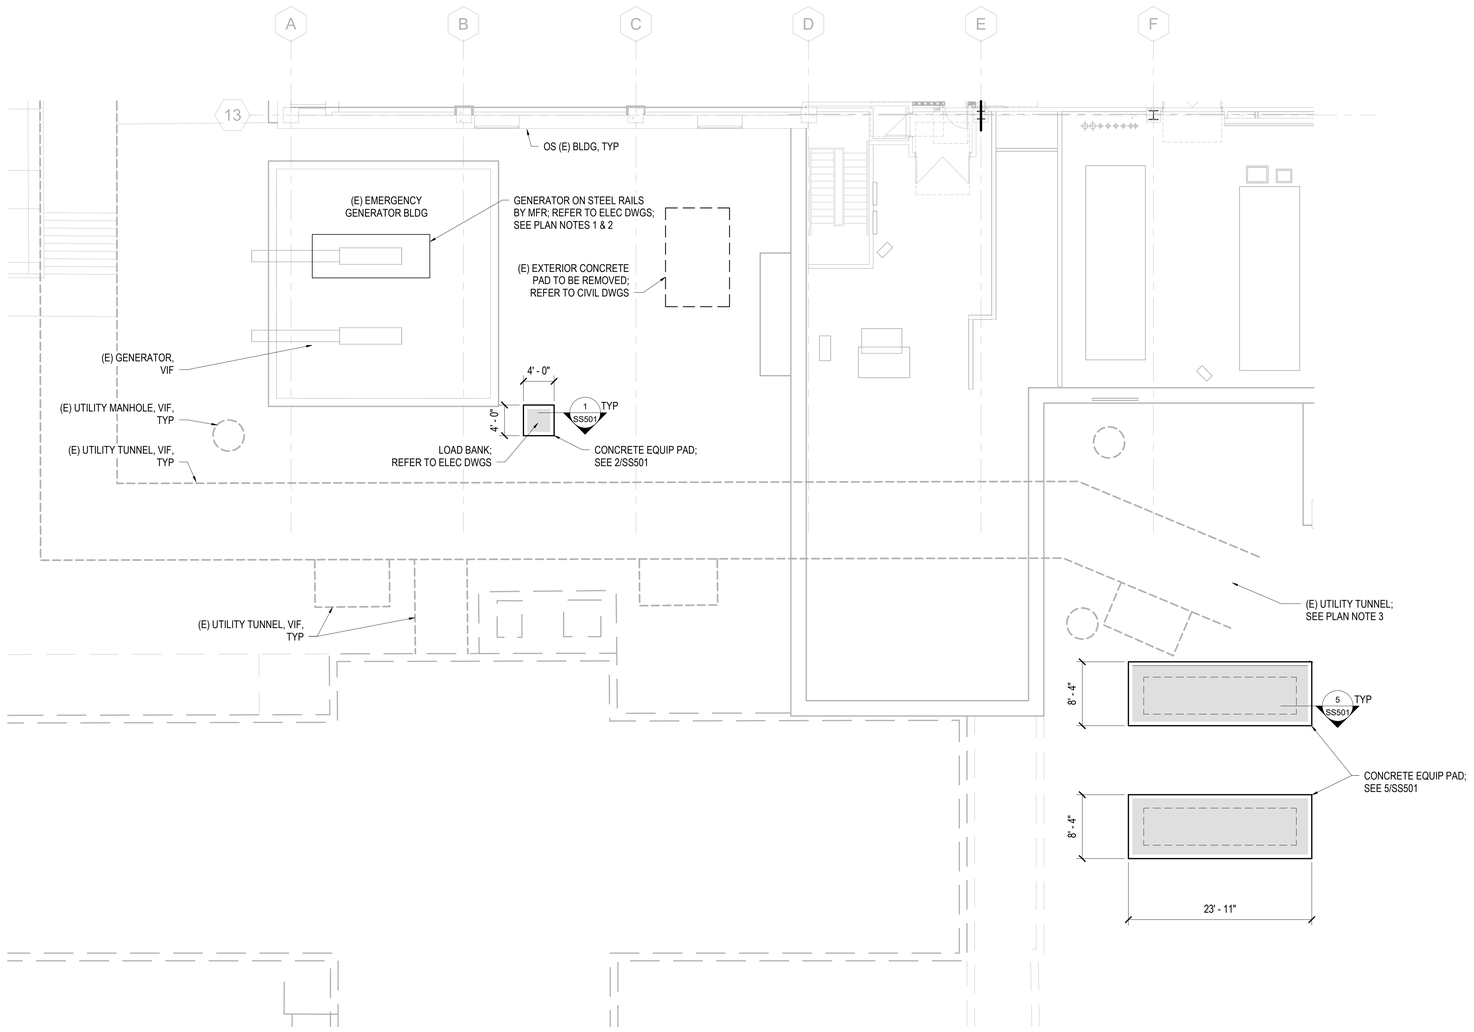

1 SITE PLAN
SCALE: 1/8" = 1'-0"

PLAN NORTH
ACTUAL NORTH

PRINTS OF THIS DRAWING SHALL NOT BE USED FOR ANY PURPOSE WHATSOEVER WITHOUT THE SEAL AND SIGNATURE OF THE PROFESSIONAL ENGINEER

Revisions:	Date:

12/29/2025 1:03:19 PM

VA FORM 08 - 6231

CONSULTANT

Architecture:	Civil Engineering:	Fire Protection:
PF&A DESIGN, P.C.	LABELLA ASSOCIATES	STANTON ENGINEERING SERVICES, LLC

ENGINEER OF RECORD

MILLER-REMICK
A Service-Disabled Veteran-Owned Small Business
(856) 429-4000 • Miller-Remick.com
18 Industrial Park, Voorhees

MILLER-REMICK LLC PROFESSIONAL ENGINEER

COMMONWEALTH OF VIRGINIA
ANTHONY DANIEL PACARD JR
Lic. No. 402055020
PROFESSIONAL ENGINEER
12.30.2025

Office of Construction and Facilities Management

VA U.S. Department of Veterans Affairs

Drawing Title STRUCTURAL SITE PLAN	**Phase** BID DOCUMENTS	**Project Title** RENOVATE SURGICAL SUITE PHASE II	**VA Drawing Number** 2617
Approved by: Jon Manninen, COR	FULLY SPRINKLERED	**Project Number** 658-19-103	**Building Number** 143
		Location SALEM VA MEDICAL CENTER	**Drawing Number** SS101
		Issue Date 2025-12-30 / **Checked** FL / **Drawn** DS	

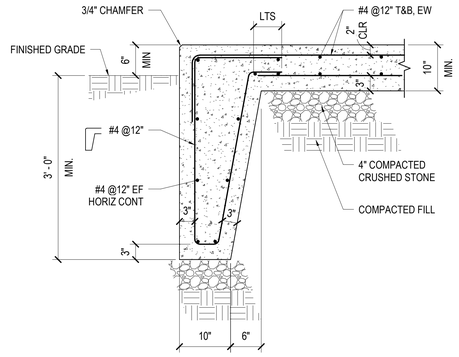

NOTES:
1. EQUIPMENT PAD SIZE TO SUIT FINAL EQUIPMENT SELECTION, REFER TO MEP DWGS.
2. FOR EQUIPMENT ATTACHMENT SEE DETAIL 3/SS501.

1 EQUIPMENT PAD EXTERIOR DETAIL
SCALE: 1" = 1'-0"

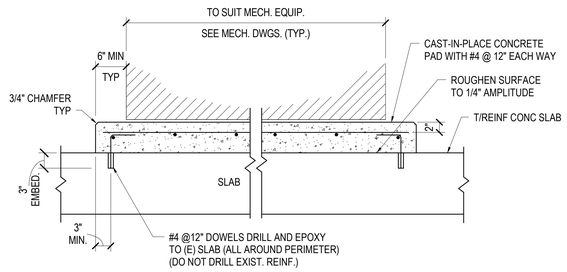

NOTES:
1. PROVIDE 4" THICK PAD FOR INTERIOR.
2. SIZE TO SUIT FINAL EQUIPMENT SELECTION, REFER TO MEP DWGS.
3. ANCHOR MEP EQUIPMENT TO CONCRETE PAD PER MFR'S REQUIREMENTS OR AS SHOWN IN DETAIL 3/SS501 (WHICHEVER IS MORE STRENGENT).
4. INTERIOR PADS TO BE PAINTED SAFETY-YELLOW ON SIDES AND EXPOSED SURFACES.
5. PERFORM NON-DESTRUCTIVE TESTING TO LOCATE EXISTING REBAR. DO NOT CUT OR DRILL EXISTING REBAR.

2 EQUIPMENT PAD INTERIOR DETAIL
SCALE: 1" = 1'-0"

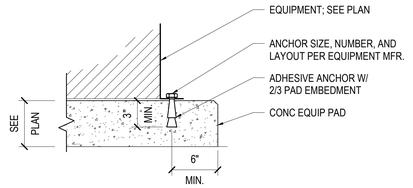

NOTES:
1. ANCHOR MEP EQUIPMENT TO CONCRETE PAD PER MFR'S REQUIREMENTS OR AS SHOWN (WHICHEVER IS MORE STRENGENT).
2. INTERIOR PADS TO BE PAINTED SAFETY-YELLOW ON SIDES AND EXPOSED SURFACES.

3 ANCHOR TO PAD ATTACHMENT DETAIL
SCALE: 1 1/2" = 1'-0"

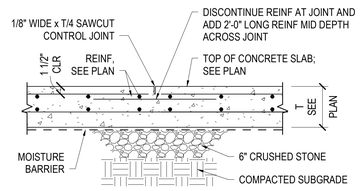

NOTES:
1. PROVIDE CONTROL JOINTS @12" OC EACH WAY MAXIMUM OR AS INDICATED ON PLANS WITHIN 8 HOURS FROM POURING CONCRETE.

4 SLAB CONTROL JOINT TYPICAL DETAIL
SCALE: 1" = 1'-0"

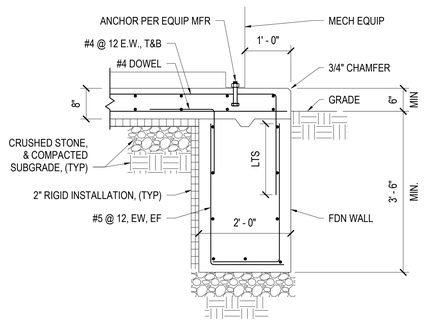

5 CHILLER FOUNDATION DETAIL
SCALE: 3/4" = 1'-0"

PRINTS OF THIS DRAWING SHALL NOT BE USED FOR ANY PURPOSE WHATSOEVER WITHOUT THE SEAL AND SIGNATURE OF THE PROFESSIONAL ENGINEER

Revisions:	Date:

CONSULTANT

Architecture:	Civil Engineering:	Fire Protection:
PF&A DESIGN, P.C.	LABELLA ASSOCIATES	STANTON ENGINEERING SERVICES, LLC

ENGINEER OF RECORD

MILLER-REMICK LLC
PROFESSIONAL ENGINEER

COMMONWEALTH OF VIRGINIA
ANTHONY DANIEL PACARO JR.
Lic. no. 402055020
PROFESSIONAL ENGINEER
12.30.2025

Office of Construction and Facilities Management

VA U.S. Department of Veterans Affairs

Drawing Title: STRUCTURAL SECTIONS & DETAILS	Phase: BID DOCUMENTS	Project Title: RENOVATE SURGICAL SUITE PHASE II	VA Drawing Number: 2617
		Project Number: 658-19-103	Building Number: 143
Approved by: Jon Manninen, COR	FULLY SPRINKLERED	Location: SALEM VA MEDICAL CENTER	Drawing Number: SS501
		Issue Date: 2025-12-30 / Checked: FL / Drawn: DS	

12/29/2025 1:02:06 PM

VA FORM 08 - 6231

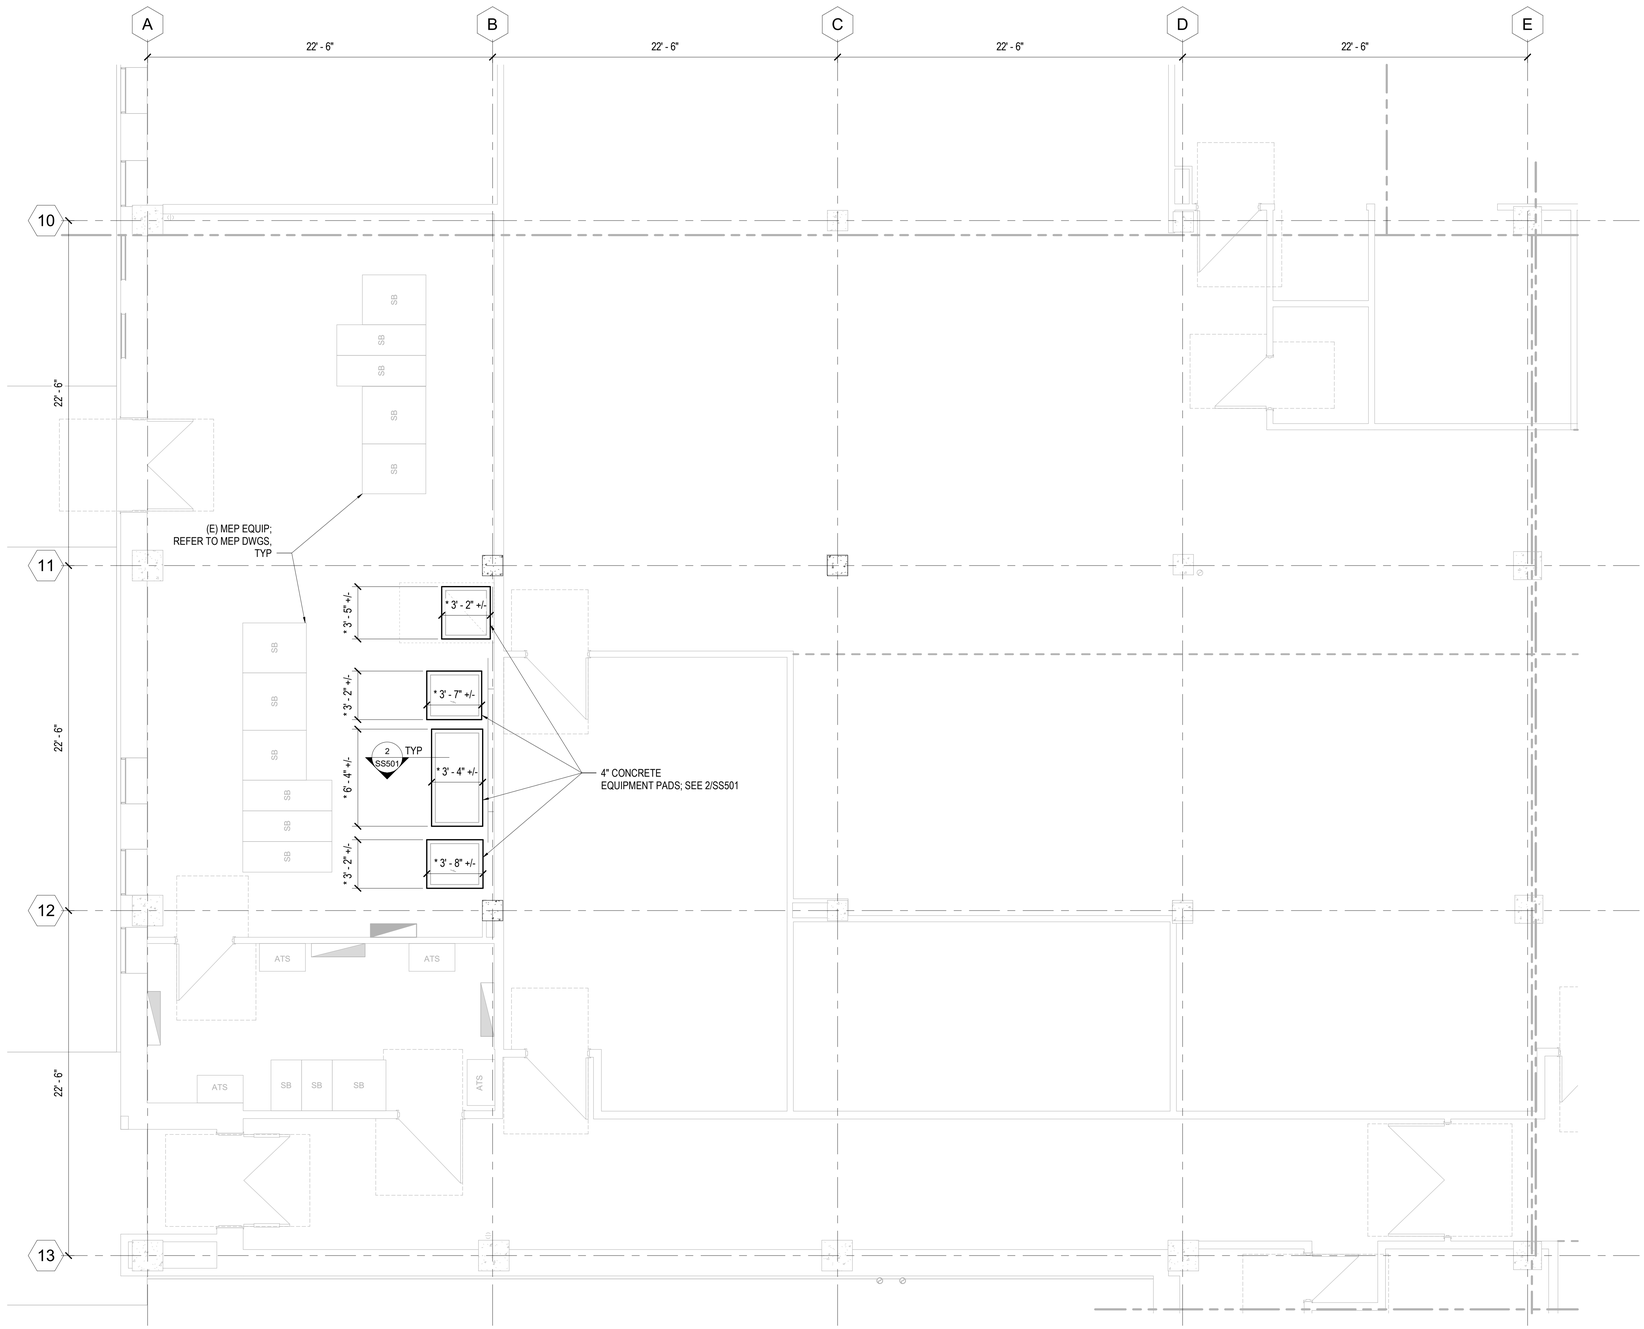

1 BASEMENT PLAN - PHASE 1
SCALE: 1/4" = 1'-0"

GENERAL SHEET NOTES:

1. FOR GENERAL STRUCTURAL NOTES SEE DRAWING S-001 AND S-002.
2. REFER TO MECHANICAL AND ARCHITECTURAL DRAWINGS FOR ALL MECHANICAL EQUIPMENT SIZES AND LOCATIONS.
3. FOR CONCRETE WORK, REFER TO SPECIFICATIONS SECTION 03-30-53.
4. TOP OF (E) SLAB ELEVATION = 1091.89 UNLESS OTHERWISE NOTED.
5. (E) REINFORCED CONCRETE SLAB THICKNESS = 8 1/2".
6. (E) DROP PANEL SIZE = 8' - 6" SQUARE BY 3 1/2" BELOW SLAB.
7. (E) STEEL COLUMNS ARE ENCASED BY CONCRETE, SIZED 22"X22" COLUMNS.
8. * INDICATES COORDINATION ITEM. FINAL EQUIPMENT PAD SIZE TO BE COORDINATED AFTER PROCURING THE FINAL EQUIPMENT FROM SELECTED MANUFACTURER.
8. FOR CONCRETE WORK, REFER TO SPECIFICATIONS SECTION 03-30-53.

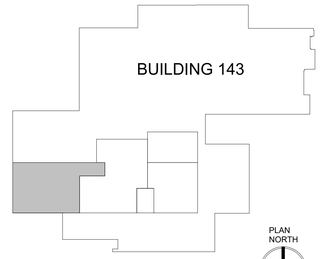

KEYPLAN

PRINTS OF THIS DRAWING SHALL NOT BE USED FOR ANY PURPOSE WHATSOEVER WITHOUT THE SEAL AND SIGNATURE OF THE PROFESSIONAL ENGINEER

Revisions: | Date:

CONSULTANT

Architecture:	Civil Engineering:	Fire Protection:
PF&A DESIGN, P.C.	LABELLA ASSOCIATES	STANTON ENGINEERING SERVICES, LLC

ENGINEER OF RECORD

MILLER-REMICK LLC
PROFESSIONAL ENGINEER

COMMONWEALTH OF VIRGINIA
ANTHONY DANIEL PACARO JR.
Lic. No. 402055070
PROFESSIONAL ENGINEER
12.30.2025

Office of Construction and Facilities Management

VA U.S. Department of Veterans Affairs

Drawing Title: STRUCTURAL BASEMENT PLAN PHASE 1	Phase: BID DOCUMENTS	Project Title: RENOVATE SURGICAL SUITE PHASE II	VA Drawing Number: 2617
Approved by: Jon Manninen, COR	FULLY SPRINKLERED	Project Number: 658-19-103	Building Number: 143
		Location: SALEM VA MEDICAL CENTER	Drawing Number: P1-SF101
		Issue Date: 2025-12-30 / Checked: FL / Drawn: DS	

12/29/2025 1:06:35 PM

VA FORM 08 - 6231

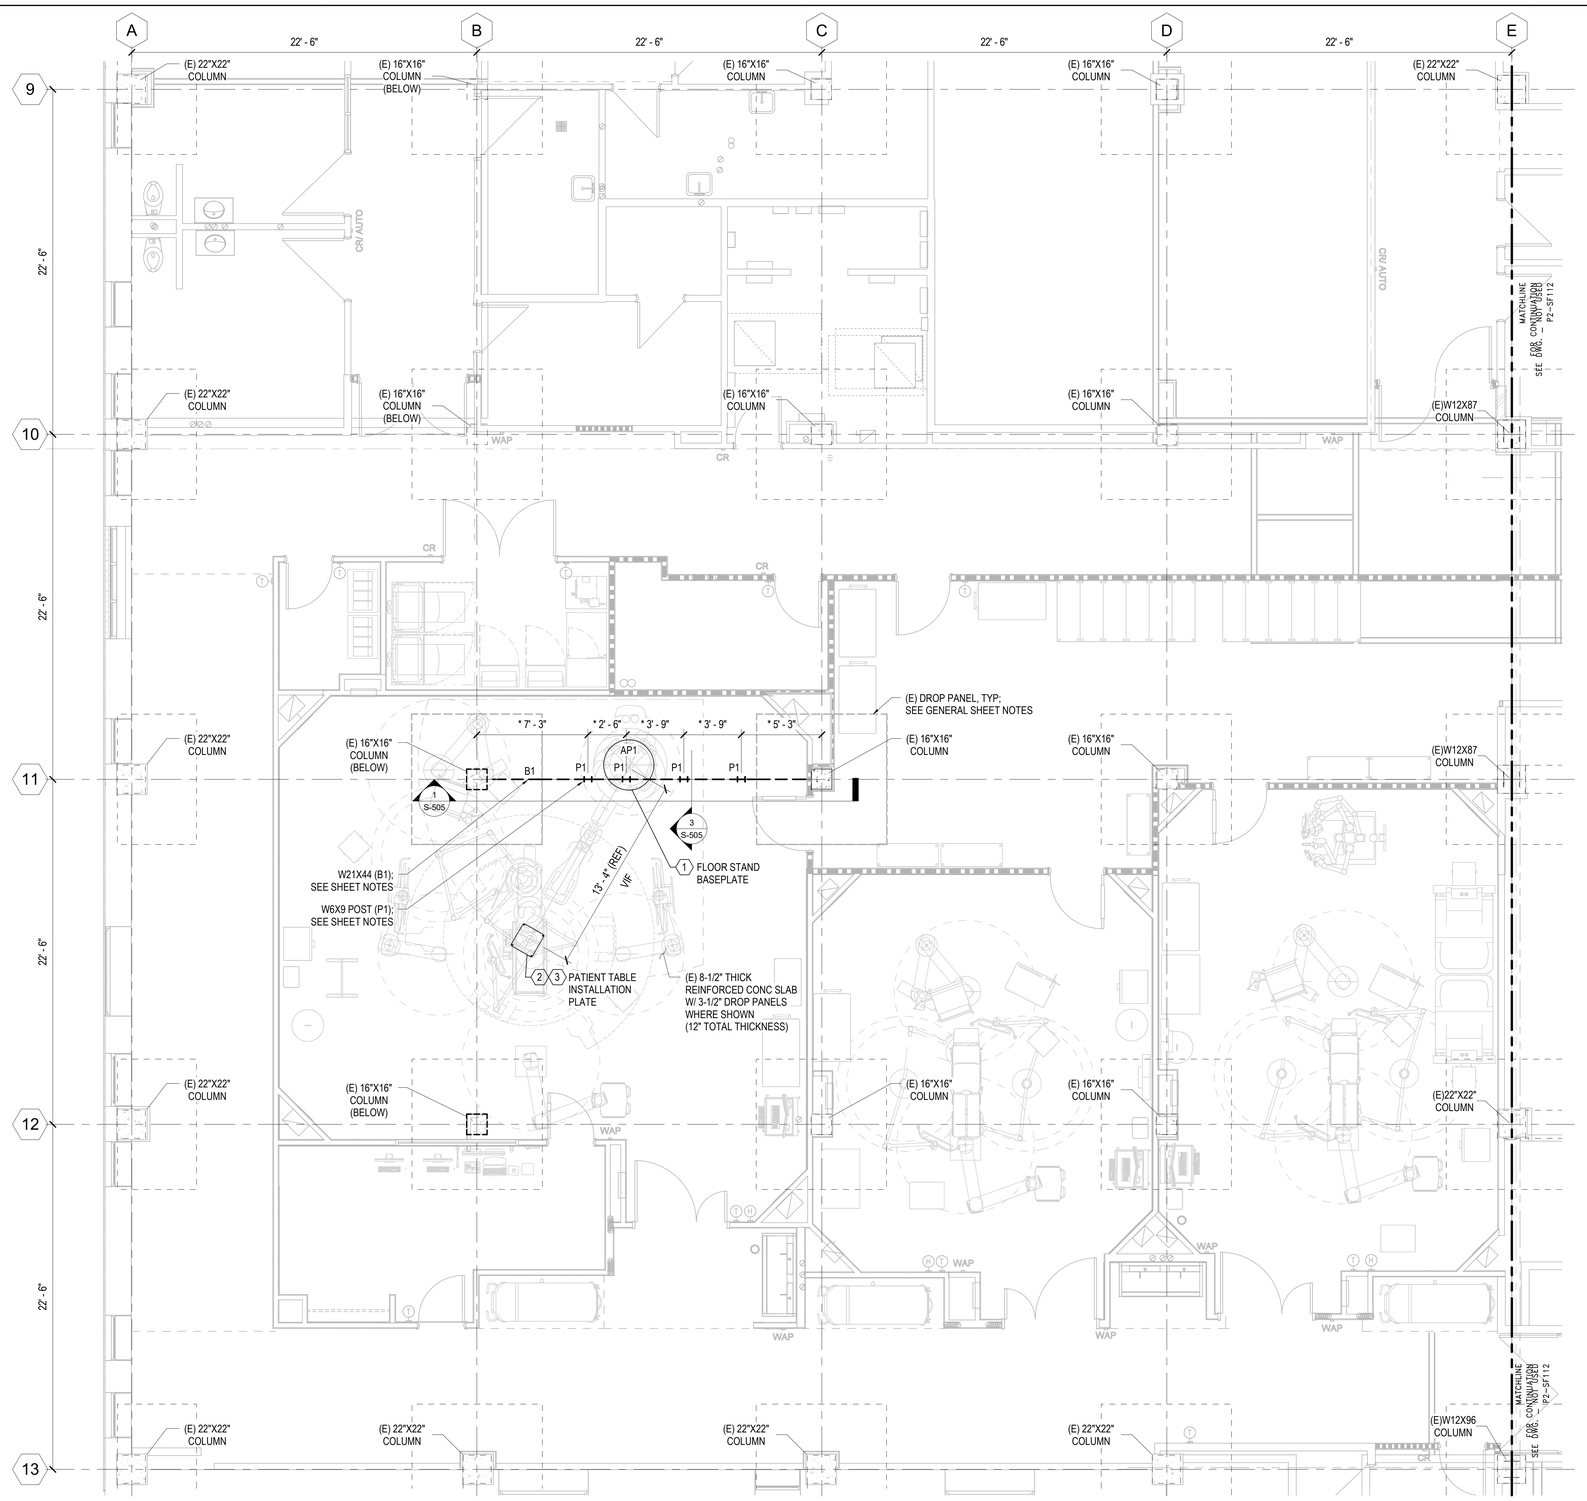

1 FRAMING PLAN - 1ST FLOOR, PHASE 1
SCALE: 1/4" = 1'-0"

GENERAL SHEET NOTES:

1. FOR GENERAL STRUCTURAL NOTES SEE DRAWING S-001 AND S-002.
2. REFER TO MECHANICAL AND ARCHITECTURAL DRAWINGS FOR ALL MECHANICAL EQUIPMENT SIZES AND LOCATIONS.
3. FOR CONCRETE WORK, REFER TO SPECIFICATIONS SECTION 03-30-53.
4. TOP OF (E) SLAB ELEVATION = 1104.91 UNLESS OTHERWISE NOTED.
5. (E) REINFORCED CONCRETE SLAB THICKNESS = 8 1/2".
6. (E) DROP PANEL SIZE = 8' - 6" SQUARE BY 3 1/2" BELOW SLAB.
7. (E) STEEL COLUMNS ARE ENCASED BY CONCRETE, SIZED 22"X22" COLUMNS.
8. * DENOTES COORDINATE FINAL LOCATION FOR CLEARANCES OF EXISTING AND NEW DUCTS, PIPES, AND CONDUITS. NOTIFY COR/EOR OF ANY IMPEDIMENTS.
9. P1 DENOTES VERTICAL POST SUPPORTED BY BEAM AND TO BE LOCATED TO AVOID CONFLICT WITH EXISTING CONDUIT AND DUCTS. POSTS WILL BE EPOXIED TO UNDERSIDE OF SLAB AT APPRX. 2'-0" ON CENTER. SEE DETAILS 3&4/S-505.
10. B1 DENOTES BEAM ACTS AS BOTTOM CHORD WITH VERTICAL POSTS (P1) CONNECTED TO BOTTOM OF EXISTING SLAB. COLUMN STRIP SLAB ACTS AS TOP CHORD. SEE DETAIL 1/S-505.
11. BEAM WILL BE PLACED LOWER TO AVOID EXISTING CONDUIT AND DUCTS. BEAM WILL BE SUPPORTED BY COLUMNS WITH EPOXIED ANCHORS PLACED BELOW DROP PANEL.
12. AP1 DENOTES ARTIS PHENO EQUIPMENT THAT WILL BE SUPPLIED BY SEIMENS ENGINEERING. SEIMENS REPRESENTATIVE, CONTRACTOR, AND INSTALLER TO COORDINATE EQUIPMENT FASTENING TO SLAB WITH THE COR DUE TO POTENTIAL CONFLICTS WITH BASEMENT CEILING DUCTS, CONDUITS, AND PIPES.

KEY NOTES:

1. INSTALL FLOOR STAND BASEPLATE. STAND SHALL BE INSTALLED FLUSH AGAINST CONCRETE SURFACE; DO NOT INSTALL ON FLOOR FINISH. INSTALL UTILIZING THREADED RODS & FASTENING PLATE (SUPPLIED BY SIEMENS). SEE SIEMENS INSTALLATION DRAWING S-101 FOR ADDITIONAL INFORMATION.
2. CORE DRILL 5" DIA HOLE THRU EXISTING CONCRETE SLAB FOR PATIENT TABLE CABLE OPENING. SEE SIEMENS INSTALLATION DRAWINGS.
3. INSTALL PATIENT TABLE INSTALLATION PLATE. PLATE SHALL BE INSTALLED FLUSH AGAINST CONCRETE SURFACE; DO NOT INSTALL ON FLOOR FINISH. INSTALL UTILIZING (4) HILTI HSL-3 EXPANSION BOLTS, M12/25 (SUPPLIED BY SIEMENS). SEE SIEMENS INSTALLATION DRAWING S-101 FOR ADDITIONAL INFORMATION.

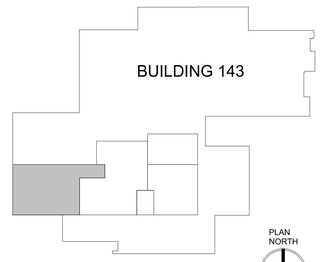

KEYPLAN

PRINTS OF THIS DRAWING SHALL NOT BE USED FOR ANY PURPOSE WHATSOEVER WITHOUT THE SEAL AND SIGNATURE OF THE PROFESSIONAL ENGINEER

Revisions: | Date:

CONSULTANT

Architecture:	Civil Engineering:	Fire Protection:
PF&A DESIGN, P.C.	LABELLA ASSOCIATES	STANTON ENGINEERING SERVICES, LLC

ENGINEER OF RECORD

MILLER-REMICK LLC PROFESSIONAL ENGINEER

COMMONWEALTH OF VIRGINIA — C. ANTHONY DANIEL PACARO JR. — Lic. No. 402055020 — PROFESSIONAL ENGINEER — 12.30.2025

MILLER•REMICK
A Service-Disabled Veteran-Owned Small Business
(856) 429-4000 • Miller-Remick.com
M-R PROJECT NO. 0409-2026

Office of Construction and Facilities Management

VA U.S. Department of Veterans Affairs

Drawing Title	STRUCTURAL FRAMING PLAN 1ST FLOOR, PHASE 1
Phase	BID DOCUMENTS
Project Title	RENOVATE SURGICAL SUITE PHASE II
Project Number	658-19-103
VA Drawing Number	2617
Building Number	143
Approved by:	Jon Manninen, COR
	FULLY SPRINKLERED
Location	SALEM VA MEDICAL CENTER
Issue Date	2025-12-30
Checked	FL
Drawn	DS
Drawing Number	P1-SF111

12/29/2025 1:06:21 PM

VA FORM 08 - 6231

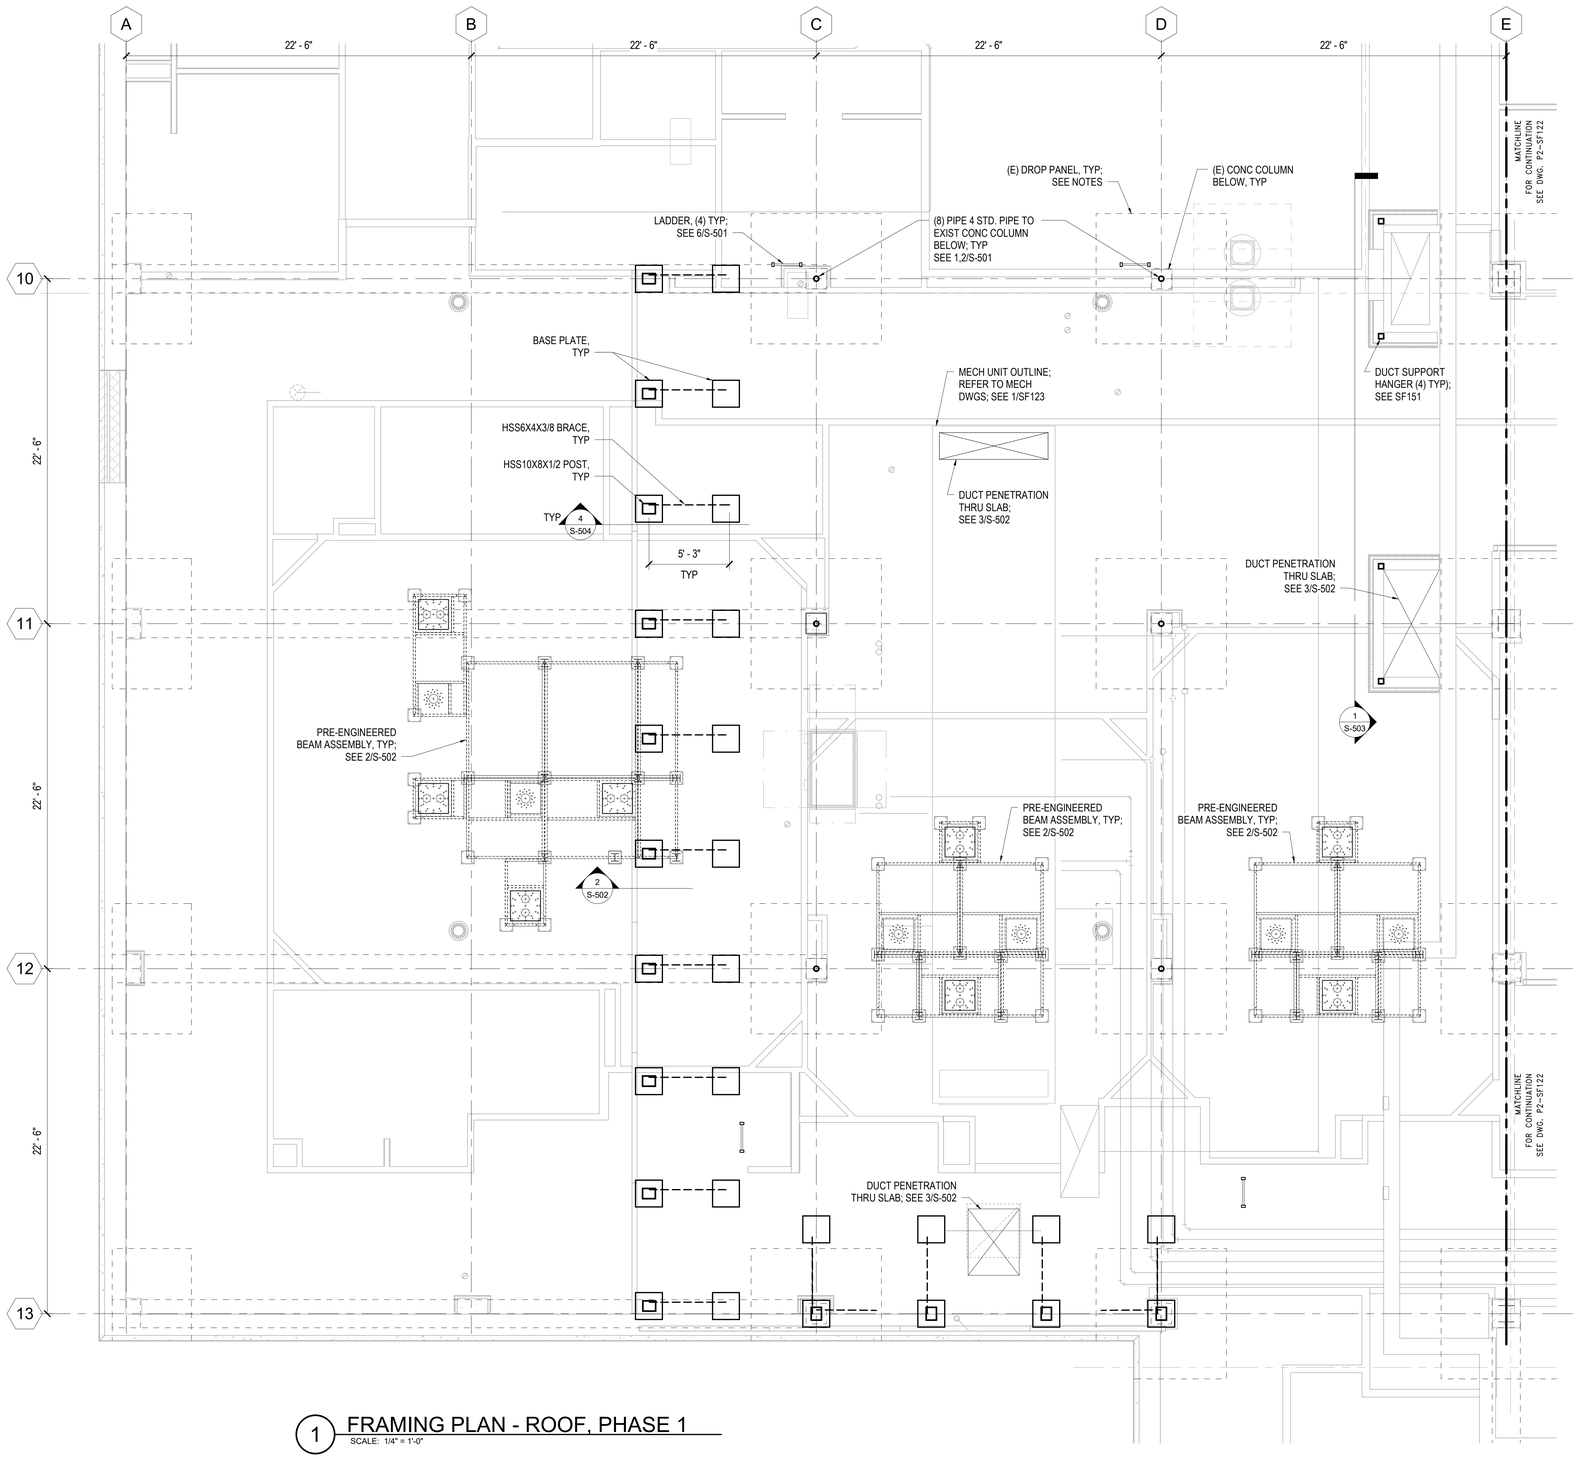

1 FRAMING PLAN - ROOF, PHASE 1
SCALE: 1/4" = 1'-0"

GENERAL SHEET NOTES:

1. FOR GENERAL STRUCTURAL NOTES SEE DRAWING S-001 AND S-002.
2. REFER TO MECHANICAL AND ARCHITECTURAL DRAWINGS FOR ALL MECHANICAL EQUIPMENT SIZES AND LOCATIONS.
3. FOR CONCRETE WORK, REFER TO SPECIFICATIONS SECTION 03-30-53.
4. T/STEEL ELEVATION FOR DUNNAGE STEEL IS +2'-1 1/2" ABOVE T/(E) ROOF STEEL.
5. FOR ROOFING AND FINISHES, REFER TO ARCHITECTURAL DRAWINGS.
6. LOCATE AND MEASURE CENTERLINE DIMENSIONS OF EXISTING MEMBERS PRIOR TO FABRICATION OF NEW SUPPORTS. NEW SUPPORT STEEL SHALL BE LOCATED ONLY ON CENTERLINE OF EXISTING MEMBERS.
7. PROVIDE STRUCTURAL STEEL DUNNAGE FOR MECHANICAL EQUIPMENT, COORDINATE WITH MECHANICAL DRAWINGS AND FINAL UNIT SELECTION.
8. SHORE EXISTING ROOF SLAB PRIOR TO DEMOLITION.
9. REMOVE PORTIONS OF EXISTING ROOF SLAB REQUIRED FOR INSTALLATION OF DUCTWORK. SEE MECHANICAL DRAWINGS AND SF123.
10. INSTALL SINGLE ROD AND OR DOUBLE ROD GRAVITY SUPPORT AS REQUIRED. SEE S-502.
11. INSTALL PIPE POSTS FOR ROOF-TOP AHU SUPPORT STEEL DUNNAGE. SEE SF123.
12. * DENOTES TO COORDINATE FINAL DIMENSIONS AND LOCATION ACCORDING TO THE SELECTED EQUIPMENT SIZES, CLEARANCES OF DUCTS, AHU, PIPES, AND CONDIUT. NOTIFY COR/EOR OF ANY IMPEDIMENTS.
13. PLAN SHOWS 2ND FLOOR STRUCTURAL FRAMING (1ST FL. CEILING).
14. REPRESENTS ESTIMATED LOCATION OF CONNECTION FROM PRE-ENGINEERED HVAC SYSTEM TO SUPPLEMENTAL STRUCTURE ABOVE, REFER TO DETAILS ON S-502. PROVIDE CONNECTION AT MODULE CORNERS, BOOM OUTRIGGERS, AND WHERE REQUIRED BY BOOM AND/OR HVAC PLENUM MANUFACTURERS.
15. GRAVITY SUPPORT FRAMING SHOWN FOR REFERENCE ONLY. ALL REQUIRED FRAMING SHALL BE COORDINATED WITH MANUFACTURERS AND EXISTING STRUCTURAL STEEL. CONTRACTOR TO RETAIN PROFESSIONAL ENGINEER TO DESIGN ALL SUPPLEMENTAL FRAMING INCLUDING BUT NOT LIMITED TO BEAMS, RODS, HANGERS, CONNECTIONS, AND SEISMIC BRACING. REFER TO DETAILS AND SPECIFICATIONS.
16. ALL SUPPLEMENTAL FRAMING SHALL BE DESIGNED FOR STRENGTH AND SERVICE/DEFLECTION AS REQUIRED BY HVAC AND BOOM MANUFACTURERS. W8 SHALL BE THE MINIMUM MEMBER SIZE. COORDINATE FLANGE WIDTHS FOR CLEARANCE, STRENGTH, DEFLECTION, AND HANGING CONNECTION ATTACHMENTS.
17. CONTRACTOR TO COORDINATE WITH EQUIPMENT MANUFACTURER FOR INSTALLATION OF STRUCTURAL EQUIPMENT SUPPORTS. DRILLED AND EPOXIED ANCHORS ARE TO AVOID EXISTING REBAR. FIELD VERIFY PLACEMENT OF EXISTING REBAR.

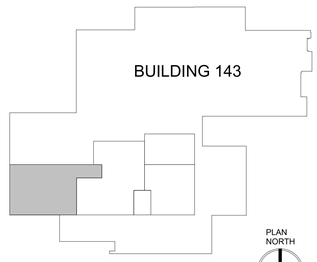

KEYPLAN

PRINTS OF THIS DRAWING SHALL NOT BE USED FOR ANY PURPOSE WHATSOEVER WITHOUT THE SEAL AND SIGNATURE OF THE PROFESSIONAL ENGINEER

Revisions: | Date:

CONSULTANT

Architecture:	Civil Engineering:	Fire Protection:
PF&A DESIGN, P.C.	LABELLA ASSOCIATES	STANTON ENGINEERING SERVICES, LLC

ENGINEER OF RECORD

MILLER-REMICK
A Service-Disabled Veteran-Owned Small Business
(856) 429-4000 • Miller-Remick.com
54 S. Route 73, Ste. 200, Voorhees, NJ

MILLER-REMICK LLC
PROFESSIONAL ENGINEER

COMMONWEALTH OF VIRGINIA
ANTHONY DANIEL PACARO JR.
Lic. no. 402055039
PROFESSIONAL ENGINEER
12-30-2025

Office of Construction and Facilities Management

VA U.S. Department of Veterans Affairs

Drawing Title	STRUCTURAL FRAMING PLAN ROOF, PHASE 1
Approved by:	Jon Manninen, COR
Phase	BID DOCUMENTS
	FULLY SPRINKLERED
Project Title	RENOVATE SURGICAL SUITE PHASE II
Project Number	658-19-103
Location	SALEM VA MEDICAL CENTER
Issue Date	2025-12-30
Checked	FL
Drawn	DS
VA Drawing Number	2617
Building Number	143
Drawing Number	P1-SF121

12/29/2025 1:06:08 PM

VA FORM 08 - 6231

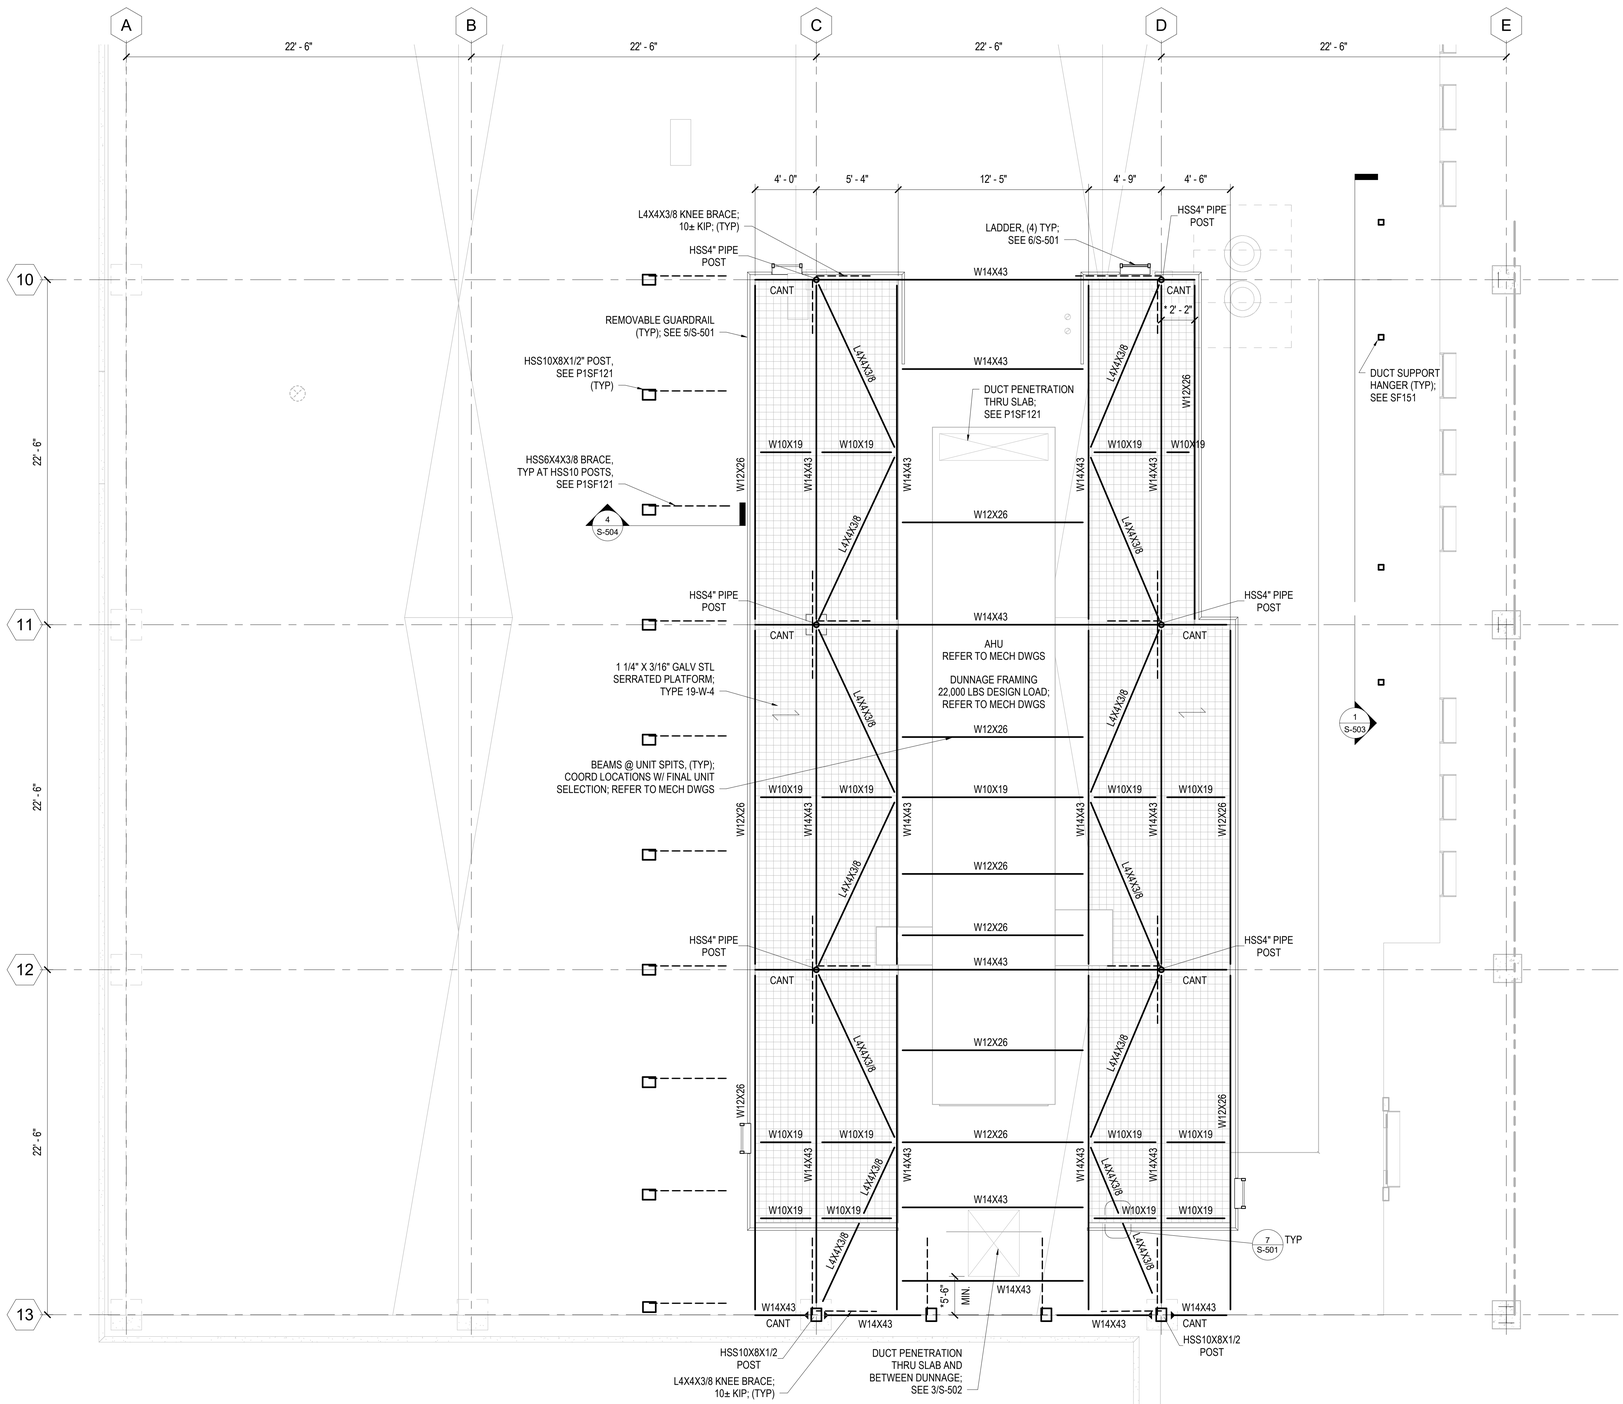

1 DUNNAGE FRAMING PLAN - LOW ROOF, PHASE 1
SCALE: 1/4" = 1'-0"

GENERAL SHEET NOTES:

1. FOR GENERAL STRUCTURAL NOTES SEE DRAWING S-001 AND S-002.
2. REFER TO MECHANICAL AND ARCHITECTURAL DRAWINGS FOR ALL MECHANICAL EQUIPMENT SIZES AND LOCATIONS.
3. FOR CONCRETE WORK, REFER TO SPECIFICATIONS SECTION 03-30-53.
4. T/STEEL ELEVATION FOR DUNNAGE STEEL IS +2'-1 1/2" ABOVE T/(E) ROOF STEEL.
5. FOR ROOFING AND FINISHES, REFER TO ARCHITECTURAL DRAWINGS.
6. LOCATE AND MEASURE CENTERLINE DIMENSIONS OF EXISTING MEMBERS PRIOR TO FABRICATION OF NEW SUPPORTS. NEW SUPPORT STEEL SHALL BE LOCATED ONLY ON CENTERLINE OF EXISTING MEMBERS.
7. PROVIDE STRUCTURAL STEEL DUNNAGE FOR MECHANICAL EQUIPMENT, COORDINATE WITH MECHANICAL DRAWINGS AND FINAL UNIT SELECTION.
8. SHORE EXISTING ROOF SLAB PRIOR TO DEMOLITION.
9. REMOVE PORTIONS OF EXISTING ROOF SLAB REQUIRED FOR INSTALLATION OF DUCTWORK. SEE MECHANICAL DRAWINGS AND SF123.
10. INSTALL SINGLE ROD AND OR DOUBLE ROD GRAVITY SUPPORT AS REQUIRED. SEE S-502.
11. INSTALL PIPE POSTS FOR ROOF-TOP AHU SUPPORT STEEL DUNNAGE. SEE SF123.
12. * DENOTES TO COORDINATE FINAL DIMENSIONS AND LOCATION ACCORDING TO THE SELECTED EQUIPMENT SIZES, CLEARANCES OF DUCTS, AHU, PIPES, AND CONDIUT. NOTIFY COR/EOR OF ANY IMPEDIMENTS.
13. PLAN SHOWS 2ND FLOOR STRUCTURAL FRAMING (1ST FL. CEILING).
14. REPRESENTS ESTIMATED LOCATION OF CONNECTION FROM PRE-ENGINEERED HVAC SYSTEM TO SUPPLEMENTAL STRUCTURE ABOVE, REFER TO DETAILS ON S-502. PROVIDE CONNECTION AT MODULE CORNERS, BOOM OUTRIGGERS, AND WHERE REQUIRED BY BOOM AND/OR HVAC PLENUM MANUFACTURERS.
15. GRAVITY SUPPORT FRAMING SHOWN FOR REFERENCE ONLY. ALL REQUIRED FRAMING SHALL BE COORDINATED WITH MANUFACTURERS AND EXISTING STRUCTURAL STEEL. CONTRACTOR TO RETAIN PROFESSIONAL ENGINEER TO DESIGN ALL SUPPLEMENTAL FRAMING INCLUDING BUT NOT LIMITED TO BEAMS, RODS, HANGERS, CONNECTIONS, AND SEISMIC BRACING. REFER TO DETAILS AND SPECIFICATIONS.
16. ALL SUPPLEMENTAL FRAMING SHALL BE DESIGNED FOR STRENGTH AND SERVICE/DEFLECTION AS REQUIRED BY HVAC AND BOOM MANUFACTURERS. W8 SHALL BE THE MINIMUM MEMBER SIZE. COORDINATE FLANGE WIDTHS FOR CLEARANCE, STRENGTH, DEFLECTION, AND HANGING CONNECTION ATTACHMENTS.
17. CONTRACTOR TO COORDINATE WITH EQUIPMENT MANUFACTURER FOR INSTALLATION OF STRUCTURAL EQUIPMENT SUPPORTS. DRILLED AND EPOXIED ANCHORS ARE TO AVOID EXISTING REBAR. FIELD VERIFY PLACEMENT OF EXISTING REBAR.

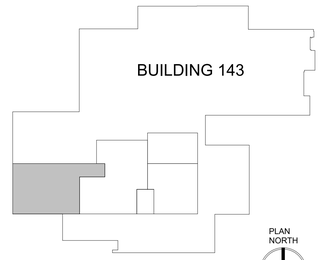

KEYPLAN

PRINTS OF THIS DRAWING SHALL NOT BE USED FOR ANY PURPOSE WHATSOEVER WITHOUT THE SEAL AND SIGNATURE OF THE PROFESSIONAL ENGINEER

Revisions:	Date:

CONSULTANT

Architecture:	Civil Engineering:	Fire Protection:
PF&A DESIGN, P.C.	LABELLA ASSOCIATES	STANTON ENGINEERING SERVICES, LLC

ENGINEER OF RECORD

MILLER•REMICK
A Service-Disabled Veteran-Owned Small Business
(856) 429-4000 • Miller-Remick.com
M-R PROJECT NO. 0499-0036

MILLER-REMICK LLC
PROFESSIONAL ENGINEER
COMMONWEALTH OF VIRGINIA
ANTHONY DANIEL PACARDO JR.
Lic. No. 0402055078
PROFESSIONAL ENGINEER
12-30-2025

Office of Construction and Facilities Management

VA U.S. Department of Veterans Affairs

Drawing Title	STRUCTURAL DUNNAGE FRAMING PLAN ROOF, PHASE 1
Approved by:	Jon Manninen, COR
Phase	BID DOCUMENTS
	FULLY SPRINKLERED
Project Title	RENOVATE SURGICAL SUITE PHASE II
Project Number	658-19-103
Location	SALEM VA MEDICAL CENTER
Issue Date	2025-12-30
Checked	FL
Drawn	DS
VA Drawing Number	2617
Building Number	143
Drawing Number	P1-SF123

12/29/2025 1:05:52 PM

VA FORM 08 - 6231

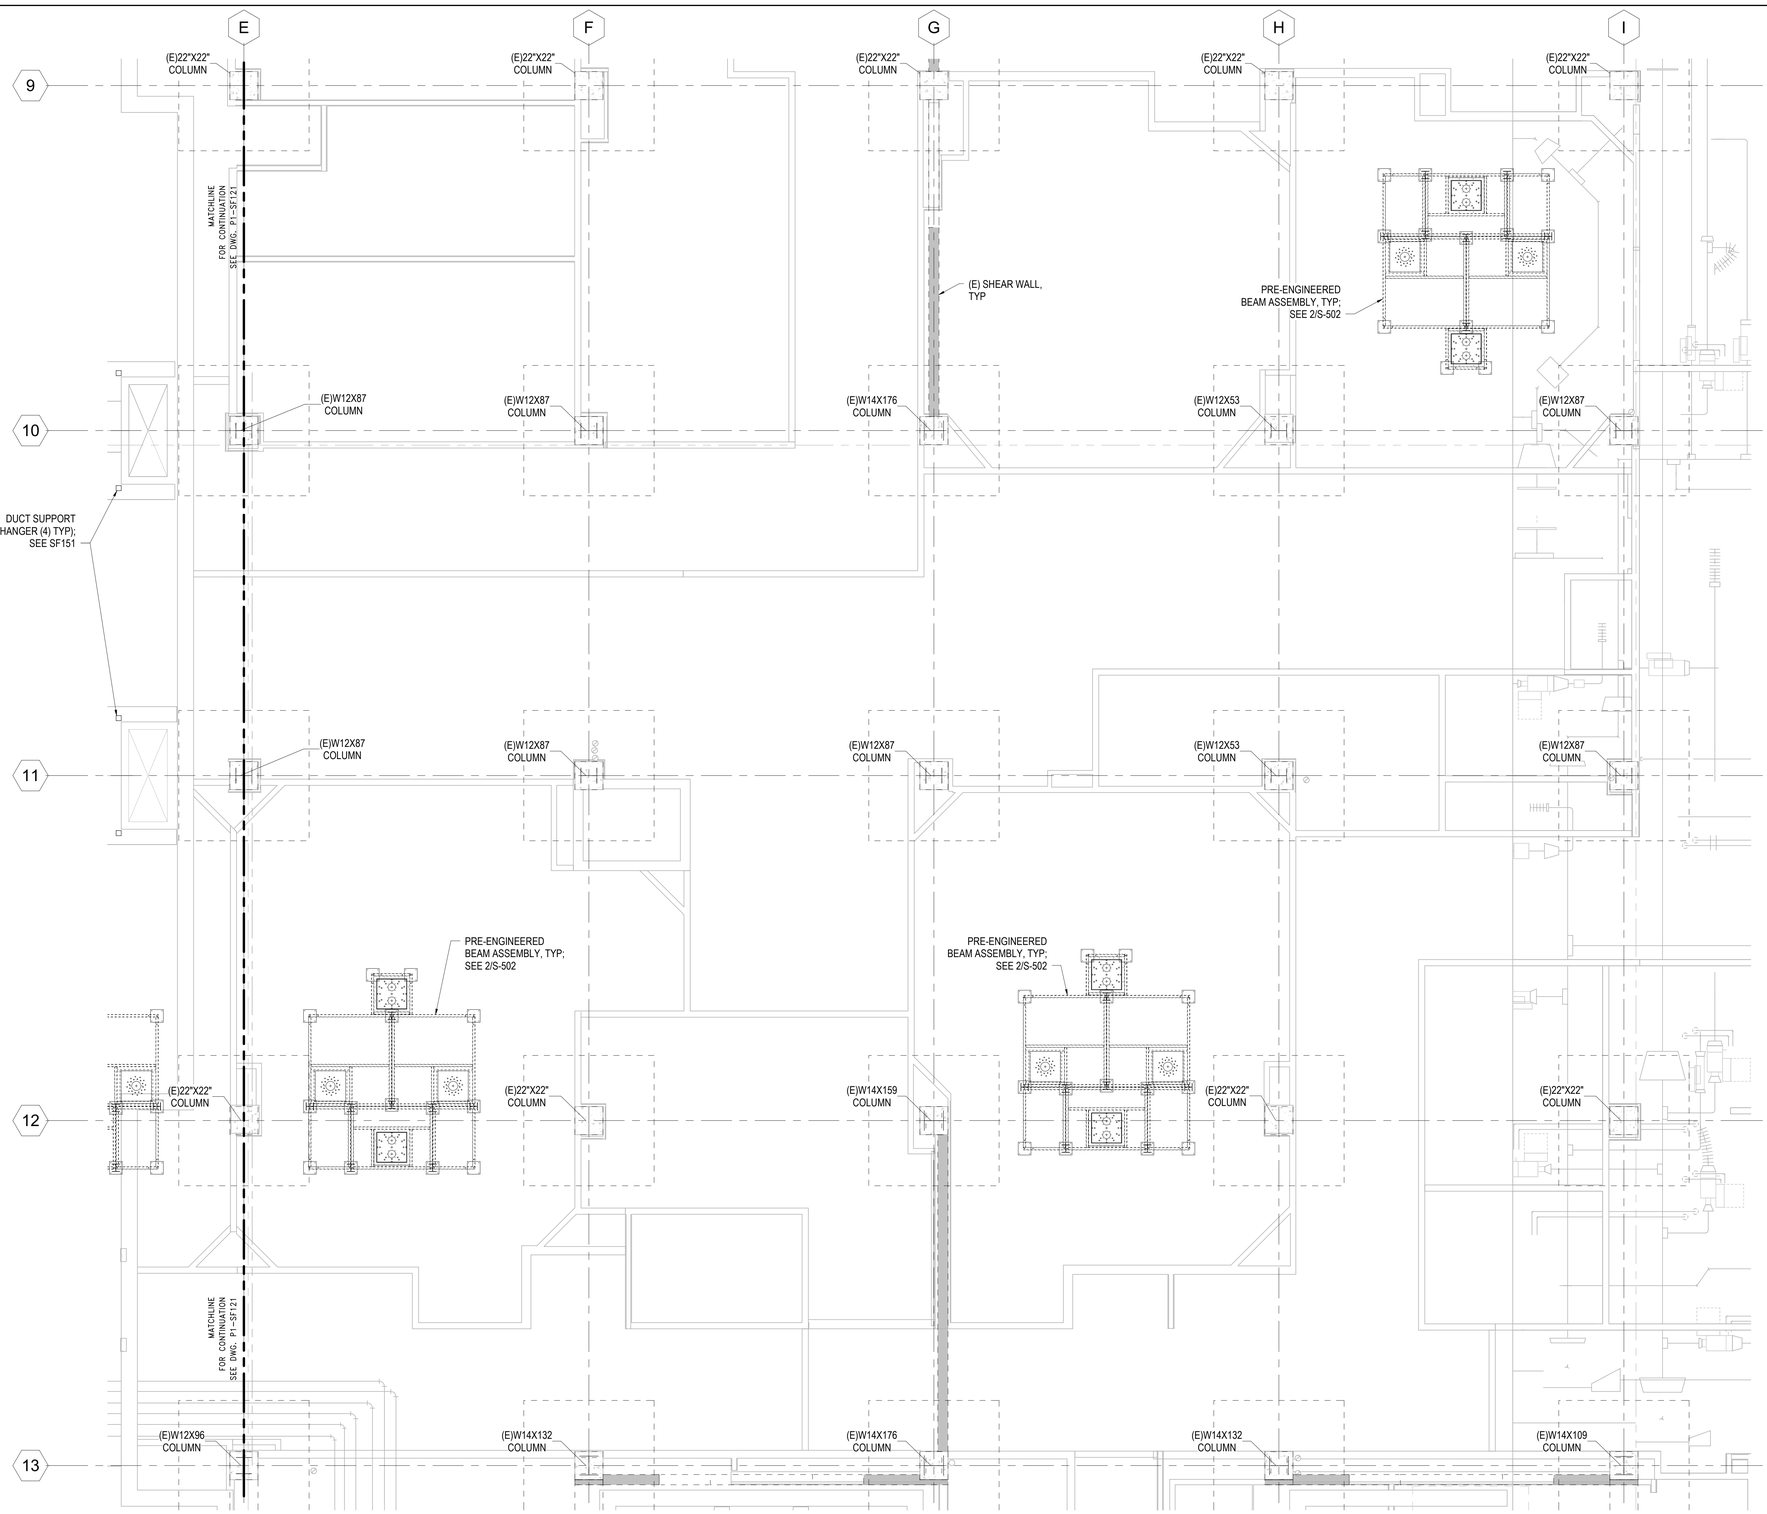

1 FRAMING PLAN - 2ND FLOOR, PHASE 2
SCALE: 1/4" = 1'-0"

GENERAL SHEET NOTES:

1. FOR GENERAL STRUCTURAL NOTES SEE DRAWING S-001 AND S-002.
2. REFER TO MECHANICAL AND ARCHITECTURAL DRAWINGS FOR ALL MECHANICAL EQUIPMENT SIZES AND LOCATIONS.
3. FOR CONCRETE WORK, REFER TO SPECIFICATIONS SECTION 03-30-53.
4. T/STEEL ELEVATION FOR DUNNAGE STEEL IS +2'-1 1/2" ABOVE T/(E) ROOF STEEL.
5. FOR ROOFING AND FINISHES, REFER TO ARCHITECTURAL DRAWINGS.
6. LOCATE AND MEASURE CENTERLINE DIMENSIONS OF EXISTING MEMBERS PRIOR TO FABRICATION OF NEW SUPPORTS. NEW SUPPORT STEEL SHALL BE LOCATED ONLY ON CENTERLINE OF EXISTING MEMBERS.
7. PROVIDE STRUCTURAL STEEL DUNNAGE FOR MECHANICAL EQUIPMENT, COORDINATE WITH MECHANICAL DRAWINGS AND FINAL UNIT SELECTION.
8. SHORE EXISTING ROOF SLAB PRIOR TO DEMOLITION.
9. REMOVE PORTIONS OF EXISTING ROOF SLAB REQUIRED FOR INSTALLATION OF DUCTWORK. SEE MECHANICAL DRAWINGS AND SF123.
10. INSTALL SINGLE ROD AND OR DOUBLE ROD GRAVITY SUPPORT AS REQUIRED. SEE S-502.
11. INSTALL PIPE POSTS FOR ROOF-TOP AHU SUPPORT STEEL DUNNAGE. SEE SF123.
12. * DENOTES TO COORDINATE FINAL DIMENSIONS AND LOCATION ACCORDING TO THE SELECTED EQUIPMENT SIZES, CLEARANCES OF DUCTS, AHU, PIPES, AND CONDIUT. NOTIFY COR/EOR OF ANY IMPEDIMENTS.
13. PLAN SHOWS 2ND FLOOR STRUCTURAL FRAMING (1ST FL. CEILING).
14. REPRESENTS ESTIMATED LOCATION OF CONNECTION FROM PRE-ENGINEERED HVAC SYSTEM TO SUPPLEMENTAL STRUCTURE ABOVE, REFER TO DETAILS ON S-502. PROVIDE CONNECTION AT MODULE CORNERS, BOOM OUTRIGGERS, AND WHERE REQUIRED BY BOOM AND/OR HVAC PLENUM MANUFACTURERS.
15. GRAVITY SUPPORT FRAMING SHOWN FOR REFERENCE ONLY. ALL REQUIRED FRAMING SHALL BE COORDINATED WITH MANUFACTURERS AND EXISTING STRUCTURAL STEEL. CONTRACTOR TO RETAIN PROFESSIONAL ENGINEER TO DESIGN ALL SUPPLEMENTAL FRAMING INCLUDING BUT NOT LIMITED TO BEAMS, RODS, HANGERS, CONNECTIONS, AND SEISMIC BRACING. REFER TO DETAILS AND SPECIFICATIONS.
16. ALL SUPPLEMENTAL FRAMING SHALL BE DESIGNED FOR STRENGTH AND SERVICE/DEFLECTION AS REQUIRED BY HVAC AND BOOM MANUFACTURERS. W8 SHALL BE THE MINIMUM MEMBER SIZE. COORDINATE FLANGE WIDTHS FOR CLEARANCE, STRENGTH, DEFLECTION, AND HANGING CONNECTION ATTACHMENTS.
17. CONTRACTOR TO COORDINATE WITH EQUIPMENT MANUFACTURER FOR INSTALLATION OF STRUCTURAL EQUIPMENT SUPPORTS. DRILLED AND EPOXIED ANCHORS ARE TO AVOID EXISTING REBAR. FIELD VERIFY PLACEMENT OF EXISTING REBAR.

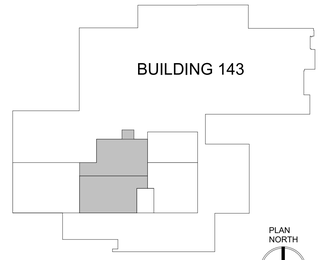

KEYPLAN

PRINTS OF THIS DRAWING SHALL NOT BE USED FOR ANY PURPOSE WHATSOEVER WITHOUT THE SEAL AND SIGNATURE OF THE PROFESSIONAL ENGINEER

Revisions:	Date:

CONSULTANT

Architecture:	Civil Engineering:	Fire Protection:
PF&A DESIGN, P.C.	LABELLA ASSOCIATES	STANTON ENGINEERING SERVICES, LLC

ENGINEER OF RECORD

MILLER-REMICK

A Service-Disabled Veteran-Owned Small Business

(856) 429-5000 ▪ Miller-Remick.com

MILLER-REMICK LLC
PROFESSIONAL ENGINEER

COMMONWEALTH OF VIRGINIA
ANTHONY DANIEL PACARO JR.
Lic. No. 402055070
PROFESSIONAL ENGINEER
12-30-2025

Office of Construction and Facilities Management

VA U.S. Department of Veterans Affairs

Drawing Title: STRUCTURAL FRAMING PLAN 2ND FLOOR, PHASE 2	Phase: BID DOCUMENTS
Approved by: Jon Manninen, COR	FULLY SPRINKLERED

Project Title: RENOVATE SURGICAL SUITE PHASE II			VA Drawing Number: 2617
Project Number: 658-19-103			Building Number: 143
Location: SALEM VA MEDICAL CENTER			Drawing Number: P2-SF122
Issue Date: 2025-12-30	Checked: FL	Drawn: DS	

12/29/2025 1:06:39 PM

VA FORM 08 - 6231

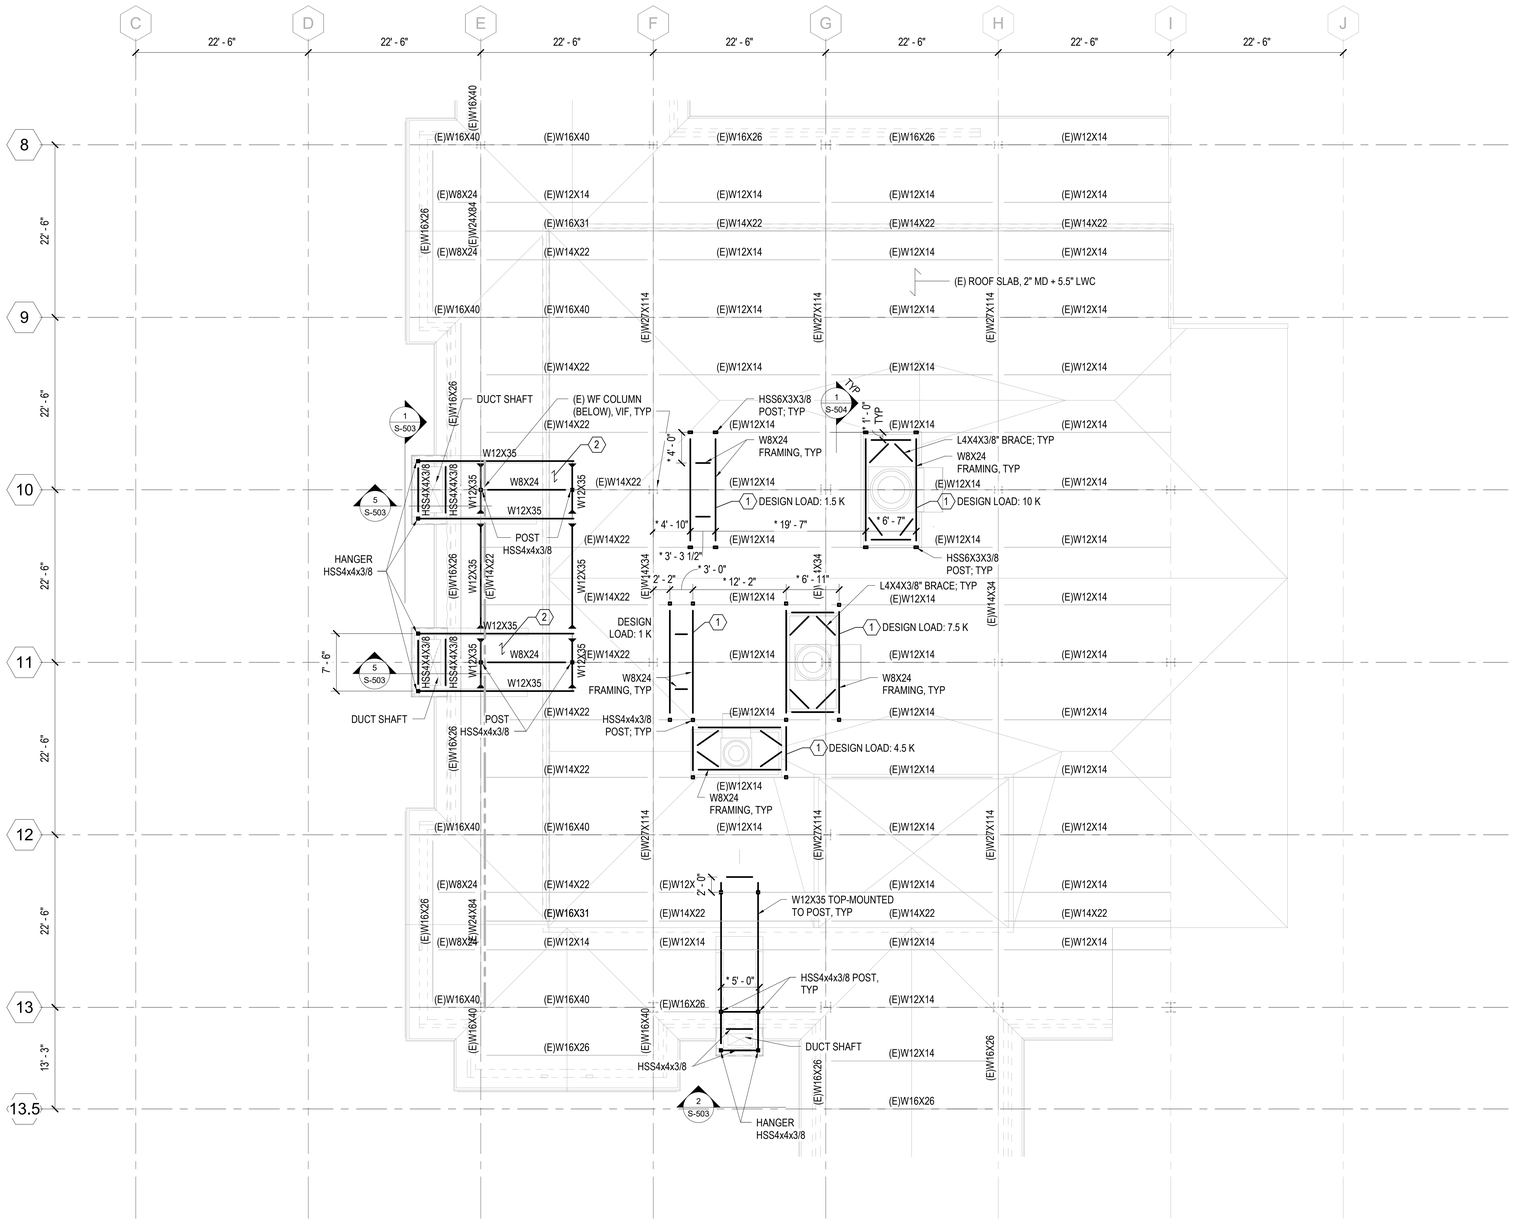

1 FRAMING PLAN - HIGH ROOF
SCALE: 1/8" = 1'-0"

GENERAL SHEET NOTES:

1. FOR GENERAL STRUCTURAL NOTES SEE DRAWING S-001 AND S-002.
2. REFER TO MECHANICAL AND ARCHITECTURAL DRAWINGS FOR ALL MECHANICAL EQUIPMENT SIZES AND LOCATIONS.
3. T/STEEL ELEVATION FOR DUNNAGE STEEL IS +2'-1 1/2" ABOVE T/(E) ROOF STEEL.
4. FOR ROOFING AND FINISHES, REFER TO ARCHITECTURAL DRAWINGS.
5. LOCATE AND MEASURE CENTERLINE DIMENSIONS OF EXISTING MEMBERS PRIOR TO FABRICATION OF NEW SUPPORTS. NEW SUPPORT STEEL SHALL BE LOCATED ONLY ON CENTERLINE OF EXISTING MEMBERS.
6. PROVIDE STRUCTURAL STEEL DUNNAGE FOR MECHANICAL EQUIPMENT, COORDINATE WITH MECHANICAL DRAWINGS AND FINAL UNIT SELECTION.
7. SHORE EXISTING ROOF SLAB PRIOR TO DEMOLITION.
8. REMOVE PORTIONS OF EXISTING ROOF SLAB REQUIRED FOR INSTALLATION OF DUCTWORK. SEE MECHANICAL DRAWINGS AND SF123.
9. * DENOTES TO COORDINATE FINAL DIMENSIONS AND LOCATION ACCORDING TO THE SELECTED EQUIPMENT SIZES, CLEARANCES OF DUCTS, AHU, PIPES, AND CONDIUT. NOTIFY COR/EOR OF ANY IMPEDIMENTS.
10. GRAVITY SUPPORT FRAMING SHOWN FOR REFERENCE ONLY. ALL REQUIRED FRAMING SHALL BE COORDINATED WITH MANUFACTURERS AND EXISTING STRUCTURAL STEEL. CONTRACTOR TO RETAIN PROFESSIONAL ENGINEER TO DESIGN ALL SUPPLEMENTAL FRAMING INCLUDING BUT NOT LIMITED TO BEAMS, RODS, HANGERS, CONNECTIONS, AND SEISMIC BRACING. REFER TO DETAILS AND SPECIFICATIONS.
11. ALL SUPPLEMENTAL FRAMING SHALL BE DESIGNED FOR STRENGTH AND SERVICE/DEFLECTION AS REQUIRED BY HVAC AND BOOM MANUFACTURERS. W8 SHALL BE THE MINIMUM MEMBER SIZE. COORDINATE FLANGE WIDTHS FOR CLEARANCE, STRENGTH, DEFLECTION, AND HANGING CONNECTION ATTACHMENTS.
12. CONTRACTOR TO COORDINATE WITH EQUIPMENT MANUFACTURER FOR INSTALLATION OF STRUCTURAL EQUIPMENT SUPPORTS. DRILLED AND EPOXIED ANCHORS ARE TO AVOID EXISTING REBAR. FIELD VERIFY PLACEMENT OF EXISTING REBAR.

KEY NOTES:

1. MECHANICAL EQUIPMENT. REFER TO MECHANICAL DRAWINGS.
2. GALV STL GRATING 1" x 3/16" 19-W-2, SPAN AS SHOWN.

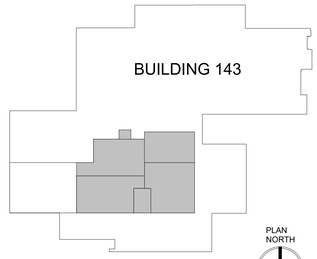

KEYPLAN

PRINTS OF THIS DRAWING SHALL NOT BE USED FOR ANY PURPOSE WHATSOEVER WITHOUT THE SEAL AND SIGNATURE OF THE PROFESSIONAL ENGINEER

Revisions: | Date:

02/28/2025 1:03:31 PM

CONSULTANT

Architecture:	Civil Engineering:	Fire Protection:
PF&A DESIGN, P.C.	LABELLA ASSOCIATES	STANTON ENGINEERING SERVICES, LLC

ENGINEER OF RECORD

MILLER-REMICK
A Service-Disabled Veteran-Owned Small Business
(856) 429-4000 • Miller-Remick.com
STA-HOSP14-DOR-20220218

MILLER-REMICK LLC PROFESSIONAL ENGINEER

COMMONWEALTH OF VIRGINIA
ANTHONY DANIEL PACARO JR.
Lic. No. 402055020
PROFESSIONAL ENGINEER
12.9.2025

Office of Construction and Facilities Management

VA U.S. Department of Veterans Affairs

Drawing Title: STRUCTURAL FRAMING PLAN 5TH FLOOR ROOF	Phase: BID DOCUMENTS	Project Title: RENOVATE SURGICAL SUITE PHASE II	VA Drawing Number: 2617
Approved by: Jon Manninen, COR	FULLY SPRINKLERED	Project Number: 658-19-103	Building Number: 143
		Location: SALEM VA MEDICAL CENTER	Drawing Number: SF151
		Issue Date: 2025-12-30 / Checked: FL / Drawn: DS	

VA FORM 08 - 6231

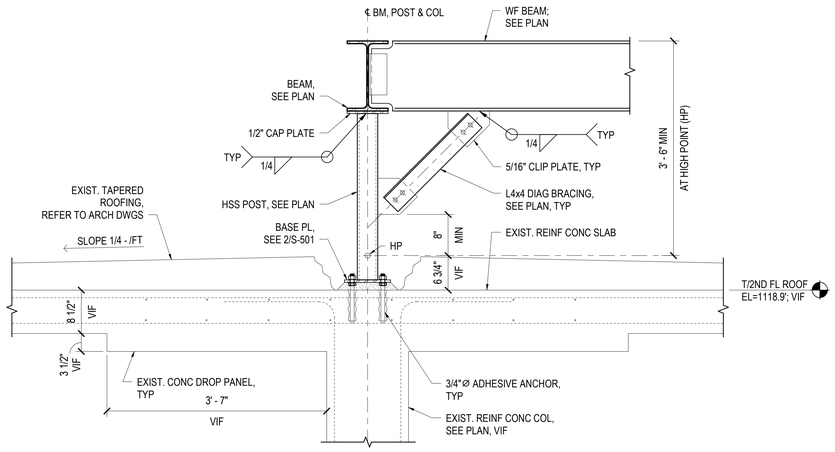

NOTES:
1. ALL STEEL FRAMING AND MATERIALS SHALL BE GALVANIZED.
2. PATCH EXISTING ROOF TO MATCH EXISTING.
3. PERFORM NON-DESTRUCTIVE TESTING TO LOCATE EXISTING REBAR. DO NOT CUT OR DRILL EXISTING REBAR.

1 DUNNAGE TYPICAL SECTION
SCALE: 1" = 1'-0"

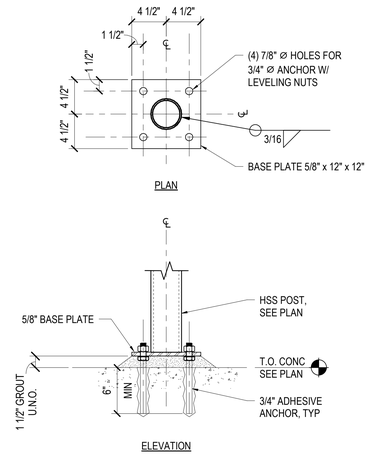

2 BASE PLATE DETAIL
SCALE: 1 1/2" = 1'-0"

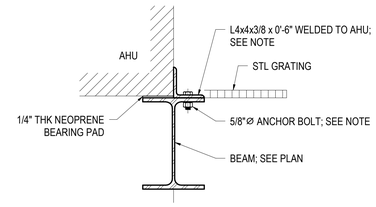

NOTE:
PROVIDE ANCHORAGE ASSEMBLY @ 2'-6" O.C. OR AS REQ'D BY MFR.

3 AHU ATTACHMENT DETAIL
SCALE: 1 1/2" = 1'-0"

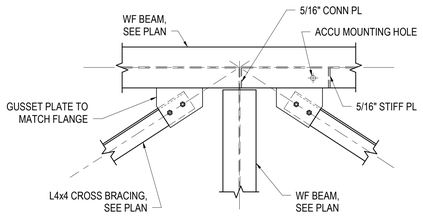

4 TYPICAL DUNNAGE BRACE DETAIL
SCALE: 1" = 1'-0"

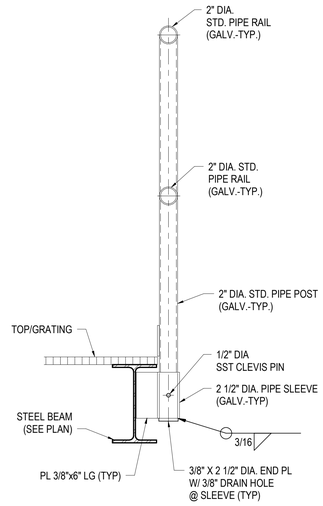

5 TYPICAL REMOVABLE GUARDRAIL DETAIL
SCALE: 1 1/2" = 1'-0"

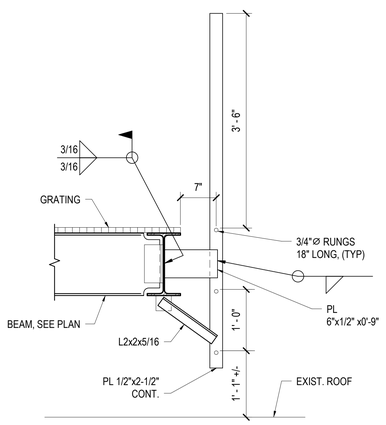

NOTES:
1. ALL STEEL FRAMING, GRATING, AND FASTENERS TO BE GALVANIZED U.N.O.
2. ATTACH GRATING TO STEEL FRAMING WITH GRATING MFR FASTENERS.
3. CONNECTIONS SHOWN FOR SCHEMATIC PURPOSES ONLY. FABRICATOR TO PROVIDE SHOP-STANDARD CONNECTIONS.

6 TYPICAL LADDER ATTACHEMENT DETAIL
SCALE: 1" = 1'-0"

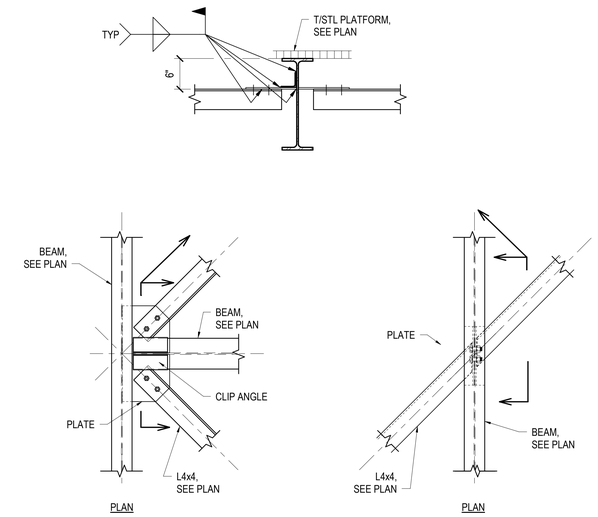

7 TYPICAL HORIZONTAL BRACE DETAIL
SCALE: 1" = 1'-0"

PRINTS OF THIS DRAWING SHALL NOT BE USED FOR ANY PURPOSE WHATSOEVER WITHOUT THE SEAL AND SIGNATURE OF THE PROFESSIONAL ENGINEER

Revisions: | Date:

12/29/2025 1:05:03 PM

CONSULTANT

Architecture:	Civil Engineering:	Fire Protection:
PF&A DESIGN, P.C.	LABELLA ASSOCIATES	STANTON ENGINEERING SERVICES, LLC

ENGINEER OF RECORD

MILLER-REMICK
A Service-Disabled Veteran-Owned Small Business
(856) 429-4000 ● Miller-Remick.com
MR PROJECT ID: 2025-036

MILLER-REMICK LLC
PROFESSIONAL ENGINEER

COMMONWEALTH OF VIRGINIA
ANTHONY DANIEL PACARO JR.
Lic. No. 402055036
PROFESSIONAL ENGINEER
12-30-2025

Office of Construction and Facilities Management

VA U.S. Department of Veterans Affairs

Drawing Title: STRUCTURAL SECTIONS & DETAILS I	Phase: BID DOCUMENTS
Approved by: Jon Manninen, COR	FULLY SPRINKLERED

Project Title: RENOVATE SURGICAL SUITE PHASE II	Project Number: 658-19-103	VA Drawing Number: 2617	Building Number: 143
Location: SALEM VA MEDICAL CENTER		Drawing Number: S-501	
Issue Date: 2025-12-30	Checked: FL	Drawn: DS	

VA FORM 08 - 6231

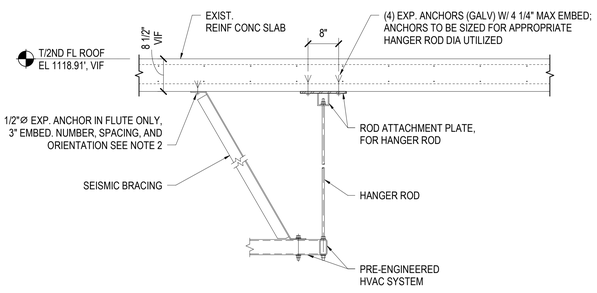

NOTES:
1. COORDINATE LOCATION OF SYSTEM WITH MECHANICAL AND ARCHITECTURAL DRAWINGS.
2. ALL NEW SUPPORT MEMBERS AND CONNECTIONS SHALL BE DESIGNED BY CONTRACTOR'S PROFESSIONAL ENGINEER.
3. PERFORM NON-DESTRUCTIVE TESTING TO LOCATE EXISTING REBAR. DO NOT CUT OR DRILL EXISTING REBAR.

1 TYPICAL PRE-ENGINEERED SYSTEM BRACE SECTION

SCALE: 3/4" = 1'-0"

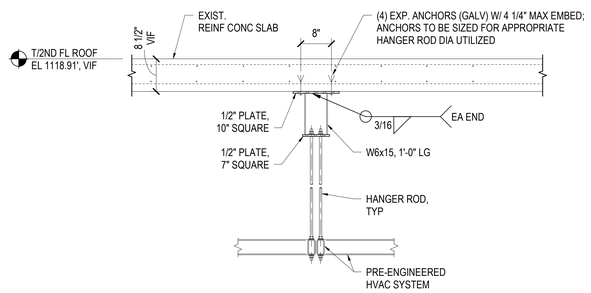

NOTES:
1. COORDINATE LOCATION OF SYSTEM WITH MECHANICAL AND ARCHITECTURAL DRAWINGS.
2. ALL NEW SUPPORT MEMBERS AND CONNECTIONS SHALL BE DESIGNED BY CONTRACTOR'S PROFESSIONAL ENGINEER
3. PERFORM NON-DESTRUCTIVE TESTING TO LOCATE EXISTING REBAR. DO NOT CUT OR DRILL EXISTING REBAR.

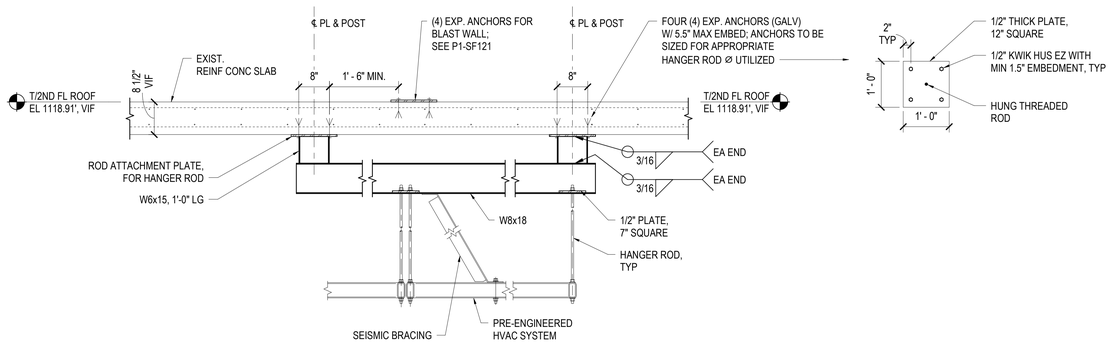

NOTES:
1. COORDINATE LOCATION OF ASSEMBLY WITH ARCHITECTURAL AND MECHANICAL DRAWINGS.
2. ALL NEW SUPPORT MEMBERS AND CONNECTIONS SHALL BE DESIGNED BY CONTRACTOR'S PROFESSIONAL ENGINEER.
3. PERFORM NON-DESTRUCTIVE TESTING TO LOCATE EXISTING REBAR. DO NOT CUT OR DRILL EXISTING REBAR.

2 TYPICAL PRE-ENGINEERED BEAM DETAIL

SCALE: 3/4" = 1'-0"

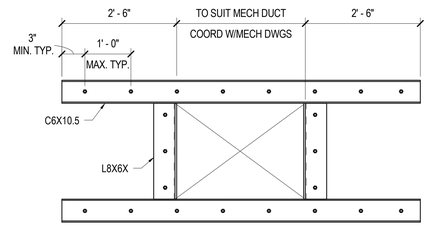

PLAN

PLAN NOTES
1. COORDINATE OPENING LOCATION AND SIZE WITH MECHANICAL DRAWINGS.
2. REFER TO ARCHITECTURAL DRAWINGS FOR ROOFING AND WATERPROOFING DETAILS.
3. PERFORM NON-DESTRUCTIVE TESTING TO LOCATE EXISTING REBAR. DO NOT CUT OR DRILL EXISTING REBAR.

3 ROOF SLAB TYPICAL OPENING DETAIL

SCALE: 3/4" = 1'-0"

PRINTS OF THIS DRAWING SHALL NOT BE USED FOR ANY PURPOSE WHATSOEVER WITHOUT THE SEAL AND SIGNATURE OF THE PROFESSIONAL ENGINEER

Revisions:	Date:

02/28/2025 1:04:51 PM

CONSULTANT

Architecture:	Civil Engineering:	Fire Protection:
PF&A DESIGN, P.C.	LABELLA ASSOCIATES	STANTON ENGINEERING SERVICES, LLC

ENGINEER OF RECORD

MILLER-REMICK

A Service-Disabled Veteran-Owned Small Business

(856) 429-4000 • Miller-Remick.com

MILLER-REMICK LLC
PROFESSIONAL ENGINEER

COMMONWEALTH OF VIRGINIA
ANTHONY DANIEL PACARO JR.
Lic. No. 402055020
PROFESSIONAL ENGINEER

12.30.2025

Office of Construction and Facilities Management

VA U.S. Department of Veterans Affairs

Drawing Title: STRUCTURAL SECTIONS & DETAILS II	Phase: BID DOCUMENTS	Project Title: RENOVATE SURGICAL SUITE PHASE II	VA Drawing Number: 2617
		Project Number: 658-19-103	Building Number: 143
Approved by: Jon Manninen, COR	FULLY SPRINKLERED	Location: SALEM VA MEDICAL CENTER	Drawing Number: S-502
		Issue Date: 2025-12-30 / Checked: FL / Drawn: DS	

VA FORM 08 - 6231

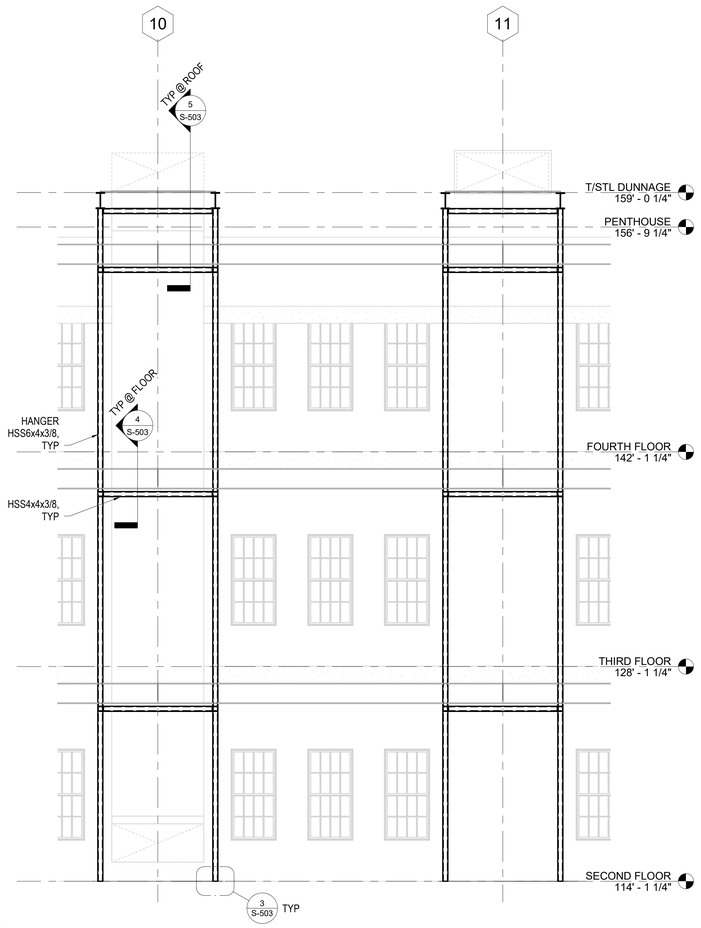

1 ELEVATION

SCALE: 1/4" = 1'-0"

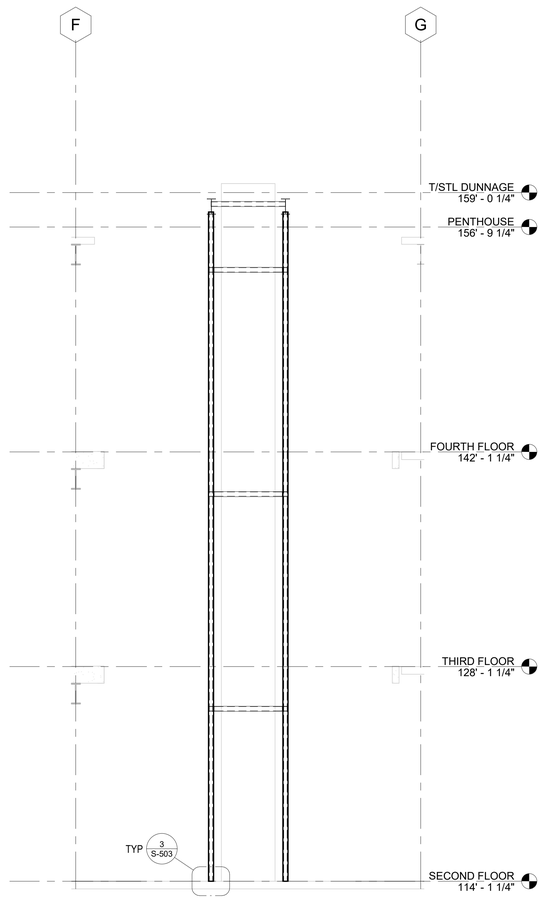

2 ELEVATION

SCALE: 1/4" = 1'-0"

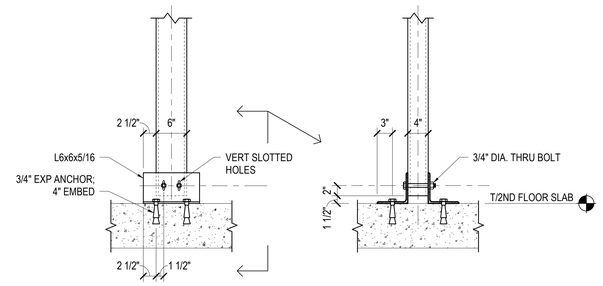

NOTE:
1. PERFORM NON-DESTRUCTIVE TESTING TO LOCATE EXISTING REBAR. DO NOT CUT OR DRILL EXISTING REBAR.

3 LATERAL ONLY HANGER SUPPORT

SCALE: 1" = 1'-0"

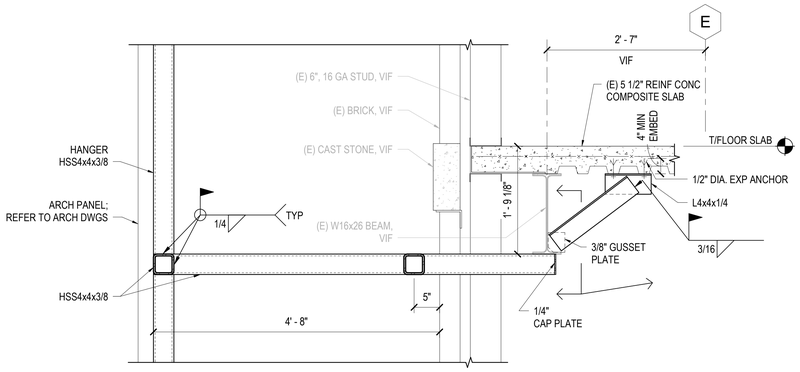

NOTES:
1. DETAIL IS TYPICAL AT ALL STORIES.
2. REMOVE ANY FIREPROOFING FROM EXISTING BEAMS THAT WILL BE WELDED.
3. PERFORM NON-DESTRUCTIVE TESTING TO LOCATE EXISTING REBAR. DO NOT CUT OR DRILL EXISTING REBAR.

4 DUCT SUPPORT BRACE SECTION

SCALE: 1" = 1'-0"

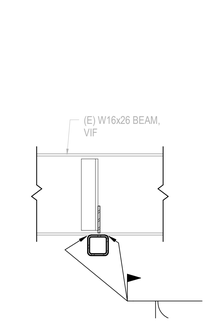

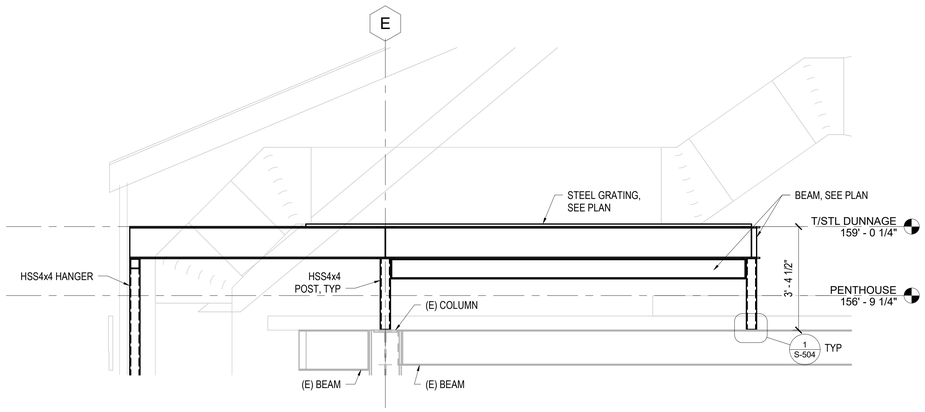

5 ROOF DUCT SUPPORT SECTION

SCALE: 1/2" = 1'-0"

PRINTS OF THIS DRAWING SHALL NOT BE USED FOR ANY PURPOSE WHATSOEVER WITHOUT THE SEAL AND SIGNATURE OF THE PROFESSIONAL ENGINEER

Revisions:	Date:

CONSULTANT

Architecture:	Civil Engineering:	Fire Protection:
PF&A DESIGN, P.C.	LABELLA ASSOCIATES	STANTON ENGINEERING SERVICES, LLC

ENGINEER OF RECORD

MILLER-REMICK

A Service-Disabled Veteran-Owned Small Business

(856) 429-4000 • Miller-Remick.com

MILLER-REMICK LLC
PROFESSIONAL ENGINEER

COMMONWEALTH OF VIRGINIA
ANTHONY DANIEL PACARO JR.
Lic. No. 402055020
PROFESSIONAL ENGINEER
12.30.2025

Office of Construction and Facilities Management

VA U.S. Department of Veterans Affairs

Drawing Title	STRUCTURAL SECTIONS & DETAILS
Approved by:	Jon Manninen, COR
Phase	BID DOCUMENTS
	FULLY SPRINKLERED
Project Title	RENOVATE SURGICAL SUITE PHASE II
Project Number	658-19-103
Location	SALEM VA MEDICAL CENTER
Issue Date	2025-12-30
Checked	FL
Drawn	DS
VA Drawing Number	2617
Building Number	143
Drawing Number	S-503

02/26/2025 1:04:39 PM

VA FORM 08 - 6231

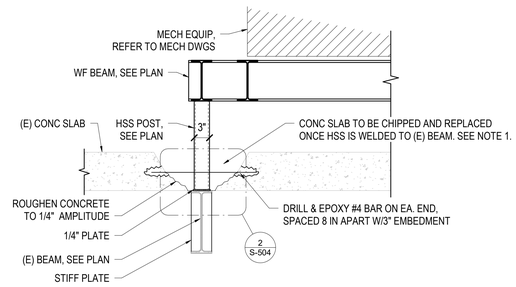

NOTES:
1. AT CONTRACTOR'S OPTION, PERFORM NON-DESTRUCTIVE TESTING TO LOCATE EXISTING REBAR. IF EXISTING REBAR IS NOT CUT, DRILL & EPOXY BARS NOT REQUIRED.

1 ROOF SUPPORT RESTRAINT
SCALE: 1" = 1'-0"

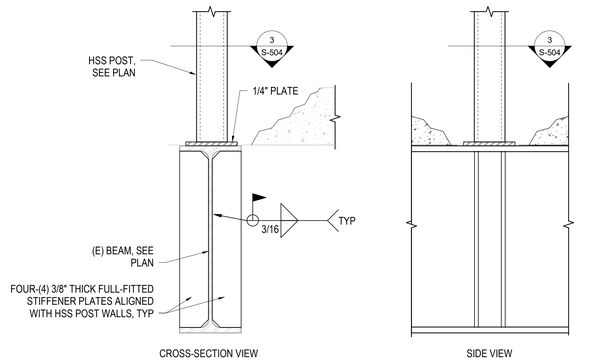

2 ROOF SUPPORT POST CONNECTION
SCALE: 3" = 1'-0"

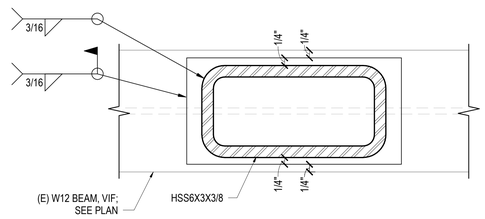

3 TOP VIEW
SCALE: 6" = 1'-0"

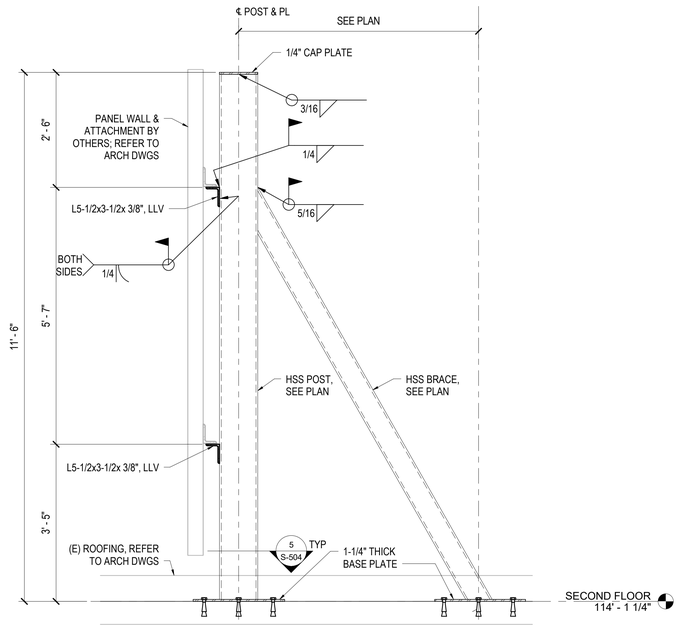

NOTES:
1. MAX DIM BETWEEN CL OF POST-BRACE ANCHORING IS 5FT.
2. HEIGHT OF VERT. POST IS 11'-6".
3. BRACE POST TO INTERSECT AT 2'-6" BELOW TOP.
4. PERFORM NON-DESTRUCTIVE TESTING TO LOCATE EXISTING REBAR. IF EXISTING REBAR IS NOT CUT, DRILL & EPOXY BARS NOT REQUIRED.

4 LOW ROOF BLAST SCREEN WALL
SCALE: 3/4" = 1'-0"

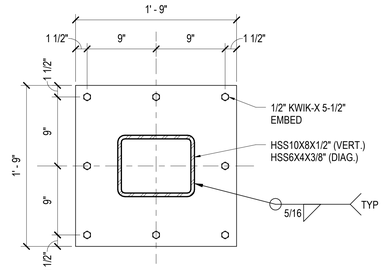

NOTES:
1. PERFORM NON-DESTRUCTIVE TESTING TO LOCATE EXISTING REBAR. IF EXISTING REBAR IS NOT CUT, DRILL & EPOXY BARS NOT REQUIRED.

5 BASE PLATE DETAIL
SCALE: 1 1/2" = 1'-0"

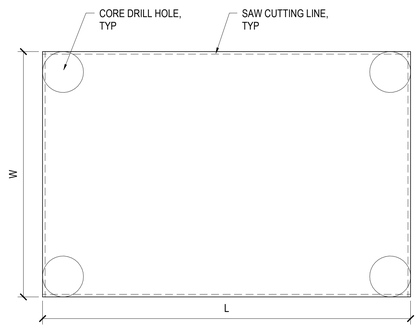

SEQUENCE OF CONSTRUCTION:
1. COMPLETE SCAN OF SLAB FOR ANY TOP REINFORCING BARS.
2. PROVIDE CORE DRILLED HOLES AT THE CORNER OF THE EXTENTS OF THE OPENING
3. SAW CUT BETWEEN THE CORE DRILLED HOLES. DO NOT OVERCUT BEYOND OPENING.
4. GRIND THE OPENING SMOOTH

6 TYPICAL EXISTING CONCRETE SLAB PENETRATION DETAIL
SCALE: 1" = 1'-0"

PRINTS OF THIS DRAWING SHALL NOT BE USED FOR ANY PURPOSE WHATSOEVER WITHOUT THE SEAL AND SIGNATURE OF THE PROFESSIONAL ENGINEER

Revisions:	Date:

CONSULTANT

Architecture:	Civil Engineering:	Fire Protection:
PF&A DESIGN, P.C.	LABELLA ASSOCIATES	STANTON ENGINEERING SERVICES, LLC

ENGINEER OF RECORD

MILLER•REMICK
A Service-Disabled Veteran-Owned Small Business
(856) 429-4000 • Miller-Remick.com
M-R PROJECT NO. 0499-0036

MILLER-REMICK LLC
PROFESSIONAL ENGINEER

COMMONWEALTH OF VIRGINIA
ANTHONY DANIEL PACARDO JR.
Lic. No. 402055029
PROFESSIONAL ENGINEER
12-30-2025

Office of Construction and Facilities Management

VA U.S. Department of Veterans Affairs

Drawing Title: STRUCTURAL SECTIONS & DETAILS	Phase: BID DOCUMENTS	Project Title: RENOVATE SURGICAL SUITE PHASE II	VA Drawing Number: 2617
Approved by: Jon Manninen, COR	FULLY SPRINKLERED	Project Number: 658-19-103	Building Number: 143
		Location: SALEM VA MEDICAL CENTER	Drawing Number: S-504
		Issue Date: 2025-12-30 / Checked: FL / Drawn: DS	

12/29/2025 1:04:11 PM

VA FORM 08 - 6231

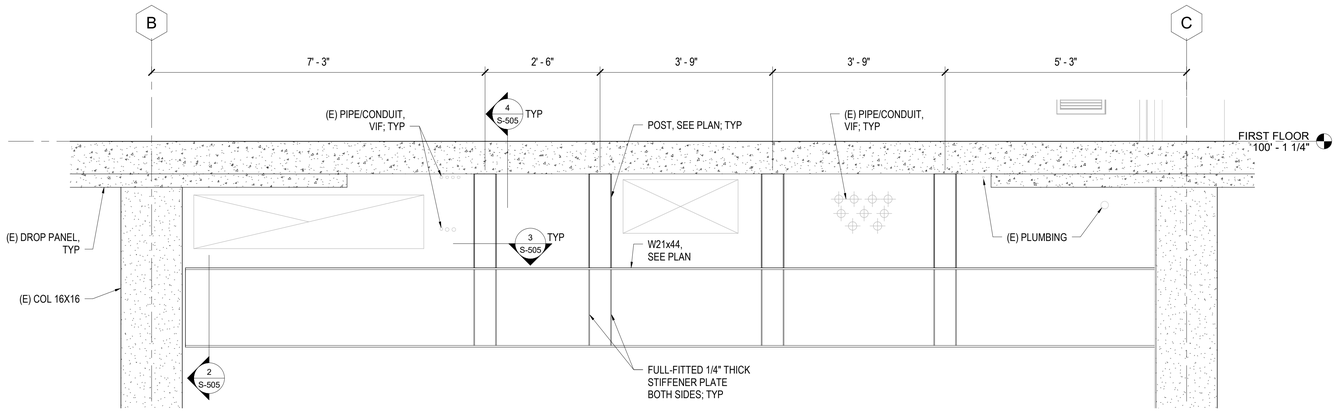

1 GIRDER ELEVATION

SCALE: 3/4" = 1'-0"

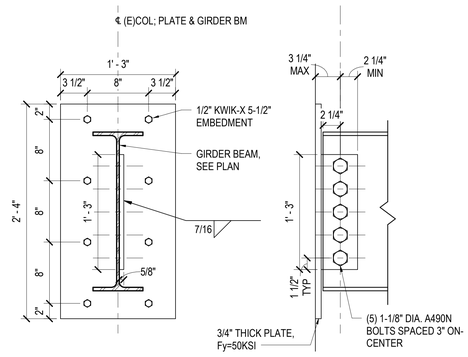

NOTES:
1. PERFORM NON-DESTRUCTIVE TESTING TO LOCATE EXISTING REBAR. IF EXISTING REBAR IS NOT CUT, DRILL & EPOXY BARS NOT REQUIRED.

2 BEAM GIRDER TO COLUMN CONNECTION

SCALE: 1 1/2" = 1'-0"

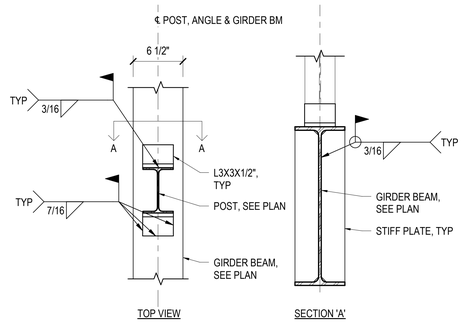

NOTES:
1. LOCATE POST TO SLAB CONNECTION PRIOR TO WELDING STIFFENER PLATES IN ALIGNMENT WITH POST FLANGE.

3 POST TO BEAM CONNECTION

SCALE: 1 1/2" = 1'-0"

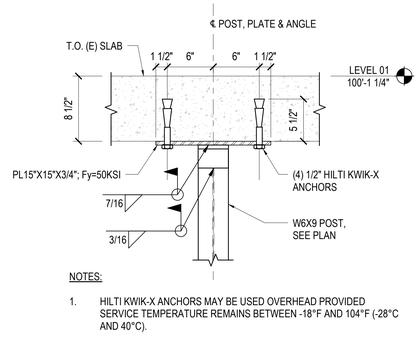

NOTES:
1. HILTI KWIK-X ANCHORS MAY BE USED OVERHEAD PROVIDED SERVICE TEMPERATURE REMAINS BETWEEN -18°F AND 104°F (-28°C AND 40°C).

4 POST TO SLAB CONNECTION

SCALE: 1 1/2" = 1'-0"

PRINTS OF THIS DRAWING SHALL NOT BE USED FOR ANY PURPOSE WHATSOEVER WITHOUT THE SEAL AND SIGNATURE OF THE PROFESSIONAL ENGINEER

Revisions: | Date:

CONSULTANT

Architecture:	Civil Engineering:	Fire Protection:
PF&A DESIGN, P.C.	LABELLA ASSOCIATES	STANTON ENGINEERING SERVICES, LLC

ENGINEER OF RECORD

MILLER+REMICK
A Service-Disabled Veteran-Owned Small Business
(856) 429-4000 • Miller-Remick.com
M-R PROJECT NO. 0909-0030

MILLER-REMICK LLC PROFESSIONAL ENGINEER

COMMONWEALTH OF VIRGINIA
ANTHONY DANIEL PACARO JR.
Lic. No. 402055020
PROFESSIONAL ENGINEER
12.30.2025

Office of Construction and Facilities Management

VA U.S. Department of Veterans Affairs

Drawing Title	STRUCTURAL SECTIONS & DETAILS
Approved by:	Jon Manninen, COR
Phase	BID DOCUMENTS
	FULLY SPRINKLERED
Project Title	RENOVATE SURGICAL SUITE PHASE II
Project Number	658-19-103
Location	SALEM VA MEDICAL CENTER
Issue Date	2025-12-30
Checked	FL
Drawn	DS
VA Drawing Number	2617
Building Number	143
Drawing Number	S-505

12/29/2025 1:03:45 PM

VA FORM 08 - 6231