ELECTRICAL ABBREVIATIONS

+	MOUNTED ABOVE STANDARD HEIGHT	JB	JUNCTION BOX
1P	SINGLE POLE	KV	KILOVOLT
1PH	SINGLE-PHASE	KVA	KILOVOLT AMPERE
2P	TWO POLE	KVAH	KILOVOLT AMPERE PER HOUR
2/C	TWO-CONDUCTOR	KVAR	KILOVOLT AMPERE REACTIVE
3P	THREE POLE	KW	KILOWATT
3PH	THREE-PHASE	KWH	KILOWATT HOUR
3W	THREE-WIRE	KWHM	KILOWATT HOUR METER
3/C	THREE-CONDUCTOR		
4/C	FOUR-CONDUCTOR	LED	LIGHT EMITTING DIODE
4W	FOUR-WIRE	LF	LINEAR FEET (FOOT)
		LM	LUMEN
A/C UNIT	AIR CONDITIONING UNIT	LP	LIGHT POLE
A/E	ARCHITECT/ENGINEER	LPS	LOW PRESSURE SODIUM
AC	ALTERNATING CURRENT OR ARMORED CABLE	LRA	LOCKED ROTOR AMPS
ADJ	ADJACENT, ADJOINING	LS	LIFE SAFETY
ADO	AUTOMATIC DOOR OPENER	LT	LIGHT
AF	AMPERE FRAME OR AMP FUSE	LTG	LIGHTING
AFC	ABOVE FINISHED COUNTER, AUTOMATIC FREQUENCY CONTROL, OR AVAILABLE FAULT CURRENT	LV	LOW VOLTAGE
		LVL	LEVEL
AFF	ABOVE FINISHED FLOOR		
AFG	ABOVE FINISHED GRADE	MATV	MASTER ANTENNA TELEVISION SYSTEM
AH	AMPERE HOUR	MAX	MAXIMUM
AHJ	AUTHORITY HAVING JURISDICTION	MC	METAL-CLAD
AIC	AMPERE INTERRUPTING CAPACITY	MCA	MINIMUM CIRCUIT AMPS
ALT	ALTERNATE	MCB	MAIN CIRCUIT BREAKER
AMP OR A	AMPERE	MCC	MOTOR CONTROL CENTER
ARCH	ARCHITECT	MDP	MAIN DISTRIBUTION PANEL
ASC	AMPS SHORT CIRCUIT	MECH	MECHANICAL
AT	AMPERE TRIP	MH	MANHOLE
ATS	AUTOMATIC TRANSFER SWITCH	MIN	MINIMUM
AUTO	AUTOMATIC	MLO	MAIN LUGS ONLY
A/V	AUDIO VISUAL	MMFO	MULTI-MODE FIBER OPTIC
		MOCP	MAXIMUM OVERCURRENT PROTECTION
BC	BARE COPPER	MTD	MOUNTED
BFF	BELOW FINISH FLOOR	MTS	MANUAL TRANSFER SWITCH
BIL	BASIC INSULATION LEVEL	MV	MEDIUM VOLTAGE
BLDG	BUILDING	MVA	MEGAVOLT-AMPERE
BRKR	BREAKER	MW	MEGAWATT
BYP	BYPASS		
		NA	NOT APPLICABLE
C	CONDUIT	NC	NORMALLY CLOSED
CALC	CALCULATE OR CALCULATION	NEC	NATIONAL ELECTRICAL CODE
CAT	CATALOG	NEMA	NATIONAL ELECTRICAL MANUFACTURERS ASSOCIATION
CATV	COMMUNITY ANTENNA TELEVISION	N	NEUTRAL
CCTV	CLOSED CIRCUIT TELEVISION	NFPA	NATIONAL FIRE PROTECTION ASSOCIATION
cd	CANDELA	NIC	NOT IN CONTRACT
CD	CONSTRUCTION DOCUMENTS	NL	NIGHT LIGHT
CF	CONTRACTOR FURNISHED	NO	NORMALLY OPEN
CF/CI	CONTRACTOR FURNISHED/CONTRACTOR INSTALLED	NS	NO SCALE
CF/OI	CONTRACTOR FURNISHED/OWNER INSTALLED	NTS	NOT TO SCALE
CFE	CONTRACTOR FURNISHED EQUIPMENT		
CHW	CHILLED WATER	OC	ON CENTER
CHWP	CHILLED WATER PUMP	OCPD	OVERCURRENT PROTECTION DEVICE
CKT	CIRCUIT	OD	OUTSIDE DIAMETER
CB	CIRCUIT BREAKER	OL	OVERLOAD
CLF	CURRENT LIMITING FUSE		
CLG	CEILING	P	POLE
CMU	CONCRETE MASONRY UNIT	PA	PUBLIC ADDRESS
COAX	COAX CABLE	PB	PULL BOX
COMM	COMMUNICATION	PBPU	PREFABRICATED BEDSIDE PATIENT UNIT
CONC	CONCRETE	PC	PHOTOCELL
CONT	CONTINUE	PCB	POLYCHLORINATED BIPHENYL
COORD	COORDINATE	PED	PEDESTAL
CPT	CONTROL POWER TRANSFORMER	PEND	PENDANT
CR	CRITICAL POWER	PF	POWER FACTOR
CRI	COLOR RENDERING INDEX	PH	PHASE
CT	CURRENT TRANSFORMER	PNL	PANEL
CU	COPPER	POE	POWER OVER ETHERNET
CU FT	CUBIC FEET	PT	POTENTIAL TRANSFORMER
		PVC	POLYVINYL CHLORIDE (PLASTIC)
(D)	DEMOLISH	PWR	POWER
DB	DECIBEL OR DIRECT BURIAL		
DC	DIRECT CURRENT	(R)	REMOVE (DEMOLISH)
DEG C	DEGREES CELSIUS	(RE)	RELOCATED EXISTING
DEG F	DEGREES FAHRENHEIT	RCP	REFLECTED CEILING PLAN
DEMO	DEMOLITION	REC OR RECPT	RECEPTACLE
DISC	DISCONNECT	RGS	RIGID GALVANIZED STEEL
DN	DOWN	RM	ROOM
DPDT	DOUBLE POLE, DOUBLE THROW	RMS	ROOT MEAN SQUARE
DPST	DOUBLE POLE, SINGLE THROW	REQD	REQUIRED
DWG	DRAWING		
		SCC	SHORT CIRCUIT CAPACITY
(E)	EXISTING	SD	SMOKE DETECTOR
(ER)	EXISTING TO BE RELOCATED	SF	SQUARE FOOT (FEET)
EC	ELECTRICAL CONTRACTOR	SHT	SHEET
ECB	ENCLOSED CIRCUIT BREAKER	SI	INTERNATIONAL SYSTEM OF UNITS
EG	EQUIPMENT GROUND	SMFO	SINGLE MODE FIBER OPTIC
EGC	EQUIPMENT GROUNDING CONDUCTOR	SPD	SURGE PROTECTIVE DEVICE
EL	ELEVATION	SPEC	SPECIFICATION
ELEC	ELECTRIC OR ELECTRICAL	SPST	SINGLE POLE, SINGLE THROW
ELEV	ELEVATOR	STP	SHIELDED TWISTED PAIR
EMER OR EM	EMERGENCY	SW	SWITCH
EMI	ELECTROMAGNETIC INTERFERENCE	SWBD	SWITCHBOARD
EMT	ELECTRICAL METALLIC TUBING	SWGR	SWITCHGEAR
ENCL	ENCLOSURE		
EPO	EMERGENCY POWER OFF	(T)	TEMPORARY
EWC	ELECTRIC WATER COOLER	TBB	TELECOM BACK BOARD
EWH	ELECTRIC WATER HEATER	TC	TIME CLOCK
		TEL	TELEPHONE
FA	FIRE ALARM	TGB	TELECOM GROUND BAR
FAAP	FIRE ALARM ANNUNCIATOR PANEL	TP	TAMPER PROOF
FACP	FIRE ALARM CONTROL PANEL	TTB	TELEPHONE TERMINAL BOARD
FC	FOOTCANDLE	TV	TELEVISION
FI	FILM ILLUMINATOR	TYP	TYPICAL
FIXT	FIXTURE		
FLA	FULL LOAD AMPS	UG OR UGND	UNDERGROUND
FMC	FLEXIBLE METALLIC CONDUIT	UL	UNDERWRITERS LABORATORY
FLT	FLOODLIGHT	UON	UNLESS OTHERWISE NOTED
FOUTT	TELEPHONE FLOOR OUTLET	UPS	UNINTERRUPTIBLE POWER SUPPLY
FP	FIRE PROTECTION	UTIL	UTILITY
FT	FEET OR FOOT		
FVNR	FULL VOLTAGE NON-REVERSING	V	VOLT OR VOLTAGE
FVR	FULL VOLTAGE REVERSING	VA	VOLT AMPERE
		VAR	VOLT AMPERE REACTIVE
G OR GND	GROUND	VFD	VARIABLE FREQUENCY DRIVE
GEN	GENERATOR		
GFCI	GROUND FAULT CIRCUIT INTERRUPTER	W	WATT
GTB	GROUND TERMINAL BOX	WH	WATER HEATER
		WP	WEATHERPROOF
HID	HIGH INTENSITY DISCHARGE		
HOA	HAND-OFF-AUTOMATIC	XFER	TRANSFER
HP	HORSEPOWER	XFMR	TRANSFORMER
HT	HEIGHT		
HZ	HERTZ		
IESNA	ILLUMINATION ENGINEERING SOCIETY OF NORTH AMERICA		
IMC	INTERMEDIATE METAL CONDUIT		
INCAND	INCANDESCENT		
IR	INFRARED		
IWH	INSTANTANEOUS WATER HEATER		

ELECTRICAL POWER SYMBOLS

- KEY NOTE SYMBOL
- MULTIPLE KEY NOTES APPLYING TO THE SAME ITEM
- DETAIL IDENTIFIER — DETAIL # — DRAWING # (WHERE DETAIL IS FOUND)
- OR — INDICATES EQUIPMENT TO BE DEMOLISHED
- DISTRIBUTION PANEL
- BRANCH CIRCUIT PANEL
- PANELBOARD CABINET, FLUSH MOUNTED
- PANELBOARD CABINET, SURFACE MOUNTED
- CIRCUIT # — BRANCH CIRCUIT HOMERUN. HALF-ARROWS INDICATE NUMBER OF CIRCUITS. ONE SEPARATE GREEN GROUNDING CONDUCTOR SHALL BE PROVIDED FOR EACH HOMERUN; NOT SHOWN
- CLEARANCE TRANSFORMER — TRANSFORMER, PLAN
- G — GROUND BUS BAR
- RECEPTACLE, DUPLEX
- FLOOR MOUNTED RECEPTACLE, DUPLEX SHOWN (DASHED LINE INDICATES FLOOR MOUNTED, TYPICAL ALL TYPES OF RECEPTACLES)
- RECEPTACLE, DUPLEX - EMERGENCY
- RECEPTACLE, DUPLEX - CEILING
- RECEPTACLE, DUPLEX WITH GROUND FAULT CIRCUIT INTERRUPTER
- RECEPTACLE, QUADRAPLEX
- EM — RECEPTACLE, QUADRAPLEX - EMERGENCY
- RECEPTACLE, QUADRAPLEX - CEILING
- RECEPTACLE, SIMPLEX
- POWER GROUND MODULE, REFER TO TYPE 7A DETAIL 7/E-502
- POWER GROUND MODULE, REFER TO TYPE 7B DETAIL 7/E-502
- POWER GROUND MODULE, REFER TO TYPE 7C DETAIL 7/E-502
- A — RECEPTACLE, SPECIAL PURPOSE
  A = 120V, 20A, 1 PHASE, 2-POLE, 3W, NEMA 5-20R.
  B = 208V, 20A, 1 PHASE, 2-POLE, 3W, NEMA 6-20R.
  C = 120V, 30A, 1 PHASE, 2-POLE, 3W, NEMA 5-30R.
  D = 208V, 30A, 1 PHASE, 2-POLE, 3W, NEMA L6-30R.
  E = 208V, 60A, 1 PHASE, 3-POLE, 4W, NEMA 14-60R.
  F = 208V, 30A, 3 PHASE, 3-POLE, 4W, NEMA 15-30R.
  G = 208V, 50A, 3 PHASE, 3 POLE, 4W, NEMA 15-30R.
  H = 208V, 60A, 3 PHASE, 3 POLE, 4W, NEMA 15-60R.
- 2' — ELECTRICAL STRIP MOLD (OUTLETS ON 2'-0" CENTERS OR AS DESIGNATED ON DRAWINGS), MTD 3'-6" AFF OR AS INDICATED.
- J — JUNCTION BOX (WALL, GENERIC, FLOOR, RESPECTIVELY)
- C — CLOCK RECEPTACLE
- G — GROUND REFERENCE POINT
- PB — PULL BOX
- $M — MANUAL MOTOR STARTING
- DISCONNECT SWITCH, FUSED
- DISCONNECT SWITCH, UNFUSED
- STARTER, COMBINATION WITH DISCONNECT SWITCH
- STARTER OR MOTOR CONTROLLER
- ENCLOSED CIRCUIT BREAKER
- VARIABLE FREQUENCY DRIVE
- M — METER
- SPD — SURGE PROTECTION DEVICE
- UPS — UNINTERRUPTED POWER SUPPLY
- EPO — EMERGENCY POWER OFF
- A — PUSH BUTTON
- LIGHTNING PROTECTION AIR TERMINAL
- L — LIGHTNING PROTECTION SYSTEM WIRE

ELECTRICAL SINGLE LINE SYMBOLS

- PANEL "NAME" "VOLT" "LOCATION 1" "LOCATION 2" "LOCATION 3" — BRANCH CIRCUIT PANEL, SINGLE LINE
- ##KVA 480-208V ROOM # #% — TRANSFORMER, SINGLE LINE
- ENCLOSED CIRCUIT BREAKER — ###A/3P — ENCLOSED CIRCUIT BREAKER, SINGLE LINE
- TRANSFORMER, DELTA CONNECTION
- TRANSFORMER, WYE CONNECTION
- POTENTIAL TRANSFORMER
- CURRENT TRANSFORMER
- EARTH GROUND
- FUSE WITH RATING
- CIRCUIT BREAKER
- LOW-VOLTAGE DRAWOUT CIRCUIT BREAKER
- MEDIUM-VOLTAGE DRAWOUT CIRCUIT BREAKER
- SPD — SURGE PROTECTIVE DEVICE WITH INTEGRAL DISC.
- G — 5 KW — GENERATOR, POWER
- 3 — MOTOR
- NORMALLY CLOSED RELAY CONTACT
- NORMALLY OPEN RELAY CONTACT

SECURITY SYMBOLS

- SECURITY ACCESS, BUZZER. MTD 1'-6" AFF UNLESS OTHERWISE NOTED
- M/T — CARD ACCESS READER; LETTER INDICATES AS FOLLOWS:
  M=MOUNT
  C-CEILING D-DESK F-FLUSH
  H-HIDDEN M-MULLION P-PEDESTAL
  R-RACK S-SURFACE W-WALL
  T=TECHNOLOGY/TYPE
  B-BARCODE F-ELEV FLOOR CALL
  H-ELEV HALL CALL M-MAG STRIP
  P-PROXIMITY S-SMART CARD T-TOKEN
- M/T — INTERCOM; LETTER INDICATES AS FOLLOWS:
  M=MOUNT
  C-CEILING D-DESK F-FLUSH
  H-HIDDEN M-MULLION P-PEDESTAL
  R-RACK S-SURFACE W-WALL
  T=TECHNOLOGY/TYPE
  M-MASTER S-SUBSTATION
- M/T — PUSH BUTTON; LETTER INDICATES AS FOLLOWS:
  M=MOUNT
  C-CEILING D-DESK F-FLUSH
  H-HIDDEN M-MULLION P-PEDESTAL
  R-RACK S-SURFACE W-WALL
  T=TECHNOLOGY/TYPE
  B-BELL PUSH D-DURESS P-PANIC
  R-DOOR RELEASE W-WAVE PLATE
  X-REQUEST-FOR-EXIT
- M — PTZ — SECURITY ACCESS, VIDEO CAMERA WITH LENS
  M = MOTION DETECTOR
  PZ = DETECTOR WITH PAN AND ZOOM
  PTZ = DETECTOR WITH PAN, TILT, AND ZOOM
- ACP — ACCESS CONTROL PANEL - WANDERGUARD SYSTEM
- 40' — SECURITY ACCESS, VIDEO CAMERA WITH LENS, ANGLE OF VIEW
  - BASIS OF DESIGN IS AVIGILON.
  - PROVIDE MANUFACTURER RECOMMENDED POE CABLE FROM CAMERA TO HEADEND LOCATED IN ROOM BC-114.

ELECTRICAL LIGHTING SYMBOLS

- S — OS — SWITCH
  a = (LOWER CASE) FIXTURE SWITCHING INTENT
  D = DIMMER
  LV = LOW VOLTAGE
  M = MANUAL MOTOR STARTING
  OS = OCCUPANCY SENSOR (W/ MANUAL OVERRIDE)
  WP = WEATHER PROOF
- OS — OCCUPANCY SENSOR (CEILING OR WALL MOUNTED)
- PC — PHOTOCELL
- UPPERCASE LETTER INDICATES FIXTURE TYPE (TYP)
- LOWERCASE LETTERS INDICATE SWITCHING INTENT (TYP)
- A a — LIGHT FIXTURE, TYPE AS INDICATED IN FIXTURE SCHED, NORMAL POWER, (TYP)
- # — INDICATES RELAY NUMBER (TYP)
- n1 — INDICATES MICRO RELAY PANEL CONTROLLING FIXTURE (TYP)
- INDICATES RELAY DESIGNATION (TYP)
- PANEL NAME AND/OR CIRCUIT # (TYP)
- INDICATES TYPE OF EMERGENCY POWER (TYP ALL EMERGENCY FIXTURES)
- CR — HALF SHADED LIGHT FIXTURE, EMERGENCY POWER (TYP):
  BLANK = LIFE SAFETY
  LS = LIFE SAFETY
  CR = CRITICAL POWER
  NL = NIGHT LIGHT
- INDUSTRIAL PENDANT HUNG LIGHT FIXTURE, NORMAL POWER
- INDUSTRIAL PENDANT HUNG LIGHT FIXTURE; EMERGENCY POWER
- LIGHT FIXTURE, WALL MOUNTED, NORMAL POWER
- LIGHT FIXTURE, WALL MOUNTED, EMERGENCY POWER
- DOWNLIGHT FIXTURE CEILING MOUNTED, NORMAL POWER
- DOWNLIGHT FIXTURE CEILING MOUNTED, EMERGENCY POWER
- WALL MOUNTED, NIGHT LIGHT FIXTURE
- EXIT SIGN: ARROW DIRECTION INDICATED ON PLANS. SINGLE SHADING INDICATES SINGLE FACE. TWO SHADED AREAS INDICATES DOUBLE FACED UNIT. — CEILING — WALL

COMMUNICATION SYMBOLS

- TELE/DATA OUTLET
- DATA OUTLET
- TELEPHONE OUTLET
  BLANK = TYPICAL MOUNTING HEIGHT
  W = WALL MOUNTED AT 58" AFF
- 3-GANG COMPARTMENT BOX IN FLOOR FOR TELEPHONE, DATA & RECEPTACLE.
- TV — TELEVISION CABLE JACK, CEILING MOUNTED
  PROVIDE BACKBOX AND 1" C. TO ACCESSIBLE CEILING.
- TV — TELEVISION CABLE JACK, WALL MOUNTED. VERIFY HEIGHT BEFORE INSTALLING.
  PROVIDE BACKBOX AND 1" C. TO ACCESSIBLE CEILING.
- S — PUBLIC ADDRESS SPEAKER, CEILING MOUNTED
- S — SPEAKER, WALL MOUNTED, MOUNTED 7'-6" AFF UON.
- CABLE TRAY
- WAP S — WIRELESS ACCESS POINT
  S = STAFF NETWORK
  G = GUEST NETWORK
- C — CENTRAK DEVICE, CEILING MOUNTED

NURSE CALL SYMBOLS

- NCS — NURSE'S CALL MASTER STATION MTD ON NURSE'S COUNTER TOP UNLESS OTHERWISE NOTED.
- NCT — NURSE CALL TERMINAL CABINET.
- N E — NURSE CALL STATION.
  2 = DUPLICATE FACILITIES FOR TWO BEDS (SEPARATE INDICATORS AT MASTER STATION) MTD 5'-0" AFF UNLESS OTHERWISE NOTED.
  CB = CODE BLUE STATION. MTD 5'-0" AFF UNLESS NOTED OTHERWISE.
  D = DUTY STATION. MTD 5'-0" AFF UNLESS NOTED OTHERWISE.
  E = MTD 6'-0" AFF FOR SHOWER LOCATION, MTD 4'-6" AFF FOR TUB LOCATION, & MTD 3'-0" AFF FOR TOILET LOCATION.
  P = PSYCHIATRIC CORRIDOR STATION WITH KEY SWITCH
  S = AUDIO VISUAL MALL STATION (STAFF) MTD 5'-0" AFF UNLESS OTHERWISE NOTED.
  U = UTILITY CALL STATION, MTD 5'-0" AFF UNLESS OTHERWISE NOTED.
- 2 N D — NURSE CALL DOME LIGHT.
  (CEILING OR WALL RESPECTIVELY)
  2 = NURSE'S CALL DOME LIGHT (SUFFIX INDICATES No OF LAMP) MTD 6" ABOVE DOOR.
  D = CORRIDOR DOME LIGHT.
  I = AUXILIARY INTERSECTIONAL DOME LIGHT.

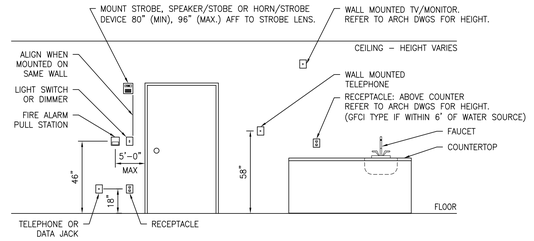

1 TYPICAL DEVICE MOUNTING HEIGHTS
SCALE: NTS
ALL DIMENSIONS SHOWN ARE TYPICAL UNLESS OTHERWISE NOTED.

PRINTS OF THIS DRAWING SHALL NOT BE USED FOR ANY PURPOSE WHATSOEVER WITHOUT THE SEAL AND SIGNATURE OF THE PROFESSIONAL ENGINEER.

NO.	DESCRIPTION	DATE

CONSULTANTS

Architecture:	Civil Engineering:	Fire & Life Safety:
PF&A DESIGN, P.C.	LABELLA ASSOCIATES	STANTON ENGINEERING SERVICES, LLC

ENGINEER OF RECORD

MILLER•REMICK
A Service-Disabled Veteran-Owned Small Business
(856) 429-4000 • Miller-Remick.com
M-R PROJECT NO. 0499-0136

MILLER-REMICK LLC PROFESSIONAL ENGINEER
COMMONWEALTH OF PENNSYLVANIA — REGISTERED PROFESSIONAL — THOMAS REGINO — ENGINEER No. PE094115
12/30/25

Office of Construction and Facilities Management

VA U.S. Department of Veterans Affairs

Drawing Title	ELECTRICAL ABBREVIATIONS & SYMBOLS
Approved by:	Jon Manninen, COR
Phase	BID DOCUMENTS
	FULLY SPRINKLERED
Project Title	RENOVATE SURGICAL SUITE PHASE II
Project Number	658-19-103
Location	SALEM VA MEDICAL CENTER
Issue Date	2025-12-30
Checked	LIB
Drawn	MJR
VA Drawing Number	2617
Building Number	143
Drawing Number	E-001

VA FORM 08-6231

P:\0499_OVA\0499-0136 Salem Renovate Surgical Suite\4_Drawings\1_Cad\1_Current Submittal Phase\7_Electrical\E-001.dwg 12-29-25 08:26:04 AM MRonca

three inches = one foot 6"
one and one half inches = one foot 0 6" 1 2
one inch = one foot 0 6" 2
three quarters inch = one foot 0 6" 2 4
one half inch = one foot 0 4 8
three eighths inch = one foot 0 4 8
one quarter inch = one foot 0 4 8 16
one eighth inch = one foot 0 4 8 16

P:\0499_DVA\0499-0136 Salem Renovate Surgical Suite\4_Drawings\1_Cad\1_Current Submittal Phase\7_Electrical\E-002.dwg 12-29-25 08:25:59 AM MRonca

ELECTRICAL DEMOLITION NOTES:

1. THE CONTRACTOR MUST INCLUDE IN HIS BID ALL COSTS ASSOCIATED WITH RELOCATION AND REMOVAL OF ELECTRICAL WORK AS DESCRIBED IN THE DRAWINGS AND SPECIFICATIONS WITH ALLOWANCES FOR EXPECTED OR UNFORESEEN ISSUES WHEN CONCEALED WORK HAS BEEN EXPOSED. NO ADDITIONAL CLAIMS FOR WORK ASSOCIATED WITH DEMOLITION WILL BE ACCEPTED, UNLESS, IN CERTAIN CASES, CONSIDERED JUSTIFIABLE BY THE ENGINEER.
2. NOTE THAT THE FACILITY WILL BE OPERATIONAL DURING THE COURSE OF THIS PROJECT.
   2.1. THE CONTRACTOR IS TO COORDINATE ALL OF THE DEMOLITION WORK WITH THE FACILITY PERSONNEL TO MINIMIZE DISTURBING THE OPERATING EQUIPMENT, WIRING AND SYSTEMS.
   2.2. THE CONTRACTOR MUST PERFORM REMOVAL AND DEMOLITION WORK WITH MINIMAL INTERFERENCE WITH EXISTING SYSTEMS.
   2.3. IF NECESSARY THE CONTRACTOR MUST PROVIDE TEMPORARY POWER FOR THE FACILITY.
3. DEMOLITION AND REMOVAL OF WORK MUST BE PERFORMED IN A NEAT AND PROFESSIONAL MANNER. THE CONTRACTOR MUST RESTORE, PATCH, PAINT, ETC., ANY INTERIOR/EXTERIOR BUILDING SURFACE TO ITS ORIGINAL CONDITION.
4. REFER TO ELECTRICAL DEMOLITION AND RENOVATION PLANS FOR NEW EQUIPMENT LAYOUT AND EXTENT OF EQUIPMENT BEING REPLACED, RELOCATED, OR REMOVED. COORDINATE WITH ALL TRADES AS TO EXTENT OF EQUIPMENT BEING REMOVED OR RELOCATED. CLOSELY COORDINATE THE EXTENT OF DEMOLITION SCOPE OF WORK WITH ARCHITECT, ENGINEER AND/OR MECHANICAL PLANS. PATCH AND PAINT (TO MATCH SURROUNDING CONDITIONS) ALL OPENINGS CREATED BY THIS DEMOLITION.
5. EXISTING CONDITIONS, EQUIPMENT, MATERIALS & SIZES ARE SHOWN FOR REFERENCE ONLY. VERIFY EXISTING CONDITIONS AND BRING ANY DISCREPANCIES TO THE ENGINEER'S ATTENTION IN WRITING PRIOR TO BID SUBMISSION.
6. ELECTRICAL CONTRACTOR IS RESPONSIBLE FOR ALL ELECTRICAL DEMOLITION WORK FOR THIS PROJECT WHETHER OR NOT SPECIFICALLY INDICATED ON THIS OR OTHER DEMOLITION PLANS. THIS WORK INCLUDES BUT IS NOT LIMITED TO THE DISCONNECTION, REMOVAL AND DISPOSAL OF: LIGHTING FIXTURES, PANELBOARDS, DISCONNECT SWITCHES, RECEPTACLES, JUNCTION BOXES, WIRE, CABLE, CONDUIT, MOUNTING HARDWARE STRAPS OR CABLES, ELECTRICAL SERVICES ETC. PER THE SCOPE OF WORK FOR THIS PROJECT.
7. THE ELECTRICAL CONTRACTOR MUST REMOVE ALL ELECTRICAL OUTLETS, SWITCHES, ETC., INCLUDING ASSOCIATED WIRING, CONDUITS, COVERS, BOXES, ETC., WHERE SHOWN ON THE DEMOLITION DRAWING. WHERE THE REMOVAL OF THESE ITEMS DISRUPTS EXISTING WIRING THAT IS TO REMAIN, THE CONTRACTOR MUST INSTALL IN THE CEILING SPACE; JUNCTION BOXES AND OTHER DEVICES AND PROVIDE BYPASS CONNECTIONS NECESSARY TO MAKE CIRCUITS AFFECTED CONTINUOUS AND READY FOR OPERATION. OTHERWISE, WIRING MUST BE REMOVED BACK TO THE NEAREST ELECTRICAL JUNCTION BOX THAT IS TO REMAIN OR TO THE SOURCE PANELBOARD.
8. ALL WORK MUST BE SCHEDULED AND PERFORMED AS NOT TO INTERRUPT NORMAL OPERATIONS. REMOVAL OF ITEMS THAT WILL CAUSE ANY TYPE OF TEMPORARY SHUTDOWN MUST BE PERFORMED DURING OFF-PEAK HOURS. ALL SUCH OUTAGES MUST BE SCHEDULED AND COORDINATED WITH OWNER FIELD REPRESENTATIVE TO ENSURE ESSENTIAL SERVICES OR AREAS CAN BE MAINTAINED.
9. THE CONTRACTOR MUST NOTIFY THE OWNER AT THE APPROPRIATE TIME OF THE PROJECTED DEMOLITION AND PHASING SCHEDULE SO THAT REMOVAL OR RELOCATION OF AFFECTED UTILITIES MAY BE CARRIED OUT IN COORDINATION WITH THE PROJECT REQUIREMENTS. THE CONTRACTOR MUST CLOSELY FOLLOW THE DEMOLITION AND PHASING SCHEDULE AND PROCEED IN THE SPECIFIED SEQUENCE.
10. THE SHUTDOWN OF EXISTING BUILDING ELECTRICAL SERVICES MUST BE COORDINATED WITH THE OWNER. MAKE APPROPRIATE ARRANGEMENTS AT LEAST 10 BUSINESS DAYS PRIOR TO A SHUTDOWN.
11. THE CONTRACTOR MUST REMOVE AND/OR RELOCATE ALL EXISTING ELECTRICAL WORK WHICH INTERFERES WITH THE NEW ELECTRICAL AND ARCHITECTURAL LAYOUTS IN FULL COORDINATION WITH THE ENGINEER'S DEMOLITION PLANS. ALL SYSTEMS WHICH ARE NO LONGER REQUIRED TO FUNCTION MUST BE DE-ENERGIZED AND DISCONNECTED AT THE POWER SUPPLY SOURCE.
12. ELECTRICAL CONTRACTOR MUST PROVIDE AND MAINTAIN ANY CONNECTIONS / DISCONNECTIONS AS NEEDED TO ENSURE ADEQUATE SAFETY AND PROTECTION OF ALL PERSONNEL AND EQUIPMENT.
13. ALL ELECTRICAL PANELS MUST BE MAINTAINED AS WORKING PANELS THROUGHOUT CONSTRUCTION AND WILL CONTINUE TO MAINTAIN CIRCUITS FOR EXISTING LIGHTING OR EQUIPMENT TO REMAIN. PROVIDE AS NECESSARY TEMPORARY LIGHTING AND ELECTRICAL FEEDS TO ANY DEVICES THAT MAY BE REQUIRED FOR UNINTERRUPTED USE. PROVIDE TEMPORARY CONNECTIONS FOR RELOCATED EQUIPMENT DURING CONSTRUCTION.
14. ELECTRICAL CONTRACTOR MUST ENSURE THAT ANY DEVICES AND/OR FIXTURES LOCATED OUTSIDE OF DEMOLITION WORK AREA ARE NOT AFFECTED BY REMOVAL OF WIRING AND/OR CIRCUITING. WIRING/CONDUIT MUST BE LEFT IN A SAFE CONDITION, LABELED FOR ITS USE, AND EXTENDED AS REQUIRED TO MAINTAIN CIRCUIT CONTINUITY, INCLUDING ALL APPLICABLE CONTROLS.
15. PORTIONS OF FEEDER RUNS THAT MUST BE REMOVED OR ABANDONED AS A RESULT OF DEMOLITION WORK, BUT WHICH ARE REQUIRED TO REMAIN ENERGIZED, MUST BE CUT AT CONVENIENT LOCATIONS, REROUTED AND RECONNECTED. NEW FEEDER EXTENSIONS MUST MATCH EXISTING FEEDER EXTENSIONS IN ALL ASPECTS INCLUDING BUT NOT LIMITED TO CABLE TYPE, CONDUIT SIZES, CONDUCTOR AMPACITY, ETC..
16. ALL EXISTING LOW VOLTAGE WIRING FOR FIRE ALARM/SECURITY, SOUND, AND/OR TELECOMMUNICATIONS THAT IS NOT REUSED MUST BE REMOVED IN ITS ENTIRETY BY THE RESPONSIBLE CONTRACTOR. ALL EXISTING LOW VOLTAGE WIRING FOR MECHANICAL SYSTEMS THAT ARE NOT USED MUST BE REMOVED IN ITS ENTIRETY BY THE CONTRACTOR.
17. CONTRACTOR IS TO EXERCISE EXTREME CAUTION WHEN CUTTING SLAB TO AVOID DAMAGE TO ANY EXISTING CONDUITS, PIPING, ETC. THAT MAY BE CONCEALED IN OR BENEATH THE SLAB. ANY FLOOR SLAB AFFECTED BY THE REMOVAL OF DEVICES FED VIA UNDERGROUND CONDUIT OR WIRING, MUST BE FIRESTOPPED AND PATCHED BY THE GENERAL CONTRACTOR AND TO MATCH SURROUNDING FLOOR.
18. ELECTRICAL CONTRACTOR IS RESPONSIBLE FOR DISCONNECTING, RELOCATING, AND/OR RECONNECTING ALL EXISTING EQUIPMENT THAT IS TO REMAIN, EVEN IF THIS EQUIPMENT IS NOT SHOWN ON PLANS OR PANEL SCHEDULES. ELECTRICAL CONTRACTOR IS RESPONSIBLE FOR EXTENDING EXISTING CIRCUITS FROM EXISTING EQUIPMENT THAT IS REMAINING TO NEW LOCATION. CONTRACTOR MUST MATCH EXISTING GAUGE WIRE FROM EXISTING BREAKER TO RELOCATED EQUIPMENT.
19. IN THE EVENT THAT ELECTRICAL PLANS CALL FOR EXISTING WIRING TO BE REUSED, THE ELECTRICAL CONTRACTOR MUST SURVEY EXISTING WIRING, BOXES, ETC. TO DETERMINE IF THE EXISTING BRANCH CIRCUIT MAY BE REUSED FOR NEW EQUIPMENT (IF WIRING REMAINS IN ITS ORIGINAL CONDUIT). ELECTRICAL CONTRACTOR MUST DETERMINE THAT THE ENTIRE RUN OF EXISTING POWER CONDUIT AND WIRING, FROM SOURCE PANEL TO LOAD FOR WIRING TO BE REUSED, IS FEASIBLE FOR REUSE AND MEETS THE REQUIREMENTS OF THE NATIONAL ELECTRICAL CODE, STATE AND LOCAL CODES HAVING JURISDICTION.

    IN INSTANCES WHERE EXISTING CIRCUITS ARE TO BE EXTENDED OR REUSED, ELECTRICAL CONTRACTOR MUST DISCONNECT EXISTING BRANCH CIRCUIT AND LEAVE IN A SAFE CONDITION (TAG AND LABEL ITS USE) FOR FUTURE RECONNECTION DURING RENOVATION PHASE.
20. ALL WIRING NOT INDICATED FOR REUSE MUST BE DISCONNECTED AND REMOVED FROM LOAD TO SOURCE (INCLUDING DATA, COMMUNICATION, OR TELEPHONE WIRING). ANY CONDUITS STUBBED OUT OF MASONRY SURFACE MUST BE CUT INTO SURFACE AND PATCHED TO MATCH SURROUNDING CONDITIONS.
21. PANELBOARD CABINETS WILL NOT BE USED FOR OTHER PURPOSES THAN CIRCUIT BREAKER INSTALLATIONS AND DISTRIBUTION POINTS, AND WILL NOT BE USED AS A JUNCTION OR PULLBOX.
22. ALL UNUSED OUTLET BOXES THAT ARE TO REMAIN MUST BE PROVIDED WITH MATCHING BLANK COVERS.
23. ALL RACEWAYS WHICH ARE EXPOSED AS A RESULT OF NEW WORK MUST BE REMOVED AND REROUTED CONCEALED BEHIND FINISHED SURFACES.
24. EXISTING RACEWAYS THAT ARE NOT BEING REUSED MUST BE REMOVED BACK TO THE NEAREST JUNCTION OR PULLBOX, AND THE OPENINGS BLANKED. ANY CONDUITS PENETRATING MASONRY SURFACES MUST BE CUT INTO SURFACE, PATCHED, AND PAINTED TO MATCH SURROUNDINGS.
25. DISCONNECT, RELOCATE OR REMOVE ELECTRICAL INSTALLATIONS AND EQUIPMENT AS INDICATED BY PLANS AND AS REQUIRED BY CHANGES IN CONSTRUCTION. WHERE EXISTING ELECTRICAL INSTALLATIONS INTERFERE WITH NEW WORK AND WHERE SUCH INSTALLATIONS ARE TO REMAIN IN USE, THE NEW INSTALLATIONS MUST BE RELOCATED AND/OR RECONNECTED TO COORDINATE WITH THE WORK INDICATED ON THE CONTRACT DRAWINGS. DETERMINE AND COORDINATE ALL EQUIPMENT LOCATIONS PRIOR TO INITIAL ROUGH-IN.
26. DISCONNECT AND RELOCATE/RECONNECT ANY ELECTRICAL LINES, BRANCH CIRCUITS, DEVICES (INCLUDING FIRE ALARM DEVICES), ETC. AND REPAIR PULL BOXES THAT MAY BE DISTURBED DURING THIS RENOVATION. UNLESS NOTED OTHERWISE, ALL EXISTING ELECTRICAL WORK WHICH WILL NOT BE RENDERED OBSOLETE AND WHICH MAY BE DISTURBED DUE TO ANY CHANGES REQUIRED UNDER THE CONTRACT, MUST BE RESTORED TO ITS ORIGINAL OPERATING CONDITION AT NO COST TO OWNER. IF ANY EQUIPMENT TO REMAIN IS DAMAGED DURING CONSTRUCTION, IT MUST BE REPLACED WITH NEW (WITH NO COST APPLIED TO OWNER).
27. FOR EXISTING PANELS MODIFIED AS PART OF THIS PROJECT, E.C. MUST TEST AND KEEP ALL EXISTING WORKING CIRCUIT BREAKERS AND MUST USE THEM FOR NEW EQUIPMENT, DEVICES, LIGHTING, AND/OR SPARES. E.C. MUST REPLACE NON-WORKING BREAKERS WITH NEW "IN KIND" BREAKERS. PROVIDE BLANK COVERS/COVERPLATES FOR ALL EXPOSED CIRCUIT BREAKER SPACES (THOSE WITHOUT INSTALLED CIRCUIT BREAKERS; EXPOSED BUS BARS) FOR PERSONNEL PROTECTION.
26. ALL MATERIALS AND EQUIPMENT TO BE DEMOLISHED ARE TO BE DISPOSED OF BY THE CONTRACTOR, UNLESS DIRECTED OTHERWISE BY THE OWNER. CONTRACTOR IS RESPONSIBLE FOR DISPOSAL OF ALL MATERIALS IN ACCORDANCE WITH LOCAL AND FEDERAL LAWS. ALL MATERIALS THAT ARE CONSIDERED TO BE RECYCLABLE ARE TO BE RECYCLED ACCORDINGLY BY THE CONTRACTOR.
27. REMOVAL OF BRANCH CIRCUITS IN ASSOCIATED PANELS MUST BE COORDINATED WITH THE REMOVAL OF EQUIPMENT IN SPECIFIED AREA. REFER TO RENOVATION PLANS AND ELECTRICAL PANEL SCHEDULES FOR NEW CIRCUITING ARRANGEMENT. ANY WIRING OR CIRCUITS BEING REVISED MUST MEET MINIMUM WIRE SIZES AS INDICATED ON DRAWINGS. ELECTRICAL CONTRACTOR MUST REMOVE WIRING/CONDUIT BACK TO SOURCE FROM UNUSED OR ABANDONED CIRCUITS. LABEL CIRCUIT BREAKER AS "SPARE", AND LEAVE IN THE "OFF" POSITION.
28. EXISTING PANELBOARD DIRECTORIES AFFECTED BY THE ALTERATION WORK MUST BE REPLACED WITH NEW "TYPED" DIRECTORIES, TO ACCURATELY REFLECT THE BRANCH CIRCUIT WIRING MODIFICATIONS AND EXISTING CONDITIONS.

GENERAL NOTES AND CONDITIONS:

1. THESE DRAWINGS WERE PREPARED FROM INFORMATION TAKEN FROM THE AVAILABLE BUILDING DRAWINGS, ARCHITECTURAL BACKGROUNDS PROVIDED BY THE OWNER AND FIELD SURVEY INFORMATION COMPILED BY THE ENGINEERING DESIGN TEAM FOR THE PURPOSE OF ENGINEERING DESIGN. EXISTING CONDITIONS ARE SHOWN AS ACCURATELY AS POSSIBLE. THERE IS THE POSSIBILITY THAT CONDITIONS SHOWN ARE NOT EXACTLY AS EXISTING. CONTRACTOR MUST VERIFY ALL DIMENSIONS, ELEVATIONS, LOCATIONS, SIZES AND CONDITIONS AT THE SITE AND REPORT ANY DISCREPANCIES TO THE ARCHITECT PRIOR TO BEGINNING INSTALLATION OR FABRICATION WORK.
   1.1. DRAWINGS ARE DIAGRAMMATIC.
   1.2. SHOULD IT APPEAR THAT THE WORK INTENDED TO BE DESCRIBED OR RELATED WORK ARE NOT SUFFICIENTLY DETAILED OR EXPLAINED ON THE DRAWINGS, OR IN THE SPECIFICATIONS, CONSULT THE ENGINEER FOR NECESSARY CLARIFICATIONS, AND CONFORM TO THOSE CLARIFICATIONS INSOFAR AS THEY ARE CONSISTENT WITH THE ORIGINAL DRAWINGS AND SPECIFICATIONS. IN NO CASE MUST WORK PROCEED IN UNCERTAINTY.
   1.3. EQUIPMENT ARRANGEMENTS ARE DESIGNED TO SHOW PREFERRED CONFIGURATIONS TO SUIT KNOWN CONDITIONS. ACTUAL INSTALLATION BY CONTRACTOR MAY BE ALTERED AS REQUIRED TO SUIT FIELD CONDITIONS ENCOUNTERED DURING CONSTRUCTION WITHOUT COMPROMISING THE INTENT OF THE ORIGINAL DESIGN.
   1.4. THE CONTRACTOR MUST CHECK AND VERIFY ALL DIMENSIONS AND CONDITIONS AT SITE PRIOR TO STARTING WORK.
2. THE CONTRACTOR WILL BE RESPONSIBLE FOR ENSURING THAT ALL RULES AND REGULATIONS, INCLUDING THOSE WHICH MAY BE ISSUED BY THE OWNER, ARE BEING OBSERVED, PARTICULARLY WORKPLACE SAFETY AND THE CONDUCT OF ALL THOSE EMPLOYED DIRECTLY AND INDIRECTLY BY HIM ON THE PREMISES, AND THE OWNER'S EMPLOYEES WHO MAY BE IMPACTED OR AFFECTED BY CONSTRUCTION ACTIVITIES. THE CONTRACTOR WILL INSTALL SIGNAGE, BARRIERS, AND OTHER MEANS TO PROVIDE WARNING AND PERSONNEL SAFETY. PLACEMENT OF THESE ITEMS WILL BE COORDINATED WITH THE OWNER AND HIS ONGOING OPERATIONS AND WILL PROMPTLY BE REVISED WHEN WORK IN A PARTICULAR AREA HAS BEEN COMPLETED.
   2.1. DURING PERFORMANCE OF WORK, THE CONTRACTOR MUST BE RESPONSIBLE FOR PROVISION AND MAINTENANCE OF WARNING SIGNS, LIGHT SIGNAL DEVICES, GUARD LIGHTS, BARRICADES, GUARD RAILS, FENCES AND OTHER DEVICES, APPROPRIATELY LOCATED ON AND AROUND THE JOB SITE WHICH GIVE PROPER AND UNDERSTANDABLE WARNING TO PERSONS WITH REGARD TO HAZARDOUS CONDITIONS, EQUIPMENT AND OPERATIONS BEING PERFORMED IN CONJUNCTION WITH THE WORK.
3. THIS INSTALLATION WILL CONFORM TO ALL CODES AND THE REQUIREMENTS OF FEDERAL, STATE, AND LOCAL REGULATORY AGENCIES HAVING JURISDICTION INCLUDING, BUT NOT LIMITED TO THE FOLLOWING:

   ELECTRICAL: NATIONAL ELECTRIC CODE: NFPA 70 – LATEST EDITION
4. ALL WORK WILL BE LAWFULLY EXECUTED IN A NEAT AND WORKMANLIKE MANNER AND WILL BE COMPLETED IN ACCORDANCE WITH THE GOVERNING CODES (ABOVE), INDUSTRY STANDARDS, AND IN CONFORMANCE WITH THE MANUFACTURERS RECOMMENDATIONS AND REQUIREMENTS.
5. WORK UNDER THIS CONTRACT CONSISTS OF THE CONTRACTOR PROVIDING ALL LABOR, MATERIALS, AND SERVICES, INCLUDING WORK NOT SPECIFICALLY SHOWN BUT REASONABLY IMPLIED. THIS INCLUDES CUTTING, PATCHING AND RESTORATION OF EXISTING SURFACES DAMAGED DURING THE CONSTRUCTION. CONTRACTOR MUST ALSO PROVIDE ALL EQUIPMENT SHOWN OR SPECIFIED OR AN APPROVED EQUIVALENT. SUBSTITUTED EQUIPMENT OR MATERIALS MUST NOT BE INSTALLED UNTIL GIVEN WRITTEN APPROVAL BY THE OWNER.
6. EACH TRADE CONTRACTOR IS WHOLLY RESPONSIBLE FOR PROVIDING, INSTALLING, AND MAINTAINING ALL TEMPORARY POWER SOURCES AND ANY REQUIRED UTILITIES FOR ANY TEMPORARY MECHANICAL, PLUMBING, AND/OR ELECTRICAL EQUIPMENT OR SYSTEMS (REQUIRED BY THEIR INDIVIDUAL TRADES SCOPE OF WORK) DURING THE COURSE OF CONSTRUCTION AND PHASING/SEQUENCING OF WORK. THIS INCLUDES BUT IS NOT BE LIMITED TO THE INSTALLATION AND ROUTING OF: TEMPORARY FEEDERS, CONDUIT, TRANSFORMERS, CONTRACTOR-SITE GENERATOR PACKAGES, OVERCURRENT PROTECTION DEVICES, DISCONNECTS, CONNECTIONS AND DISCONNECTION OF EQUIPMENT, ETC. ALL ELECTRICAL WORK MUST BE PERFORMED BY A LICENSED ELECTRICIAN. REFER TO SPECIFICATIONS FOR ADDITIONAL INFORMATION.
7. CONTRACTOR IS RESPONSIBLE FOR COSTS INCURRED FOR NONCOMPLIANCE WITH THESE CONTRACT DOCUMENTS. CONTRACTOR WILL NOT BE ALLOWED CHANGE ORDERS FOR PROBLEMS ARISING FROM NEGLECT OF PROVISIONS INCLUDED IN THESE CONDITIONS.
8. MAINTAIN ORDERLY HOUSEKEEPING DURING CONSTRUCTION, AND UPON SUBSTANTIAL COMPLETION PERFORM FINAL CLEANUP. REMOVE CONSTRUCTION RUBBISH, SCAFFOLDING, EQUIPMENT, TEMPORARY PROTECTION, TEMPORARY FIELD STRUCTURES, AND OTHER MATERIALS OR EQUIPMENT THAT WAS REQUIRED IN CONNECTION WITH THE CONSTRUCTION, BUT NOT A PERMANENT PART THEREOF.
9. THOSE PERFORMING WORK AS A CONTRACTOR MUST EXAMINE SUBSTRATES AND CONDITIONS UNDER WHICH THE WORK IS TO BE PERFORMED AND NOTIFY THE CONTRACTOR IN WRITING, OF CONDITIONS DETRIMENTAL TO THE PROPER AND TIMELY COMPLETION OF THE WORK. COMMENCEMENT OF WORK BY A TRADE ON A SURFACE OR CONSTRUCTION IMPLIES ACCEPTANCE OF SUCH SURFACE OR CONSTRUCTION. DO NOT PROCEED WITH INSTALLATION UNTIL UNSATISFACTORY CONDITIONS HAVE BEEN CORRECTED.
10. THE CONTRACTOR MUST SECURE ALL APPLICATIONS AND PAY ANY AND ALL FEES AS REQUIRED. THE CONTRACTOR MUST GIVE ALL NECESSARY NOTICES AND CERTIFICATES OF INSPECTION REQUIRED BY THE AUTHORITIES HAVING JURISDICTION. DELIVER ALL CERTIFICATES AND APPROVALS TO THE OWNER AGENT PRIOR TO FINAL ACCEPTANCE OF THE WORK. THE CONTRACTOR MUST FILE NECESSARY DRAWINGS, PREPARE DOCUMENTS AND MAKE APPLICATIONS FOR EACH REQUIRED INSPECTION, PRIOR TO COMMENCING WORK TO AVOID DELAYS DURING CONSTRUCTION.
11. CONTRACTOR MUST SUBMIT SHOP DRAWINGS AND MANUFACTURERS DATA SHEETS ON ALL EQUIPMENT AND MATERIALS SPECIFIED ON DRAWINGS FOR APPROVAL BY OWNER OR AGENT FOR THE OWNER. THESE DRAWINGS OR SHEETS MUST CONTAIN ALL NECESSARY DATA, I.E., MANUFACTURER, CATALOG NUMBER, SIZE, DIMENSIONS, CAPACITY, WIRING DETAILS AND ALL OTHER ENGINEERING DATA AND DETAILS NECESSARY FOR COMPLETE CLARITY AND INSTALLATION.
12. THE CONTRACTOR MUST KEEP ONE SET OF THE LATEST ISSUE OF DRAWINGS WHICH MUST REFLECT THE ACTUAL INSTALLED CONDITIONS AND CONNECTIONS OF ALL EQUIPMENT AND DEVICES. THE CONTRACTOR MUST PROVIDE COPIES OF ALL MAINTENANCE INFORMATION AND INSTRUCTIONS RECEIVED WITH EQUIPMENT AND SYSTEMS, ALL "AS-BUILT" DRAWINGS AND MISCELLANEOUS INFORMATION MUST BE GIVEN TO THE OWNER AND ENGINEER AT COMPLETION OF WORK. THE CONTRACTOR MUST GUARANTEE ALL MATERIAL AND LABOR TO BE FREE FROM DEFECTS FOR A ONE YEAR PERIOD FROM THE TIME OF OWNER ACCEPTANCE. ANY DEFECTS OCCURRING DURING THIS PERIOD MUST BE CORRECTED BY THE CONTRACTOR AT NO ADDITIONAL COST TO THE OWNER.
13. CONTRACTOR IS TO PROVIDE ALL REQUIRED SCAFFOLDING, LADDERS, RIGGING, HOISTING AND ALL OTHER EQUIPMENT REQUIRED FOR THE INSTALLATION OF THEIR WORK.
14. ESTABLISH PASSAGE CLEARANCES REQUIRED TO DELIVER, INSTALL AND ERECT ALL REQUIRED EQUIPMENT. IF STRUCTURES, EQUIPMENT AND SYSTEMS MUST BE ALTERED TO PROVIDE PASSAGE OF EQUIPMENT, THE CONTRACTOR MUST RESTORE STRUCTURES, EQUIPMENT AND SYSTEMS TO THEIR ORIGINAL CONDITION AT THE CONTRACTOR'S EXPENSE; INCLUDING REMOVING AND REPLACEMENT OF ALL CEILING AS REQUIRED TO COMPLETE THE WORK.
15. THE CONTRACTOR MUST REPLACE ALL FIREPROOFING MATERIAL, INCLUDING SPRAY APPLIED AND MASONRY TYPES, THAT IS REMOVED TO ACCOMMODATE EQUIPMENT, HANGERS, ANCHORS, ETC. ALL FIREPROOFING MATERIAL THAT IS INTEGRAL TO THE RATING OF AN EXISTING FIRE-RATED ASSEMBLY MUST BE REPLACED SO THAT THE FULL FIRE RATING IS PRESERVED. SEE SPECIFICATIONS FOR FURTHER INFORMATION.

GENERAL ELECTRICAL NOTES:

1. COORDINATE ALL ELECTRICAL WORK WITH THE CONSTRUCTION MANAGER/GENERAL CONTRACTOR AND ALL OTHER DISCIPLINES INVOLVED IN THIS PROJECT.
   1.1. CONTRACTOR MUST REVIEW ALL TRADES' CONTRACT DOCUMENTS AND APPLICABLE SHOP DRAWINGS TO DETERMINE SPECIFIC MOUNTING LOCATIONS FOR ELECTRICAL EQUIPMENT.
   1.2. VERIFY EXACT LOCATIONS AND MOUNTING OF ALL LIGHT FIXTURES, SWITCHES, RECEPTACLES, OUTLETS, FIRE ALARM DEVICES, VOICE/DATA DEVICES AND OTHER EQUIPMENT WITH ARCHITECTURAL DRAWINGS AND IN THE FIELD PRIOR TO ROUGH-IN. IN CENTERING OUTLETS AND LOCATION BOXES, ALLOW FOR OVERHEAD PIPES, DUCTS AND MECHANICAL EQUIPMENT VARIATIONS IN FIREPROOFING AND PLASTERING, WINDOW AND DOOR TRIM, PANELING, HUNG CEILINGS AND THE LIKE, AND CORRECT ANY INACCURACY RESULTING FROM FAILURE TO DO SO WITHOUT EXPENSE TO OWNER.
   1.3. LOCATIONS INDICATED FOR LOCAL WALL SWITCHES ARE SUBJECT TO MODIFICATIONS AT OR NEAR DOORS. COORDINATE WITH ARCHITECTURAL AND/OR ENGINEERING PLANS AND INSTALL SWITCH ON SIDE OPPOSITE HINGE. VERIFY FINAL HINGE LOCATIONS IN FIELD PRIOR TO SWITCH OUTLET INSTALLATION.
2. THE CONDUITS SHOWN ON THESE DRAWINGS ARE DIAGRAMMATIC IN NATURE, THEY SHOW THE GENERAL ARRANGEMENT AND SIZE OF THE CONDUITS. THEY ARE NOT INTENDED TO SHOW EVERY OFFSET OR INTERFERENCE THAT MAY BE ENCOUNTERED. CONTRACTOR IS RESPONSIBLE FOR ROUTING ALL CONDUIT IN THE MOST EFFICIENT MANNER IN ACCORDANCE WITH PROJECT SPECIFICATIONS.
3. ALL CONTRACTOR SUPPLIED MATERIALS MUST BE NEW AND UL APPROVED (OR APPROVED BY ANOTHER NATIONALLY RECOGNIZED ORGANIZATION).
4. ALL EQUIPMENT MUST BE INSTALLED IN A NEAT AND WORKMANLIKE MANNER, RECTILINEAR TO BUILDING STRUCTURE. HORIZONTAL OR CROSS RUNS IN PARTITIONS AND WALLS NOT PERMITTED.
5. UNLESS OTHERWISE STATED, ALL ABOVE GROUND WIRING MUST BE IN CONDUIT, 3/4 INCH MINIMUM SIZE FOR ELECTRIC SERVICES. ALL CONDUIT BENDS MUST BE OF THE LONG RADIUS TYPE. ALL OUTDOOR WIRING MUST BE IN CONDUIT, 3/4 INCH MINIMUM SIZE. ALL MOTORS AND TRANSFORMERS MUST HAVE FLEXIBLE CONNECTIONS TO MINIMIZE VIBRATION. REFER TO ELECTRICAL SPECIFICATIONS FOR ADDITIONAL INFORMATION.
6. ALL WIRING MUST BE RUN CONCEALED IN CONDUIT UNLESS SPECIFIED OTHERWISE.
7. CONTRACTOR MUST USE TRAPEZE TO SUPPORT MULTIPLE CONDUITS FROM BUILDING STEEL
8. SECURE ALL SUPPORTS TO BUILDING STRUCTURE BY STEEL FOR VERTICAL SUPPORT AND BY MEANS OF TOGGLE BOLTS ON HOLLOW MASONRY UNITS, EXPANSION SHIELDS IN CONCRETE OR BRICK. MACHINE SCREWS ON METAL SURFACE, AND WOOD SCREWS ON WOOD CONSTRUCTION. NAILS, RAWL OR WOOD PLUGS NOT PERMITTED. SUPPORT HORIZONTAL RUNS OF METALLIC CONDUITS NOT MORE THAN 10 FT. APART. SUPPORT RACEWAY RISERS AT EACH FLOOR LEVEL. RUN EXPOSED RACEWAYS PARALLEL WITH OR AT RIGHT ANGLES TO WALLS.
9. ALL CONDUIT INSTALLATIONS CROSSING EXPANSION JOINTS MUST HAVE EXPANSION OR EXPANSION/DEFLECTION TYPE FITTINGS AS REQUIRED. NOTE: FOR THE EXACT LOCATIONS OF EXPANSION JOINTS, SEE OWNER FOR EXISTING STRUCTURAL DRAWINGS.
10. ALL UNDERGROUND CONDUITS MUST BE SEALED TO PREVENT THE ENTRY OF WATER OR GASES.
11. PASS RACEWAYS OVER WATER, STEAM, OR OTHER PIPING WHEN PULL BOXES ARE NOT REQUIRED. INSTALL NO RACEWAY WITHIN 6 IN. OF STEAM OR HOT WATER PIPES, OR APPLIANCES, EXCEPT CROSSINGS WHERE RACEWAY MUST BE AT LEAST 2 IN. FROM PIPE COVER.
12. FURNISH PULL STRING IN EACH RACEWAY RUN OVER 10 FT IN WHICH WIRING IS NOT INSTALLED.
13. CUT STEEL CONDUIT ENDS SQUARE, REAM SMOOTH, PAINT MALE THREADS OF FIELD THREADED CONDUIT WITH GRAPHITE BASE PIPE COMPOUND. DRAW UP TIGHT WITH CONDUIT COUPLINGS.
14. ALL WIRING MUST BE STRANDED COPPER CONDUCTOR. MINIMUM SIZE #12 AWG (POWER) & 14 AWG (CONTROL), 600 VOLT INSULATION THW/THWN. REFERENCE SPECIFICATIONS FOR MORE INFORMATION. EQUIPMENT GROUNDING CONDUCTOR #10 AND SMALLER MUST BE SOLID.
15. GROUNDING MUST BE INSTALLED IN ACCORDANCE WITH THE NATIONAL ELECTRICAL CODE REGARDING ELECTRODE, GROUNDING AND BONDING REQUIREMENTS FOR SERVICE, EQUIPMENT AND ENCLOSURES. ALL EQUIPMENT MUST BE PROVIDED WITH A SEPARATE GROUNDING CONDUCTOR.
16. CONNECT CONDUIT TO MOTOR CONDUIT TERMINAL BOXES WITH FLEXIBLE CONDUIT (MINIMUM 18 IN. LENGTH AND 50% SLACK). DO NOT TERMINATE IN OR FASTEN RACEWAYS TO MOTOR FOUNDATION.
17. PROVIDE SEPARATE RACEWAYS FOR CONDUCTORS OF NORMAL AND EMERGENCY CIRCUITS. IN COMMON BOXES, PROVIDE BARRIERS BETWEEN EMERGENCY AND NORMAL WIRING.
18. LEAVE WIRE SUFFICIENTLY LONG TO PERMIT MAKING FINAL CONNECTIONS.
19. WIRE COLOR CODING: PER CODE. WHERE COLOR-CODED CABLE IS NOT AVAILABLE, CERTIFY IN WRITING AND REQUEST PERMISSION FOR OVERLAP COLOR TAPING OF CONDUCTORS (MINIMUM LENGTH 6") IN ACCESSIBLE LOCATIONS. COLOR CODING, ONCE SELECTED, MUST BE USED CONSISTENTLY FOR THE ENTIRE PROJECT.
20. PULL NO THERMOPLASTIC WIRES AT TEMPERATURES LOWER THAN 32°F.
21. PROVIDE CABLE SUPPORTS FOR WIRE IN RISER CONDUITS AS REQUIRED BY CODE.
22. ALL SWITCHES MUST BE MOUNTED AT 48" (TOP OF THE TOGGLE SWITCH) ABOVE THE TOP OF FINISHED FLOOR, UNLESS OTHERWISE NOTED. ALL RECEPTACLES MUST BE MOUNTED AT 18" ABOVE THE TOP OF FINISHED FLOOR, UNLESS OTHERWISE NOTED.
23. PROVIDE PULL BOXES AS INDICATED AND WHEREVER NECESSARY TO FACILITATE PULLING OF WIRE AND COORDINATE LOCATIONS WITH OTHER TRADES.
24. FOR EMPTY RACEWAY RUNS, PROVIDE PULL BOXES EVERY 100FT AND AS INDICATED. COORDINATE LOCATIONS WITH OTHER TRADES.
25. JUNCTION AND PULL BOXES: LOCATE GENERALLY NOT EXPOSED IN FINISHED SPACES. WHERE NECESSARY, REROUTE CONDUITS OR MAKE OTHER ARRANGEMENTS FOR CONCEALMENT. COVERS OF JUNCTION AND PULL BOXES MUST BE ACCESSIBLE.
26. SUPPORT JUNCTION AND PULL BOXES INDEPENDENTLY TO BUILDING STRUCTURE WITH NO WEIGHT BEARING ON CONDUITS.
27. ALL ACCESS DOOR LOCATIONS MUST BE REVIEWED BY ARCHITECT AND/OR ENGINEER PRIOR TO INSTALLATION.
28. FIRESTOP MUST BE INSTALLED WHENEVER WIRING OR RACEWAYS CROSS FIRE RATED WALLS.
29. PANELBOARDS, DISCONNECTS, AUTOMATI

GENERAL SHEET NOTES:

1. SEE DRAWINGS E-001 AND E-002 FOR ABBREVIATIONS, SYMBOLS AND NOTES.
2. AREA OF UNDERGROUND DUCTBANKS IS CONGESTED WITH EXISTING UTILITIES. CONTRACTOR SHALL PERFORM A GROUND PENETRATING RADAR SURVEY OF AREA TO IDENTIFY CONFLICTS. PROVIDE ALLOWANCE FOR HAND-DIGGING A SIGNIFICANT PORTION OF THE UNDERGROUND WORK.
3. SEE ELECTRICAL CONNECTION SCHEDULE ON DRAWING E-704 FOR FURTHER INFORMATION ON ELECTRICAL CONNECTIONS TO MECHANICAL EQUIPMENT.
4. ALL SECURITY CAMERAS SHOWN SHALL BE WIRED BACK TO EXISTING SECURITY HEADEND IN ROOM BC-114 WITH MANUFACTURER RECOMMENDED POE CABLE.

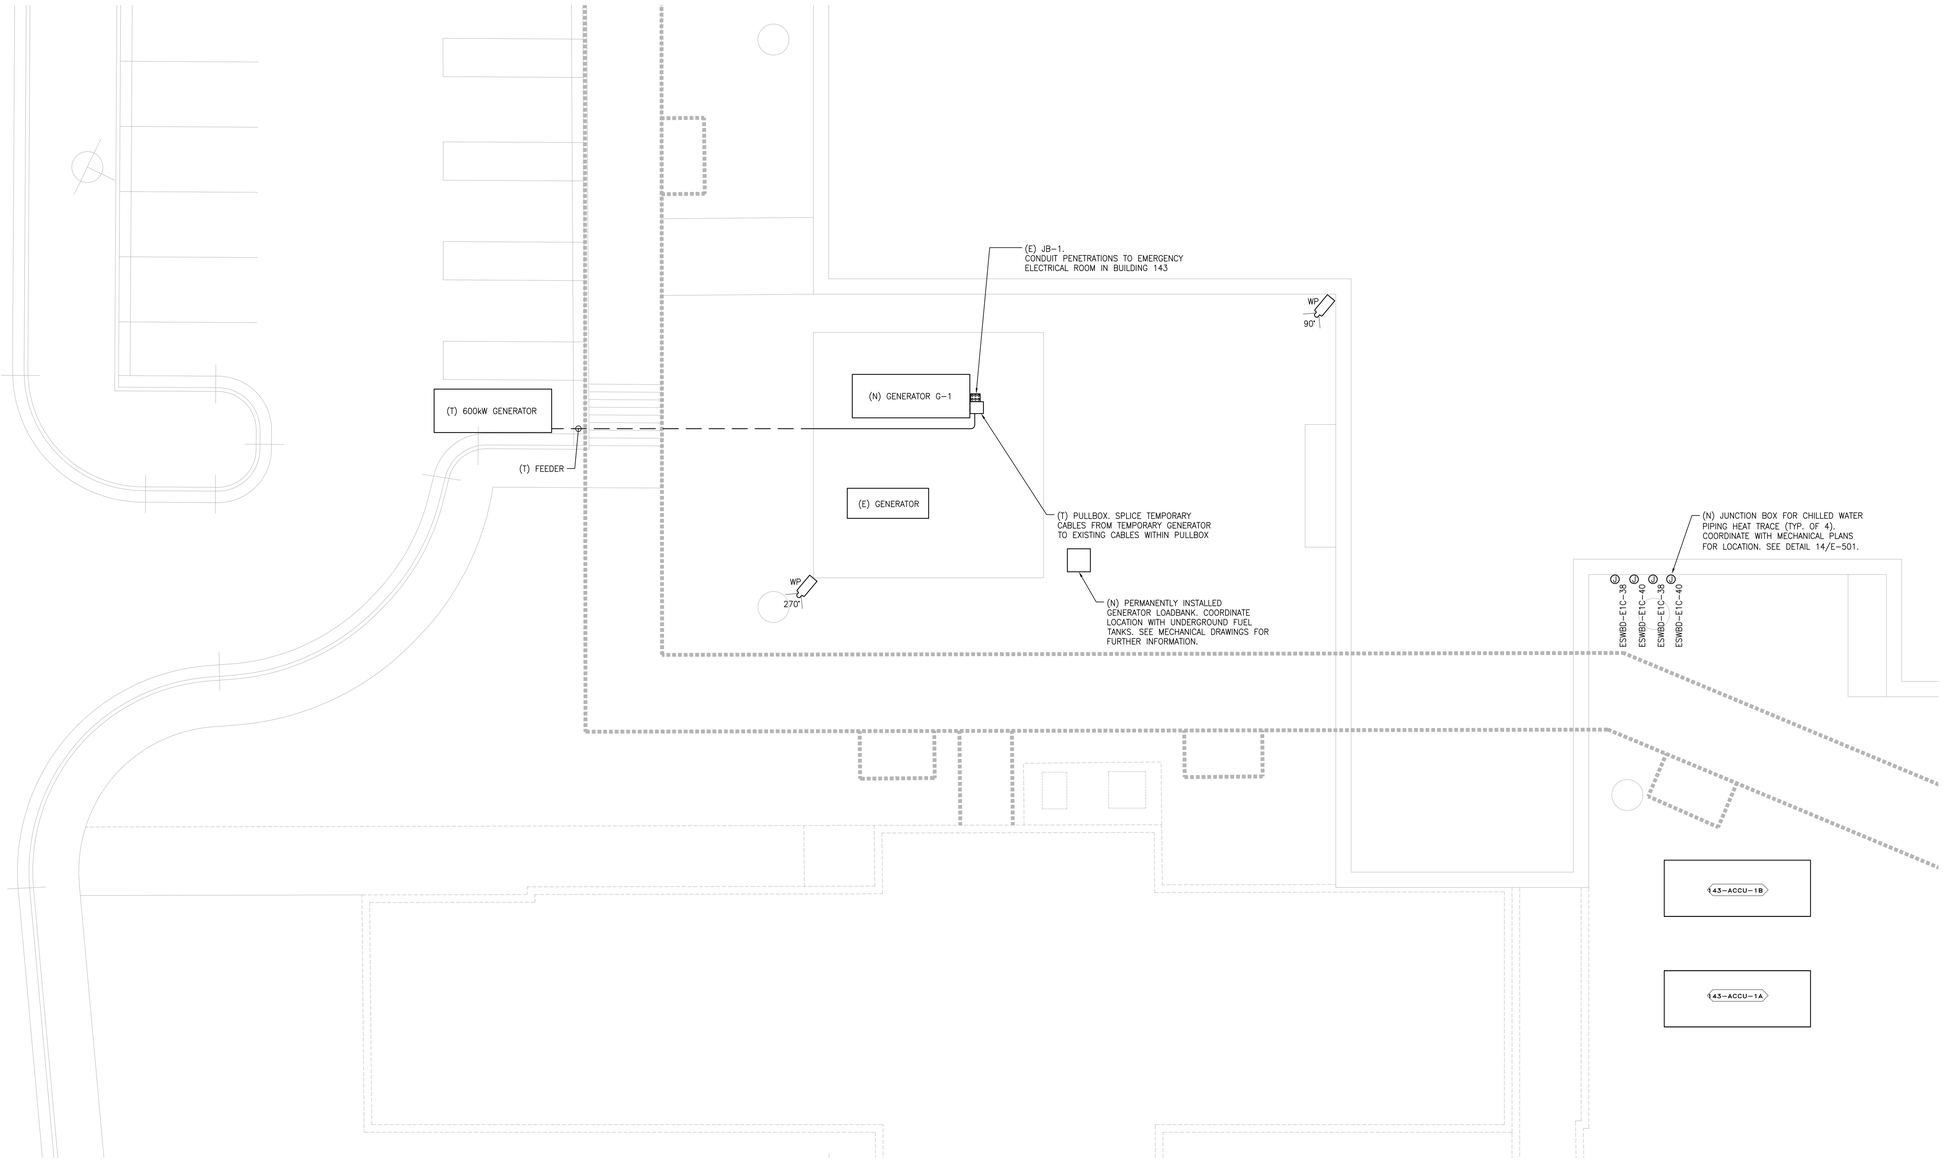

1 ELECTRICAL SITE PLAN
SCALE: 1/8" = 1'-0"

PLAN NORTH
ACTUAL NORTH

PRINTS OF THIS DRAWING SHALL NOT BE USED FOR ANY PURPOSE WHATSOEVER WITHOUT THE SEAL AND SIGNATURE OF THE PROFESSIONAL ENGINEER.

NO.	DESCRIPTION	DATE

CONSULTANTS

Architecture:	Civil Engineering:	Fire & Life Safety:
PF&A DESIGN, P.C.	LABELLA ASSOCIATES	STANTON ENGINEERING SERVICES, LLC

ENGINEER OF RECORD

MILLER•REMICK
A Service-Disabled Veteran-Owned Small Business
(856) 429-4000 ✶ Miller-Remick.com
M-R PROJECT NO 0499-0136

MILLER-REMICK LLC
PROFESSIONAL ENGINEER

COMMONWEALTH OF PENNSYLVANIA REGISTERED PROFESSIONAL THOMAS REGINO ENGINEER In MEMORIS
12/30/25

Office of Construction and Facilities Management

VA U.S. Department of Veterans Affairs

Drawing Title ELECTRICAL SITE PLAN	**Phase** BID DOCUMENTS	**Project Title** RENOVATE SURGICAL SUITE PHASE II	**VA Drawing Number** 2617
		Project Number 658-19-103	**Building Number** 143
Approved by: Jon Manninen, COR	FULLY SPRINKLERED	**Location** SALEM VA MEDICAL CENTER	**Drawing Number** ES101
		Issue Date 2025-12-30 / **Checked** MJR / **Drawn** MJR	

VA FORM 08-6231

P:\0499_DVA\0499-0136 Salem Renovate Surgical Suite\4_Drawings\1_Cad\1_Current Submittal Phase\7_Electrical\ES101.dwg 12-29-25 08:23:08 AM MRonca

GENERAL SHEET NOTES:

1. SEE DRAWING E-001 FOR ELECTRICAL SYMBOLS AND ABBREVIATIONS AND DRAWING E-002 FOR ELECTRICAL NOTES.

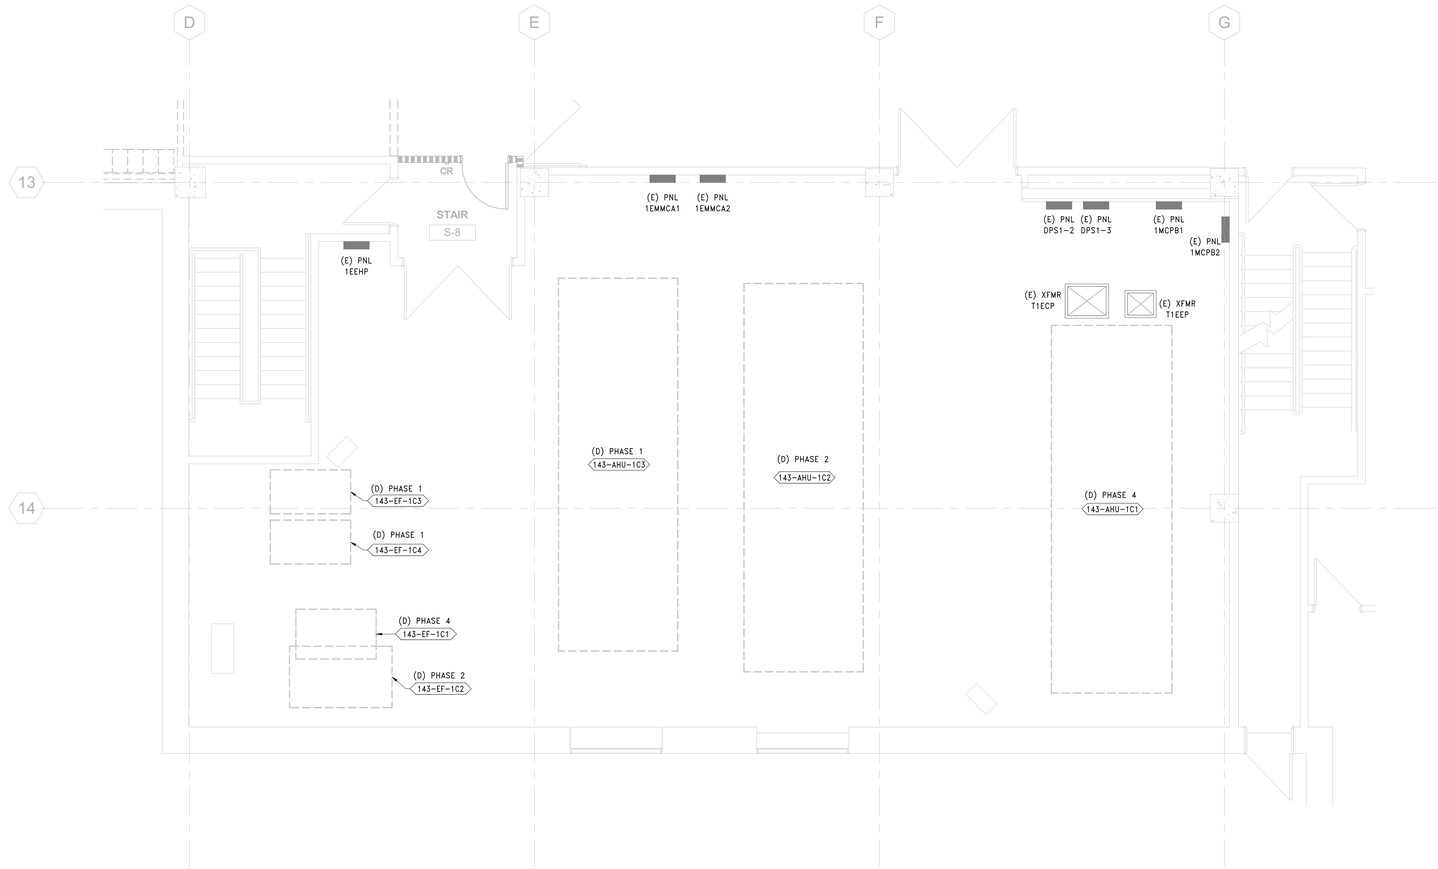

1 DEMOLITION PLAN - MECHANICAL ROOM

SCALE: 1/4" = 1'-0"

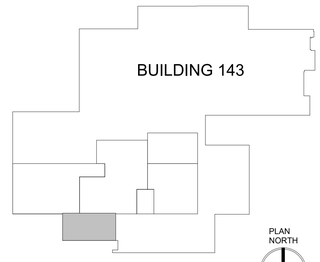

KEYPLAN

PRINTS OF THIS DRAWING SHALL NOT BE USED FOR ANY PURPOSE WHATSOEVER WITHOUT THE SEAL AND SIGNATURE OF THE PROFESSIONAL ENGINEER

Revisions:	Date:

CONSULTANT

Architecture:	Civil Engineering:	Fire Protection:
PF&A DESIGN, P.C.	LABELLA ASSOCIATES	STANTON ENGINEERING SERVICES, LLC

ENGINEER OF RECORD

MILLER+REMICK
A Service-Disabled Veteran-Owned Small Business
(856) 429-4000 • Miller-Remick.com
M-R PROJECT NO. 0909-0030

MILLER-REMICK LLC PROFESSIONAL ENGINEER

COMMONWEALTH OF PENNSYLVANIA — REGISTERED PROFESSIONAL — THOMAS REGINO — ENGINEER No. PE094186
12/30/25

Office of Construction and Facilities Management

VA U.S. Department of Veterans Affairs

Drawing Title ELECTRICAL DEMOLITION PLAN MECHANICAL ROOM	**Phase** BID DOCUMENTS	**Project Title** RENOVATE SURGICAL SUITE PHASE II	**VA Drawing Number** 2617
Approved by: Jon Manninen, COR	FULLY SPRINKLERED	**Project Number** 658-19-103	**Building Number** 143
		Location SALEM VA MEDICAL CENTER	**Drawing Number** ED111
		Issue Date 2025-12-30 · **Checked** MJR · **Drawn** DRR	

12/29/2025 9:31:55 PM

VA FORM 08 - 6231

GENERAL SHEET NOTES:

1. REFER TO DRAWINGS E-001 AND E-002 FOR ELECTRICAL GENERAL NOTES, ABBREVIATIONS & SYMBOLS.
2. SEE ELECTRICAL CONNECTION SCHEDULE ON DRAWING E-704 FOR FURTHER INFORMATION ON ELECTRICAL CONNECTIONS TO MECHANICAL EQUIPMENT.

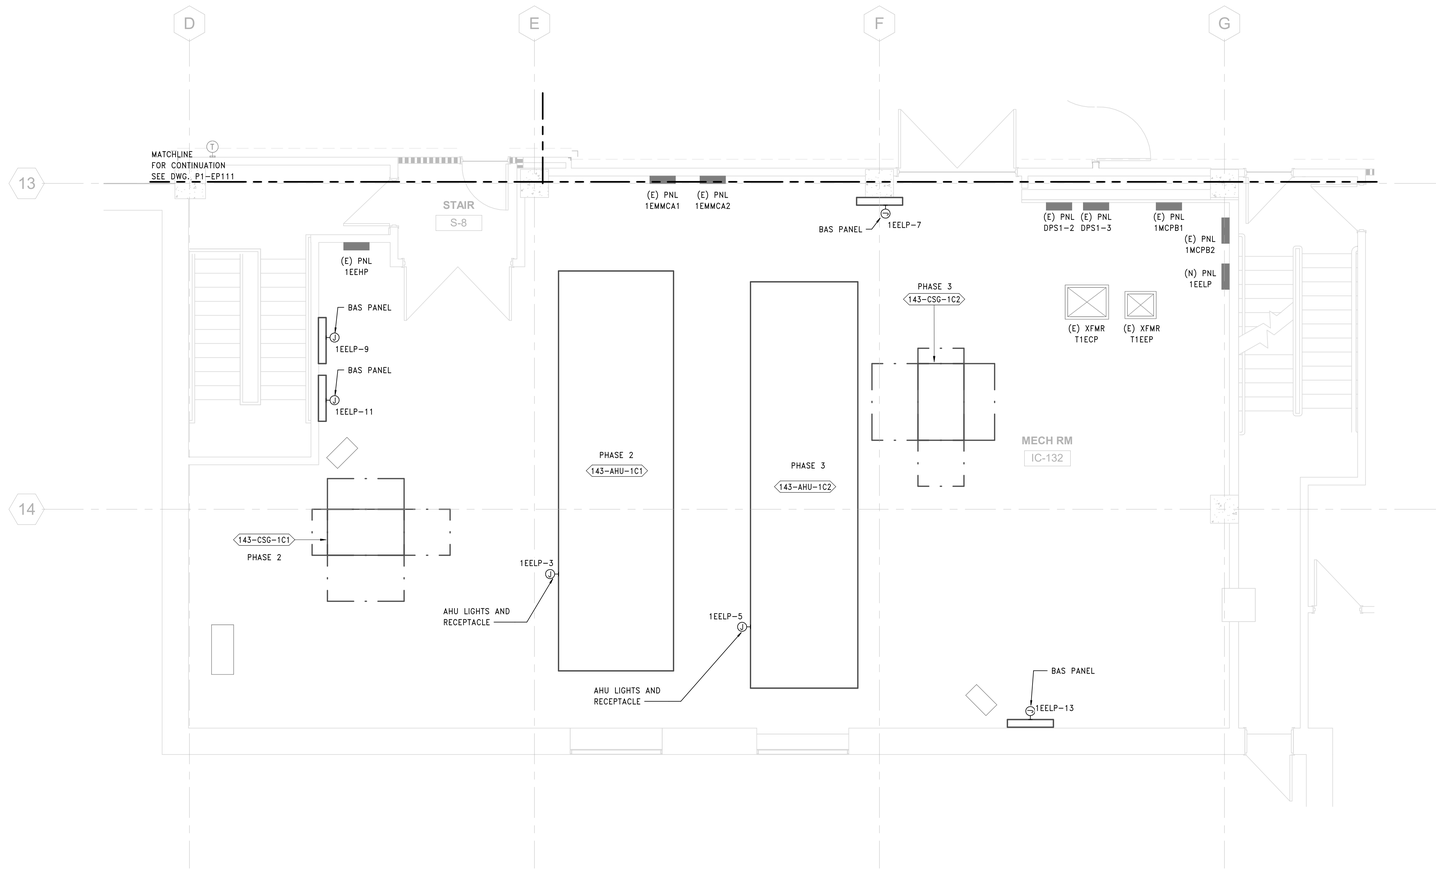

1 POWER PLAN - MECHANICAL ROOM 1C-132

SCALE: 1/4" = 1'-0"

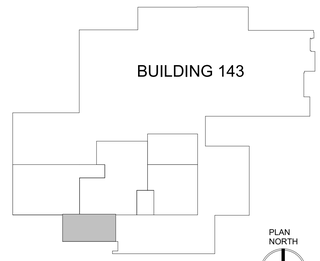

KEYPLAN

PRINTS OF THIS DRAWING SHALL NOT BE USED FOR ANY PURPOSE WHATSOEVER WITHOUT THE SEAL AND SIGNATURE OF THE PROFESSIONAL ENGINEER

Revisions:	Date:

CONSULTANT

Architecture:	Civil Engineering:	Fire Protection:
PF&A DESIGN, P.C.	LABELLA ASSOCIATES	STANTON ENGINEERING SERVICES, LLC

ENGINEER OF RECORD

MILLER•REMICK
A Service-Disabled Veteran-Owned Small Business
(856) 429-4000 • Miller-Remick.com

MILLER-REMICK LLC PROFESSIONAL ENGINEER

COMMONWEALTH OF PENNSYLVANIA REGISTERED PROFESSIONAL THOMAS REGINO ENGINEER No. PE094195
12/30/25

Office of Construction and Facilities Management

VA U.S. Department of Veterans Affairs

Drawing Title	ELECTRICAL POWER PLAN MECHANICAL ROOM
Approved by:	Jon Manninen, COR
Phase	BID DOCUMENTS
	FULLY SPRINKLERED
Project Title	RENOVATE SURGICAL SUITE PHASE II
Project Number	658-19-103
Location	SALEM VA MEDICAL CENTER
Issue Date	2025-12-30
Checked	CS
Drawn	SP
VA Drawing Number	2617
Building Number	143
Drawing Number	EP111

12/29/2025 5:31:36 PM

VA FORM 08 - 6231

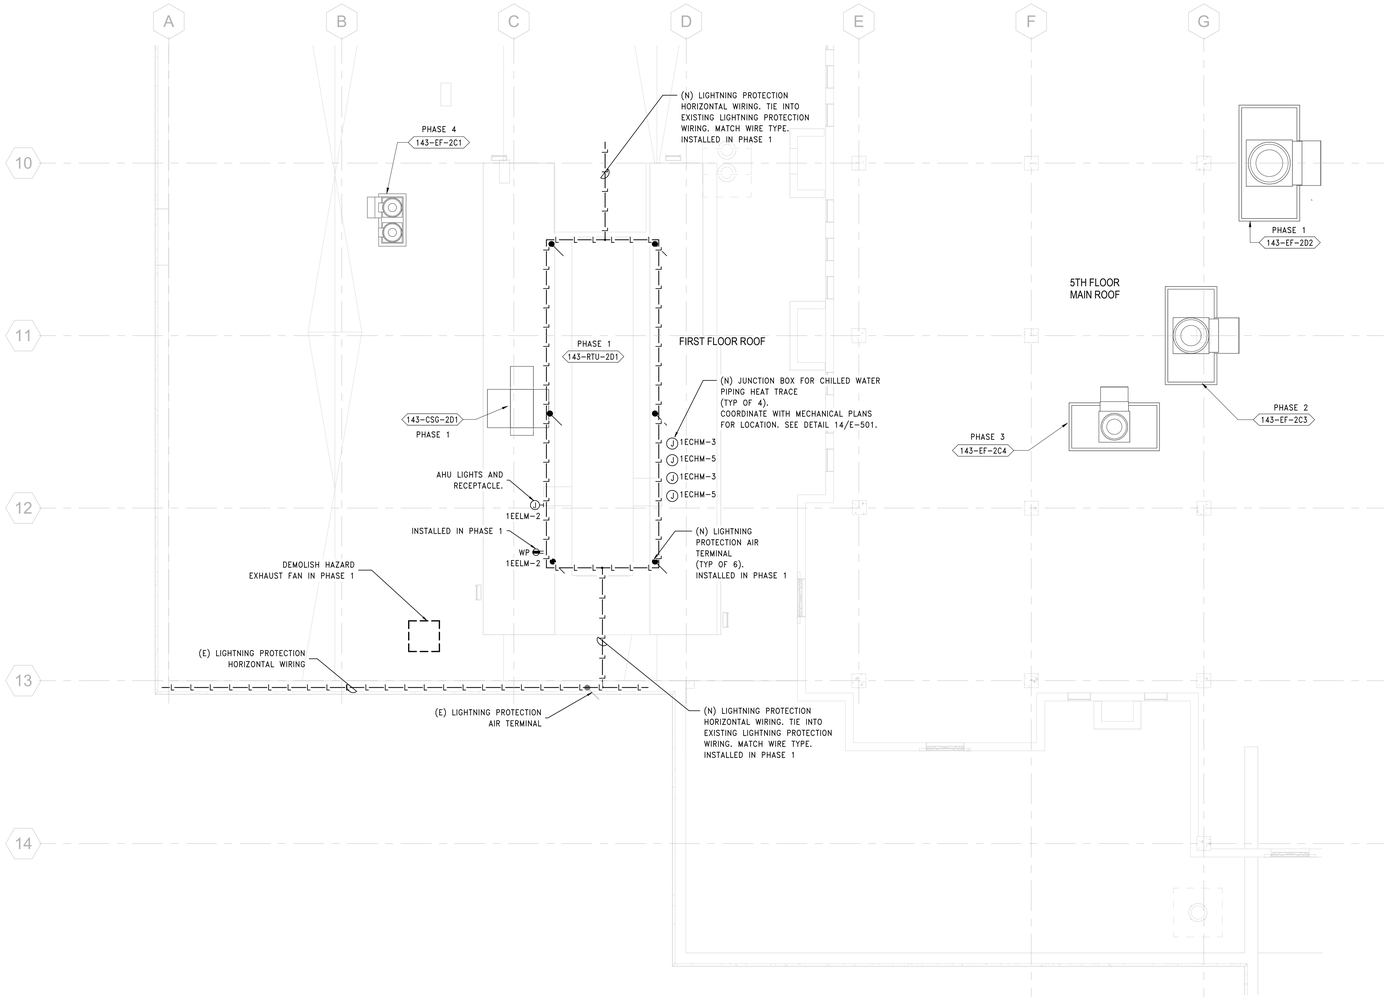

1 POWER PLAN - ROOF

SCALE: 1/8" = 1'-0"

GENERAL SHEET NOTES:

1. SEE DRAWINGS E-001 AND E-002 FOR ABBREVIATIONS, SYMBOLS AND NOTES.
2. SEE LIGHTNING PROTECTION DETAILS ON E-501 FOR FURTHER INFORMATION ON THE EXTENSION OF THE EXISTING SYSTEM.
3. ALL LIGHTNING PROTECTION CONDUCTORS ARE TO BE RUN AT RIGHT ANGLES TO ALL BUILDING STRUCTURES, ROOF EDGES AND ROOF EQUIPMENT WHERE FEASIBLE.
4. SEE ELECTRICAL CONNECTION SCHEDULE ON DRAWING E-704 FOR FURTHER INFORMATION ON ELECTRICAL CONNECTIONS TO MECHANICAL EQUIPMENT.

LIGHTNING PROTECTION SHEET NOTES:

1. THE COMPLETED INSTALLATION SHALL MEET THE "INSTALLATION REQUIREMENTS FOR LIGHTNING PROTECTION SYSTEMS, UL96A" OF UNDERWRITERS LABORATORIES – CURRENT EDITION AND NFPA 780 2017 EDITION. CERTIFICATIONS: TWO WEEKS PRIOR TO FINAL INSPECTION, SUBMIT THE FOLLOWING TO OWNER:
   a. CERTIFICATION BY THE MANUFACTURER THAT THE LIGHTNING PROTECTION SYSTEM CONFORMS TO THE REQUIREMENTS OF THE DRAWINGS AND SPECIFICATIONS.
   b. CERTIFICATION BY THE CONTRACTOR THAT THE LIGHTNING PROTECTION SYSTEM HAS BEEN PROPERLY INSTALLED AND INSPECTED.
   c. CERTIFICATION THAT THE LIGHTNING PROTECTION SYSTEM HAS BEEN INSPECTED BY A UL REPRESENTATIVE AND HAS BEEN APPROVED BY UL WITHOUT VARIATION".A CERTIFICATE OF COMPLETION FROM AN AUTHORITY HAVING JURISDICTION SHALL BE FURNISHED TO THE OWNER UPON COMPLETION.
2. WHERE ELEMENTS OF THE SYSTEM ARE IN DIRECT CONTACT WITH ALUMINUM BUILDING MATERIALS OR EXISTING ALUMINUM LIGHTNING PROTECTION WIRING, UTILIZE ALUMINUM WIRING, WHERE IN CONTACT WITH ANY OTHER BUILDING MATERIALS, UTILIZE COPPER EQUIPMENT AND WIRING.
3. METAL BODIES WITHIN 6'-0" OF THE LIGHTNING PROTECTION SYSTEM SHALL BE BONDED TO THE SYSTEM IN ACCORDANCE WITH UL96A.
4. ALL LIGHTNING CONDUCTORS ARE TO MAINTAIN A HORIZONTAL OR DOWNWARD PATH. ALL BENDS IN THE CONDUCTOR SHALL HAVE A RADIUS BEND OF 8 INCHES OR GREATER, AND SHALL HAVE AN ANGLE BEND OF 90 DEGREES OR GREATER.
5. EACH INDIVIDUAL ITEM OF THE LIGHTNING PROTECTION SYSTEM IS NOT LABELED FOR THE SAKE OF CLARITY, BUT A COMPLETE SYSTEM SHALL BE PROVIDED TO MEET CODE REQUIREMENTS.
6. ROOF PADS, PAVERS, FLASHING OR ANY OTHER SPECIAL ROOFING MATERIALS REQUIRED FOR THE INSTALLATION OF THE LIGHTNING PROTECTION SYSTEM SHALL BE FURNISHED AND INSTALLED BY THE ROOFING CONTRACTOR.
7. ALL ITEMS FASTENED TO ARCHITECTURAL ELEMENTS OF THE BUILDING SHALL MEET WITH THE ARCHITECT'S APPROVAL.
8. THE SYSTEM SHALL BE THE PRODUCT OF ONE MANUFACTURER REGULARLY ENGAGED IN THE PRODUCTION OF LIGHTNING PROTECTION SYSTEMS AND SHALL BE REGISTERED AND APPROVED BY THE LIGHTNING PROTECTION INSTITUTE.
9. INSTALLATION SHALL BE UL96A MASTER LABEL CERTIFIED FOR LIGHTNING PROTECTION AS AN EXTENSION OF AN EXISTING MASTER LABELED SYSTEM. CERTIFICATE OF COMPLIANCE SHALL BE PROVIDED.
10. SEE SPEC SECTION 264100 FOR FURTHER INFORMATION.

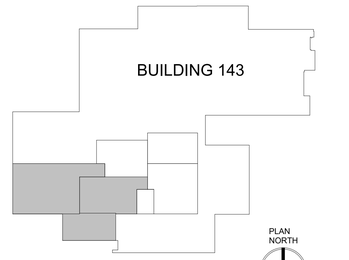

KEYPLAN

PRINTS OF THIS DRAWING SHALL NOT BE USED FOR ANY PURPOSE WHATSOEVER WITHOUT THE SEAL AND SIGNATURE OF THE PROFESSIONAL ENGINEER

Revisions:	Date:

CONSULTANT

Architecture:	Civil Engineering:	Fire Protection:
PF&A DESIGN, P.C.	LABELLA ASSOCIATES	STANTON ENGINEERING SERVICES, LLC

ENGINEER OF RECORD

MILLER-REMICK

A Service-Disabled Veteran-Owned Small Business

(856) 429-4000 • Miller-Remick.com

MILLER-REMICK LLC PROFESSIONAL ENGINEER

COMMONWEALTH OF PENNSYLVANIA — REGISTERED PROFESSIONAL ENGINEER — THOMAS REGINO — ENGINEER IN CHARGE

12/30/25

Office of Construction and Facilities Management

VA U.S. Department of Veterans Affairs

Drawing Title ELECTRICAL POWER PLAN ROOF	**Phase** BID DOCUMENTS	**Project Title** RENOVATE SURGICAL SUITE PHASE II	**VA Drawing Number** 2617
Approved by: Jon Manninen, COR	FULLY SPRINKLERED	**Project Number** 658-19-103	**Building Number** 143
		Location SALEM VA MEDICAL CENTER	**Drawing Number** EP121
		Issue Date 2025-12-30 / **Checked** MJR / **Drawn** DRR	

12/29/2025 5:31:56 PM

VA FORM 08 - 6231

GENERAL SHEET NOTES:

1. SEE DRAWING E-001 FOR ELECTRICAL SYMBOLS AND ABBREVIATIONS AND DRAWING E-002 FOR ELECTRICAL NOTES.
2. ALL LIGHTING SHALL BE EXISTING TO REMAIN.

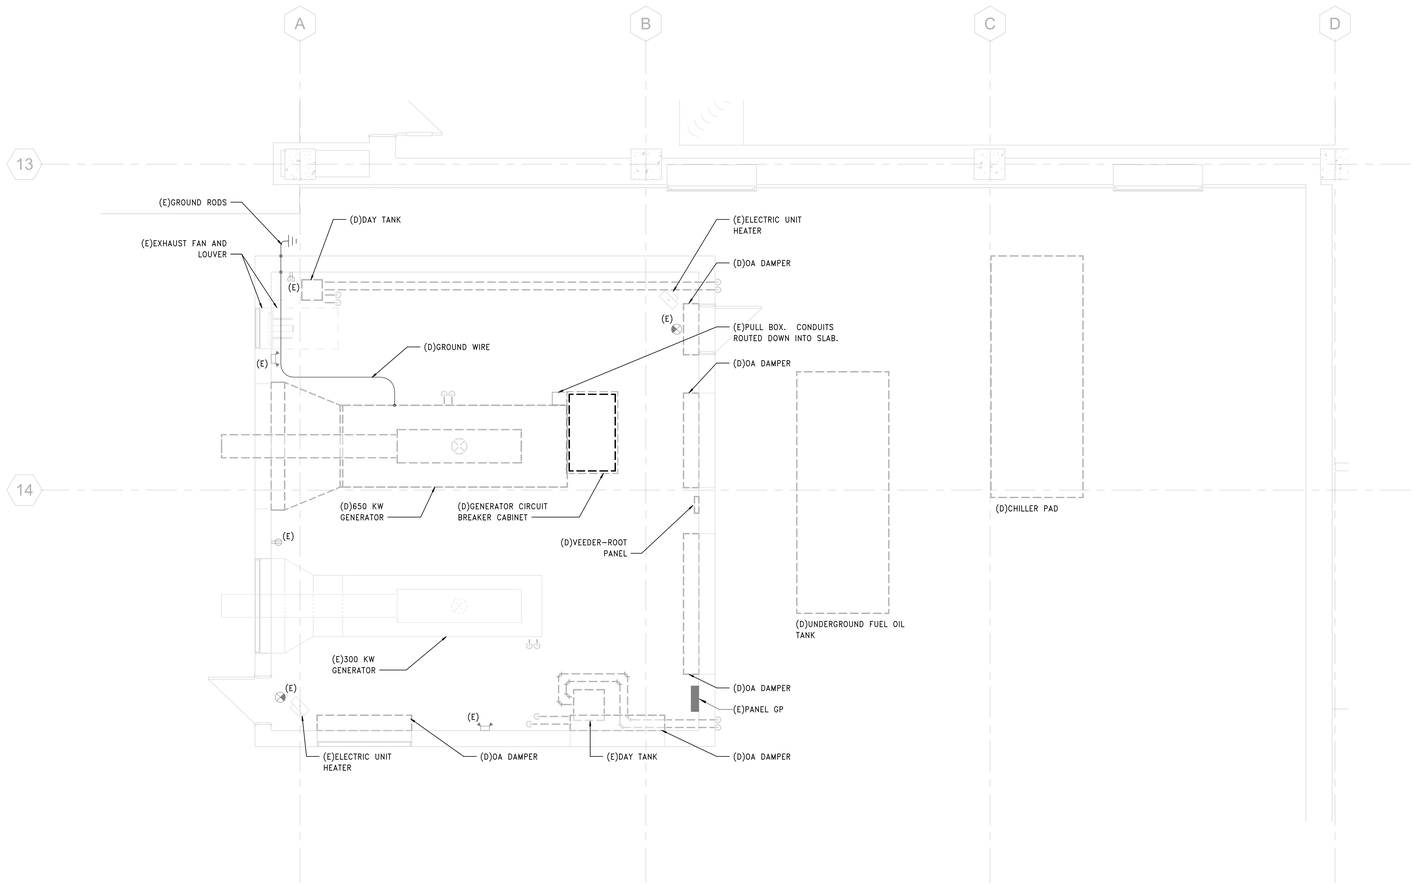

1 DEMOLITION PLAN - BASEMENT, PHASE 1

SCALE: 1/4" = 1'-0"

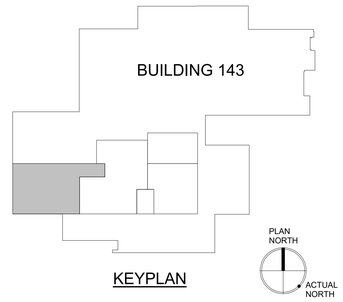

KEYPLAN

PRINTS OF THIS DRAWING SHALL NOT BE USED FOR ANY PURPOSE WHATSOEVER WITHOUT THE SEAL AND SIGNATURE OF THE PROFESSIONAL ENGINEER

Revisions:	Date:

12/29/2025 9:31:57 PM

VA FORM 08 - 6231

CONSULTANT

Architecture:	Civil Engineering:	Fire Protection:
PF&A DESIGN, P.C.	LABELLA ASSOCIATES	STANTON ENGINEERING SERVICES, LLC

ENGINEER OF RECORD

MILLER•REMICK

A Service-Disabled Veteran-Owned Small Business

(856) 429-4000 • Miller-Remick.com

M-R PROJECT NO. 0909-0030

MILLER-REMICK LLC PROFESSIONAL ENGINEER

COMMONWEALTH OF PENNSYLVANIA — REGISTERED PROFESSIONAL — THOMAS REGINO — ENGINEER No. PE094186

12/30/25

Office of Construction and Facilities Management

VA U.S. Department of Veterans Affairs

Drawing Title	ELECTRICAL DEMOLITION PLAN BASEMENT, PHASE 1
Approved by:	Jon Manninen, COR
Phase	BID DOCUMENTS
	FULLY SPRINKLERED
Project Title	RENOVATE SURGICAL SUITE PHASE II
Project Number	658-19-103
Location	SALEM VA MEDICAL CENTER
Issue Date	2025-12-30
Checked	MJR
Drawn	PDK
VA Drawing Number	2617
Building Number	143
Drawing Number	P1-ED101

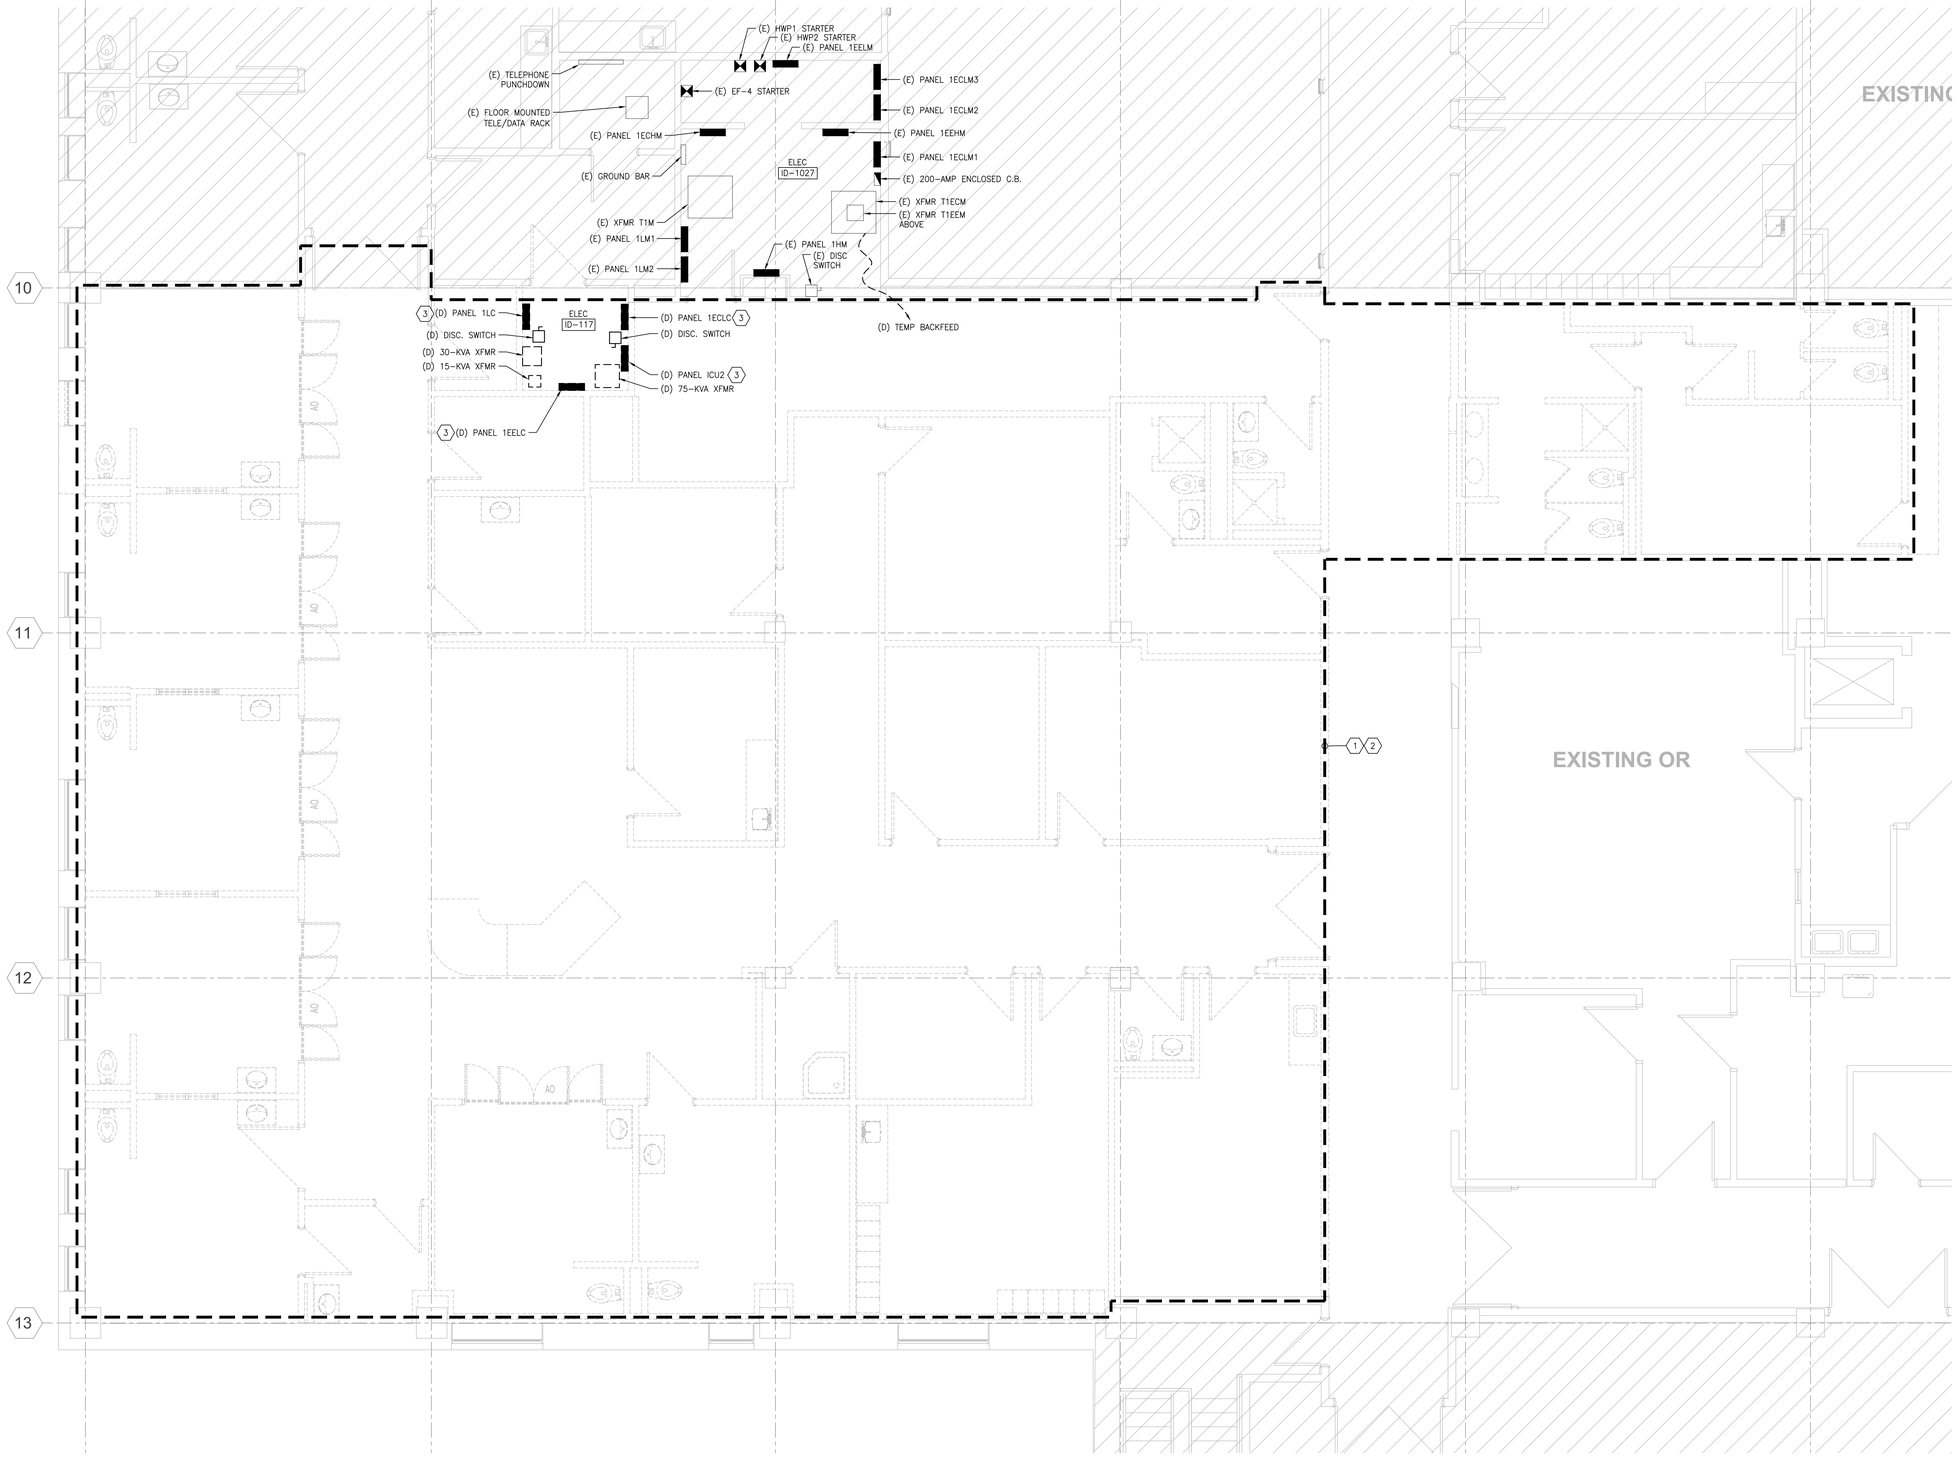

GENERAL SHEET NOTES:

1. SEE DRAWINGS E-001 AND E-002 FOR ABBREVIATIONS, SYMBOLS AND NOTES.

SHEET KEYNOTES:

1. DEMOLISH ALL ELECTRICAL DEVICES INCLUDING, BUT NOT LIMITED TO, PANELBOARDS, LIGHTING, LIGHTING CONTROL, RECEPTACLES, TELE/DATA AND FIRE ALARM DEVICES, ETC. WITHIN BOUNDARY, UNLESS OTHERWISE NOTED. DEMOLISH ALL ELECTRICAL DEVICE WIRING AND RACEWAYS BACK TO SOURCE.
2. ALL WIRELESS ACCESS POINTS AND CENTRAK DEVICES WITHIN THIS BOUNDARY SHALL BE REMOVED, CLEANED, AND STORED FOR REINSTALLATION.
3. ALL BRANCH CIRCUITS IN THIS PANEL ARE BELIEVED TO BE FED INTO THE PHASE 1 DEMOLITION AREA. ELECTRICAL CONTRACTOR SHALL VERIFY ALL CIRCUITS PRIOR TO DEMOLITION AND SHALL COORDINATE WITH COR PRIOR TO DEMOLITION IF A CIRCUIT IS FOUND THAT FEEDS OUTSIDE OF THE PHASE 1 DEMOLITION AREA.

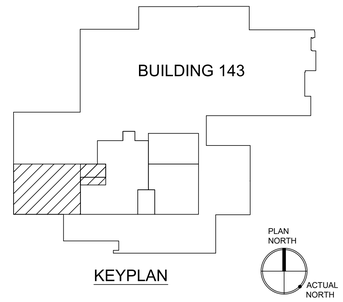

KEYPLAN

1 ELECTRICAL DEMOLITION PLAN – 1ST FLOOR, PHASE 1
SCALE: 1/4" = 1'-0"

PRINTS OF THIS DRAWING SHALL NOT BE USED FOR ANY PURPOSE WHATSOEVER WITHOUT THE SEAL AND SIGNATURE OF THE PROFESSIONAL ENGINEER.

NO.	DESCRIPTION	DATE

CONSULTANTS

Architecture:	Civil Engineering:	Fire & Life Safety:
PF&A DESIGN, P.C.	LABELLA ASSOCIATES	STANTON ENGINEERING SERVICES, LLC

ENGINEER OF RECORD

MILLER•REMICK
A Service-Disabled Veteran-Owned Small Business
(856) 429-4000 ★ Miller-Remick.com
M-R PROJECT NO: 0499-0136

MILLER-REMICK LLC
PROFESSIONAL ENGINEER

COMMONWEALTH OF PENNSYLVANIA
REGISTERED PROFESSIONAL
THOMAS REGINO
ENGINEER
No. PE044135
12/30/25

Office of Construction and Facilities Management

VA U.S. Department of Veterans Affairs

Drawing Title	ELECTRICAL DEMOLITION PLAN 1ST FLOOR, PHASE 1
Approved by:	Jon Manninen, COR
Phase	BID DOCUMENTS / FULLY SPRINKLERED
Project Title	RENOVATE SURGICAL SUITE PHASE II
Project Number	658-19-103
Location	SALEM VA MEDICAL CENTER
Issue Date	2025-12-30
Checked	MJR
Drawn	MJR
VA Drawing Number	2617
Building Number	143
Drawing Number	P1-ED111

VA FORM 08-6231

three inches = one foot
one and one half inches = one foot
one inch = one foot
three quarters inch = one foot
one half inch = one foot
three eighths inch = one foot
one quarter inch = one foot
one eighth inch = one foot
P:\0499_DVA\0499-0136 Salem Renovate Surgical Suite\4_Drawings\1_Cad\1_Current Submittal Phase\7_Electrical\P1-ED111.dwg 12-29-25 05:55:11 PM mcifelli

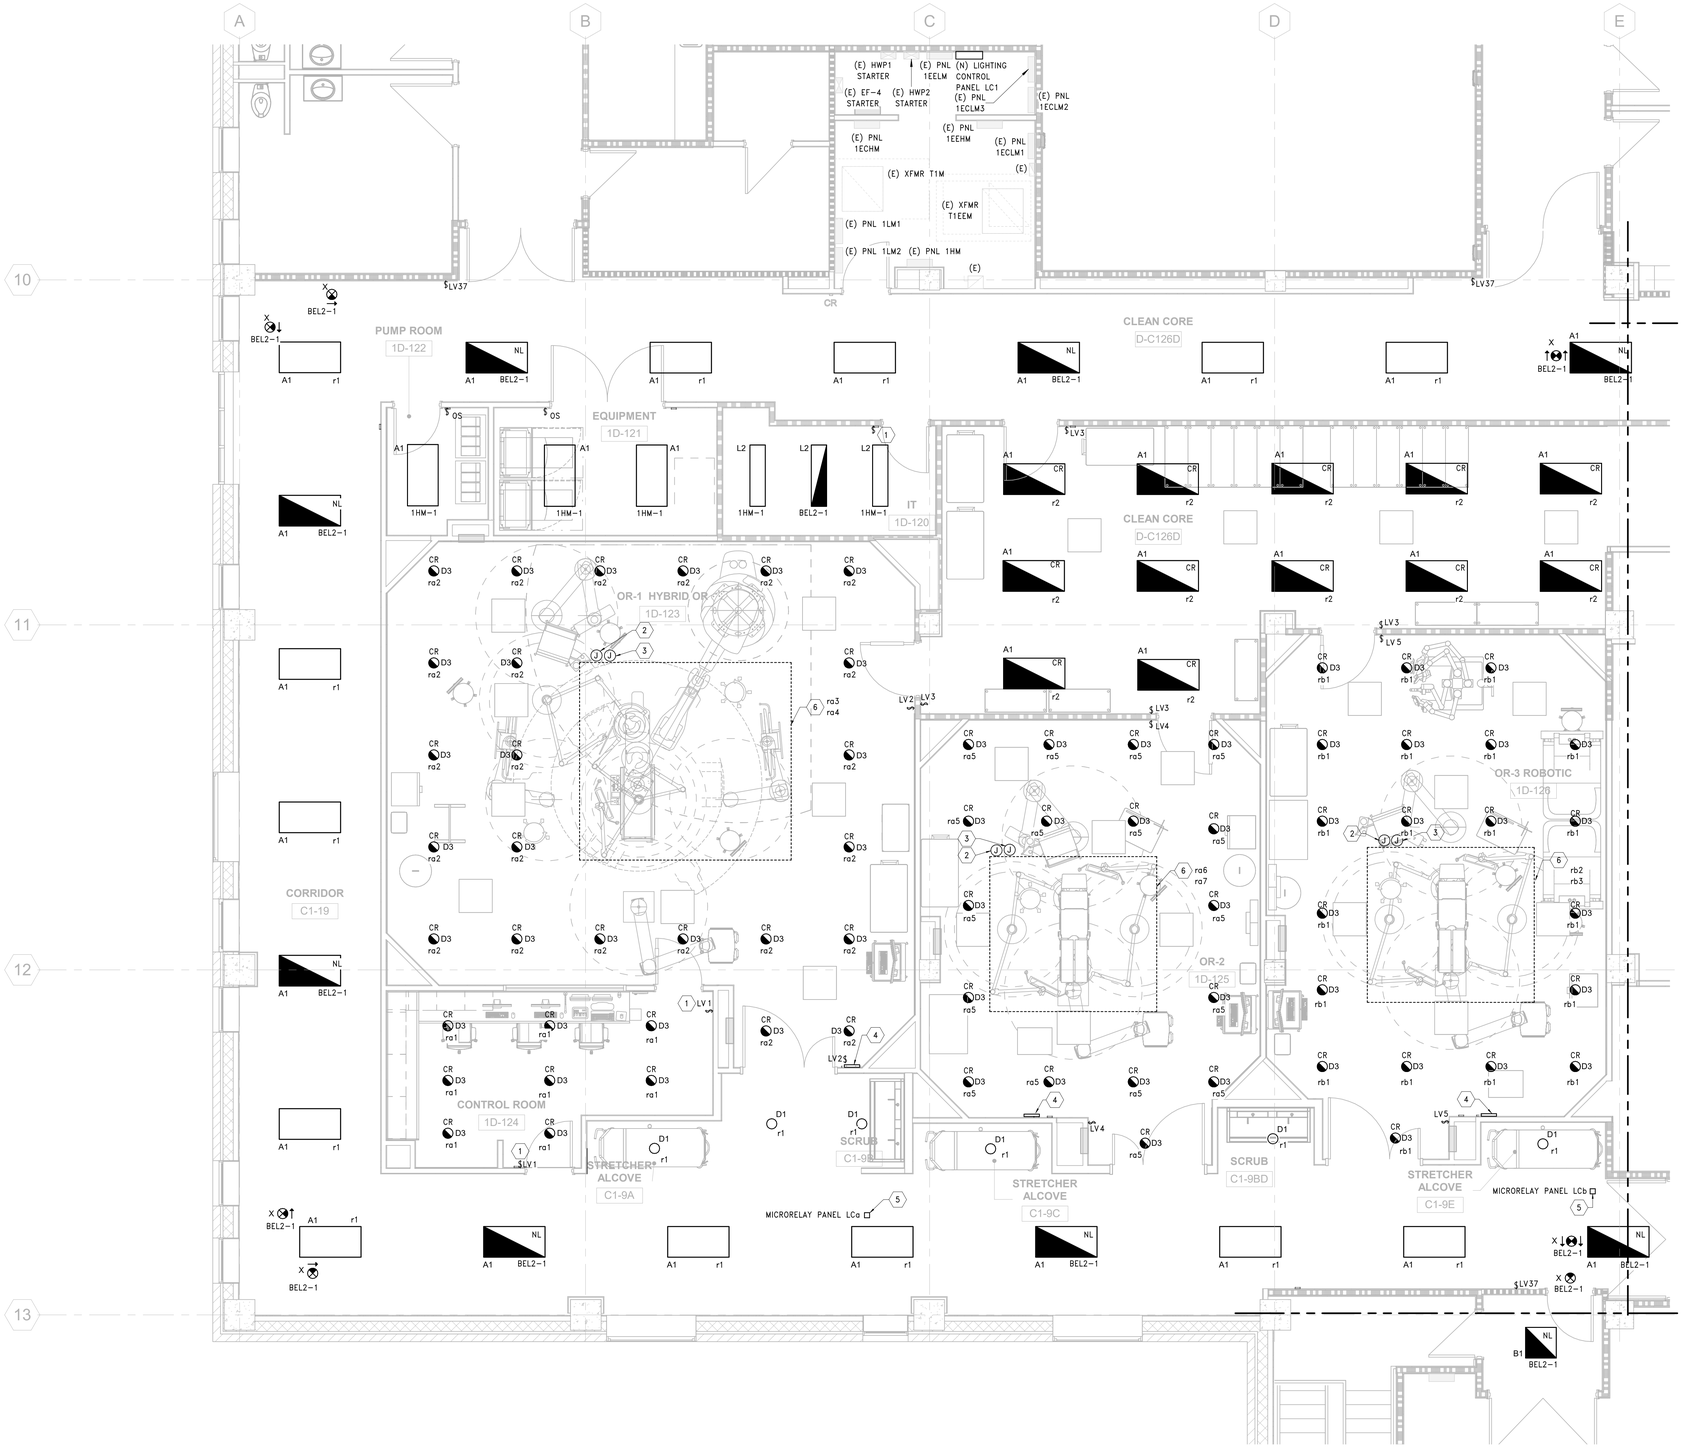

GENERAL SHEET NOTES:

1. SEE DRAWING E-001 FOR ELECTRICAL SYMBOLS AND ABBREVIATIONS AND DRAWING E-002 FOR ELECTRICAL NOTES.
2. ALL ELECTRICAL DEVICES ON THIS SHEET SHALL BE NEW, UNLESS OTHERWISE NOTED.
3. SEE DRAWING E-704 AND E-705 FOR LIGHTING FIXTURE SCHEDULE, CIRCUITRY AND LIGHTING CONTROL INFORMATION. SEE DRAWING E-701 AND E-702 FOR PANEL SCHEDULES.
4. EXIT SIGNS SHALL BE CIRCUITED AHEAD OF ALL CONTROL DEVICES.

SHEET KEYNOTES:

1 SEE DETAIL 10/E-501 FOR FURTHER INFORMATION ON SWITCHING OF EMERGENCY LIGHTING FIXTURES.

2 EC TO RUN LIGHTING CONTROL WIRE(S) TO CEILING SYSTEM JUNCTION BOX (BY CLEANSUITE).

3 EC TO SPLICE 277-VOLT LIGHTING CIRCUITS IN CEILING SYSTEM JUNCTION BOX (BY CLEANSUITE).

4 SURGICAL LIGHTHEAD WALL CONTROLLER.

5 MICROPANEL LOCATED ABOVE ACCESSIBLE CEILING. LABEL CEILING TILE TO INDICATE MICROPANEL ABOVE.

6 O.R. TABLE LIGHTING AND JUNCTION BOXES SHALL BE PROVIDED IN CONJUNCTION WITH MECHANICAL DIFFUSERS AS A SINGLE COMBINED UNIT (BY OTHERS). EC SHALL WIRE POWER AND LOW VOLTAGE CONTROL WIRING TO PRE-WIRED COMBINED CEILING BOX. CONFIRM ALL REQUIREMENTS WITH MANUFACTURER. IN ADDITION, EC SHALL PROVIDE AND INSTALL JUMPER CONNECTIONS BETWEEN THE (4) FOUR MODULAR PIECES OF THE COMBINED CEILING UNIT FOR POWER AND LOW VOLTAGE CONTROL WIRING. LIGHT FIELD SHALL BE WIRED AND CONTROLLED AS SHOWN ON DRAWINGS. TWO SEPARATE LIGHTING CIRCUITS SHALL BE PROVIDED FOR EACH ASSEMBLY (FIELD PERIMETER LIGHTS AND FIELD INTERIOR LIGHTS). EACH CIRCUIT SHALL BE MAPPED TO A UNIQUE RELAY.

1 LIGHTING PLAN - 1ST FLOOR, PHASE 1

SCALE: 1/4" = 1'-0"

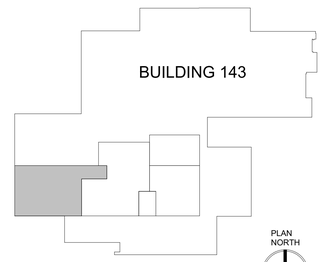

KEYPLAN

PRINTS OF THIS DRAWING SHALL NOT BE USED FOR ANY PURPOSE WHATSOEVER WITHOUT THE SEAL AND SIGNATURE OF THE PROFESSIONAL ENGINEER

Revisions: | Date:

CONSULTANT

Architecture:	Civil Engineering:	Fire Protection:
PF&A DESIGN, P.C.	LABELLA ASSOCIATES	STANTON ENGINEERING SERVICES, LLC

ENGINEER OF RECORD

MILLER-REMICK

A Service-Disabled Veteran-Owned Small Business

(856) 429-4000 • Miller-Remick.com

M-R PROJECT NO. 0909-0636

MILLER-REMICK LLC PROFESSIONAL ENGINEER

COMMONWEALTH OF PENNSYLVANIA — REGISTERED PROFESSIONAL — THOMAS REGINO — ENGINEER — 12/30/25

Office of Construction and Facilities Management

VA U.S. Department of Veterans Affairs

Drawing Title	ELECTRICAL LIGHTING PLAN 1ST FLOOR, PHASE 1
Approved by:	Jon Manninen, COR
Phase	BID DOCUMENTS
	FULLY SPRINKLERED
Project Title	RENOVATE SURGICAL SUITE PHASE II
Project Number	658-19-103
Location	SALEM VA MEDICAL CENTER
Issue Date	2025-12-30
Checked	MJR
Drawn	PDK
VA Drawing Number	2617
Building Number	143
Drawing Number	P1-EL111

12/29/2025 5:32:00 PM

VA FORM 08 - 6231

GENERAL SHEET NOTES:

1. SEE DRAWINGS E-001 AND E-002 FOR ABBREVIATIONS, NOTES, & SYMBOLS.
2. SEE ELECTRICAL CONNECTION SCHEDULE ON E-704 FOR FURTHER INFORMATION ON ELECTRICAL CONNECTIONS TO MECHANICAL EQUIPMENT.

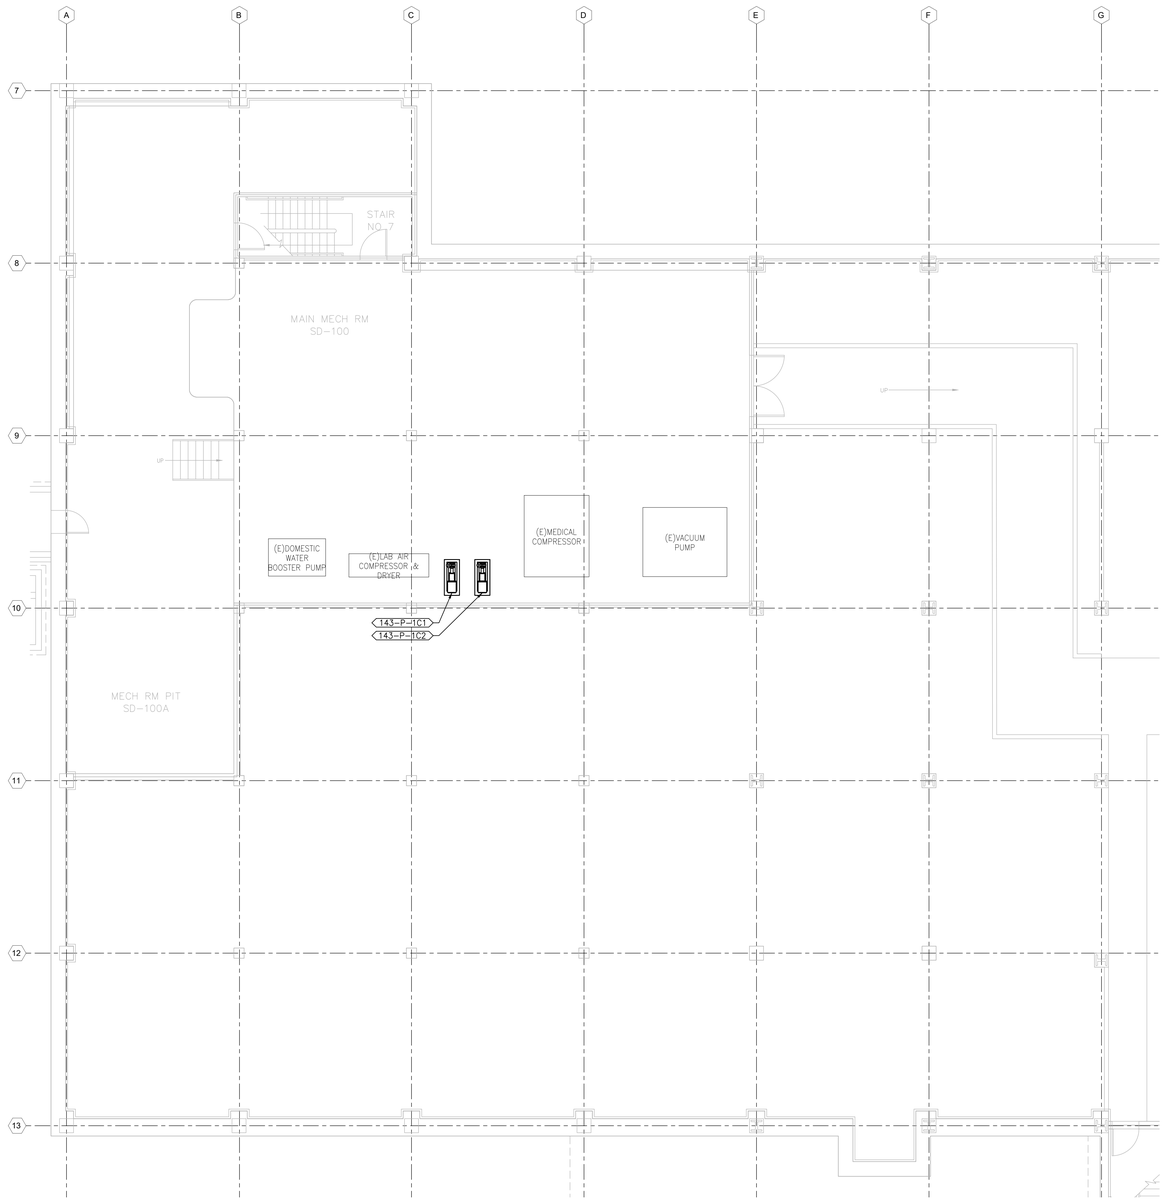

1 SUB-BASEMENT POWER PLAN
SCALE: 1/8" = 1'-0"

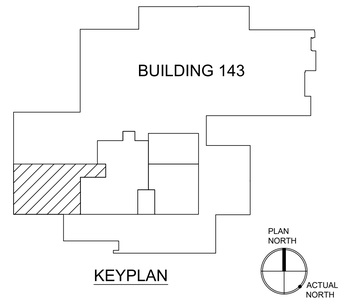

KEYPLAN

PRINTS OF THIS DRAWING SHALL NOT BE USED FOR ANY PURPOSE WHATSOEVER WITHOUT THE SEAL AND SIGNATURE OF THE PROFESSIONAL ENGINEER.

NO.	DESCRIPTION	DATE

CONSULTANTS

Architecture:	Civil Engineering:	Fire & Life Safety:
PF&A DESIGN, P.C.	LABELLA ASSOCIATES	STANTON ENGINEERING SERVICES, LLC

ENGINEER OF RECORD

MILLER•REMICK
A Service-Disabled Veteran-Owned Small Business
(856) 429-4000 ✳ Miller-Remick.com
M-R PROJECT NO. 0499-0136

MILLER-REMICK LLC
PROFESSIONAL ENGINEER

COMMONWEALTH OF PENNSYLVANIA
REGISTERED PROFESSIONAL
THOMAS REGINO
ENGINEER No. PE094195
12/30/25

Office of Construction and Facilities Management

U.S. Department of Veterans Affairs

Drawing Title ELECTRICAL POWER PLAN SUB-BASEMENT, PHASE 1	**Phase** BID DOCUMENTS	**Project Title** RENOVATE SURGICAL SUITE PHASE II	**VA Drawing Number** 2617
Approved by: Jon Manninen, COR	FULLY SPRINKLERED	**Project Number** 658-19-103	**Building Number** 143
		Location SALEM VA MEDICAL CENTER	**Drawing Number** P1-EP100
		Issue Date 2025-12-30 / **Checked** LIB / **Drawn** MJR	

VA FORM 08-6231

P:\0499_PVA\0499-0136 Salem Renovate Surgical Suite\4_Drawings\1_Cad\1_Current Submittal Phase\7_Electrical\P1-EP100.dwg 12-29-25 05:55:12 PM mcfeliff

GENERAL SHEET NOTES:

1. SEE DRAWING E-001 FOR ELECTRICAL SYMBOLS AND ABBREVIATIONS AND DRAWING E-002 FOR ELECTRICAL NOTES.
2. SEE DRAWING E-701 AND E-702 FOR PANEL SCHEDULES AND E-602 FOR SINGLE LINE DIAGRAM.
3. ALL ELECTRICAL DEVICES ON THIS SHEET SHALL BE NEW, UNLESS OTHERWISE NOTED.

SHEET KEYNOTES:

1 STRUCTURAL WORK TO BRACE HYBRID EQUIPMENT ABOVE IN THIS AREA. EXISTING CEILING SHALL BE DROPPED TO ACCOMMODATE STRUCTURAL WORK. E.C. SHALL DISCONNECT, CLEAN, AND STORE ALL LIGHT FIXTURES AND OTHER ELECTRICAL DEVICES IN THIS AREA AND REINSTALL BACK INTO THE NEW CEILING IN THE SAME LOCATION. SPLICE AND EXTEND BRANCH CIRCUITING AS REQUIRED. COORDINATE EXTENT OF WORK WITH STRUCTURAL AND ARCHITECTURAL DRAWINGS.

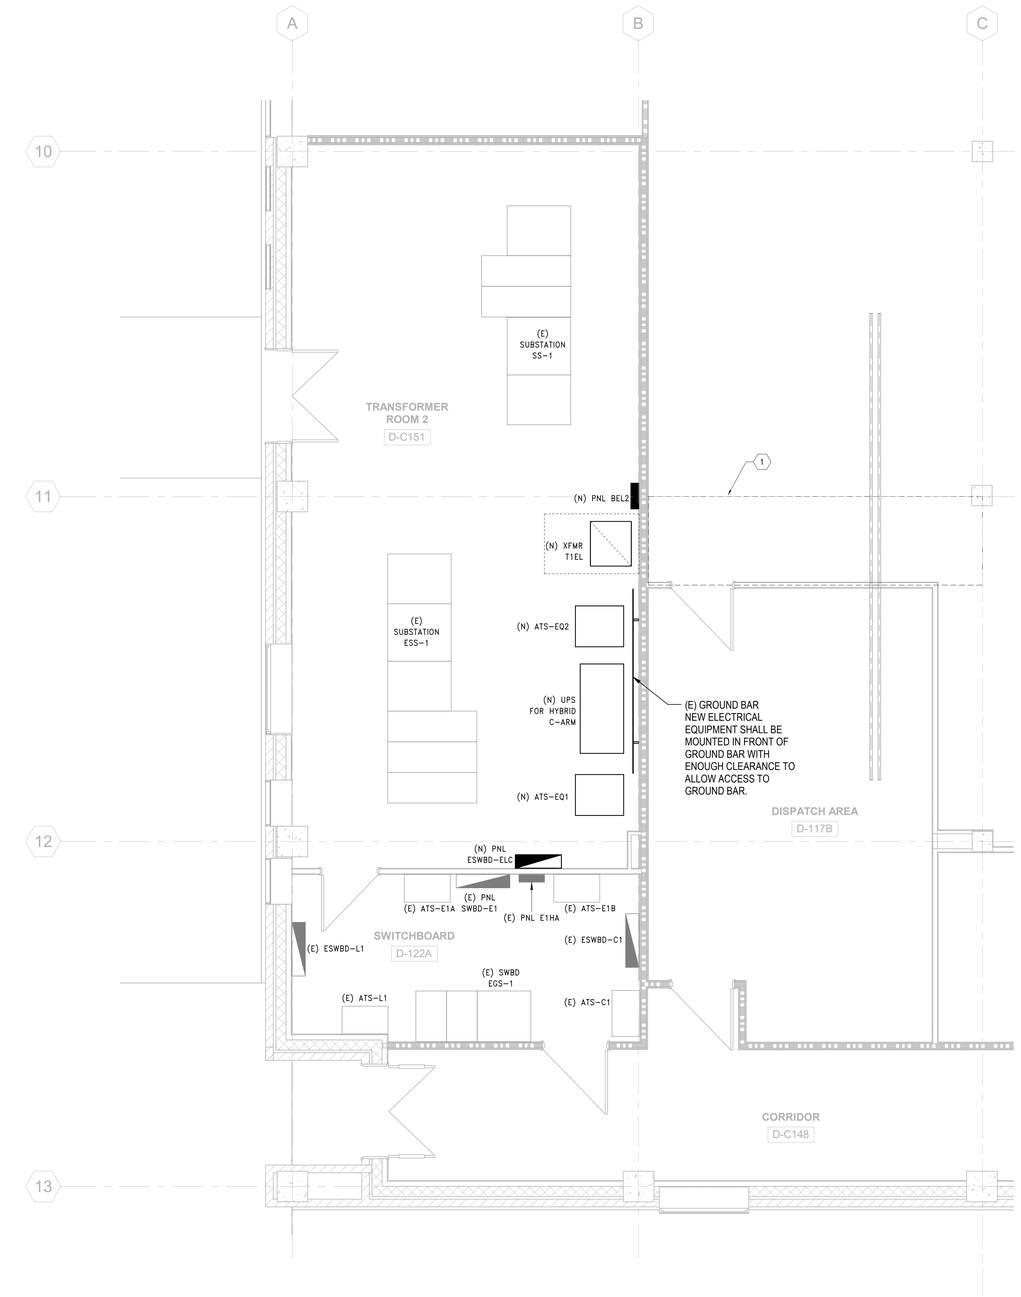

1 POWER PLAN - BASEMENT (BASEMENT TRANSFORMER RM BD-122/ELECTRICAL RM BD-122A)
SCALE: 1/4" = 1'-0"

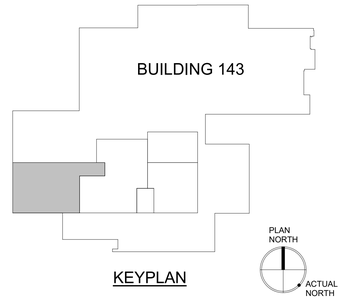

KEYPLAN

PRINTS OF THIS DRAWING SHALL NOT BE USED FOR ANY PURPOSE WHATSOEVER WITHOUT THE SEAL AND SIGNATURE OF THE PROFESSIONAL ENGINEER

Revisions:	Date:

CONSULTANT

Architecture:	Civil Engineering:	Fire Protection:
PF&A DESIGN, P.C.	LABELLA ASSOCIATES	STANTON ENGINEERING SERVICES, LLC

ENGINEER OF RECORD

MILLER-REMICK
A Service-Disabled Veteran-Owned Small Business
(856) 429-4000 • Miller-Remick.com
STA-HOCH14-DOE-20072018

MILLER-REMICK LLC PROFESSIONAL ENGINEER

COMMONWEALTH OF PENNSYLVANIA REGISTERED PROFESSIONAL THOMAS REGINO ENGINEER PA PE084195
12/30/25

Office of Construction and Facilities Management

VA U.S. Department of Veterans Affairs

Drawing Title ELECTRICAL POWER PLAN BASEMENT, PHASE 1	**Phase** BID DOCUMENTS	**Project Title** RENOVATE SURGICAL SUITE PHASE II	**VA Drawing Number** 2617
Approved by: Jon Manninen, COR	FULLY SPRINKLERED	**Project Number** 658-19-103	**Building Number** 143
		Location SALEM VA MEDICAL CENTER	**Drawing Number** P1-EP101
		Issue Date 2025-12-30 / **Checked** MJR / **Drawn** PDK	

12/29/2025 5:32:00 PM

VA FORM 08 - 6231

GENERAL SHEET NOTES:

1. SEE DRAWING E-001 FOR ELECTRICAL SYMBOLS AND ABBREVIATIONS AND DRAWING E-002 FOR ELECTRICAL NOTES.
2. SEE DRAWING E-701 AND E-702 FOR PANEL SCHEDULES AND E-602 FOR SINGLE LINE DIAGRAM.
3. ALL ELECTRICAL DEVICES ON THIS SHEET SHALL BE NEW, UNLESS OTHERWISE NOTED.

⬡ SHEET KEYNOTES:

1 NEW MOTORIZED DAMPER. PROVIDE JUNCTION BOX FOR 120V POWER CONNECTION AND 3/4" C, FROM CIRCUIT GL-4, TO GENERATOR CONTROLLER FOR SIGNALING WIRE.

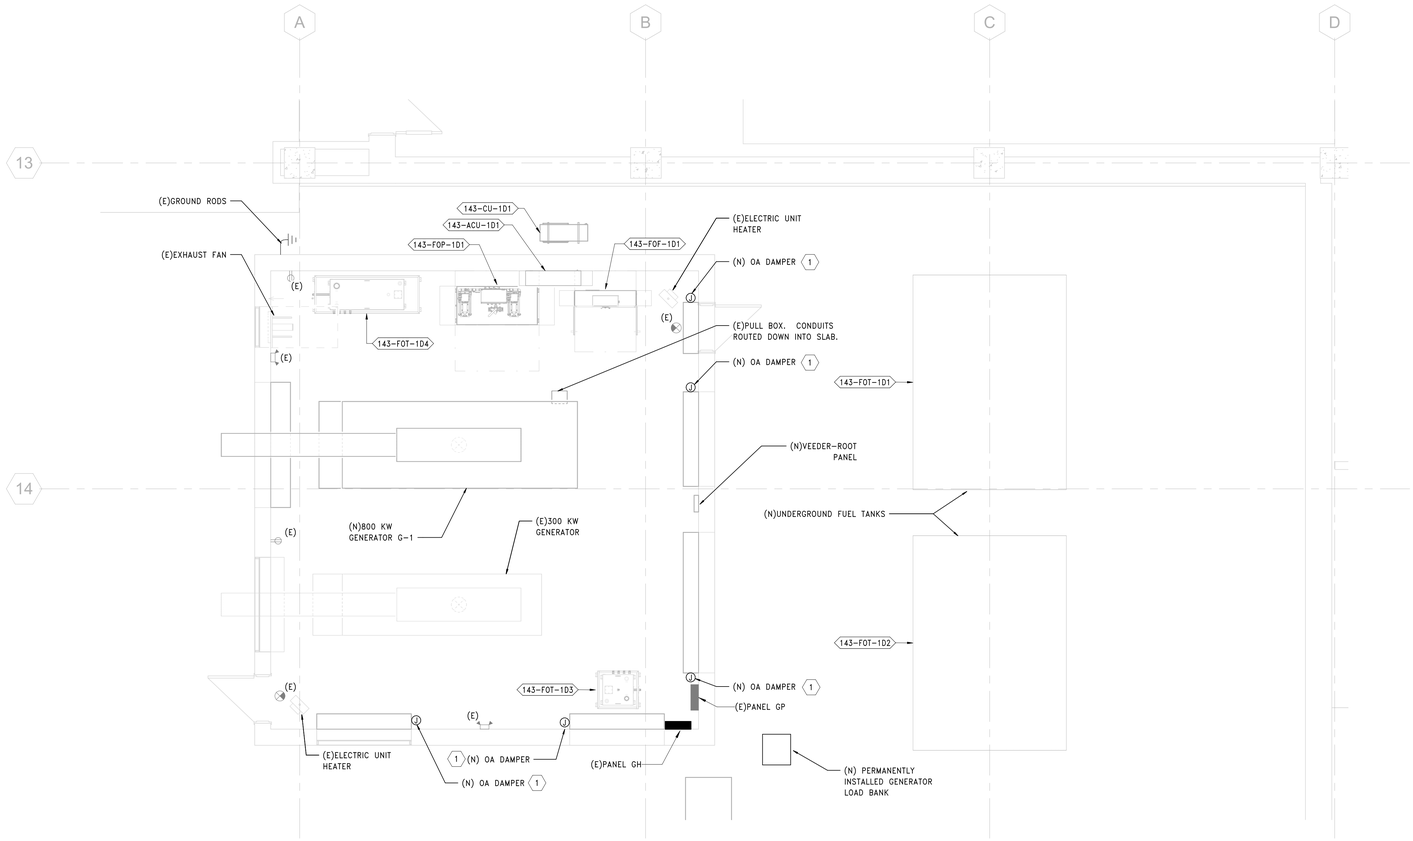

1 POWER PLAN - BASEMENT, PHASE 1 - GENERATOR

SCALE: 1/4" = 1'-0"

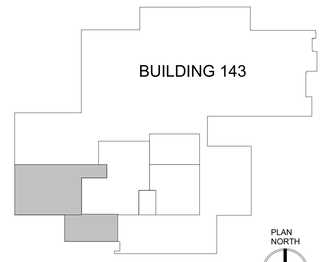

KEYPLAN

PRINTS OF THIS DRAWING SHALL NOT BE USED FOR ANY PURPOSE WHATSOEVER WITHOUT THE SEAL AND SIGNATURE OF THE PROFESSIONAL ENGINEER

Revisions:	Date:

12/29/2025 9:32:09 PM

CONSULTANT

Architecture:	Civil Engineering:	Fire Protection:
PF&A DESIGN, P.C.	LABELLA ASSOCIATES	STANTON ENGINEERING SERVICES, LLC

ENGINEER OF RECORD

MILLER+REMICK
A Service-Disabled Veteran-Owned Small Business
(856) 429-4000 ★ Miller-Remick.com
M-R PROJECT NO. 0909-0036

MILLER-REMICK LLC PROFESSIONAL ENGINEER

COMMONWEALTH OF PENNSYLVANIA — REGISTERED PROFESSIONAL — THOMAS REGINO — ENGINEER — No. PE094176

12/30/25

Office of Construction and Facilities Management

VA U.S. Department of Veterans Affairs

Drawing Title ELECTRICAL POWER PLAN BASEMENT, PHASE 1	**Phase** BID DOCUMENTS	**Project Title** RENOVATE SURGICAL SUITE PHASE II	**VA Drawing Number** 2617
Approved by: Jon Manninen, COR	FULLY SPRINKLERED	**Project Number** 658-19-103	**Building Number** 143
		Location SALEM VA MEDICAL CENTER	**Drawing Number** P1-EP102
		Issue Date 2025-12-30 / **Checked** MJR / **Drawn** PDK	

VA FORM 08 - 6231

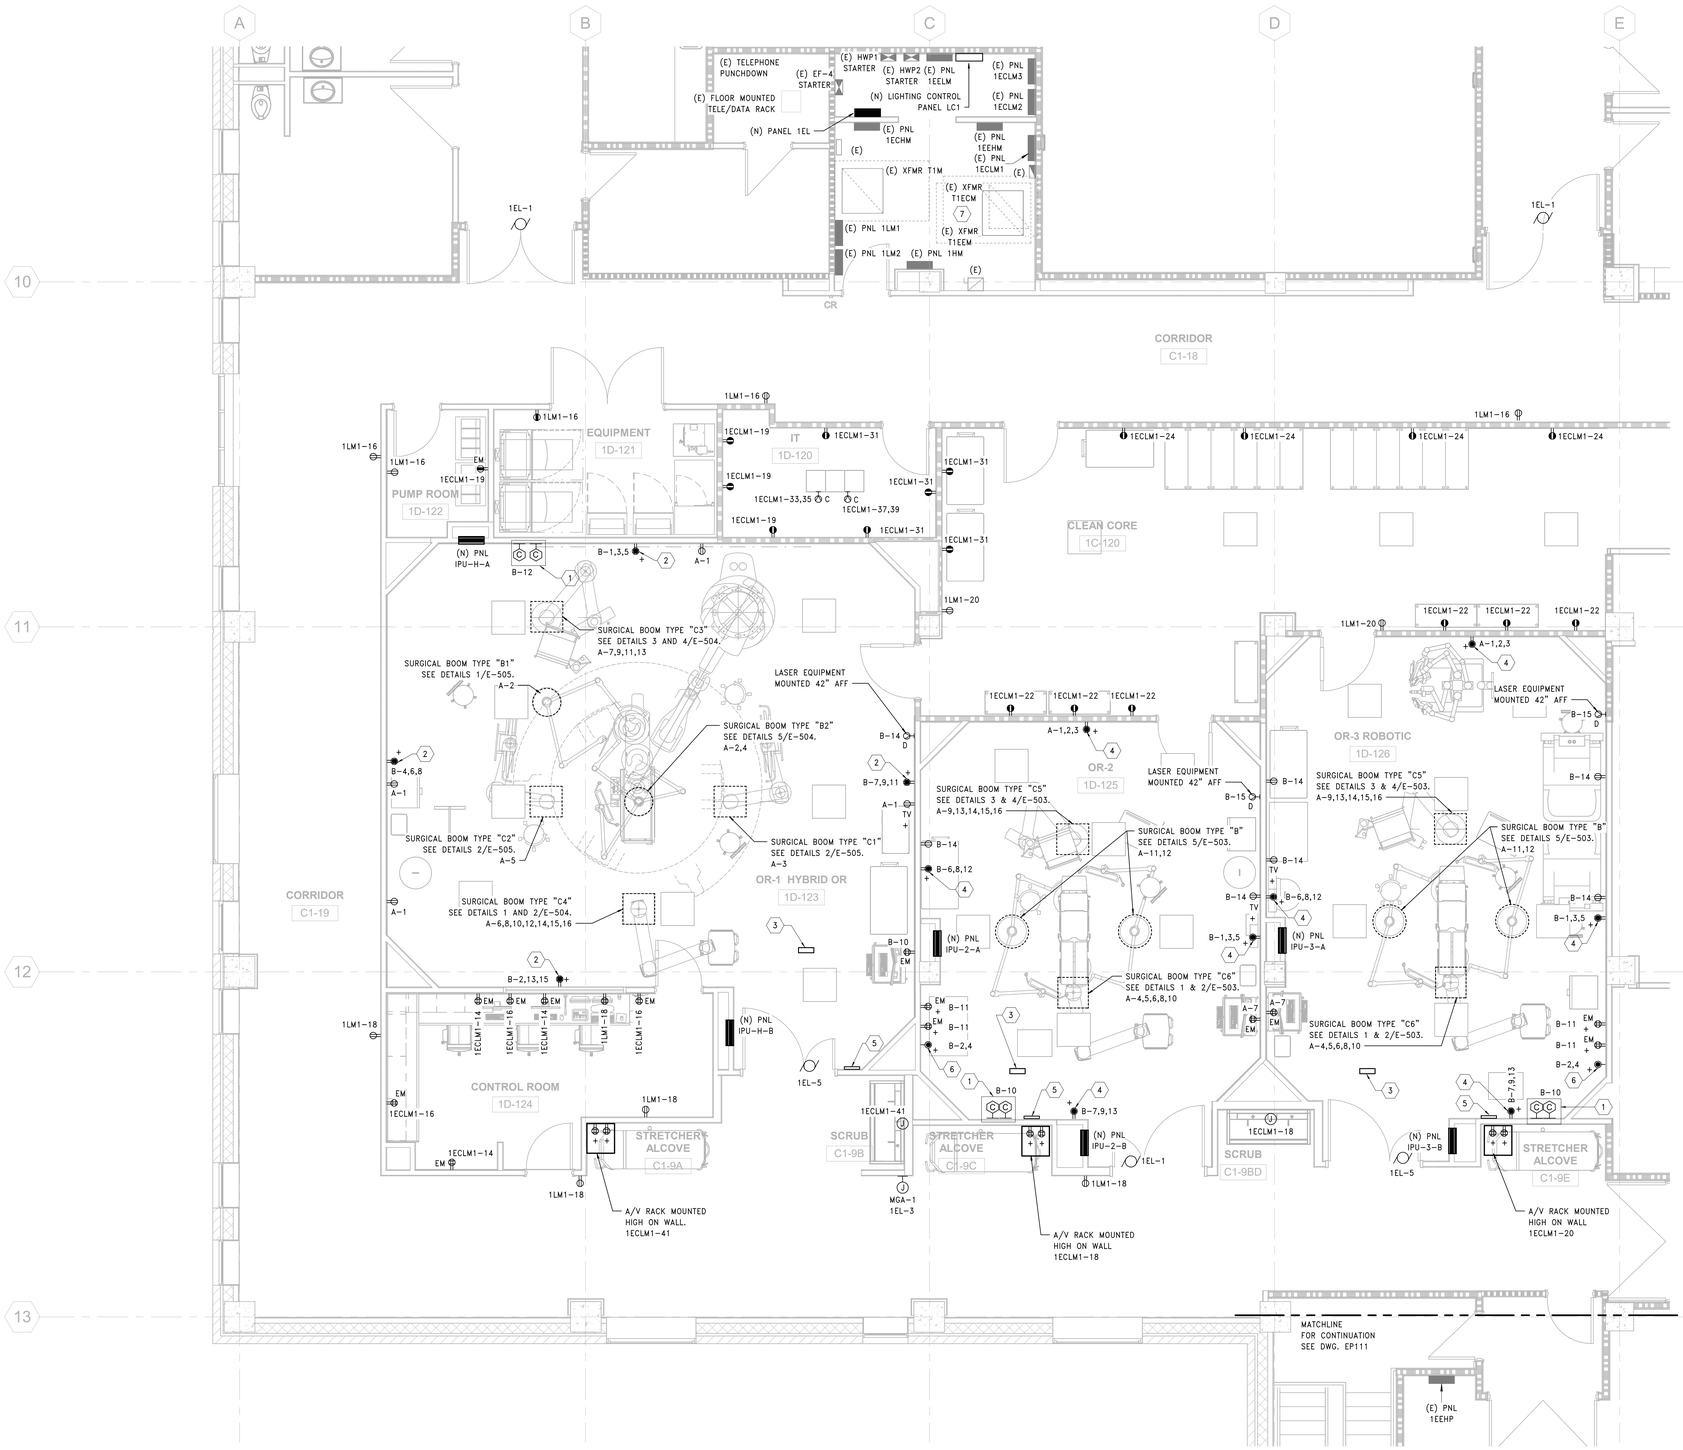

GENERAL SHEET NOTES:

1. SEE DRAWING E-001 FOR ELECTRICAL SYMBOLS AND ABBREVIATIONS AND DRAWING E-002 FOR ELECTRICAL NOTES.
2. SEE DRAWING E-602 FOR SINGLE LINE DIAGRAM.
3. SEE DRAWING E-701 AND E-702 FOR PANEL SCHEDULES AND E-703 FOR ISOLATION PANEL SCHEDULES.
4. ALL ELECTRICAL DEVICES ON THIS SHEET SHALL BE NEW, UNLESS OTHERWISE NOTED.
5. UNLESS OTHERWISE NOTED ALL CIRCUITS WITHIN AN OR SHALL BE FED FROM THE A OR B IPU PANELS LOCATED WITHIN THAT OR.

SHEET KEYNOTES:

1. DIGITAL TIME CLOCK AND ELAPSED TIMER. DISPLAY REMOTELY CONTROLLED BY USER WITH 2-GANG BACKBOX AND BATTERY PACK.
2. POWER GROUND MODULE. REFER TO DETAIL 7C/E-502 FOR BACKBOX CONFIGURATION AND MOUNTING HEIGHT.
3. GROUND REFERENCE POINT. REFER TO DETAIL 2/E-502.
4. POWER GROUND MODULE. REFER TO DETAIL 7A/E-502 FOR BACK BOX CONFIGURATION AND MOUNTING HEIGHT.
5. SURGICAL BOOM LIGHT HEAD CONTROLLER UNIT. REFER TO DETAIL 5/E-503 FOR WIRING AND CONNECTIONS. CONTRACTOR SHALL COORDINATE WITH EQUIPMENT MANUFACTURER INSTALLATION GUIDELINES FOR WALL CONTROLLER.
6. POWER GROUND MODULE. REFER TO DETAIL 7B/E-502 FOR BACK BOX CONFIGURATION AND MOUNTING HEIGHT.
7.

1 POWER PLAN - 1ST FLOOR, PHASE 1

SCALE: 1/4" = 1'-0"

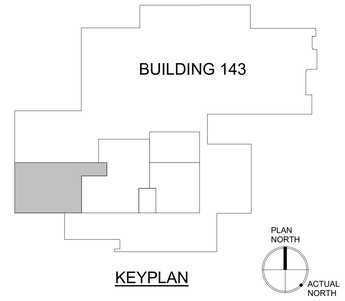

KEYPLAN

PRINTS OF THIS DRAWING SHALL NOT BE USED FOR ANY PURPOSE WHATSOEVER WITHOUT THE SEAL AND SIGNATURE OF THE PROFESSIONAL ENGINEER

Revisions:	Date:

12/29/2025 5:32:12 PM

CONSULTANT

Architecture:	Civil Engineering:	Fire Protection:
PF&A DESIGN, P.C.	LABELLA ASSOCIATES	STANTON ENGINEERING SERVICES, LLC

ENGINEER OF RECORD

MILLER-REMICK
A Service-Disabled Veteran-Owned Small Business
(856) 429-4000 ▪ Miller-Remick.com
1845 Route 70 East, Cherry Hill, NJ 08003

MILLER-REMICK LLC PROFESSIONAL ENGINEER

COMMONWEALTH OF PENNSYLVANIA — REGISTERED PROFESSIONAL — THOMAS REGINO — ENGINEER No. PE094195
12/30/25

Office of Construction and Facilities Management

VA U.S. Department of Veterans Affairs

Drawing Title	ELECTRICAL POWER PLAN 1ST FLOOR, PHASE 1
Approved by:	Jon Manninen, COR
Phase	BID DOCUMENTS
	FULLY SPRINKLERED
Project Title	RENOVATE SURGICAL SUITE PHASE II
Project Number	658-19-103
Location	SALEM VA MEDICAL CENTER
Issue Date	2025-12-30
Checked	MJR
Drawn	PDK
VA Drawing Number	2617
Building Number	143
Drawing Number	P1-EP111

VA FORM 08 - 6231

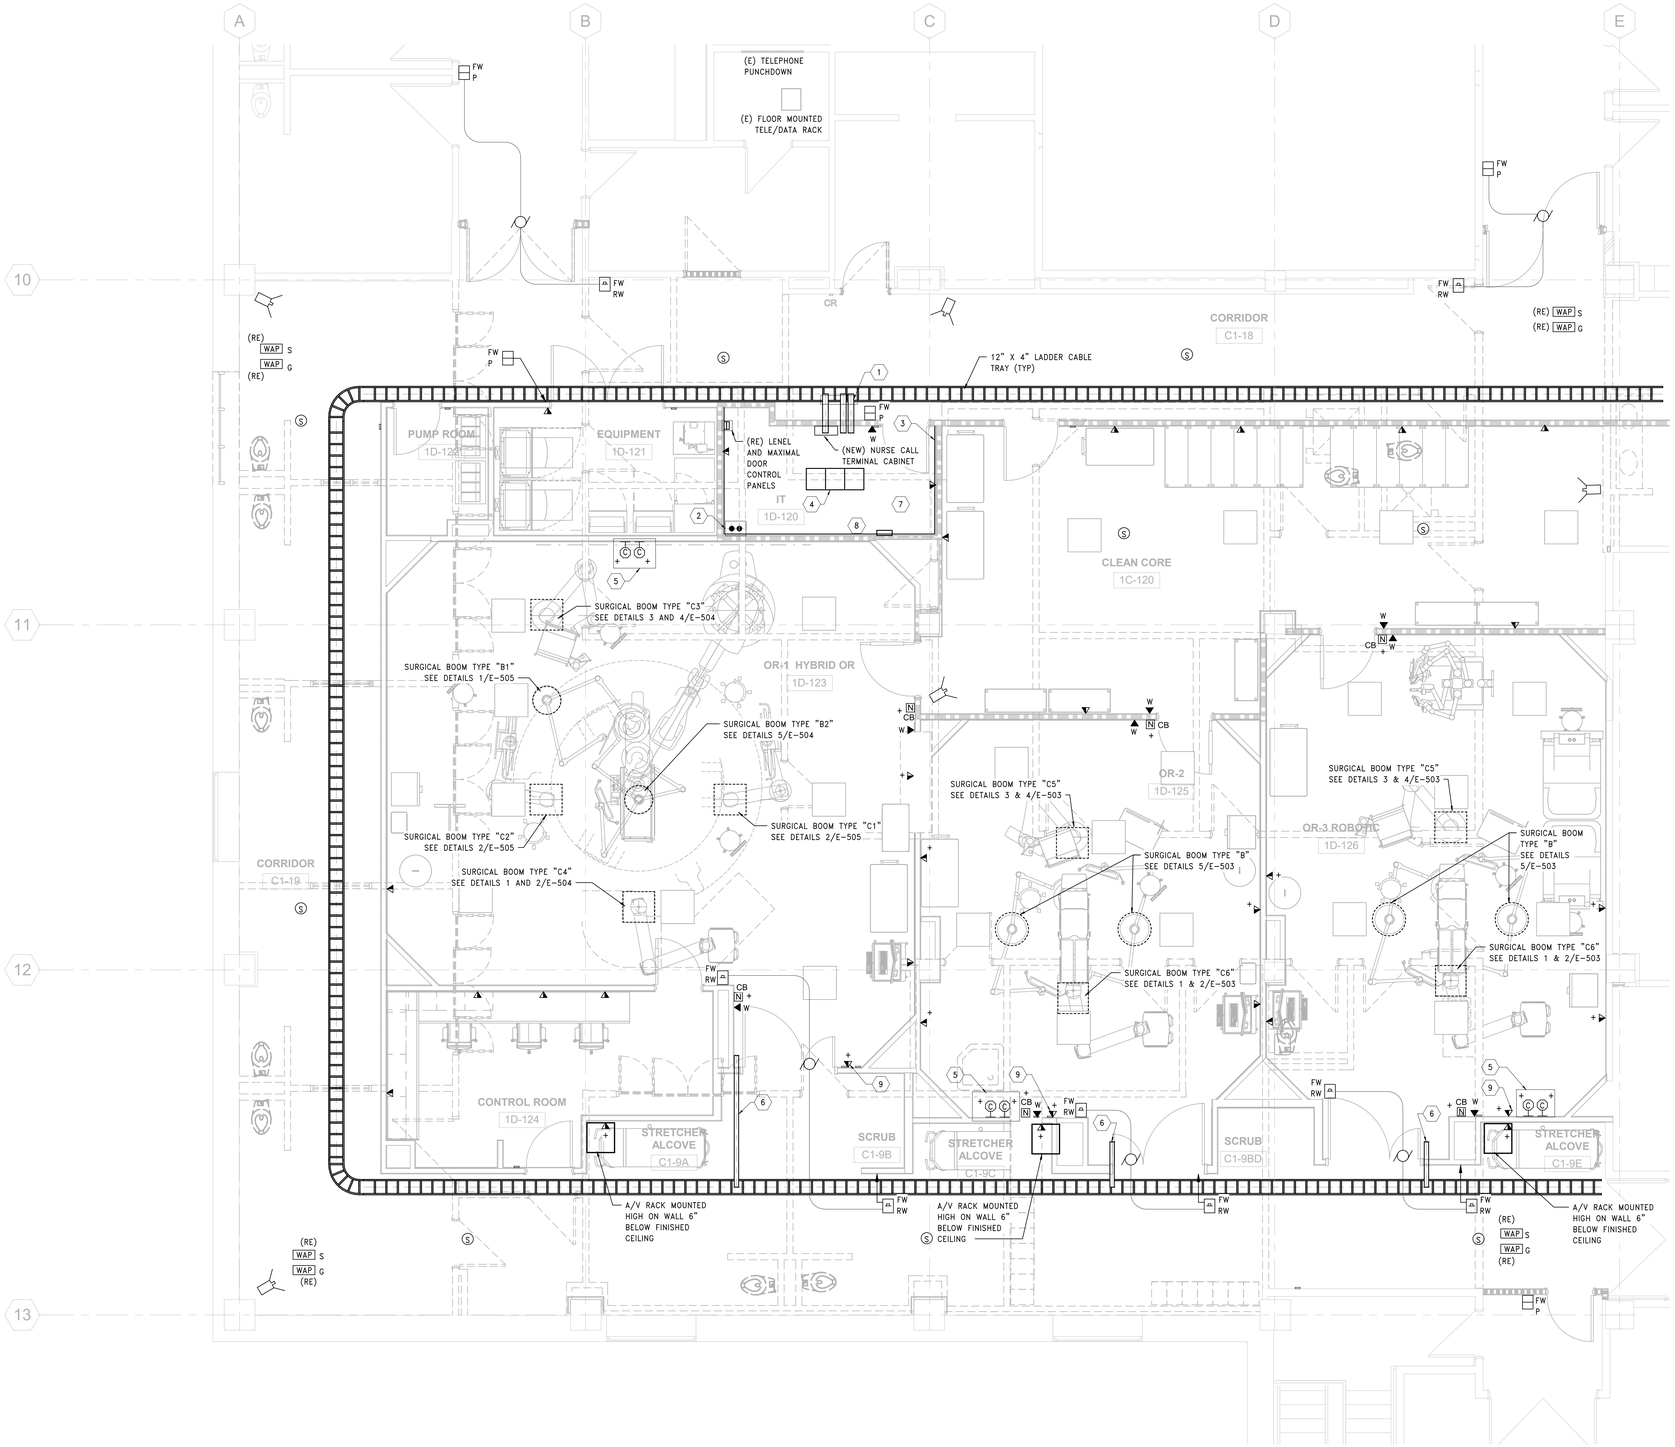

GENERAL SHEET NOTES:

1. SEE DRAWING E-001 FOR ELECTRICAL SYMBOLS AND ABBREVIATIONS AND DRAWING E-002 FOR ELECTRICAL NOTES.
2. SEE DRAWING E-603 FOR TELE/DATA DEVICE DETAILS, CABLE TRAY DETAILS, AND TELE/DATA RISER DIAGRAM.
3. ALL TELE/DATA DEVICES ON THIS SHEET SHALL BE NEW, UNLESS OTHERWISE NOTED.
4. FOR FURTHER INFORMATION ON CARD ACCESS AND MOTORIZED DOORS, REFER TO DETAILS 3 AND 4/E-502.
5. ALL TELE/DATA WIRING FOR DEVICES ON THIS DRAWING SHALL BE PULLED BACK TO NEW TELE/DATA RACK IN IT ID-1002.
6. EC SHALL REINSTALL AND PULL NEW CAT6 WIRING TO ALL CEILING MOUNTED CENTRAK DEVICES IN THIS AREA. E.C. SHALL ALSO PROVIDE NEW CENTRAK DEVICES TO MATCH EXISTING DEVICES AS REQUIRED TO MEET THE NEEDS OF THE PROGRAM FOR THIS PROJECT. E.C. SHALL COORDINATE WITH VA AND THEIR CENTRAK REPRESENTATIVE IN REGARDS TO THE QUANTITY AND PLACEMENT REQUIREMENTS OF ALL RELOCATED AND NEW DEVICES, AS WELL AS THE WIRING REQUIREMENTS.
7. SEE NOTES 58 AND 59 ON DRAWING E-002 FOR FURTHER INFORMATION ON WIRELESS ACCESS POINT REQUIREMENTS.
8. ALL SECURITY CAMERAS SHOWN SHALL BE WIRED BACK TO EXISTING SECURITY HEADEND IN ROOM BC-114 WITH MANUFACTURER RECOMMENDED POE CABLE.

SHEET KEYNOTES:

1
2 PROVIDE (2) TWO – 4" FLOOR CORES WITH CONDUIT SLEEVES AND BUSHED CAPS. SEAL PENETRATION AS REQUIRED.
3 PROVIDE 4' X 8' X 3/4" FIRE RETARDANT PAINTED PLYWOOD BACKBOARD (TYP OF 3 WALLS).
4 TOTAL OF (3) THREE IT RACKS.
5 DIGITAL TIME CLOCK AND ELAPSED TIMER. DISPLAY REMOTELY CONTROLLED BY USER WITH 2-GANG BACKBOX AND BATTERY PACK.
6 PROVIDE (1) ONE – 3" CONDUIT ABOVE ACCESSIBLE CEILING AS A PASS-THRU FOR TELECOMMUNICATION CABLING. CONDUIT SHALL BE PROVIDED WITH BUSHED ENDS AND PULL STRING. SEAL PENETRATION AS REQUIRED.
7 EC SHALL PROVIDE 12" LADDER CABLE TRAY AROUND PERIMETER OF ROOM AND ALSO TO EACH IT RACK.
8 GROUND BAR. REFER TO DETAIL 11/E-501 FOR FURTHER INFORMATION.
9 TELECOMMUNICATION DROP FOR SURGICAL BOOM LIGHT HEAD CONTROLLER. REFER TO DETAIL 5/E-503 FOR FURTHER INFORMATION.

1 SYSTEMS PLAN - 1ST FLOOR, PHASE 1

SCALE: 1/4" = 1'-0"

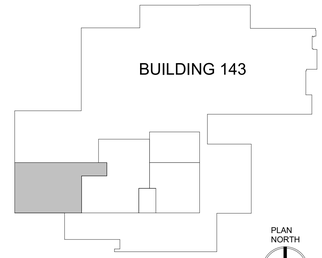

KEYPLAN

PRINTS OF THIS DRAWING SHALL NOT BE USED FOR ANY PURPOSE WHATSOEVER WITHOUT THE SEAL AND SIGNATURE OF THE PROFESSIONAL ENGINEER

Revisions:	Date:

CONSULTANT

Architecture:	Civil Engineering:	Fire Protection:
PF&A DESIGN, P.C.	LABELLA ASSOCIATES	STANTON ENGINEERING SERVICES, LLC

ENGINEER OF RECORD

MILLER-REMICK

A Service-Disabled Veteran-Owned Small Business

(856) 429-5000 ▪ Miller-Remick.com

MILLER-REMICK LLC
PROFESSIONAL ENGINEER

COMMONWEALTH OF PENNSYLVANIA — REGISTERED PROFESSIONAL — THOMAS REGINO — ENGINEER No. PE094195 — 12/30/25

Office of Construction and Facilities Management

VA U.S. Department of Veterans Affairs

Drawing Title: ELECTRICAL SYSTEMS PLAN 1ST FLOOR, PHASE 1	Phase: BID DOCUMENTS	Project Title: RENOVATE SURGICAL SUITE PHASE II	VA Drawing Number: 2617
Approved by: Jon Manninen, COR	FULLY SPRINKLERED	Project Number: 658-19-103	Building Number: 143
		Location: SALEM VA MEDICAL CENTER	Drawing Number: P1-EY111
		Issue Date: 2025-12-30 / Checked: MJR / Drawn: PDK	

12/29/2025 5:32:13 PM

VA FORM 08 - 6231

GENERAL SHEET NOTES:

1. SEE DRAWINGS E-001 AND E-002 FOR ABBREVIATIONS, SYMBOLS AND NOTES.

SHEET KEYNOTES:

1. DEMOLISH ALL ELECTRICAL DEVICES INCLUDING, BUT NOT LIMITED TO, PANELBOARDS, LIGHTING, LIGHTING CONTROL, RECEPTACLES, TELE/DATA AND FIRE ALARM DEVICES, ETC. WITHIN BOUNDARY, UNLESS OTHERWISE NOTED. DEMOLISH ALL ELECTRICAL DEVICE WIRING AND RACEWAYS BACK TO SOURCE.
2. DOOR CONTROL PANELS SHALL BE RELOCATED TO NEW IT ID-1002. SPLICE AND EXTEND ALL EXISTING DOOR CONTROL WIRING TO EXISTING DOORS WITHIN NEW ABOVE CEILING MOUNTED JUNCTION BOXES. COORDINATE DOOR CONTROL OUTAGES WITH VA PRIOR TO SERVICE DOWNTIME.
3. ALL WIRELESS ACCESS POINTS AND CENTRAK DEVICES WITHIN THIS BOUNDARY SHALL BE REMOVED, CLEANED, AND STORED FOR REINSTALLATION.

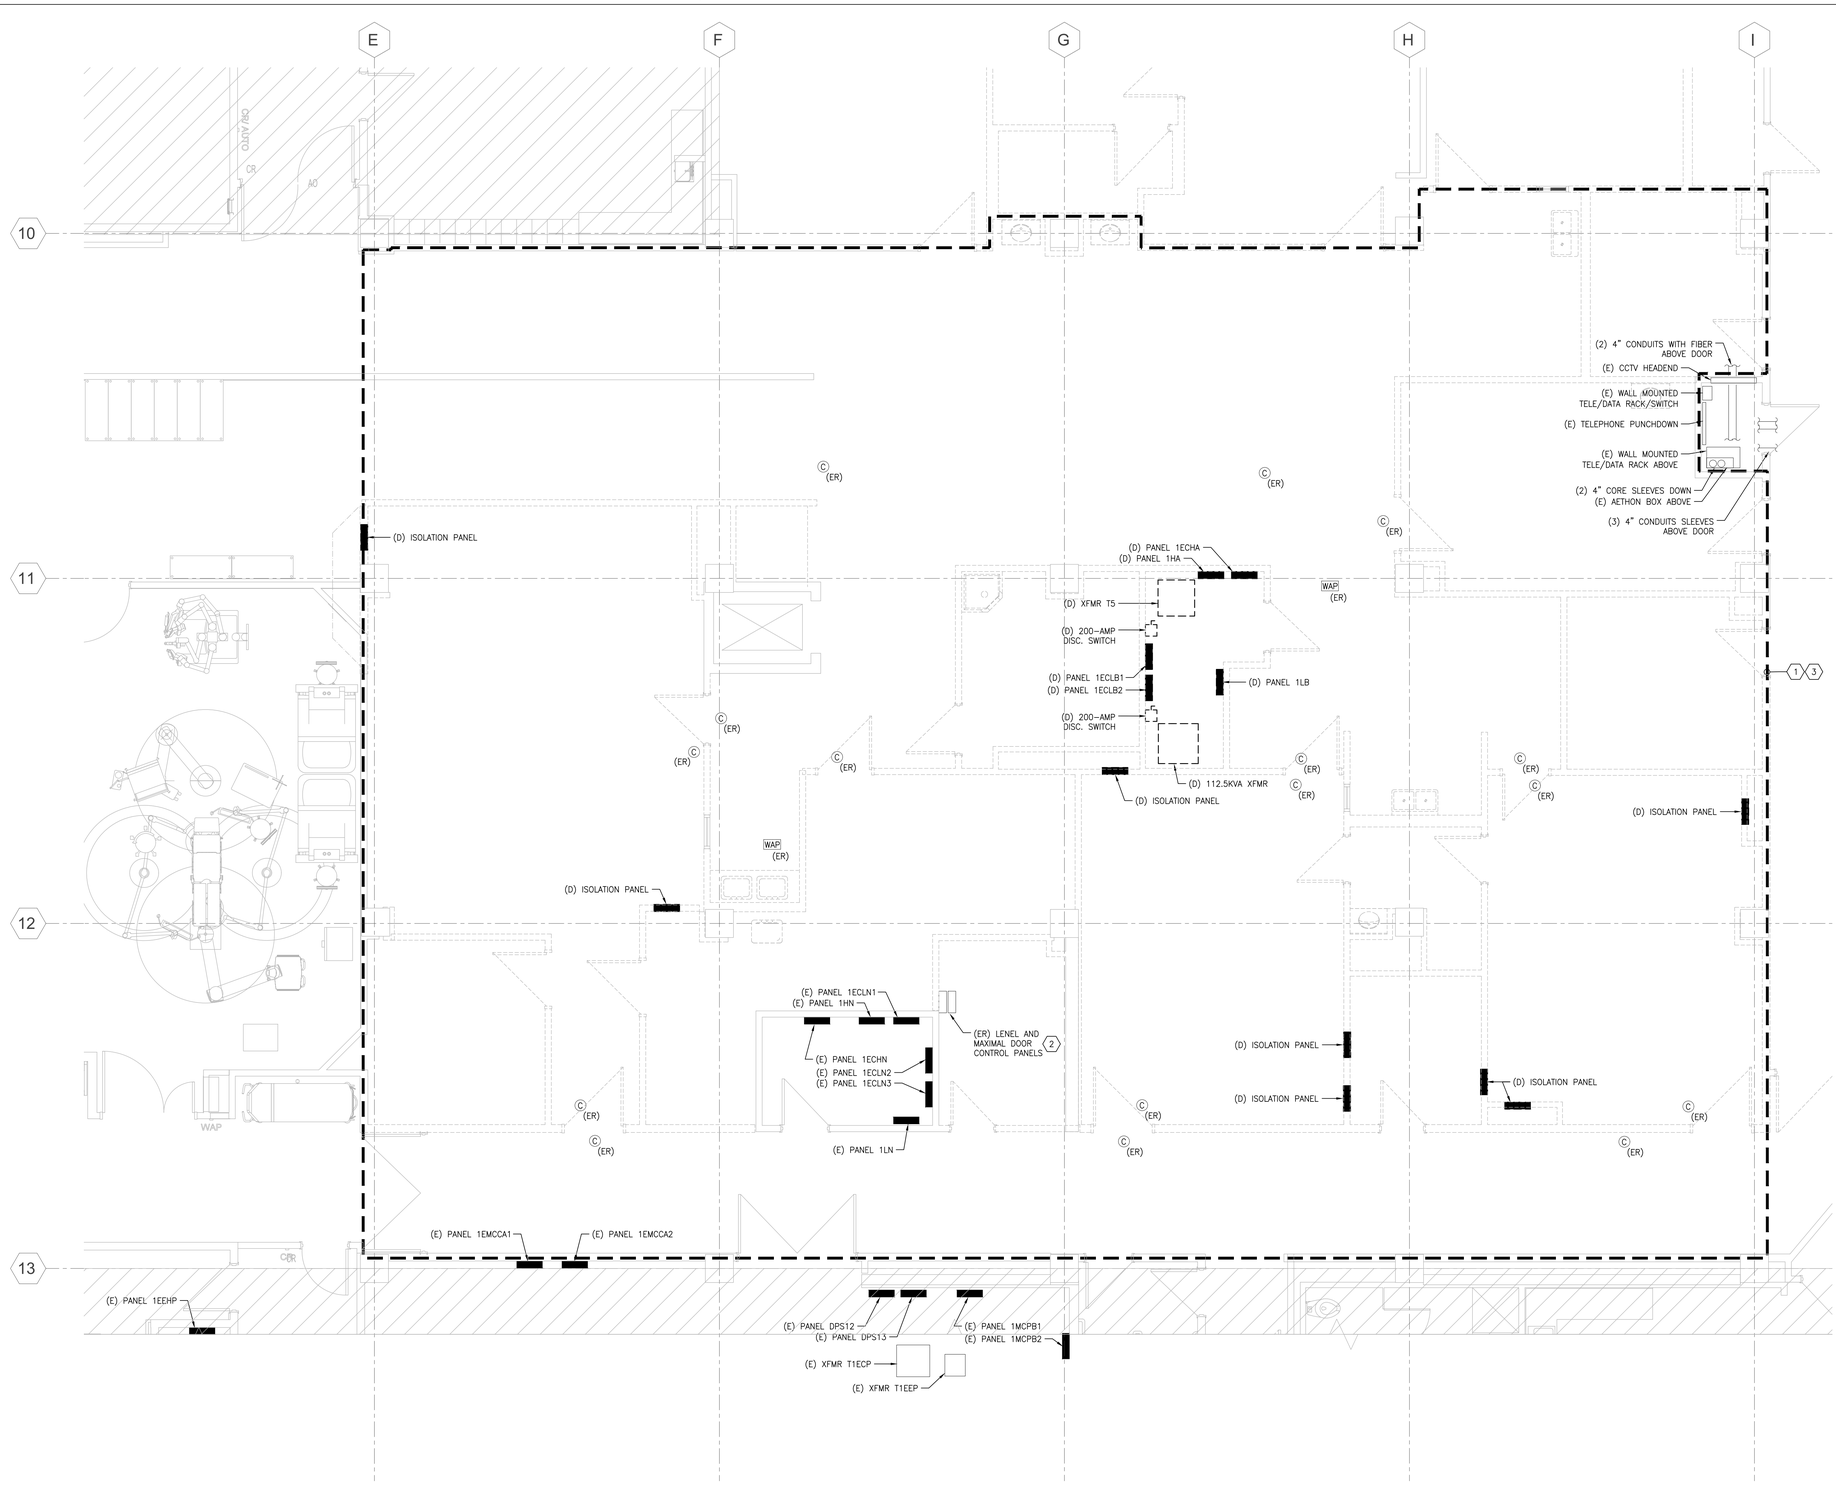

1 ELECTRICAL DEMOLITION PLAN – 1ST FLOOR, PHASE 2 (SOUTH)
SCALE: 1/4" = 1'-0"

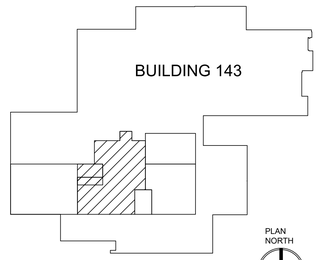

KEYPLAN

PRINTS OF THIS DRAWING SHALL NOT BE USED FOR ANY PURPOSE WHATSOEVER WITHOUT THE SEAL AND SIGNATURE OF THE PROFESSIONAL ENGINEER.

NO.	DESCRIPTION	DATE

CONSULTANTS

Architecture:	Civil Engineering:	Fire & Life Safety:
PF&A DESIGN, P.C.	LABELLA ASSOCIATES	STANTON ENGINEERING SERVICES, LLC

ENGINEER OF RECORD

MILLER-REMICK
A Service-Disabled Veteran-Owned Small Business
(856) 429-4000 • Miller-Remick.com
M-R PROJECT NO: 04099-0156

MILLER-REMICK LLC
PROFESSIONAL ENGINEER
COMMONWEALTH OF PENNSYLVANIA
REGISTERED PROFESSIONAL ENGINEER
THOMAS REGINO
ENGINEER No. PE094195
12/30/25

Office of Construction and Facilities Management

VA U.S. Department of Veterans Affairs

Drawing Title	ELECTRICAL DEMOLITION PLAN 1ST FLOOR, PHASE 2 (SOUTH)
Approved by:	Jon Manninen, COR
Phase	BID DOCUMENTS
	FULLY SPRINKLERED
Project Title	RENOVATE SURGICAL SUITE PHASE II
Project Number	658-19-103
Location	SALEM VA MEDICAL CENTER
Issue Date	2025-12-30
Checked	MJR
Drawn	MJR
VA Drawing Number	2617
Building Number	143
Drawing Number	P2-ED111

VA FORM 08-6231

C:\Users\mcifelli\AppData\Local\Temp\AcPublish_11328\P2-ED111.dwg 12-29-25 05:55:14 PM mcifelli

GENERAL SHEET NOTES:

1. SEE DRAWINGS E-001 AND E-002 FOR ABBREVIATIONS, SYMBOLS AND NOTES.

SHEET KEYNOTES:

1. DEMOLISH ALL ELECTRICAL DEVICES INCLUDING, BUT NOT LIMITED TO, PANELBOARDS, LIGHTING, LIGHTING CONTROL, RECEPTACLES, TELE/DATA AND FIRE ALARM DEVICES, ETC. WITHIN BOUNDARY, UNLESS OTHERWISE NOTED. DEMOLISH ALL ELECTRICAL DEVICE WIRING AND RACEWAYS BACK TO SOURCE.
2. ALL WIRELESS ACCESS POINTS AND CENTRAX DEVICES WITHIN THIS BOUNDARY SHALL BE REMOVED, CLEANED, AND STORED FOR REINSTALLATION.

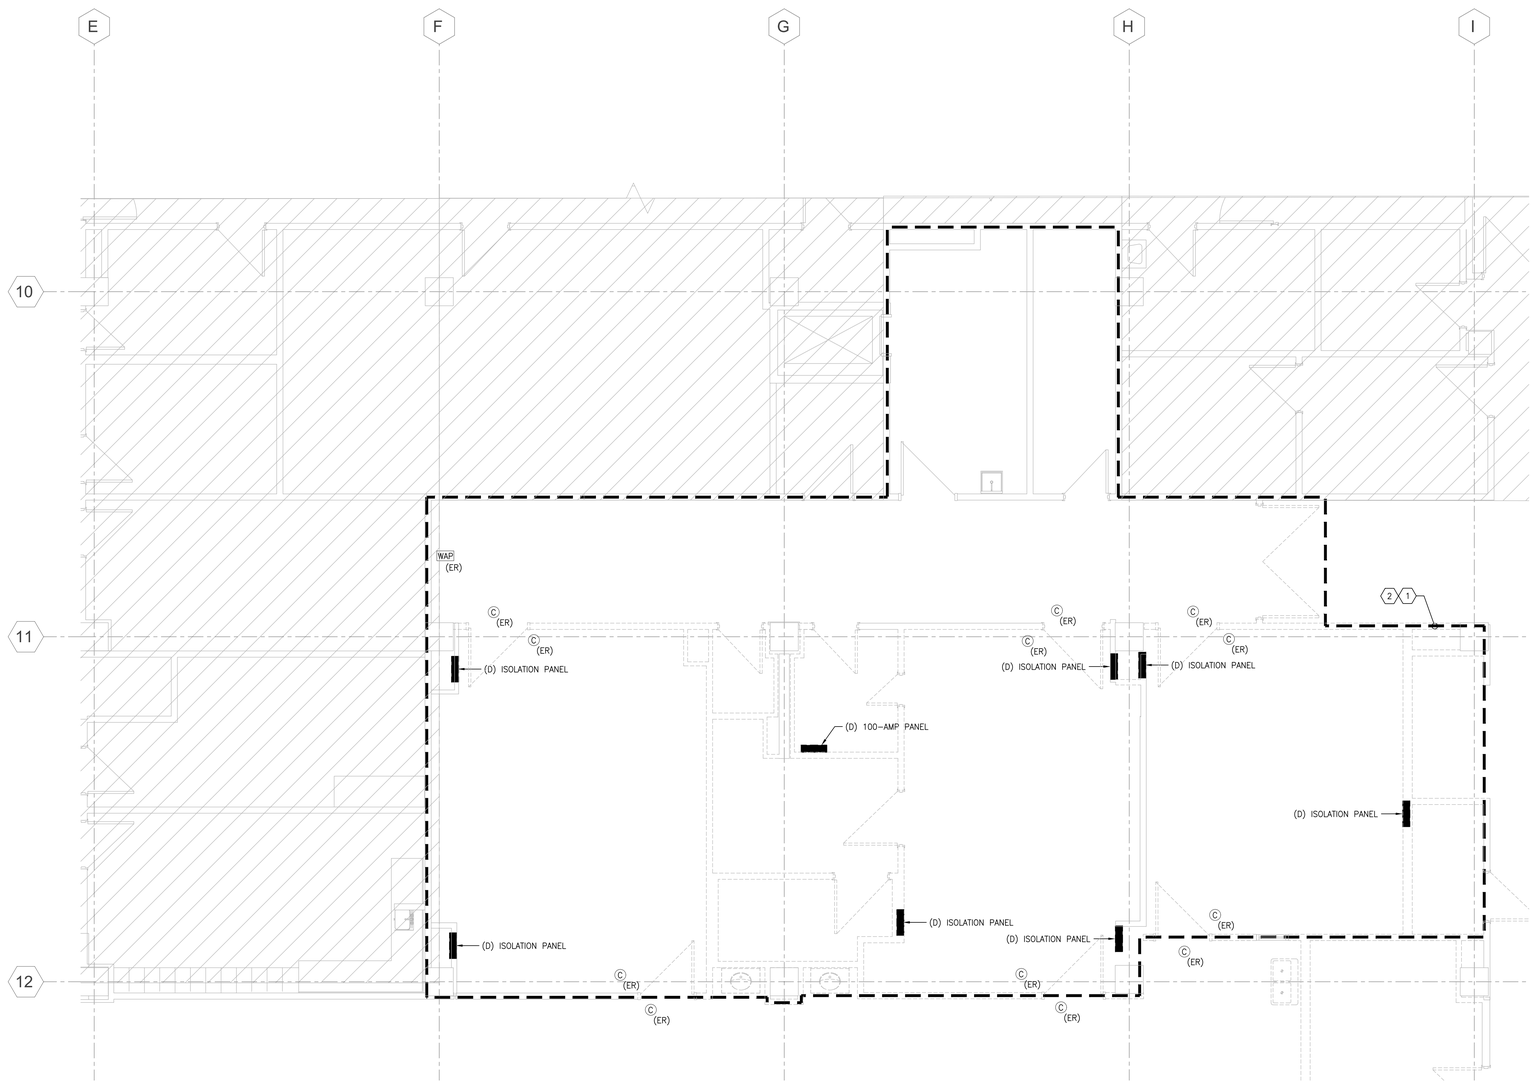

1 ELECTRICAL DEMOLITION PLAN – 1ST FLOOR, PHASE 2 (NORTH)
SCALE: 1/4" = 1'-0"

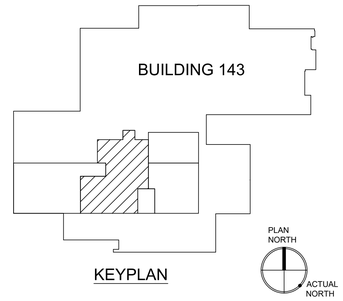

KEYPLAN

PRINTS OF THIS DRAWING SHALL NOT BE USED FOR ANY PURPOSE WHATSOEVER WITHOUT THE SEAL AND SIGNATURE OF THE PROFESSIONAL ENGINEER.

NO.	DESCRIPTION	DATE

CONSULTANTS

Architecture:	Civil Engineering:	Fire & Life Safety:
PF&A DESIGN, P.C.	LABELLA ASSOCIATES	STANTON ENGINEERING SERVICES, LLC

ENGINEER OF RECORD

MILLER•REMICK
A Service-Disabled Veteran-Owned Small Business
(856) 429-4000 ★ Miller-Remick.com
M-R PROJECT NO. 24XP-0256

MILLER-REMICK LLC
PROFESSIONAL ENGINEER
COMMONWEALTH OF PENNSYLVANIA
REGISTERED PROFESSIONAL ENGINEER
THOMAS REGINO
ENGINEER No. PE054195
12/30/25

Office of Construction and Facilities Management

VA U.S. Department of Veterans Affairs

Drawing Title ELECTRICAL DEMOLITION PLAN 1ST FLOOR, PHASE 2 (NORTH)	**Phase** BID DOCUMENTS	**Project Title** RENOVATE SURGICAL SUITE PHASE II	**VA Drawing Number** 2617
		Project Number 658-19-103	**Building Number** 143
Approved by: Jon Manninen, COR	FULLY SPRINKLERED	**Location** SALEM VA MEDICAL CENTER	**Drawing Number** P2-ED112
		Issue Date 2025-12-30 / **Checked** MJR / **Drawn** DRR	

VA FORM 08-6231

C:\Users\mcliteli\AppData\Local\Temp\AcPublish_11328\P2-ED112.dwg 12-29-25 05:55:16 PM mcliteli

GENERAL SHEET NOTES:

1. SEE DRAWING E-001 FOR ELECTRICAL SYMBOLS AND ABBREVIATIONS AND DRAWING E-002 FOR ELECTRICAL NOTES.
2. ALL ELECTRICAL DEVICES ON THIS SHEET SHALL BE NEW, UNLESS OTHERWISE NOTED.
3. SEE DRAWING E-704 AND E-705 FOR LIGHTING FIXTURE SCHEDULE, CIRCUITRY AND LIGHTING CONTROL INFORMATION. SEE DRAWING E-701 AND E-702 FOR PANEL SCHEDULES.
4. EXIT SIGNS SHALL BE CIRCUITED AHEAD OF ALL CONTROL DEVICES.

SHEET KEYNOTES:

1 EC TO RUN LIGHTING CONTROL WIRE(S) TO CEILING SYSTEM JUNCTION BOX (BY CLEANSUITE).
2 EC TO SPLICE 277-VOLT LIGHTING CIRCUITS IN CEILING SYSTEM JUNCTION BOX (BY CLEANSUITE).
3 SURGICAL LIGHTHEAD WALL CONTROLLER.
4 MICROPANEL LOCATED ABOVE ACCESSIBLE CEILING. LABEL CEILING TILE TO INDICATE MICROPANEL ABOVE.
5 O.R. TABLE LIGHTING AND JUNCTION BOXES SHALL BE PROVIDED IN CONJUNCTION WITH MECHANICAL DIFFUSERS AS A SINGLE COMBINED UNIT (BY OTHERS). EC SHALL WIRE POWER AND LOW VOLTAGE CONTROL WIRING TO PRE-WIRED COMBINED CEILING BOX. CONFIRM ALL REQUIREMENTS WITH MANUFACTURER. IN ADDITION, EC SHALL PROVIDE AND INSTALL JUMPER CONNECTIONS BETWEEN THE (4) FOUR MODULAR PIECES OF THE COMBINED CEILING UNIT FOR POWER AND LOW VOLTAGE CONTROL WIRING. LIGHT FIELD SHALL BE WIRED AND CONTROLLED AS SHOWN ON DRAWINGS. TWO SEPARATE LIGHTING CIRCUITS SHALL BE PROVIDED FOR EACH ASSEMBLY (FIELD PERIMETER LIGHTS AND FIELD INTERIOR LIGHTS). EACH CIRCUIT SHALL BE MAPPED TO A UNIQUE RELAY.

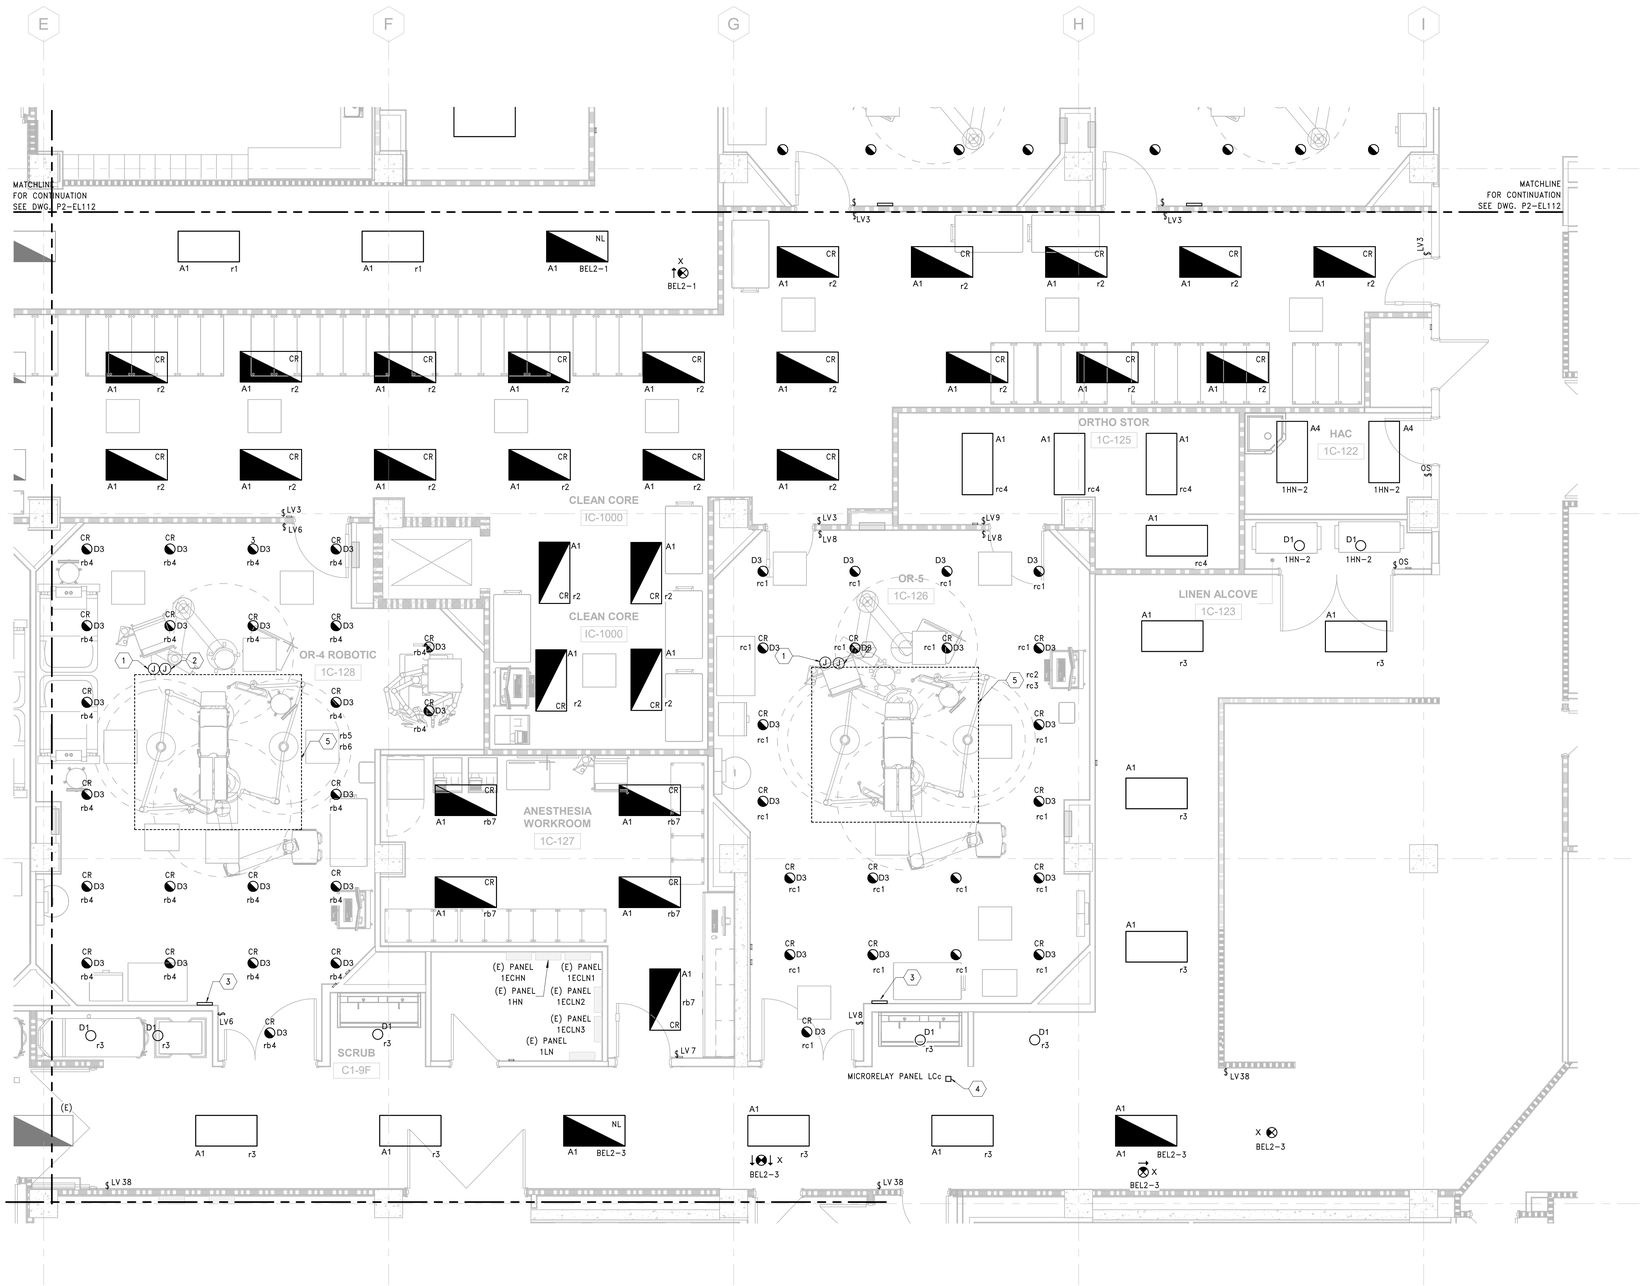

1 LIGHTING PLAN - 1ST FLOOR, PHASE 2 (SOUTH)

SCALE: 1/4" = 1'-0"

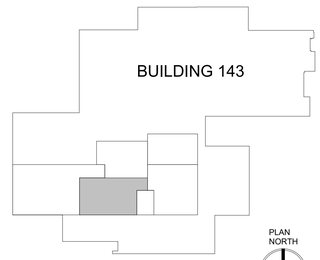

KEYPLAN

PRINTS OF THIS DRAWING SHALL NOT BE USED FOR ANY PURPOSE WHATSOEVER WITHOUT THE SEAL AND SIGNATURE OF THE PROFESSIONAL ENGINEER

Revisions: | Date:

CONSULTANT

Architecture:	Civil Engineering:	Fire Protection:
PF&A DESIGN, P.C.	LABELLA ASSOCIATES	STANTON ENGINEERING SERVICES, LLC

ENGINEER OF RECORD

MILLER+REMICK
A Service-Disabled Veteran-Owned Small Business
(856) 429-6000 • Miller-Remick.com
M-R PROJECT NO. 0609-008

MILLER-REMICK LLC PROFESSIONAL ENGINEER

COMMONWEALTH OF PENNSYLVANIA REGISTERED PROFESSIONAL THOMAS REGINO ENGINEER No. PE094185
12/30/25

Office of Construction and Facilities Management

VA U.S. Department of Veterans Affairs

Drawing Title: ELECTRICAL LIGHTING PLAN 1ST FLOOR, PHASE 2 (SOUTH)	Phase: BID DOCUMENTS	Project Title: RENOVATE SURGICAL SUITE PHASE II	VA Drawing Number: 2617
Approved by: Jon Manninen, COR	FULLY SPRINKLERED	Project Number: 658-19-103	Building Number: 143
		Location: SALEM VA MEDICAL CENTER	Drawing Number: P2-EL111
		Issue Date: 2025-12-30 / Checked: MJR / Drawn: PDK	

12/29/2025 5:32:14 PM

VA FORM 08 - 6231

GENERAL SHEET NOTES:

1. SEE DRAWING E-001 FOR ELECTRICAL SYMBOLS AND ABBREVIATIONS AND DRAWING E-002 FOR ELECTRICAL NOTES.
2. ALL ELECTRICAL DEVICES ON THIS SHEET SHALL BE NEW, UNLESS OTHERWISE NOTED.
3. SEE DRAWING E-704 AND E-705 FOR LIGHTING FIXTURE SCHEDULE, CIRCUITRY AND LIGHTING CONTROL INFORMATION. SEE DRAWING E-701 AND E-702 FOR PANEL SCHEDULES.
4. EXIT SIGNS SHALL BE CIRCUITED AHEAD OF ALL CONTROL DEVICES.

SHEET KEYNOTES:

1 SURGICAL LIGHTHEAD WALL CONTROLLER.
2 MICROPANEL LOCATED ABOVE ACCESSIBLE CEILING. LABEL CEILING TILE TO INDICATE MICROPANEL ABOVE.
3 EC TO RUN LIGHTING CONTROL WIRE(S) TO CEILING SYSTEM JUNCTION BOX (BY CLEANSUITE).
4 EC TO SPLICE 277-VOLT LIGHTING CIRCUITS IN CEILING SYSTEM JUNCTION BOX (BY CLEANSUITE).
5 O.R. TABLE LIGHTING AND JUNCTION BOXES SHALL BE PROVIDED IN CONJUNCTION WITH MECHANICAL DIFFUSERS AS A SINGLE COMBINED UNIT (BY OTHERS). EC SHALL WIRE POWER AND LOW VOLTAGE CONTROL WIRING TO PRE-WIRED COMBINED CEILING BOX. CONFIRM ALL REQUIREMENTS WITH MANUFACTURER. IN ADDITION, EC SHALL PROVIDE AND INSTALL JUMPER CONNECTIONS BETWEEN THE (4) FOUR MODULAR PIECES OF THE COMBINED CEILING UNIT FOR POWER AND LOW VOLTAGE CONTROL WIRING. LIGHT FIELD SHALL BE WIRED AND CONTROLLED AS SHOWN ON DRAWINGS. TWO SEPARATE LIGHTING CIRCUITS SHALL BE PROVIDED FOR EACH ASSEMBLY (FIELD PERIMETER LIGHTS AND FIELD INTERIOR LIGHTS). EACH CIRCUIT SHALL BE MAPPED TO A UNIQUE RELAY.

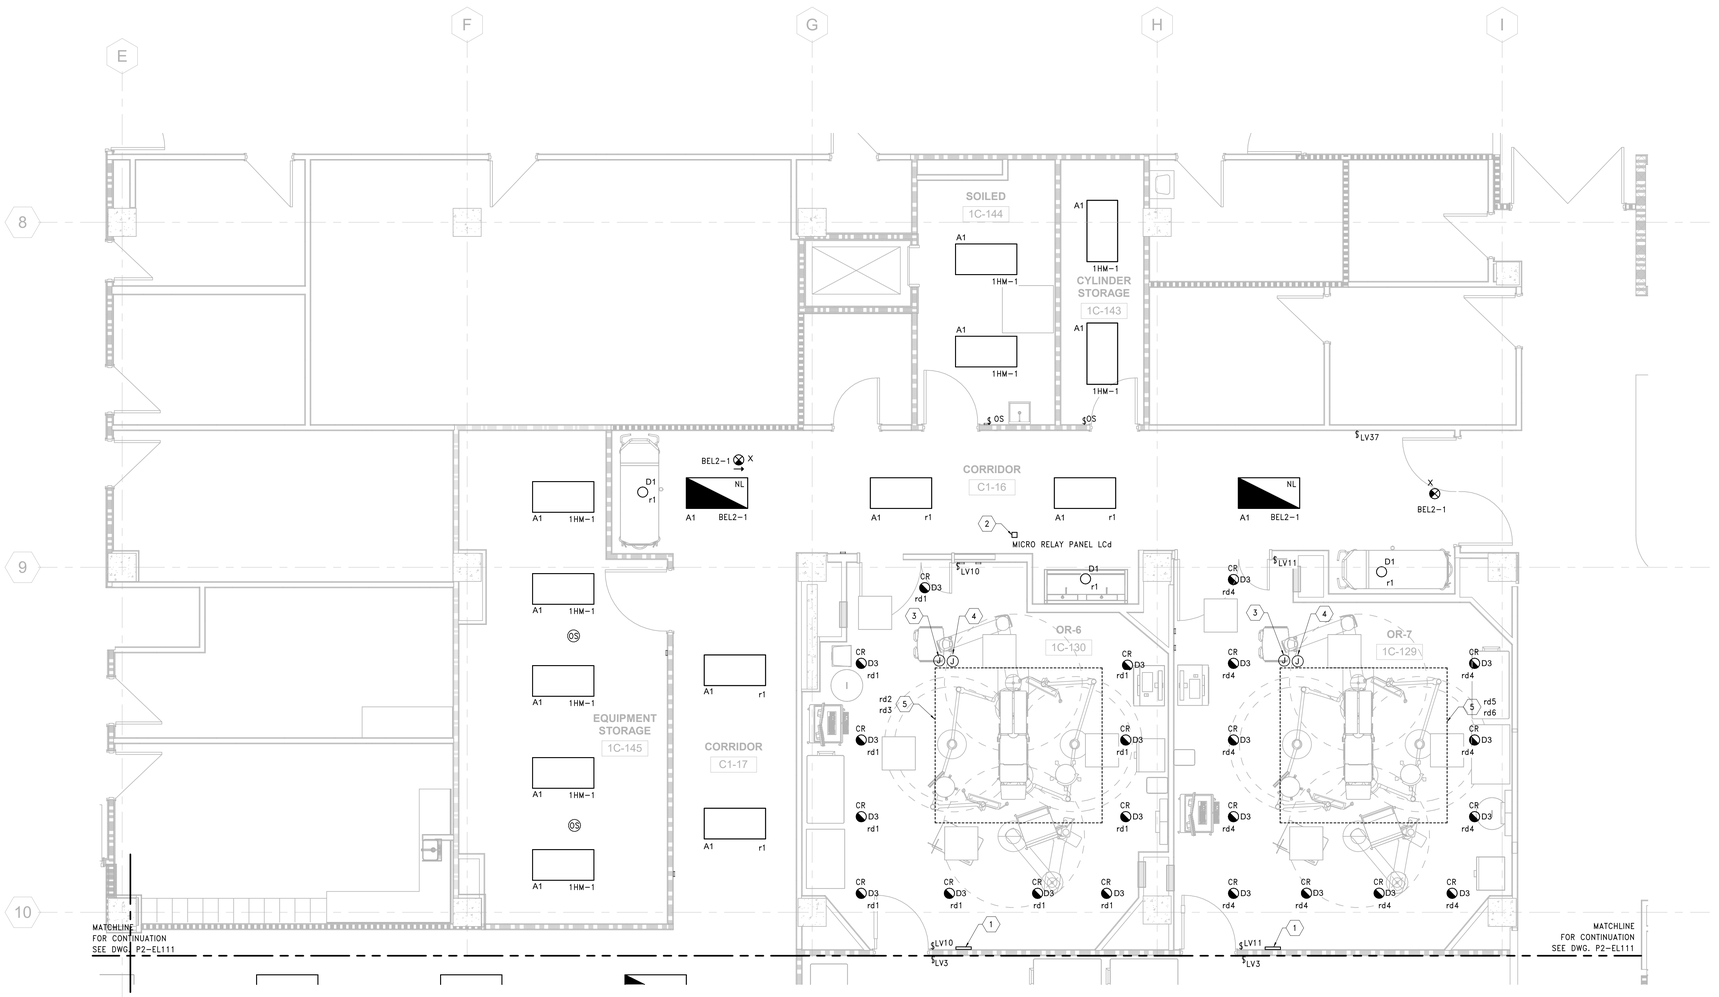

1 LIGHTING PLAN - 1ST FLOOR, PHASE 2 (NORTH)

SCALE: 1/4" = 1'-0"

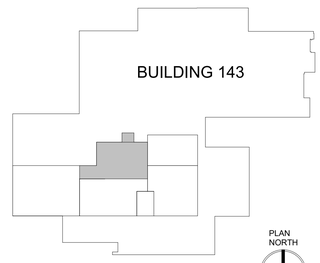

KEYPLAN

PRINTS OF THIS DRAWING SHALL NOT BE USED FOR ANY PURPOSE WHATSOEVER WITHOUT THE SEAL AND SIGNATURE OF THE PROFESSIONAL ENGINEER

Revisions: | Date:

CONSULTANT

Architecture:	Civil Engineering:	Fire Protection:
PF&A DESIGN, P.C.	LABELLA ASSOCIATES	STANTON ENGINEERING SERVICES, LLC

ENGINEER OF RECORD

MILLER-REMICK
A Service-Disabled Veteran-Owned Small Business
(856) 429-6000 • Miller-Remick.com
M-R PROJECT NO. 0409-036

MILLER-REMICK LLC
PROFESSIONAL ENGINEER
COMMONWEALTH OF PENNSYLVANIA REGISTERED PROFESSIONAL THOMAS REGINO ENGINEER PENNSYLVANIA
12/30/25

Office of Construction and Facilities Management

U.S. Department of Veterans Affairs

Drawing Title: ELECTRICAL LIGHTING PLAN 1ST FLOOR, PHASE 2 (NORTH)	Phase: BID DOCUMENTS	Project Title: RENOVATE SURGICAL SUITE PHASE II	VA Drawing Number: 2617
Approved by: Jon Manninen, COR	FULLY SPRINKLERED	Project Number: 658-19-103	Building Number: 143
		Location: SALEM VA MEDICAL CENTER	Drawing Number: P2-EL112
		Issue Date: 2025-12-30 / Checked: MJR / Drawn: PDK	

12/29/2025 5:32:15 PM

VA FORM 08 - 6231

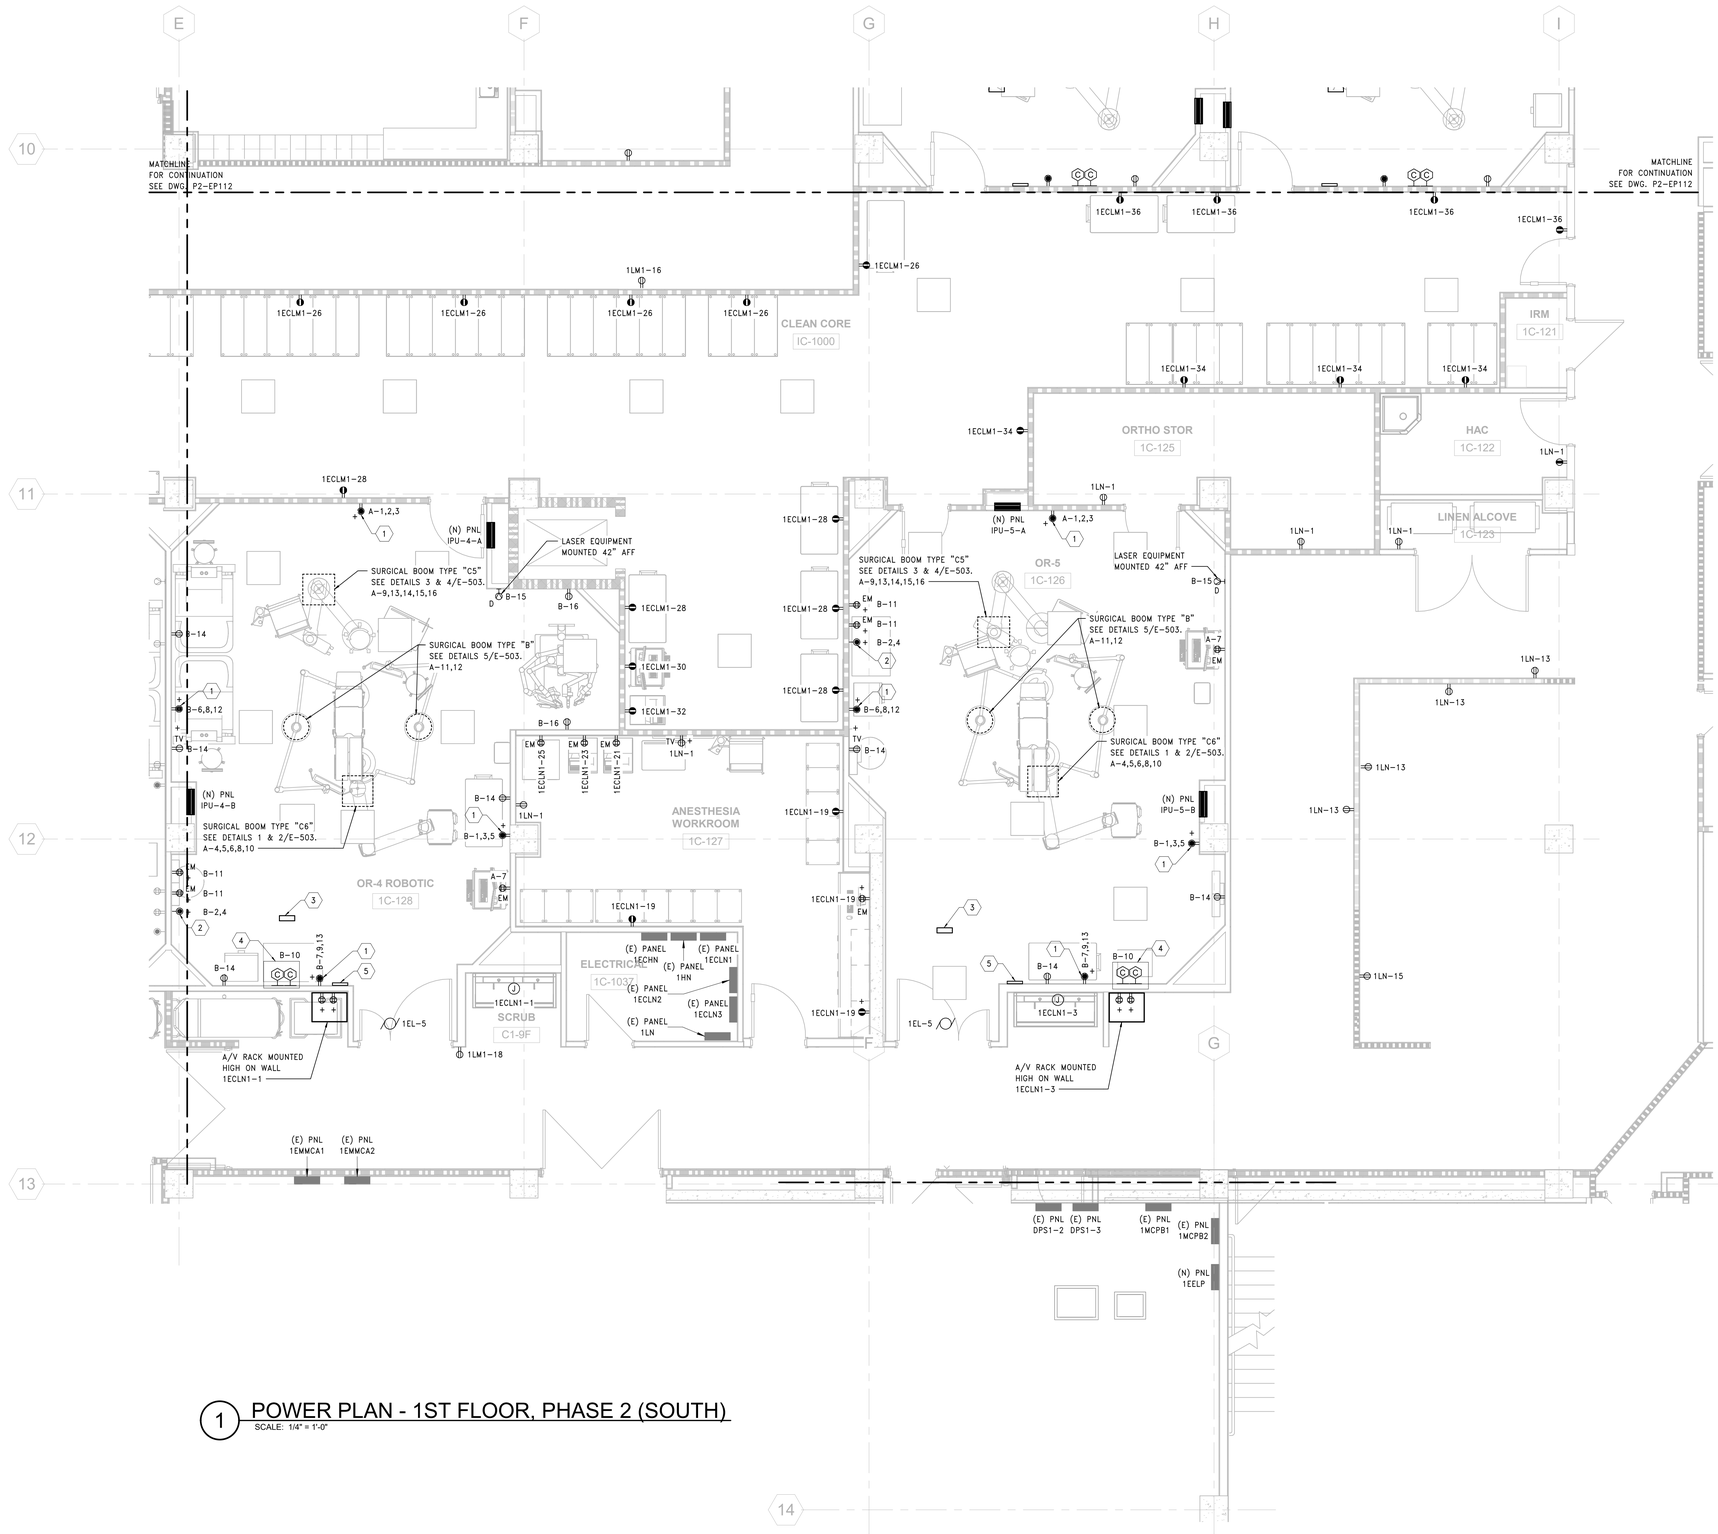

GENERAL SHEET NOTES:

1. SEE DRAWING E-001 FOR ELECTRICAL SYMBOLS AND ABBREVIATIONS AND DRAWING E-002 FOR ELECTRICAL NOTES.
2. SEE DRAWING E-602 FOR SINGLE LINE DIAGRAM.
3. SEE DRAWING E-701 AND E-702 FOR PANEL SCHEDULES AND E-703 FOR ISOLATION PANEL SCHEDULES.
4. ALL ELECTRICAL DEVICES ON THIS SHEET SHALL BE NEW, UNLESS OTHERWISE NOTED.
5. UNLESS OTHERWISE NOTED ALL CIRCUITS WITHIN AN OR SHALL BE FED FROM THE A OR B IPU PANELS LOCATED WITHIN THAT OR.

SHEET KEYNOTES:

1. POWER GROUND MODULE. REFER TO DETAIL 7A/E-502 FOR BACK BOX CONFIGURATION AND MOUNTING HEIGHT.
2. POWER GROUND MODULE. REFER TO DETAIL 7B/E-502 FOR BACK BOX CONFIGURATION AND MOUNTING HEIGHT.
3. GROUND REFERENCE POINT. REFER TO DETAIL 2/E-502.
4. DIGITAL TIME CLOCK AND ELAPSED TIMER. DISPLAY REMOTELY CONTROLLED BY USER WITH 2-GANG BACKBOX AND BATTERY PACK.
5. SURGICAL BOOM LIGHT HEAD CONTROLLER UNIT. REFER TO DETAIL 5/E-503 FOR WIRING AND CONNECTIONS. CONTRACTOR SHALL COORDINATE WITH EQUIPMENT MANUFACTURER INSTALLATION GUIDELINES FOR WALL CONTROLLER.

1 POWER PLAN - 1ST FLOOR, PHASE 2 (SOUTH)

SCALE: 1/4" = 1'-0"

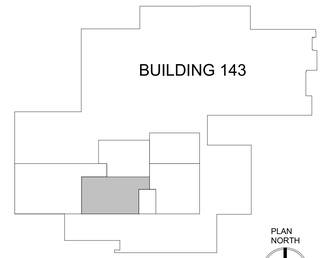

KEYPLAN

PRINTS OF THIS DRAWING SHALL NOT BE USED FOR ANY PURPOSE WHATSOEVER WITHOUT THE SEAL AND SIGNATURE OF THE PROFESSIONAL ENGINEER

Revisions:	Date:

02/26/2025 5:32:17 PM

CONSULTANT

Architecture:	Civil Engineering:	Fire Protection:
PF&A DESIGN, P.C.	LABELLA ASSOCIATES	STANTON ENGINEERING SERVICES, LLC

ENGINEER OF RECORD

MILLER-REMICK
A Service-Disabled Veteran-Owned Small Business
(856) 429-4000 ★ Miller-Remick.com

MILLER-REMICK LLC PROFESSIONAL ENGINEER

COMMONWEALTH OF PENNSYLVANIA REGISTERED PROFESSIONAL THOMAS REGINO ENGINEER IN PERMITS 12/30/25

Office of Construction and Facilities Management

VA U.S. Department of Veterans Affairs

Drawing Title ELECTRICAL POWER PLAN 1ST FLOOR, PHASE 2 (SOUTH)	**Phase** BID DOCUMENTS	**Project Title** RENOVATE SURGICAL SUITE PHASE II	**VA Drawing Number** 2617
Approved by: Jon Manninen, COR	FULLY SPRINKLERED	**Project Number** 658-19-103	**Building Number** 143
		Location SALEM VA MEDICAL CENTER	**Drawing Number** P2-EP111
		Issue Date 2025-12-30 / **Checked** MJR / **Drawn** PDK	

VA FORM 08 - 6231

GENERAL SHEET NOTES:

1. SEE DRAWING E-001 FOR ELECTRICAL SYMBOLS AND ABBREVIATIONS AND DRAWING E-002 FOR ELECTRICAL NOTES.
2. SEE DRAWING E-602 FOR SINGLE LINE DIAGRAM.
3. SEE DRAWING E-701 AND E-702 FOR PANEL SCHEDULES AND E-703 FOR ISOLATION PANEL SCHEDULES.
4. ALL ELECTRICAL DEVICES ON THIS SHEET SHALL BE NEW, UNLESS OTHERWISE NOTED.
5. UNLESS OTHERWISE NOTED ALL CIRCUITS WITHIN AN OR SHALL BE FED FROM THE A OR B IPU PANELS LOCATED WITHIN THAT OR.

SHEET KEYNOTES:

1 POWER GROUND MODULE. REFER TO DETAIL 7A/E-502 FOR BACK BOX CONFIGURATION AND MOUNTING HEIGHT.
2 POWER GROUND MODULE. REFER TO DETAIL 7B/E-502 FOR BACK BOX CONFIGURATION AND MOUNTING HEIGHT.
3 SURGICAL BOOM LIGHT HEAD CONTROLLER UNIT. REFER TO DETAIL 5/E-503 FOR WIRING AND CONNECTIONS. CONTRACTOR SHALL COORDINATE WITH EQUIPMENT MANUFACTURER INSTALLATION GUIDELINES FOR WALL CONTROLLER.
4 DIGITAL TIME CLOCK AND ELAPSED TIMER. DISPLAY REMOTELY CONTROLLED BY USER WITH 2-GANG BACKBOX AND BATTERY PACK.
5 GROUND REFERENCE POINT. REFER TO DETAIL 2/E-502.

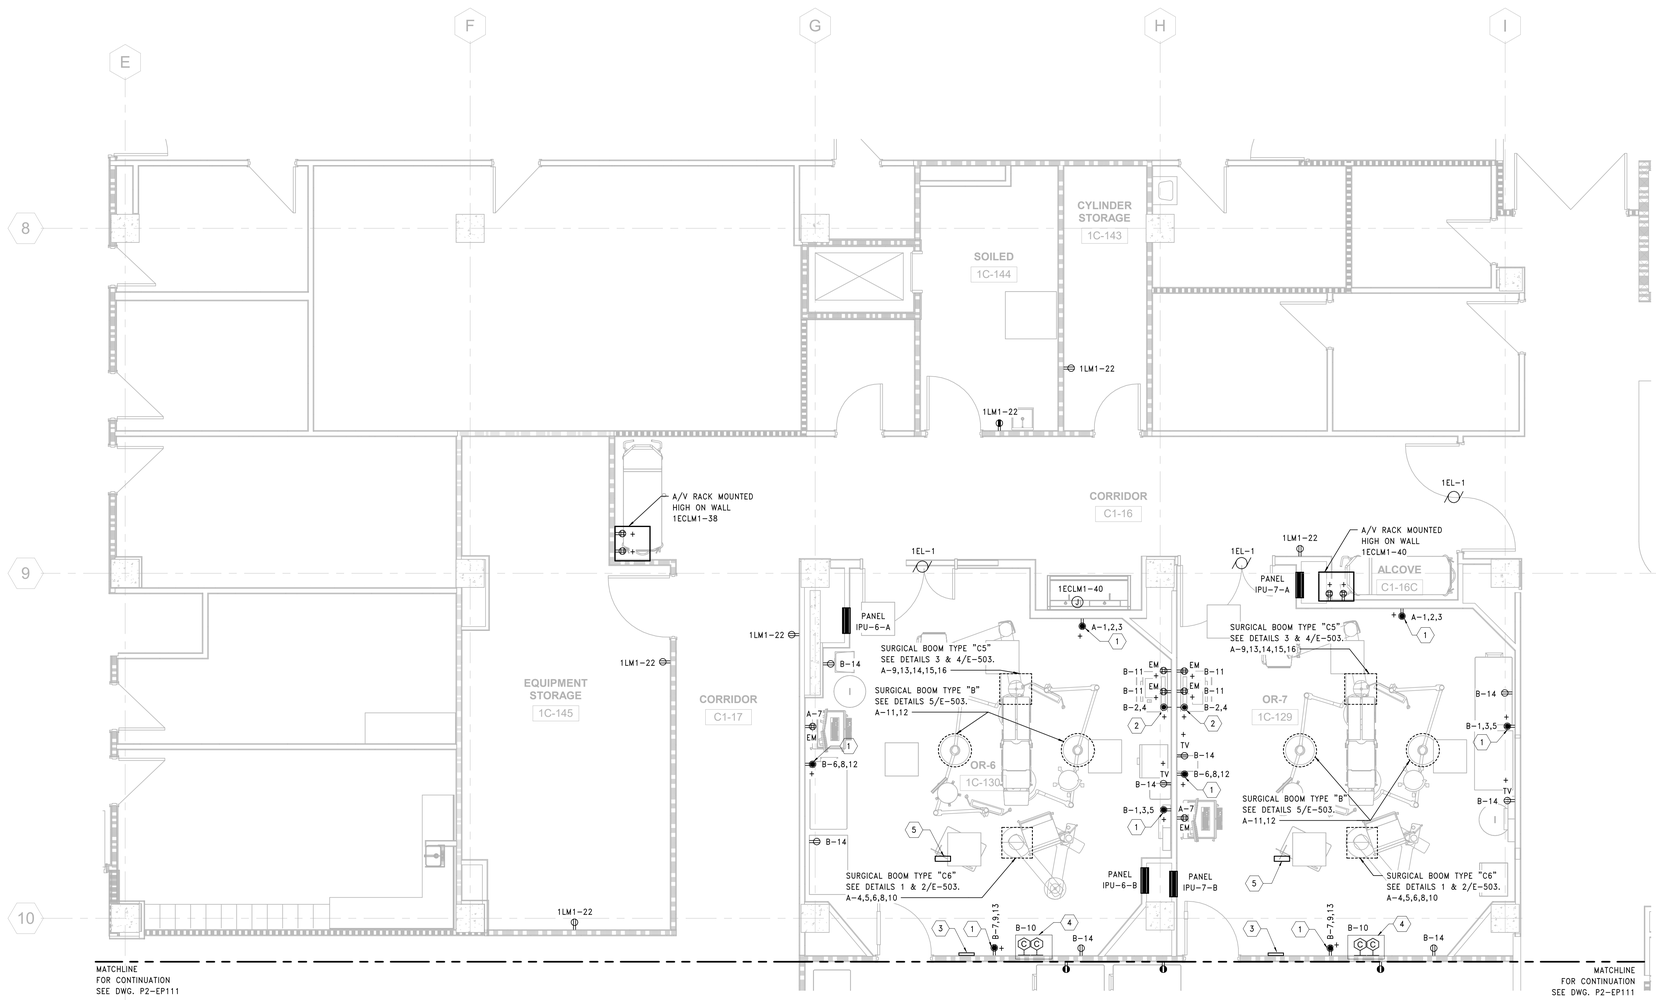

1 POWER PLAN - 1ST FLOOR, PHASE 2 (NORTH)

SCALE: 1/4" = 1'-0"

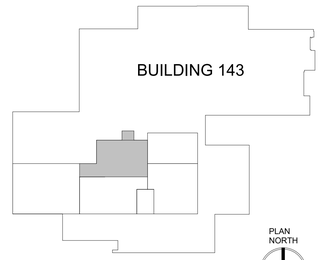

KEYPLAN

PRINTS OF THIS DRAWING SHALL NOT BE USED FOR ANY PURPOSE WHATSOEVER WITHOUT THE SEAL AND SIGNATURE OF THE PROFESSIONAL ENGINEER

Revisions:	Date:

CONSULTANT

Architecture:	Civil Engineering:	Fire Protection:
PF&A DESIGN, P.C.	LABELLA ASSOCIATES	STANTON ENGINEERING SERVICES, LLC

ENGINEER OF RECORD

MILLER-REMICK
A Service-Disabled Veteran-Owned Small Business
(856) 429-4000 • Miller-Remick.com
VA VERIFICATION # VOSB-000125038

MILLER-REMICK LLC PROFESSIONAL ENGINEER

COMMONWEALTH OF PENNSYLVANIA REGISTERED PROFESSIONAL ENGINEER THOMAS REGINO ENGINEER In MEMORIS 12/30/25

Office of Construction and Facilities Management

U.S. Department of Veterans Affairs

Drawing Title	ELECTRICAL POWER PLAN 1ST FLOOR, PHASE 2 (NORTH)
Approved by:	Jon Manninen, COR
Phase	BID DOCUMENTS
	FULLY SPRINKLERED
Project Title	RENOVATE SURGICAL SUITE PHASE II
Project Number	658-19-103
Location	SALEM VA MEDICAL CENTER
Issue Date	2025-12-30
Checked	MJR
Drawn	PDK
VA Drawing Number	2617
Building Number	143
Drawing Number	P2-EP112

12/29/2025 5:32:17 PM

VA FORM 08 - 6231

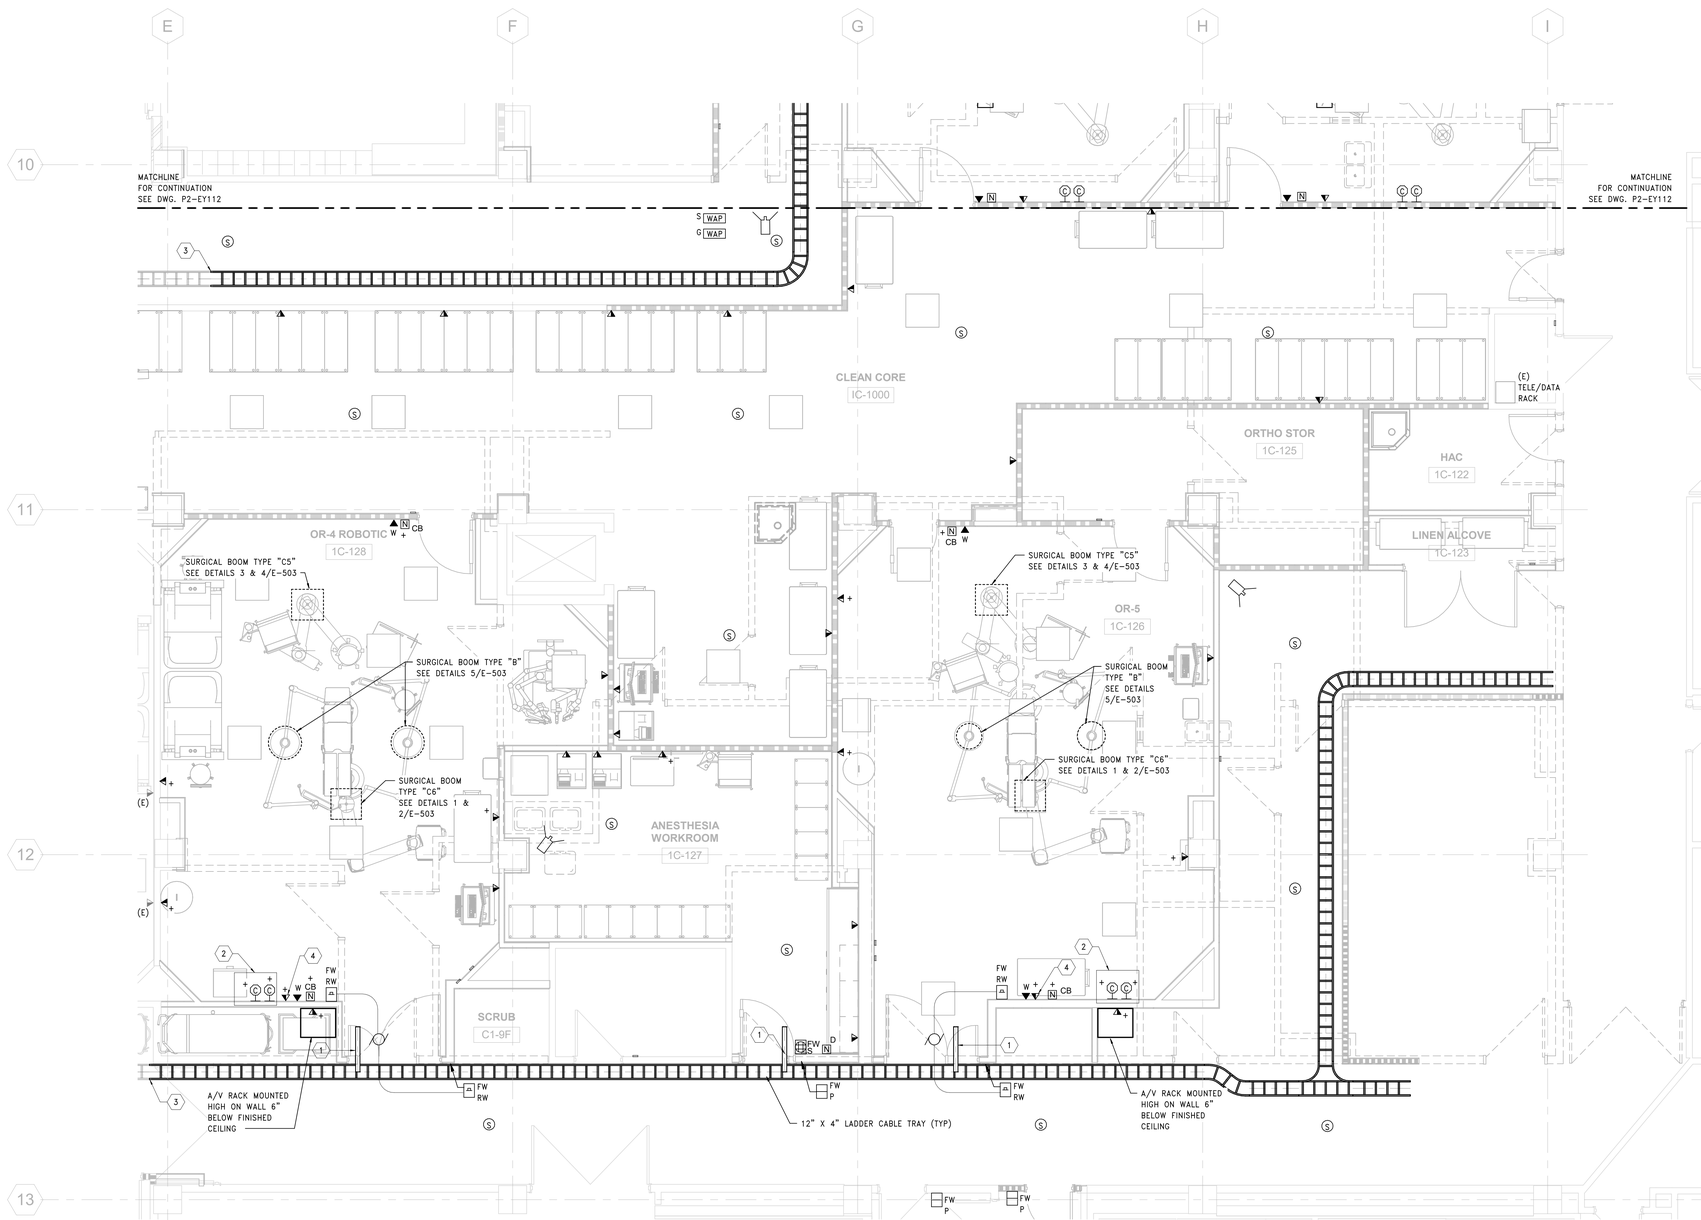

1 SYSTEMS PLAN - 1ST FLOOR, PHASE 2 (SOUTH)

SCALE: 1/4" = 1'-0"

GENERAL SHEET NOTES:

1. SEE DRAWING E-001 FOR ELECTRICAL SYMBOLS AND ABBREVIATIONS AND DRAWING E-002 FOR ELECTRICAL NOTES.
2. SEE DRAWING E-603 FOR TELE/DATA DEVICE DETAILS, CABLE TRAY DETAILS, AND TELE/DATA RISER DIAGRAM.
3. ALL TELE/DATA DEVICES ON THIS SHEET SHALL BE NEW, UNLESS OTHERWISE NOTED.
4. ALL TELE/DATA WIRING FOR DEVICES ON THIS DRAWING SHALL BE PULLED BACK TO NEW TELE/DATA RACK IN IT ID-1002.
5. EC SHALL REINSTALL AND PULL NEW CAT6 WIRING TO ALL CEILING MOUNTED CENTRAK DEVICES IN THIS AREA. E.C. SHALL ALSO PROVIDE NEW CENTRAK DEVICES TO MATCH EXISTING DEVICES AS REQUIRED TO MEET THE NEEDS OF THE PROGRAM FOR THIS PROJECT. E.C. SHALL COORDINATE WITH VA AND THEIR CENTRAK REPRESENTATIVE IN REGARDS TO THE QUANTITY AND PLACEMENT REQUIREMENTS OF ALL RELOCATED AND NEW DEVICES, AS WELL AS THE WIRING REQUIREMENTS.
6. SEE NOTES 58 AND 59 ON DRAWING E-002 FOR FURTHER INFORMATION ON WIRELESS ACCESS POINT REQUIREMENTS.
7. ALL SECURITY CAMERAS SHOWN SHALL BE WIRED BACK TO EXISTING SECURITY HEADEND IN ROOM BC-114 WITH MANUFACTURER RECOMMENDED POE CABLE.

SHEET KEYNOTES:

1 PROVIDE (1) ONE – 3" CONDUIT ABOVE ACCESSIBLE CEILING AS A PASS-THRU FOR TELECOMMUNICATION CABLING. CONDUIT SHALL BE PROVIDED WITH BUSHED ENDS AND PULL STRING. SEAL PENETRATION AS REQUIRED.

2 DIGITAL TIME CLOCK AND ELAPSED TIMER. DISPLAY REMOTELY CONTROLLED BY USER WITH 2-GANG BACKBOX AND BATTERY PACK.

3 PROVIDE ALL NECESSARY COMPONENTS NEEDED FOR A CONTINUOUS RUN FROM A PREVIOUSLY INSTALLED CABLE TRAY AT AN EARLIER PHASE.

4 TELECOMMUNICATION DROP FOR SURGICAL BOOM LIGHT HEAD CONTROLLER. REFER TO DETAIL 5/E-503 FOR FURTHER INFORMATION.

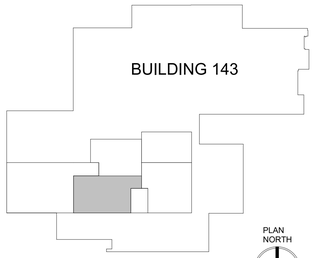

KEYPLAN

PRINTS OF THIS DRAWING SHALL NOT BE USED FOR ANY PURPOSE WHATSOEVER WITHOUT THE SEAL AND SIGNATURE OF THE PROFESSIONAL ENGINEER

Revisions: | Date:

12/29/2025 5:32:18 PM

CONSULTANT

Architecture:	Civil Engineering:	Fire Protection:
PF&A DESIGN, P.C.	LABELLA ASSOCIATES	STANTON ENGINEERING SERVICES, LLC

ENGINEER OF RECORD

MILLER•REMICK
A Service-Disabled Veteran-Owned Small Business
(856) 429-4000 • Miller-Remick.com

MILLER-REMICK LLC
PROFESSIONAL ENGINEER

COMMONWEALTH OF PENNSYLVANIA — REGISTERED PROFESSIONAL — THOMAS REGINO — ENGINEER No. PE094195
12/30/25

Office of Construction and Facilities Management

VA U.S. Department of Veterans Affairs

Drawing Title: ELECTRICAL SYSTEMS PLAN 1ST FLOOR, PHASE 2 (SOUTH)	Phase: BID DOCUMENTS	Project Title: RENOVATE SURGICAL SUITE PHASE II	VA Drawing Number: 2617
Approved by: Jon Manninen, COR	FULLY SPRINKLERED	Project Number: 658-19-103	Building Number: 143
		Location: SALEM VA MEDICAL CENTER	Drawing Number: P2-EY111
		Issue Date: 2025-12-30 / Checked: MJR / Drawn: PDK	

VA FORM 08 - 6231

GENERAL SHEET NOTES:

1. SEE DRAWING E-001 FOR ELECTRICAL SYMBOLS AND ABBREVIATIONS AND DRAWING E-002 FOR ELECTRICAL NOTES.
2. SEE DRAWING E-603 FOR TELE/DATA DEVICE DETAILS, CABLE TRAY DETAILS, AND TELE/DATA RISER DIAGRAM.
3. ALL TELE/DATA DEVICES ON THIS SHEET SHALL BE NEW, UNLESS OTHERWISE NOTED.
4. ALL TELE/DATA WIRING FOR DEVICES ON THIS DRAWING SHALL BE PULLED BACK TO NEW TELE/DATA RACK IN IT ID-1002.
5. EC SHALL REINSTALL AND PULL NEW CAT6 WIRING TO ALL CEILING MOUNTED CENTRAK DEVICES IN THIS AREA. E.C. SHALL ALSO PROVIDE NEW CENTRAK DEVICES TO MATCH EXISTING DEVICES AS REQUIRED TO MEET THE NEEDS OF THE PROGRAM FOR THIS PROJECT. E.C. SHALL COORDINATE WITH VA AND THEIR CENTRAK REPRESENTATIVE IN REGARDS TO THE QUANTITY AND PLACEMENT REQUIREMENTS OF ALL RELOCATED AND NEW DEVICES, AS WELL AS THE WIRING REQUIREMENTS.
6. SEE NOTES 58 AND 59 ON DRAWING E-002 FOR FURTHER INFORMATION ON WIRELESS ACCESS POINT REQUIREMENTS.
7. ALL SECURITY CAMERAS SHOWN SHALL BE WIRED BACK TO EXISTING SECURITY HEADEND IN ROOM BC-114 WITH MANUFACTURER RECOMMENDED POE CABLE.

SHEET KEYNOTES:

1 PROVIDE (1) ONE – 3" CONDUIT ABOVE ACCESSIBLE CEILING AS A PASS-THRU FOR TELECOMMUNICATION CABLING. CONDUIT SHALL BE PROVIDED WITH BUSHED ENDS AND PULL STRING. SEAL PENETRATION AS REQUIRED.

2 TELECOMMUNICATION DROP FOR SURGICAL BOOM LIGHT HEAD CONTROLLER. REFER TO DETAIL 5/E-503 FOR FURTHER INFORMATION.

3 DIGITAL TIME CLOCK AND ELAPSED TIMER. DISPLAY REMOTELY CONTROLLED BY USER WITH 2-GANG BACKBOX AND BATTERY PACK.

4 PROVIDE (2) TWO – 4" CONDUITS ABOVE ACCESSIBLE CEILING AS A PASS-THRU FOR TELECOMMUNICATION CABLING. CONDUIT SHALL BE PROVIDED WITH BUSHED ENDS AND PULL STRING. SEAL PENETRATION AS REQUIRED.

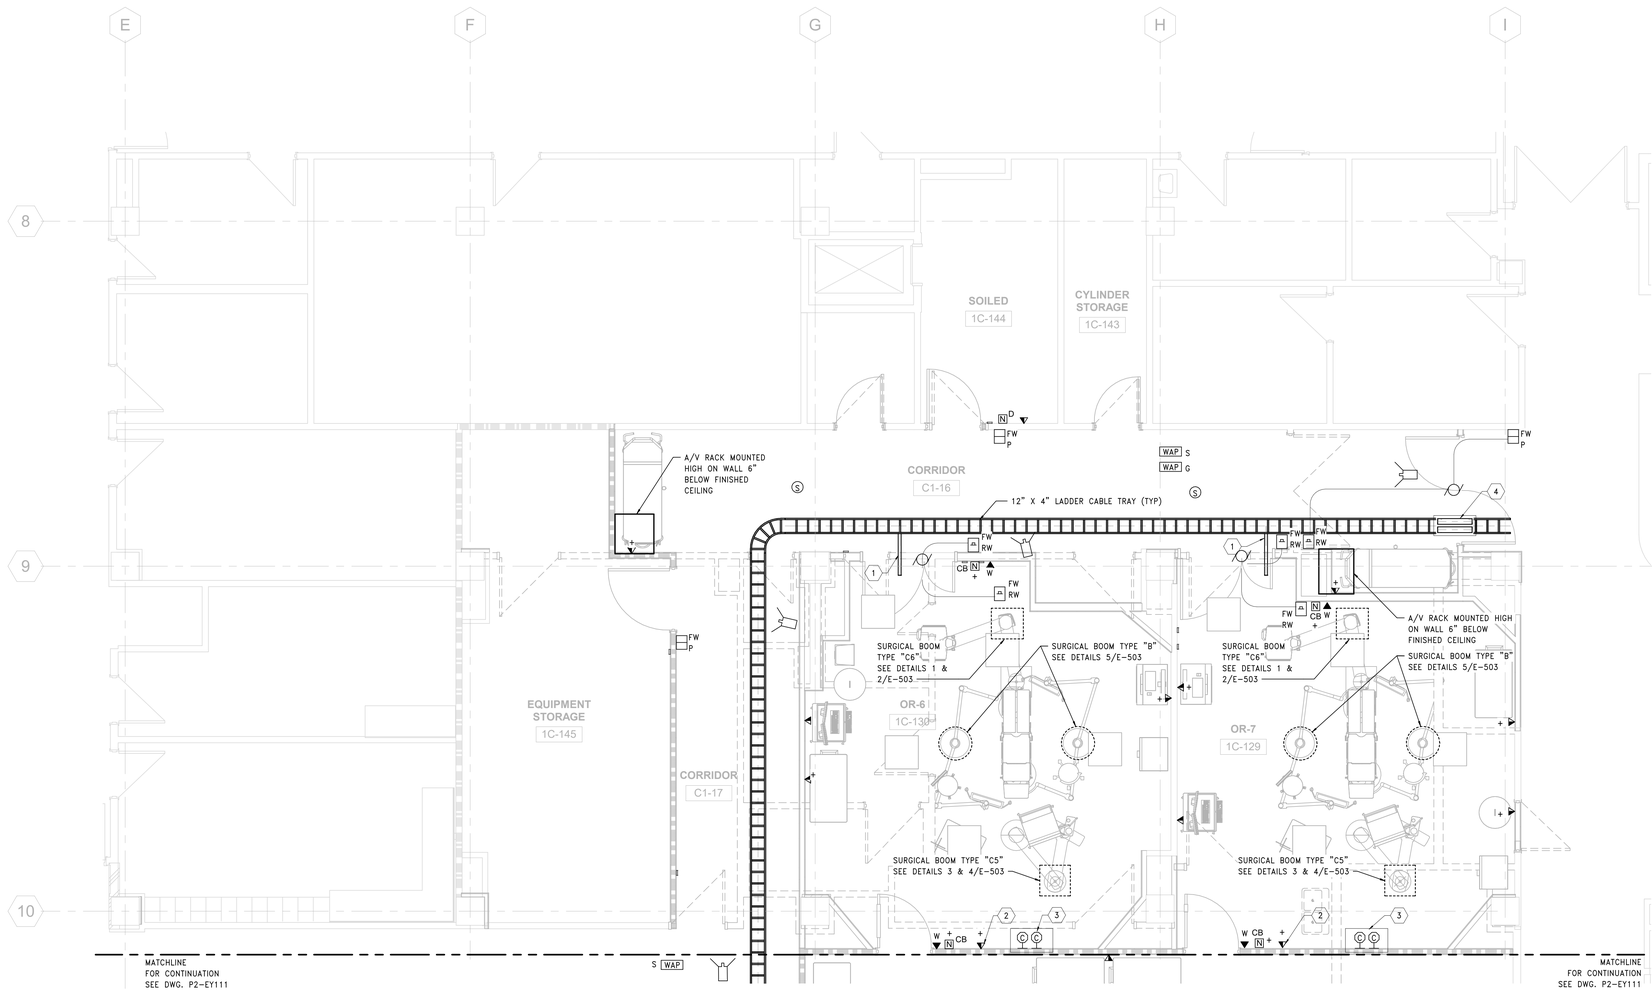

1 SYSTEMS PLAN - 1ST FLOOR, PHASE 2 (NORTH)

SCALE: 1/4" = 1'-0"

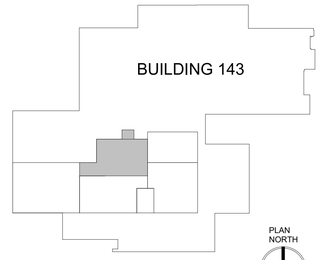

KEYPLAN

PRINTS OF THIS DRAWING SHALL NOT BE USED FOR ANY PURPOSE WHATSOEVER WITHOUT THE SEAL AND SIGNATURE OF THE PROFESSIONAL ENGINEER

Revisions:	Date:

CONSULTANT

Architecture:	Civil Engineering:	Fire Protection:
PF&A DESIGN, P.C.	LABELLA ASSOCIATES	STANTON ENGINEERING SERVICES, LLC

ENGINEER OF RECORD

MILLER•REMICK
A Service-Disabled Veteran-Owned Small Business
(856) 429-4000 • Miller-Remick.com

MILLER-REMICK LLC PROFESSIONAL ENGINEER

COMMONWEALTH OF PENNSYLVANIA — REGISTERED PROFESSIONAL — THOMAS REGINO — ENGINEER No. PE094195
12/30/25

Office of Construction and Facilities Management

VA U.S. Department of Veterans Affairs

Drawing Title	ELECTRICAL SYSTEMS PLAN 1ST FLOOR, PHASE 2 (NORTH)
Approved by:	Jon Manninen, COR
Phase	BID DOCUMENTS
	FULLY SPRINKLERED
Project Title	RENOVATE SURGICAL SUITE PHASE II
Project Number	658-19-103
Location	SALEM VA MEDICAL CENTER
Issue Date	2025-12-30
Checked	MJR
Drawn	PDK
VA Drawing Number	2617
Building Number	143
Drawing Number	P2-EY112

12/29/2025 5:32:19 PM

VA FORM 08 - 6231

GENERAL SHEET NOTES:

1. SEE DRAWINGS E-001 AND E-002 FOR ABBREVIATIONS, SYMBOLS AND NOTES.

SHEET KEYNOTES:

1. DEMOLISH ALL ELECTRICAL DEVICES INCLUDING, BUT NOT LIMITED TO, PANELBOARDS, LIGHTING, LIGHTING CONTROL, RECEPTACLES, TELE/DATA AND FIRE ALARM DEVICES, ETC. WITHIN BOUNDARY, UNLESS OTHERWISE NOTED. DEMOLISH ALL ELECTRICAL DEVICE WIRING AND RACEWAYS BACK TO SOURCE.
2. ALL WIRELESS ACCESS POINTS AND CENTRAK DEVICES WITHIN THIS BOUNDARY SHALL BE REMOVED, CLEANED, AND STORED FOR REINSTALLATION.
3. TELE/DATA DEVICES SERVED BY THIS RACK, THAT ARE TO REMAIN ACTIVE AFTER PHASE 3, SHALL BE REROUTED TO EXISTING TELE/DATA RACK IN IRM 1C-121 AS REQUIRED.

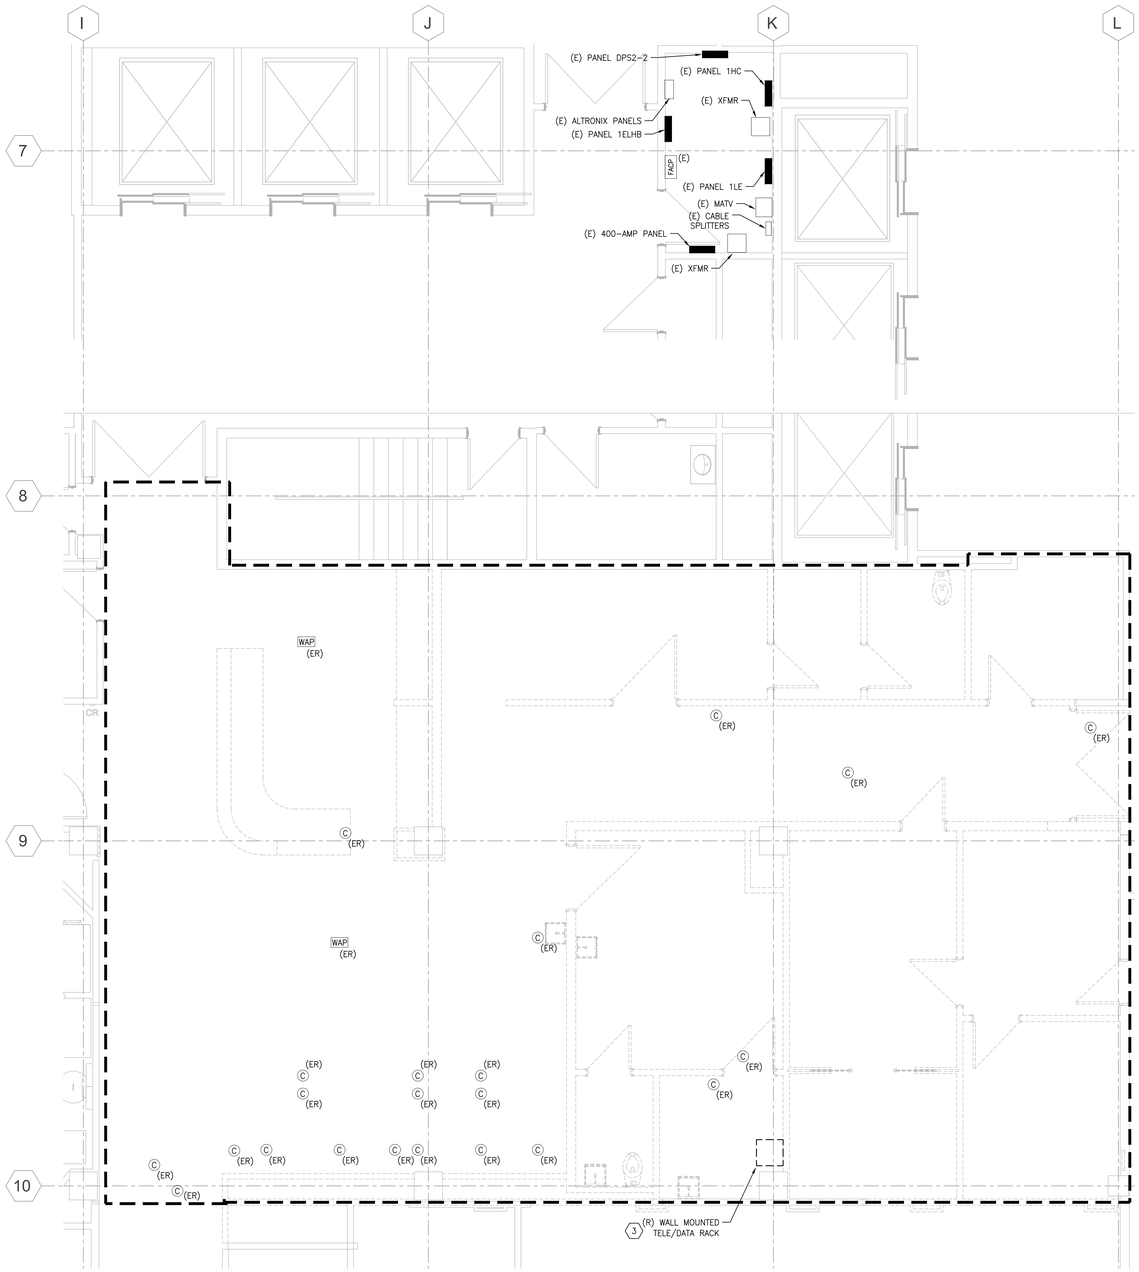

1 ELECTRICAL DEMOLITION PLAN – 1ST FLOOR, PHASE 3
SCALE: 1/4" = 1'-0"

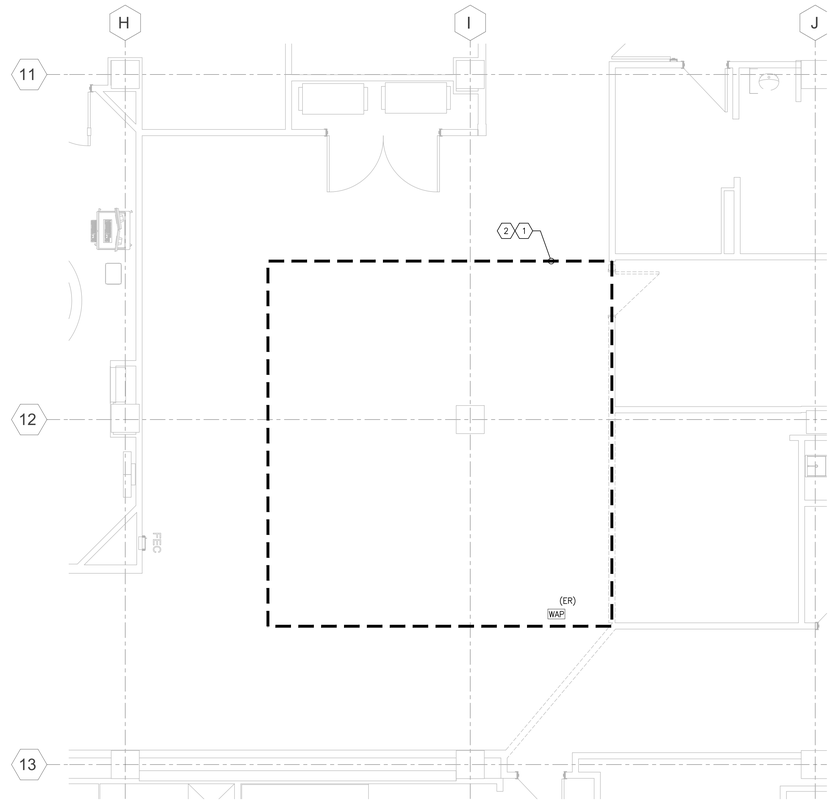

2 ELECTRICAL DEMOLITION PLAN – 1ST FLOOR, PHASE 3, SOUTH
SCALE: 1/4" = 1'-0"

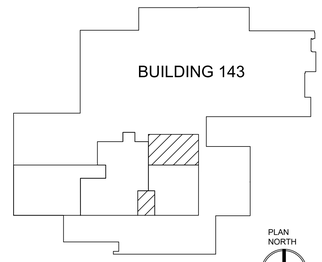

KEYPLAN

PRINTS OF THIS DRAWING SHALL NOT BE USED FOR ANY PURPOSE WHATSOEVER WITHOUT THE SEAL AND SIGNATURE OF THE PROFESSIONAL ENGINEER.

NO.	DESCRIPTION	DATE

CONSULTANTS

Architecture:	Civil Engineering:	Fire & Life Safety:
PF&A DESIGN, P.C.	LABELLA ASSOCIATES	STANTON ENGINEERING SERVICES, LLC

ENGINEER OF RECORD

MILLER-REMICK
A Service-Disabled Veteran-Owned Small Business
(856) 429-4000 ✕ Miller-Remick.com
M-R PROJECT NO. 0499-0156

MILLER-REMICK LLC
PROFESSIONAL ENGINEER
COMMONWEALTH OF PENNSYLVANIA – REGISTERED PROFESSIONAL – THOMAS REGINO – ENGINEER No. PE094195
12/30/25

Office of Construction and Facilities Management

VA U.S. Department of Veterans Affairs

Drawing Title ELECTRICAL DEMOLITION PLAN 1ST FLOOR, PHASE 3	**Phase** BID DOCUMENTS	**Project Title** RENOVATE SURGICAL SUITE PHASE II	**VA Drawing Number** 2617
Approved by: Jon Manninen, COR	FULLY SPRINKLERED	**Project Number** 658-19-103	**Building Number** 143
		Location SALEM VA MEDICAL CENTER	**Drawing Number** P3-ED111
		Issue Date 2025-12-30 / **Checked** MJR / **Drawn** DRR	

VA FORM 08-6231

C:\Users\mcifelli\AppData\Local\Temp\AcPublish_11328\P3-ED111.dwg 12-29-25 05:55:20 PM mcifelli

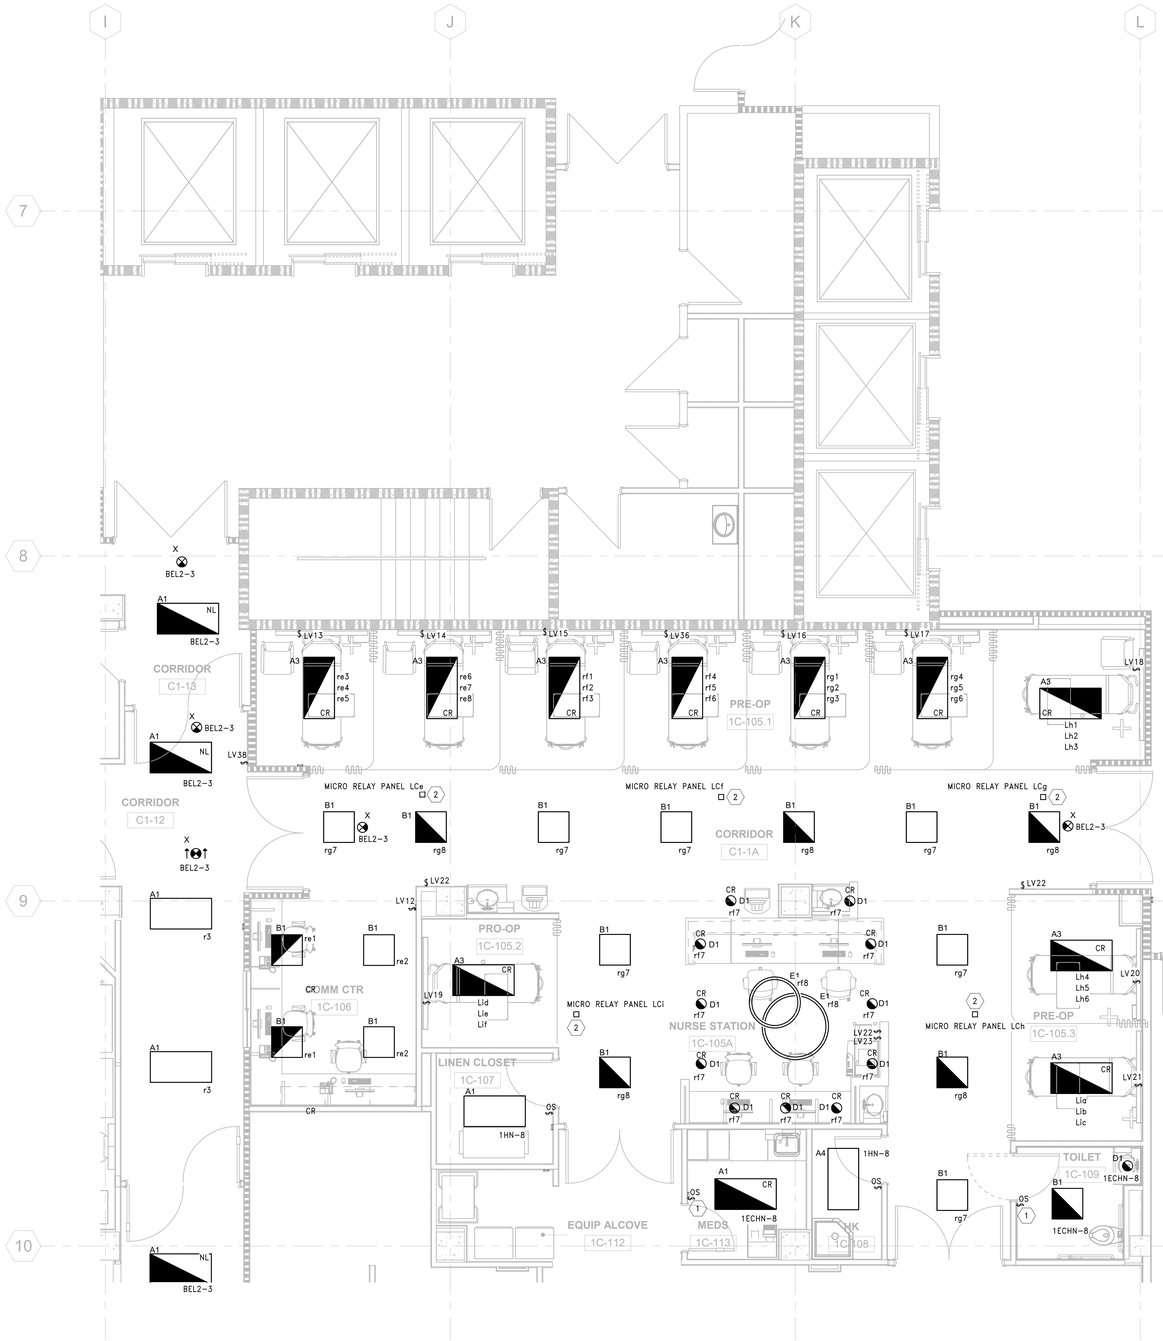

1 LIGHTING PLAN - 1ST FLOOR, PHASE 3 (NORTH)
SCALE: 1/4" = 1'-0"

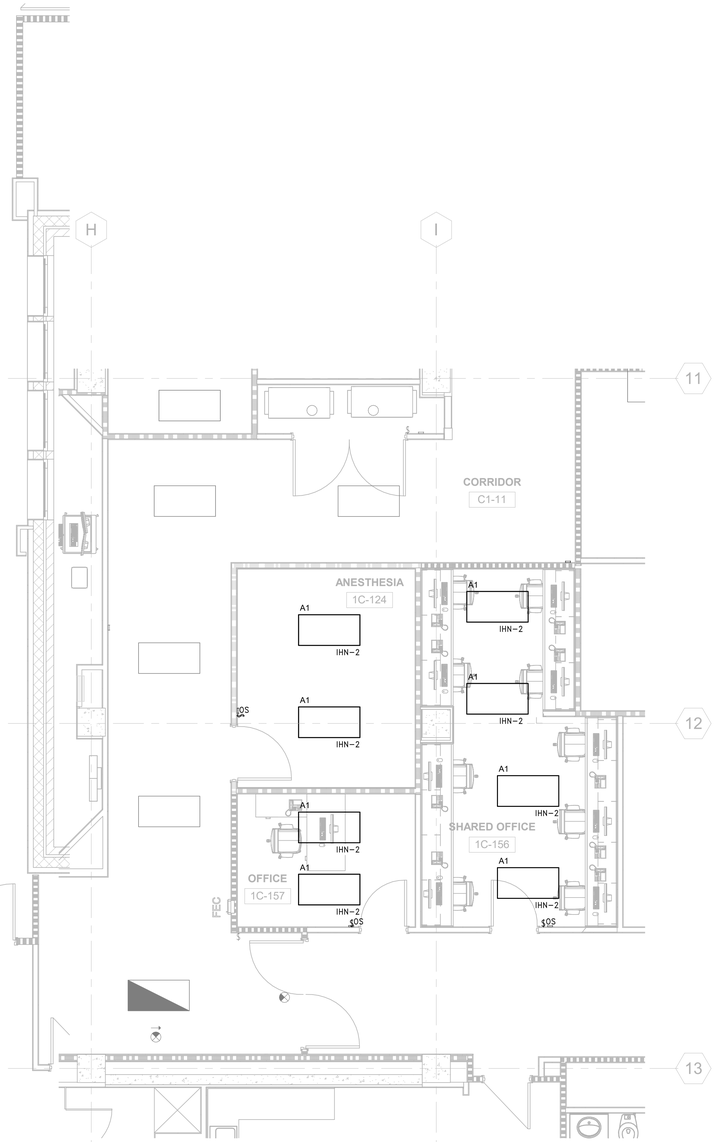

2 LIGHTING PLAN - 1ST FLOOR, PHASE 3 (SOUTH)
SCALE: 1/4" = 1'-0"

GENERAL SHEET NOTES:

1. SEE DRAWING E-001 FOR ELECTRICAL SYMBOLS AND ABBREVIATIONS AND DRAWING E-002 FOR ELECTRICAL NOTES.
2. ALL ELECTRICAL DEVICES ON THIS SHEET SHALL BE NEW, UNLESS OTHERWISE NOTED.
3. SEE DRAWING E-704 AND E-705 FOR LIGHTING FIXTURE SCHEDULE, CIRCUITRY AND LIGHTING CONTROL INFORMATION. SEE DRAWING E-701 AND E-702 FOR PANEL SCHEDULES.
4. EXIT SIGNS SHALL BE CIRCUITED AHEAD OF ALL CONTROL DEVICES.

SHEET KEYNOTES:

1 SEE DETAIL 10/E-501 FOR FURTHER INFORMATION ON SWITCHING OF EMERGENCY LIGHTING FIXTURES.
2 MICROPANEL LOCATED ABOVE ACCESSIBLE CEILING. LABEL CEILING TILE TO INDICATE MICROPANEL ABOVE.

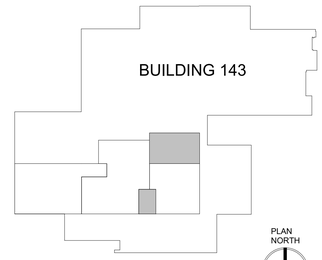

KEYPLAN

PRINTS OF THIS DRAWING SHALL NOT BE USED FOR ANY PURPOSE WHATSOEVER WITHOUT THE SEAL AND SIGNATURE OF THE PROFESSIONAL ENGINEER

Revisions:	Date:

CONSULTANT

Architecture:	Civil Engineering:	Fire Protection:
PF&A DESIGN, P.C.	LABELLA ASSOCIATES	STANTON ENGINEERING SERVICES, LLC

ENGINEER OF RECORD

MILLER•REMICK
A Service-Disabled Veteran-Owned Small Business
(856) 429-4000 • Miller-Remick.com

MILLER-REMICK LLC PROFESSIONAL ENGINEER

COMMONWEALTH OF PENNSYLVANIA — REGISTERED PROFESSIONAL — THOMAS REGINO — ENGINEER No. PE094195 — 12/30/25

Office of Construction and Facilities Management

VA U.S. Department of Veterans Affairs

Drawing Title: ELECTRICAL LIGHTING PLAN 1ST FLOOR, PHASE 3	Phase: BID DOCUMENTS	Project Title: RENOVATE SURGICAL SUITE PHASE II	VA Drawing Number: 2617
Approved by: Jon Manninen, COR	FULLY SPRINKLERED	Project Number: 658-19-103	Building Number: 143
		Location: SALEM VA MEDICAL CENTER	Drawing Number: P3-EL111
		Issue Date: 2025-12-30 / Checked: MJR / Drawn: PDK	

12/29/2025 5:32:21 PM

VA FORM 08 - 6231

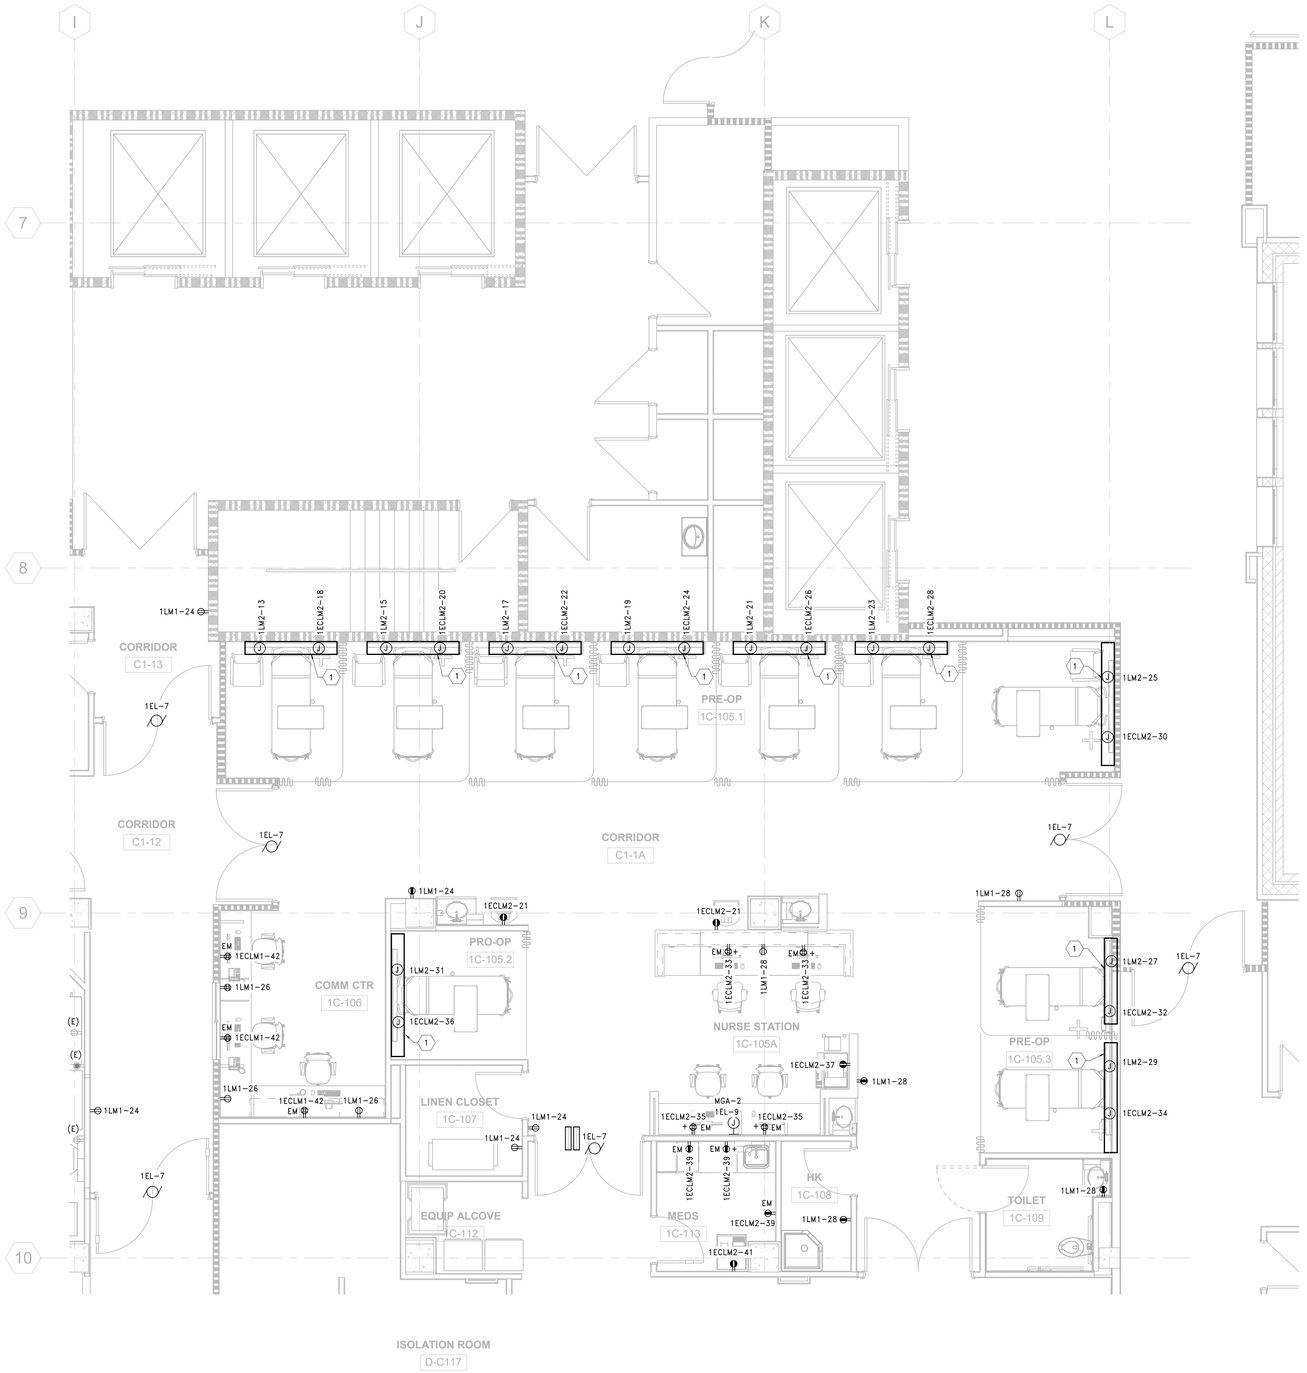

1 POWER PLAN - 1ST FLOOR, PHASE 3 (NORTH)
SCALE: 1/4" = 1'-0"

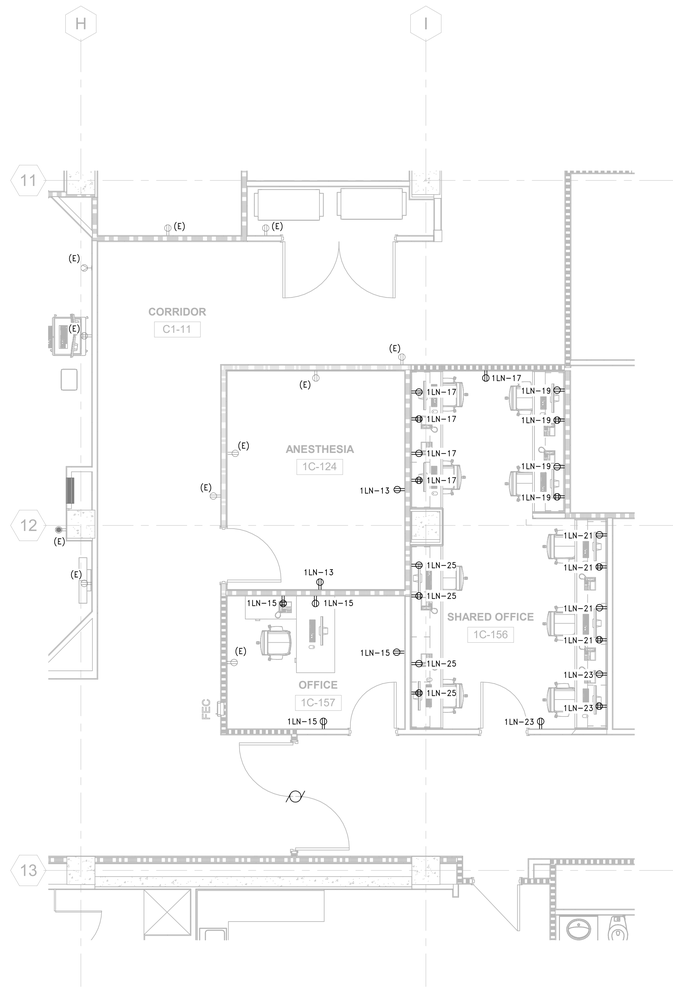

2 POWER PLAN - 1ST FLOOR, PHASE 3 (SOUTH)
SCALE: 1/4" = 1'-0"

GENERAL SHEET NOTES:

1. SEE DRAWING E-001 FOR ELECTRICAL SYMBOLS AND ABBREVIATIONS AND DRAWING E-002 FOR ELECTRICAL NOTES.
2. SEE DRAWING E-602 FOR SINGLE LINE DIAGRAM.
3. SEE DRAWING E-701 AND E-702 FOR PANEL SCHEDULES AND E-703 FOR ISOLATION PANEL SCHEDULES.
4. ALL ELECTRICAL DEVICES ON THIS SHEET SHALL BE NEW, UNLESS OTHERWISE NOTED.
5. UNLESS OTHERWISE NOTED ALL CIRCUITS WITHIN AN OR SHALL BE FED FROM THE A OR B IPU PANELS LOCATED WITHIN THAT OR.

SHEET KEYNOTES:

1 SEE DETAIL 9/E-502 FOR FURTHER INFORMATION REGARDING PRE-OP HEAD WALL UNITS.

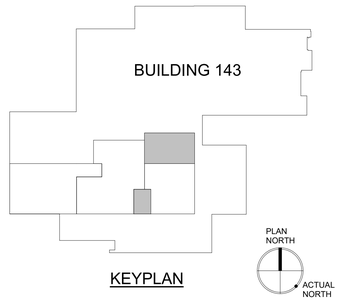

KEYPLAN

PRINTS OF THIS DRAWING SHALL NOT BE USED FOR ANY PURPOSE WHATSOEVER WITHOUT THE SEAL AND SIGNATURE OF THE PROFESSIONAL ENGINEER

Revisions:	Date:

CONSULTANT

Architecture:	Civil Engineering:	Fire Protection:
PF&A DESIGN, P.C.	LABELLA ASSOCIATES	STANTON ENGINEERING SERVICES, LLC

ENGINEER OF RECORD

MILLER-REMICK
A Service-Disabled Veteran-Owned Small Business
(856) 429-4000 • Miller-Remick.com

MILLER-REMICK LLC
PROFESSIONAL ENGINEER
COMMONWEALTH OF PENNSYLVANIA
REGISTERED PROFESSIONAL ENGINEER
THOMAS REGINO
ENGINEER IN CHARGE
12/30/25

Office of Construction and Facilities Management
VA U.S. Department of Veterans Affairs

Drawing Title: ELECTRICAL POWER PLAN 1ST FLOOR, PHASE 3	Phase: BID DOCUMENTS	Project Title: RENOVATE SURGICAL SUITE PHASE II	VA Drawing Number: 2617
Approved by: Jon Manninen, COR	FULLY SPRINKLERED	Project Number: 658-19-103	Building Number: 143
		Location: SALEM VA MEDICAL CENTER	Drawing Number: P3-EP111
		Issue Date: 2025-12-30 / Checked: MJR / Drawn: PDK	

12/29/2025 5:32:23 PM

VA FORM 08 - 6231

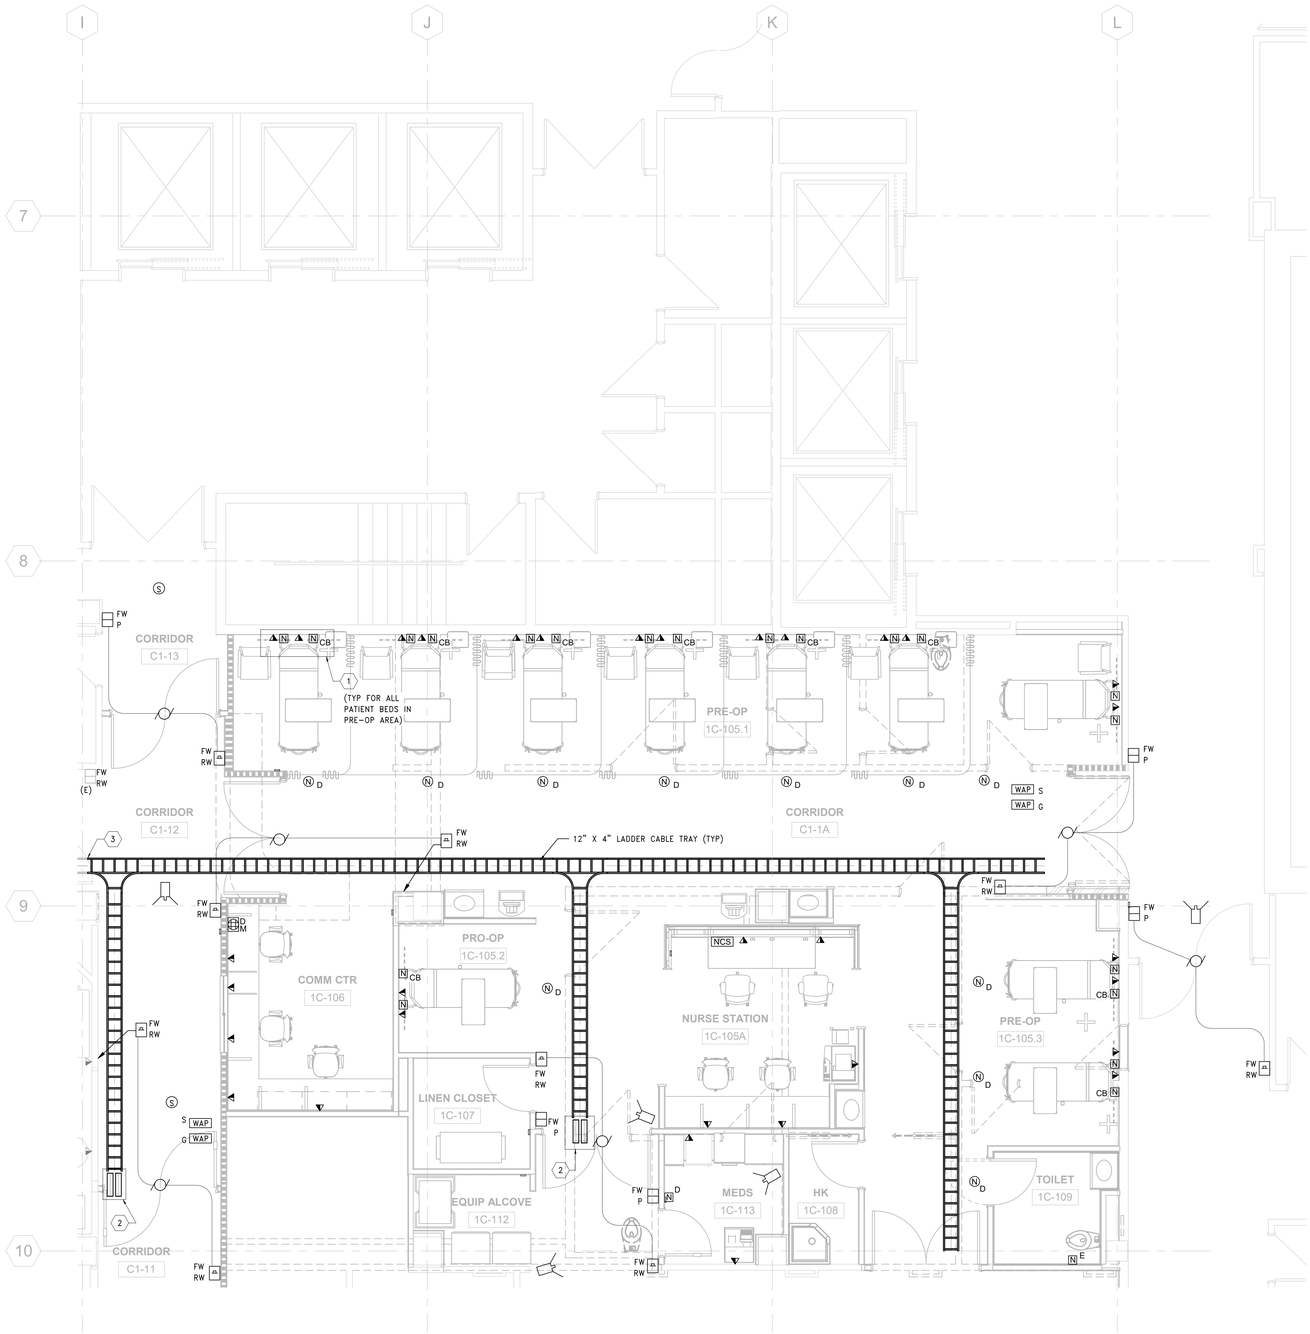

1 SYSTEMS PLAN - 1ST FLOOR, PHASE 3 (NORTH)

SCALE: 1/4" = 1'-0"

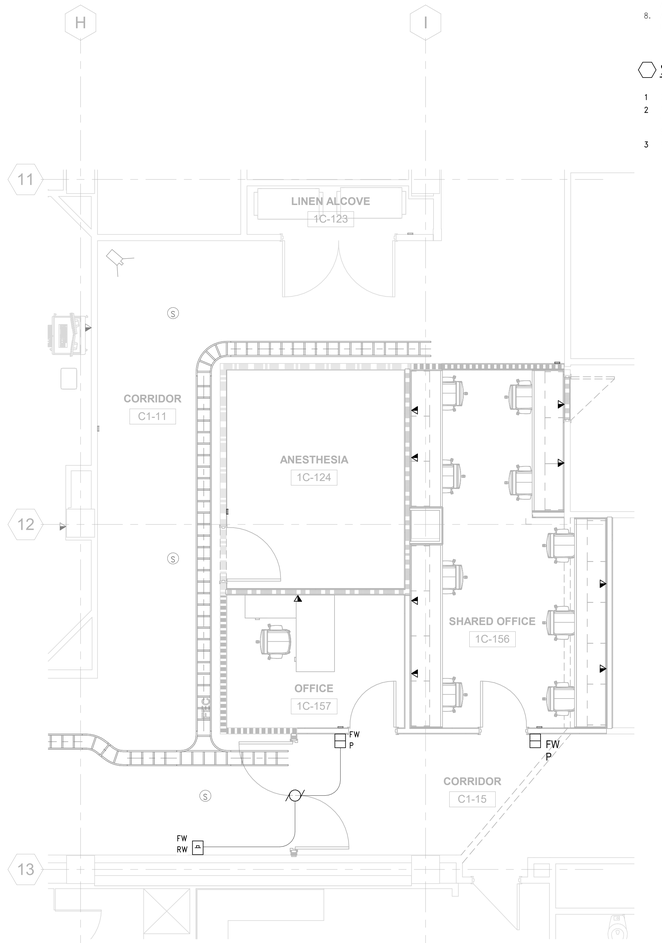

2 SYSTEMS PLAN - 1ST FLOOR, PHASE 3 (SOUTH)

SCALE: 1/4" = 1'-0"

GENERAL SHEET NOTES:

1. SEE DRAWING E-001 FOR ELECTRICAL SYMBOLS AND ABBREVIATIONS AND DRAWING E-002 FOR ELECTRICAL NOTES.
2. SEE DRAWING E-603 FOR TELE/DATA DEVICE DETAILS, CABLE TRAY DETAILS, AND TELE/DATA RISER DIAGRAM.
3. ALL TELE/DATA DEVICES ON THIS SHEET SHALL BE NEW, UNLESS OTHERWISE NOTED.
4. FOR FURTHER INFORMATION ON CARD ACCESS AND MOTORIZED DOORS, REFER TO DETAILS 3 AND 4/E-502.
5. ALL TELE/DATA WIRING FOR DEVICES ON THIS DRAWING SHALL BE PULLED BACK TO NEW TELE/DATA RACK IN IT ID-1002.
6. EC SHALL REINSTALL AND PULL NEW CAT6 WIRING TO ALL CEILING MOUNTED CENTRAK DEVICES IN THIS AREA. E.C. SHALL ALSO PROVIDE NEW CENTRAK DEVICES TO MATCH EXISTING DEVICES AS REQUIRED TO MEET THE NEEDS OF THE PROGRAM FOR THIS PROJECT. E.C. SHALL COORDINATE WITH VA AND THEIR CENTRAK REPRESENTATIVE IN REGARDS TO THE QUANTITY AND PLACEMENT REQUIREMENTS OF ALL RELOCATED AND NEW DEVICES, AS WELL AS THE WIRING REQUIREMENTS.
7. SEE NOTES 58 AND 59 ON DRAWING E-002 FOR FURTHER INFORMATION ON WIRELESS ACCESS POINT REQUIREMENTS.
8. ALL SECURITY CAMERAS SHOWN SHALL BE WIRED BACK TO EXISTING SECURITY HEADEND IN ROOM BC-114 WITH MANUFACTURER RECOMMENDED POE CABLE.

SHEET KEYNOTES:

1 DEVICES SHOWN SHALL BE MOUNTED IN THE HEADWALL.

2 PROVIDE (2) TWO – 4" CONDUITS ABOVE ACCESSIBLE CEILING AS A PASS-THRU FOR TELECOMMUNICATION CABLING. CONDUIT SHALL BE PROVIDED WITH BUSHED ENDS AND PULL STRING. SEAL PENETRATION AS REQUIRED.

3 PROVIDE ALL NECESSARY COMPONENTS NEEDED FOR A CONTINUOUS RUN FROM A PREVIOUSLY INSTALLED CABLE TRAY AT AN EARLIER PHASE.

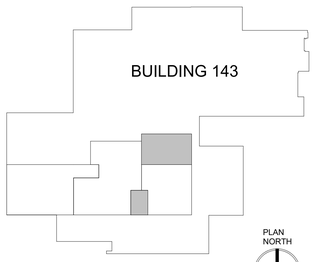

KEYPLAN

PRINTS OF THIS DRAWING SHALL NOT BE USED FOR ANY PURPOSE WHATSOEVER WITHOUT THE SEAL AND SIGNATURE OF THE PROFESSIONAL ENGINEER

Revisions: | Date:

CONSULTANT

Architecture:	Civil Engineering:	Fire Protection:
PF&A DESIGN, P.C.	LABELLA ASSOCIATES	STANTON ENGINEERING SERVICES, LLC

ENGINEER OF RECORD

MILLER•REMICK
A Service-Disabled Veteran-Owned Small Business
(856) 429-4000 • Miller-Remick.com

MILLER-REMICK LLC PROFESSIONAL ENGINEER

COMMONWEALTH OF PENNSYLVANIA — REGISTERED PROFESSIONAL — THOMAS REGINO — ENGINEER No. PE094195

12/30/25

Office of Construction and Facilities Management

VA U.S. Department of Veterans Affairs

Drawing Title: ELECTRICAL SYSTEMS PLAN 1ST FLOOR, PHASE 3	Phase: BID DOCUMENTS
Approved by: Jon Manninen, COR	FULLY SPRINKLERED

Project Title	VA Drawing Number
RENOVATE SURGICAL SUITE PHASE II	2617
Project Number: 658-19-103	Building Number: 143
Location: SALEM VA MEDICAL CENTER	Drawing Number: P3-EY111
Issue Date: 2025-12-30 / Checked: MJR / Drawn: PDK	

VA FORM 08 - 6231

12/29/2025 5:32:24 PM

three inches = one foot
one and one half inches = one foot
one inch = one foot
three quarters inch = one foot
one half inch = one foot
three eighths inch = one foot
one quarter inch = one foot
one eighth inch = one foot
P:\0499_DVA\0499-0136 Salem Renovate Surgical Suite\4_Drawings\1_Cost\1_Current Submittal Phase\7_Electrical\P4-ED111.dwg 12-29-25 05:55:22 PM mcitelli

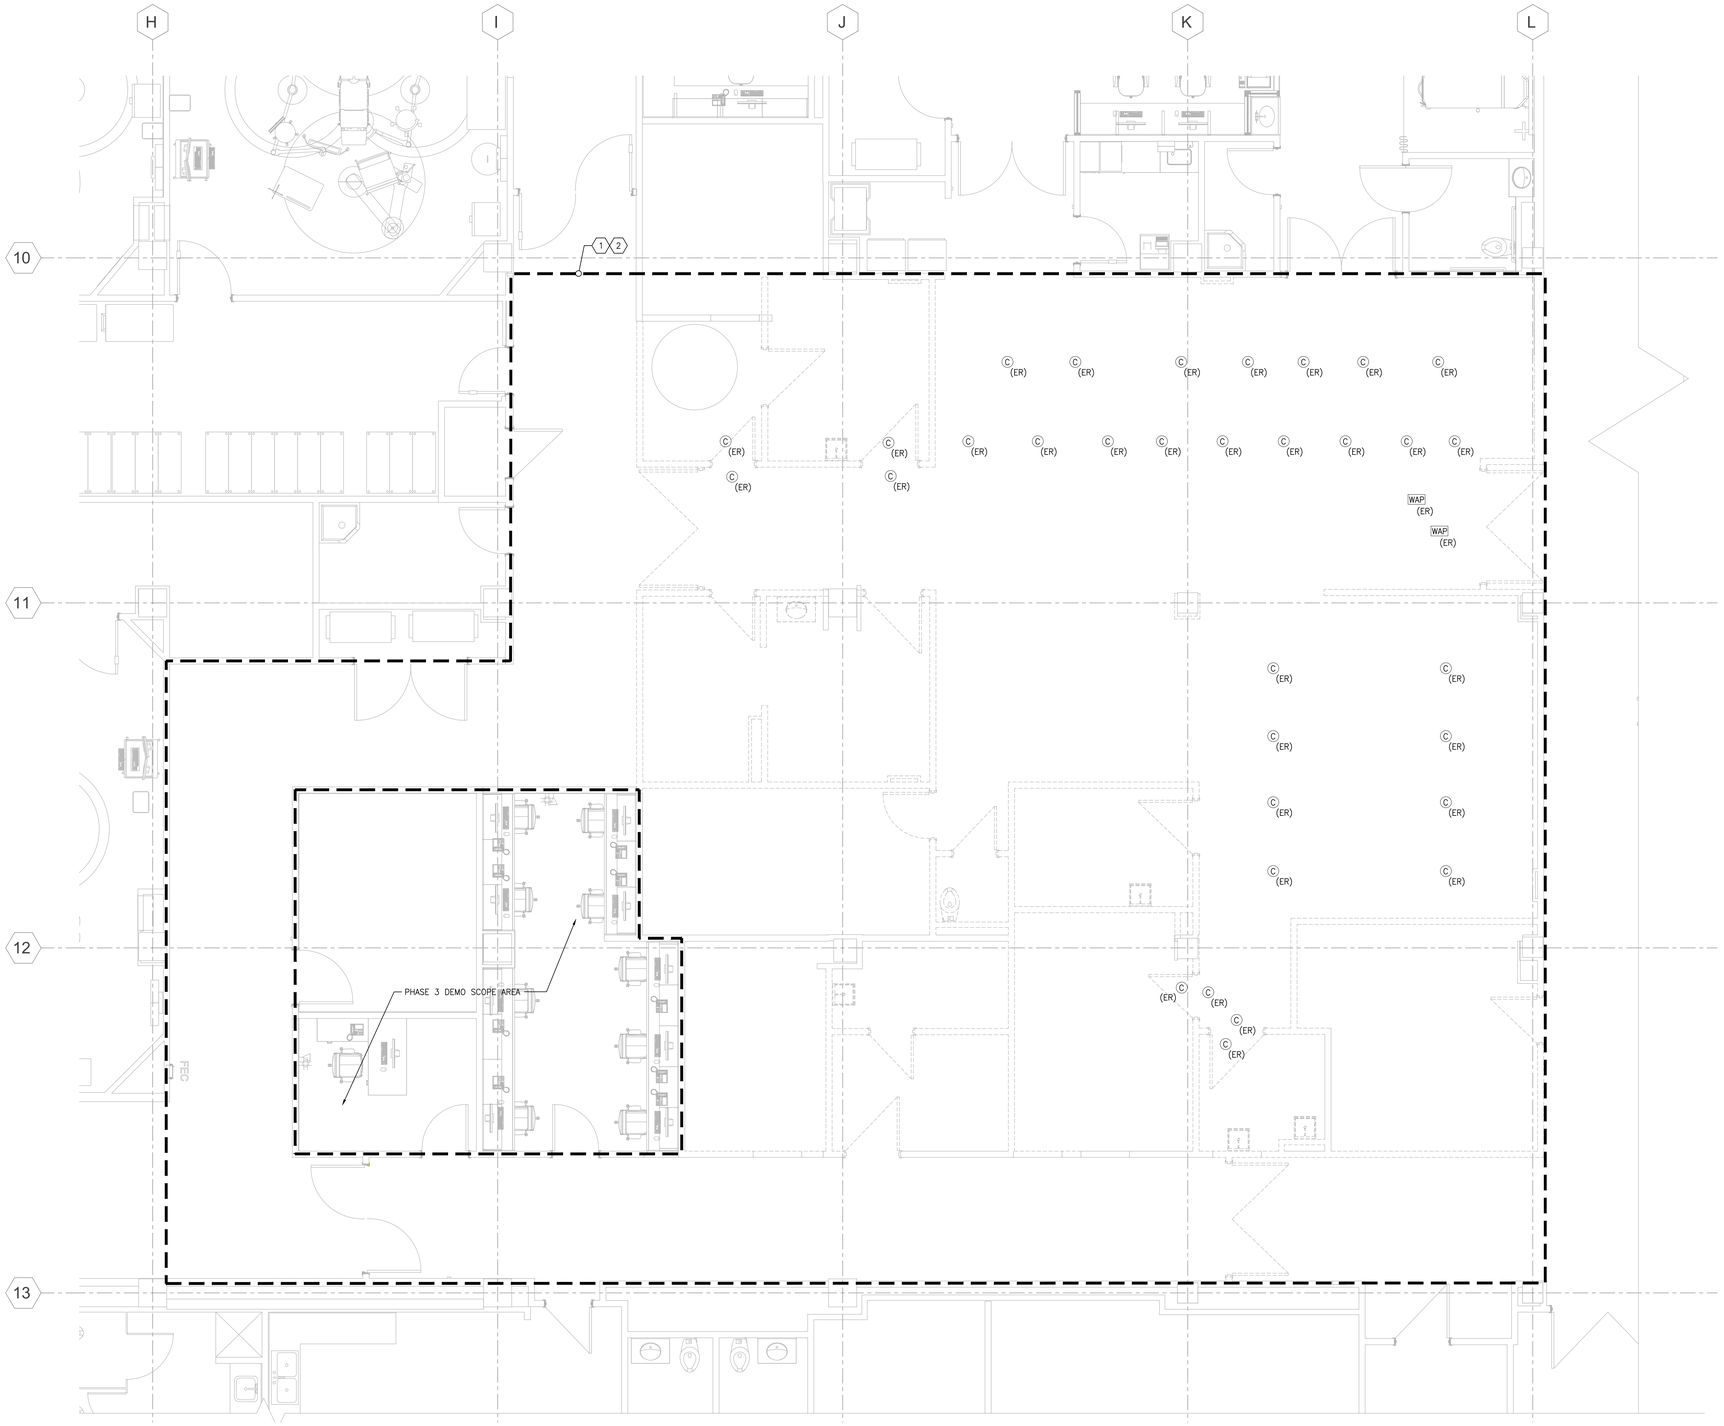

GENERAL SHEET NOTES:

1. SEE DRAWINGS E-001 AND E-002 FOR ABBREVIATIONS, SYMBOLS AND NOTES.
2. SCOPE SHOWN IS BASE BID. SEE DRAWING AE110 FOR BID DEDUCT SCOPE.

SHEET KEYNOTES:

1. DEMOLISH ALL ELECTRICAL DEVICES INCLUDING, BUT NOT LIMITED TO, PANELBOARDS, LIGHTING, LIGHTING CONTROL, RECEPTACLES, TELE/DATA AND FIRE ALARM DEVICES, ETC. WITHIN BOUNDARY, UNLESS OTHERWISE NOTED. DEMOLISH ALL ELECTRICAL DEVICE WIRING AND RACEWAYS BACK TO SOURCE.
2. ALL WIRELESS ACCESS POINTS AND CENTRAK DEVICES WITHIN THIS BOUNDARY SHALL BE REMOVED, CLEANED, AND STORED FOR REINSTALLATION.

1 ELECTRICAL DEMOLITION PLAN – 1ST FLOOR, PHASE 4
SCALE: 1/4" = 1'-0"

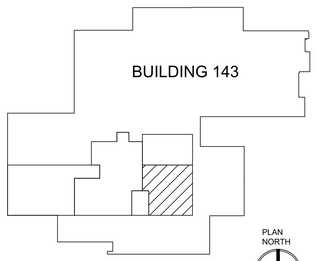

KEYPLAN

PRINTS OF THIS DRAWING SHALL NOT BE USED FOR ANY PURPOSE WHATSOEVER WITHOUT THE SEAL AND SIGNATURE OF THE PROFESSIONAL ENGINEER.

NO.	DESCRIPTION	DATE

CONSULTANTS

Architecture:	Civil Engineering:	Fire & Life Safety:
PF&A DESIGN, P.C.	LABELLA ASSOCIATES	STANTON ENGINEERING SERVICES, LLC

ENGINEER OF RECORD

MILLER•REMICK
A Service-Disabled Veteran-Owned Small Business
(856) 429-4000 • Miller-Remick.com
M-R PROJECT NO. 0499-0136

MILLER-REMICK LLC
PROFESSIONAL ENGINEER
COMMONWEALTH OF PENNSYLVANIA
REGISTERED PROFESSIONAL
THOMAS REGINO
ENGINEER
No. PE094195
12/30/25

Office of Construction and Facilities Management

VA U.S. Department of Veterans Affairs

Drawing Title	ELECTRICAL DEMOLITION PLAN 1ST FLOOR, PHASE 4
Approved by:	Jon Manninen, COR
Phase	BID DOCUMENTS
	FULLY SPRINKLERED
Project Title	RENOVATE SURGICAL SUITE PHASE II
Project Number	658-19-103
Location	SALEM VA MEDICAL CENTER
Issue Date	2025-12-30
Checked	MJR
Drawn	MJR
VA Drawing Number	2617
Building Number	143
Drawing Number	P4-ED111

VA FORM 08-6231

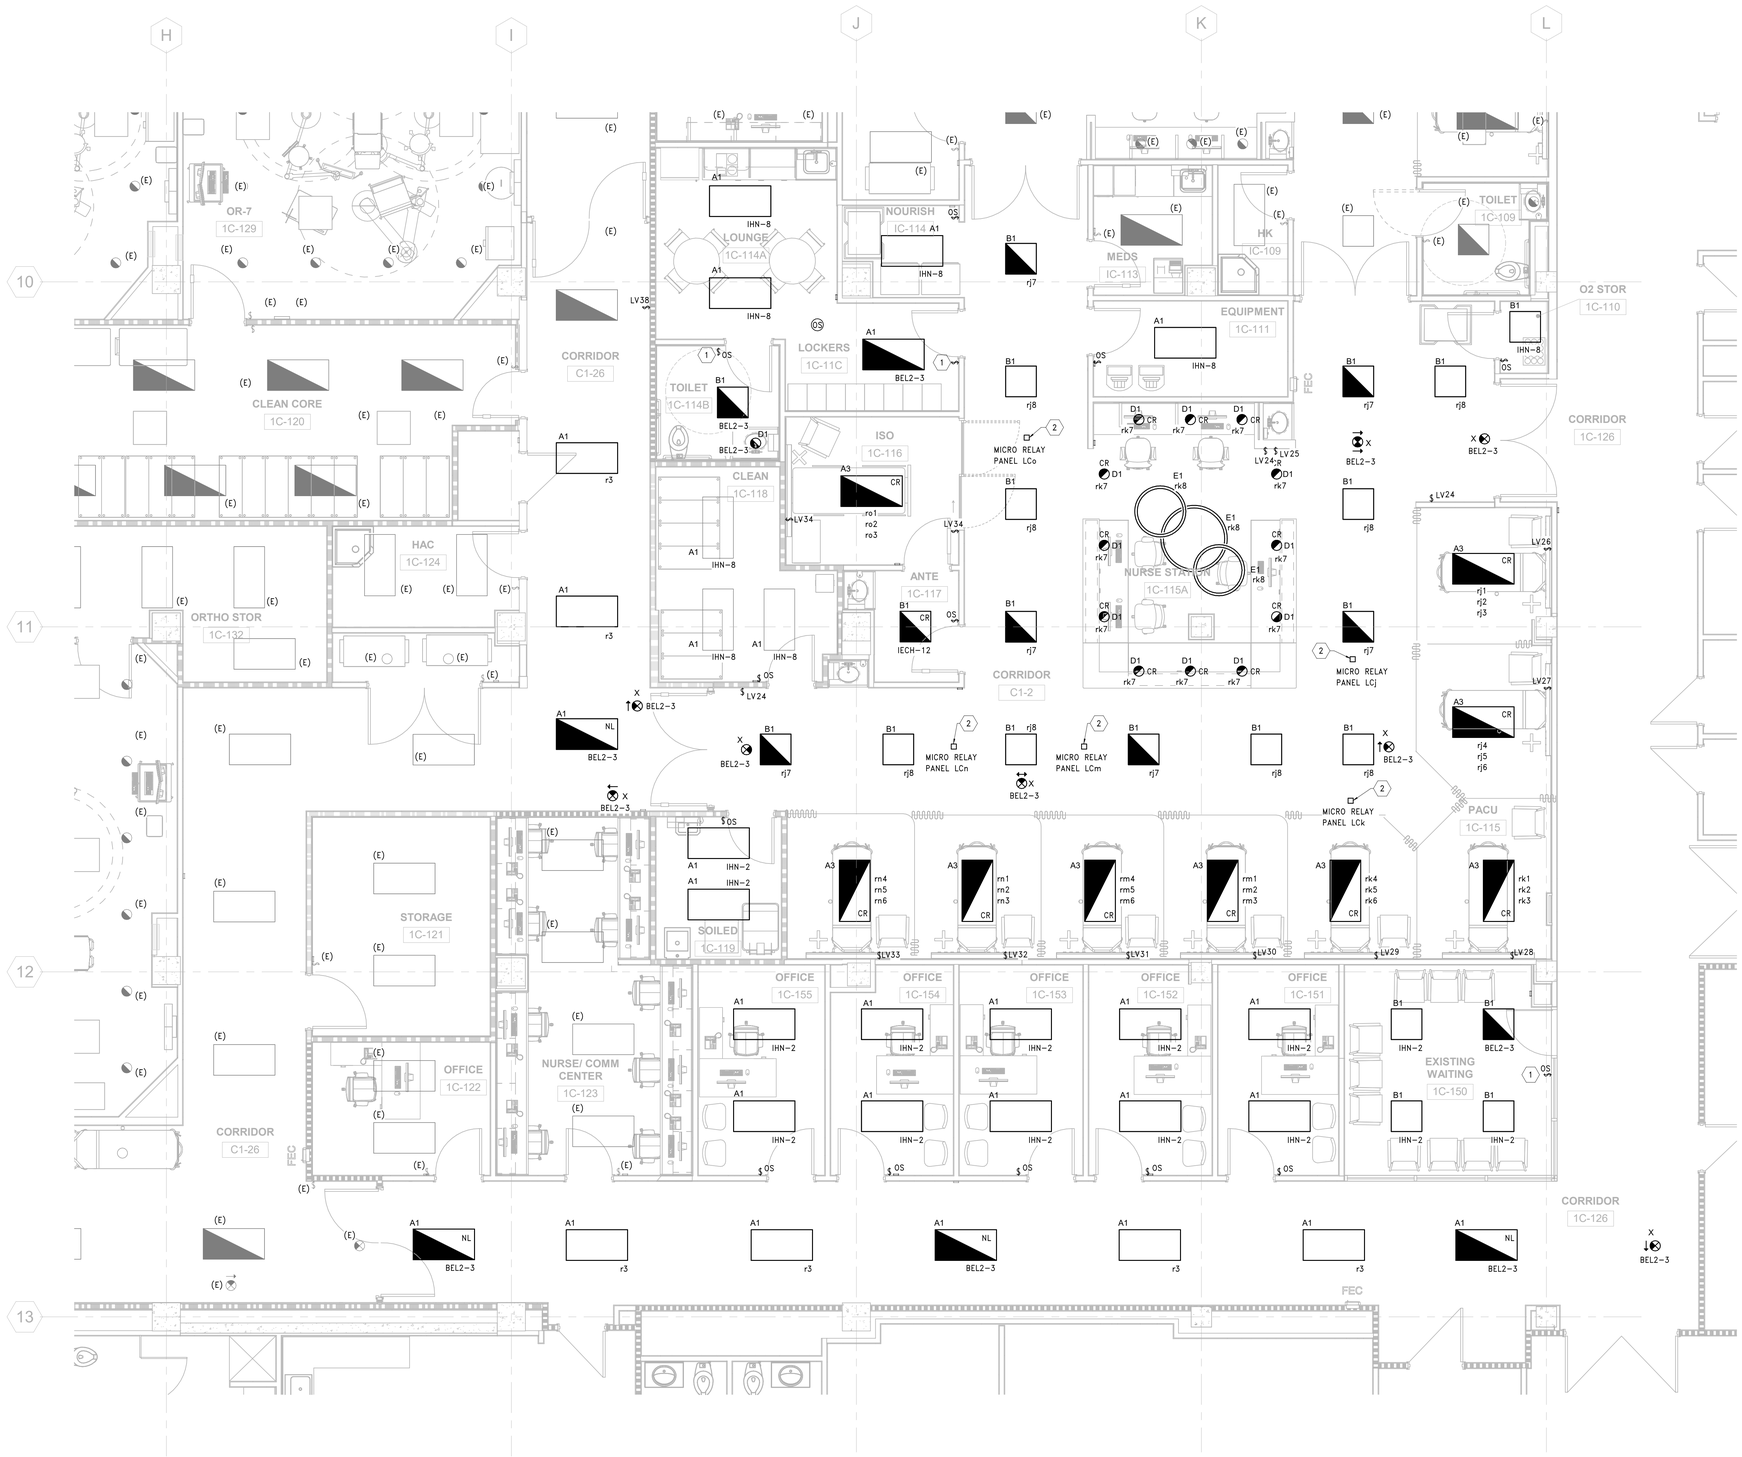

1 LIGHTING PLAN - 1ST FLOOR, PHASE 4

SCALE: 1/4" = 1'-0"

GENERAL SHEET NOTES:

1. SEE DRAWING E-001 FOR ELECTRICAL SYMBOLS AND ABBREVIATIONS AND DRAWING E-002 FOR ELECTRICAL NOTES.
2. ALL ELECTRICAL DEVICES ON THIS SHEET SHALL BE NEW, UNLESS OTHERWISE NOTED.
3. SEE DRAWING E-704 AND E-705 FOR LIGHTING FIXTURE SCHEDULE, CIRCUITRY AND LIGHTING CONTROL INFORMATION. SEE DRAWING E-701 AND E-702 FOR PANEL SCHEDULES.
4. EXIT SIGNS SHALL BE CIRCUITED AHEAD OF ALL CONTROL DEVICES.
5. SCOPE SHOWN IS BASE BID. SEE DRAWING AE110 FOR BID DEDUCT SCOPE.

SHEET KEYNOTES:

1 SEE DETAIL 10/E-501 FOR FURTHER INFORMATION ON SWITCHING OF EMERGENCY LIGHTING FIXTURES.

2 MICROPANEL LOCATED ABOVE ACCESSIBLE CEILING. LABEL CEILING TILE TO INDICATE MICROPANEL ABOVE.

BUILDING 143

KEYPLAN

PLAN NORTH

ACTUAL NORTH

PRINTS OF THIS DRAWING SHALL NOT BE USED FOR ANY PURPOSE WHATSOEVER WITHOUT THE SEAL AND SIGNATURE OF THE PROFESSIONAL ENGINEER

Revisions:	Date:

CONSULTANT

Architecture:	Civil Engineering:	Fire Protection:
PF&A DESIGN, P.C.	LABELLA ASSOCIATES	STANTON ENGINEERING SERVICES, LLC

ENGINEER OF RECORD

MILLER-REMICK LLC
PROFESSIONAL ENGINEER

COMMONWEALTH OF PENNSYLVANIA — REGISTERED PROFESSIONAL — THOMAS REGINO — ENGINEER — No. PE094176

12/30/25

A Service-Disabled Veteran-Owned Small Business
(856) 429-6000 ★ Miller-Remick.com
M-R PROJECT NO. 0909-0036

Office of Construction and Facilities Management

U.S. Department of Veterans Affairs

Drawing Title	ELECTRICAL LIGHTING PLAN 1ST FLOOR, PHASE 4
Approved by:	Jon Manninen, COR
Phase	BID DOCUMENTS
	FULLY SPRINKLERED
Project Title	RENOVATE SURGICAL SUITE PHASE II
Project Number	658-19-103
Location	SALEM VA MEDICAL CENTER
Issue Date	2025-12-30
Checked	MJR
Drawn	PDK
VA Drawing Number	2617
Building Number	143
Drawing Number	P4-EL111

12/29/2025 9:32:27 PM

VA FORM 08 - 6231

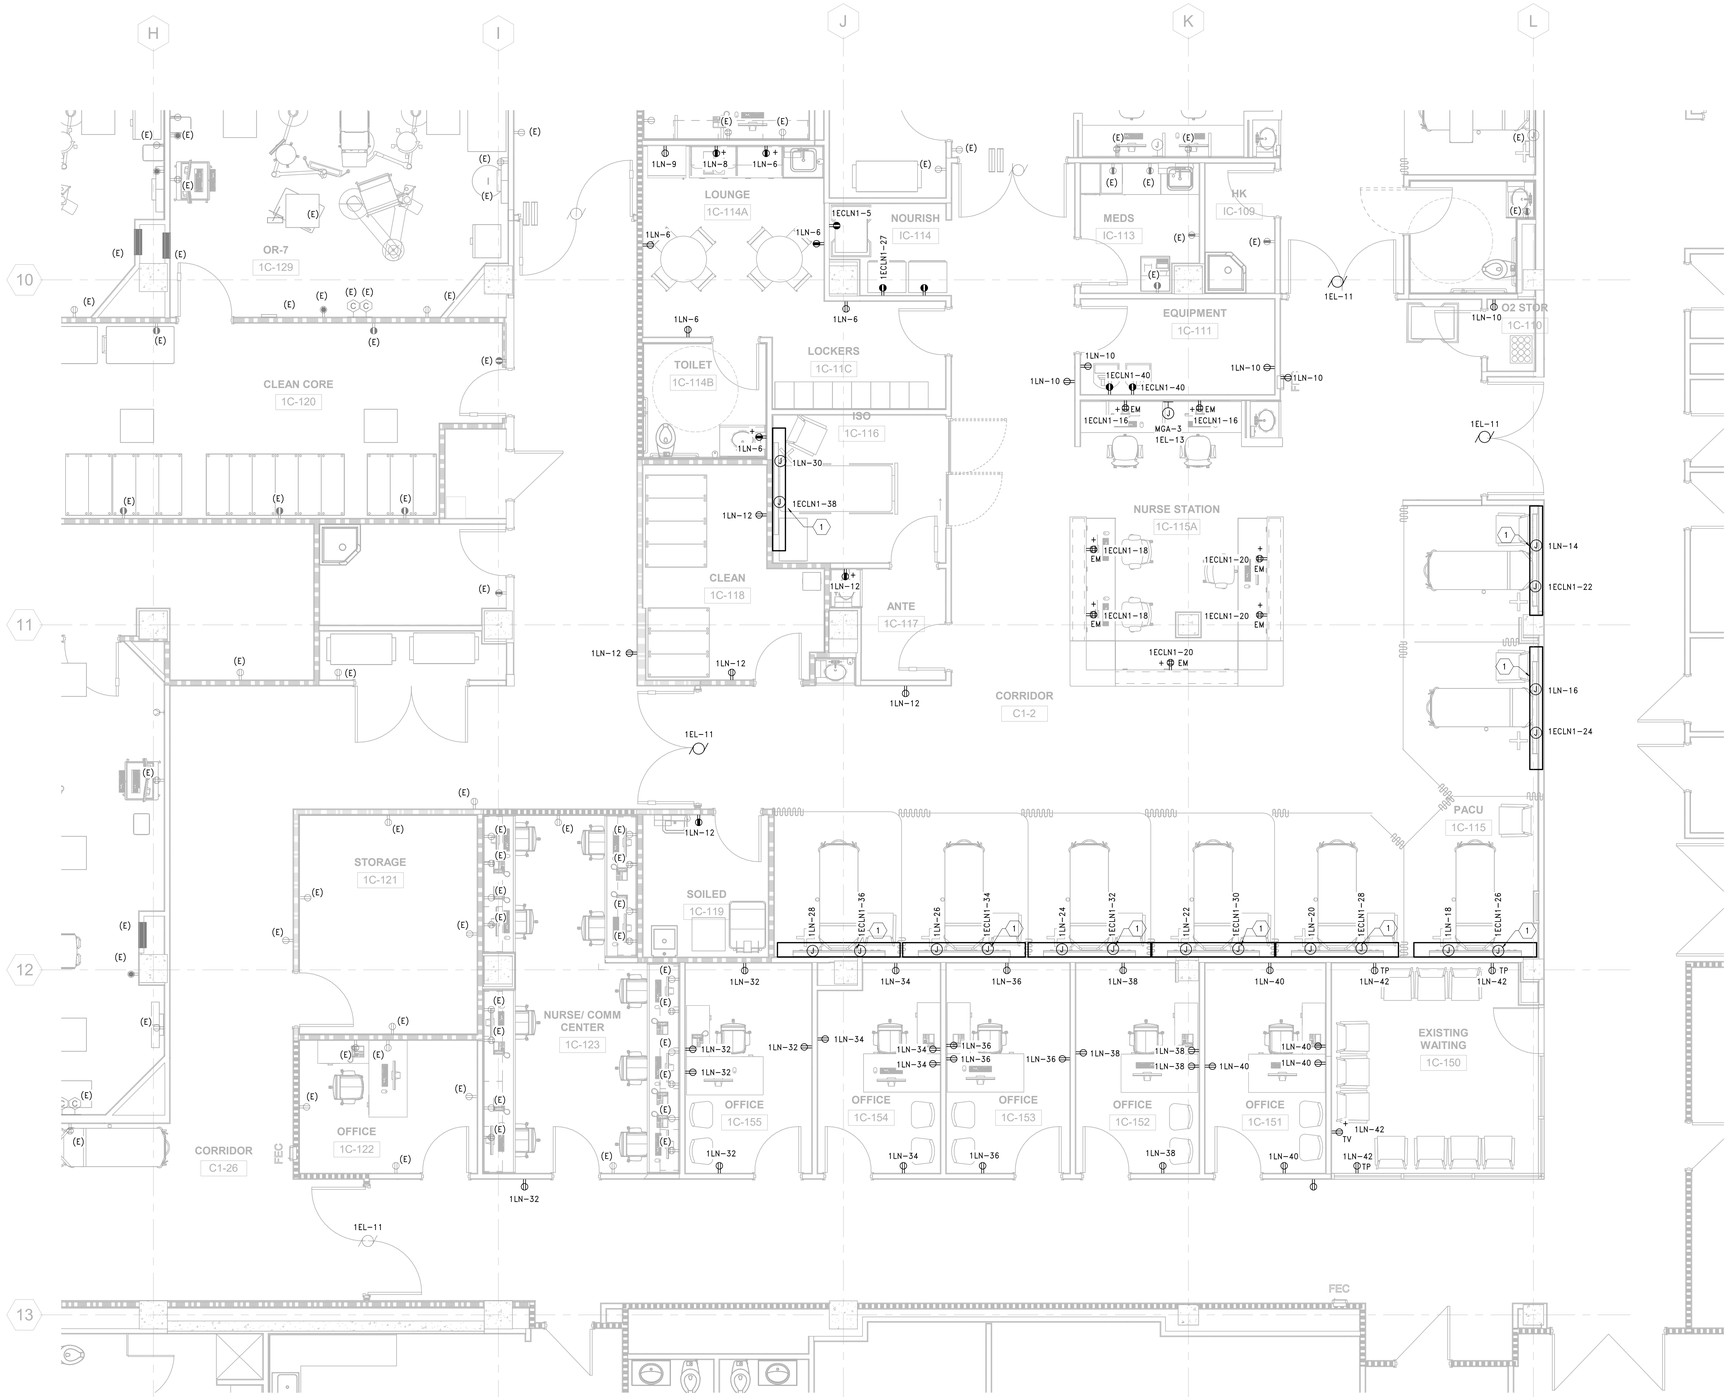

GENERAL SHEET NOTES:

1. SEE DRAWING E-001 FOR ELECTRICAL SYMBOLS AND ABBREVIATIONS AND DRAWING E-002 FOR ELECTRICAL NOTES.
2. SEE DRAWING E-602 FOR SINGLE LINE DIAGRAM.
3. SEE DRAWING E-701 AND E-702 FOR PANEL SCHEDULES AND E-703 FOR ISOLATION PANEL SCHEDULES.
4. ALL ELECTRICAL DEVICES ON THIS SHEET SHALL BE NEW, UNLESS OTHERWISE NOTED.
5. UNLESS OTHERWISE NOTED ALL CIRCUITS WITHIN AN OR SHALL BE FED FROM THE A OR B IPU PANELS LOCATED WITHIN THAT OR.

SHEET KEYNOTES:

1 SEE DETAIL 8/E-502 FOR FURTHER INFORMATION REGARDING PACU HEAD WALL UNITS.

1 POWER PLAN - 1ST FLOOR, PHASE 4

SCALE: 1/4" = 1'-0"

BUILDING 143

KEYPLAN

PLAN NORTH

ACTUAL NORTH

PRINTS OF THIS DRAWING SHALL NOT BE USED FOR ANY PURPOSE WHATSOEVER WITHOUT THE SEAL AND SIGNATURE OF THE PROFESSIONAL ENGINEER

Revisions: | Date:

CONSULTANT

Architecture:	Civil Engineering:	Fire Protection:
PF&A DESIGN, P.C.	LABELLA ASSOCIATES	STANTON ENGINEERING SERVICES, LLC

ENGINEER OF RECORD

MILLER-REMICK

A Service-Disabled Veteran-Owned Small Business

(856) 429-5000 • Miller-Remick.com

MILLER-REMICK LLC
PROFESSIONAL ENGINEER

COMMONWEALTH OF PENNSYLVANIA REGISTERED PROFESSIONAL THOMAS REGINO ENGINEER No. PE094195

12/30/25

Office of Construction and Facilities Management

VA U.S. Department of Veterans Affairs

Drawing Title: ELECTRICAL POWER PLAN 1ST FLOOR, PHASE 4	Phase: BID DOCUMENTS	Project Title: RENOVATE SURGICAL SUITE PHASE II	VA Drawing Number: 2617
		Project Number: 658-19-103	Building Number: 143
Approved by: Jon Manninen, COR	FULLY SPRINKLERED	Location: SALEM VA MEDICAL CENTER	Drawing Number: P4-EP111
		Issue Date: 2025-12-30 / Checked: MJR / Drawn: PDK	

12/29/2025 5:32:28 PM

VA FORM 08 - 6231

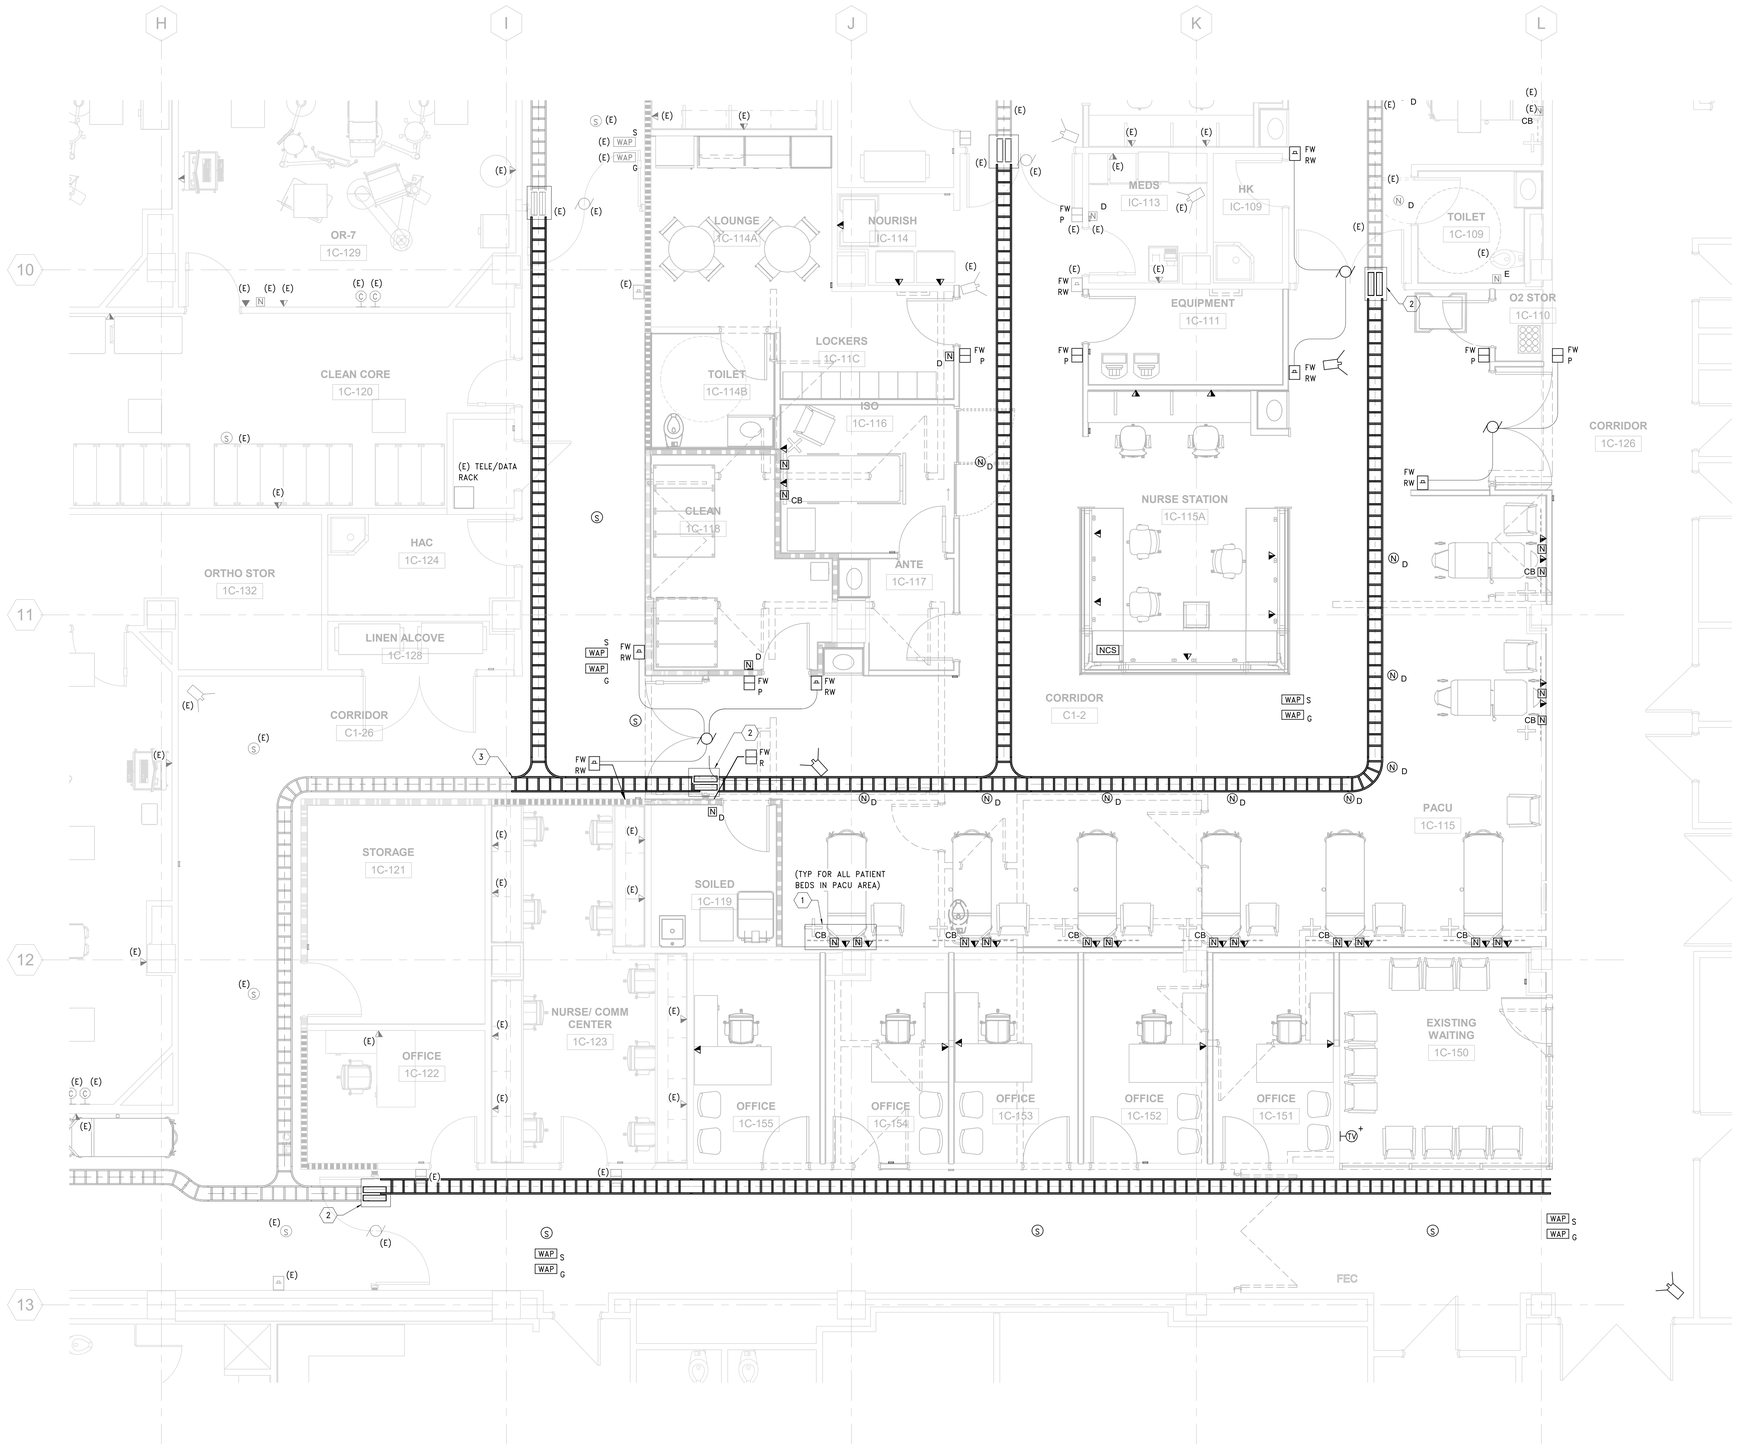

GENERAL SHEET NOTES:

1. SEE DRAWING E-001 FOR ELECTRICAL SYMBOLS AND ABBREVIATIONS AND DRAWING E-002 FOR ELECTRICAL NOTES.
2. SEE DRAWING E-603 FOR TELE/DATA DEVICE DETAILS, CABLE TRAY DETAILS, AND TELE/DATA RISER DIAGRAM.
3. ALL TELE/DATA DEVICES ON THIS SHEET SHALL BE NEW, UNLESS OTHERWISE NOTED.
4. FOR FURTHER INFORMATION ON CARD ACCESS AND MOTORIZED DOORS, REFER TO DETAILS 3 AND 4/E-502.
5. ALL TELE/DATA WIRING FOR DEVICES ON THIS DRAWING SHALL BE PULLED BACK TO EXISTING TELE/DATA RACK IN IRM IC-121.
6. EC SHALL REINSTALL AND PULL NEW CAT6 WIRING TO ALL CEILING MOUNTED CENTRAK DEVICES IN THIS AREA. E.C. SHALL ALSO PROVIDE NEW CENTRAK DEVICES TO MATCH EXISTING DEVICES AS REQUIRED TO MEET THE NEEDS OF THE PROGRAM FOR THIS PROJECT. E.C. SHALL COORDINATE WITH VA AND THEIR CENTRAK REPRESENTATIVE IN REGARDS TO THE QUANTITY AND PLACEMENT REQUIREMENTS OF ALL RELOCATED AND NEW DEVICES, AS WELL AS THE WIRING REQUIREMENTS.
7. SCOPE SHOWN IS BASE BID. SEE DRAWING AE110 FOR BID DEDUCT SCOPE.
8. SEE NOTES 58 AND 59 ON DRAWING E-002 FOR FURTHER INFORMATION ON WIRELESS ACCESS POINT REQUIREMENTS.
9. ALL SECURITY CAMERAS SHOWN SHALL BE WIRED BACK TO EXISTING SECURITY HEADEND IN ROOM BC-114 WITH MANUFACTURER RECOMMENDED POE CABLE.

SHEET KEYNOTES:

1 DEVICES SHOWN SHALL BE MOUNTED IN THE HEADWALL.

2 PROVIDE (2) TWO – 4" CONDUITS ABOVE ACCESSIBLE CEILING AS A PASS-THRU FOR TELECOMMUNICATION CABLING. CONDUIT SHALL BE PROVIDED WITH BUSHED ENDS AND PULL STRING. SEAL PENETRATION AS REQUIRED.

3 PROVIDE ALL NECESSARY COMPONENTS NEEDED FOR A CONTINUOUS RUN FROM A PREVIOUSLY INSTALLED CABLE TRAY AT AN EARLIER PHASE.

1 SYSTEMS PLAN - 1ST FLOOR, PHASE 4

SCALE: 1/4" = 1'-0"

BUILDING 143

KEYPLAN

PLAN NORTH

ACTUAL NORTH

PRINTS OF THIS DRAWING SHALL NOT BE USED FOR ANY PURPOSE WHATSOEVER WITHOUT THE SEAL AND SIGNATURE OF THE PROFESSIONAL ENGINEER

Revisions:	Date:

CONSULTANT

Architecture:	Civil Engineering:	Fire Protection:
PF&A DESIGN, P.C.	LABELLA ASSOCIATES	STANTON ENGINEERING SERVICES, LLC

ENGINEER OF RECORD

MILLER-REMICK

A Service-Disabled Veteran-Owned Small Business

(856) 429-4000 • Miller-Remick.com

M-R PROJECT NO. 3699-036

MILLER-REMICK LLC
PROFESSIONAL ENGINEER

COMMONWEALTH OF PENNSYLVANIA REGISTERED PROFESSIONAL THOMAS REGINO ENGINEER No. PE094195

12/30/25

Office of Construction and Facilities Management

VA U.S. Department of Veterans Affairs

Drawing Title: ELECTRICAL SYSTEMS PLAN 1ST FLOOR, PHASE 4	Phase: BID DOCUMENTS	Project Title: RENOVATE SURGICAL SUITE PHASE II	VA Drawing Number: 2617
		Project Number: 658-19-103	Building Number: 143
Approved by: Jon Manninen, COR	FULLY SPRINKLERED	Location: SALEM VA MEDICAL CENTER	Drawing Number: P4-EY111
		Issue Date: 2025-12-30 / Checked: MJR / Drawn: PDK	

12/29/2025 5:32:30 PM

VA FORM 08 - 6231

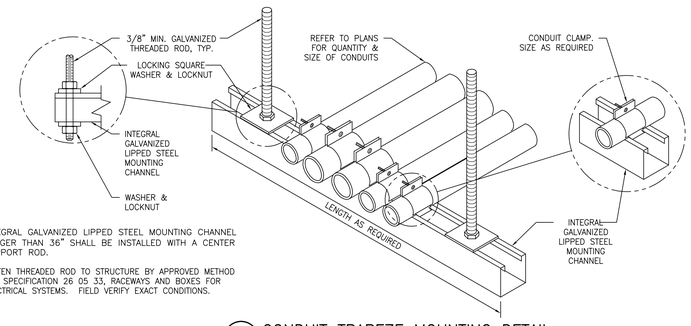

NOTES
1. INTEGRAL GALVANIZED LIPPED STEEL MOUNTING CHANNEL LONGER THAN 36" SHALL BE INSTALLED WITH A CENTER SUPPORT ROD.
2. FASTEN THREADED ROD TO STRUCTURE BY APPROVED METHOD PER SPECIFICATION 26 05 33, RACEWAYS AND BOXES FOR ELECTRICAL SYSTEMS. FIELD VERIFY EXACT CONDITIONS.

1 CONDUIT TRAPEZE MOUNTING DETAIL
SCALE: NTS

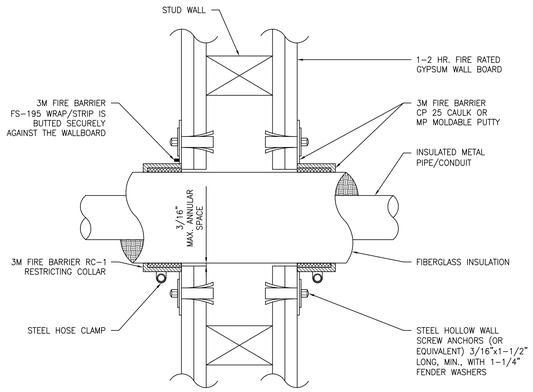

2 FIRE STOP FOR CONDUIT PENETRATION THROUGH GYPSUM BOARD
SCALE: NTS

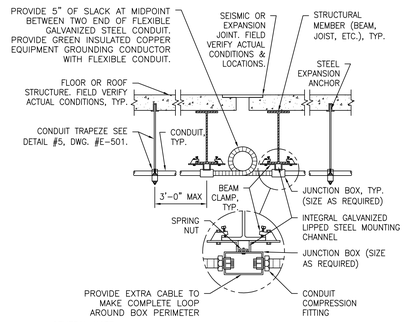

GENERAL NOTE:
1. DETAIL IS APPLICABLE ONLY FOR CONDUIT SMALLER THAN 76mm (3").

3 CONDUIT – JOINT CROSSING DETAIL
SCALE: NTS

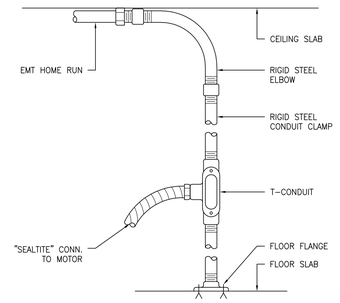

4 CONDUIT – OVERHEAD DROP DETAIL
SCALE: NTS

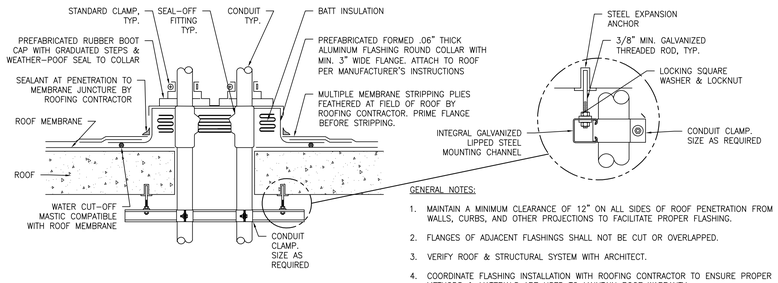

GENERAL NOTES:
1. MAINTAIN A MINIMUM CLEARANCE OF 12" ON ALL SIDES OF ROOF PENETRATION FROM WALLS, CURBS, AND OTHER PROJECTIONS TO FACILITATE PROPER FLASHING.
2. FLANGES OF ADJACENT FLASHINGS SHALL NOT BE CUT OR OVERLAPPED.
3. VERIFY ROOF & STRUCTURAL SYSTEM WITH ARCHITECT.
4. COORDINATE FLASHING INSTALLATION WITH ROOFING CONTRACTOR TO ENSURE PROPER METHODS & MATERIALS ARE USED TO MAINTAIN ROOF WARRANTY.

5 CONDUIT – ROOF PENETRATION DETAIL
SCALE: NTS

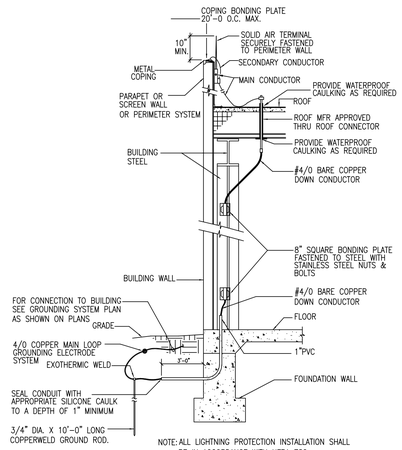

NOTE: ALL LIGHTNING PROTECTION INSTALLATION SHALL BE IN ACCORDANCE WITH NFPA 780

6 TYPICAL LIGHTNING PROTECTION SYSTEM CONNECTION DETAIL
SCALE: NTS

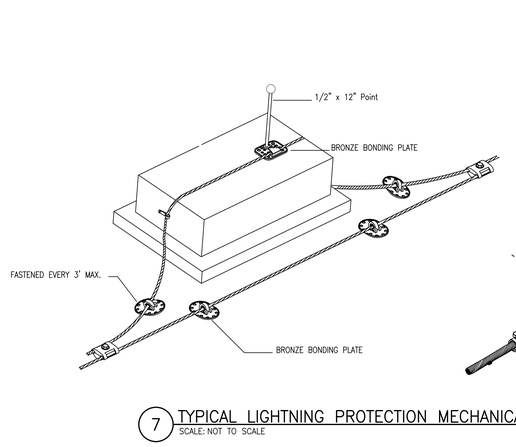

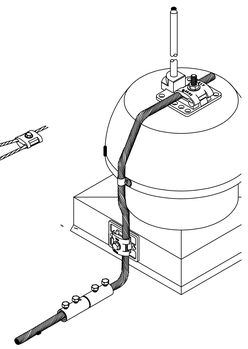

7 TYPICAL LIGHTNING PROTECTION MECHANICAL EQUIPMENT
SCALE: NOT TO SCALE

NOTES:
1. NEW MATERIAL SHALL MATCH EXISTING HORIZONTAL WIRING CURRENTLY INSTALLED ON ROOF. ALUMINUM AIR TERMINALS AND WIRING ARE ACCEPTABLE, PROVIDED THAT THIS MATERIAL MATCHES THE EXISTING INSTALLATION.

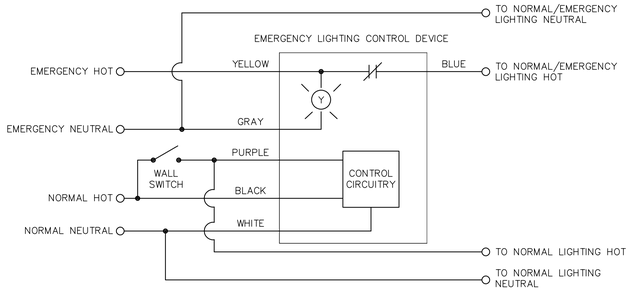

10 UL 924 EMERGENCY LIGHT FIXTURE SWITCHING CONTROL SCHEMATIC
SCALE: NTS

NOTES:
1. DEVICE SHALL BE MOUNTED ABOVE ACCESSIBLE CEILING AHEAD OF LIGHTING CONTROL DEVICE, I.E. LIGHT SWITCH.
2. DEVICE IS RATED FOR A 20-AMP CIRCUIT WHEN CONTROLLING FLUORESCENT FIXTURES AND AN 8-AMP CIRCUIT WHEN CONTROLLING LED FIXTURES.

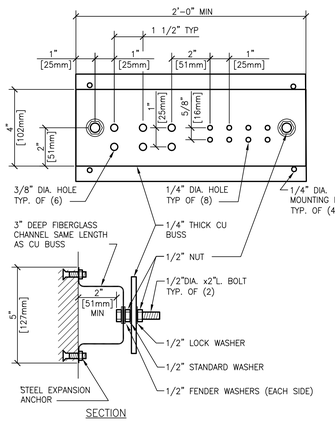

SECTION

11 GROUNDING BAR DETAIL
SCALE: NTS

NOTES
1. ALL HARDWARE SHOWN SHALL BE STAINLESS STEEL.
2. PROVIDE 1 MOUNTING POINT PER 12" OF BAR LENGTH.
3. HOLES MAY BE ADDED IF REQUIRED.

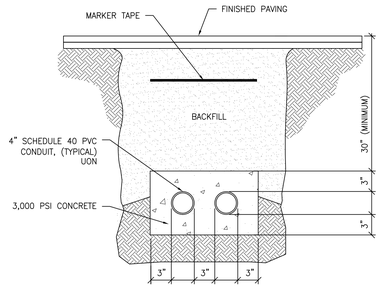

12 TYPICAL CONCRETE ENCASED DUCTBANK SECTION
SCALE: NONE

NOTES:
1. PAVING CONSTRUCTION SHOWN FOR REFERENCE ONLY.

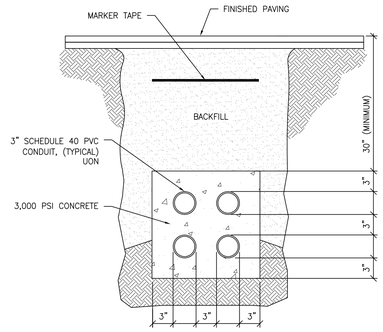

13 TYPICAL CONCRETE ENCASED DUCTBANK SECTION
SCALE: NONE

NOTES:
1. USE THIS DETAIL FOR DUCTBANKS LOCATED UNDER ALL PAVED AREAS OF PARKING LOTS.
2. PAVING CONSTRUCTION SHOWN FOR REFERENCE ONLY.

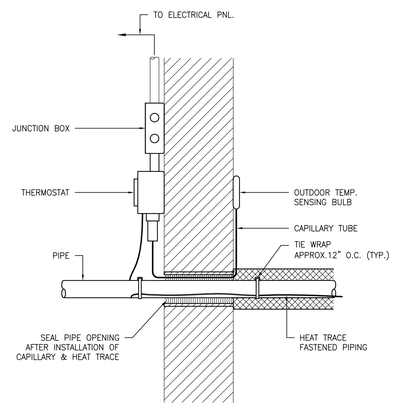

14 HEAT TRACE DETAIL
SCALE: NONE

PRINTS OF THIS DRAWING SHALL NOT BE USED FOR ANY PURPOSE WHATSOEVER WITHOUT THE SEAL AND SIGNATURE OF THE PROFESSIONAL ENGINEER.

NO.	DESCRIPTION	DATE

CONSULTANTS

Architecture:	Civil Engineering:	Fire & Life Safety:
PF&A DESIGN, P.C.	LABELLA ASSOCIATES	STANTON ENGINEERING SERVICES, LLC

ENGINEER OF RECORD

MILLER•REMICK
A Service-Disabled Veteran-Owned Small Business
(856) 429-4000 • Miller-Remick.com
M-R PROJECT NO. 0499-0136

MILLER-REMICK LLC PROFESSIONAL ENGINEER

COMMONWEALTH OF PENNSYLVANIA — REGISTERED PROFESSIONAL — THOMAS REGINO — ENGINEER No. PE094195
12/30/25

Office of Construction and Facilities Management

VA U.S. Department of Veterans Affairs

Drawing Title ELECTRICAL DETAILS	**Phase** BID DOCUMENTS	**Project Title** RENOVATE SURGICAL SUITE PHASE II Project Number 658-19-103	**VA Drawing Number** 2617 **Building Number** 143
Approved by: Jon Manninen, COR	FULLY SPRINKLERED	**Location** SALEM VA MEDICAL CENTER **Issue Date** 2025-12-30 · **Checked** MJR · **Drawn** MJR	**Drawing Number** E-501

VA FORM 08-6231

P:\0499_OVA\0499-0136 Salem Renovate Surgical Suite\4_Drawings\1_Cad\1_Current Submittal Phase\7_Electrical\E-501.dwg 12-29-25 08:25:54 AM MRonco

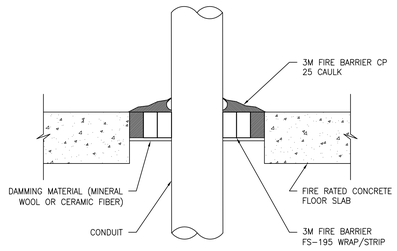

NOTES:
1. THE MAX. ANNULAR SPACE TO BE FILLED IS 3", & THE MIN. ANNULAR SPACE IS 3/4".
2. FS-195 WRAP/STRIPS ARE FRICTION FIT INTO THE OPENING OR SECURED WITH 16 GA. STEEL TIE WIRE OR ALUMINUM FOIL TAPE & SLID INTO THE OPENING WITH A MIN. 1/4" BEAD OF CP 25 CAULK.
3. THE MIN. ANNULAR SPACE MUST ACCOMMODATE THE MIN. NUMBER OF FS-195 WRAP/STIPS REQUIRED PER INSULATION THICKNESS. SEE TABLE 1 BELOW.

TABLE 1

WRAP	CAULK	INSULATION
1 WRAP	1" DEPTH	1" THICK
2 WRAP	2" DEPTH	2" THICK
3 WRAP	3" DEPTH	3" THICK

1 PENETRATION FIRE STOP FOR CONDUIT THROUGH FIRE-RATED FLOOR SLAB
SCALE: NONE

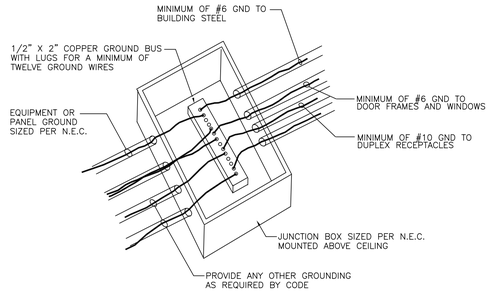

2 REFERENCE GROUNDING POINT DETAIL
SCALE: NONE

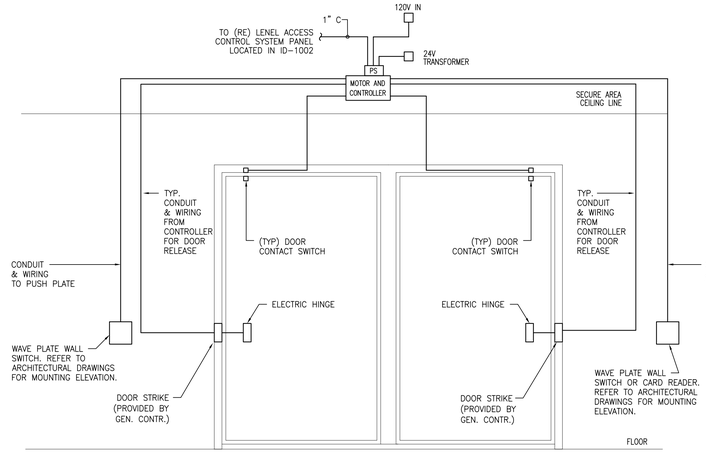

NOTE:
1. EC TO COORDINATE WITH DOOR VENDOR THE REQUIRED DOOR LOCKING HARDWARE.
2. CONDUIT AND WIRE SIZE AS RECOMMENDED BY MANUFACTURER

3 MOTORIZED DOUBLE DOOR DETAIL: PUSH PLATE / PUSH PLATE
SCALE: NONE

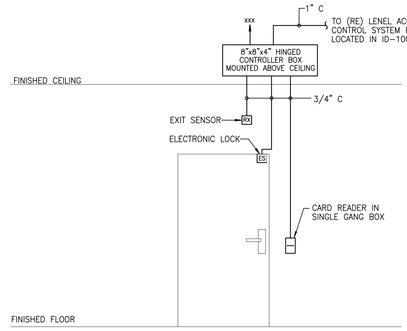

4 SINGLE DOOR CARD ACCESS DETAIL
SCALE: N.T.S.

NOTES:
1. EC TO COORDINATE SHALL PROVIDE CONDUIT, BOXES AND SUPPORTS. COORDINATE AND VERIFY LOCATIONS WITH OWNER.
2. PROVIDE CABLING PER MANUFACTURER'S RECOMMENDATIONS.

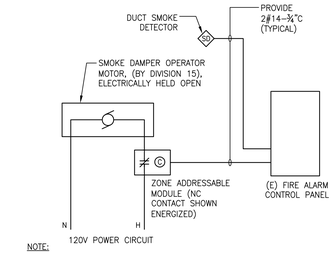

NOTE:
1. ACTIVATION OF DUCT DETECTOR(S) SHALL SIGNAL FIRE ALARM CONTROL PANEL, WHICH WILL THEN SIGNAL RESPECTIVE SMOKE DAMPER ZONE ADDRESSABLE MODEL (ZAM), OPEN ZAM N.C. CONTACT, INTERRUPT POWER TO DAMPER MOTOR AND CAUSE DAMPER TO CLOSE. DAMPER REOPENS ON RESET OF FIRE ALARM SYSTEM.

5 TYPICAL FIRE ALARM/SMOKE DAMPER INTERFACE WIRING DIAGRAM
SCALE: NONE

NOTE:
1. FURNISHED AND INSTALLED BY MECHANICAL CONTRACTOR AND INSTALLED BY ELECTRICAL CONTRACTOR.
2. ALL FIRE/SMOKE DAMPERS SHALL BE PROVIDED WITH END SWITCHES AND OR POSITION ENCODERS WITH A LOW VOLTAGE CONNECTION BACK TO THE BUILDING BMS SYSTEM.

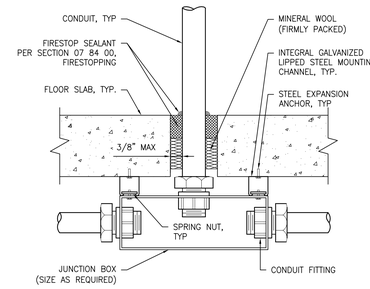

6 FLOOR SLAB PENETRATION DETAIL
SCALE: NTS

DEVICE AND ACCESSORY CHART POSITION FOR POWER/GROUND MODULES				
BACK BOXES	DESCRIPTION	CIRCUIT NUMBER	PANEL NAME	REMARKS
1	3 -30A TWIST-TO-LOCK GROUND JACK RECEPTACLES			BACK BOX #304 STAINLESS STEEL WITH #4 BRUSHED FINISH AND 14 GAUGE STAINLESS STEEL.
2	3 - 20A RED DUPLEX HOSPITAL GRADE RECEPTACLES	DEDICATED	ISOLATION PANEL	
3	2 -30A TWIST-TO-LOCK GROUND JACK RECEPTACLES			BACK BOX #304 STAINLESS STEEL WITH #4 BRUSHED FINISH AND 14 GAUGE STAINLESS STEEL.
4	2 - 20A RED DUPLEX HOSPITAL GRADE RECEPTACLES	DEDICATED	ISOLATION PANEL	
5	4 -30A TWIST-TO-LOCK GROUND JACK RECEPTACLES			BACK BOX #304 STAINLESS STEEL WITH #4 BRUSHED FINISH AND 14 GAUGE STAINLESS STEEL.
6	4 - 20A RED DUPLEX HOSPITAL GRADE RECEPTACLES	DEDICATED	ISOLATION PANEL	

7 POWER GROUND MODULE
SCALE: SCHEMATIC

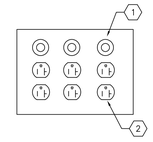

POWER GROUND MODULE TYPE 7A

7A POWER GROUND MODULE
SCALE: SCHEMATIC

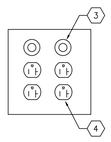

POWER GROUND MODULE TYPE 7B

7B POWER GROUND MODULE
SCALE: SCHEMATIC

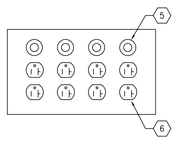

POWER GROUND MODULE TYPE 7C

7C POWER GROUND MODULE
SCALE: SCHEMATIC

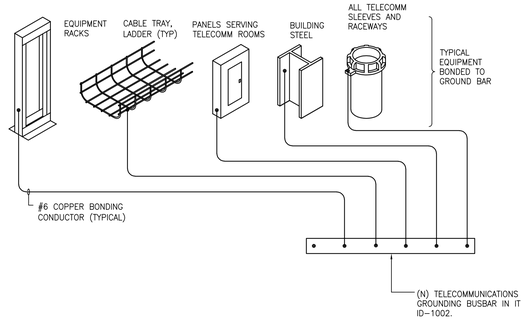

NOTES:
1. ALL BUSBARS SHALL BE 1/4" X 4" X 24" PRE-DRILLED TIN-PLATED COPPER. MOUNT ON WALL WITH 2" STANDOFF INSULATORS.
2. ALL CABLE CONNECTIONS TO GROUND BAR SHALL BE TWO HOLE TONGUE COMPRESSION LUGS.
3. ALL GROUNDING CONDUCTORS SHALL BE COPPER CONDUCTORS WITH GREEN INSULATION OR DISTINCTIVE GREEN MARKING.

8 TELECOMM AND DATA GROUND DIAGRAM
SCALE: SCHEMATIC

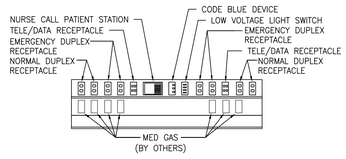

8 HORIZONTAL PATIENT HEADWALL - PACU
SCALE: NONE

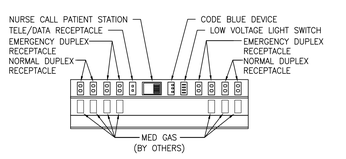

9 HORIZONTAL PATIENT HEADWALL - PRE-OP
SCALE: NONE

POWER GROUND MODULES TO BE MOUNTED 42" A.F.F. UNLESS OTHERWISE NOTED

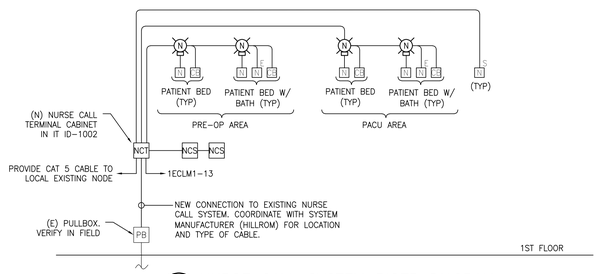

10 NURSE CALL SYSTEM RISER DIAGRAM
SCALE: NONE

PRINTS OF THIS DRAWING SHALL NOT BE USED FOR ANY PURPOSE WHATSOEVER WITHOUT THE SEAL AND SIGNATURE OF THE PROFESSIONAL ENGINEER.

NO.	DESCRIPTION	DATE

CONSULTANTS

Architecture:	Civil Engineering:	Fire & Life Safety:
PF&A DESIGN, P.C.	LABELLA ASSOCIATES	STANTON ENGINEERING SERVICES, LLC

ENGINEER OF RECORD

MILLER•REMICK
A Service-Disabled Veteran-Owned Small Business
(856) 429-4000 • Miller-Remick.com
M-R PROJECT NO: 0499-0136

MILLER-REMICK LLC
PROFESSIONAL ENGINEER
COMMONWEALTH OF PENNSYLVANIA
REGISTERED PROFESSIONAL
THOMAS REGINO
ENGINEER No. PE094195
12/30/25

Office of Construction and Facilities Management

U.S. Department of Veterans Affairs

Drawing Title: ELECTRICAL DETAILS	Phase: BID DOCUMENTS	Project Title: RENOVATE SURGICAL SUITE PHASE II	VA Drawing Number: 2617
Approved by: Jon Manninen, COR	FULLY SPRINKLERED	Project Number: 658-19-103	Building Number: 143
		Location: SALEM VA MEDICAL CENTER	Drawing Number: E-502
		Issue Date: 2025-12-30 / Checked: MJR / Drawn: MJR	

VA FORM 08-6231

P:\0499_OVA\0499-0136 Salem Renovate Surgical Suite\4_Drawings\1_Cad\1_Current Submittal Phase\7_Electrical\E-502.dwg 12-29-25 08:25:51 AM MRonca

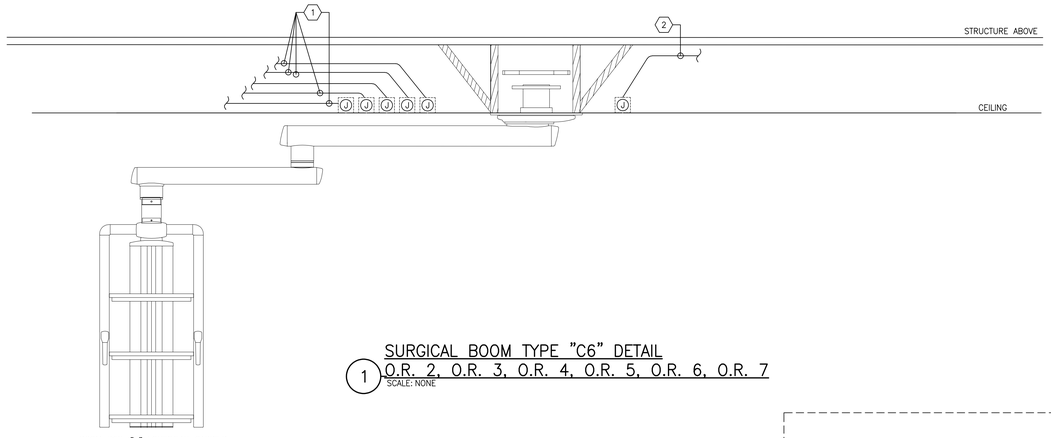

BOOM TYPE "C" EQUIPMENT CARRIER.
SEE DETAIL 2 THIS SHEET FOR
FURTHER INFORMATION.

SURGICAL BOOM TYPE "C6" DETAIL
O.R. 2, O.R. 3, O.R. 4, O.R. 5, O.R. 6, O.R. 7
1 SCALE: NONE

PATHWAY AND WIRING CHART FOR SURGICAL BOOM TYPE "C6"				
EQUIPMENT	DESCRIPTION	CIRCUIT NUMBER	PANEL NAME	REMARKS
1	PROVIDE 2-#10, 1-#10 GND, 3/4" C. FOR EACH SET OF 120VAC CIRCUITS FROM SURGICAL BOOM TO ISOLATION PANEL IPU-#-B	DEDICATED CKT 4,6,8,10 CKT 5	IPU-#-A	CKT 4,6,8,10 ARE RECEPTACLE CIRCUITS. CKT 5 IS FOR THE EMS BRAKING SYSTEM.
2	PROVIDE (1) 1-1/4" CONDUIT FROM ACCESSIBLE CEILING SPACE ABOVE BOOM FOR TELE/DATA WIRING TO EQUIPMENT CARRIER.			DATA CONNECTION TO NEW TELE/DATA RACK IN IT ID-1002

ALL CONDUIT, WIRING, AND OTHER ELECTRICAL MATERIALS AS WELL AS INSTALLATION LABOR FOR SUCH MATERIALS ASSOCIATED WITH THE NEW SURGICAL BOOM TO BE PROVIDED BY ELECTRICAL CONTRACTOR. THE INSTALLATION OF THE NEW SURGICAL BOOM SHOULD BE UNDER THE DIRECT SUPERVISION OF AN EQUIPMENT REPRESENTATIVE. ALL WIRING TO BE IN ACCORDANCE WITH LOCAL CODES.

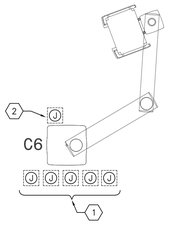

CEILING VIEW

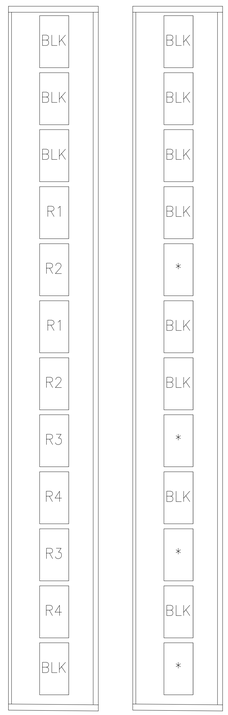

SIDE A

SIDE B

BOOM TYPE "C6" EQUIPMENT CARRIER

DEVICE AND CIRCUITING CHART FOR "C6" BOOM EQUIPMENT CARRIER			
TAG	DESCRIPTION	CIRCUIT NUMBER	PANEL NAME
R1	DUPLEX RECEPTACLE - RED HOSPITAL GRADE 20 AMP	4	IPU-#-A
R2	DUPLEX RECEPTACLE - RED HOSPITAL GRADE 20 AMP	6	IPU-#-A
R3	DUPLEX RECEPTACLE - RED HOSPITAL GRADE 20 AMP	8	IPU-#-A
R4	DUPLEX RECEPTACLE - RED HOSPITAL GRADE 20 AMP	10	IPU-#-A
T/D	VA STANDARD TELE/DATA DEVICE		NEW DATA RACK
BLK	BLANK COVER		
*	DEDICATED TO MED GAS		

BOOM TYPE "C6" EQUIPMENT CARRIER DETAIL
O.R. 2, O.R. 3, O.R. 4, O.R. 5, O.R. 6, O.R. 7
2 SCALE: NONE

GENERAL SURGICAL BOOM NOTES:

1. ALL RECEPTACLES IN COLUMNS AND BOOMS SHALL BE PREWIRED TO JUNCTION BOXES LOCATED AT TOP OF COLUMN.
2. ALL CIRCUITS SHALL CONTAIN SEPARATE PHASE, NEUTRAL, AND GROUND CONDUCTORS. COMBINING OF THREE CIRCUITS WITH A COMMON NEUTRAL IS NOT PERMITTED.
3. ELECTRICAL CONTRACTOR TO ENGRAVE THE PROPER PANEL AND CIRCUIT NUMBER INTO RECEPTACLE FACEPLATES.
4. PROVIDE ADDITIONAL PATHWAYS FOR NURSE CALL AND DATA/TELECOMMUNICATIONS WIRING.
5. ALL INTERNAL WIRING SHALL UTILIZE LOW LEAKAGE XHHW-2, 600V INSULATION.

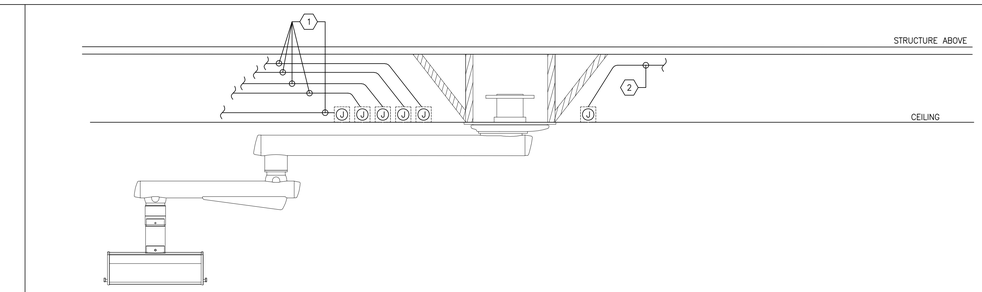

BOOM TYPE "A" EQUIPMENT CARRIER.
SEE DETAIL 4 THIS SHEET FOR
FURTHER INFORMATION.

SURGICAL ANESTHESIA BOOM TYPE "C5" DETAIL
O.R. 2, O.R. 3, O.R. 4, O.R. 5, O.R. 6, O.R. 7
3 SCALE: NONE

PATHWAY AND WIRING CHART FOR SURGICAL BOOM TYPE "C5"				
EQUIPMENT	DESCRIPTION	CIRCUIT NUMBER	PANEL NAME	REMARKS
1	PROVIDE 2-#10, 1-#10 GND, 3/4" C. FOR EACH SET OF 120VAC CIRCUITS FROM SURGICAL BOOM TO ISOLATION PANEL IPU-#-B	DEDICATED CKT 13,14,15,16 CKT 9	IPU-#-A	CKT 13,14,15,16 ARE RECEPTACLE CIRCUITS. CKT 9 IS FOR THE EMS BRAKING SYSTEM.
2	PROVIDE (1) 1-1/4" CONDUIT FROM ACCESSIBLE CEILING SPACE ABOVE BOOM FOR TELE/DATA WIRING TO EQUIPMENT CARRIER.			DATA CONNECTION TO NEW TELE/DATA RACK IN IT ID-1002

ALL CONDUIT, WIRING, AND OTHER ELECTRICAL MATERIALS AS WELL AS INSTALLATION LABOR FOR SUCH MATERIALS ASSOCIATED WITH THE NEW SURGICAL BOOM TO BE PROVIDED BY ELECTRICAL CONTRACTOR. THE INSTALLATION OF THE NEW SURGICAL BOOM SHOULD BE UNDER THE DIRECT SUPERVISION OF AN EQUIPMENT REPRESENTATIVE. ALL WIRING TO BE IN ACCORDANCE WITH LOCAL CODES.

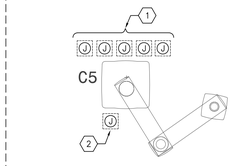

CEILING VIEW

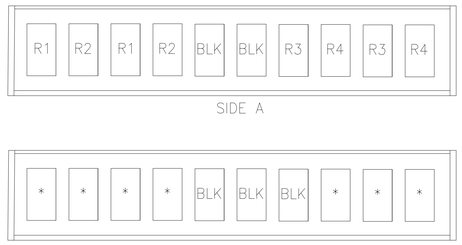

SIDE A

SIDE B

BOOM TYPE "C5" EQUIPMENT CARRIER

DEVICE AND CIRCUITING CHART FOR "C5" BOOM EQUIPMENT CARRIER			
TAG	DESCRIPTION	CIRCUIT NUMBER	PANEL NAME
R1	DUPLEX RECEPTACLE - RED HOSPITAL GRADE 20 AMP	13	IPU-#-A
R2	DUPLEX RECEPTACLE - RED HOSPITAL GRADE 20 AMP	14	IPU-#-A
R3	DUPLEX RECEPTACLE - RED HOSPITAL GRADE 20 AMP	15	IPU-#-A
R4	DUPLEX RECEPTACLE - RED HOSPITAL GRADE 20 AMP	16	IPU-#-A
T/D	VA STANDARD TELE/DATA DEVICE		NEW DATA RACK
BLK	BLANK COVER		
*	DEDICATED TO MED GAS		

ANESTHESIA BOOM TYPE "C5" DETAIL
O.R. 2, O.R. 3, O.R. 4, O.R. 5, O.R. 6, O.R. 7
4 SCALE: NONE

GENERAL SURGICAL BOOM NOTES:

1. ALL RECEPTACLES IN COLUMNS AND BOOMS SHALL BE PREWIRED TO JUNCTION BOXES LOCATED AT TOP OF COLUMN.
2. ALL CIRCUITS SHALL CONTAIN SEPARATE PHASE, NEUTRAL, AND GROUND CONDUCTORS. COMBINING OF THREE CIRCUITS WITH A COMMON NEUTRAL IS NOT PERMITTED.
3. ELECTRICAL CONTRACTOR TO ENGRAVE THE PROPER PANEL AND CIRCUIT NUMBER INTO RECEPTACLE FACEPLATES.
4. PROVIDE ADDITIONAL PATHWAYS FOR NURSE CALL AND DATA/TELECOMMUNICATIONS WIRING.
5. ALL INTERNAL WIRING SHALL UTILIZE LOW LEAKAGE XHHW-2, 600V INSULATION.

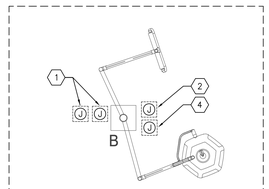

CEILING VIEW

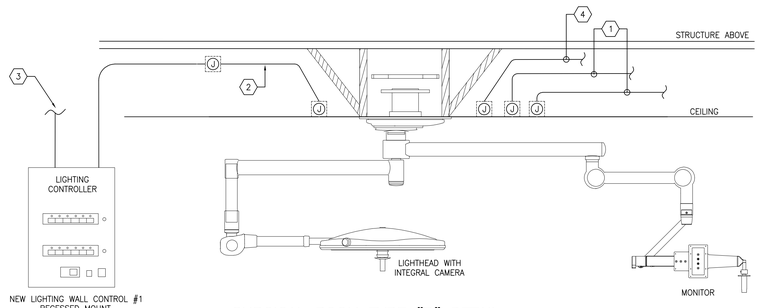

NEW LIGHTING WALL CONTROL #1
RECESSED MOUNT
55" A.F.F.
TERMINATION SHALL BE DUAL BACKBOX -
11 5/8"H x 8.5"W x 4"D BOX OR PER
MANUFACTURER'S RECOMMENDATION.

SURGICAL BOOM TYPE "B" DETAIL
O.R. 2, O.R. 3, O.R. 4, O.R. 5, O.R. 6, O.R. 7
5 SCALE: NONE

PATHWAY AND WIRING CHART FOR SURGICAL BOOM TYPE "B"				
EQUIPMENT	DESCRIPTION	CIRCUIT NUMBER	PANEL NAME	REMARKS
1	PROVIDE ONE JUNCTION BOX TO POWER 120VAC DEDICATED CIRCUIT CONNECTED TO MONITOR. PROVIDE ONE JUNCTION BOX AND 1" C DEDICATED TO DATA WIRING CONNECTION TO MONITOR.	DEDICATED CIRCUIT 11	IPU-#-A AND DATA CONNECTION TO NEW TELE/DATA RACK IN IT ID-1002	1" METAL CONDUIT AND COMMUNICATION WIRING TO MONITOR(S). E.C. TO COORDINATE WITH EQUIPMENT MANUFACTURER DATA WIRING REQUIREMENTS FOR MONITOR(S).
2	3/4" METAL CONDUIT AND WIRING TO LIGHTHEAD. INSTALL 18" OF FLEXIBLE CONDUIT BELOW CEILING. 3-#12 AWG (W, R & BL) AND 1-#12 AWG GND (GREEN)	DEDICATED CIRCUIT 12	IPU-#-A	COMBINE LIGHTING LOW VOLTAGE WIRING WITH OTHER "B" BOOM LOW VOLTAGE WIRING IN JUNCTION BOX. BOTH LIGHTING CIRCUITS SHALL SHARE SAME CONDUIT TO THE LIGHTING CONTROLLER.
3	3/4" METAL CONDUIT AND WIRING INPUT (120 VAC, 20A)	DEDICATED CIRCUIT 12	IPU-#-A	
4	PROVIDE (1) 1-1/4" CONDUIT FROM JUNCTION BOX ABOVE BOOM FOR CAMERA WIRING TO CAMERA CONTROL BOX AT DOCUMENTATION STATION, IF REQUIRED			CAMERA WIRING SHALL BE BY MANUFACTURER.

ALL CONDUIT, WIRING, AND OTHER ELECTRICAL MATERIALS AS WELL AS INSTALLATION LABOR FOR SUCH MATERIALS ASSOCIATED WITH THE NEW SURGICAL BOOM TO BE PROVIDED BY ELECTRICAL CONTRACTOR. THE INSTALLATION OF THE NEW SURGICAL BOOM SHOULD BE UNDER THE DIRECT SUPERVISION OF AN EQUIPMENT REPRESENTATIVE. ALL WIRING TO BE IN ACCORDANCE WITH LOCAL CODES.

PRINTS OF THIS DRAWING SHALL NOT BE USED FOR ANY PURPOSE WHATSOEVER WITHOUT THE SEAL AND SIGNATURE OF THE PROFESSIONAL ENGINEER.

NO.	DESCRIPTION	DATE

CONSULTANTS

Architecture:	Civil Engineering:	Fire & Life Safety:
PF&A DESIGN, P.C.	LABELLA ASSOCIATES	STANTON ENGINEERING SERVICES, LLC

ENGINEER OF RECORD

MILLER-REMICK
A Service-Disabled Veteran-Owned Small Business
(856) 429-4000 • Miller-Remick.com
M-R PROJECT NO. 0499-0136

MILLER-REMICK LLC
PROFESSIONAL ENGINEER

COMMONWEALTH OF PENNSYLVANIA
REGISTERED PROFESSIONAL
THOMAS REGINO
ENGINEER
No. PE084176
12/30/25

Office of Construction and Facilities Management

U.S. Department of Veterans Affairs

Drawing Title: ELECTRICAL O.R. DETAILS	Phase: BID DOCUMENTS	Project Title: RENOVATE SURGICAL SUITE PHASE II	VA Drawing Number: 2617
Approved by: Jon Manninen, COR	FULLY SPRINKLERED	Project Number: 658-19-103	Building Number: 143
		Location: SALEM VA MEDICAL CENTER	Drawing Number: E-503
		Issue Date: 2025-12-30 / Checked: MJR / Drawn: MJR	

P:\0499_DWA\0499-0136 Salem Renovate Surgical Suite\4_Drawings\1_Cad\1_Current Submittal Phase\7_Electrical\E-503.dwg 12-29-25 08:25:46 AM MRenca

VA FORM 08-6231

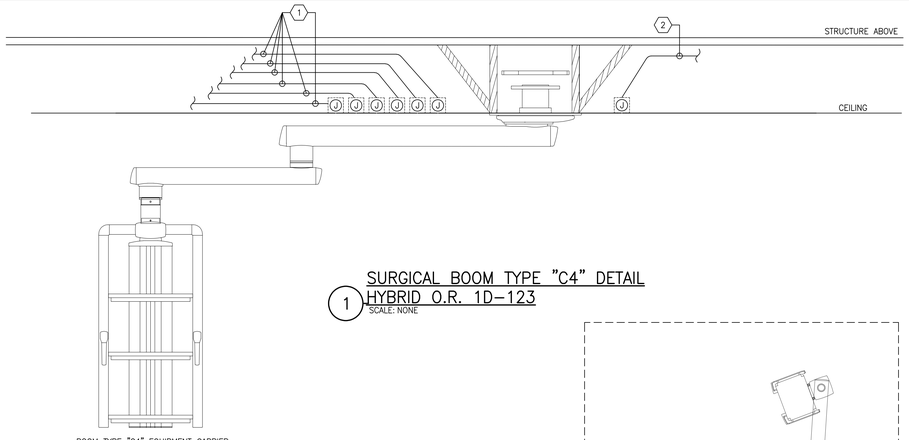

BOOM TYPE "C4" EQUIPMENT CARRIER.
SEE DETAIL 2/THIS SHEET FOR
FURTHER INFORMATION.

1 SURGICAL BOOM TYPE "C4" DETAIL HYBRID O.R. 1D–123

SCALE: NONE

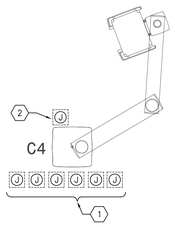

CEILING VIEW

PATHWAY AND WIRING CHART FOR SURGICAL BOOM TYPE "C4"				
EQUIPMENT	DESCRIPTION	CIRCUIT NUMBER	PANEL NAME	REMARKS
1	PROVIDE 2–#10, 1–#10 GND, 3/4" C. FOR EACH SET OF 120VAC CIRCUITS FROM SURGICAL BOOM TO ISOLATION PANEL IPU–H–A	DEDICATED CKT 6,8,10,12,14,16 CKT 15	IPU–H–A	CKT 6,8,10,12,14,16 ARE RECEPTACLE CIRCUITS. CKT 15 IS FOR THE EMS BRAKING SYSTEM.
2	PROVIDE (1) 1–1/4" CONDUIT FROM ACCESSIBLE CEILING SPACE ABOVE BOOM FOR TELE/DATA WIRING TO EQUIPMENT CARRIER.			DATA CONNECTION TO NEW TELE/DATA RACK IN IT ID–1002

ALL CONDUIT, WIRING, AND OTHER ELECTRICAL MATERIALS AS WELL AS INSTALLATION LABOR FOR SUCH MATERIALS ASSOCIATED WITH THE NEW SURGICAL BOOM TO BE PROVIDED BY ELECTRICAL CONTRACTOR. THE INSTALLATION OF THE NEW SURGICAL BOOM SHOULD BE UNDER THE DIRECT SUPERVISION OF AN EQUIPMENT REPRESENTATIVE. ALL WIRING TO BE IN ACCORDANCE WITH LOCAL CODES.

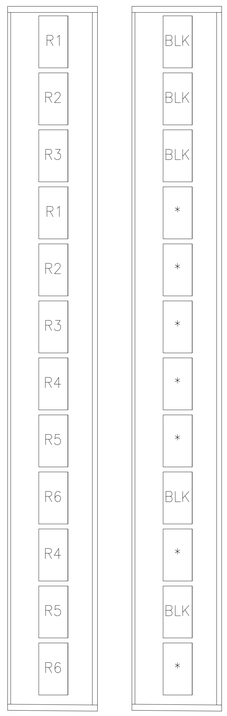

SIDE A

SIDE B

BOOM TYPE "C4" EQUIPMENT CARRIER

DEVICE AND CIRCUITING CHART FOR "C4" BOOM EQUIPMENT CARRIER			
TAG	DESCRIPTION	CIRCUIT NUMBER	PANEL NAME
R1	DUPLEX RECEPTACLE – RED HOSPITAL GRADE 20 AMP	6	IPU–H–A
R2	DUPLEX RECEPTACLE – RED HOSPITAL GRADE 20 AMP	8	IPU–H–A
R3	DUPLEX RECEPTACLE – RED HOSPITAL GRADE 20 AMP	10	IPU–H–A
R4	DUPLEX RECEPTACLE – RED HOSPITAL GRADE 20 AMP	12	IPU–H–A
R5	DUPLEX RECEPTACLE – RED HOSPITAL GRADE 20 AMP	14	IPU–H–A
R6	DUPLEX RECEPTACLE – RED HOSPITAL GRADE 20 AMP	16	IPU–H–A
T/D	VA STANDARD TELE/DATA DEVICE		NEW DATA RACK
BLK	BLANK COVER		
*	DEDICATED TO MED GAS		

2 BOOM TYPE "C4" EQUIPMENT CARRIER DETAIL HYBRID O.R. 1D–123

SCALE: NONE

GENERAL SURGICAL BOOM NOTES:

1. ALL RECEPTACLES IN COLUMNS AND BOOMS SHALL BE PREWIRED TO JUNCTION BOXES LOCATED AT TOP OF COLUMN.
2. ALL CIRCUITS SHALL CONTAIN SEPARATE PHASE, NEUTRAL, AND GROUND CONDUCTORS. COMBINING OF THREE CIRCUITS WITH A COMMON NEUTRAL IS NOT PERMITTED.
3. ELECTRICAL CONTRACTOR TO ENGRAVE THE PROPER PANEL AND CIRCUIT NUMBER INTO RECEPTACLE FACEPLATES.
4. PROVIDE ADDITIONAL PATHWAYS FOR NURSE CALL AND DATA/TELECOMMUNICATIONS WIRING.
5. ALL INTERNAL WIRING SHALL UTILIZE LOW LEAKAGE XHHW–2, 600V INSULATION.

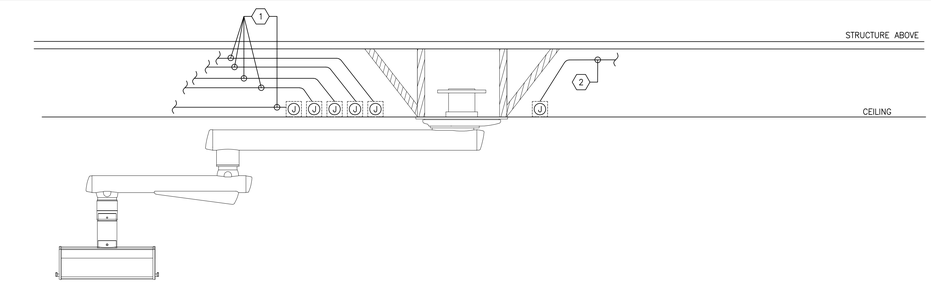

BOOM TYPE "C3" EQUIPMENT CARRIER.
SEE DETAIL 4/THIS SHEET FOR
FURTHER INFORMATION.

3 SURGICAL ANESTHESIA BOOM TYPE "C3" DETAIL HYBRID O.R. 1D–123

SCALE: NONE

PATHWAY AND WIRING CHART FOR SURGICAL BOOM TYPE "C3"				
EQUIPMENT	DESCRIPTION	CIRCUIT NUMBER	PANEL NAME	REMARKS
1	PROVIDE 2–#10, 1–#10 GND, 3/4" C. FOR EACH SET OF 120VAC CIRCUITS FROM SURGICAL BOOM TO ISOLATION PANEL IPU–H–A	DEDICATED CKT 7,9,11,13 CKT 15	IPU–H–A	CKT 7,9,11,13 ARE RECEPTACLE CIRCUITS. CKT 15 IS FOR THE EMS BRAKING SYSTEM.
2	PROVIDE (1) 1–1/4" CONDUIT FROM ACCESSIBLE CEILING SPACE ABOVE BOOM FOR TELE/DATA WIRING TO EQUIPMENT CARRIER.			DATA CONNECTION TO NEW TELE/DATA RACK IN IT ID–1002

ALL CONDUIT, WIRING, AND OTHER ELECTRICAL MATERIALS AS WELL AS INSTALLATION LABOR FOR SUCH MATERIALS ASSOCIATED WITH THE NEW SURGICAL BOOM TO BE PROVIDED BY ELECTRICAL CONTRACTOR. THE INSTALLATION OF THE NEW SURGICAL BOOM SHOULD BE UNDER THE DIRECT SUPERVISION OF AN EQUIPMENT REPRESENTATIVE. ALL WIRING TO BE IN ACCORDANCE WITH LOCAL CODES.

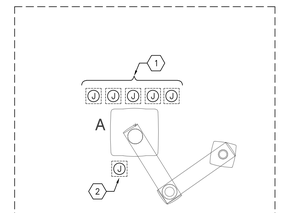

CEILING VIEW

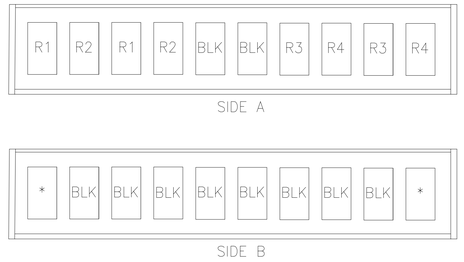

SIDE A

SIDE B

BOOM TYPE "C3" EQUIPMENT CARRIER

DEVICE AND CIRCUITING CHART FOR "C3" BOOM EQUIPMENT CARRIER			
TAG	DESCRIPTION	CIRCUIT NUMBER	PANEL NAME
R1	DUPLEX RECEPTACLE – RED HOSPITAL GRADE 20 AMP	7	IPU–H–A
R2	DUPLEX RECEPTACLE – RED HOSPITAL GRADE 20 AMP	9	IPU–H–A
R3	DUPLEX RECEPTACLE – RED HOSPITAL GRADE 20 AMP	11	IPU–H–A
R4	DUPLEX RECEPTACLE – RED HOSPITAL GRADE 20 AMP	13	IPU–H–A
T/D	VA STANDARD TELE/DATA DEVICE		NEW DATA RACK
BLK	BLANK COVER		
*	DEDICATED TO MED GAS		

4 ANESTHESIA BOOM TYPE "C3" DETAIL HYBRID O.R. 1D–123

SCALE: NONE

GENERAL SURGICAL BOOM NOTES:

1. ALL RECEPTACLES IN COLUMNS AND BOOMS SHALL BE PREWIRED TO JUNCTION BOXES LOCATED AT TOP OF COLUMN.
2. ALL CIRCUITS SHALL CONTAIN SEPARATE PHASE, NEUTRAL, AND GROUND CONDUCTORS. COMBINING OF THREE CIRCUITS WITH A COMMON NEUTRAL IS NOT PERMITTED.
3. ELECTRICAL CONTRACTOR TO ENGRAVE THE PROPER PANEL AND CIRCUIT NUMBER INTO RECEPTACLE FACEPLATES.
4. PROVIDE ADDITIONAL PATHWAYS FOR NURSE CALL AND DATA/TELECOMMUNICATIONS WIRING.
5. ALL INTERNAL WIRING SHALL UTILIZE LOW LEAKAGE XHHW–2, 600V INSULATION.

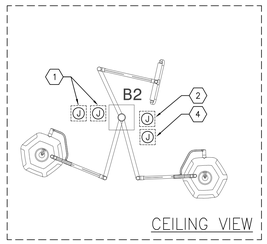

CEILING VIEW

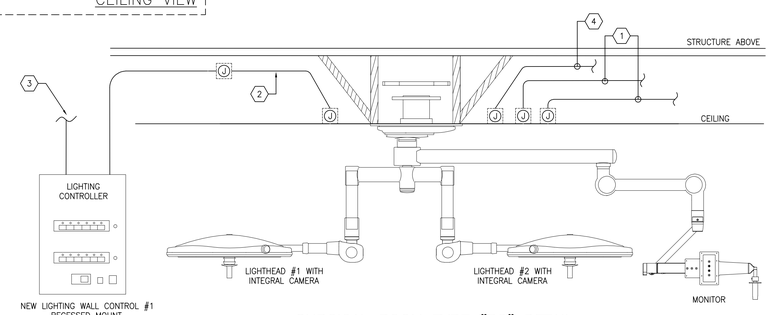

NEW LIGHTING WALL CONTROL #1
RECESSED MOUNT
55" A.F.F.
TERMINATION SHALL BE DUAL BACKBOX –
11 5/8"H x 8.5"W x 4"D BOX OR PER
MANUFACTURER'S RECOMMENDATION.

5 SURGICAL BOOM TYPE "B2" DETAIL HYBRID O.R. 1D–123

SCALE: NONE

PATHWAY AND WIRING CHART FOR SURGICAL BOOM TYPE "B"				
EQUIPMENT	DESCRIPTION	CIRCUIT NUMBER	PANEL NAME	REMARKS
1	PROVIDE ONE JUNCTION BOX TO POWER 120VAC DEDICATED CIRCUIT CONNECTED TO MONITOR. PROVIDE ONE JUNCTION BOX AND 1" C DEDICATED TO DATA WIRING CONNECTION TO MONITOR.	DEDICATED CIRCUIT 4	IPU–H–A AND DATA CONNECTION TO NEW TELE/DATA RACK IN IT ID–1002	1" METAL CONDUIT AND COMMUNICATION WIRING TO MONITOR(S). E.C. TO COORDINATE WITH EQUIPMENT MANUFACTURER DATA WIRING REQUIREMENTS FOR MONITOR(S).
2	3/4" METAL CONDUIT AND WIRING TO LIGHTHEAD. INSTALL 18" OF FLEXIBLE CONDUIT BELOW CEILING. 3–#12 AWG (W, R & BL) AND 1–#12 AWG GND (GREEN)	DEDICATED CIRCUIT 2	IPU–H–A	COMBINE LIGHTING LOW VOLTAGE WIRING WITH "B1" BOOM LOW VOLTAGE WIRING IN JUNCTION BOX. BOTH LIGHTING CIRCUITS SHALL SHARE SAME CONDUIT TO THE LIGHTING CONTROLLER.
3	3/4" METAL CONDUIT AND WIRING INPUT (120 VAC, 20A)	DEDICATED CIRCUIT 2	IPU–H–A	
4	PROVIDE (1) 1–1/4" CONDUIT FROM JUNCTION BOX ABOVE BOOM FOR CAMERA WIRING TO CAMERA CONTROL BOX AT DOCUMENTATION STATION, IF REQUIRED			CAMERA WIRING SHALL BE BY MANUFACTURER.

ALL CONDUIT, WIRING, AND OTHER ELECTRICAL MATERIALS AS WELL AS INSTALLATION LABOR FOR SUCH MATERIALS ASSOCIATED WITH THE NEW SURGICAL BOOM TO BE PROVIDED BY ELECTRICAL CONTRACTOR. THE INSTALLATION OF THE NEW SURGICAL BOOM SHOULD BE UNDER THE DIRECT SUPERVISION OF AN EQUIPMENT REPRESENTATIVE. ALL WIRING TO BE IN ACCORDANCE WITH LOCAL CODES.

PRINTS OF THIS DRAWING SHALL NOT BE USED FOR ANY PURPOSE WHATSOEVER WITHOUT THE SEAL AND SIGNATURE OF THE PROFESSIONAL ENGINEER.

NO.	DESCRIPTION	DATE

CONSULTANTS

Architecture:	Civil Engineering:	Fire & Life Safety:
PF&A DESIGN, P.C.	LABELLA ASSOCIATES	STANTON ENGINEERING SERVICES, LLC

ENGINEER OF RECORD

MILLER•REMICK

A Service-Disabled Veteran-Owned Small Business

(856) 429-4000 ★ Miller-Remick.com

M-R PROJECT NO: 0499-0156

MILLER-REMICK LLC
PROFESSIONAL ENGINEER

COMMONWEALTH OF PENNSYLVANIA
REGISTERED PROFESSIONAL
THOMAS REGINO
ENGINEER
12/30/25

Office of Construction and Facilities Management

VA U.S. Department of Veterans Affairs

Drawing Title: ELECTRICAL HYBRID O.R. DETAILS	Phase: BID DOCUMENTS	Project Title: RENOVATE SURGICAL SUITE PHASE II	VA Drawing Number: 2617
Approved by: Jon Manninen, COR	FULLY SPRINKLERED	Project Number: 658-19-103	Building Number: 143
		Location: SALEM VA MEDICAL CENTER	Drawing Number: E-504
		Issue Date: 2025-12-30 / Checked: MJR / Drawn: MJR	

VA FORM 08-6231

P:\0499_DVA\0499-0156 Salem Renovate Surgical Suite\4_Drawings\1_CadV\1_Current Submittal Phase\7_Electrical\E-504.dwg 12-29-25 08:25:41 AM MRonca

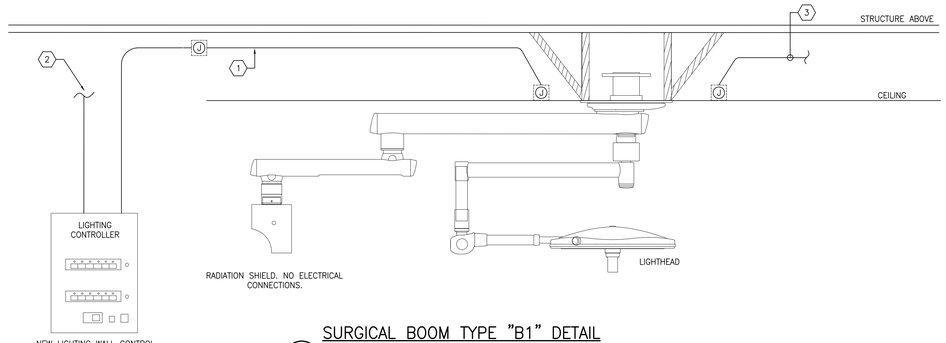

1 SURGICAL BOOM TYPE "B1" DETAIL HYBRID O.R. 1D-123

SCALE: NONE

PATHWAY AND WIRING CHART FOR SURGICAL BOOM TYPE "B1"				
EQUIPMENT	DESCRIPTION	CIRCUIT NUMBER	PANEL NAME	REMARKS
1	3/4" METAL CONDUIT AND WIRING TO LIGHTHEAD. INSTALL 18" OF FLEXIBLE CONDUIT BELOW CEILING. 3-#12 AWG (W, R & BL) AND 1-#12 AWG GND (GREEN)	DEDICATED CIRCUIT 2	IPU-H-A	*2 DEDICATED CONDUIT RUNS REQUIRED AT WALL CONTROL TO SEPARATE 100-240VAC INPUT LINES FROM DC OUTPUT LINES TO LIGHT FIXTURE TO PREVENT THE MIGRATION OF ELECTRICAL MAGNETIC INTERFERENCE WHICH WILL DISRUPT THE OPERATION OF THE LIGHT.
2	3/4" METAL CONDUIT AND WIRING INPUT (120 VAC, 20A)	DEDICATED CIRCUIT 2	IPU-H-A	
3	PROVIDE (1) 1-1/4" CONDUIT FROM JUNCTION BOX ABOVE BOOM FOR CAMERA WIRING TO CAMERA CONTROL BOX AT DOCUMENTATION STATION			PROVIDE JUNCTION BOX AND CONDUIT FOR CAMERA IN BOOM. CAMERA WIRING SHALL BE BY MANUFACTURER.

ALL CONDUIT, WIRING, AND OTHER ELECTRICAL MATERIALS AS WELL AS INSTALLATION LABOR FOR SUCH MATERIALS ASSOCIATED WITH THE NEW SURGICAL BOOM TO BE PROVIDED BY ELECTRICAL CONTRACTOR. THE INSTALLATION OF THE NEW SURGICAL BOOM SHOULD BE UNDER THE DIRECT SUPERVISION OF AN EQUIPMENT REPRESENTATIVE. ALL WIRING TO BE IN ACCORDANCE WITH LOCAL CODES.

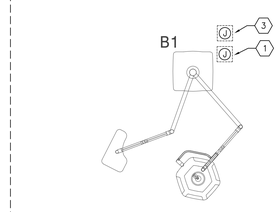

CEILING VIEW

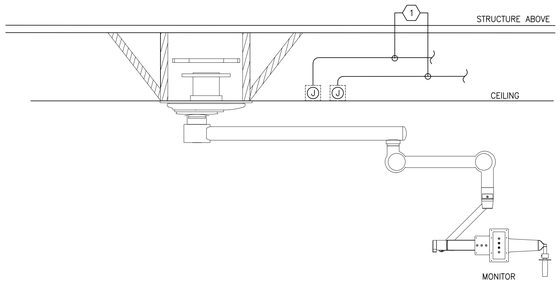

2 SURGICAL BOOM TYPES "C1" AND "C2" DETAIL HYBRID O.R. 1D-123

SCALE: NONE

PATHWAY AND WIRING CHART FOR SURGICAL BOOM TYPE "C1" OR "C2"				
EQUIPMENT	DESCRIPTION	CIRCUIT NUMBER	PANEL NAME	REMARKS
1	PROVIDE ONE JUNCTION BOX TO POWER 120VAC DEDICATED CIRCUIT CONNECTED TO MONITOR. PROVIDE ONE JUNCTION BOX AND 1" C DEDICATED TO DATA WIRING CONNECTION TO MONITOR.	DEDICATED "C1"-CIRCUIT 3 "C2"-CIRCUIT 5	IPU-H-A AND DATA CONNECTION TO NEW TELE/DATA RACK IN IT ID-1002	1" METAL CONDUIT AND COMMUNICATION WIRING TO MONITOR(S). E.C. TO COORDINATE WITH EQUIPMENT MANUFACTURER DATA WIRING REQUIREMENTS FOR MONITOR(S).

ALL CONDUIT, WIRING, AND OTHER ELECTRICAL MATERIALS AS WELL AS INSTALLATION LABOR FOR SUCH MATERIALS ASSOCIATED WITH THE NEW SURGICAL BOOM TO BE PROVIDED BY ELECTRICAL CONTRACTOR. THE INSTALLATION OF THE NEW SURGICAL BOOM SHOULD BE UNDER THE DIRECT SUPERVISION OF AN EQUIPMENT REPRESENTATIVE. ALL WIRING TO BE IN ACCORDANCE WITH LOCAL CODES.

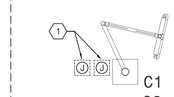

CEILING VIEW

PRINTS OF THIS DRAWING SHALL NOT BE USED FOR ANY PURPOSE WHATSOEVER WITHOUT THE SEAL AND SIGNATURE OF THE PROFESSIONAL ENGINEER.

NO.	DESCRIPTION	DATE

CONSULTANTS

Architecture:	Civil Engineering:	Fire & Life Safety:
PF&A DESIGN, P.C.	LABELLA ASSOCIATES	STANTON ENGINEERING SERVICES, LLC

ENGINEER OF RECORD

MILLER•REMICK
A Service-Disabled Veteran-Owned Small Business
(856) 429-4000 ▪ Miller-Remick.com
M-R PROJECT NO. 24VA10499

MILLER-REMICK LLC
PROFESSIONAL ENGINEER

COMMONWEALTH OF PENNSYLVANIA
REGISTERED PROFESSIONAL ENGINEER
THOMAS REGINO
ENGINEER
No. PE054195
12/30/25

Office of Construction and Facilities Management

VA U.S. Department of Veterans Affairs

Drawing Title: ELECTRICAL HYBRID O.R. DETAILS

Approved by: Jon Manninen, COR

Phase: BID DOCUMENTS

FULLY SPRINKLERED

Project Title: RENOVATE SURGICAL SUITE PHASE II
Project Number: 658-19-103

Location: SALEM VA MEDICAL CENTER

Issue Date: 2025-12-30
Checked: MJR
Drawn: MJR

VA Drawing Number: 2617
Building Number: 143
Drawing Number: E-505

VA FORM 08-6231

P:\10499_DVA\10499-0136 Salem Renovate Surgical Suite\4_Drawings\1_Cad\1_Current Submittal Phase\7_Electrical\E-505.dwg 12-29-25 08:25:37 AM MRonca

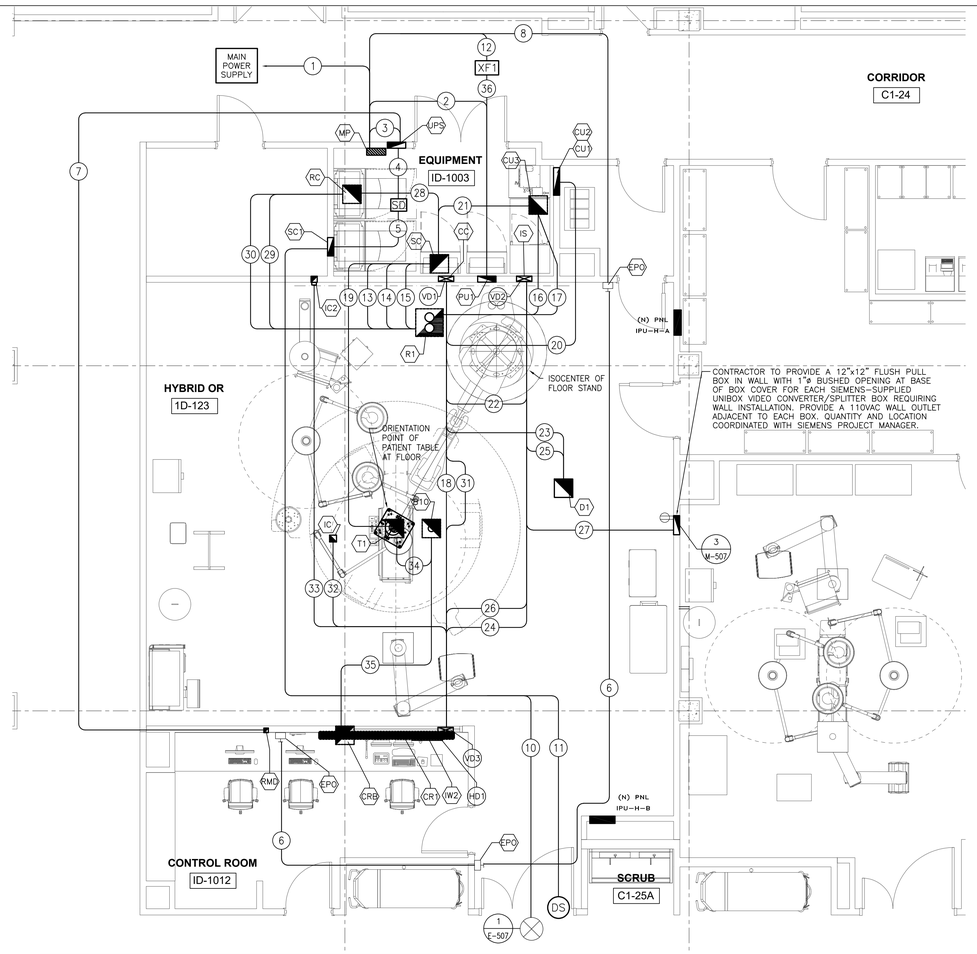

CONTRACTOR SUPPLIED CABLES

FROM	VIA	TO	DESCRIPTION	REMARKS
PANEL	1	MP	ELECTRICAL CONTRACTOR TO SIZE PLUS GROUND	SEE "POWER SCHEDULE" & E-602
MP	2	PU1	3#2, 1#2 GROUND AND CONNECT	SEE "POWER SCHEDULE"
MP	3	UPS	ELECTRICAL CONTRACTOR TO SIZE	SEE "POWER SCHEDULE"
UPS	4	SD	ELECTRICAL CONTRACTOR TO SIZE PLUS GROUND	SEE "POWER SCHEDULE"
SD	5	SC1	ELECTRICAL CONTRACTOR TO SIZE PLUS GROUND (MAX #6 AWG)	SEE "POWER SCHEDULE"
UPS	6	EPO	ELECTRICAL CONTRACTOR TO SIZE	SEE "POWER SCHEDULE"
RMD	7	UPS	CAT 5 NETWORK CABLE, UP TO 328'	SEE "POWER SCHEDULE"
MP	8	EPO	ELECTRICAL CONTRACTOR TO SIZE	SEE "POWER SCHEDULE"
EPO	9	EPO	4#12, PLUS GROUND	EMERGENCY POWER
SC1	10	WL	14-18 AWG	SEE "LIGHTING DETAIL" SHEET E-507
SC1	11	DS	3#12, PLUS GROUND	DOOR SWITCH
MP	12	XF1	EC TO SIZE (OPTIONAL TABLE POWER OUTLET)	SEE "POWER SCHEDULE"

SIEMENS SUPPLIED CABLES

FROM	VIA	TO	DESCRIPTION	REMARKS
R1	13, SC	PU1		MAXIMUM LENGTH 52'
R1	14, SC	PU1	(2) HIGH VOLTAGE CABLES	MAXIMUM LENGTH 52'
R1	15, SC	SC1		MAXIMUM LENGTH 52'
R1	16, CU3	CU1	LIQUID COOLING HOSES	MAXIMUM LENGTH 91'
R1	17, CU3	CU2	LIQUID COOLING HOSES	MAXIMUM LENGTH 52'
SC1	18, VD1, VD3, HD1	CR1	FOR CONTROL ROOM OPTIONS (CONTROL MODULES, FOOT SWITCH, DISPLAY, ECG)	MAXIMUM LENGTH 62'
SC1	19, SC	T1		MAXIMUM LENGTH 45'
SC1	20, VD1	CU1		MAXIMUM LENGTH 98'
SC1	21, SC2	CU3		MAXIMUM LENGTH 32'
SC1	22, VD1, VD2	IS		MAXIMUM LENGTH 26'
SC1	23, VD1	D1		MAXIMUM LENGTH 62'
IS	24, VD2, VD3	CR1		MAXIMUM LENGTH 59'
IS	25, VD2	D1	DCS LARGE DISPLAY (STANDARD CABLE)	MAXIMUM LENGTH 82'
IS	26, VD2	VD3	CUSTOMER LD INPUTS IN CONTROL ROOM	MAXIMUM LENGTH 118'
IS	27, VD2	CUSTOMER SOURCES	CUSTOMER LD INPUTS IN PROCEDURE ROOM	MAXIMUM LENGTH 118'
SC1	28, SC	RC		MAXIMUM LENGTH 32'
RC	29	R1		MAXIMUM LENGTH 44'
RC	30	R1		MAXIMUM LENGTH 44'
SC1	31, VD1, VD3, HD1	IW2	2ND OPERATION/INJECTOR CONNECTION (CONTROL ROOM)	MAXIMUM LENGTH 62'
VD3	32	IC	INTERCOM PROCEDURE ROOM MICROPHONE	MAXIMUM LENGTH 82'
VD3	33	IC2	INTERCOM PROCEDURE ROOM LOUDSPEAKER	MAXIMUM LENGTH 82'
T1	34	B10		
CRB	35	B10	CUSTOMER PATIENT MONITORING, ETC.	
XF1	36, SC1, CONDUIT 18	T1	OPTIONAL TABLE POWER OUTLET	MAXIMUM LENGTH 91'

SYMBOLS

ALL MAY NOT APPLY

	CIRCUIT BREAKER BY CUSTOMER/CONTRACTOR
	OPENING IN RACEWAY OR TRENCHDUCT
	PULLBOX IN (FLOOR/WALL/CEILING)
	OPENING IN ACCESS FLOORING
	WARNING LIGHT (X-RAY ON)
DS	DOOR SAFETY SWITCH
	(EPO) EMERGENCY POWER OFF BUTTON
	TRENCHDUCT
	CEILING DUCT
	UNDER FLOOR DUCT
	SURFACE DUCT
	VERTICAL DUCT
	ETHERNET CONNECTION TO CUSTOMER'S INFORMATION SYSTEMS NETWORK (VERIFY WITH SMS PROJECT MANAGER).
	110 VOLT, 20 AMP, HOSPITAL GRADE DUPLEX OUTLET
	110 VOLT, 20 AMP, HOSPITAL GRADE QUAD OUTLET

ELECTRICAL LEGEND

SYM	SIZE	DESCRIPTION SUPPLIED AND INSTALLED BY CUSTOMER/CONTRACTOR	REMARKS
B10	AS REQUIRED	PULL BOX MOUNTED BELOW FINISHED FLOOR WITH REMOVABLE BOTTOM COVER. PROVIDE 4"ø SLEEVE FROM BOX TO FLUSH WITH FINISHED FLOOR. PROVIDE STAINLESS STEEL WATERPROOF PLATE ON TOP OF CORED OPENING IN FLOOR.	TABLE, ACCESSORIES
CC	10"x8"	BUSHED OPENING IN VERTICAL DUCT "VD1" COVER AT FLOOR LINE.	CABLE CABINET
CR1	3"ø	BUSHED OPENING IN TOP OF HORIZONTAL DUCT "HD1".	CONTROL ROOM DISTRIBUTOR
CRB	AS REQUIRED	PULL BOX MOUNTED BELOW FINISHED FLOOR WITH REMOVABLE BOTTOM COVER. PROVIDE (2) 4" CONDUITS THRU FLOOR. E.C. TO DESIGN TRANSITION TO SURFACE FLOOR DUCT AS REQUIRED.	CONTROL ROOM UNDER-FLOOR BOX
CU1	AS REQUIRED	PULL BOX MOUNTED FLUSH IN FINISHED WALL AT FLOOR LINE. PROVIDE BOX WITH REMOVABLE FRONT COVER AND (1) 4"ø BUSHING IN CENTER OF REMOVABLE COVER FOR CABLE EXIT. SEE PLAN FOR LOCATION.	TUBE COOLING UNIT
CU2	---	FIXED POINT DESIGNATION, SAME BOX AS "CU1".	FD COOLING UNIT
CU3	AS REQUIRED	PULL BOX MOUNTED BELOW FINISHED FLOOR WITH REMOVABLE BOTTOM COVER. PROVIDE 5"ø SLEEVE FROM BOX TO FLUSH WITH FINISHED FLOOR WITH BUSHING AT FLOOR LINE.	COOLING UNITS
D1	AS REQUIRED	PULL BOX MOUNTED ABOVE FINISHED CEILING WITH REMOVABLE BOTTOM COVER WITH 4"ø BUSHED OPENING.	LARGE DISPLAY
EPO	---	EMERGENCY OFF BUTTONS FOR CIRCUIT BREAKERS. EPO'S MUST PREVENT RESETTING OF CIRCUIT BREAKERS WHEN IN OFF POSITION. EPO'S MUST BE RECESSED OR SHIELDED. FINAL LOCATION DETERMINED BY CUSTOMER.	EMERGENCY POWER OFF
IC	---	PULL BOX MOUNTED FLUSH IN FINISHED CEILING IN LOCATION COORDINATED WITH INTERCOM INSTALLATION. PROVIDE REMOVABLE BOTTOM COVER WITH 3/4"ø BUSHED OPENING.	INTERCOM MIC
IC2	AS REQUIRED	PULL BOX MOUNTED FLUSH IN FINISHED WALL AT A RECOMMENDED HEIGHT OF 6' AFF.	INTERCOM LOUDSPEAKER
IS	5"ø	BUSHED OPENING IN VERTICAL DUCT "VD2" COVER AT FLOOR LINE.	IMAGE SYSTEM
IW2	3"ø	BUSHED OPENING IN TOP OF HORIZONTAL DUCT "HD1".	CONTROL RM INJ/CONTROLS
MP	---	MAIN PANEL WITH MAIN BREAKER. LOCATION DETERMINED BY CUSTOMER/CONTRACTOR. SEE "POWER SCHEDULE" ON DRAWING E-507.	BREAKER PANEL
PU1	AS REQUIRED	PULL BOX MOUNTED FLUSH IN FINISHED WALL AT FLOOR LINE. PROVIDE BOX WITH REMOVABLE FRONT COVER WITH 4"ø BUSHED OPENING AT BOTTOM OF COVER.	GENERATOR
R1	AS REQUIRED	PULL BOX MOUNTED BELOW FINISHED FLOOR WITH REMOVABLE BOTTOM COVER. PROVIDE (2) 6"ø SLEEVES FROM BOX TO FLUSH WITH FINISHED FLOOR WITH BUSHING AT FLOOR LINE.	FLOOR STAND
RC	AS REQUIRED	PULL BOX MOUNTED BELOW FINISHED FLOOR WITH REMOVABLE BOTTOM COVER. PROVIDE 6"ø SLEEVE FROM BOX TO FLUSH WITH FINISHED FLOOR WITH BUSHING AT FLOOR LINE.	FLOOR STAND CABINET
RMD	AS REQUIRED	SINGLE-GANG RJ45 JACK	UPS REMOTE DISPLAY
SC1	AS REQUIRED	PULL BOX MOUNTED FLUSH IN FINISHED WALL AT FLOOR LINE. PROVIDE BOX WITH REMOVABLE FRONT COVER WITH 4"ø BUSHED OPENING AT BOTTOM OF COVER.	SYSTEM CABINET
SC	AS REQUIRED	PULL BOX MOUNTED BELOW FINISHED FLOOR WITH REMOVABLE BOTTOM COVER. PROVIDE (2) 6"ø SLEEVES FROM BOX TO FLUSH WITH FINISHED FLOOR WITH BUSHINGS AT FLOOR LINE.	SYSTEM CABINET
T1	AS REQUIRED	PULL BOX MOUNTED BELOW FINISHED FLOOR WITH REMOVABLE BOTTOM COVER. IF LOCAL CODE ALLOWS, PROVIDE 3"ø BARE CONCRETE CORE THRU SLAB FROM BOX TO FINISHED FLOOR. OTHERWISE, PROVIDE A 6"ø CONDUIT THRU SLAB FROM BOX WITH A CONDUIT BUSHING FLUSH WITH FINISHED FLOOR. CONTACT SIEMENS PROJECT MANAGER.	TABLE
UPS	AS REQUIRED	PULL BOX MOUNTED FLUSH IN FINISHED WALL AT FLOOR LINE. PROVIDE BOX WITH REMOVABLE FRONT COVER WITH 4"ø BUSHED OPENING.	15KVA UPS
XF1	750VA	STEP-DOWN TRANSFORMER. SEE POWER SCHEDULE ON DRAWING E-507.	XFMR FOR TABLE OUTLET
HD1	3 1/2"x10"	HORIZONTAL DUCT MOUNTED ON FINISHED WALL AT FLOOR LINE. PROVIDE DUCT WITH REMOVABLE FRONT COVER. CONNECT TO VERTICAL DUCT "VD2" AS SHOWN.	HORIZONTAL WALL DUCT
VD1 VD2 VD3	3 1/2"x10"	VERTICAL DUCT MOUNTED FLUSH IN FINISHED WALL. BEGIN DUCT AT FLOOR LINE AND EXTEND UP WALL ABOVE FINISHED CEILING. PROVIDE JUNCTION BOX (SIZED BY E.C.) AT TOP OF DUCT FOR CONDUIT TRANSITIONS.	VERTICAL DUCT
1	EC TO SIZE	CONDUIT FROM PANEL TO "MP"	SEE "POWER SCHEDULE"
2	EC TO SIZE	CONDUIT FROM "MP" TO "PU1"	SEE "POWER SCHEDULE"
3	EC TO SIZE	CONDUIT FROM "MP" TO "UPS" WITH FLEX CONDUIT FROM UPS BOX TO UPS CABINET.	SEE "POWER SCHEDULE"
4	EC TO SIZE	CONDUIT FROM "UPS" TO "SD" WITH FLEX CONDUIT FROM UPS BOX TO XFMR CABINET.	SEE "POWER SCHEDULE"
5	EC TO SIZE	CONDUIT FROM "SD" TO "SC1".	SEE "POWER SCHEDULE"
6	3/4"ø	CONDUIT FROM "UPS" TO "EPO" WITH FLEX CONDUIT FROM UPS BOX TO UPS CABINET.	SEE "POWER SCHEDULE"
7	3/4"ø	CONDUIT FROM "RMD" TO "UPS"	SEE "POWER SCHEDULE"
8	3/4"ø	CONDUIT FROM "MP" TO "EPO"	SEE "POWER SCHEDULE"
9	EC TO SIZE	CONDUIT FROM "EPO" TO "EPO"	
10	EC TO SIZE	CONDUIT FROM "SC1" TO "WL"	
11	EC TO SIZE	CONDUIT FROM "SC1" TO "DS"	
12	EC TO SIZE	CONDUIT FROM "MP" TO "XF1" (OPTIONAL)	TABLE POWER OUTLET
13	2"ø	CONDUIT FROM "R1" TO "SC" (PU1) UNDER FLOOR	MAX. CONDUIT LENGTH 42'
14	(2) 3"ø	CONDUIT FROM "R1" TO "SC" (PU1) UNDER FLOOR	MAX. CONDUIT LENGTH 42'
15	(2) 3"ø	CONDUIT FROM "R1" TO "SC" (SC1) UNDER FLOOR	MAX. CONDUIT LENGTH 42'
16	3"ø	CONDUIT FROM "R1" TO "CU3" (CU1) UNDER FLOOR FOR LIQUID COOLING HOSES	MAX. CONDUIT LENGTH 75'
17	2"ø	CONDUIT FROM "R1" TO "CU3" (CU2) UNDER FLOOR FOR LIQUID COOLING HOSES	MAX. CONDUIT LENGTH 35'
18	3"ø	CONDUITS FROM "VD1" (SC1) TO "VD3" (CR1)	MAX. CONDUIT LENGTH 32'
19	(2) 3"ø	CONDUIT FROM "SC" TO "T1" UNDER FLOOR	MAX. CONDUIT LENGTH 36'
20	2"ø	CONDUIT FROM "VD1" (SC1) TO "CU1"	MAX. CONDUIT LENGTH 83'
21	2 1/2"ø	CONDUIT FROM "SC" (SC1) TO "CU3" (CU2) UNDER FLOOR	MAX. CONDUIT LENGTH 17'
22	3"ø	CONDUIT FROM "VD1" (SC1) TO "VD2" (IS)	MAX. CONDUIT LENGTH 35'
23	3"ø	CONDUIT FROM "VD1" (SC1) TO "D1"	MAX. CONDUIT LENGTH 47'
24	(2) 3"ø	CONDUITS FROM "VD2" (IS) TO "VD3" (CR1)	MAX. CONDUIT LENGTH 32'
25	2"ø	CONDUIT FROM "VD2" (IS) TO "D1"	MAX. CONDUIT LENGTH 70'
26	(2) 3"ø	CONDUITS FROM "VD2" (IS) TO "VD3" (C-ROOM CUSTOMER LD INPUTS)	MAX. CONDUIT LENGTH 80'
27	VARIES	CONDUIT(S) FROM "VD2" (IS) TO CUSTOMER SOURCES	MAX. CONDUIT LENGTH 80'
28	4"ø	CONDUITS FROM "SC" TO "RC" UNDER FLOOR	MAX. CONDUIT LENGTH 22'
29	6"ø	CONDUIT FROM "RC" TO "R1" UNDER FLOOR	MAX. CONDUIT LENGTH 38'
30	3"ø	CONDUIT FROM "RC" TO "R1" UNDER FLOOR	MAX. CONDUIT LENGTH 38'
31	3"ø	CONDUIT FROM "VD1" (SC1) TO "VD3" (IW2)	MAX. CONDUIT LENGTH 33'
32	3/4"ø	CONDUIT FROM "VD3" TO "IC"	MAX. CONDUIT LENGTH 62'
33	3/4"ø	CONDUIT FROM "VD3" TO "IC2"	MAX. CONDUIT LENGTH 62'
34	3"ø	CONDUIT FROM "T1" TO "B10" UNDER FLOOR	
35	3"ø	CONDUIT FROM "CRB" TO "B10" UNDER FLOOR (CUSTOMER PATIENT MONITORING)	
36	1/2"ø	CONDUIT FROM "XF1" TO "SC1" ("T1") (OPTIONAL TABLE POWER OUTLET)	MAX. CONDUIT LENGTH 60'

ELECTRICAL NOTES

1) COMPLIANCE: ELECTRICAL WORK SHALL BE IN COMPLIANCE WITH THE NATIONAL ELECTRICAL CODE (NFPA-70), O.S.H.A. REGULATIONS, AS WELL AS APPLICABLE REGULATIONS OF CITY, COUNTY, STATE AND FEDERAL AGENCIES. PROVIDE MATERIALS AND EQUIPMENT THAT COMPLY WITH ANSI, IEEE AND NEMA STANDARDS AND ARE U.L. LISTED AND LABELED. THE CUSTOMER'S/CONTRACTOR'S WORK AND ALL EQUIPMENT INSTALLED SHALL COMPLY WITH THE CURRENT EDITION OF THE NATIONAL ELECTRICAL CODE ADOPTED/ENFORCED BY THE AUTHORITY HAVING JURISDICTION.
2) QUALITY ASSURANCE: THE CONTRACTOR SHALL VERIFY EXISTING CONDITIONS IN THE FIELD TO INSURE THAT THE NEW WORK WILL FIT INTO THE EXISTING STRUCTURE AS SHOWN ON THE DRAWINGS. SHOULD ANY CONDITIONS EXIST OR BE DISCOVERED THAT PREVENT THE INSTALLATION OF WORK AS SHOWN, THE CONTRACTOR SHALL NOTIFY THE OWNER'S REPRESENTATIVE PRIOR TO FABRICATION OF EQUIPMENT, OR THE PERFORMANCE OF ANY WORK THAT MAY BE AFFECTED. DO NOT ALTER DRAWINGS, DIMENSIONS, OR SPECIFICATIONS IN ANY WAY WITHOUT CONTACTING AND RECEIVING WRITTEN CONFIRMATION FROM SIEMENS PROJECT MANAGER. ALL DIMENSIONS ARE FROM FINISHED SURFACES. CONDUIT AND PULL BOXES TO BE INSTALLED BY THE CUSTOMER/CONTRACTOR WITH LOCATIONS BEING FIELD VERIFIED BY THE SIEMENS PROJECT MANAGER.
3) POWER SUPPLY SOURCE: POWER SUPPLIES FOR SIEMENS HEALTHCARE EQUIPMENT SHALL BE FROM A MEDICAL IMAGING PANEL OR BUILDING SERVICE EQUIPMENT THAT IS A GROUNDED 3 OR 4-WIRE 'WYE' SOURCE PER THE SPECIFIC EQUIPMENT OPERATION REQUIREMENTS. A DEDICATED CIRCUIT SHALL BE PROVIDED THAT IS KEPT ENTIRELY FREE AND INDEPENDENT OF ALL OTHER BUILDING WIRING. NO ELEVATORS, GENERATORS, PUMPS, HVAC OR SIMILAR EQUIPMENT SHALL BE CONNECTED TO THE SAME CIRCUIT OR MEDICAL IMAGING PANEL THAT SERVES THE SIEMENS HEALTHCARE EQUIPMENT. IF THE POWER SUPPLY SOURCE DOES NOT MEET THE SPECIFIC SIEMENS EQUIPMENT POWER REQUIREMENTS, THE CONTRACTOR SHALL PROVIDE THE NECESSARY EQUIPMENT REQUIRED TO ESTABLISH THE POWER SUPPLY IN ACCORDANCE WITH THE REQUIRED POWER SUPPLY PARAMETERS OF THE SIEMENS EQUIPMENT. THE CONTRACTOR SHALL COORDINATE THIS WORK WITH THE CUSTOMER AND/OR UTILITY COMPANY FIELD REPRESENTATIVE.
4) WORK FURNISHED BY CUSTOMER/CONTRACTOR: WORK NOT PROVIDED BY SIEMENS HEALTHCARE BUT SHOWN ON DRAWINGS TO BE FURNISHED AND INSTALLED BY CUSTOMER/CONTRACTOR INCLUDES, BUT IS NOT LIMITED TO, THE FOLLOWING, UNLESS NOTED OTHERWISE: ELECTRICAL RACEWAYS AND DUCTS, WIRING TROUGHS, PULL BOXES, CONDUITS, CIRCUIT BREAKERS, ACCESS PANELS, EMERGENCY OFF BUTTONS, DOOR SWITCHES, WARNING LIGHTS, WIRING, WIRING DEVICES, CONNECTORS, LIGHTING EQUIPMENT AND GROUNDING.
5) RACEWAY AND CONDUIT NOTES: ALL CONDUITS SHALL BE INSTALLED IN COMPLIANCE WITH THE CURRENT ENFORCED EDITION OF THE NATIONAL ELECTRICAL CODE.
CONDUIT BODIES SHALL NOT BE USED, WHERE A CONDUIT ENTERS A BOX, FITTING, OR OTHER ENCLOSURE, AN INSULATED THROAT CONNECTOR SHALL BE PROVIDED TO PROTECT THE WIRE FROM ABRASION. ALL CONNECTORS FOR EMT SHALL BE COMPRESSION OR DOUBLE SET SCREW TYPE.
KEEP RACEWAYS AT LEAST 6 INCHES AWAY FROM PARALLEL RUNS OF FLUES OR STEAM AND HOT WATER PIPES. INSTALL RACEWAY RUNS ABOVE WATER AND STEAM PIPES PROVIDED THAT CABLE RUN DISTANCES ARE MAINTAINED. USE TEMPORARY CLOSURES TO PREVENT FOREIGN MATTER FROM ENTERING RACEWAY.
CONDUIT RUNS ARE SHOWN SCHEMATICALLY. INSTALL CONDUIT WITH A MINIMUM OF BENDS IN THE SHORTEST PRACTICAL DISTANCE CONSIDERING THE BUILDING CONSTRUCTION AND OBSTRUCTIONS, EXCEPT AS OTHERWISE INDICATED. THE CONTRACTOR SHALL MAKE CERTAIN THAT ANY CONDUIT/RACEWAY RUNS CONTAINING SIEMENS HEALTHCARE CABLES DO NOT EXCEED THE SPECIFIED MAXIMUM DISTANCES AS SHOWN ON THE ELECTRICAL DETAILS. LISTED CONDUIT SIZES FOR SIEMENS-SUPPLIED CABLES MUST BE MAINTAINED IN ORDER TO ENABLE THE TOTAL CABLE BUNDLE INCLUDING CONNECTORS TO BE PULLED THROUGH WITHOUT DAMAGE.
PROVIDE ENCLOSED METAL WIRE DUCT RACEWAY SYSTEM WHERE SHOWN ON DRAWINGS WITH DIVIDERS TO SEPARATE THE DUCT INTO TWO OR THREE SEPARATE COMPARTMENTS AS SHOWN ON THE SIEMENS PLANS (FOR POWER AND SIEMENS HEALTHCARE CABLING). DIVIDERS AND CROSSOVER PIECES TO BE PROVIDED AS NECESSARY. THE CABLE TO CABLE AS WELL AS THE CIRCUIT TO CIRCUIT SEPARATION REQUIREMENT WAS EVALUATED DURING THE UL SYSTEM CERTIFICATION OF THE EQUIPMENT. ADDITIONAL SEPARATION OF THE SYSTEM CABLE ASSEMBLIES INTO SEPARATE OR PARTITIONED RACEWAYS, UNLESS OTHERWISE NOTED, IS NOT NECESSARY TO INSURE SEPARATION OF CIRCUITS.
PROVIDE WIRE DUCT/RACEWAY WITH ACCESSIBLE REMOVABLE COVERS. LOCATIONS OF BUILDING MATERIAL OPENINGS (I.E. ACCESS PANELS) TO BE CUT IN FIELD ARE TO BE COORDINATED WITH THE DRAWING REQUIREMENTS AND BUILDING STRUCTURE. THOSE THAT ARE NOT INDICATED OR INTERFER WITH BUILDING ELEMENTS SHALL BE COORDINATED WITH SIEMENS PROJECT MANAGER. ELECTRICAL PULL BOXES AND RACEWAY COVERS SHALL BE INSTALLED IN A MANNER TO ALLOW ACCESSIBILITY FOR INSTALLATION AND MAINTENANCE. CONTRACTORS MUST PROVIDE PULL STRINGS FOR ALL CONDUIT AND WIRE DUCT/RACEWAY. IN-FLOOR TRENCH DUCT AND FLUSH FLOOR BOXES SHALL BE PROVIDED WITH FULLY GASKETED REMOVABLE COVERS.
WHEN JUNCTION BOXES AND WIRE DUCT/RACEWAY ARE MOUNTED HIGHER THAN 14 FEET ABOVE FINISHED FLOOR, THE ELECTRICAL CONTRACTOR SHALL PROVIDE TWO ELECTRICIANS TO HELP THE SIEMENS INSTALLERS PULL SIEMENS SUPPLIED CABLES AT CUSTOMER'S EXPENSE. WHEN JUNCTION BOXES AND WIRE DUCT/RACEWAY ARE MOUNTED ABOVE A HARD CEILING (I.E. SHEET ROCK), A 24" x 24" ACCESS PANEL IS REQUIRED AT EACH JUNCTION BOX AND WITHIN 2 FEET OF EACH RACEWAY TRANSITION (SUCH AS A 90 DEGREE ELBOW OR TEE) IN DUCT/RACEWAY. THERE MUST BE FREE AND CLEAR ACCESS TO JUNCTION BOXES AND WIRE DUCT/RACEWAY. WHEN ACCESS PANELS ARE LOCATED MORE THAN 3 FEET FROM JUNCTION BOXES AND WIRE DUCT/RACEWAY THE ELECTRICAL CONTRACTOR SHALL PROVIDE TWO ELECTRICIANS TO HELP SIEMENS INSTALLERS PULL SIEMENS SUPPLIED CABLES AT CUSTOMER'S EXPENSE. WHEN JUNCTION BOXES AND WIRE DUCT/RACEWAY ARE MOUNTED ABOVE A HARD CEILING (I.E. SHEET ROCK), A 24" x 24" ACCESS PANEL IS REQUIRED AT EACH JUNCTION BOX AND WITHIN 2 FEET OF EACH RACEWAY TRANSITION (SUCH AS A 90 DEGREE ELBOW OR TEE) IN DUCT/RACEWAY. THERE MUST BE FREE AND CLEAR ACCESS TO JUNCTION BOXES AND WIRE DUCT/RACEWAY. WHEN ACCESS PANELS ARE LOCATED MORE THAN 3 FEET FROM JUNCTION BOXES AND WIRE DUCT/RACEWAY THE ELECTRICAL CONTRACTOR SHALL PROVIDE TWO ELECTRICIANS TO HELP SIEMENS INSTALLERS PULL SIEMENS SUPPLIED CABLES AT CUSTOMER'S EXPENSE.
6) WIRING: ALL WIRING INSTALLED SHALL BE 600 VOLT CLASS, STRANDED TYPE THHN/THWN-2, SINGLE CONDUCTOR ANNEALED COPPER FOR A MAXIMUM OPERATING TEMPERATURE OF 90°C (194°F), SIZED AS INDICATED, INSTALLED IN METAL RACEWAYS. THE CUSTOMER/CONTRACTOR SHALL LEAVE A MINIMUM 10 FEET OF WIRE TAILS AT ALL OUTLET POINTS WITH WIRE IDENTIFICATION TAGGED AT BOTH ENDS FOR FINAL CONNECTION BY THE CUSTOMER/ELECTRICAL CONTRACTOR.
7) SHORT CIRCUIT REQUIREMENTS: ALL CIRCUIT BREAKERS SUPPLIED FOR THE SIEMENS EQUIPMENT REQUIREMENTS SHALL BE RATED HIGHER THAN THE SHORT CIRCUIT AVAILABLE AT THE TERMINALS OF THE ELECTRICAL EQUIPMENT AS DETERMINED BY THE ENGINEER OF RECORD, BUT NOT LESS THAN 35,000A RMS SYMMETRICAL AT 480V, 3-PHASE, 60 HERTZ. THE CONTRACTOR SHALL OBTAIN THE CORRECT SHORT CIRCUIT CURRENT RATING OF ALL THE NEW EQUIPMENT FOR INSTALLATION FROM THE ENGINEER OF RECORD.

CONDUIT LENGTH CALCULATIONS

IF SITE-SPECIFIC CONDITIONS EXCEED THE FOLLOWING ASSUMED VALUES, THEN ADDITIONAL LENGTH MUST BE SUBTRACTED BY THE ELECTRICAL CONTRACTOR FROM THE MAXIMUM CONDUIT LENGTHS LISTED.
IF DUCT LOCATIONS ARE ALTERED FROM THE SHOWN LAYOUT, IT IS THE ELECTRICAL CONTRACTOR'S RESPONSIBILITY TO RECALCULATE THE MAXIMUM CONDUIT LENGTHS.
ASSUMED VALUES USED IN CALCULATING STATED MAXIMUM CONDUIT LENGTHS:
VERTICAL DUCTS – 12'-0"
FLOOR PENETRATIONS – 3'-0"

PRINTS OF THIS DRAWING SHALL NOT BE USED FOR ANY PURPOSE WHATSOEVER WITHOUT THE SEAL AND SIGNATURE OF THE PROFESSIONAL ENGINEER.

NO.	DESCRIPTION	DATE

CONSULTANTS

Architecture:	Civil Engineering:	Fire & Life Safety:
PF&A DESIGN, P.C.	LABELLA ASSOCIATES	STANTON ENGINEERING SERVICES, LLC

ENGINEER OF RECORD

MILLER•REMICK
A Service-Disabled Veteran-Owned Small Business
(856) 429-4000 ★ Miller-Remick.com
M-R PROJECT NO. 0499-0136

MILLER-REMICK LLC
PROFESSIONAL ENGINEER
COMMONWEALTH OF PENNSYLVANIA REGISTERED PROFESSIONAL THOMAS REGINO ENGINEER PENNSYLVANIA
12/30/25

Office of Construction and Facilities Management

VA U.S. Department of Veterans Affairs

Drawing Title: ELECTRICAL HYBRID O.R. DETAILS	Phase: BID DOCUMENTS	Project Title: RENOVATE SURGICAL SUITE PHASE II	VA Drawing Number: 2617
Approved by: Jon Manninen, COR	FULLY SPRINKLERED	Project Number: 658-19-103	Building Number: 143
		Location: SALEM VA MEDICAL CENTER	Drawing Number: E-506
		Issue Date: 2025-12-30 / Checked: MJR / Drawn: MJR	

VA FORM 08-6231

P:\0499_DWA\0499-0136 Salem Renovate Surgical Suite\A_Drawings\1_Cad\1_Current Submittal Phase\7_Electric\E-506.dwg 12-29-25 08:25:32 AM MRonco

POWER SCHEDULE

ALL CONDUITS AND WIRES SIZES MUST BE DETERMINED BY THE ELECTRICAL ENGINEER OF RECORD PER N.E.C. AND TO MAINTAIN SIEMENS IMPEDANCE REQUIREMENTS.

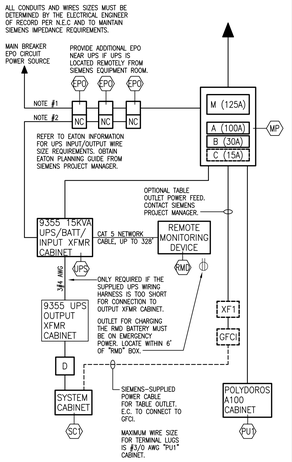

ITEM	QTY	DESCRIPTION				
MP	1	MAIN PANEL WITH CIRCUIT BREAKERS FLUSH OR SURFACE MOUNTED.				
M	1	MAIN BREAKER MUST HAVE TRIPPING DEVICE SO WHEN ANY EPO IS PRESSED, THE MAIN BREAKER TRIPS.				
		MAIN BREAKER AMPS: 125				
		VOLTS	PHASES	NEUTRAL	GROUND	TOTAL WIRES
		480/277Y	3	1	1	5 (NOTE 1)
A	1	BREAKER AMPS: 100 (FOR PU1)				
		VOLTS	PHASES	NEUTRAL	GROUND	TOTAL WIRES
		480Y	3	0	1	4 (NOTE 1)
B	1	BREAKER AMPS: 30 (FOR SC1)				
		VOLTS	PHASES	NEUTRAL	GROUND	TOTAL WIRES
		480/277Y	3	1	1	5 (NOTE 1)
C	1	BREAKER AMPS: 15 (FOR STEP-DOWN XFMR "XF1")				
		VOLTS	PHASES	NEUTRAL	GROUND	TOTAL WIRES
		480	1 (L1,L2)	0	1	3
1) PHASE AND NEUTRAL TO BE THE SAME SIZE. GROUND SIZED PER NEC. NOTE: UNLESS OTHERWISE NOTED, ALL BREAKERS WILL BE 80% RATED						
D	1	3-PHASE (PLUS N,G) 30A, 600V HD FUSIBLE SERVICE DISCONNECT LOCATED AT EYE-LEVEL, WITHIN 10' OF SIEMENS SYSTEM CABINET (SC1) AND 30A RK5 FUSES.				
XF1	1	1.5kVA, 480V PRIMARY, 120V GROUNDED SECONDARY STEP-DOWN SINGLE-PHASE TRANSFORMER WITH PRIMARY AND SECONDARY FUSE PROTECTION FOR TABLE OUTLET POWER, CONNECTED TO AN ADJACENT FLUSH WALL-MOUNTED 15A, 125V AC UL 943 GFCI WITH BLANK FACE (NO CONTACT OPENINGS OR NEMA CONFIGURATION) WITH LED INDICATION, PUSH-TO-TEST AND PUSH-TO-RESET BUTTONS, AND A CLEAR LEXAN HINGED COVER TO AVOID INADVERTENT MANUAL TRIP.				
EPO	VARIES	NOTE 1-EPO CIRCUIT #1 MAIN CIRCUIT BREAKER EMERGENCY POWER OFF BUTTON WITH PROTECTIVE COVER THAT PREVENTS ACCIDENTAL ACTIVATION. THE EPO MUST BE OF FAIL-SAFE DESIGN. ALL EPO'S TO HAVE MECHANICAL LATCHING MECHANISM. EPO MUST BE RESET BEFORE MAIN BREAKER CAN RESUME OPERATION. CONTACTS AND WIRING CONFIGURATION TO BE DESIGNED BY ELECTRICAL ENGINEER OF RECORD. NOTE 2-EPO CIRCUIT #2 EPO CONTACTS TO BE NORMALLY CLOSED, WIRED IN SERIES, CONNECTED TO 9355 UPS ONLY. THE EPOs MUST BE INSTALLED BY A QUALIFIED ELECTRICAL CONTRACTOR ACCORDING TO NATIONAL ELECTRICAL CODE, STATE AND LOCAL REGULATIONS. MEASURES SHOULD BE TAKEN TO DESIGN THE CIRCUIT IN SUCH A WAY THAT IT WILL ALWAYS WORK WHEN THE MEDICAL EQUIPMENT IS POWERED. THE CUSTOMER IS SOLELY RESPONSIBLE FOR THE IMPLEMENTATION OF THE EPOs AND THEIR ASSOCIATED CIRCUITS AND MUST MAKE THE FINAL DETERMINATION CONSIDERING ALL SITE CONDITIONS AND REGULATORY FACTORS.				
ALL ITEMS LISTED IN THIS SCHEDULE SHALL BE SUPPLIED AND INSTALLED BY CUSTOMER/CONTRACTOR.						

MAXIMUM CABLE LENGTHS (TYPICAL EQUIPMENT)

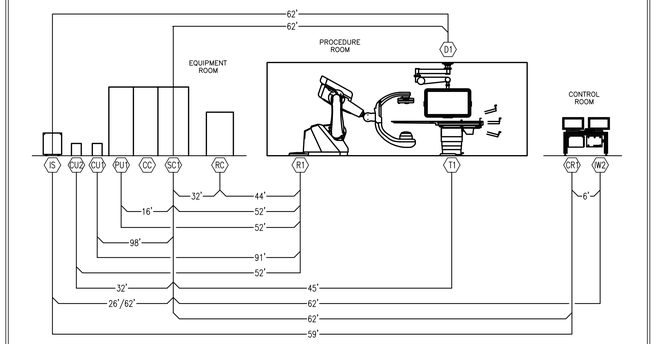

POWER REQUIREMENTS

WIRING SYSTEM:	480Y/277V, 3 PHASE, 5-WIRE, 60 HZ.

MINIMUM POWER SUPPLY:

IF AN ON-SITE TRANSFORMER IS REQUIRED TO OBTAIN OPERATING VOLTAGE, IT MUST BE OF SUFFICIENT CAPACITY AND CHARACTERISTICS TO MAINTAIN SUPPLY VOLTAGE AND IMPEDANCE REQUIREMENTS (TRANSFORMER AND CONDUCTORS).

X-RAY GENERATOR (PU1) MOMENTARY RATING: (RADIOGRAPHIC EXPOSURE)	162 KVA
X-RAY GENERATOR (PU1) LONG-TIME RATING: (FLUOROSCOPY)	8 KVA
SYSTEM CABINET (SC1) LONG-TIME RATING:	17.2 KVA
LINE IMPEDANCE	≤ 120 (mΩ)

POWER QUALITY PARAMETERS

MAXIMUM LINE VOLTAGE VARIATION	±10% OF SYSTEM VOLTAGE
PHASE IMBALANCE:	2%
FREQUENCY VARIATION:	± 1 HZ

POWER SUPPLY NOTES:

1. INCOMING POWER SUPPLIES FOR SIEMENS EQUIPMENT SHOULD BE DEDICATED (BACK TO SOURCE), ISOLATED AND INSULATED FROM ANY OTHER EQUIPMENT SUCH AS ELEVATORS, GENERATORS, HVAC SYSTEMS, ETC.
2. SIEMENS HEALTHCARE REQUIRES THAT THE INCOMING POWER MEETS THE POWER QUALITY REQUIREMENTS.

GROUNDING NOTES

EQUIPMENT GROUND CONDUCTOR TO COMPLY WITH THE FOLLOWING:

1) SIZE GROUNDING WIRE TO SIEMENS EQUIPMENT PER POWER SCHEDULE REQUIREMENTS.
2) DERIVED FROM THE ELECTRICAL SERVICE, TRANSFORMER OR MAIN DISTRIBUTION PANEL FEEDING THE SIEMENS EQUIPMENT.
3) RUN IN THE SAME CONDUIT, TROUGH OR RACEWAY AS THE PHASE CONDUCTORS.
4) CONTINUOUS, WITH NO BREAKS OR USE OF CONDUIT, CHASSIS OR EARTH AS THE SOLE GROUNDING PATH.
5) BONDED TO CHASSIS AND/OR CONDUIT IN ACCORDANCE WITH THE NEC REQUIREMENTS.
6) MINIMIZE CONNECTIONS OR TERMINALS TO ENSURE CONTINUITY OVER THE LIFE OF THE INSTALLATION.
7) AS A NORM, THERE SHOULD NOT BE ANY CURRENT PRESENCE ON THE GROUND CONDUCTOR, BUT IT IS ACCEPTABLE TO HAVE <500mA DURING OPERATION OF THE IMAGING EQUIPMENT.

POWER QUALITY

POOR POWER WILL ALTER EQUIPMENT PERFORMANCE

IT IS IN THE CUSTOMER'S INTEREST THAT THE ELECTRICAL CONTRACTOR BE RESPONSIBLE FOR TESTING AND VERIFYING THAT THE EQUIPMENT POWER SUPPLY COMPLIES WITH THE SIEMENS SPECIFICATIONS.

SIEMENS REMOTE SERVICE

TO ENSURE THE UPTIME OF YOUR SYSTEM DURING THE WARRANTY PERIOD (AND BEYOND WITH A SERVICE AGREEMENT), SIEMENS REMOTE SERVICES (SRS) REQUIRES REMOTE LOCAL AREA NETWORK ACCESS TO SIEMENS SYSTEMS.

THE PREFERRED CONNECTION METHOD IS (VPN) VIRTUAL PRIVATE NETWORK (WHERE THE CUSTOMER HAS AVAILABLE A VPN CAPABLE FIREWALL OR OTHER VPN APPLIANCE). THIS METHOD PROVIDES THE POSSIBILITY FOR REMOTE SYSTEM DIAGNOSTICS WITHOUT ADDITIONAL HARDWARE. PLEASE CONTACT SIEMENS REMOTE SERVICES (800-888-SIEM) TO DETERMINE IF THIS METHOD IS SUITABLE FOR YOUR SITE.

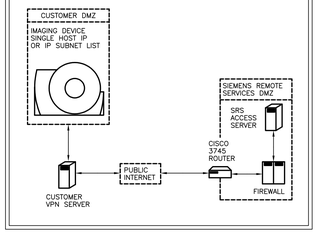

TABLE POWER OUTLET SAFETY

NOTE: LIFE-SUSTAINING EQUIPMENT MUST NOT BE CONNECTED TO THE TABLE POWER OUTLET (IF INSTALLED) IN THE SIEMENS PATIENT TABLE. POWER WILL BE DISCONNECTED IF EPO BUTTON IS PRESSED. TABLE OUTLET IS 120V, FUSED AT 5A.

NETWORK REQUIREMENT

A GIGABIT NETWORK IS REQUIRED FOR ADEQUATE IMAGE DATA TRANSFER SPEED BETWEEN THE IMAGER AND 3D RECONSTRUCTION WORKSTATION. WORKFLOW AND CLINICAL NEEDS DEMAND 3D IMAGES BE AVAILABLE FOR REVIEW BY CLINICAL STAFF IMMEDIATELY UPON ACQUISITION.

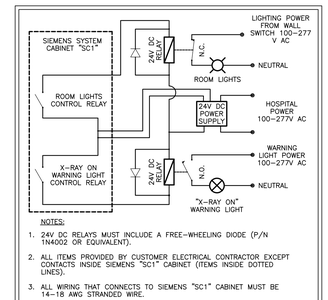

NOTES:

1. 24V DC RELAYS MUST INCLUDE A FREE-WHEELING DIODE (P/N 1N4002 OR EQUIVALENT).
2. ALL ITEMS PROVIDED BY CUSTOMER ELECTRICAL CONTRACTOR EXCEPT CONTACTS INSIDE SIEMENS "SC1" CABINET (ITEMS INSIDE DOTTED LINES).
3. ALL WIRING THAT CONNECTS TO SIEMENS "SC1" CABINET MUST BE 14-18 AWG STRANDED WIRE.
4. ONLY 3 WIRES LABELED "24V DC", "ROOM LIGHTS" AND "X-RAY ON" SHOULD BE SENT TO SIEMENS "SC1" CABINET.
5. 24V DC RELAYS ARE TO BE SELECTED BY ELECTRICAL CONTRACTOR TO HANDLE THE VOLTAGE AND AMPERAGE OF LIGHTING CIRCUIT.
6. IF NEEDED, A SWITCH TO BLOCK RADIATION CAN BE INSTALLED IN SERIES WITH THE DOOR CONTACT.
   - THE SWITCH (24V DC/20 MA) MUST BE PROVIDED ON SITE.
   - CONTROL USING +24V FROM THE SYSTEM CONTROL CABINET
   - PLAN THE SWITCH SO THAT UNINTENTIONAL OPERATION IS NOT POSSIBLE.
   - THE SWITCH MUST BE PROVIDED WITH AN APPROPRIATE SYMBOL (OR DESIGNATION) FROM WHICH THE FUNCTION CAN BE RECOGNIZED.

WARNING LIGHT/ROOM LIGHT SCHEMATIC

1	LIGHTING DETAIL	SCALE: NONE

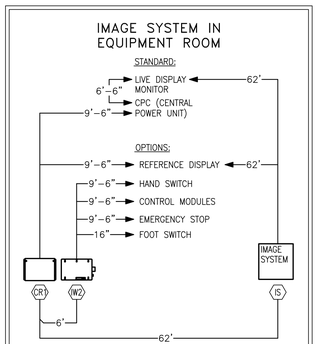

2	CONTROL ROOM SYSTEM CONNECTIONS	SCALE: NONE

PRINTS OF THIS DRAWING SHALL NOT BE USED FOR ANY PURPOSE WHATSOEVER WITHOUT THE SEAL AND SIGNATURE OF THE PROFESSIONAL ENGINEER.

NO.	DESCRIPTION	DATE

CONSULTANTS

Architecture:	Civil Engineering:	Fire & Life Safety:
PF&A DESIGN, P.C.	LABELLA ASSOCIATES	STANTON ENGINEERING SERVICES, LLC

ENGINEER OF RECORD

MILLER-REMICK

A Service-Disabled Veteran-Owned Small Business

(856) 429-4000 ★ Miller-Remick.com

M-R PROJECT NO 0499-0136

MILLER-REMICK LLC
PROFESSIONAL ENGINEER

COMMONWEALTH OF PENNSYLVANIA — REGISTERED PROFESSIONAL — ENGINEER & PLANNER — THOMAS REGINO — 12/30/25

Office of Construction and Facilities Management

VA U.S. Department of Veterans Affairs

Drawing Title: ELECTRICAL HYBRID O.R. DETAILS	Phase: BID DOCUMENTS	Project Title: RENOVATE SURGICAL SUITE PHASE II	VA Drawing Number: 2617
Approved by: Jon Manninen, COR	FULLY SPRINKLERED	Project Number: 658-19-103	Building Number: 143
		Location: SALEM VA MEDICAL CENTER	Drawing Number: E-507
		Issue Date: 2025-12-30 / Checked: MJR / Drawn: MJR	

VA FORM 08-6231

P:\0499_DVA\0499-0136 Salem Renovate Surgical Suite\4_Drawings\1_Cad\1_Current Submittal Phase\7_Electrical\E-507.dwg 12-29-25 08:25:26 AM MRonca

GENERAL SHEET NOTES:

1. SEE DRAWING E-001 FOR ELECTRICAL NOTES AND ABBREVIATIONS AND DRAWING E-002 FOR ELECTRICAL NOTES.
2. ALL EQUIPMENT SHOWN IS EXISTING TO REMAIN, UNLESS OTHERWISE NOTED.

⬡ SHEET KEYNOTES:

1. REFEED ACTIVE PHASE 2 AND PHASE 3 LOADS IN DEMOLISHED PANEL 1ECLC AND PANEL ICU2 FROM THIS PANEL.
2. REFEED ACTIVE PHASE 3 AND PHASE 4 LOADS FROM DEMOLISHED PANEL TO EXISTING PANELS IN ELECTRICAL ROOM 1D-1027 OR EXISTING PANELS IN ELECTRICAL ROOM ID-1037.
3. DEMOLISH FEEDER FROM PANEL 1ECLC TO LOCATION OF NEW JUNCTION BOX MOUNTED TO CEILING SLAB OF DEMOLISHED ELECTRICAL ROOM 1D-117. FEEDER SHALL BE EXTENDED TO EXISTING 60-AMP CIRCUIT BREAKER IN PANEL 1ECLM2 IN PHASE 1. COORDINATE ALL SHUTDOWNS WITH VA AT LEAST 2 WEEKS PRIOR TO CONSTRUCTION. SEE E-602 FOR CONTINUATION.
4. PROVIDE TEMPORARY FEEDER FROM PANEL 1LM1 TO POWER O.R. PANEL DURING PHASE 2 CONSTRUCTION. DEMOLISH TEMPORARY FEEDER DURING PHASE 3. TEMPORARY FEEDER WIRE SIZE SHALL MATCH EXISTING FEEDER.
5. SPLICE AND EXTEND FEEDER IN NEW FLOOR MOUNTED PULLBOX WHERE EXISTING FEEDER ENTERS GENERATOR BUILDING 143 FROM THE FLOOR.

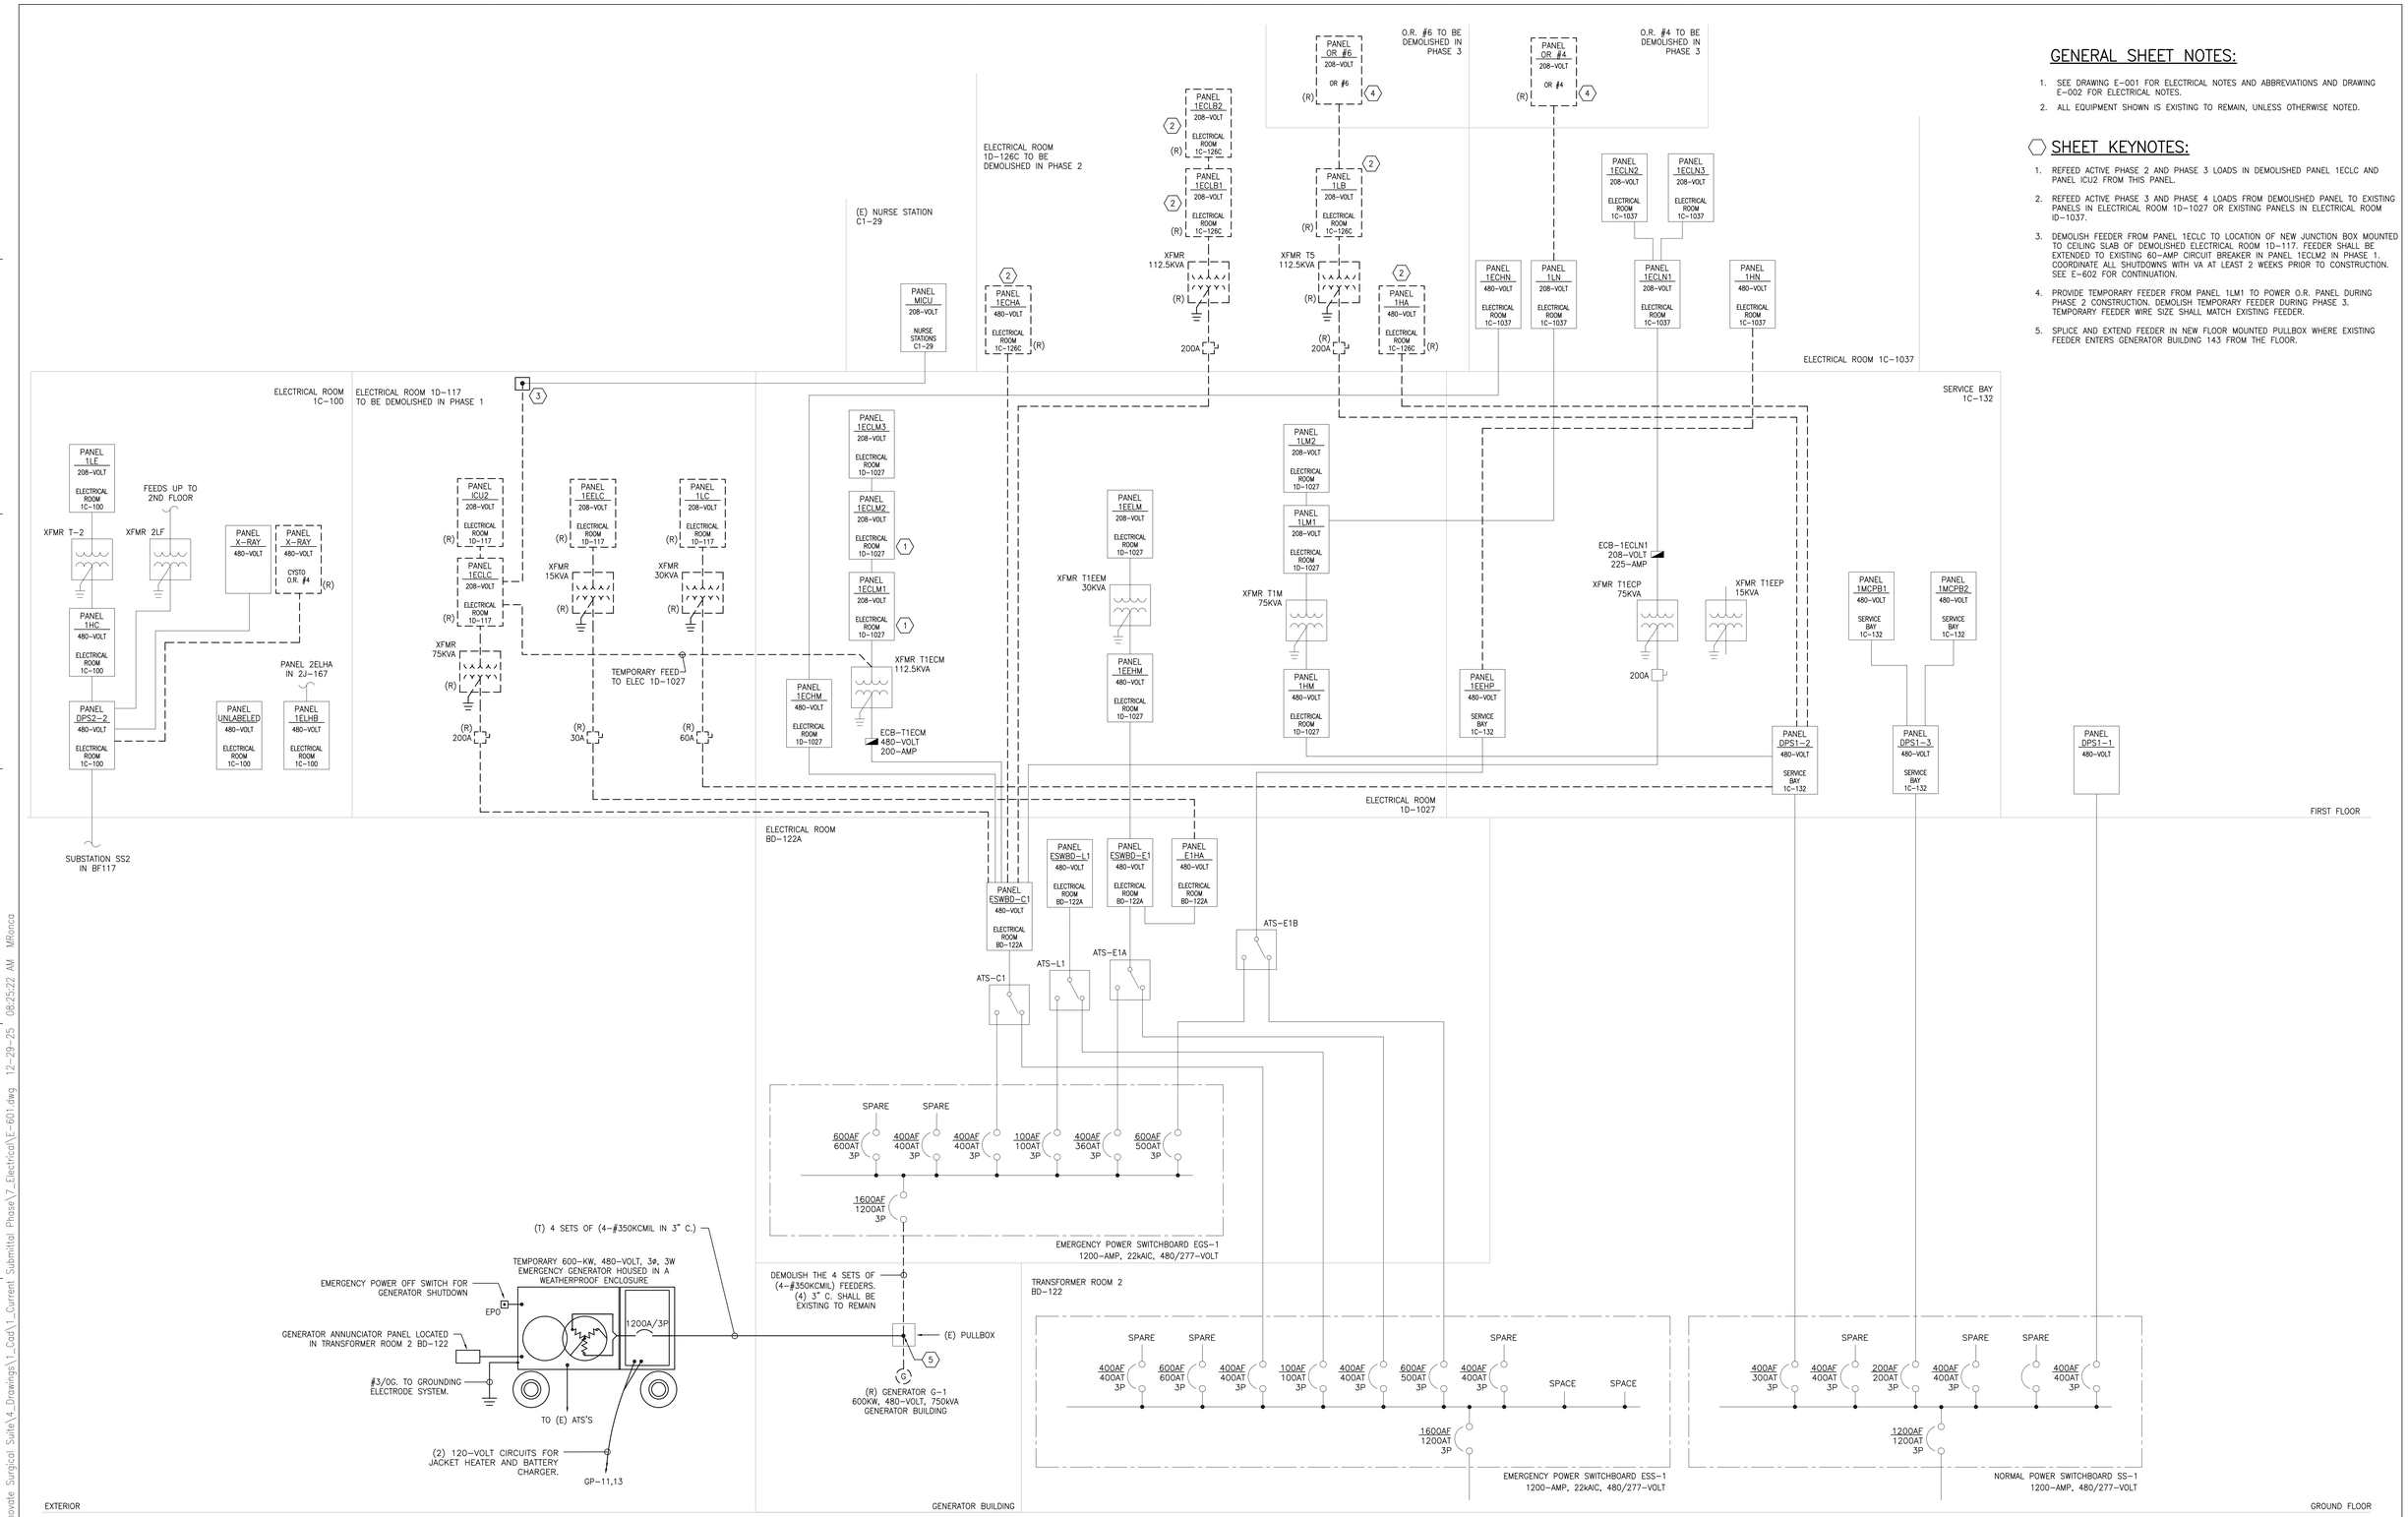

PRINTS OF THIS DRAWING SHALL NOT BE USED FOR ANY PURPOSE WHATSOEVER WITHOUT THE SEAL AND SIGNATURE OF THE PROFESSIONAL ENGINEER.

NO.	DESCRIPTION	DATE

CONSULTANTS

Architecture:	Civil Engineering:	Fire & Life Safety:
PF&A DESIGN, P.C.	LABELLA ASSOCIATES	STANTON ENGINEERING SERVICES, LLC

ENGINEER OF RECORD

MILLER•REMICK
A Service-Disabled Veteran-Owned Small Business
(856) 429-4000 • Miller-Remick.com
M-R PROJECT NO. 0499-0136

MILLER-REMICK LLC PROFESSIONAL ENGINEER

COMMONWEALTH OF PENNSYLVANIA REGISTERED PROFESSIONAL THOMAS REGINO ENGINEER No. PE094195
12/30/25

Office of Construction and Facilities Management

VA U.S. Department of Veterans Affairs

Drawing Title ELECTRICAL DEMOLITION SINGLE LINE DIAGRAM	**Phase** BID DOCUMENTS	**Project Title** RENOVATE SURGICAL SUITE PHASE II	**VA Drawing Number** 2617
Approved by: Jon Manninen, COR	FULLY SPRINKLERED	**Project Number** 658-19-103	**Building Number** 143
		Location SALEM VA MEDICAL CENTER	**Drawing Number** E-601
		Issue Date 2025-12-30 / **Checked** MJR / **Drawn** MJR	

VA FORM 08-6231

P:\0499_OVA\0499-0136 Salem Renovate Surgical Suite\4_Drawings\1_Cad\1_Current Submittal Phase\7_Electrical\E-601.dwg 12-29-25 08:25:22 AM MRonca

GENERAL SHEET NOTES:

1. SEE DRAWING E-001 FOR ELECTRICAL NOTES AND ABBREVIATIONS AND DRAWING E-002 FOR ELECTRICAL NOTES.
2. ALL EQUIPMENT SHOWN IS EXISTING TO REMAIN, UNLESS OTHERWISE NOTED.
3. CONTRACTOR SHALL PERFORM ARC FLASH, SHORT CIRCUIT, AND SELECTIVE COORDINATION CALCULATIONS IN ACCORDANCE WITH SPECIFICATION 260573.

⬡ SHEET KEYNOTES:

1. SPLICE AND EXTEND FEEDER FROM EXISTING PANEL MICU TO EXISTING 60-AMP CIRCUIT BREAKER IN PANEL 1ECLM2 WITHIN NEW JUNCTION BOX LOCATED ON CEILING SLAB OF DEMOLISHED ELECTRICAL ROOM 1D-117.
2. PROVIDE NEW CIRCUIT BREAKER IN EXISTING BLANK SPACE. NEW CIRCUIT BREAKER SHALL MATCH EXISTING BREAKER'S TYPE (G.E.) AND AIC RATING.
3. EATON 93PM 150KW UPS MATCHED TO HYBRID EQUIPMENT WITH INPUT AND OUTPUT CIRCUIT BREAKERS PROVIDED BY THE ELECTRICAL CONTRACTOR. COORDINATE FEEDER SIZES INTO AND OUT OF THE UPS BASED ON MANUFACTURER'S RECOMMENDATIONS.
4. PROVIDE EPO SWITCH ADJACENT TO UPS. EPO SHALL BE CONNECTED TO THE (3) EPO SWITCHES LOCATED IN THE HYBRID O.R. EPO SWITCH SHALL ADHERE TO THE REQUIREMENTS SHOWN ON POWER SCHEDULE ON DRAWING E-507.

WIRE AND CONDUIT SIZING SCHEDULE

1. CONDUIT SIZES SHOWN ARE TYPICAL FOR CONDUCTOR SIZES AND QUANTITY. CONDUIT AND WIRE SIZE NOTED ON THE ELECTRICAL FLOOR PLANS AND SINGLE LINE TAKE PRECEDENCE.

SINGLE LINE TAG: THIS COLUMN COMBINED WITH "A", "B", OR "C" COLUMN	WIRE SIZE (AWG/KCMIL)		NO. OF WIRES & CONDUIT SIZE IN INCHES		
	CONDUCTOR PHASE & NEUTRAL	GROUND	A 1PH, 2W+G	B 3PH, 3W+G	C 3PH, 4W+G
1	14	14	3/4	3/4	3/4
2	12	12	3/4	3/4	3/4
3	10	10	3/4	3/4	3/4
4	8	10	3/4	3/4	1
5	6	10	3/4	3/4	1
6	4	10	3/4	1	1 1/4
7	4	8	3/4	1	1 1/4
8	3	8	1	1	1 1/4
9	2	8	1	1 1/4	1 1/4
10	1	8	1 1/4	1 1/4	1 1/2
11	1	6	1 1/4	1 1/4	1 1/2
12	1	6	1 1/4	1 1/4	1 1/2
13	1/0	6	1 1/4	1 1/2	1 1/2
14	2/0	6	1 1/2	2	2
15	3/0	6	1 1/2	2	2
16	4/0	4	1 1/2	2	2 1/2
17	250	4	2	2 1/2	2 1/2
18	350	4	2 1/2	2 1/2	3
19	500	3	2 1/2	3	3
20	(2) 3/0	(2) 3	(2) 1 1/2	(2) 2	(2) 2
21	(2) 4/0	(2) 2		(2) 2	(2) 2 1/2
22	(2) 250	(2) 2		(2) 2	(2) 2 1/2
23	(2) 350	(2) 1		(2) 2 1/2	(2) 3
24	(2) 500	(2) 1/0		(2) 3	(2) 3 1/2
25	(3) 300	(3) 1/0		(3) 2 1/2	(3) 3
26	(3) 400	(3) 2/0		(3) 3	(3) 3
27	(4) 350	(4) 3/0		(4) 2 1/2	(4) 3
28	(5) 400	(5) 4/0		(5) 3	(5) 3
29	(6) 400	(6) 250		(6) 3	(6) 3
30	(7) 500	(7) 350		(7) 3	(7) 3 1/2
31 *	350	4		(2) 4	3
32	350	4			3

* – ELECTRICAL CONTRACTOR SHALL PULL EXTRA NEUTRAL WIRE/PHASE.

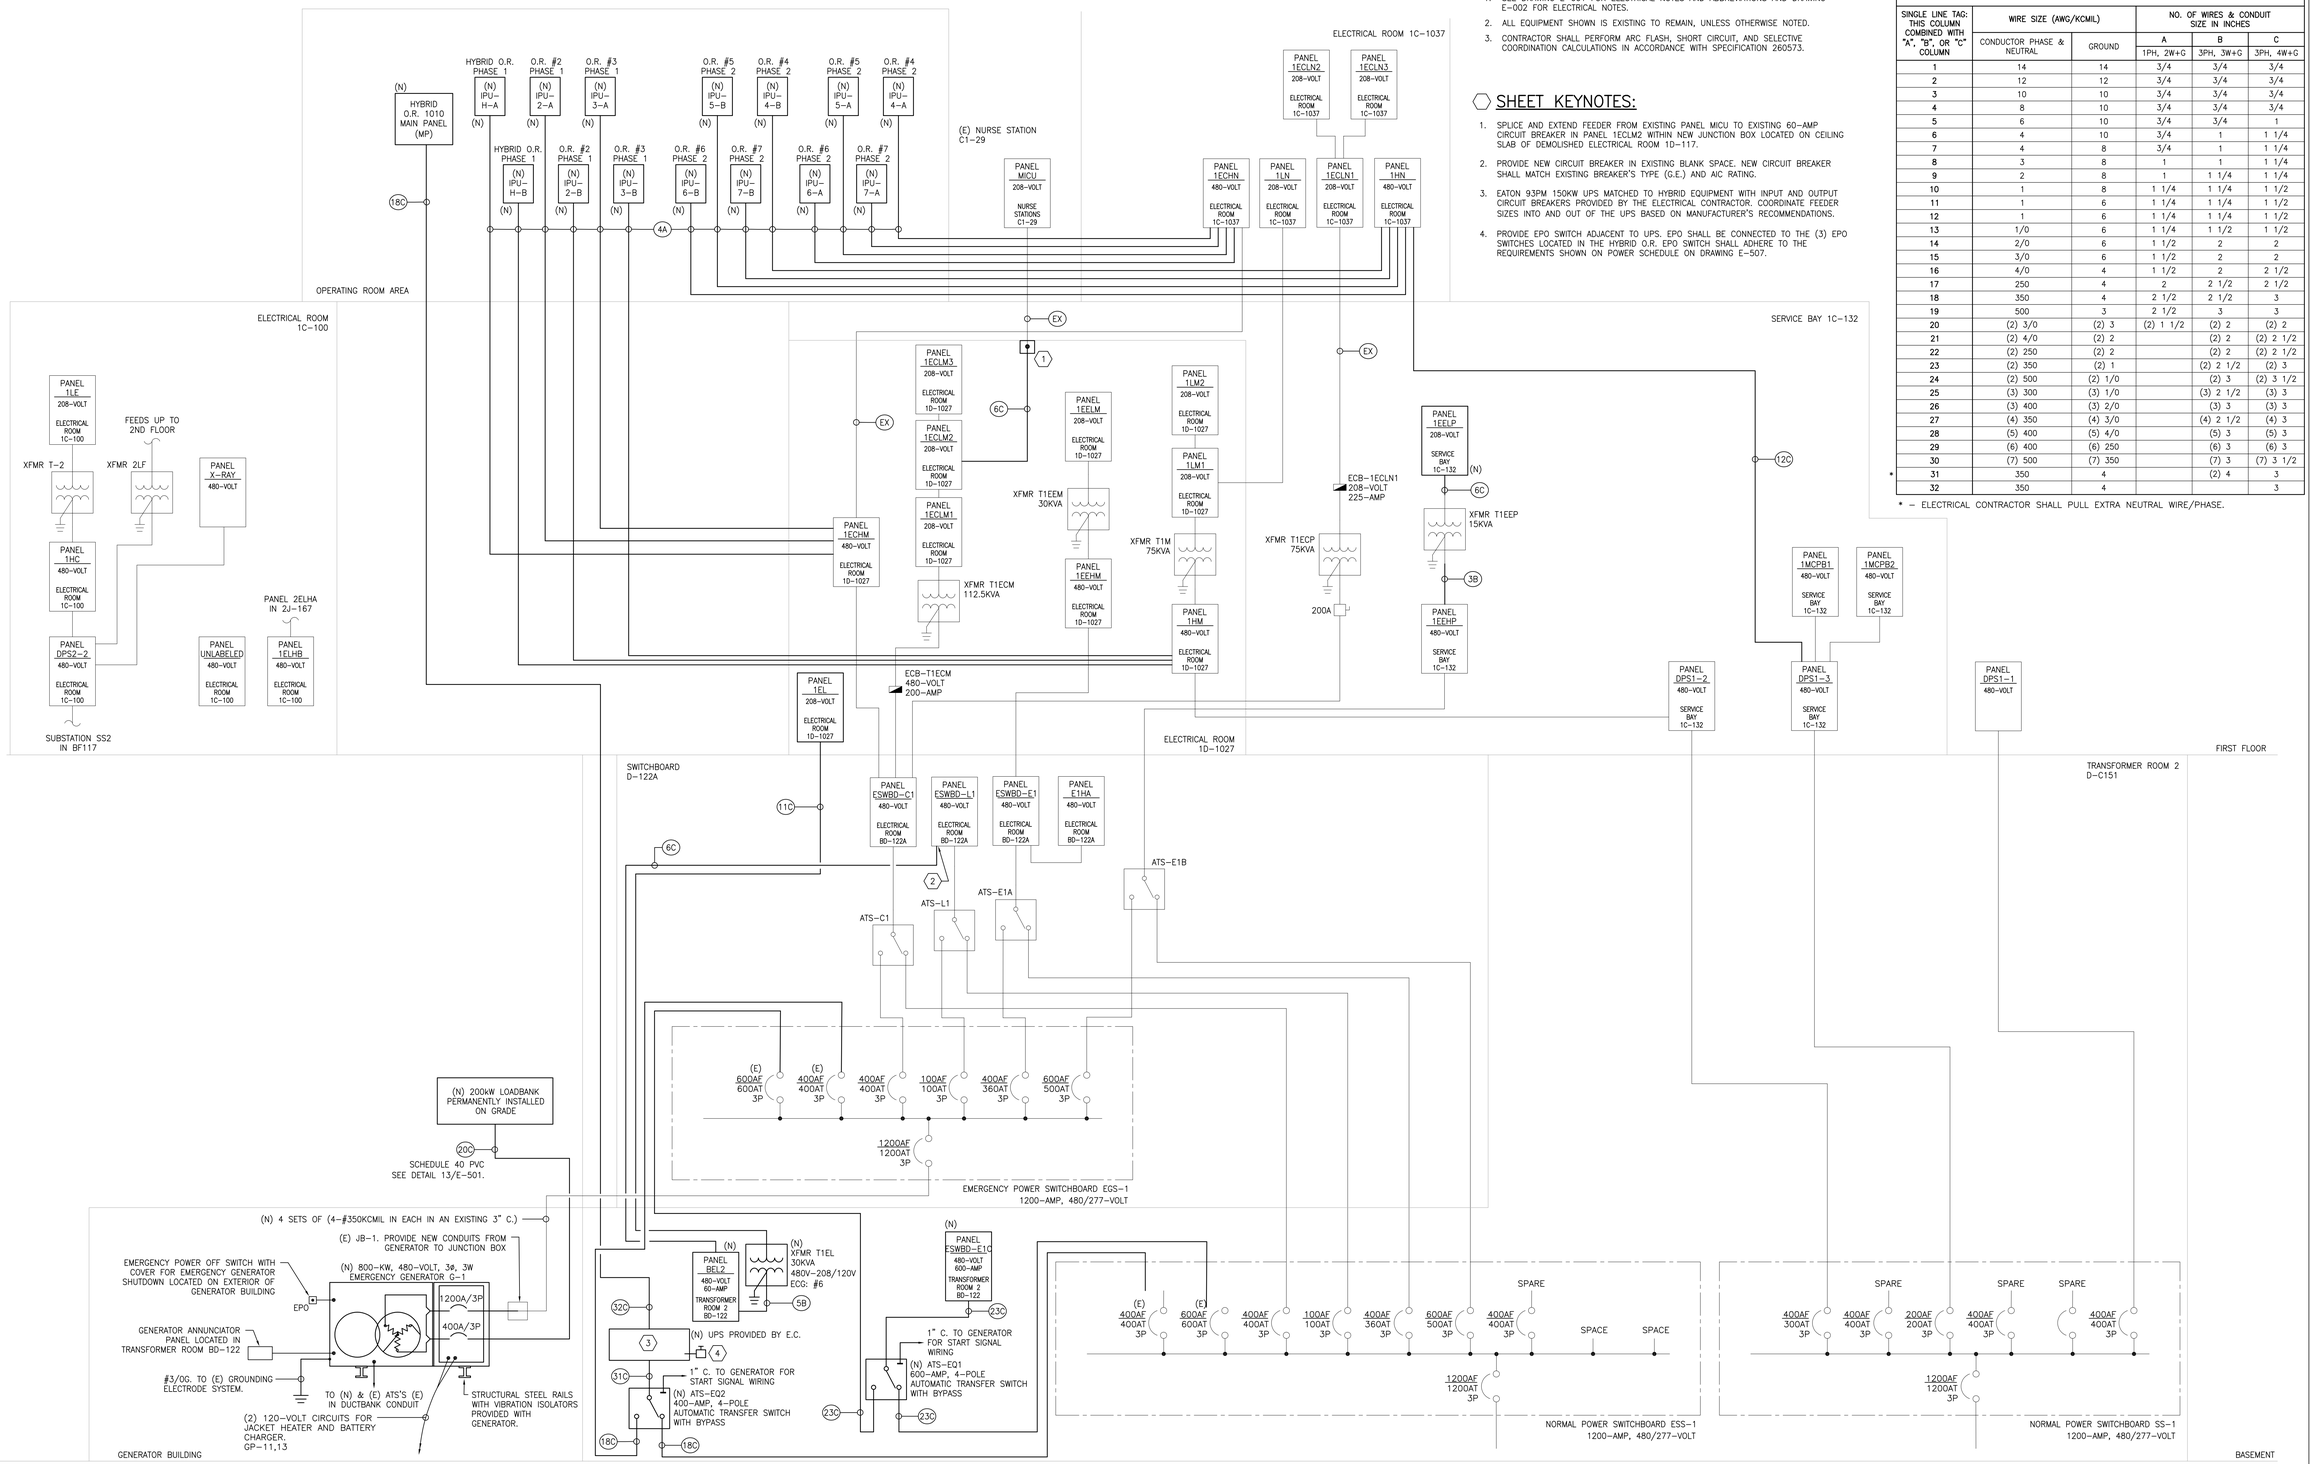

PRINTS OF THIS DRAWING SHALL NOT BE USED FOR ANY PURPOSE WHATSOEVER WITHOUT THE SEAL AND SIGNATURE OF THE PROFESSIONAL ENGINEER.

NO.	DESCRIPTION	DATE

CONSULTANTS

Architecture:	Civil Engineering:	Fire & Life Safety:
PF&A DESIGN, P.C.	LABELLA ASSOCIATES	STANTON ENGINEERING SERVICES, LLC

ENGINEER OF RECORD

MILLER•REMICK
A Service-Disabled Veteran-Owned Small Business
(856) 429-4000 ★ Miller-Remick.com
M-R PROJECT NO. 0499-0136

MILLER-REMICK LLC
PROFESSIONAL ENGINEER

Office of Construction and Facilities Management

VA U.S. Department of Veterans Affairs

Drawing Title: ELECTRICAL NEW WORK SINGLE LINE DIAGRAM	Phase: BID DOCUMENTS	Project Title: RENOVATE SURGICAL SUITE PHASE II Project Number: 658-19-103	VA Drawing Number: 2617
Approved by: Jon Manninen, COR	FULLY SPRINKLERED	Location: SALEM VA MEDICAL CENTER Issue Date: 2025-12-30 / Checked: MJR / Drawn: MJR	Building Number: 143 Drawing Number: E-602

VA FORM 08-6231

P:\0499_DVA\0499-0136 Salem Renovate Surgical Suite\4_Drawings\1_Cad\1_Current Submittal Phase\7_Electrical\E-602.dwg 5-14-26 01:00:49 PM Mranco

three inches = one foot 6"
one and one half inches = one foot 1 0 6"
one inch = one foot 2 0 6"
three quarters inch = one foot 2 0 6"
one half inch = one foot 4 0 6"
three eighths inch = one foot 8 0 4"
one quarter inch = one foot 8 0 4"
one eighth inch = one foot 16 0 8 4 0

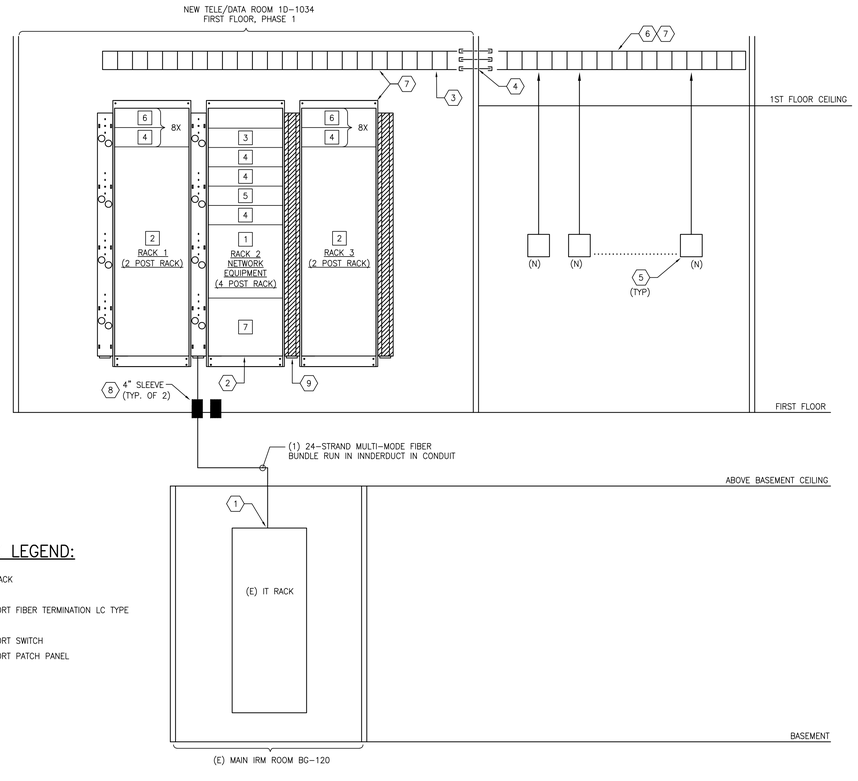

DATA RACK LEGEND:

1. 4-POST NETWORK RACK
2. 2-POST DATA RACK
3. HIGH DENSITY 24-PORT FIBER TERMINATION LC TYPE
4. CABLE MANAGEMENT
5. HIGH DENSITY 48-PORT SWITCH
6. HIGH DENSITY 48-PORT PATCH PANEL
7. UPS

1 TELECOMMUNICATIONS RISER DIAGRAM
SCALE: NONE

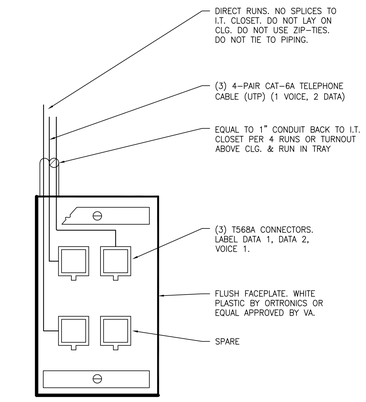

2 TELEPHONE/DATA OUTLET DETAIL
SCALE: NONE

NOTES:

1. TERMINATE & TEST ALL WIRING.

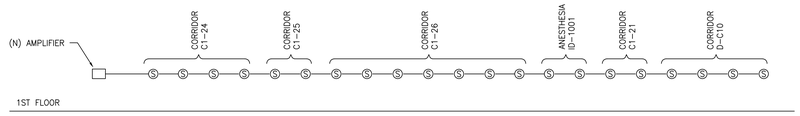

3 PAGING RISER DIAGRAM
SCALE: NONE

GENERAL SHEET NOTES:

1. SEE DRAWINGS E-001 AND E-002 FOR GENERAL NOTES, SYMBOLS AND ABBREVIATIONS.
2. PROVIDE FIRE-RATED SLEEVES IN PARTITIONS AT I.T. CLOSETS & CORRIDORS.
3. TERMINATE AND TEST ALL WIRING.
4. INSTALL SHEETS OF 4' x 8.75' PLYWOOD, PAINTED WITH FIRE RETARDANT PAINT, ON WALL BEHIND TELE/DATA RACKS.

SHEET KEYNOTES:

1. E.C. TO PROVIDE AND INSTALL CONNECTIONS BETWEEN NEW TELE/DATA RACKS AND EXISTING MAIN IRM NETWORK EQUIPMENT. EXISTING NETWORK FIBER SWITCHES HAVE ENOUGH SPARE PORTS TO ACCOMMODATE THE NEW FIBER RUN.

   CONNECTIONS SHALL BE DONE IN MULTI-MODE OPTICAL FIBER, 24-STRAND TERMINATED, LC ENDS AND CERTIFIED.

2. RACK-MOUNTED UPS SHALL BE POWERED VIA A DEDICATED L5-30P TWISTLOCK RECEPTACLE MOUNTED ON THE CEILING ABOVE RACK.

   REFER TO DRAWING P1-EP111 FOR POWER CONNECTIONS.

3. E.C. TO PROVIDE AND INSTALL A WIRE MESH TYPE CABLE TRAY TO RACKS AND ALSO AROUND PERIMETER OF NEW IRM ROOM ID-1002. CABLE TRAY SUPPORTS SHALL COMPLY WITH NEC-392, NEMA V1 AND NEMA FG1 STANDARDS.

   E.C. TO COORDINATE ELEVATION OF CABLE TRAY ABOVE NEW IT RACKS.

   HORIZONTAL WIRE MANAGEMENT SYSTEM (BASIS OF DESIGN), COORDINATE WITH VA FACILITY IT PERSONNEL BEFORE SHOP DRAWING SUBMITTALS:
   - CABLE RUNWAY, 18"W x 10'L, B-LINE PART# SB1718BFB.
   - CROSS MEMBER RADIUS DROP, 18"W, B-LINE PART# SB212918FB
   - WALL ANGLE SUPPORT KIT, 18"W, B-LINE PART# SB211318FB
   - OUTSIDE RADIUS BEND, 18"W, B-LINE PART# SB17VRB18
   - WIRE MESH CABLE TRAY RUNWAY, 16"W x 4"H x 10'L CABLOFIL OR APPROVED EQUAL, PART# CF-105, WITH ACCESSORIES CAN BE USED IN PLACE OF B-LINE LADDER RACK SYSTEM.

4. PROVIDE (3) 4" CONDUITS THROUGH WALL OF NEW TELE/DATA ROOM 1D-1034 ABOVE ACCESSIBLE CEILING FOR IT CABLE PATHWAYS. FIRE SEAL ALL PENETRATIONS. PROVIDE PINK BUSHING CAPS ON EITHER SIDE OF THE CORRIDOR WALL. CAT 6A FILL IN CONDUITS NOT TO EXCEED 40%. ADD CONDUIT IF CONDUITS FILL TO THE 40% LEVEL.

5. ALL NEW JACKS SHALL BE CATEGORY 6A-COMPLIANT EIGHT POSITION RJ-45 NON-KEYED (EIA/TIA 568A).

   ALL NEW OUTLETS SHALL BE QUADPLEX JACKS WITH QUADPLEX FLUSH MOUNTED FACEPLATE. TWO JACKS ARE DESIGNED FOR DATA, ONE JACK FOR VOICE AND THE FOURTH JACK SHALL BE SPARE. SEE DETAIL 2/THIS SHEET FOR FURTHER INFORMATION ON BACKBOX, JACK AND CONDUIT REQUIREMENTS.

   CATEGORY 6A WIRING SHALL BE INSTALLED FROM EACH JACK TO NEW IT RACK AND SHALL BE OF A TYPE DESIGNED TO SUPPORT LEVEL FIVE DATA COMMUNICATION (NOT LESS THAN 100MHz/Mpbs).

   EACH JACK SHALL HOMERUN TO A DIFFERENT JACK PANEL IN NEW TELE/DATA RACK

   EACH UNSHIELDED PAIR WIRE SHALL BE ROUTED IN 1" CONDUIT UP INTO ACCESSIBLE CEILING OR THROUGH HARD CEILING OUT TO CABLE TRAY.

   LEVITON QUICK PORT CAT 6A JACKS PREFERRED. TERMINATIONS T568B. NO DESIGNATION OF VOICE VERSUS DATA, ALL SHOULD BE DESIGNATED BY PATCH PANEL LETTER AND PORT NUMBER (A-19, B-19, C-19, ETC.)

6. PROVIDE AND INSTALL NEW OPEN LADDER TYPE CABLE TRAY 4"H X 12" W ABOVE ACCESSIBLE CEILING AS SHOWN ON "E1" SERIES DRAWINGS. PRIOR TO INSTALLATION, COORDINATE ALL NEW CABLE TRAY LOCATIONS WITH MECHANICAL DUCTWORK TO MAINTAIN ACCESS TO CABLE TRAY. CABLE TRAY SUPPORTS SHALL COMPLY WITH NEC-392, NEMA V1 AND NEMA FG1 STANDARDS.

7. GROUND ALL EQUIPMENT AND CONNECTING HARDWARE WITH APPROVED GROUNDING SYSTEMS ACCORDING TO NFPA/NEC AND ANSI/TIA-607 STANDARDS. CONNECT #6 (THHN) GREEN GROUND WIRE TO AUTHORIZED TELECOMMUNICATION GROUNDING BUSBAR (TGB) USING TWO-HOLE #6 LUGS. (BASIS OF DESIGN) B-LINE PART# SBTGBK.

8. PROVIDE HILTI SLEEVES FOR 4" CONDUIT CABLE PATHWAYS. FIRE SEAL ALL PENETRATIONS. PROVIDE PINK BUSHING CAPS ON EITHER SIDE OF THE SLAB. CAP SPARE CONDUIT STUB-UP FOR FUTURE USE.

9. E.C. TO PROVIDE AND INSTALL POWER STRIP ON ONE SIDE OF THE NEW RACK. POWER STRIP WILL HAVE A TOTAL OF (10) 5-15 STANDARD RECEPTACLES CONNECTED TO THE RACK UPS.

   REFER TO DRAWING P1-EP111 FOR POWER CONNECTIONS.

PRINTS OF THIS DRAWING SHALL NOT BE USED FOR ANY PURPOSE WHATSOEVER WITHOUT THE SEAL AND SIGNATURE OF THE PROFESSIONAL ENGINEER.

NO.	DESCRIPTION	DATE

CONSULTANTS

Architecture:	Civil Engineering:	Fire & Life Safety:
PF&A DESIGN, P.C.	LABELLA ASSOCIATES	STANTON ENGINEERING SERVICES, LLC

ENGINEER OF RECORD
MILLER•REMICK
A Service-Disabled Veteran-Owned Small Business
(856) 429-4000 • Miller-Remick.com
M-R PROJECT NO. 0499-0136

MILLER-REMICK LLC
PROFESSIONAL ENGINEER
COMMONWEALTH OF PENNSYLVANIA REGISTERED PROFESSIONAL ENGINEER THOMAS REGINO ENGINEER No. PE084195
12/30/25

Office of Construction and Facilities Management
VA U.S. Department of Veterans Affairs

Drawing Title: ELECTRICAL TELE/DATA RISER DIAGRAM	Phase: BID DOCUMENTS	Project Title: RENOVATE SURGICAL SUITE PHASE II	VA Drawing Number: 2617
Approved by: Jon Manninen, COR	FULLY SPRINKLERED	Project Number: 658-19-103	Building Number: 143
		Location: SALEM VA MEDICAL CENTER	Drawing Number: E-603
		Issue Date: 2025-12-30 / Checked: MJR / Drawn: MJR	

P:\0499_DWA\0499-0136 Salem Renovate Surgical Suite\4_Drawings\1_Cad\1_Current Submittal Phase\7_Electrical\E-603.dwg 12-29-25 08:25:13 AM MRonca

VA FORM 08-6231

Panel Name: 1EEHP

Panel Voltage: 480Y/277V, 3 Phase, 4 Wire

Existing Panel

Main Lugs Only: ____ Main Breaker: 400

Panel A.I.C. Rating: 35k

ID	Ckt #	Description	Breaker P	Trip	Load Code	Load VA	Phase A	Phase B	Phase C	Load VA	Load Code	Breaker Trip	Breaker P	Description	Ckt #	ID
	1					20166	20166								2	
N	3	**143-AHU-1C1. SEE NOTE 1.**	3	90	AC	20166		20166				70	3	SPARE	4	EX
	5					20166			20166						6	
	7					10415	10415								8	
N	9	**143-AHU-1C2. SEE NOTE 1.**	3	45	AC	10415		10415				70	3	SPARE	10	EX
	11					10415			10415						12	
EX	13	SPARE	3	60								40	3	SPARE	14	EX
	15														16	
EX	17	SPARE	3	40								40	3	SPARE	18	EX
	19														20	
EX	21	SPARE	3	40								40	3	SPARE	22	EX
	23														24	
EX	25	SPARE	3	40								40	3	SPARE	26	EX
	27														28	
EX	29	SPARE	3	40								25	3	SPARE	30	EX
	31														32	
EX	33	SPARE	3	40								25	3	SPARE	34	EX
	35														36	
	37														38	
EX	39	SPARE	3	15								125	3	SPARE (CURRENTLY TEMPORARY FEED TO PANEL 1HN)	40	EX
	41														42	

Total Connected Load: 30581 | 30581 | 30581 (VA/PHASE)

N.E.C. LOAD SUMMARY

Load Types and Codes	Total Load (VA)	Demand Factor	NEC Sizing Load (VA)
Air Conditioning (AC)	91743	1.00	91743
Heating (H)		1.00	
Kitchen Equipment (K)		1.00	
Lighting (L)		1.00	
Receptacles (REC)		1.00	
Existing (E)		1.00	
Continuous (C)		1.00	
Non-Continuous (NC)		1.00	
Refrigeration (REF)		1.00	
Elec. Load Totals:	**91743**		**91743** VA

ELECTRICAL DATA

Total Conn. Load: 92 KVA
Total Conn. Load: 110 Amps
NEC Sizing Load: 92 KVA
NEC Sizing Load: 110 Amps
Main Bus Size: 400 Amps

PANEL LEGEND (ID)

ST - Shunt-Trip C.B.; G - GFI C.B.
LB - "Lock-On" C.B.
"C1" - Contactor Designation
--Remodels--
N - New C.B.; EX - Existing C.B.

PANEL INFORMATION

Location: Service Bay 1C-132
Mounting: Surface Enclosure Type: Nema 1
Fed From: ATS-E1B
Equipment Ground Bus: Yes Bus Material: Copper
Isolated Ground Bus: No Neutral Size: 100%

PANEL NOTES

Note 1: Provide new circuit breaker. New circuit breaker shall match existing breaker's type and AIC rating.

Panel Name: 1ELP

Panel Voltage: 208Y/120V, 3 Phase, 4 Wire

New Panel

Main Lugs Only: ____ Main Breaker: 60

Panel A.I.C. Rating: 22k

ID	Ckt #	Description	Breaker P	Trip	Load Code	Load VA	Phase A	Phase B	Phase C	Load VA	Load Code	Breaker Trip	Breaker P	Description	Ckt #	ID
N	1	**143-CSG-1C1, 143-CSG-1C2**	1	20	NC	720	720					20	1	SPARE	2	N
N	3	**143-AHU-1C1 LIGHTS AND RECEPTACLES**	1	20	REC	500		500				20	1	SPARE	4	N
N	6	**143-AHU-1C2 LIGHTS AND RECEPTACLES**	1	20	REC	500			500			20	1	SPARE	6	N
N	7	**BAS PANEL**	1	20	C	500	500					20	1	SPARE	8	N
N	9	**BAS PANEL**	1	20	C	500		500				20	1	SPARE	10	N
N	11	**BAS PANEL**	1	20	C	500			500			20	1	SPARE	12	N
N	13	**BAS PANEL**	1	20	C	500	500					20	1	SPARE	14	N
N	15	SPARE	1	20								20	1	SPARE	16	N
N	17	SPARE	1	20								20	1	SPARE	18	N
N	19	SPARE	1	20								20	1	SPARE	20	N
N	21	SPARE	1	20								20	1	SPARE	22	N
N	23	SPARE	1	20								20	1	SPARE	24	N
N	25	SPARE	1	20								20	1	SPARE	26	N
N	27	SPARE	1	20								20	1	SPARE	28	N
N	29	SPARE	1	20								20	1	SPARE	30	N

Total Connected Load: 1720 | 1000 | 1000 (VA/PHASE)

N.E.C. LOAD SUMMARY

Load Types and Codes	Total Load (VA)	Demand Factor	NEC Sizing Load (VA)
Air Conditioning (AC)		1.00	
Heating (H)		1.00	
Kitchen Equipment (K)		1.00	
Lighting (L)		1.00	
Receptacles (REC)	1000	1.00	1000
Existing (E)		1.00	
Continuous (C)	2000	1.00	2000
Non-Continuous (NC)	720	1.00	720
Refrigeration (REF)		1.00	
Elec. Load Totals:	**3720**		**3720** VA

ELECTRICAL DATA

Total Conn. Load: 4 KVA
Total Conn. Load: 10 Amps
NEC Sizing Load: 4 KVA
NEC Sizing Load: 10 Amps
Main Bus Size: 100 Amps

PANEL LEGEND (ID)

ST - Shunt-Trip C.B.; G - GFI C.B.
LB - "Lock-On" C.B.
"C1" - Contactor Designation
--Remodels--
N - New C.B.; EX - Existing C.B.

PANEL INFORMATION

Location: Service Bay 1C-132
Mounting: Surface Enclosure Type: Nema 1
Fed From: Panel 1EEHP via XFMR T1EEP
Equipment Ground Bus: Yes Bus Material: Copper
Isolated Ground Bus: No Neutral Size: 100%

PANEL NOTES

Panel Name: 1LN

Panel Voltage: 208Y/120V, 3 Phase, 4 Wire

Existing Panel

Main Lugs Only: **Yes** Main Breaker: ____

Panel A.I.C. Rating: 10k

ID	Ckt #	Description	Breaker P	Trip	Load Code	Load VA	Phase A	Phase B	Phase C	Load VA	Load Code	Breaker Trip	Breaker P	Description	Ckt #	ID
EX	1	**RECPT - CORRIDOR, 1C-127, 125, 122**	1	20	REC	1060	1060					30	2	SPARE	2	EX
EX	3	EXISTING LOAD	1	20	REC	720		720							4	EX
EX	5	EXISTING LOAD	1	20	REC	720			1020	900	REC	20	1	**RECPT - LOUNGE 1C-114A**	6	EX
EX	7	EXISTING LOAD	1	20	REC	720	1720			1000	REC	20	1	**RECPT - LOUNGE 1C-114A, COFFEE**	8	EX
EX	9	EXISTING LOAD	1	20	REC	720		1620		900	REC	20	1	**RECPT - PACU, 1C-111, 1C-110**	10	EX
EX	11	EXISTING LOAD	1	20	REC	720			1780	1060	REC	20	1	**RECPT - 1C-117, 1C-118, CORRIDOR, 1C-119**	12	EX
EX	13	**RECPT - CORRIDOR, ANES 1C-124**	1	20	REC	1060	1780			720	REC	20	1	**RECPT - PACU, 1C-115, HEADWALL**	14	EX
EX	15	**RECPT - OFFICE 1C-157**	1	20	REC	1060		1780		720	REC	20	1	**RECPT - PACU, 1C-115, HEADWALL**	16	EX
EX	17	**RECPT - SHARED OFFICE 1C-156**	1	20	REC	1060			1780	720	REC	20	1	**RECPT - PACU, 1C-115, HEADWALL**	18	EX
EX	19	**RECPT - SHARED OFFICE 1C-156**	1	20	REC	1060	1780			720	REC	20	1	**RECPT - PACU, 1C-115, HEADWALL**	20	EX
EX	21	**RECPT - SHARED OFFICE 1C-156**	1	20	REC	1060		1780		720	REC	20	1	**RECPT - PACU, 1C-115, HEADWALL**	22	EX
EX	23	**RECPT - SHARED OFFICE 1C-156**	1	20	REC	720			1440	720	REC	20	1	**RECPT - PACU, 1C-115, HEADWALL**	24	EX
EX	25	**RECPT - SHARED OFFICE 1C-156**	1	20	REC	1060	1780			720	REC	20	1	**RECPT - PACU, 1C-115, HEADWALL**	26	EX
EX	27	**RECPT - LOUNGE 1C-114A, REFRIG**	1	20	REC	1200		1920		720	REC	20	1	**RECPT - PACU, 1C-115, HEADWALL**	28	EX
EX	29	SPARE	2	30					720	720	REC	20	1	**RECPT - PACU, 1C-115, HEADWALL**	30	EX
EX	31	SPARE					1060			1060	REC	20	1	**RECPT - OFFICE 1C 155**	32	EX
EX	33	SPARE	2	30				900		900	REC	20	1	**RECPT - OFFICE 1C-154**	34	EX
	35								900	900	REC	20	1	**RECPT - OFFICE 1C-153**	36	EX
	37	SPACE					900			900	REC	20	1	**RECPT - OFFICE 1C-152. SEE NOTE 1.**	38	N
	39	SPACE						900		900	REC	20	1	**RECPT - OFFICE 1C-154. SEE NOTE 1.**	40	N
	41	SPACE							900	900	REC	20	1	**RECPT - WAITING 1C-150. SEE NOTE 1.**	42	N

Total Connected Load: 10080 | 9020 | 9140 (VA/PHASE)

N.E.C. LOAD SUMMARY

Load Types and Codes	Total Load (VA)	Demand Factor	NEC Sizing Load (VA)
Air Conditioning (AC)		1.00	
Heating (H)		1.00	
Kitchen Equipment (K)		1.00	
Lighting (L)		1.00	
Receptacles (REC)	28840	0.67	19420
Existing (E)		1.00	
Continuous (C)		1.00	
Non-Continuous (NC)		1.00	
Refrigeration (REF)		1.00	
Elec. Load Totals:	**28840**		**19420** VA

ELECTRICAL DATA

Total Conn. Load: 29 KVA
Total Conn. Load: 80 Amps
NEC Sizing Load: 19 KVA
NEC Sizing Load: 54 Amps
Main Bus Size: 225 Amps

PANEL LEGEND (ID)

ST - Shunt-Trip C.B.; G - GFI C.B.
LB - "Lock-On" C.B.
"C1" - Contactor Designation
--Remodels--
N - New C.B.; EX - Existing C.B.

PANEL INFORMATION

Location: Electrical Room IC-1037
Mounting: Surface Enclosure Type: Nema 1
Fed From: Panel 1LM1
Equipment Ground Bus: Yes Bus Material: Copper
Isolated Ground Bus: No Neutral Size: 100%

PANEL NOTES

Note 1 - Provide new circuit breaker. New circuit breaker shall match existing breaker's type (GE A-series) and AIC rating (10K).

Panel Name: 1HN

Panel Voltage: 480Y/277V, 3 Phase, 4 Wire

Existing Panel

Main Lugs Only: **Yes** Main Breaker: ____

Panel A.I.C. Rating: 14k

ID	Ckt #	Description	Breaker P	Trip	Load Code	Load VA	Phase A	Phase B	Phase C	Load VA	Load Code	Breaker Trip	Breaker P	Description	Ckt #	ID
N	1	**IPU-4-B. SEE NOTE 1.**	2	40	REC	6000	8715			2715	L	20	1	**LIGHTING - PHASE 2 AND PHASE 3**	2	EX
	3				REC	6000		6713		713	L	20	1	**LIGHTING 1C-125, 1C-126**	4	EX
N	5	**IPU-7-B. SEE NOTE 1.**	2	40	REC	6000			6800	800	L	20	1	**LIGHTING - 1C-129, 1C-130**	6	EX
	7				REC	6000	8314			2314	L	20	1	**LIGHTING - PHASE 3 AND PHASE 4**	8	EX
N	9	**IPU-5-B. SEE NOTE 1.**	2	40	REC	6000		6000				20	1	SPARE	10	EX
	11				REC	6000			6000			20	1	SPARE	12	EX
N	13	**IPU-6-B. SEE NOTE 1.**	2	40	REC	6000	6000					20	1	SPARE	14	EX
	15				REC	6000		6000				20	1	SPARE	16	EX
EX	17	SPARE	1	20								20	1	SPARE	18	EX
EX	19	SPARE	1	20								20	1	SPARE	20	EX
EX	21	SPARE	1	20								20	1	SPARE	22	EX
EX	23	SPARE	1	20								20	1	SPARE	24	EX
	25	SPACE												SPACE	26	
	27	SPACE												SPACE	28	
	29	SPACE												SPACE	30	
	31	SPACE												SPACE	32	
	33	SPACE												SPACE	34	
	35	SPACE												SPACE	36	
	37	SPACE												SPACE	38	
	39	SPACE												SPACE	40	
	41	SPACE												SPACE	42	

Total Connected Load: 23029 | 18713 | 12800 (VA/PHASE)

N.E.C. LOAD SUMMARY

Load Types and Codes	Total Load (VA)	Demand Factor	NEC Sizing Load (VA)
Air Conditioning (AC)		1.00	
Heating (H)		1.00	
Kitchen Equipment (K)		1.00	
Lighting (L)	6542	1.00	6542
Receptacles (REC)	48000	0.60	29000
Existing (E)		1.00	
Continuous (C)		1.00	
Non-Continuous (NC)		1.00	
Refrigeration (REF)		1.00	
Elec. Load Totals:	**54542**		**35542** VA

ELECTRICAL DATA

Total Conn. Load: 55 KVA
Total Conn. Load: 66 Amps
NEC Sizing Load: 36 KVA
NEC Sizing Load: 43 Amps
Main Bus Size: 125 Amps

PANEL LEGEND (ID)

ST - Shunt-Trip C.B.; G - GFI C.B.
LB - "Lock-On" C.B.
"C1" - Contactor Designation
--Remodels--
N - New C.B.; EX - Existing C.B.

PANEL INFORMATION

Location: Electrical Room IC-1037
Mounting: Surface Enclosure Type: Nema 1
Fed From: Panel DPS1-3
Equipment Ground Bus: Yes Bus Material: Copper
Isolated Ground Bus: No Neutral Size: 100%

PANEL NOTES

Existing G.E. A-Series II Panelboard.
Note 1: Provide new circuit breaker. New breaker shall match existing circuit breaker type (G.E.) and AIC rating (14kAIC).

Panel Name: 1ECHN

Panel Voltage: 480Y/277V, 3 Phase, 4 Wire

Existing Panel

Main Lugs Only: **Yes** Main Breaker: ____

Panel A.I.C. Rating: 14k

ID	Ckt #	Description	Breaker P	Trip	Load Code	Load VA	Phase A	Phase B	Phase C	Load VA	Load Code	Breaker Trip	Breaker P	Description	Ckt #	ID
EX	1	EXISTING LOAD - TEMP TO 1HN1	1	20	L	500	1200			700	L	20	1	EXISTING LOAD - LTG - ZONE C	2	EX
EX	3	**IPU-6-A. SEE NOTE 1.**	1	35	REC	6000		7240		1240	L	20	1	**LIGHTING - 1C-126**	4	EX
EX	5	**IPU-4-A. SEE NOTE 1.**	1	35	REC	6000			7680	1680	L	20	1	**LIGHTING - 1C-129, 1C-130**	6	EX
EX	7	**IPU-5-A. SEE NOTE 1.**	1	35	REC	6000	8211			2211	L	20	1	**LIGHTING - PHASE 3**	8	EX
EX	9	**IPU-7-A. SEE NOTE 1.**	1	35	REC	6000		6812		812	L	20	1	**LIGHTING - PHASE 3**	10	EX
EX	11	SPARE	1	20					500	500	L	20	1	**EXISTING LOAD - LTG - MECH RM 1066**	12	EX
EX	13	SPARE	1	20			1225			1225	L	20	1	**LIGHTING - PHASE 4**	14	EX
EX	15	SPARE	1	20				812		812	L	20	1	**LIGHTING - PHASE 4**	16	EX
EX	17	SPARE	1	20								20	1	SPARE	18	EX
EX	19	SPARE	1	20								20	1	SPARE	20	EX
EX	21	SPARE	1	20								20	1	SPARE	22	EX
EX	23	SPARE	1	20								20	1	SPARE	24	EX
EX	25	SPARE	1	20								20	1	SPARE	26	EX
	27	SPACE												SPACE	28	
	29	SPACE												SPACE	30	
	31	SPACE												SPACE	32	
	33	SPACE												SPACE	34	
	35	SPACE												SPACE	36	
	37	SPACE												SPACE	38	
	39	SPACE												SPACE	40	
	41	SPACE												SPACE	42	

Total Connected Load: 10636 | 14864 | 8180 (VA/PHASE)

N.E.C. LOAD SUMMARY

Load Types and Codes	Total Load (VA)	Demand Factor	NEC Sizing Load (VA)
Air Conditioning (AC)		1.00	
Heating (H)		1.00	
Kitchen Equipment (K)		1.00	
Lighting (L)	9680	1.00	9680
Receptacles (REC)	24000	0.71	17000
Existing (E)		1.00	
Continuous (C)		1.00	
Non-Continuous (NC)		1.00	
Refrigeration (REF)		1.00	
Elec. Load Totals:	**33680**		**26680** VA

ELECTRICAL DATA

Total Conn. Load: 34 KVA
Total Conn. Load: 41 Amps
NEC Sizing Load: 27 KVA
NEC Sizing Load: 32 Amps
Main Bus Size: 125 Amps

PANEL LEGEND (ID)

ST - Shunt-Trip C.B.; G - GFI C.B.
LB - "Lock-On" C.B.
"C1" - Contactor Designation
--Remodels--
N - New C.B.; EX - Existing C.B.

PANEL INFORMATION

Location: Electrical Room IC-1037
Mounting: Surface Enclosure Type: Nema 1
Fed From: Panel 1ECHM
Equipment Ground Bus: Yes Bus Material: Copper
Isolated Ground Bus: No Neutral Size: 100%

PANEL NOTES

Existing G.E. A-Series II Panelboard.
Note 1: Provide new circuit breaker. New breaker shall match existing circuit breaker type (G.E.) and AIC rating (14kAIC).

Panel Name: 1ECLN1

Panel Voltage: 208Y/120V, 3 Phase, 4 Wire

Existing Panel

Main Lugs Only: ____ Main Breaker: 225

Panel A.I.C. Rating: 10k

ID	Ckt #	Description	Breaker P	Trip	Load Code	Load VA	Phase A	Phase B	Phase C	Load VA	Load Code	Breaker Trip	Breaker P	Description	Ckt #	ID
EX	1	**RECPT - AV RACK (OR-4)**	1	20	REC	500	500							SPACE	2	
EX	3	**RECPT - AV RACK (OR-4)**	1	20	REC	500		500						SPACE	4	
EX	5	**RECPT - NOURISH 1C-114**	1	20	REC	1000			1000			20	1	SPARE	6	EX
EX	7	SPARE	2	60								60	2	SPARE	8	EX
	9														10	
EX	11	SPARE	2	60								60	2	SPARE	12	EX
	13														14	
EX	15	SPARE	2	60				720		720	REC	20	1	**RECPT - NURSE 1C-116A**	16	EX
	17								720	720	REC	20	1	**RECPT - NURSE 1C-116A**	18	EX
EX	19	**RECPT - ANES WORKROOM 1C-127**	1	20	REC	900	1960			1060	REC	20	1	**RECPT - NURSE 1C-116A**	20	EX
EX	21	**RECPT - ANES WORKROOM 1C-127**	1	20	REC	1000		1720		720	REC	20	1	**RECPT - PACU, 1C-116, HEADWALL**	22	EX
EX	23	**RECPT - ANES WORKROOM 1C-127**	1	20	REC	1000			1720	720	REC	20	1	**RECPT - PACU, 1C-116, HEADWALL**	24	EX
EX	25	**RECPT - ANES WORKROOM 1C-127**	1	20	REC	1000	1720			720	REC	20	1	**RECPT - PACU, 1C-116, HEADWALL**	26	EX
EX	27	**RECPT - NOURISH 1C-114**	1	20	REC	1000		1720		720	REC	20	1	**RECPT - PACU, 1C-116, HEADWALL**	28	EX
EX	29	**RECPT - NOURISH 1C-114**	1	20	REC	1000			1720	720	REC	20	1	**RECPT - PACU, 1C-116, HEADWALL**	30	EX
EX	31	SPARE	3	50				720		720	REC	20	1	**RECPT - PACU, 1C-116, HEADWALL**	32	EX
	33								720	720	REC	20	1	**RECPT - PACU, 1C-116, HEADWALL**	34	EX
EX	35	SPARE						720		720	REC	20	1	**RECPT - PACU, 1C-116, HEADWALL**	36	EX
	37								720	720	REC	20	1	**RECPT - PACU, 1C-116, HEADWALL**	38	EX
EX	39	FEEDER TO PANEL 1ECLN3	3	90				1000		1000	REC	20	1	**RECPT - 1C-111**	40	EX
	41								1000	1000	REC	20	1	**RECPT - WAITING 1C-150. SEE NOTE 1.**	42	N

Total Connected Load: 5620 | 6380 | 5880 (VA/PHASE)

N.E.C. LOAD SUMMARY

Load Types and Codes	Total Load (VA)	Demand Factor	NEC Sizing Load (VA)
Air Conditioning (AC)		1.00	
Heating (H)		1.00	
Kitchen Equipment (K)		1.00	
Lighting (L)		1.00	
Receptacles (REC)	17880	0.78	13940
Existing (E)		1.00	
Continuous (C)		1.00	
Non-Continuous (NC)		1.00	
Refrigeration (REF)		1.00	
Elec. Load Totals:	**17880**		**13940** VA

ELECTRICAL DATA

Total Conn. Load: 18 KVA
Total Conn. Load: 50 Amps
NEC Sizing Load: 14 KVA
NEC Sizing Load: 39 Amps
Main Bus Size: 225 Amps

PANEL LEGEND (ID)

ST - Shunt-Trip C.B.; G - GFI C.B.
LB - "Lock-On" C.B.
"C1" - Contactor Designation
--Remodels--
N - New C.B.; EX - Existing C.B.

PANEL INFORMATION

Location: Electrical Room IC-1037
Mounting: Surface Enclosure Type: Nema 1
Fed From: Panel ESWBD-C1 via XFMR T1ECP
Equipment Ground Bus: Yes Bus Material: Copper
Isolated Ground Bus: No Neutral Size: 100%

PANEL NOTES

Panel includes a 125-amp circuit breaker that feeds Panel 1ECLN2

Panel Name: BEL2

Panel Voltage: 208Y/120V, 3 Phase, 4 Wire

New Panel

Main Lugs Only: ____ Main Breaker: 60

Panel A.I.C. Rating: 14k

ID	Ckt #	Description	Breaker P	Trip	Load Code	Load VA	Phase A	Phase B	Phase C	Load VA	Load Code	Breaker Trip	Breaker P	Description	Ckt #	ID
N	1	LIFE SAFETY LIGHTING, PHASE 1 CORRIDOR	1	20	L	756	756					20	1	SPARE	2	N
N	3	LIGHTING - PHASE 2 ,3 ,4	1	20	L	1323		1323				20	1	SPARE	4	N
N	5	SPARE	1	20								20	1	SPARE	6	N
N	7	SPARE	1	20								20	1	SPARE	8	N
N	9	SPARE	1	20								20	1	SPARE	10	N
N	11	SPARE	1	20								20	1	SPARE	12	N
N	13	SPARE	1	20								20	1	SPARE	14	N
N	15	SPARE	1	20								20	1	SPARE	16	N
N	17	SPARE	1	20								20	1	SPARE	18	N
N	19	SPARE	1	20								20	1	SPARE	20	N
N	21	SPARE	1	20								20	1	SPARE	22	N
N	23	SPARE	1	20								20	1	SPARE	24	N
N	25	SPARE	1	20			1700			1700					26	
N	27	SPARE	1	20				1000		1000	C	50	3	FEEDER TO TRANSFORMER T1EL	28	N
N	29	SPARE	1	20					1000	1000					30	

Total Connected Load: 2456 | 2323 | 1000 (VA/PHASE)

N.E.C. LOAD SUMMARY

Load Types and Codes	Total Load (VA)	Demand Factor	NEC Sizing Load (VA)
Air Conditioning (AC)		1.00	
Heating (H)		1.00	
Kitchen Equipment (K)		1.00	
Lighting (L)	2079	1.00	2079
Receptacles (REC)		1.00	
Existing (E)		1.00	
Continuous (C)	3700	1.00	3700
Non-Continuous (NC)		1.00	
Refrigeration (REF)		1.00	
Elec. Load Totals:	**5779**		**5779** VA

ELECTRICAL DATA

Total Conn. Load: 6 KVA
Total Conn. Load: 16 Amps
NEC Sizing Load: 6 KVA
NEC Sizing Load: 16 Amps
Main Bus Size: 225 Amps

PANEL LEGEND (ID)

ST - Shunt-Trip C.B.; G - GFI C.B.
LB - "Lock-On" C.B.
"C1" - Contactor Designation
--Remodels--
N - New C.B.; EX - Existing C.B.

PANEL INFORMATION

Location: Transformer Room 2 BD-122A
Mounting: Surface Enclosure Type: Nema 1
Fed From: Panel ESWBD-L1
Equipment Ground Bus: Yes Bus Material: Copper
Isolated Ground Bus: No Neutral Size: 100%

PANEL NOTES

Panel Name: GP

Panel Voltage: 208Y/120V, 3 Phase, 4 Wire

Existing Panel

Main Lugs Only: ____ Main Breaker: 100

Panel A.I.C. Rating: ____

ID	Ckt #	Description	Breaker P	Trip	Load Code	Load VA	Phase A	Phase B	Phase C	Load VA	Load Code	Breaker Trip	Breaker P	Description	Ckt #	ID
EX	1	EXISTING LOAD	1	20								20	1	EXISTING LOAD - BATTERY CHARGER	2	EX
EX	3	EXISTING LOAD - RECPT	1	20								20	1	EXISTING LOAD - LOUVERS	4	EX
EX	5	EXISTING LOAD - RECPT	1	20								20	1	EXISTING LOAD - DAY TANKS	6	EX
N	7	**143-FOF-1D1. SEE NOTE 1.**	1	20	NC	1176	1176								8	EX
EX	9	EXISTING LOAD - BLOCK HEATER	1	30											10	
N	11	**GENERATOR JACKET HEATER. SEE NOTE 1.**	1	20	NC	500			500			30	3	EXISTING LOAD - BIG HEATER	12	EX
N	13	**GENERATOR BATTERY CHARGER. SEE NOTE 1.**	1	20	NC	500	500								14	
N	15	**143-ACU-1D1. SEE NOTE 1.**	2	30	AC	2288		2288							16	
	17					2288			2288			30	3	EXISTING LOAD - SMALL HEATER	18	EX
	19	SPACE													20	
	21	SPACE												SPACE	22	
	23	SPACE												SPACE	24	

Total Connected Load: 1676 | 2288 | 2788 (VA/PHASE)

N.E.C. LOAD SUMMARY

Load Types and Codes	Total Load (VA)	Demand Factor	NEC Sizing Load (VA)
Air Conditioning (AC)	4576	1.00	4576
Heating (H)		1.00	
Kitchen Equipment (K)		1.00	
Lighting (L)		1.00	
Receptacles (REC)		1.00	
Existing (E)		1.00	
Continuous (C)		1.00	
Non-Continuous (NC)	2176	1.00	2176
Refrigeration (REF)		1.00	
Elec. Load Totals:	**6752**		**6752** VA

ELECTRICAL DATA

Total Conn. Load: 7 KVA
Total Conn. Load: 19 Amps
NEC Sizing Load: 7 KVA
NEC Sizing Load: 19 Amps
Main Bus Size: 100 Amps

PANEL LEGEND (ID)

ST - Shunt-Trip C.B.; G - GFI C.B.
LB - "Lock-On" C.B.
"C1" - Contactor Designation
--Remodels--
N - New C.B.; EX - Existing C.B.

PANEL INFORMATION

Location: Generator Building
Mounting: Surface Enclosure Type: Nema 1
Fed From: Panel 7-GH via integral transformer
Equipment Ground Bus: Yes Bus Material: Copper
Isolated Ground Bus: No Neutral Size: 100%

PANEL NOTES

Note 1: Provide new circuit breaker. New circuit breaker shall match existing breaker's type and AIC rating.

Panel Name: ESWBD-E1C

Panel Voltage: 480Y/277V, 3 Phase, 4 Wire

New Panel

Main Lugs Only: ____ Main Breaker: 600

Panel A.I.C. Rating: 35k

| ID | Ckt # | Description | Brea

Panel Name: 1HM

Panel Voltage: 480Y/277V, 3 Phase, 4 Wire

Existing Panel

Main Lugs Only: | Main Breaker: 225 | Panel A.I.C. Rating: 35k

ID	Ckt #	Description	Breaker P	Trip	Load Code	VA	Phase A	B	C	Load VA	Code	Breaker Trip	P	Description	Ckt #	ID
EX	1	**LIGHTING - PHASE 1 AND PHASE 2 CORRIDORS**	1	20	L	2394	2394					20	1	SPARE	2	EX
EX	3	**LIGHTING - 1D-123, 1D-126**	1	20	L	1000		1000				20	1	SPARE	4	EX
EX	5	**LIGHTING - 1C-126, 1C-128**	1	20	L	1000			1000			20	1	SPARE	6	EX
EX	7	SPARE	1	20								20	1	SPARE	8	EX
EX	9	SPARE	1	20								20	1	SPARE	10	EX
EX	11	SPARE	1	20								20	1	SPARE	12	EX
EX	13	SPARE	1	20								20	1	SPARE	14	EX
EX	15	SPARE	1	20								20	1	SPARE	16	N
N	17	**IPU-H-B. SEE NOTE 1.**	2	40	REC	6000			6000			20	1	SPARE. SEE NOTE 1.	18	N
N	19				REC	6000	6000					20	1	SPARE. SEE NOTE 1.	20	N
N	21	**IPU-2-B. SEE NOTE 1.**	2	40	REC	6000		6000				20	1	SPARE. SEE NOTE 1.	22	N
N	23				REC	6000			6000			20	1	SPARE. SEE NOTE 1.	24	N
N	25	**IPU-3-B. SEE NOTE 1.**	2	40	REC	6000	6000					20	1	SPARE. SEE NOTE 1.	26	N
N	27				REC	6000		6000				20	1	SPARE. SEE NOTE 1.	28	N
N	29	SPARE. SEE NOTE 1.	1	20								20	1	SPARE. SEE NOTE 1.	30	N
N	31	SPARE. SEE NOTE 1.	1	20								20	1	SPARE. SEE NOTE 1.	32	N
N	33	SPARE. SEE NOTE 1.	1	20								20	1	SPARE. SEE NOTE 1.	34	N
N	35	SPARE. SEE NOTE 1.	1	20								20	1	SPARE. SEE NOTE 1.	36	N
N	37	SPARE. SEE NOTE 1.	1	20								20	1	SPARE. SEE NOTE 1.	38	N
N	39	SPARE. SEE NOTE 1.	1	20								20	1	SPARE. SEE NOTE 1.	40	N
N	41	SPARE. SEE NOTE 1.	1	20								20	1	SPARE. SEE NOTE 1.	42	N

Total Connected Load 14394 | 13000 | 13000 (VA/PHASE)

N.E.C. LOAD SUMMARY

Load Types and Codes	Total Load (VA)	Demand Factor	NEC Sizing Load (VA)
Air Conditioning (AC)		1.00	
Heating (H)		1.00	
Kitchen Equipment (K)		1.00	
Lighting (L)	4394	1.00	4394
Receptacles (REC)	36000	0.64	23000
Existing (E)		1.00	
Continuous (C)		1.00	
Non-Continuous (NC)		1.00	
Refrigeration (REF)		1.00	
Elec. Load Totals:	**40394**		**27394** VA

ELECTRICAL DATA

Total Conn. Load: 40 KVA
Total Conn. Load: 49 Amps
NEC Sizing Load: 27 KVA
NEC Sizing Load: 33 Amps
Main Bus Size: 225 Amps

PANEL LEGEND (ID)

ST - Shunt-Trip C.B.; G - GFI C.B.
LB - "Lock-On" C.B.
"C1" - Contactor Designation
--Remodels--
N - New C.B.; EX - Existing C.B.

PANEL INFORMATION

Location: Electrical Room 1D-1027
Mounting: Surface | Enclosure Type: Nema 1
Fed From: Panel DPS1-2
Equipment Ground Bus: Yes | Bus Material: Copper
Isolated Ground Bus: No | Neutral Size: 100%

PANEL NOTES

Existing G.E. A-Series II Panelboard.
Note 1: Provide new circuit breaker. New breaker shall match existing circuit breaker type (G.E.) and AIC rating (14kAIC).

Panel Name: 1ECHM

Panel Voltage: 480Y/277V, 3 Phase, 4 Wire

Existing Panel

Main Lugs Only: | Main Breaker: 150 | Panel A.I.C. Rating: 14k

ID	Ckt #	Description	Breaker P	Trip	Load Code	VA	Phase A	B	C	Load VA	Code	Breaker Trip	P	Description	Ckt #	ID
EX	1	EXISTING LOAD - LTG ZONE C/D	1	20			2268			2268	L	20	1	**LIGHTING - CLEAN CORE 1C-120**	2	EX
EX	3	**HEAT TRACE FOR 1ST FLOOR ROOF PIPING**	1	20	H	1500		3878		2378	L	20	1	**LIGHTING - 1D-123, 1D-126**	4	EX
EX	5	**HEAT TRACE FOR 1ST FLOOR ROOF PIPING**	1	20	H	1500			4215	2715	L	20	1	**LIGHTING - 1C-126, 1C-127, 1C-128**	6	EX
EX	7	SPARE	1	20								20	1	SPARE	8	EX
EX	9	SPARE	1	20								20	1	SPARE	10	EX
EX	11	SPARE	1	20								20	1	SPARE	12	EX
N	13	**IPU-H-A. SEE NOTE 1.**	1	35	REC	6000	6000					20	1	SPARE. SEE NOTE 1.	14	N
N	15	**IPU-3-A. SEE NOTE 1.**	1	35	REC	6000		6000				20	1	SPARE. SEE NOTE 1.	16	N
N	17	**IPU-3-A. SEE NOTE 1.**	1	35	REC	6000			6000			20	1	SPARE. SEE NOTE 1.	18	N
N	19	SPARE. SEE NOTE 1.	1	20								20	1	SPARE. SEE NOTE 1.	20	N
N	21	SPARE. SEE NOTE 1.	1	20								20	1	SPARE. SEE NOTE 1.	22	N
N	23	SPARE. SEE NOTE 1.	1	20								20	1	SPARE. SEE NOTE 1.	24	N
N	25	SPARE. SEE NOTE 1.	1	20								20	1	SPARE. SEE NOTE 1.	26	N
N	27	SPARE. SEE NOTE 1.	1	20								20	1	SPARE. SEE NOTE 1.	28	N
N	29	SPARE. SEE NOTE 1.	1	20								20	1	SPARE. SEE NOTE 1.	30	N
N	31	SPARE. SEE NOTE 1.	1	20								20	1	SPARE. SEE NOTE 1.	32	N
N	33	SPARE. SEE NOTE 1.	1	20								20	1	SPARE. SEE NOTE 1.	34	N
N	35	SPARE. SEE NOTE 1.	1	20								20	1	SPARE. SEE NOTE 1.	36	N
N	37	SPARE. SEE NOTE 1.	1	20								20	1	SPARE. SEE NOTE 1.	38	N
N	39	SPARE. SEE NOTE 1.	1	20								20	1	SPARE. SEE NOTE 1.	40	N
N	41	SPARE. SEE NOTE 1.	1	20								20	1	SPARE. SEE NOTE 1.	42	N

Total Connected Load 8268 | 9878 | 10215 (VA/PHASE)

N.E.C. LOAD SUMMARY

Load Types and Codes	Total Load (VA)	Demand Factor	NEC Sizing Load (VA)
Air Conditioning (AC)		1.00	
Heating (H)	3000	1.00	3000
Kitchen Equipment (K)		1.00	
Lighting (L)	7361	1.00	7361
Receptacles (REC)	18000	0.78	14000
Existing (E)		1.00	
Continuous (C)		1.00	
Non-Continuous (NC)		1.00	
Refrigeration (REF)		1.00	
Elec. Load Totals:	**28361**		**24361** VA

ELECTRICAL DATA

Total Conn. Load: 28 KVA
Total Conn. Load: 34 Amps
NEC Sizing Load: 24 KVA
NEC Sizing Load: 29 Amps
Main Bus Size: 225 Amps

PANEL LEGEND (ID)

ST - Shunt-Trip C.B.; G - GFI C.B.
LB - "Lock-On" C.B.
"C1" - Contactor Designation
--Remodels--
N - New C.B.; EX - Existing C.B.

PANEL INFORMATION

Location: Electrical Room 1D-1027
Mounting: Surface | Enclosure Type: Nema 1
Fed From: Panel ESWBD-C1
Equipment Ground Bus: Yes | Bus Material: Copper
Isolated Ground Bus: No | Neutral Size: 100%

PANEL NOTES

Existing G.E. A-Series II Panelboard.
Note 1: Provide new circuit breaker. New breaker shall match existing circuit breaker type (G.E.) and AIC rating (14kAIC).

Panel Name: 1ECLM1

Panel Voltage: 208Y/120V, 3 Phase, 4 Wire

Existing Panel

Main Lugs Only: | Main Breaker: 400 | Panel A.I.C. Rating: 10k

ID	Ckt #	Description	Breaker P	Trip	Load Code	VA	Phase A	B	C	Load VA	Code	Breaker Trip	P	Description	Ckt #	ID
	1														2	
EX	3	SPARE	2	60								60	2	SPARE	4	EX
	5														6	
EX	7	SPARE	2	60								60	2	SPARE	8	EX
	9														10	
EX	11	SPARE	2	45								45	2	SPARE	12	EX
EX	13	**NURSE CALL TERMINAL CABINET**	1	20	C	500	1560			1060	REC	20	1	**RECPT - CONTROL ROOM 1D-124**	14	EX
EX	15	EXISTING LOAD	1	20				1060		1060	REC	20	1	**RECPT - CONTROL ROOM 1D-124**	16	EX
EX	17	EXISTING LOAD	1	20					500	500	C	20	1	**RECPT - AV RACK (OR-2)**	18	EX
EX	19	RECPT - 122, 120	1	20	REC	720	1220			500	C	20	1	**RECPT - AV RACK (OR-3)**	20	EX
EX	21	EXISTING LOAD	1	20				1060		1060	REC	20	1	**RECPT - CLEAN CORE 1C-120**	22	EX
EX	23	EXISTING LOAD	1	20					720	720	REC	20	1	**RECPT - CLEAN CORE 1C-120**	24	EX
EX	25	EXISTING LOAD	1	20			900			900	REC	20	1	**RECPT - CLEAN CORE 1C-120**	26	EX
EX	27	EXISTING LOAD	1	20				900		900	REC	20	1	**RECPT - CLEAN CORE 1C-120**	28	EX
EX	29	EXISTING LOAD	1	20					1000	1000	REC	20	1	**RECPT - CLEAN CORE 1C-120**	30	EX
EX	31	**RECPT - 1C-120, 1D-120**	1	20	REC	900	1900			1000	REC	20	1	**RECPT - CLEAN CORE 1C-120**	32	EX
N	33	**RACK - 1D-120**	2	30	C	1500		2220		720	REC	20	1	**RECPT - CLEAN CORE 1C-120**	34	EX
	35				C	1500			2220	720	REC	20	1	**RECPT - CLEAN CORE 1C-120**	36	EX
N	37	**RACK - 1D-120**	2	30	C	1500	2000			500	REC	20	1	**RECPT - AV RACK (OR-6)**	38	EX
	39				C	1500		2000		500	REC	20	1	**RECPT - AV RACK (OR-7)**	40	EX
EX	41	**RECPT - AV RACK (HYBRID)**	1	20	C	500			1560	1060	REC	20	1	**RECPT - COMM CTR 1C-106**	42	EX

Total Connected Load 7580 | 7240 | 6000 (VA/PHASE)

N.E.C. LOAD SUMMARY

Load Types and Codes	Total Load (VA)	Demand Factor	NEC Sizing Load (VA)
Air Conditioning (AC)		1.00	
Heating (H)		1.00	
Kitchen Equipment (K)		1.00	
Lighting (L)		1.00	
Receptacles (REC)	12820	0.89	11410
Existing (E)		1.00	
Continuous (C)	8000	1.00	8000
Non-Continuous (NC)		1.00	
Refrigeration (REF)		1.00	
Elec. Load Totals:	**20820**		**19410** VA

ELECTRICAL DATA

Total Conn. Load: 21 KVA
Total Conn. Load: 58 Amps
NEC Sizing Load: 19 KVA
NEC Sizing Load: 54 Amps
Main Bus Size: 400 Amps

PANEL LEGEND (ID)

ST - Shunt-Trip C.B.; G - GFI C.B.
LB - "Lock-On" C.B.
"C1" - Contactor Designation
--Remodels--
N - New C.B.; EX - Existing C.B.

PANEL INFORMATION

Location: Electrical Room 1D-1027
Mounting: Flush | Enclosure Type: Nema 1
Fed From: Panel ESWBD-C1 via XFMR T1ECM
Equipment Ground Bus: Yes | Bus Material: Copper
Isolated Ground Bus: No | Neutral Size: 100%

PANEL NOTES

Existing G.E. A-Series II Panelboard.
Note 1: Provide new circuit breaker. New breaker shall match existing circuit breaker type (G.E.) and AIC rating (14kAIC).

Panel Name: 1LM1

Panel Voltage: 208Y/120V, 3 Phase, 4 Wire

Existing Panel

Main Lugs Only: | Main Breaker: 225 | Panel A.I.C. Rating:

ID	Ckt #	Description	Breaker P	Trip	Load Code	VA	Phase A	B	C	Load VA	Code	Breaker Trip	P	Description	Ckt #	ID
	1														2	
EX	3	FEEDER TO PANEL 1LM2	3	100								30	2	SPARE	4	EX
	5														6	
EX	7	EXISTING LOAD	1	20								30	2	SPARE	8	EX
EX	9	EXISTING LOAD	1	20											10	
EX	11	EXISTING LOAD	1	20								30	2	SPARE	12	EX
EX	13	EXISTING LOAD	1	20								20	1	EXISTING LOAD	14	EX
EX	15	EXISTING LOAD	1	20				900		900	REC	20	1	**RECPT - CORRIDORS, 121, 122**	16	EX
EX	17	EXISTING LOAD	1	20					1060	1060	REC	20	1	**RECPT - C1-19, 124**	18	EX
EX	19	EXISTING LOAD	1	20			360			360	REC	20	1	**RECPT - CLEAN CORE 1C-120**	20	EX
EX	21	EXISTING LOAD	1	20				1060		1060	REC	20	1	**RECPT - CORRIDORS, PHASE 2 NORTH**	22	EX
EX	23	EXISTING LOAD	1	20					900	900	REC	20	1	**RECPT - PRE-OP 1C-105, CORRIDORS**	24	EX
EX	25	EXISTING LOAD	1	20			720			720	REC	20	1	**RECPT - COMM CTR 1C-106**	26	EX
EX	27	EXISTING LOAD	1	20				900		900	REF	20	1	**RECPT - PRE-OP 1C-106**	28	EX
EX	29	SPARE	1	20								20	1	SPARE	30	EX
EX	31	SPARE	2	30								20	1	SPARE	32	EX
	33											20	1	SPARE	34	EX
EX	35	SPARE	2	30								20	1	SPARE	36	EX
	37											20	1	SPARE	38	EX
	39	SPACE												SPACE	40	
	41	SPACE												SPACE	42	

Total Connected Load 1080 | 2860 | 1960 (VA/PHASE)

N.E.C. LOAD SUMMARY

Load Types and Codes	Total Load (VA)	Demand Factor	NEC Sizing Load (VA)
Air Conditioning (AC)		1.00	
Heating (H)		1.00	
Kitchen Equipment (K)		1.00	
Lighting (L)		1.00	
Receptacles (REC)	5000	1.00	5000
Existing (E)		1.00	
Continuous (C)		1.00	
Non-Continuous (NC)		1.00	
Refrigeration (REF)	900	1.00	900
Elec. Load Totals:	**5900**		**5900** VA

ELECTRICAL DATA

Total Conn. Load: 6 KVA
Total Conn. Load: 16 Amps
NEC Sizing Load: 6 KVA
NEC Sizing Load: 16 Amps
Main Bus Size: 225 Amps

PANEL LEGEND (ID)

ST - Shunt-Trip C.B.; G - GFI C.B.
LB - "Lock-On" C.B.
"C1" - Contactor Designation
--Remodels--
N - New C.B.; EX - Existing C.B.

PANEL INFORMATION

Location: Electrical Room 1D-1027
Mounting: Surface | Enclosure Type: Nema 1
Fed From: Panel 1HM via XFMR T1M
Equipment Ground Bus: Yes | Bus Material: Copper
Isolated Ground Bus: No | Neutral Size: 100%

PANEL NOTES

Existing G.E. A-Series II Panelboard.
Includes a 125-amp circuit breaker for (N) Panel 1LN
Note 1: Provide new circuit breaker. New breaker shall match existing circuit breaker type (G.E.) and AIC rating

Panel Name: 1EEHM

Panel Voltage: 480Y/277V, 3 Phase, 4 Wire

Existing Panel

Main Lugs Only: | Main Breaker: 225 | Panel A.I.C. Rating:

ID	Ckt #	Description	Breaker P	Trip	Load Code	VA	Phase A	B	C	Load VA	Code	Breaker Trip	P	Description	Ckt #	ID
	1						2050			2050					2	
EX	3	EX. LOAD - 143-1D-HWP1	3	15				3210		3210	REC	45	3	**FEEDER TO PANEL 1EELM VIA XFRM T1EEM**	4	EX
	5								2020	2020					6	
EX	7														8	
	9	EX. LOAD - 143-1D-HWP2	3	15								??	3	EX. LOAD - 143-1D-RTU1 (SF)	10	EX
	11														12	
	13														14	
EX	15	EX. LOAD - 143-1D-EF4	3	15								??	3	SPARE	16	EX
	17														18	
	19				AC	443	443								20	
N	21	**143-EF-2C1A. SEE NOTE 1.**	3	15	AC	443		443				30	3	SPARE	22	EX
	23				AC	443			443						24	
	25				AC	443	443								26	
N	27	**143-EF-2C1B. SEE NOTE 1.**	3	15	AC	443		443				35	3	EX. LOAD - 143-1D-RTU1 (RF)	28	EX
	29				AC	443			443						30	
	31	SPACE												SPACE	32	
	33	SPACE												SPACE	34	
	35	SPACE												SPACE	36	
	37	SPACE												SPACE	38	
	39	SPACE												SPACE	40	
	41	SPACE												SPACE	42	

Total Connected Load 2936 | 4096 | 2906 (VA/PHASE)

N.E.C. LOAD SUMMARY

Load Types and Codes	Total Load (VA)	Demand Factor	NEC Sizing Load (VA)
Air Conditioning (AC)	2658	1.00	2658
Heating (H)		1.00	
Kitchen Equipment (K)		1.00	
Lighting (L)		1.00	
Receptacles (REC)	7280	1.00	7280
Existing (E)		1.00	
Continuous (C)		1.00	
Non-Continuous (NC)		1.00	
Refrigeration (REF)		1.00	
Elec. Load Totals:	**9938**		**9938** VA

ELECTRICAL DATA

Total Conn. Load: 10 KVA
Total Conn. Load: 12 Amps
NEC Sizing Load: 10 KVA
NEC Sizing Load: 12 Amps
Main Bus Size: 225 Amps

PANEL LEGEND (ID)

ST - Shunt-Trip C.B.; G - GFI C.B.
LB - "Lock-On" C.B.
"C1" - Contactor Designation
--Remodels--
N - New C.B.; EX - Existing C.B.

PANEL INFORMATION

Location: Electrical Room 1D-1027
Mounting: Surface | Enclosure Type: Nema 1
Fed From: Panel ESWBD-E1
Equipment Ground Bus: Yes | Bus Material: Copper
Isolated Ground Bus: No | Neutral Size: 100%

PANEL NOTES

Existing G.E. A-Series II Panelboard.
Note 1: Provide new circuit breaker. New breaker shall match existing circuit breaker type (G.E.) and AIC rating (14kAIC).

Panel Name: 1ECLM2

Panel Voltage: 208Y/120V, 3 Phase, 4 Wire

New Panel

Main Lugs Only: Yes | Main Breaker: | Panel A.I.C. Rating: 10k

ID	Ckt #	Description	Breaker P	Trip	Load Code	VA	Phase A	B	C	Load VA	Code	Breaker Trip	P	Description	Ckt #	ID
	1														2	
EX	3	FEEDER TO PANEL 1ECLM3	3	100	REC							60	3	FEEDER TO PANEL MICU	4	EX
	5														6	
EX	7	EXISTING LOAD	1	20								20	1	EXISTING LOAD	8	EX
EX	9	EXISTING LOAD	1	20								20	1	EXISTING LOAD	10	EX
EX	11	EXISTING LOAD	1	20								20	1	EXISTING LOAD	12	EX
EX	13	EXISTING LOAD	1	20								20	1	EXISTING LOAD	14	EX
EX	15	EXISTING LOAD	1	20								20	1	EXISTING LOAD	16	EX
EX	17	EXISTING LOAD	1	20					720	720	REC	20	1	**RECPT - PRE-OP 1C-106 HEADWALL**	18	EX
EX	19	EXISTING LOAD	1	20			720			720	REC	20	1	**RECPT - PRE-OP 1C-106 HEADWALL**	20	EX
EX	21	**RECPT - PRE-OP 1C-106**	1	20	REC	1000		1720		720	REC	20	1	**RECPT - PRE-OP 1C-106 HEADWALL**	22	EX
EX	23	EXISTING LOAD	1	20					720	720	REC	20	1	**RECPT - PRE-OP 1C-106 HEADWALL**	24	EX
EX	25	EXISTING LOAD	1	20			720			720	REC	20	1	**RECPT - PRE-OP 1C-106 HEADWALL**	26	EX
EX	27	EXISTING LOAD	1	20				720		720	REC	20	1	**RECPT - PRE-OP 1C-106 HEADWALL**	28	EX
EX	29	EXISTING LOAD	1	20					720	720	REC	20	1	**RECPT - PRE-OP 1C-106 HEADWALL**	30	EX
EX	31	EXISTING LOAD	1	20			720			720	REC	20	1	**RECPT - PRE-OP 1C-106 HEADWALL**	32	EX
EX	33	**RECPT - NURSE STATION 1C-106A**	1	20	REC	720		1440		720	REC	20	1	**RECPT - PRE-OP 1C-106 HEADWALL**	34	EX
EX	35	**RECPT - NURSE STATION 1C-106A**	1	20	REC	720			1440	720	REC	20	1	**RECPT - PRE-OP 1C-106 HEADWALL**	36	EX
EX	37	**RECPT - NURSE STATION 1C-106A**	1	20	REC	1000	1000					20	1	SPARE	38	EX
EX	39	**RECPT - MEDS 1C-113**	1	20	REC	540		540				20	1	SPARE	40	EX
EX	41	**RECPT - MEDS 1C-113**	1	20	REC	1000			1000			20	1	SPARE	42	EX

Total Connected Load 3160 | 4420 | 4600 (VA/PHASE)

N.E.C. LOAD SUMMARY

Load Types and Codes	Total Load (VA)	Demand Factor	NEC Sizing Load (VA)
Air Conditioning (AC)		1.00	
Heating (H)		1.00	
Kitchen Equipment (K)		1.00	
Lighting (L)		1.00	
Receptacles (REC)	12180	0.91	11090
Existing (E)		1.00	
Continuous (C)		1.00	
Non-Continuous (NC)		1.00	
Refrigeration (REF)		1.00	
Elec. Load Totals:	**12180**		**11090** VA

ELECTRICAL DATA

Total Conn. Load: 12 KVA
Total Conn. Load: 34 Amps
NEC Sizing Load: 11 KVA
NEC Sizing Load: 31 Amps
Main Bus Size: 225 Amps

PANEL LEGEND (ID)

ST - Shunt-Trip C.B.; G - GFI C.B.
LB - "Lock-On" C.B.
"C1" - Contactor Designation
--Remodels--
N - New C.B.; EX - Existing C.B.

PANEL INFORMATION

Location: Electrical Room 1D-1027
Mounting: Surface | Enclosure Type: Nema 1
Fed From: Panel ECLM1 via feedthrough lugs
Equipment Ground Bus: Yes | Bus Material: Copper
Isolated Ground Bus: No | Neutral Size: 100%

PANEL NOTES

Existing G.E. A-Series II Panelboard.
Note 1: Provide new circuit breaker. New breaker shall match existing circuit breaker type (G.E.) and AIC rating (10kAIC).

Panel Name: 1LM2

Panel Voltage: 208Y/120V, 3 Phase, 4 Wire

Existing Panel

Main Lugs Only: | Main Breaker: 125 | Panel A.I.C. Rating: 14k

ID	Ckt #	Description	Breaker P	Trip	Load Code	VA	Phase A	B	C	Load VA	Code	Breaker Trip	P	Description	Ckt #	ID
EX	1	EXISTING LOAD	1	20								20	1	EXISTING LOAD	2	EX
EX	3	EXISTING LOAD	1	20								20	1	EXISTING LOAD	4	EX
EX	5	EXISTING LOAD	1	20								20	1	EXISTING LOAD	6	EX
EX	7	EXISTING LOAD	1	20								20	1	EXISTING LOAD	8	EX
EX	9	EXISTING LOAD	1	20								20	1	EXISTING LOAD	10	EX
EX	11	EXISTING LOAD	1	20								20	1	SPARE	12	EX
EX	13	**RECPT - PRE-OP 1C-105 HEADWALL**	1	20	REC	720	720					20	1	SPARE	14	EX
EX	15	**RECPT - PRE-OP 1C-105 HEADWALL**	1	20	REC	720		720				20	1	SPARE	16	EX
EX	17	**RECPT - PRE-OP 1C-105 HEADWALL**	1	20	REC	720			720			20	1	SPARE	18	EX
EX	19	**RECPT - PRE-OP 1C-105 HEADWALL**	1	20	REC	720	720					20	1	SPARE	20	EX
EX	21	**RECPT - PRE-OP 1C-105 HEADWALL**	1	20	REC	720		720				20	1	SPARE	22	EX
EX	23	**RECPT - PRE-OP 1C-105 HEADWALL**	1	20	REC	720			720			20	1	SPARE	24	EX
EX	25	**RECPT - PRE-OP 1C-105 HEADWALL**	1	20	REC	720	720					20	1	SPARE	26	EX
EX	27	**RECPT - PRE-OP 1C-105 HEADWALL**	1	20	REC	720		720				20	1	SPARE	28	EX
EX	29	**RECPT - PRE-OP 1C-105 HEADWALL**	1	20	REC	720			720			20	1	SPARE	30	EX
EX	31	**RECPT - PRE-OP 1C-105 HEADWALL**	1	20	REC	720	720					20	1	SPARE	32	EX
EX	33	SPARE	1	20								20	1	SPARE	34	EX
EX	35	SPARE	1	20								20	1	SPARE	36	EX
EX	37	SPARE	1	20								20	1	SPARE	38	EX
EX	39	SPARE	1	20								20	1	SPARE	40	EX
	41	SPACE												SPACE	42	

Total Connected Load 2880 | 2160 | 2160 (VA/PHASE)

N.E.C. LOAD SUMMARY

Load Types and Codes	Total Load (VA)	Demand Factor	NEC Sizing Load (VA)
Air Conditioning (AC)		1.00	
Heating (H)		1.00	
Kitchen Equipment (K)		1.00	
Lighting (L)		1.00	
Receptacles (REC)	7200	1.00	7200
Existing (E)		1.00	
Continuous (C)		1.00	
Non-Continuous (NC)		1.00	
Refrigeration (REF)		1.00	
Elec. Load Totals:	**7200**		**7200** VA

ELECTRICAL DATA

Total Conn. Load: 7 KVA
Total Conn. Load: 20 Amps
NEC Sizing Load: 7 KVA
NEC Sizing Load: 20 Amps
Main Bus Size: 225 Amps

PANEL LEGEND (ID)

ST - Shunt-Trip C.B.; G - GFI C.B.
LB - "Lock-On" C.B.
"C1" - Contactor Designation
--Remodels--
N - New C.B.; EX - Existing C.B.

PANEL INFORMATION

Location: Electrical Room 1D-1027
Mounting: Surface | Enclosure Type: Nema 1
Fed From: Panel 1LM1
Equipment Ground Bus: Yes | Bus Material: Copper
Isolated Ground Bus: No | Neutral Size: 100%

PANEL NOTES

Existing G.E. A-Series II Panelboard.
Note 1: Provide new circuit breaker. New breaker shall match existing circuit breaker type (G.E.) and AIC rating (14kAIC).

Panel Name: 1EELM

Panel Voltage: 208Y/120V, 3 Phase, 4 Wire

Existing Panel

Main Lugs Only: | Main Breaker: 100 | Panel A.I.C. Rating: 10k

ID	Ckt #	Description	Breaker P	Trip	Load Code	VA	Phase A	B	C	Load VA	Code	Breaker Trip	P	Description	Ckt #	ID
EX	1			15		

GENERAL SHEET NOTES:

1. REFER TO DRAWING E-001 AND E-002 FOR NOTES, SYMBOLS & ABBREVIATIONS.
2. ISOLATION PANELS TO BE PROVIDED WITH ISOLATION TRANSFORMER RATED AT 220°C INSULATION SYSTEM- 80° C TEMPERATURE RISE, 30 dB SOUND LEVEL, NON-VENTILATED, AND ELECTROSTATIC SHIELD BETWEEN THE PRIMARY AND SECONDARY WINDINGS.
3. ISOLATION PANELS TO BE PROVIDED WITH PRIMARY CIRCUIT BREAKER AND 2-POLE SECONDARY CIRCUIT BREAKER. ALL PANELS SHALL BE PROVIDED TO ACCEPT 16 SECONDARY BREAKERS PER UL.
4. ISOLATION PANELS TO BE FLUSH MOUNTED, FRONT TRIM #304 STAINLESS STEEL WITH A BRUSHED FINISH TO ENSURE CORROSION RESISTANCE AND EASE OF CLEANING.
5. ISOLATION PANELS SHALL BE PROVIDED TO THE FIELD COMPLETELY FACTORY WIRED AND TESTED. FIELD WIRING BY THE CONTRACTOR SHOULD INVOLVE JUST THE CONNECTIONS OF THE PRIMARY FEEDERS AND SECONDARY CIRCUITS TO THE TERMINALS.
6. REFER TO DRAWING E-602 FOR NEW WORK SINGLE LINE DIAGRAM AND DRAWINGS P1-EP111, P2-EP111 AND P3-EP111.A FOR POWER FLOOR PLANS.

ISOLATION PANEL IPU-2-A — LOCATION: O.R. 2 1D-125

FED FROM PANEL 1ECHM CIRCUIT 15
120V, 1ø, 2W, WITH LINE ISOLATION MONITOR.

DESCRIPTION	Bkr	No.	No.	Bkr	DESCRIPTION
WALL GROUND MODULE	20/2	1	2	20/2	WALL GROUND MODULE
WALL GROUND MODULE	20/2	3	4	20/2	BOOM TYPE "C6" RECEPTACLES
EMS BRAKING SYSTEM – BOOM "C6"	20/2	5	6	20/2	BOOM TYPE "C6" RECEPTACLES
PYXSIS MACHINE	20/2	7	8	20/2	BOOM TYPE "C6" RECEPTACLES
EMS BRAKING SYSTEM – BOOM "C5"	20/2	9	10	20/2	BOOM TYPE "C6" RECEPTACLES
BOOM TYPES "B" MONITORS (2)	20/2	11	12	20/2	BOOM TYPES "B" LIGHTHEADS (2)
BOOM TYPE "C5" RECEPTACLES	20/2	13	14	20/2	BOOM TYPE "C5" RECEPTACLES
BOOM TYPE "C5" RECEPTACLES	20/2	15	16	20/2	BOOM TYPE "C5" RECEPTACLES

XFMR KVA	INPUT VOLTS	INPUT AMPS	INPUT PHASE	HERTZ	OUTPUT VOLTS	OUTPUT AMPS	OUTPUT PHASE	A.I.C RATING
7.5	277	27	1	60	120	62.5	1	22,000

ISOLATION PANEL IPU-2-B — LOCATION: O.R. 2 1D-125

FED FROM PANEL 1HM CIRCUIT 21,23
120V, 1ø, 2W, WITH LINE ISOLATION MONITOR.

DESCRIPTION	Bkr	No.	No.	Bkr	DESCRIPTION
WALL GROUND MODULE	20/2	1	2	20/2	WALL GROUND MODULE
WALL GROUND MODULE	20/2	3	4	20/2	WALL GROUND MODULE
WALL GROUND MODULE	20/2	5	6	20/2	WALL GROUND MODULE
WALL GROUND MODULE	20/2	7	8	20/2	WALL GROUND MODULE
WALL GROUND MODULE	20/2	9	10	20/2	RECEPTACLES, ELAPSED TIME CLOCK
ROOM RECEPTACLES	20/2	11	12	20/2	WALL GROUND MODULE
WALL GROUND MODULE	20/2	13	14	20/2	WALL MOUNTED TV MONITOR
208-VOLT LASER RECEPTACLE – SEE NOTE	30/2	15	16	20/2	SPARE

XFMR KVA	INPUT VOLTS	INPUT AMPS	INPUT PHASE	HERTZ	OUTPUT VOLTS	OUTPUT AMPS	OUTPUT PHASE	A.I.C RATING
15	480	31	1	60	120	62.5	1	22,000

NOTE – *208-VOLT CIRCUIT BREAKER IS WIRED TO A SEPARATE WINDING OFF OF THE UNIT TRANSFORMER. CIRCUIT BREAKER IS HOUSED IN A SEPARATE SECTION OF THE PANEL.

ISOLATION PANEL IPU-6-A — LOCATION: O.R. 6 1C-130

FED FROM PANEL 1ECHN CIRCUIT 3
120V, 1ø, 2W, WITH LINE ISOLATION MONITOR.

DESCRIPTION	Bkr	No.	No.	Bkr	DESCRIPTION
WALL GROUND MODULE	20/2	1	2	20/2	WALL GROUND MODULE
WALL GROUND MODULE	20/2	3	4	20/2	WALL GROUND MODULE
WALL GROUND MODULE	20/2	5	6	20/2	WALL GROUND MODULE
WALL GROUND MODULE	20/2	7	8	20/2	WALL GROUND MODULE
WALL GROUND MODULE	20/2	9	10	20/2	ELAPSED TIME CLOCK
PYXSIS MACHINE	20/2	11	12	20/2	WALL GROUND MODULE
208-VOLT LASER RECEPTACLE – SEE NOTE	30/2	15	16	20/2	SPARE

XFMR KVA	INPUT VOLTS	INPUT AMPS	INPUT PHASE	HERTZ	OUTPUT VOLTS	OUTPUT AMPS	OUTPUT PHASE	A.I.C RATING
7.5	277	27	1	60	120	62.5	1	22,000

ISOLATION PANEL IPU-6-B — LOCATION: O.R. 6 1C-130

FED FROM PANEL 1HN CIRCUIT 13,15
120V, 1ø, 2W, WITH LINE ISOLATION MONITOR.

DESCRIPTION	Bkr	No.	No.	Bkr	DESCRIPTION
WALL GROUND MODULE	20/2	1	2	20/2	WALL GROUND MODULE
WALL GROUND MODULE	20/2	3	4	20/2	BOOM TYPE "C6" RECEPTACLES
BOOM TYPE "C6" ACCESSORIES	20/2	5	6	20/2	BOOM TYPE "C6" RECEPTACLES
PYXSIS MACHINE	20/2	7	8	20/2	BOOM TYPE "C6" RECEPTACLES
EMS ELECTRO-MAGNETIC BRAKING SYSTEM	20/2	9	10	20/2	BOOM TYPE "C6" RECEPTACLES
BOOM TYPE "B" MONITOR	20/2	11	12	20/2	BOOM TYPE "B" AND "C6" LIGHTHEAD
BOOM TYPE "C5" RECEPTACLES	20/2	13	14	20/2	BOOM TYPE "C5" RECEPTACLES
BOOM TYPE "C5" RECEPTACLES	20/2	15	16	20/2	BOOM TYPE "C5" ACCESSORIES

XFMR KVA	INPUT VOLTS	INPUT AMPS	INPUT PHASE	HERTZ	OUTPUT VOLTS	OUTPUT AMPS	OUTPUT PHASE	A.I.C RATING
15	480	31	1	60	120	62.5	1	22,000

NOTE – *208-VOLT CIRCUIT BREAKER IS WIRED TO A SEPARATE WINDING OFF OF THE UNIT TRANSFORMER. CIRCUIT BREAKER IS HOUSED IN A SEPARATE SECTION OF THE PANEL.

ISOLATION PANEL IPU-3-A — LOCATION: O.R. 3 1D-126

FED FROM PANEL 1ECHM CIRCUIT 17
120V, 1ø, 2W, WITH LINE ISOLATION MONITOR.

DESCRIPTION	Bkr	No.	No.	Bkr	DESCRIPTION
WALL GROUND MODULE	20/2	1	2	20/2	WALL GROUND MODULE
WALL GROUND MODULE	20/2	3	4	20/2	BOOM TYPE "C6" RECEPTACLES
EMS BRAKING SYSTEM – BOOM "C6"	20/2	5	6	20/2	BOOM TYPE "C6" RECEPTACLES
PYXSIS MACHINE	20/2	7	8	20/2	BOOM TYPE "C6" RECEPTACLES
EMS BRAKING SYSTEM – BOOM "C5"	20/2	9	10	20/2	BOOM TYPE "C6" RECEPTACLES
BOOM TYPES "B" MONITORS (2)	20/2	11	12	20/2	BOOM TYPES "B" LIGHTHEADS (2)
BOOM TYPE "C5" RECEPTACLES	20/2	13	14	20/2	BOOM TYPE "C5" RECEPTACLES
BOOM TYPE "C5" RECEPTACLES	20/2	15	16	20/2	BOOM TYPE "C5" RECEPTACLES

XFMR KVA	INPUT VOLTS	INPUT AMPS	INPUT PHASE	HERTZ	OUTPUT VOLTS	OUTPUT AMPS	OUTPUT PHASE	A.I.C RATING
7.5	277	27	1	60	120	62.5	1	22,000

ISOLATION PANEL IPU-3-B — LOCATION: O.R. 3 1D-126

FED FROM PANEL 1HM CIRCUIT 25,27
120V, 1ø, 2W, WITH LINE ISOLATION MONITOR.

DESCRIPTION	Bkr	No.	No.	Bkr	DESCRIPTION
WALL GROUND MODULE	20/2	1	2	20/2	WALL GROUND MODULE
WALL GROUND MODULE	20/2	3	4	20/2	WALL GROUND MODULE
WALL GROUND MODULE	20/2	5	6	20/2	WALL GROUND MODULE
WALL GROUND MODULE	20/2	7	8	20/2	WALL GROUND MODULE
WALL GROUND MODULE	20/2	9	10	20/2	RECEPTACLES, ELAPSED TIME CLOCK
ROOM RECEPTACLES	20/2	11	12	20/2	WALL GROUND MODULE
WALL GROUND MODULE	20/2	13	14	20/2	WALL MOUNTED TV MONITOR
208-VOLT LASER RECEPTACLE – SEE NOTE	30/2	15	16	20/2	SPARE

XFMR KVA	INPUT VOLTS	INPUT AMPS	INPUT PHASE	HERTZ	OUTPUT VOLTS	OUTPUT AMPS	OUTPUT PHASE	A.I.C RATING
15	480	31	1	60	120	62.5	1	22,000

NOTE – *208-VOLT CIRCUIT BREAKER IS WIRED TO A SEPARATE WINDING OFF OF THE UNIT TRANSFORMER. CIRCUIT BREAKER IS HOUSED IN A SEPARATE SECTION OF THE PANEL.

ISOLATION PANEL IPU-7-A — LOCATION: O.R. 7 1C-129

FED FROM PANEL 1ECHN CIRCUIT 9
120V, 1ø, 2W, WITH LINE ISOLATION MONITOR.

DESCRIPTION	Bkr	No.	No.	Bkr	DESCRIPTION
WALL GROUND MODULE	20/2	1	2	20/2	WALL GROUND MODULE
WALL GROUND MODULE	20/2	3	4	20/2	BOOM TYPE "C6" RECEPTACLES
EMS BRAKING SYSTEM – BOOM "C6"	20/2	5	6	20/2	BOOM TYPE "C6" RECEPTACLES
PYXSIS MACHINE	20/2	7	8	20/2	BOOM TYPE "C6" RECEPTACLES
EMS BRAKING SYSTEM – BOOM "C5"	20/2	9	10	20/2	BOOM TYPE "C6" RECEPTACLES
BOOM TYPES "B" MONITORS (2)	20/2	11	12	20/2	BOOM TYPES "B" LIGHTHEADS (2)
BOOM TYPE "C5" RECEPTACLES	20/2	13	14	20/2	BOOM TYPE "C5" RECEPTACLES
BOOM TYPE "C5" RECEPTACLES	20/2	15	16	20/2	BOOM TYPE "C5" RECEPTACLES

XFMR KVA	INPUT VOLTS	INPUT AMPS	INPUT PHASE	HERTZ	OUTPUT VOLTS	OUTPUT AMPS	OUTPUT PHASE	A.I.C RATING
7.5	277	27	1	60	120	62.5	1	22,000

ISOLATION PANEL IPU-7-B — LOCATION: O.R. 7 1C-129

FED FROM PANEL 1HN CIRCUIT 5,7
120V, 1ø, 2W, WITH LINE ISOLATION MONITOR.

DESCRIPTION	Bkr	No.	No.	Bkr	DESCRIPTION
WALL GROUND MODULE	20/2	1	2	20/2	WALL GROUND MODULE
WALL GROUND MODULE	20/2	3	4	20/2	WALL GROUND MODULE
WALL GROUND MODULE	20/2	5	6	20/2	WALL GROUND MODULE
WALL GROUND MODULE	20/2	7	8	20/2	WALL GROUND MODULE
WALL GROUND MODULE	20/2	9	10	20/2	RECEPTACLES, ELAPSED TIME CLOCK
ROOM RECEPTACLES	20/2	11	12	20/2	WALL GROUND MODULE
WALL GROUND MODULE	20/2	13	14	20/2	WALL MOUNTED TV MONITOR
208-VOLT LASER RECEPTACLE – SEE NOTE	30/2	15	16	20/2	SPARE

XFMR KVA	INPUT VOLTS	INPUT AMPS	INPUT PHASE	HERTZ	OUTPUT VOLTS	OUTPUT AMPS	OUTPUT PHASE	A.I.C RATING
15	480	31	1	60	120	62.5	1	22,000

NOTE – *208-VOLT CIRCUIT BREAKER IS WIRED TO A SEPARATE WINDING OFF OF THE UNIT TRANSFORMER. CIRCUIT BREAKER IS HOUSED IN A SEPARATE SECTION OF THE PANEL.

ISOLATION PANEL IPU-4-A — LOCATION: O.R. 4 1C-128

FED FROM PANEL 1ECHN CIRCUIT 5
120V, 1ø, 2W, WITH LINE ISOLATION MONITOR.

DESCRIPTION	Bkr	No.	No.	Bkr	DESCRIPTION
WALL GROUND MODULE	20/2	1	2	20/2	WALL GROUND MODULE
WALL GROUND MODULE	20/2	3	4	20/2	BOOM TYPE "C6" RECEPTACLES
EMS BRAKING SYSTEM – BOOM "C6"	20/2	5	6	20/2	BOOM TYPE "C6" RECEPTACLES
PYXSIS MACHINE	20/2	7	8	20/2	BOOM TYPE "C6" RECEPTACLES
EMS BRAKING SYSTEM – BOOM "C5"	20/2	9	10	20/2	BOOM TYPE "C6" RECEPTACLES
BOOM TYPES "B" MONITORS (2)	20/2	11	12	20/2	BOOM TYPES "B" LIGHTHEADS (2)
BOOM TYPE "C5" RECEPTACLES	20/2	13	14	20/2	BOOM TYPE "C5" RECEPTACLES
BOOM TYPE "C5" RECEPTACLES	20/2	15	16	20/2	BOOM TYPE "C5" RECEPTACLES

XFMR KVA	INPUT VOLTS	INPUT AMPS	INPUT PHASE	HERTZ	OUTPUT VOLTS	OUTPUT AMPS	OUTPUT PHASE	A.I.C RATING
7.5	277	27	1	60	120	62.5	1	22,000

ISOLATION PANEL IPU-4-B — LOCATION: O.R. 4 1C-128

FED FROM PANEL 1HN CIRCUIT 1,3
120V, 1ø, 2W, WITH LINE ISOLATION MONITOR.

DESCRIPTION	Bkr	No.	No.	Bkr	DESCRIPTION
WALL GROUND MODULE	20/2	1	2	20/2	WALL GROUND MODULE
WALL GROUND MODULE	20/2	3	4	20/2	WALL GROUND MODULE
WALL GROUND MODULE	20/2	5	6	20/2	WALL GROUND MODULE
WALL GROUND MODULE	20/2	7	8	20/2	WALL GROUND MODULE
WALL GROUND MODULE	20/2	9	10	20/2	RECEPTACLES, ELAPSED TIME CLOCK
ROOM RECEPTACLES	20/2	11	12	20/2	WALL GROUND MODULE
WALL GROUND MODULE	20/2	13	14	20/2	WALL MOUNTED TV MONITOR
208-VOLT LASER RECEPTACLE – SEE NOTE	30/2	15	16	20/2	ROBOT RECEPTACLES

XFMR KVA	INPUT VOLTS	INPUT AMPS	INPUT PHASE	HERTZ	OUTPUT VOLTS	OUTPUT AMPS	OUTPUT PHASE	A.I.C RATING
15	480	31	1	60	120	62.5	1	22,000

NOTE – *208-VOLT CIRCUIT BREAKER IS WIRED TO A SEPARATE WINDING OFF OF THE UNIT TRANSFORMER. CIRCUIT BREAKER IS HOUSED IN A SEPARATE SECTION OF THE PANEL.

ISOLATION PANEL IPU-H-A — LOCATION: HYBRID O.R. 1D-123

FED FROM PANEL 1ECHM CIRCUIT 13
120V, 1ø, 2W, WITH LINE ISOLATION MONITOR.

DESCRIPTION	Bkr	No.	No.	Bkr	DESCRIPTION
WALL MOUNTED TV MONITOR	20/2	1	2	20/2	BOOM TYPES "B2" & "B1" LIGHTHEADS (3)
BOOM TYPE "C1" RECEPTACLES	20/2	3	4	20/2	BOOM TYPE "B2" MONITOR
BOOM TYPE "C2" RECEPTACLES	20/2	5	6	20/2	BOOM TYPE "C4" RECEPTACLES
BOOM TYPE "C3" RECEPTACLES	20/2	7	8	20/2	BOOM TYPE "C4" RECEPTACLES
BOOM TYPE "C3" RECEPTACLES	20/2	9	10	20/2	BOOM TYPE "C4" RECEPTACLES
BOOM TYPE "C3" RECEPTACLES	20/2	11	12	20/2	BOOM TYPE "C4" RECEPTACLES
BOOM TYPE "C3" RECEPTACLES	20/2	13	14	20/2	BOOM TYPE "C4" RECEPTACLES
EMS BRAKING SYSTEM – BOOM "C4"	20/2	15	16	20/2	BOOM TYPE "C4" RECEPTACLES

XFMR KVA	INPUT VOLTS	INPUT AMPS	INPUT PHASE	HERTZ	OUTPUT VOLTS	OUTPUT AMPS	OUTPUT PHASE	A.I.C RATING
7.5	277	27	1	60	120	62.5	1	22,000

ISOLATION PANEL IPU-H-B — LOCATION: HYBRID O.R. 1D-123

FED FROM PANEL 1HM CIRCUIT 17,19
120V, 1ø, 2W, WITH LINE ISOLATION MONITOR.

DESCRIPTION	Bkr	No.	No.	Bkr	DESCRIPTION
WALL GROUND MODULE	20/2	1	2	20/2	WALL GROUND MODULE
WALL GROUND MODULE	20/2	3	4	20/2	WALL GROUND MODULE
WALL GROUND MODULE	20/2	5	6	20/2	WALL GROUND MODULE
WALL GROUND MODULE	20/2	7	8	20/2	WALL GROUND MODULE
WALL GROUND MODULE	20/2	9	10	20/2	PYXSIS MACHINE
WALL GROUND MODULE	20/2	11	12	20/2	ELAPSED TIME CLOCK
WALL GROUND MODULE	20/2	13	14	20/2	*208-VOLT LASER RECEPTACLE – SEE NOTE*
WALL GROUND MODULE	30/2	15	16	20/2	SPARE

XFMR KVA	INPUT VOLTS	INPUT AMPS	INPUT PHASE	HERTZ	OUTPUT VOLTS	OUTPUT AMPS	OUTPUT PHASE	A.I.C RATING
15	480	31	1	60	120	62.5	1	22,000

NOTE – *208-VOLT CIRCUIT BREAKER IS WIRED TO A SEPARATE WINDING OFF OF THE UNIT TRANSFORMER. CIRCUIT BREAKER IS HOUSED IN A SEPARATE SECTION OF THE PANEL.

ISOLATION PANEL IPU-5-A — LOCATION: ORTHO O.R. 5 1C-126

FED FROM PANEL 1ECHN CIRCUIT 7
120V, 1ø, 2W, WITH LINE ISOLATION MONITOR.

DESCRIPTION	Bkr	No.	No.	Bkr	DESCRIPTION
WALL GROUND MODULE	20/2	1	2	20/2	WALL GROUND MODULE
WALL GROUND MODULE	20/2	3	4	20/2	BOOM TYPE "C6" RECEPTACLES
EMS BRAKING SYSTEM – BOOM "C6"	20/2	5	6	20/2	BOOM TYPE "C6" RECEPTACLES
PYXSIS MACHINE	20/2	7	8	20/2	BOOM TYPE "C6" RECEPTACLES
EMS BRAKING SYSTEM – BOOM "C5"	20/2	9	10	20/2	BOOM TYPE "C6" RECEPTACLES
BOOM TYPES "B" MONITORS (2)	20/2	11	12	20/2	BOOM TYPES "B" LIGHTHEADS (2)
BOOM TYPE "C5" RECEPTACLES	20/2	13	14	20/2	BOOM TYPE "C5" RECEPTACLES
BOOM TYPE "C5" RECEPTACLES	20/2	15	16	20/2	BOOM TYPE "C5" RECEPTACLES

XFMR KVA	INPUT VOLTS	INPUT AMPS	INPUT PHASE	HERTZ	OUTPUT VOLTS	OUTPUT AMPS	OUTPUT PHASE	A.I.C RATING
7.5	277	27	1	60	120	62.5	1	22,000

ISOLATION PANEL IPU-5-B — LOCATION: ORTHO O.R. 5 1C-126

FED FROM PANEL 1HN CIRCUIT 9,11
120V, 1ø, 2W, WITH LINE ISOLATION MONITOR.

DESCRIPTION	Bkr	No.	No.	Bkr	DESCRIPTION
WALL GROUND MODULE	20/2	1	2	20/2	WALL GROUND MODULE
WALL GROUND MODULE	20/2	3	4	20/2	WALL GROUND MODULE
WALL GROUND MODULE	20/2	5	6	20/2	WALL GROUND MODULE
WALL GROUND MODULE	20/2	7	8	20/2	WALL GROUND MODULE
WALL GROUND MODULE	20/2	9	10	20/2	RECEPTACLES, ELAPSED TIME CLOCK
ROOM RECEPTACLES	20/2	11	12	20/2	WALL GROUND MODULE
WALL GROUND MODULE	20/2	13	14	20/2	WALL MOUNTED TV MONITOR
208-VOLT LASER RECEPTACLE – SEE NOTE	30/2	15	16	20/2	SPARE

XFMR KVA	INPUT VOLTS	INPUT AMPS	INPUT PHASE	HERTZ	OUTPUT VOLTS	OUTPUT AMPS	OUTPUT PHASE	A.I.C RATING
15	480	31	1	60	120	62.5	1	22,000

NOTE – *208-VOLT CIRCUIT BREAKER IS WIRED TO A SEPARATE WINDING OFF OF THE UNIT TRANSFORMER. CIRCUIT BREAKER IS HOUSED IN A SEPARATE SECTION OF THE PANEL.

PRINTS OF THIS DRAWING SHALL NOT BE USED FOR ANY PURPOSE WHATSOEVER WITHOUT THE SEAL AND SIGNATURE OF THE PROFESSIONAL ENGINEER.

NO.	DESCRIPTION	DATE

CONSULTANTS

Architecture:	Civil Engineering:	Fire & Life Safety:
PF&A DESIGN, P.C.	LABELLA ASSOCIATES	STANTON ENGINEERING SERVICES, LLC

ENGINEER OF RECORD

MILLER-REMICK

A Service-Disabled Veteran-Owned Small Business

(856) 429-4000 ● Miller-Remick.com

M-R PROJECT NO. 24-0136

MILLER-REMICK LLC
PROFESSIONAL ENGINEER

COMMONWEALTH OF PENNSYLVANIA — REGISTERED PROFESSIONAL — THOMAS REGINO — ENGINEER No. PE054195

12/30/25

Office of Construction and Facilities Management

U.S. Department of Veterans Affairs

Drawing Title	ELECTRICAL ISOLATION PANEL SCHEDULES
Approved by:	Jon Manninen, COR
Phase	BID DOCUMENTS
	FULLY SPRINKLERED
Project Title	RENOVATE SURGICAL SUITE PHASE II
Project Number	658-19-103
Location	SALEM VA MEDICAL CENTER
Issue Date	2025-12-30
Checked	MJR
Drawn	MJR
VA Drawing Number	2617
Building Number	143
Drawing Number	E-703

VA FORM 08-6231

P:\0499_0VA\0499-0136 Salem Renovate Surgical Suite\4_Drawings\1_Cad\1_Current Submittal Phase\7_Electrical\E-703.dwg 12-29-25 08:23:40 AM MRonca

LIGHTING FIXTURE SCHEDULE

TYPE	DIMENSIONS	DESCRIPTION	WATTAGE	TYPE	VOLTS	MOUNTING	REMARKS
A1	2'x4'	DIRECT/INDIRECT GASKETED BASKET TYPE LED TROFFER WITH PERFORATED METAL DIFFUSER AND GRID FLANGE 3500K, 5000 LUMENS OUTPUT	63W	LED	UNVERSAL	RECESSED	GRID MOUNTED FIXTURE
A1A	2'x4'	SLIM PROFILE DIRECT/INDIRECT GASKETED BASKET TYPE LED TROFFER WITH PERFORATED METAL DIFFUSER AND GRID FLANGE 3500K, 5000 LUMENS OUTPUT	63W	LED	UNIVERSAL	RECESSED	GRID MOUNTED FIXTURE. ZERO PLENUM FIXTURE SHALL BE NO THICKER THAN 2" SO THAT IT CAN BE INSTALLED IN CEILING WITH VERY LITTLE CLEARANCE ABOVE.
A2	2'x4'	OPERATING ROOM GRADE LED TROFFER. ALUMNUM HOUSING, 0.125 ACRYLIC LENS, GASKETING AND GRID FLANGE 5000K, 16000 LUMENS OUTPUT	200W	LED	277V	RECESSED	GRID MOUNTED. FIXTURE SHALL MEET ALL ANTI-MICROBIAL REQUIREMENTS FOR OPERATING ROOM LIGHT FIXTURE.
A3	2'x4'	MULTI-FUNCTION WHITE OVER-BED LIGHT FIXTURE, AMBIENT / EXAM / (2) READING LIGHTS, SINGLE CIRCUIT	AMBIENT 62W EXAM 203W READING 15W	LED	277V	RECESSED	FIXTURE SHALL BE 3000K WITH 6080 AMBIENT LUMENS AND 7400 EXAM LUMENS
A4	2'x4'	DIRECT/INDIRECT BASKET TYPE LED TROFFER WITH PERFORATED METAL DIFFUSER AND HARD CEILING FLANGE 3500K, 5000 LUMENS OUTPUT	63W	LED	277V	RECESSED	DRYWALL CEILING MOUNTED FIXTURE
A6	2'x4'	OPERATING ROOM GRADE LED TROFFER. ALUMNUM HOUSING, 0.125 ACRYLIC LENS, GASKETING AND GRID FLANGE. BACKUP BATTERY BALLAST 5000K, 17000 LUMENS OUTPUT	200W	LED	277V	RECESSED	GRID MOUNTED FIXTURE. PROVIDE EMERGENCY BATTERY PACK WITHIN FIXTURE. FIXTURE SHALL MEET ALL ANTI-MICROBIAL REQUIREMENTS FOR OPERATING ROOM LIGHT FIXTURE.
B1	2'x2'	DIRECT/INDIRECT GASKETED BASKET TYPE LED TROFFER WITH PERFORATED METAL DIFFUSER AND GRID FLANGE 3500K, 2500 LUMENS OUTPUT	31W	LED	UNIVERSAL	RECESSED	GRID MOUNTED FIXTURE
B3	2'x2'	OPERATING ROOM GRADE LED TROFFER. ALUMNUM HOUSING, 0.125 ACRYLIC LENS AND GRID FLANGE 5000K, 6000 LUMENS OUTPUT	100W	LED	277V	RECESSED	GRID MOUNTED FIXTURE
D1	6" APERTURE	SELF FLANGED 6" VERTICAL LED DOWNLIGHT WITH WHITE TRIM AND INTEGRAL LENS 3500K, 3000 LUMENS OUTPUT	40W	LED	UNIVERSAL	RECESSED	
D2	4.5" x 4.5"	SELF FLANGED SQUARE TYPE VERTICAL LED DOWNLIGHT WITH WHITE TRIM AND INTEGRAL LENS 3500K, 3000 LUMENS OUTPUT	40W	LED	UNIVERSAL	RECESSED	
D3	6" APERTURE	OPERATING ROOM GRADE VERTICAL LED DOWNLIGHT WITH WHITE TRIM AND GASKETING 5000K, 3600 LUMENS OUTPUT	40W	LED	277V	RECESSED	PROVIDE LENS SO FIXTURE MEETS ALL ANTI-MICROBIAL REQUIREMENTS FOR OPERATING ROOM LIGHT FIXTURES.
E1		DECORATIVE PENDANT FIXTURE TO BE SELECTED BY ARCHITECT				PENDANT	
L2	1'x4'	DIRECT LED TROFFER WITH ACRYLIC LENS AND DRYWALL CEILING FLANGE 3500K, 5000 LUMENS	63W	LED	277V	RECESSED	DRYWALL CEILING MOUNTED FIXTURE
L3	1'x4'	DIRECT/INDIRECT BASKET TYPE LED TROFFER WITH PERFORATED METAL DIFFUSER AND GRID FLANGE 3500K, 5000 LUMENS OUTPUT	63W	LED	277V	RECESSED	GRID MOUNTED FIXTURE
L4	1'x4'	DIRECT/INDIRECT BASKET TYPE LED TROFFER WITH PERFORATED METAL DIFFUSER AND GRID FLANGE 3500K, 5000 LUMENS OUTPUT	63W	LED	277V	SURFACE	PROVIDE WALL MOUNTING BRACKET TIGHT TO CEILING GRID.
S	4'-0"	INDUSTRIAL LED STRIP WITH 10% UPLIGHT 3500K, 6000 LUMENS	52W	LED	277V	CHAIN SUSPENDED	PROVIDE WIRE GUARD CAGE.
X	N/A	VA STANDARD EXIT SIGN. EDGE LIT, RED LED ON MIRROR	3W	LED	277V	SURFACE	SEE PLANS FOR MOUNTING AND DIRECTIONAL ARROW REQUIREMENTS

Panel Name: BEL2 — New Panel — Main Lugs Only: ____ Main Breaker: 60
Panel Voltage: 208Y/120V, 3 Phase, 4 Wire — Panel A.I.C. Rating: 14k

ID	Ckt #	Description	Breaker P	Trip	Code	Load VA	Phase A	Phase B	Phase C	Load VA	Code	Breaker Trip	P	Description	Ckt #	ID
N	1	LIFE SAFETY LIGHTING, PHASE 1 CORRIDOR	1	20	L	756	756					20	1	SPARE	2	N
N	3	LIGHTING - PHASE 2 ,3 ,4	1	20	L	1323		1323				20	1	SPARE	4	N
N	5	SPARE	1	20								20	1	SPARE	6	N
N	7	SPARE	1	20								20	1	SPARE	8	N
N	9	SPARE	1	20								20	1	SPARE	10	N
N	11	SPARE	1	20								20	1	SPARE	12	N
N	13	SPARE	1	20								20	1	SPARE	14	N
N	15	SPARE	1	20								20	1	SPARE	16	N
N	17	SPARE	1	20								20	1	SPARE	18	N
N	19	SPARE	1	20								20	1	SPARE	20	N
N	21	SPARE	1	20								20	1	SPARE	22	N
N	23	SPARE	1	20								20	1	SPARE	24	N
N	25	SPARE	1	20			1700			1700					26	
N	27	SPARE	1	20				1000		1000	C	50	3	FEEDER TO TRANSFORMER T1EL	28	N
N	29	SPARE	1	20					1000	1000					30	

Total Connected Load: 2456 | 2323 | 1000 (VA/PHASE)

N.E.C. LOAD SUMMARY

Load Types and Codes	Total Load (VA)	Demand Factor	NEC Sizing Load (VA)
Air Conditioning (AC)		1.00	
Heating (H)		1.00	
Kitchen Equipment (K)		1.00	
Lighting (L)	2079	1.00	2079
Receptacles (REC)		1.00	
Existing (E)		1.00	
Continuous (C)	3700	1.00	3700
Non-Continuous (NC)		1.00	
Refrigeration (REF)		1.00	
Elec. Load Totals:	**5779**		**5779** VA

ELECTRICAL DATA
Total Conn. Load: 6 KVA
Total Conn. Load: 16 Amps
NEC Sizing Load: 6 KVA
NEC Sizing Load: 16 Amps
Main Bus Size: 225 Amps

PANEL LEGEND (ID)
ST - Shunt-Trip C.B.; G - GFI C.B.
LB - "Lock-On" C.B.
"C1" - Contactor Designation
--Remodels--
N - New C.B.; EX - Existing C.B.

PANEL INFORMATION
Location: Transformer Room 2 BD-122A
Mounting: Surface Enclosure Type: Nema 1
Fed From: Panel ESWBD-L1
Equipment Ground Bus: Yes Bus Material: Copper
Isolated Ground Bus: No Neutral Size: 100%

PANEL NOTES

Panel Name: 1EL — New Panel — Main Lugs Only: ____ Main Breaker: 100
Panel Voltage: 208Y/120V, 3 Phase, 4 Wire — Panel A.I.C. Rating: 14k

ID	Ckt #	Description	Breaker P	Trip	Code	Load VA	Phase A	Phase B	Phase C	Load VA	Code	Breaker Trip	P	Description	Ckt #	ID
N	1	DOOR OPERATORS	1	20	C	500	500					20	1	SPARE	2	N
N	3	MED GAS ALARM PANEL MGA-1	1	20	C	500		500				20	1	SPARE	4	N
N	5	DOOR OPERATORS	1	20	C	500			500			20	1	SPARE	6	N
N	7	DOOR OPERATORS	1	20	C	700	700					20	1	SPARE	8	N
N	9	MED GAS ALARM PANEL MGA-2	1	20	C	500		500				20	1	SPARE	10	N
N	11	DOOR OPERATORS	1	20	C	500			500			20	1	SPARE	12	N
N	13	MED GAS ALARM PANEL MGA-3	1	20	C	500	500					20	1	SPARE	14	N
N	15	SPARE	1	20								20	1	SPARE	16	N
N	17	SPARE	1	20								20	1	SPARE	18	N
N	19	SPARE	1	20								20	1	SPARE	20	N
N	21	SPARE	1	20								20	1	SPARE	22	N
N	23	SPARE	1	20								20	1	SPARE	24	N
N	25	SPARE	1	20								20	1	SPARE	26	N
N	27	SPARE	1	20								20	1	SPARE	28	N
N	29	SPARE	1	20								20	1	SPARE	30	N

Total Connected Load: 1700 | 1000 | 1000 (VA/PHASE)

N.E.C. LOAD SUMMARY

Load Types and Codes	Total Load (VA)	Demand Factor	NEC Sizing Load (VA)
Air Conditioning (AC)		1.00	
Heating (H)		1.00	
Kitchen Equipment (K)		1.00	
Lighting (L)		1.00	
Receptacles (REC)		1.00	
Existing (E)		1.00	
Continuous (C)	3700	1.00	3700
Non-Continuous (NC)		1.00	
Refrigeration (REF)		1.00	
Elec. Load Totals:	**3700**		**3700** VA

ELECTRICAL DATA
Total Conn. Load: 4 KVA
Total Conn. Load: 10 Amps
NEC Sizing Load: 4 KVA
NEC Sizing Load: 10 Amps
Main Bus Size: 125 Amps

PANEL LEGEND (ID)
ST - Shunt-Trip C.B.; G - GFI C.B.
LB - "Lock-On" C.B.
"C1" - Contactor Designation
--Remodels--
N - New C.B.; EX - Existing C.B.

PANEL INFORMATION
Location: Electrical Room 1D-1027
Mounting: Surface Enclosure Type: Nema 1
Fed From: Transformer T1EL
Equipment Ground Bus: Yes Bus Material: Copper
Isolated Ground Bus: No Neutral Size: 100%

PANEL NOTES

ELECTRICAL CONNECTION SCHEDULE

TAG	LOCATION	NOTES	ELECTRICAL CHARACTERISTICS V/PH/HZ	MCA	MOCP	KW	HP	LOCAL DISCONNECT DEVICE UNFUSED SWITCH	FUSED SWITCH	MANUAL MOTOR SWITCH OL	PILOT	DIV	STARTER TYPE	SIZE	COMBINATION SW UNFU	COMBINATION SW/ FUSE	COMBINATION MCP	ACCESSORIES HOA	ACCESSORIES PILOT	DIV	WIRE & CONDUIT	CIRCUITING
143-ACCU-1D1A	EXTERIOR GRADE	1,2,3	480/3/60	231.2	250	217.5		X				23									3-250KCMIL + 1-#4G. In 3" C.	ESWBD-E1C-1,3,5
143-ACCU-1D1B	EXTERIOR GRADE	1,2,3	480/3/60	231.2	250	217.5		X				23									3-250KCMIL + 1-#4G. In 3" C.	ESWBD-E1C-7,9,11
143-RTU-2D1 (SUPPLY)	ROOF		480/3/60	136.9	150								VFD							23	3-#1/0 + 1-#6G. IN 2" C	ESWBD-E1C-13,15,17
143-RTU-2D1 (RETURN)	ROOF		480/3/60	53.1	60								VFD							23	3-#6 + 1-#10G. IN 3/4" C.	ESWBD-E1C-19,21,23
143-AHU-1C1	MECH 1C-132		480/3/60	77.4	90								VFD							23	3-#3 + 1-#8G. IN 1 1/4" C.	1EEHP-1,3,5
143-AHU-1C2	MECH 1C-132		480/3/60	40.0	45								VFD							23	3-#8 + 1-#10G. IN 3/4" C.	1EEHP-7,9,11
143-EF-2C1A	ROOF		480/3/60	2.0	15		3/4	30A				26		ECM							3-#12 + 1-#12G. IN 3/4" C.	1EEHM-19,21,23
143-EF-2C1B	ROOF		480/3/60	2.0	15		3/4	30A				26		ECM							3-#12 + 1-#12G. IN 3/4" C.	1EEHM-25,27,29
143-EF-2D2	ROOF		480/3/60	50.0	70		30						VFD							23	3-#6 + 1-#10G. IN 3/4" C.	ESWBD-E1C-31,33,35
143-EF-2C3	ROOF		480/3/60	42.5	60		25						VFD							23	3-#6 + 1-#10G. IN 3/4" C.	ESWBD-E1C-373,39,41
143-EF-2C4	ROOF		480/3/60	26.3	40		15						VFD							23	3-#10 + 1-#10G. IN 3/4" C.	ESWBD-E1C-25,27,29
143-CSG-2D1	ROOF		120/1/60	3.0	20					X		26									2-#12 + 1-#12G. IN 3/4" C.	1EELM-4
143-CSG-1C1	MECH 1C-132		120/1/60	3.0	20					X		26									2-#12 + 1-#12G. IN 3/4" C.	1EELP-1
143-CSG-1C2	MECH 1C-132		120/1/60	3.0	20					X		26									2-#12 + 1-#12G. IN 3/4" C.	1EELP-1
143-P-1C1	SUB-BASEMENT MECH		480/3/60	33.8	50		20						VFD							23	3-#8 + 1-#10G. IN 3/4" C.	ESWBD-E1C-19,21,23
143-P-1C2	SUB-BASEMENT MECH		480/3/60	33.8	50		20						VFD							23	3-#8 + 1-#10G. IN 3/4" C.	ESWBD-E1C-26,28,30
143-FOF-1D1	GENERATOR BUILDING		120/1/60	9.8	20		1/2			X		26									2-#12 + 1-#12G. IN 3/4" C.	GP-7
143-FOP-1D1A	GENERATOR BUILDING		480/3/60	1.4	15		1/2	30A				26									3-#12 + 1-#12G. IN 3/4" C.	GH-5,7,9
143-FOP-1D1B	GENERATOR BUILDING		480/3/60	1.4	15		1/2	30A				26									3-#12 + 1-#12G. IN 3/4" C.	GH-5,7,9
143-ACU-1D1/143-CU-1	GENERATOR BUILDING	4	208/1/60	22.0	30			30A		X		26									2-#10 + 1-#10G. IN 3/4" C.	GP-15,17

SCHEDULE NOTES:
1. AS FEEDER TRANSFERS TO EXTERIOR OF BUILDING, IT SHALL RUN IN A SPARE CONDUIT IN GENERATOR DUCTBANK. FEEDER SHALL SPLIT OFF TO ITS OWN DUCTBANK AT THE LOCATION OF THE GENERATOR.
2. SEE DETAIL 12/E-501 FOR DUCTBANK DETAIL.
3. CHILLERS ARE N+1 AND WILL NOT OPERATE CONCURRENTLY.
4. ELECTRICAL CONTRACTOR SHALL PROVIDE 2-#12 + 1-#12 GND IN 3/4" C. FROM OUTDOOR UNIT TO INDOOR UNIT AND MANUAL MOTOR SWITCH AT INDOOR UNIT.

Panel Name: GH — Existing Panel — Main Lugs Only: ____ Main Breaker: 100
Panel Voltage: 480Y/277V, 3 Phase, 4 Wire — Panel A.I.C. Rating: 14k

ID	Ckt #	Description	Breaker P	Trip	Code	Load VA	Phase A	Phase B	Phase C	Load VA	Code	Breaker Trip	P	Description	Ckt #	ID
	1	SPACE												SPACE	2	
	3	SPACE												SPACE	4	
	5														6	
N	7	143-FOP-1D1A&1D1B. SEE NOTE 1.	3	15	NC	609	2897			2288	C	50	3	FEEDER TO PANEL GP VIA TRANSFORMER	8	EX
	9				NC	609		3397		2788	C				10	
	11														12	
EX	13	EXISTING UNIT HEATER #2 (OFF)	3	30								30	3	EXISTING UNIT HEATER #1 (OFF)	14	EX
	15														16	
EX	17	SPARE	1	20								20	1	SPARE	18	EX

Total Connected Load: 2897 | 3397 | 2285 (VA/PHASE)

N.E.C. LOAD SUMMARY

Load Types and Codes	Total Load (VA)	Demand Factor	NEC Sizing Load (VA)
Air Conditioning (AC)		1.00	
Heating (H)		1.00	
Kitchen Equipment (K)		1.00	
Lighting (L)		1.00	
Receptacles (REC)		1.00	
Existing (E)		1.00	
Continuous (C)	6752	1.00	6752
Non-Continuous (NC)	1827	1.00	1827
Refrigeration (REF)		1.00	
Elec. Load Totals:	**8579**		**8579** VA

ELECTRICAL DATA
Total Conn. Load: 9 KVA
Total Conn. Load: 10 Amps
NEC Sizing Load: 9 KVA
NEC Sizing Load: 10 Amps
Main Bus Size: 100 Amps

PANEL LEGEND (ID)
ST - Shunt-Trip C.B.; G - GFI C.B.
LB - "Lock-On" C.B.
"C1" - Contactor Designation
--Remodels--
N - New C.B.; EX - Existing C.B.

PANEL INFORMATION
Location: Generator Building 7
Mounting: Surface Enclosure Type: Nema 1
Fed From:
Equipment Ground Bus: Yes Bus Material: Copper
Isolated Ground Bus: No Neutral Size: 100%

PANEL NOTES
Note 1: Provide new circuit breaker. New circuit breaker shall match existing breaker's type and AIC rating.

GENERAL SHEET NOTES:

1. SEE DRAWING E–001 FOR ELECTRICAL SYMBOLS AND ABBREVIATIONS AND DRAWING E–002 FOR ELECTRICAL NOTES.
2. SEE DRAWINGS P1–EL111, P2–EL111, P3–EL111.A, P3–EL111.B AND P4–EL111 FOR LIGHTING FLOOR PLANS.

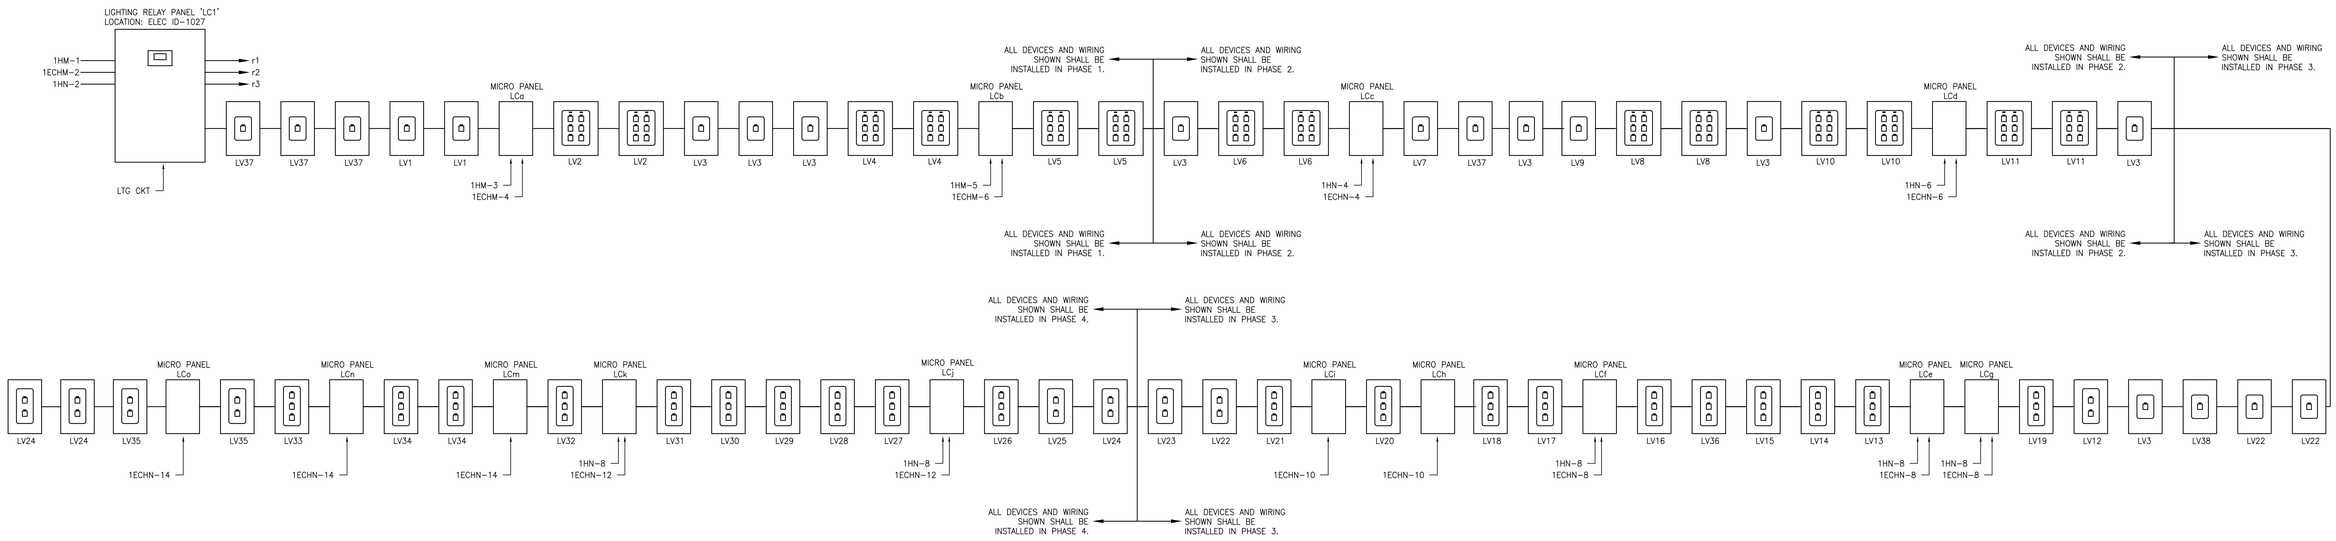

1 LIGHTING CONTROL RISER DIAGRAM
SCALE: NONE

NOTES:
1. ALL INTERCONNECTING WIRES BETWEEN DEVICES SHOWN SHALL BE CAT 5 NETWORK CABLE.

PRINTS OF THIS DRAWING SHALL NOT BE USED FOR ANY PURPOSE WHATSOEVER WITHOUT THE SEAL AND SIGNATURE OF THE PROFESSIONAL ENGINEER.

NO.	DESCRIPTION	DATE

CONSULTANTS

Architecture:	Civil Engineering:	Fire & Life Safety:
PF&A DESIGN, P.C.	LABELLA ASSOCIATES	STANTON ENGINEERING SERVICES, LLC

ENGINEER OF RECORD
MILLER•REMICK
A Service-Disabled Veteran-Owned Small Business
(856) 429-4000 • Miller-Remick.com
M-R PROJECT NO 0499-0136

MILLER-REMICK LLC
PROFESSIONAL ENGINEER
COMMONWEALTH OF PENNSYLVANIA — REGISTERED PROFESSIONAL — THOMAS REGINO — ENGINEER No. PE094135
12/30/25

Office of Construction and Facilities Management
VA U.S. Department of Veterans Affairs

Drawing Title: ELECTRICAL SCHEDULES & LIGHTING CONTROL RISER DIAGRAM
Approved by: Jon Manninen, COR
Phase: BID DOCUMENTS
FULLY SPRINKLERED
Project Title: RENOVATE SURGICAL SUITE PHASE II
Project Number: 658-19-103
Location: SALEM VA MEDICAL CENTER
Issue Date: 2025-12-30
Checked: MJR
Drawn: MJR
VA Drawing Number: 2617
Building Number: 143
Drawing Number: E-704

VA FORM 08-6231

P:\0499_OVA\0499-0136 Salem Renovate Surgical Suite\4_Drawings\1_Cad\1_Current Submittal Phase\7_Electrical\E-704.dwg 12-29-25 08:23:30 AM MRonca

RELAY	CONTROL SWITCH	SWITCH QTY	FUNCTION	ROOMS CONTROLLED	LIGHT FIXTURES CONTROLLED	CIRCUIT
r1	LV37	4	TOGGLE: ON/OFF	PHASE 1 COORIDORS C1-24	ALL NORMAL POWER FIXTURES	1HM-1
r2	LV3	9	TOGGLE: ON/OFF	CLEAN CORE 1C-120	ALL CRITICAL POWER FIXTURES	1ECHM-2
r3	LV38	5	TOGGLE: ON/OFF	CORRIDOR C1-11	ALL NORMAL POWER FIXTURES	1HN-2
r4						
r5						
r6						
r7						
r8						

1 LIGHTING CONTROL PANEL "LC1"

NOTES:

1. LIGHTING RELAY PANEL "LC1" CONTAINS THE ASTRONOMICAL TIME CLOCK AND PROGRAMMING MODULES TO CONTROL THE LIGHTING CIRCUITS IN THE O.R. SUITE.
2. COORDINATE SWITCH PLATE AND SWITCH BUTTON COLOR WITH ARCHITECT AND SPECIFICATIONS.
3. REFER TO FLOOR PLANS FOR QUANTITY AND LOCATION OF SWITCHES.

RELAY	CONTROL SWITCH	SWITCH QTY	FUNCTION	ROOMS CONTROLLED	LIGHT FIXTURES CONTROLLED	CIRCUIT
ra1	LV1	2	TOGGLE: ON/OFF	CONTROL ROOM 1D-124	ALL FIXTURES	1ECHM-4
ra2	LV2	2	TOGGLE: ON/OFF	HYBRID OR 1D-123	ALL ROOM DOWNLIGHTS	1ECHM-4
ra3	LV2	2	TOGGLE: ON/OFF	HYBRID OR 1D-123	OR FIELD PERIMETER LIGHTS	1HM-3
ra4	LV2	2	TOGGLE: ON/OFF	HYBRID OR 1D-123	OR FIELD INTERIOR LIGHTS	1ECHM-4
ra5	LV4	2	TOGGLE: ON/OFF	O.R. 2 1D-125	ALL ROOM DOWNLIGHTS	1ECHM-4
ra6	LV4	2	TOGGLE: ON/OFF	O.R. 2 1D-125	OR FIELD PERIMETER LIGHTS	1HM-3
ra7	LV4	2	TOGGLE: ON/OFF	O.R. 2 1D-125	OR FIELD INTERIOR LIGHTS	1ECHM-4
ra8			TOGGLE: ON/OFF			

2 MICRO PANEL "LCa"

RELAY	CONTROL SWITCH	SWITCH QTY	FUNCTION	ROOMS CONTROLLED	LIGHT FIXTURES CONTROLLED	CIRCUIT
rb1	LV5	2	TOGGLE: ON/OFF	O.R. 3 ROBOTIC 1D-126	ALL ROOM DOWNLIGHTS	1ECHM-6
rb2	LV5	2	TOGGLE: ON/OFF	O.R. 3 ROBOTIC 1D-126	OR FIELD PERIMETER LIGHTS	1HM-5
rb3	LV5	2	TOGGLE: ON/OFF	O.R. 3 ROBOTIC 1D-126	OR FIELD INTERIOR LIGHTS	1ECHM-6
rb4	LV6	2	TOGGLE: ON/OFF	O.R. 4 ROBOTIC 1C-128	ALL ROOM DOWNLIGHTS	1ECHM-6
rb5	LV6	2	TOGGLE: ON/OFF	O.R. 4 ROBOTIC 1C-128	OR FIELD PERIMETER LIGHTS	1HM-5
rb6	LV6	2	TOGGLE: ON/OFF	O.R. 4 ROBOTIC 1C-128	OR FIELD INTERIOR LIGHTS	1ECHM-6
rb7	LV7	1	TOGGLE: ON/OFF	ANESTHESIA WORKROOM 1C-127	ALL LIGHTS	1ECHM-6
rb8						

3 MICRO PANEL "LCb"

RELAY	CONTROL SWITCH	SWITCH QTY	FUNCTION	ROOMS CONTROLLED	LIGHT FIXTURES CONTROLLED	CIRCUIT
rc1	LV8	2	TOGGLE: ON/OFF	O.R. 5 1C-126	ALL ROOM DOWNLIGHTS	1ECHN-4
rc2	LV8	2	TOGGLE: ON/OFF	O.R. 5 1C-126	OR FIELD PERIMETER LIGHTS	1HN-4
rc3	LV8	2	TOGGLE: ON/OFF	O.R. 5 1C-126	OR FIELD INTERIOR LIGHTS	1ECHN-4
rc4	LV9	1	TOGGLE: ON/OFF	ORTHO STORAGE 1C-125	ALL LIGHTS	1HN-4
rc5						
rc6						
rc7						
rc8						

4 MICRO PANEL "LCc"

RELAY	CONTROL SWITCH	SWITCH QTY	FUNCTION	ROOMS CONTROLLED	LIGHT FIXTURES CONTROLLED	CIRCUIT
rd1	LV10	2	TOGGLE: ON/OFF	O.R. 6 1C-130	ALL ROOM DOWNLIGHTS	1ECHN-6
rd2	LV10	2	TOGGLE: ON/OFF	O.R. 6 1C-130	OR FIELD PERIMETER LIGHTS	1HN-6
rd3	LV10	2	TOGGLE: ON/OFF	O.R. 6 1C-130	OR FIELD INTERIOR LIGHTS	1ECHN-6
rd4	LV11	2	TOGGLE: ON/OFF	O.R. 7 1C-129	ALL ROOM DOWNLIGHTS	1ECHN-6
rd5	LV11	2	TOGGLE: ON/OFF	O.R. 7 1C-129	OR FIELD PERIMETER LIGHTS	1HN-6
rd6	LV11	2	TOGGLE: ON/OFF	O.R. 7 1C-129	OR FIELD INTERIOR LIGHTS	1ECHN-6
rd7						
rd8						

5 MICRO PANEL "LCd"

RELAY	CONTROL SWITCH	SWITCH QTY	FUNCTION	ROOMS CONTROLLED	LIGHT FIXTURES CONTROLLED	CIRCUIT
re1	LV12	1	TOGGLE: ON/OFF	COMM CENTER 1C-106	ALL CRITICAL FIXTURES	1ECHN-8
re2	LV12	1	TOGGLE: ON/OFF	COMM CENTER 1C-106	ALL NORMAL FIXTURES	1HN-8
re3	LV13	1	TOGGLE: ON/OFF	PRE-OP 1C-105	OVER BED "AMBIENT"	1ECHN-8
re4	LV13	1	TOGGLE: ON/OFF	PRE-OP 1C-105	OVER BED "EXAM LIGHT"	1ECHN-8
re5	LV13	1	TOGGLE: ON/OFF	PRE-OP 1C-105	OVER BED "READING"	1ECHN-8
re6	LV14	1	TOGGLE: ON/OFF	PRE-OP 1C-105	OVER BED "AMBIENT"	1ECHN-8
re7	LV14	1	TOGGLE: ON/OFF	PRE-OP 1C-105	OVER BED "EXAM LIGHT"	1ECHN-8
re8	LV14	1	TOGGLE: ON/OFF	PRE-OP 1C-105	OVER BED "READING"	1ECHN-8

6 MICRO PANEL "LCe"

RELAY	CONTROL SWITCH	SWITCH QTY	FUNCTION	ROOMS CONTROLLED	LIGHT FIXTURES CONTROLLED	CIRCUIT
rf1	LV15	1	TOGGLE: ON/OFF	PRE-OP 1C-105	OVER BED "AMBIENT"	1ECHN-8
rf2	LV15	1	TOGGLE: ON/OFF	PRE-OP 1C-105	OVER BED "EXAM LIGHT"	1ECHN-8
rf3	LV15	1	TOGGLE: ON/OFF	PRE-OP 1C-105	OVER BED "READING"	1ECHN-8
rf4	LV36	1	TOGGLE: ON/OFF	PRE-OP 1C-105	OVER BED "AMBIENT"	1ECHN-8
rf5	LV36	1	TOGGLE: ON/OFF	PRE-OP 1C-105	OVER BED "EXAM LIGHT"	1ECHN-8
rf6	LV36	1	TOGGLE: ON/OFF	PRE-OP 1C-105	OVER BED "READING"	1ECHN-8
rf7	LV23	1	TOGGLE: ON/OFF	NURSE STATION 1C-105A	DOWNLIGHTS	1ECHN-8
rf8	LV23	1	TOGGLE: ON/OFF	NURSE STATION 1C-105A	DECORATIVE PENDANT	1HN-8

7 MICRO PANEL "LCf"

RELAY	CONTROL SWITCH	SWITCH QTY	FUNCTION	ROOMS CONTROLLED	LIGHT FIXTURES CONTROLLED	CIRCUIT
rg1	LV16	1	TOGGLE: ON/OFF	PRE-OP 1C-105	OVER BED "AMBIENT"	1ECHN-8
rg2	LV16	1	TOGGLE: ON/OFF	PRE-OP 1C-105	OVER BED "EXAM LIGHT"	1ECHN-8
rg3	LV16	1	TOGGLE: ON/OFF	PRE-OP 1C-105	OVER BED "READING"	1ECHN-8
rg4	LV17	1	TOGGLE: ON/OFF	PRE-OP 1C-105	OVER BED "AMBIENT"	1ECHN-8
rg5	LV17	1	TOGGLE: ON/OFF	PRE-OP 1C-105	OVER BED "EXAM LIGHT"	1ECHN-8
rg6	LV17	1	TOGGLE: ON/OFF	PRE-OP 1C-105	OVER BED "READING"	1ECHN-8
rg7	LV22	3	TOGGLE: ON/OFF	PRE-OP 1C-105 CORRIDOR	ALL CRITICAL FIXTURES	BEL2-3
rg8	LV22	3	TOGGLE: ON/OFF	PRE-OP 1C-105 CORRIDOR	ALL NORMAL FIXTURES	1HN-8

8 MICRO PANEL "LCg"

RELAY	CONTROL SWITCH	SWITCH QTY	FUNCTION	ROOMS CONTROLLED	LIGHT FIXTURES CONTROLLED	CIRCUIT
rh1	LV18	1	TOGGLE: ON/OFF	PRE-OP 1C-105	OVER BED "AMBIENT"	1ECHN-10
rh2	LV18	1	TOGGLE: ON/OFF	PRE-OP 1C-105	OVER BED "EXAM LIGHT"	1ECHN-10
rh3	LV18	1	TOGGLE: ON/OFF	PRE-OP 1C-105	OVER BED "READING"	1ECHN-10
rh4	LV20	1	TOGGLE: ON/OFF	PRE-OP 1C-105	OVER BED "AMBIENT"	1ECHN-10
rh5	LV20	1	TOGGLE: ON/OFF	PRE-OP 1C-105	OVER BED "EXAM LIGHT"	1ECHN-10
rh6	LV20	1	TOGGLE: ON/OFF	PRE-OP 1C-105	OVER BED "READING"	1ECHN-10
rh7						
rh8						

9 MICRO PANEL "LCh"

RELAY	CONTROL SWITCH	SWITCH QTY	FUNCTION	ROOMS CONTROLLED	LIGHT FIXTURES CONTROLLED	CIRCUIT
ri1	LV21	1	TOGGLE: ON/OFF	PRE-OP 1C-105	OVER BED "AMBIENT"	1ECHN-10
ri2	LV21	1	TOGGLE: ON/OFF	PRE-OP 1C-105	OVER BED "EXAM LIGHT"	1ECHN-10
ri3	LV21	1	TOGGLE: ON/OFF	PRE-OP 1C-105	OVER BED "READING"	1ECHN-10
ri4	LV19	1	TOGGLE: ON/OFF	PRE-OP 1C-105	OVER BED "AMBIENT"	1ECHN-10
ri5	LV19	1	TOGGLE: ON/OFF	PRE-OP 1C-105	OVER BED "EXAM LIGHT"	1ECHN-10
ri6	LV19	1	TOGGLE: ON/OFF	PRE-OP 1C-105	OVER BED "READING"	1ECHN-10
ri7						
ri8						

10 MICRO PANEL "LCi"

RELAY	CONTROL SWITCH	SWITCH QTY	FUNCTION	ROOMS CONTROLLED	LIGHT FIXTURES CONTROLLED	CIRCUIT
rj1	LV26	1	TOGGLE: ON/OFF	PACU 1C-115	OVER BED "AMBIENT"	1ECHN-16
rj2	LV26	1	TOGGLE: ON/OFF	PACU 1C-115	OVER BED "EXAM LIGHT"	1ECHN-16
rj3	LV26	1	TOGGLE: ON/OFF	PACU 1C-115	OVER BED "READING"	1ECHN-16
rj4	LV27	1	TOGGLE: ON/OFF	PACU 1C-115	OVER BED "AMBIENT"	1ECHN-16
rj5	LV27	1	TOGGLE: ON/OFF	PACU 1C-115	OVER BED "EXAM LIGHT"	1ECHN-16
rj6	LV27	1	TOGGLE: ON/OFF	PACU 1C-115	OVER BED "READING"	1ECHN-16
rj7	LV24	3	TOGGLE: ON/OFF	PACU 1C-115 CORRIDOR	ALL CRITICAL FIXTURES	1ECHN-16
rj8	LV24	3	TOGGLE: ON/OFF	PACU 1C-115 CORRIDOR	ALL NORMAL FIXTURES	1HN-8

11 MICRO PANEL "LCj"

RELAY	CONTROL SWITCH	SWITCH QTY	FUNCTION	ROOMS CONTROLLED	LIGHT FIXTURES CONTROLLED	CIRCUIT
rk1	LV28	1	TOGGLE: ON/OFF	PACU 1C-115	OVER BED "AMBIENT"	1ECHN-16
rk2	LV28	1	TOGGLE: ON/OFF	PACU 1C-115	OVER BED "EXAM LIGHT"	1ECHN-16
rk3	LV28	1	TOGGLE: ON/OFF	PACU 1C-115	OVER BED "READING"	1ECHN-16
rk4	LV29	1	TOGGLE: ON/OFF	PACU 1C-115	OVER BED "AMBIENT"	1ECHN-16
rk5	LV29	1	TOGGLE: ON/OFF	PACU 1C-115	OVER BED "EXAM LIGHT"	1ECHN-16
rk6	LV29	1	TOGGLE: ON/OFF	PACU 1C-115	OVER BED "READING"	1ECHN-16
rk7	LV23	1	TOGGLE: ON/OFF	NURSE STATION 1C-115A	DOWNLIGHTS	1ECHN-16
rk8	LV23	1	TOGGLE: ON/OFF	NURSE STATION 1C-115A	DECORATIVE PENDANT	1HN-8

12 MICRO PANEL "LCk"

GENERAL SHEET NOTES:

1. SEE DRAWING E-001 FOR ELECTRICAL SYMBOLS AND ABBREVIATIONS AND DRAWING E-002 FOR ELECTRICAL NOTES.
2. SEE DRAWINGS P1-EL111, P2-EL111, P3-EL111.A, P3-EL111.B AND P4-EL111 FOR LIGHTING FLOOR PLANS.

RELAY	CONTROL SWITCH	SWITCH QTY	FUNCTION	ROOMS CONTROLLED	LIGHT FIXTURES CONTROLLED	CIRCUIT
rm1	LV30	1	TOGGLE: ON/OFF	PACU 1C-115	OVER BED "AMBIENT"	1ECHN-14
rm2	LV30	1	TOGGLE: ON/OFF	PACU 1C-115	OVER BED "EXAM LIGHT"	1ECHN-14
rm3	LV30	1	TOGGLE: ON/OFF	PACU 1C-115	OVER BED "READING"	1ECHN-14
rm4	LV31	1	TOGGLE: ON/OFF	PACU 1C-115	OVER BED "AMBIENT"	1ECHN-14
rm5	LV31	1	TOGGLE: ON/OFF	PACU 1C-115	OVER BED "EXAM LIGHT"	1ECHN-14
rm6	LV31	1	TOGGLE: ON/OFF	PACU 1C-115	OVER BED "READING"	1ECHN-14
rm7						
rm8						

13 MICRO PANEL "LCm"

RELAY	CONTROL SWITCH	SWITCH QTY	FUNCTION	ROOMS CONTROLLED	LIGHT FIXTURES CONTROLLED	CIRCUIT
rn1	LV32	1	TOGGLE: ON/OFF	PACU 1C-115	OVER BED "AMBIENT"	1ECHN-14
rn2	LV32	1	TOGGLE: ON/OFF	PACU 1C-115	OVER BED "EXAM LIGHT"	1ECHN-14
rn3	LV32	1	TOGGLE: ON/OFF	PACU 1C-115	OVER BED "READING"	1ECHN-14
rn4	LV33	1	TOGGLE: ON/OFF	PACU 1C-115	OVER BED "AMBIENT"	1ECHN-14
rn5	LV33	1	TOGGLE: ON/OFF	PACU 1C-115	OVER BED "EXAM LIGHT"	1ECHN-14
rn6	LV33	1	TOGGLE: ON/OFF	PACU 1C-115	OVER BED "READING"	1ECHN-14
rn7						
rn8						

14 MICRO PANEL "LCn"

RELAY	CONTROL SWITCH	SWITCH QTY	FUNCTION	ROOMS CONTROLLED	LIGHT FIXTURES CONTROLLED	CIRCUIT
ro1	LV34	1	TOGGLE: ON/OFF	PACU 1C-115	OVER BED "AMBIENT"	1ECHN-14
ro2	LV34	1	TOGGLE: ON/OFF	PACU 1C-115	OVER BED "EXAM LIGHT"	1ECHN-14
ro3	LV34	1	TOGGLE: ON/OFF	PACU 1C-115	OVER BED "READING"	1ECHN-14
ro4						
ro5						
ro6						
ro7						
ro8						

15 MICRO PANEL "LCo"

three inches = one foot
one and one half inches = one foot
one inch = one foot
three quarters inch = one foot
one half inch = one foot
three eighths inch = one foot
one quarter inch = one foot
one eighth inch = one foot

P:\0499_DVA\0499-0136 Salem Renovate Surgical Suite\4_Drawings\1_Cad\1_Current Submittal Phase\7_Electrical\E-705.dwg 12-29-25 08:23:12 AM MRonco

PRINTS OF THIS DRAWING SHALL NOT BE USED FOR ANY PURPOSE WHATSOEVER WITHOUT THE SEAL AND SIGNATURE OF THE PROFESSIONAL ENGINEER.

NO.	DESCRIPTION	DATE

CONSULTANTS

Architecture:	Civil Engineering:	Fire & Life Safety:
PF&A DESIGN, P.C.	LABELLA ASSOCIATES	STANTON ENGINEERING SERVICES, LLC

ENGINEER OF RECORD

MILLER•REMICK
A Service-Disabled Veteran-Owned Small Business
(856) 429-4000 • Miller-Remick.com
M-R PROJECT NO. 0499-0136

MILLER-REMICK LLC
PROFESSIONAL ENGINEER

COMMONWEALTH OF PENNSYLVANIA — REGISTERED PROFESSIONAL — THOMAS REGINO — ENGINEER No. PE094195
12/30/25

Office of Construction and Facilities Management

VA U.S. Department of Veterans Affairs

Drawing Title	ELECTRICAL RELAY PANEL SCHEDULES
Approved by:	Jon Manninen, COR
Phase	BID DOCUMENTS
	FULLY SPRINKLERED
Project Title	RENOVATE SURGICAL SUITE PHASE II
Project Number	658-19-103
Location	SALEM VA MEDICAL CENTER
Issue Date	2025-12-30
Checked	MJR
Drawn	MJR
VA Drawing Number	2617
Building Number	143
Drawing Number	E-705

VA FORM 08-6231

FIRE ALARM ABBREVIATIONS

AAR	AUTOMATIC AIR RELEASE	FS	FLOW SWITCH
AFF	ABOVE FINISHED FLOOR	FT	FEET
AHU	AIR HANDLING UNIT	GA	GAUGE
ALV	ALARM CHECK VALVE	GC	GENERAL CONTRACTOR
AS	AUTOMATIC SPRINKLER	GPM	GALLONS PER MINUTE
BATT	BATTERY	GR	GENERATOR RUNNING
BFP	BACK FLOW PREVENTER	GF	GENERATOR FAULT
BOR	BOTTOM OF RISER	HGT	HEIGHT
CHV	CHECK VALVE	HL	HI/LOW AIR SUPERVISORY
CIS	COMMON INTELLIGIBILITY SCORE	HT	HEAT TRACING
CLG	CEILING	ID	INSIDE DIAMETER
CONT	CONTINUE/ CONTINUOUS	KH	KITCHEN HOOD SUPPRESSION SYSTEM
COR	CONTRACTING OFFICER'S REPRESENTATIVE	LH	LIGHT HAZARD
CTR	CENTER	LOC	LOCAL OPERATING CONSOLE
CV	CONTROL VALVE	MNS	MASS NOTIFICATION SYSTEM
DACT	DIGITAL ALARM COMMUNICATOR TRANSMITTER	OD	OUTSIDE DIAMETER
DBA	DECIBEL A-WEIGHTED	OH	ORDINARY HAZARD
DEMO	DEMOLISH, DEMOLITION	PER	PRIMARY ELEVATOR RECALL
DC	DIRECT CURRENT	PS	PRESSURE SWITCH
DD	DUCT SMOKE DETECTOR	PSI	POUNDS PER SQUARE INCH
DH	DOOR HOLD	R	RISER/RADIUS/RETURN
DIA	DIAMETER	RCV	RISER CONTROL VALVE
DIM	DIMENSION	REQ	REQUIRED
DN	DOWN/DROP NIPPLE	RM	ROOM
E	ELEVATOR RECALL	RN	RISER NIPPLE
EA	EACH	RPZ	REDUCED PRESSURE ZONE
EAR	ELEVATOR ALTERNATE FLOOR RECALL	S	SUPPLY
EB	ELECTRIC BELL	SBV	SUPERVISED BUTTERFLY VALVE
EF	EXHAUST FAN	SCHED	SCHEDULE
EFF	ELEVATOR FIRE HAT FLASHING	SCV	SUPERVISED CONTROL VALVE
EFS	ELEVATOR FIRE HAT SOLID	SD	SMOKE DETECTOR
EH	EXTRA HAZARD	SDC	SMOKE DAMPER CONTROL
EJ	EXPANSION JOINT	SGV	SUPERVISED GATE VALVE
EL	ELEVATION	SIM	SIMILAR
ELEV	ELEVATOR	SO	SOUND SYSTEM OVERRIDE
EMER	EMERGENCY	SP	SPEAKER
EPR	ELEVATOR PRIMARY FLOOR RECALL	SPEC	SPECIFICATION
EPS	ELEVATOR SHUNT TRIP POWER MONITORING	SPKR	SPRINKLER
EQUIP	EQUIPMENT	SP/ST	SPEAKER/ STROBE
EST	ELEVATOR SHUNT TRIP	SQ	SQUARE
ETR	EXISTING TO REMAIN	SR	SLEEPING ROOM
EXIST	EXISTING	SSI	SECURITY SYSTEM INTERFACE
FA	FIRE ALARM	ST	STROBE
FMCP	FIRE ALARM/MASS NOTIFICATION CONTROL PANEL	STP	STANDPIPE
FD	FLOOR DRAIN	STOR	STORAGE
FDC	FIRE DEPARTMENT CONNECTION	STS	SHUNT TRIP SUPERVISION
FE	FIRE EXTINGUISHER	SYST	SYSTEM
FEC	FIRE EXTINGUISHER CABINET	SYST-FEED	SPRINKLER SYSTEM FEED MAIN
FFE	FINISHED FLOOR ELEVATION	TEMP	TEMPERATURE
FH	FIRE HAT	TOR	TOP OF RISER
FHV	FIRE HOSE VALVE	TS	TAMPER SWITCH
FLR	FLOOR	TYP	TYPICAL
FM	FACTORY MUTUAL	UL	UNDERWRITERS' LABORATORY
FP	FIRE PUMP	UNO	UNLESS NOTED OTHERWISE
FPE	FIRE PUMP EMERGENCY ISOLATING SWITCH OPEN	VAC	VOLT, ALTERNATING CURRENT
FPF	FIRE PUMP FAULT	W/	WITH
FPL	FIRE PUMP POWER/PHASE LOSS	WMG	WATER MOTOR GONG
FPO	FIRE PUMP POWER AVAILABLE	W/O	WITHOUT
FPP	FIRE PUMP PHASE REVERSAL	WP	WEATHERPROOF
FPR	FIRE PUMP RUNNING	WS	WET SYSTEM
FPT	FIRE PUMP TRANSFER SWITCH IN EMERGENCY POSITION	ZCA	ZONE CONTROL ASSEMBLY

FIRE ALARM LEGEND (EXISTING, DEMOLITION, NEW WORK)

SMOKE DETECTOR (YY - SEE ABBREVIATIONS)

DUCT SMOKE DETECTOR

SPEAKER /STROBE (CLEAR)
(C - CEILING MOUNTED)
(XX - CANDELA RATING)
(YY - SEE ABBREVIATIONS)

SPEAKER (C - CEILING MOUNTED)
(YY - SEE ABBREVIATIONS)

MANUAL PULL STATION

FIRE ALARM/MASS NOTIFICATION CONTROL PANEL

ADDRESSABLE OUTPUT MODULE

ADDRESSALBE INPUT MODULE

FIRE ALARM ANNUNCIATOR

ZONE BOUNDARY

FIRE ALARM GENERAL NOTES

1. THE FIRE ALARM SCOPE OF WORK FOR THE PROJECT INVOLVES MODIFICATIONS TO THE EXISTING SIMPLEX 4100U FIRE ALARM SYSTEM SERVING THE AREAS IN THE PROJECT SCOPE OF WORK AREA AS INDICATED ON THE DRAWINGS AND THE GENERATOR BUILDING.
2. SYSTEMS SHALL BE DESIGNED, INSTALLED AND TESTED IN ACCORDANCE WITH THE CONTRACT DOCUMENTS AS WELL AS THE FOLLOWING CODES AND STANDARDS:
   A. CRITERIA IN VA-PG-18-10 FIRE PROTECTION DESIGN MANUAL (DECEMBER 2015)
   B. IBC - INTERNATIONAL BUILDING CODE, 2018 (WITH AMENDMENTS)
   C. NFPA 70 - NATIONAL ELECTRIC CODE, 2017 EDITION
   D. NFPA 72 - NATIONAL FIRE ALARM AND SIGNALING CODE, 2019 EDITION
   E. NFPA 101 - LIFE SAFETY CODE, 2018 EDITION
3. ALL NEW FIRE ALARM DEVICES SHALL BE COMPATIBLE WITH THE EXISTING SIMPLEX 4100U FIRE ALARM SYSTEM.
4. MODIFICATIONS TO THE FIRE ALARM SHALL FOLLOW THE BUILDING'S EXISTING FIRE ALARM SEQUENCE OF OPERATIONS.
5. TWO WEEKS PRIOR TO FINAL INSPECTION, CONTRACTOR SHALL DELIVER TO THE COR 3 SETS OF AS-BUILT DRAWINGS AND ONE SET OF THE AS BUILT DRAWING COMPUTER FILES SHOWING ALL NEW AND/OR EXISTING DEVICES AND CONDUIT USED FOR THE FIRE ALARM SYSTEM.
6. FINAL FIRE ALARM SYSTEM TESTING SHALL BE WITNESSED BY THE COR.
7. FILE A "RECORD OF COMPLETION" PREPARED IN ACCORDANCE WITH NFPA 72, AND THE FIRE ALARM TEST REPORT, WITH THE COR.
8. TAMPER SWITCHES AND FLOW SWITCHES SHALL BE INSTALLED UNDER DIVISION 21 BUT SHALL BE CONNECTED TO THE FIRE ALARM SYSTEM BY THE FIRE ALARM CONTRACTOR.
9. FIRE AND SMOKE STOP ALL PENETRATIONS THROUGH RATED ASSEMBLIES. PROVIDE THROUGH-PENETRATION FIRESTOP SYSTEM PER UL 1479 AND SPECIFICATIONS.
10. ALL NEW FIRE ALARM WIRING SHALL BE CLASS B AND INSTALLED IN RED METALLIC CONDUIT. ALL FIRE ALARM WIRING MUST BE INSTALLED IN CONDUIT SEPARATE FROM ALL OTHER SYSTEMS.
11. DEVICES SHOWN ON THE DRAWINGS ARE THE REQUIRED TYPE IN APPROXIMATE LOCATIONS. AUDIO/VISUAL DEVICES ARE REQUIRED IN ALL NORMALLY OCCUPIED, PUBLIC AND COMMON USE AREAS AS SHOWN ON THE DRAWINGS HEREIN.
12. AUDIBLE FIRE ALARM SOUND LEVEL SHALL BE AT LEAST 15 dBA ABOVE THE AVERAGE AMBIENT SOUND LEVEL OR 5 dBA ABOVE THE MAXIMUM SOUND LEVEL HAVING A DURATION OF AT LEAST 60 SECONDS, WHICHEVER IS GREATER, MEASURING 5 FEET ABOVE THE FLOOR IN THE OCCUPIABLE AREA, BUT NOT GREATER THAN 120 dBA AT THE MINIMUM HEARING DISTANCE FROM THE AUDIBLE APPLIANCE. CONTRACTOR SHALL BE RESPONSIBLE FOR FINAL SPEAKER QUANTITY IN ORDER TO COMPLY WITH NFPA 72 AUDIBILITY REQUIREMENTS.

OUTAGE REQUIREMENTS

1. THERE SHALL BE NO INTERRUPTION OF THE EXISTING SPRINKLER PROTECTION, WATER, ELECTRIC OR FIRE ALARM SERVICES WITHOUT PRIOR PERMISSION OF THE COR.
2. CONTRACTOR SHALL DEVELOP AN INTERIM FIRE PROTECTION PROGRAM WHERE INTERRUPTIONS INVOLVE OCCUPIED SPACES. REQUEST IN WRITING AT LEAST ONE WEEK PRIOR TO THE PLANNED INTERRUPTION.
3. CONTRACTOR SHALL RECEIVE DIRECTION FROM THE COR TO PERFORM TIE IN OF NEW WORK AND/OR REPROGRAMMING OF OPERATING, EXISTING FIRE ALARM AND SPRINKLER SYSTEMS.

PRINTS OF THIS DRAWING SHALL NOT BE USED FOR ANY PURPOSE WHATSOEVER WITHOUT THE SEAL AND SIGNATURE OF THE PROFESSIONAL ENGINEER

Revisions: | Date:

CONSULTANT

Architecture:	Civil Engineering:	Fire & Life Safety:
PF&A DESIGN, P.C.	LABELLA ASSOCIATES	STANTON ENGINEERING SERVICES, LLC

ENGINEER OF RECORD

MILLER•REMICK
A Service-Disabled Veteran-Owned Small Business
(856) 429-4000 • Miller-Remick.com
M-R PROJECT NO. 2025-0136

STANTON ENGINEERING SERVICES PROFESSIONAL ENGINEER

PATRICK KENNETH JOHNSON — STATE OF WASHINGTON — 20108259 — REGISTERED PROFESSIONAL ENGINEER
12-30-2025

Office of Construction and Facilities Management

VA U.S. Department of Veterans Affairs

Drawing Title: FIRE ALARM COVERSHEET	Phase: BID DOCUMENTS
Approved by: Jon Manninen, COR	FULLY SPRINKLERED

Project Title: RENOVATE SURGICAL SUITE PHASE II	VA Drawing Number: 2617
Project Number: 658-19-103	Building Number: 143
Location: SALEM VA MEDICAL CENTER	Drawing Number: FA001
Issue Date: 2025-12-30 / Checked: PJ / Drawn: CA	

12/29/2025 4:46:27 PM

VA FORM 08 - 6231

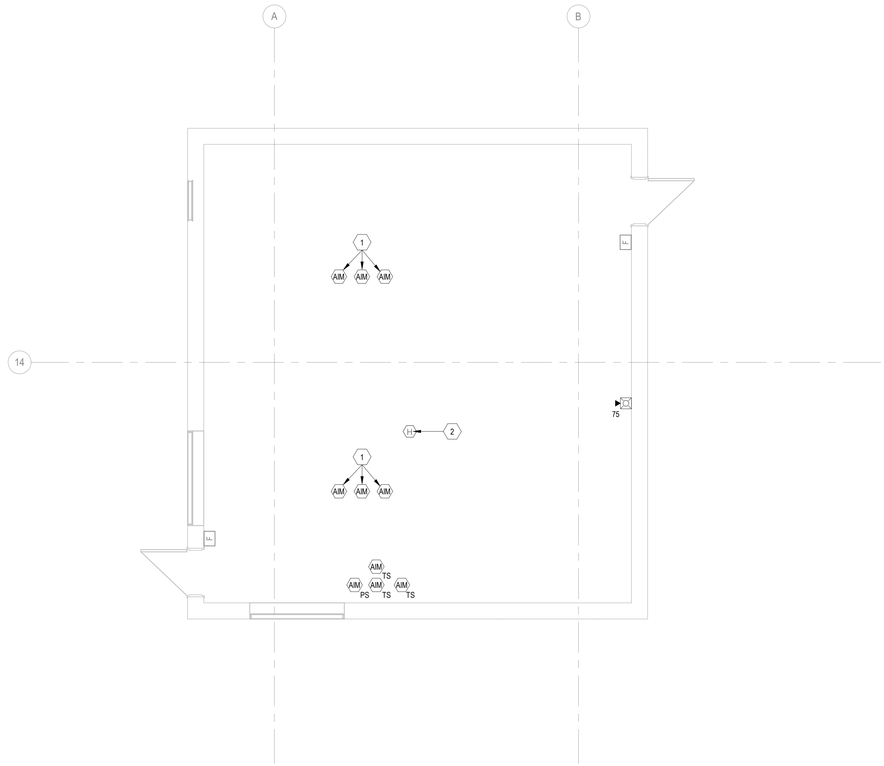

F1 GENERATOR BUILDING FIRE ALARM PLAN
1/4" = 1'-0"

GENERAL NOTES

1. ALL NEW FIRE ALARM DEVICES MUST BE COMPATIBLE WITH BUILDING 143'S EXISTING SIMPLEX 4100U CONTROL PANEL LOCATED IN THE ENGINEERING CONTROL ROOM BD-124 ON THE BASEMENT LEVEL.

KEYED NOTES

1 PROVIDE FIRE ALARM MODULES FOR MONITORING OF THE GENERATOR FOR THE FOLLOWING CONDITIONS: GENERATOR FAULT, GENERATOR RUNNING, AND GENERATOR IN NON-AUTO POSITION.

2 DEMOLISH EXISTING HEAT DETECTOR. PROJECT SCOPE OF WORK INCLUDES INSTALLATION OF NEW SPRINKLER SYSTEM, THEREFORE, HEAT DETECTOR IS NO LONGER REQUIRED PER VA FIRE PROTECTION DESIGN MANUAL 7.4.E.

PLAN NORTH
ACTUAL NORTH

PRINTS OF THIS DRAWING SHALL NOT BE USED FOR ANY PURPOSE WHATSOEVER WITHOUT THE SEAL AND SIGNATURE OF THE PROFESSIONAL ENGINEER

Revisions:	Date:

CONSULTANT

Architecture:	Civil Engineering:	Fire & Life Safety:
PF&A DESIGN, P.C.	LABELLA ASSOCIATES	STANTON ENGINEERING SERVICES, LLC

ENGINEER OF RECORD

MILLER•REMICK
A Service-Disabled Veteran-Owned Small Business
(856) 429-4000 • Miller-Remick.com
M-R PROJECT NO. 0499-0136

STANTON ENGINEERING SERVICES
PROFESSIONAL ENGINEER
PATRICK KENNETH STANTON
STATE OF WASHINGTON
REGISTERED PROFESSIONAL ENGINEER
12-30-2025

Office of Construction and Facilities Management

VA U.S. Department of Veterans Affairs

Drawing Title	FIRE ALARM NEW WORK PLAN GENERATOR BUILIDNG
Approved by:	Jon Manninen, COR
Phase	BID DOCUMENTS
	FULLY SPRINKLERED
Project Title	RENOVATE SURGICAL SUITE PHASE II
Project Number	658-19-103
Location	SALEM VA MEDICAL CENTER
Issue Date	2025-12-30
Checked	PJ
Drawn	CA
VA Drawing Number	2617
Building Number	143
Drawing Number	FA101

12/29/2025 4:33:19 PM

VA FORM 08 - 6231

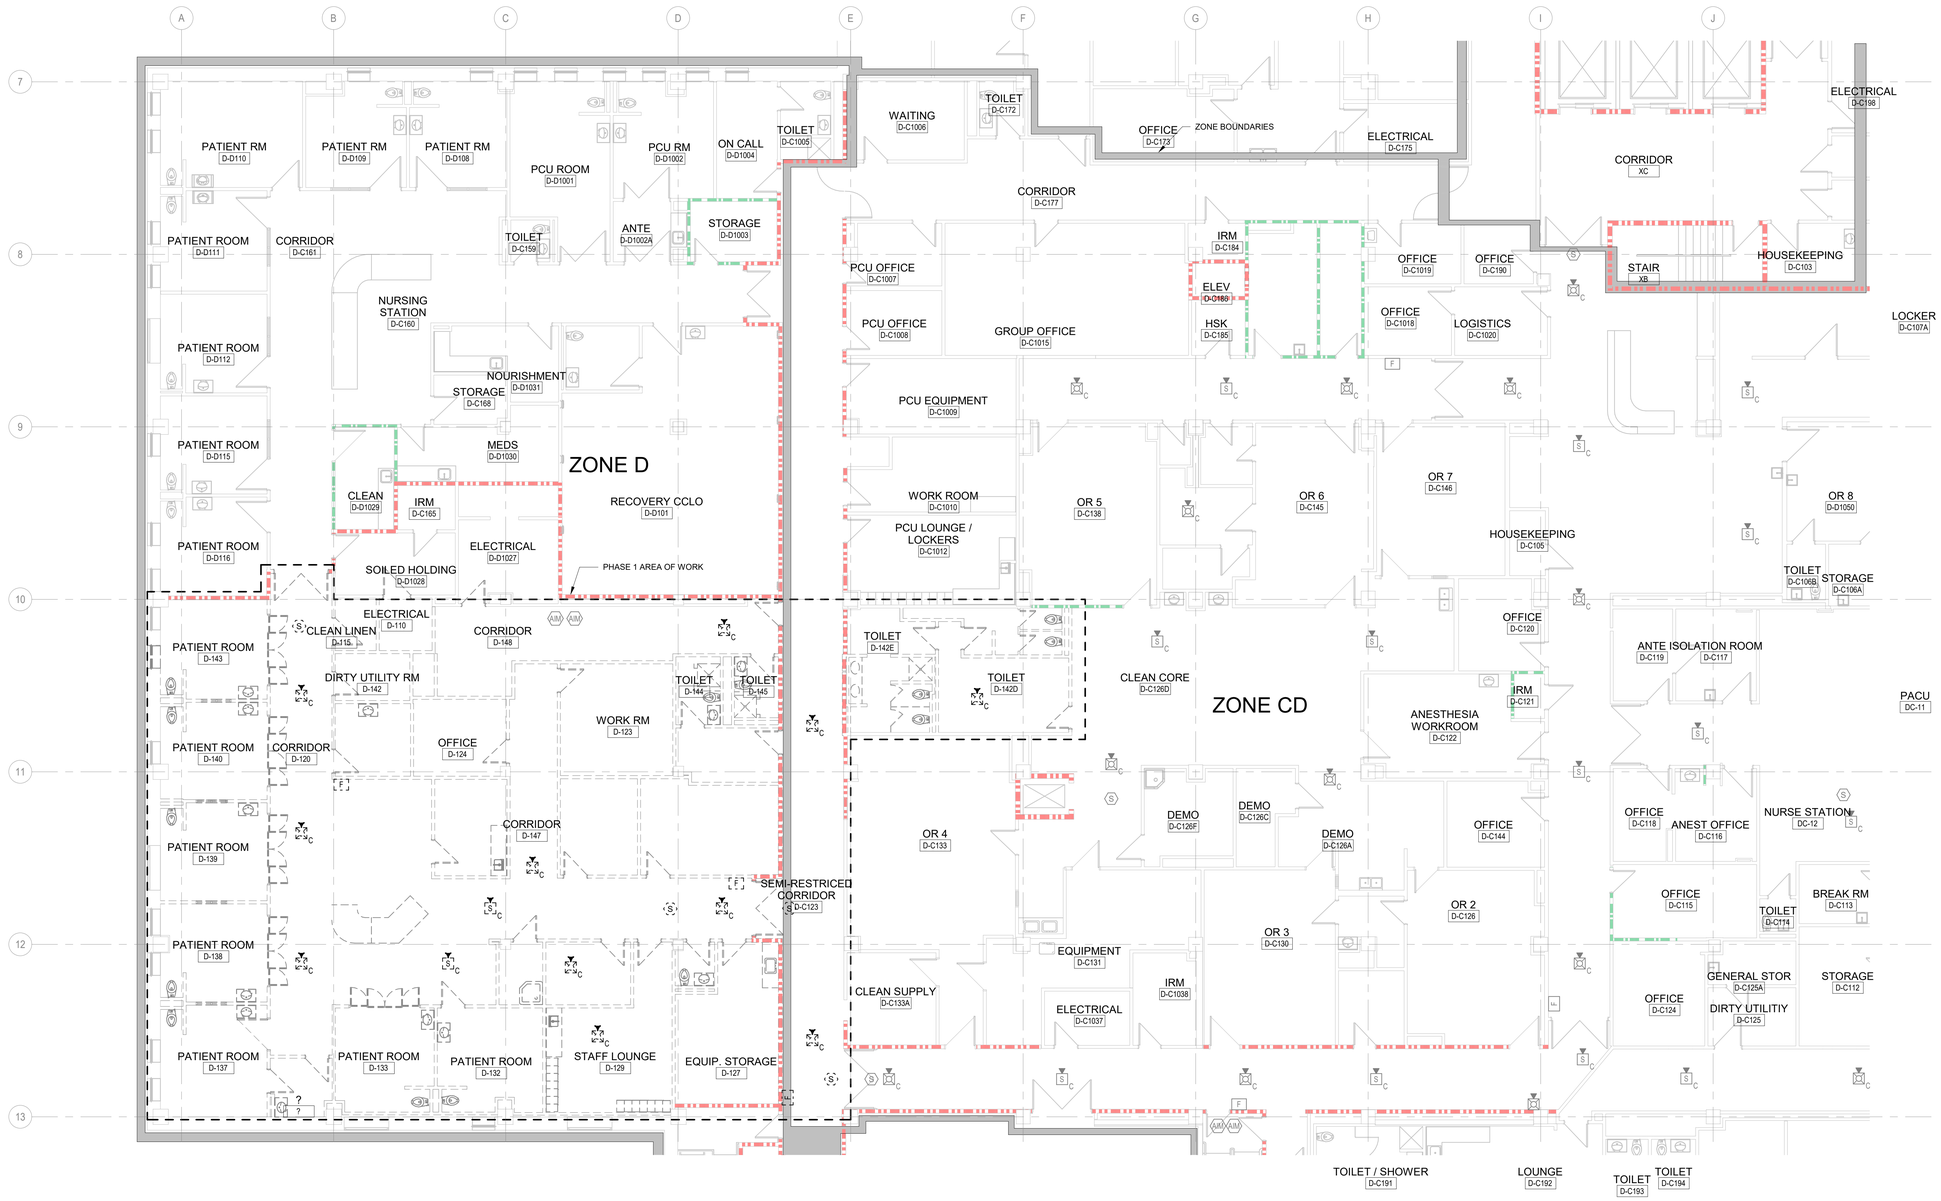

FIRST FLOOR FIRE ALARM DEMOLITION PLAN - PHASE 1

F1 1/8" = 1'-0"

GENERAL NOTES

1. DISCONNECT AND REMOVE EXISTING FIRE ALARM DEVICES INSIDE THE AREA OF WORK. REMOVE FIRE ALARM CABLING BACK TO NEXT DEVICE ON FIRE ALARM CIRCUIT THAT IS INDICATED AS EXISTING TO REMAIN, OR LOCATED OUTSIDE THE AREA OF DEMOLITION. IF NO OTHER DEVICES REMAIN ON FIRE ALARM CIRCUIT, REMOVE CABLE BACK TO SIMPLEX 4100U FIRE ALARM PANEL LOCATED IN THE ENGINEERING CONTROL ROOM BD-124 ON THE BASEMENT LEVEL.
2. CONTRACTOR SHALL COORDINATE WITH THE COR AND VA PERSONNEL PRIOR TO ANY WORK ON THE EXISTING FIRE ALARM SYSTEM.
3. EXISTING SMOKE ZONE BOUNDARIES SHOWN ARE BASED ON RECORD DOCUMENTATION AND GENERAL INFORMATION DRAWINGS. CONTRACTOR SHALL COORDINATE WITH THE COR AND VA PERSONNEL IF ANY DISCREPANCIES ARE DISCOVERED IN THE FIELD.
4. REFER TO GENERAL INFORMATION DRAWINGS FOR CONSTRUCTION PHASING INFORMATION.

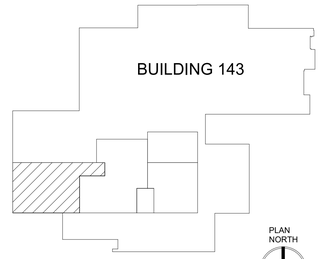

KEYPLAN

PRINTS OF THIS DRAWING SHALL NOT BE USED FOR ANY PURPOSE WHATSOEVER WITHOUT THE SEAL AND SIGNATURE OF THE PROFESSIONAL ENGINEER

Revisions: | Date:

CONSULTANT

Architecture:	Civil Engineering:	Fire & Life Safety:
PF&A DESIGN, P.C.	LABELLA ASSOCIATES	STANTON ENGINEERING SERVICES, LLC

ENGINEER OF RECORD

MILLER•REMICK
A Service-Disabled Veteran-Owned Small Business
(856) 429-4000 • Miller-Remick.com

STANTON ENGINEERING SERVICES PROFESSIONAL ENGINEER

PATRICK KENNETH JOHNSON — STATE OF WASHINGTON — 20100250 — REGISTERED PROFESSIONAL ENGINEER
12-30-2025

Office of Construction and Facilities Management

VA U.S. Department of Veterans Affairs

Drawing Title	FIRE ALARM DEMOLITION PLAN FIRST FLOOR PHASE 1
Approved by:	Jon Manninen, COR
Phase	BID DOCUMENTS
	FULLY SPRINKLERED
Project Title	RENOVATE SURGICAL SUITE PHASE II
Project Number	658-19-103
Location	SALEM VA MEDICAL CENTER
Issue Date	2025-12-30
Checked	PJ
Drawn	CA
VA Drawing Number	2617
Building Number	143
Drawing Number	P1-FD101

02/26/2025 4:46:43 PM

VA FORM 08 - 6231

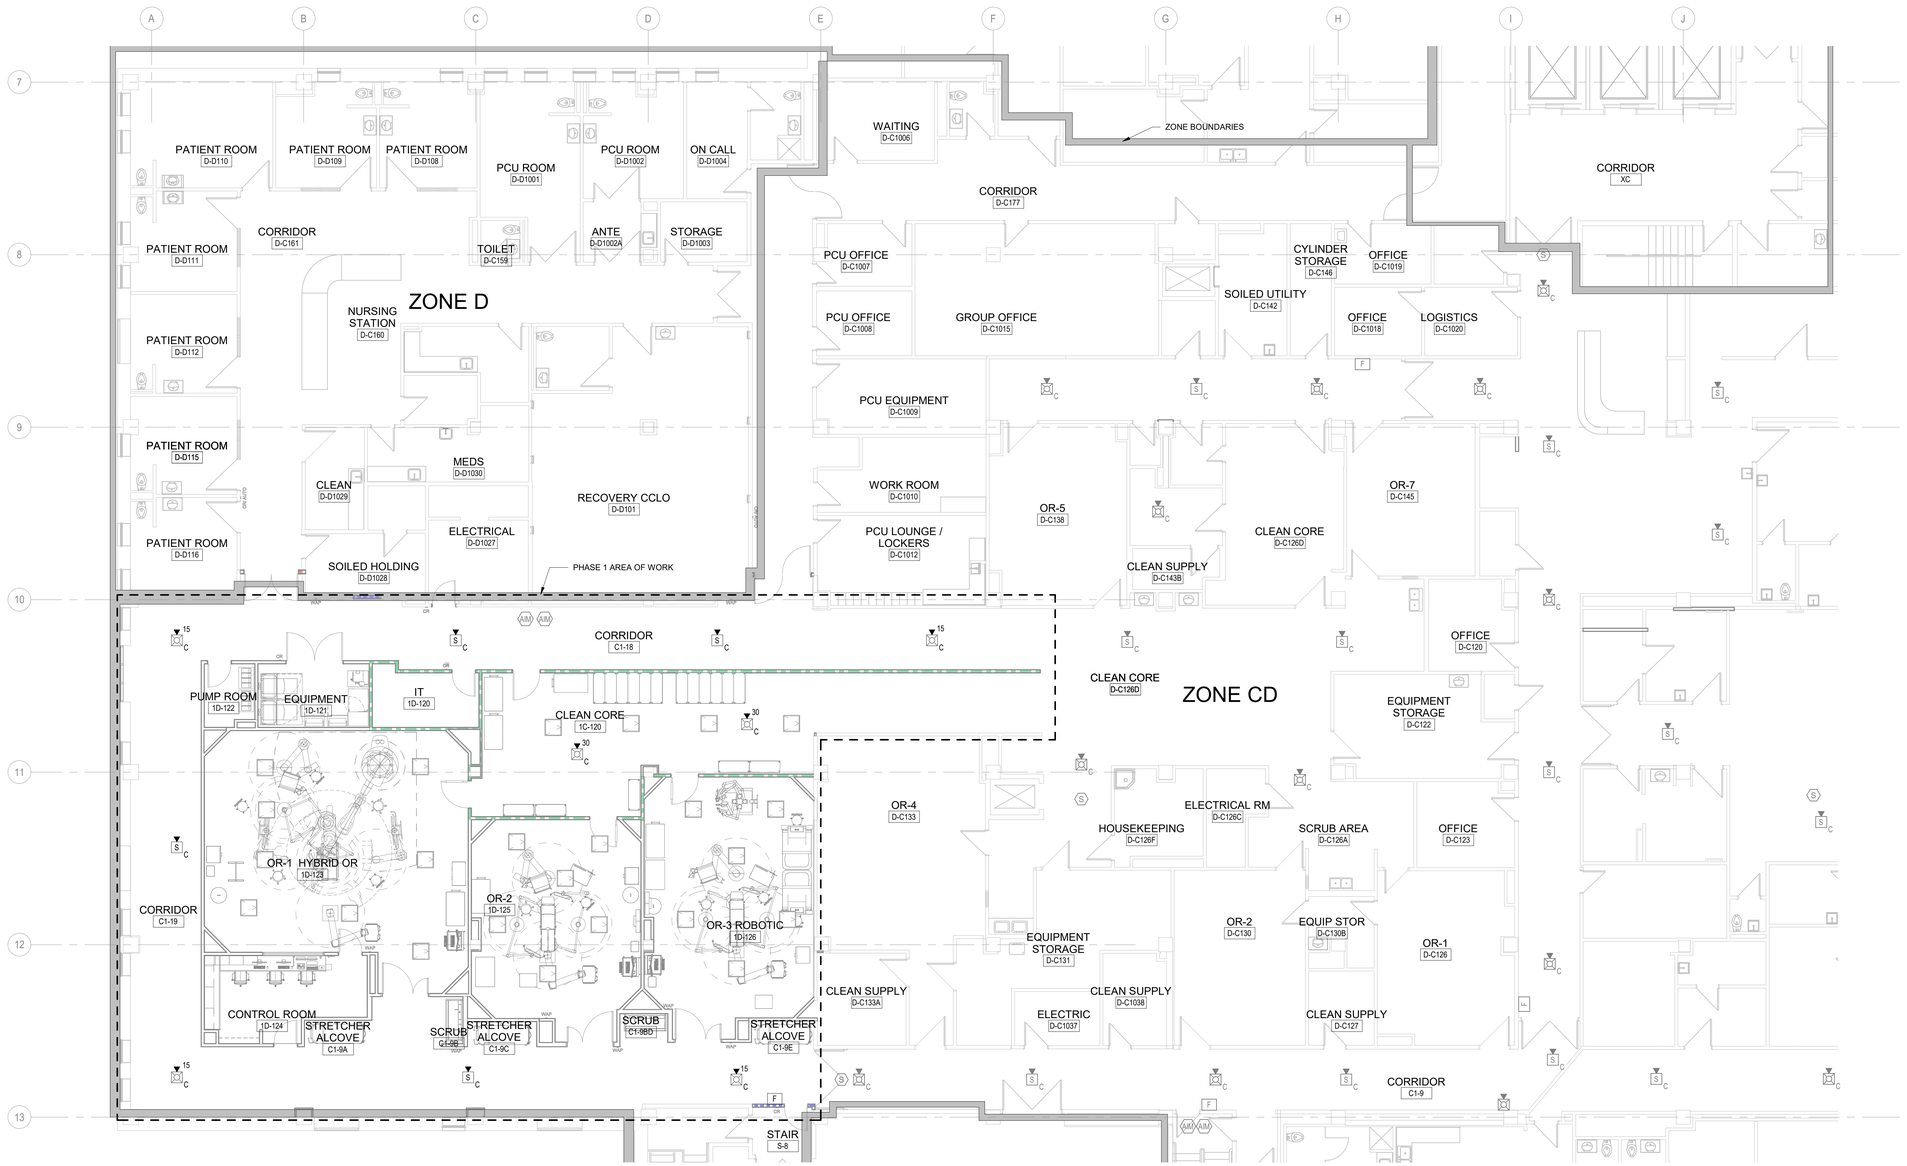

F1 FIRST FLOOR FIRE ALARM PLAN - PHASE 1

1/8" = 1'-0"

GENERAL NOTES

1. ALL NEW FIRE ALARM DEVICES MUST BE COMPATIBLE WITH THE BUILDING'S EXISTING SIMPLEX 4100U CONTROL PANEL LOCATED IN THE ENGINEERING CONTROL ROOM BD-124 ON THE BASEMENT LEVEL.
2. PROVIDE DUCT SMOKE DETECTORS FOR NEW ROOF TOP AIR HANDLING UNIT "143-RTU-2D1". PROVIDE DETECTORS IN BOTH SUPPLY AND RETURN AIR DUCTS IN ACCORDANCE WITH NFPA 90A. REFER TO AND COORDINATE WITH MECHANICAL DRAWINGS FOR EXACT LOCATIONS.
3. REFER TO GENERAL INFORMATION DRAWINGS FOR CONSTRUCTION PHASING INFORMATION.
4. ALL FIRE ALARM DEVICES, NEW AND EXISTING, SHALL BE PROGRAMMED TO MATCH THE NEW SMOKE ZONES AFTER EACH PHASE. THE NEW SMOKE ZONES BOUNDARIES SHOWN SHALL MATCH THE NEW SMOKE COMPARTMENTS SHOWN IN THE GENERAL INFORMATION DRAWINGS. ANY DISCREPANCIES SHALL BE COORDINATED WITH THE COR AND VA PERSONNEL.

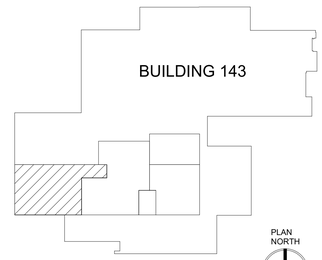

KEYPLAN

PRINTS OF THIS DRAWING SHALL NOT BE USED FOR ANY PURPOSE WHATSOEVER WITHOUT THE SEAL AND SIGNATURE OF THE PROFESSIONAL ENGINEER

Revisions: | Date:

CONSULTANT

Architecture:	Civil Engineering:	Fire & Life Safety:
PF&A DESIGN, P.C.	LABELLA ASSOCIATES	STANTON ENGINEERING SERVICES, LLC

ENGINEER OF RECORD

MILLER•REMICK
A Service-Disabled Veteran-Owned Small Business
(856) 429-4000 | Miller-Remick.com
M-R PROJECT NO. 2025-138

STANTON ENGINEERING SERVICES PROFESSIONAL ENGINEER

PATRICK KENNETH STANTON — STATE OF WASHINGTON — 20190299 — REGISTERED PROFESSIONAL ENGINEER
12-30-2025

Office of Construction and Facilities Management

U.S. Department of Veterans Affairs

Drawing Title	FIRE ALARM NEW WORK PLAN FIRST FLOOR PHASE 1
Approved by:	Jon Manninen, COR
Phase	BID DOCUMENTS
	FULLY SPRINKLERED
Project Title	RENOVATE SURGICAL SUITE PHASE II
Project Number	658-19-103
Location	SALEM VA MEDICAL CENTER
Issue Date	2025-12-30
Checked	PJ
Drawn	CA
VA Drawing Number	2617
Building Number	143
Drawing Number	P1-FA101

12/29/2025 4:46:39 PM

VA FORM 08 - 6231

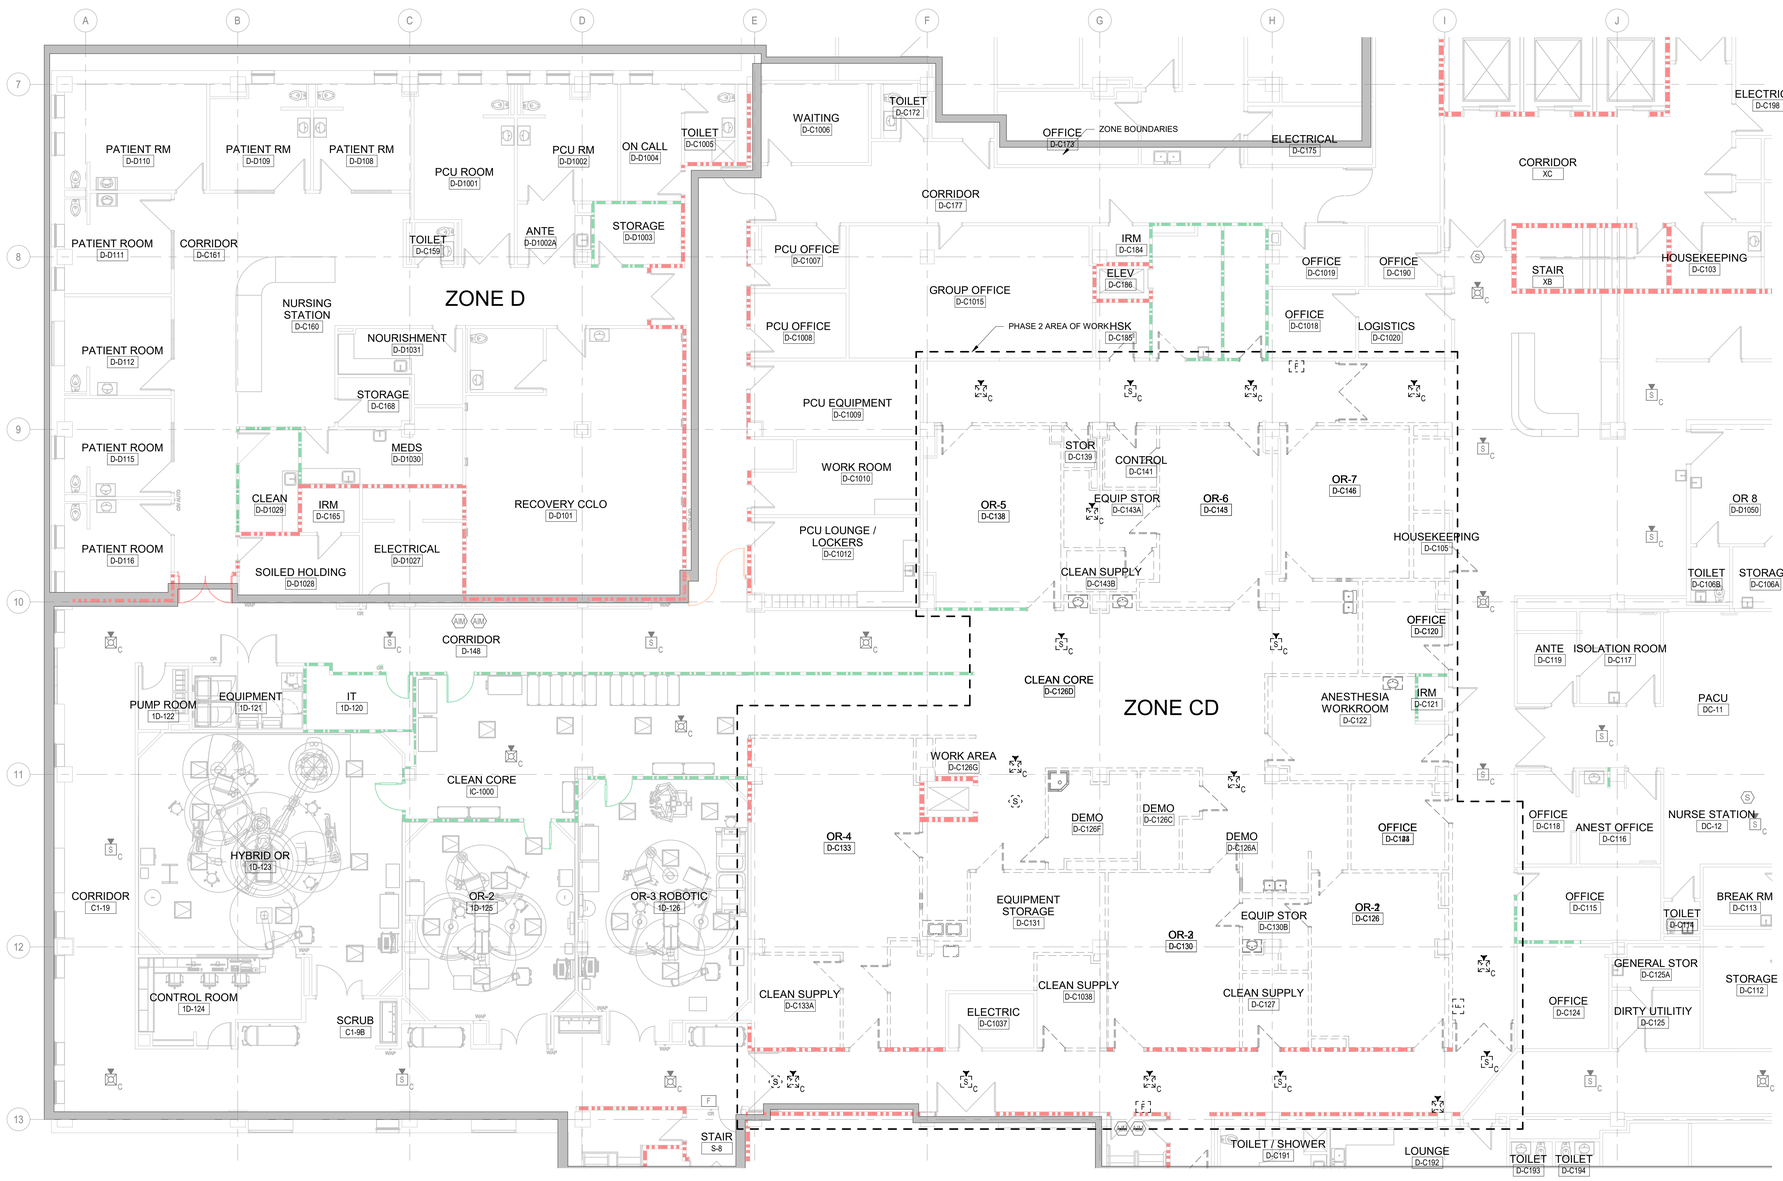

FIRST FLOOR FIRE ALARM DEMOLITION PLAN - PHASE 2

F1 1/8" = 1'-0"

GENERAL NOTES

1. DISCONNECT AND REMOVE EXISTING FIRE ALARM DEVICES INSIDE THE AREA OF WORK. REMOVE FIRE ALARM CABLING BACK TO NEXT DEVICE ON FIRE ALARM CIRCUIT THAT IS INDICATED AS EXISTING TO REMAIN, OR LOCATED OUTSIDE THE AREA OF DEMOLITION. IF NO OTHER DEVICES REMAIN ON FIRE ALARM CIRCUIT, REMOVE CABLE BACK TO SIMPLEX 4100U FIRE ALARM PANEL LOCATED IN THE ENGINEERING CONTROL ROOM BD-124 ON THE BASEMENT LEVEL.
2. CONTRACTOR SHALL COORDINATE WITH THE COR AND VA PERSONNEL PRIOR TO ANY WORK ON THE EXISTING FIRE ALARM SYSTEM.
3. EXISTING SMOKE ZONE BOUNDARIES SHOWN ARE BASED ON RECORD DOCUMENTATION AND GENERAL INFORMATION DRAWINGS. CONTRACTOR SHALL COORDINATE WITH THE COR AND VA PERSONNEL IF ANY DISCREPANCIES ARE DISCOVERED IN THE FIELD.
4. REFER TO GENERAL INFORMATION DRAWINGS FOR CONSTRUCTION PHASING INFORMATION.

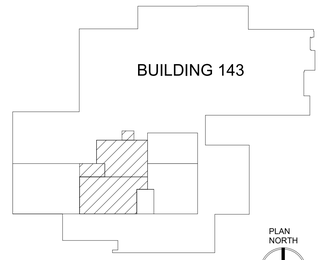

KEYPLAN

PRINTS OF THIS DRAWING SHALL NOT BE USED FOR ANY PURPOSE WHATSOEVER WITHOUT THE SEAL AND SIGNATURE OF THE PROFESSIONAL ENGINEER

Revisions: | Date:

CONSULTANT

Architecture:	Civil Engineering:	Fire & Life Safety:
PF&A DESIGN, P.C.	LABELLA ASSOCIATES	STANTON ENGINEERING SERVICES, LLC

ENGINEER OF RECORD

MILLER•REMICK
A Service-Disabled Veteran-Owned Small Business
(856) 429-4000 • Miller-Remick.com
M-R PROJECT NO. 0499-2136

STANTON ENGINEERING SERVICES PROFESSIONAL ENGINEER

12-30-2025

Office of Construction and Facilities Management

VA U.S. Department of Veterans Affairs

Drawing Title: FIRE ALARM DEMOLITION PLAN FIRST FLOOR PHASE 2	Phase: BID DOCUMENTS	Project Title: RENOVATE SURGICAL SUITE PHASE II	VA Drawing Number: 2617
		Project Number: 658-19-103	Building Number: 143
Approved by: Jon Manninen, COR	FULLY SPRINKLERED	Location: SALEM VA MEDICAL CENTER	Drawing Number: P2-FD101
		Issue Date: 2025-12-30 / Checked: PJ / Drawn: CA	

12/29/2025 4:47:06 PM

VA FORM 08 - 6231

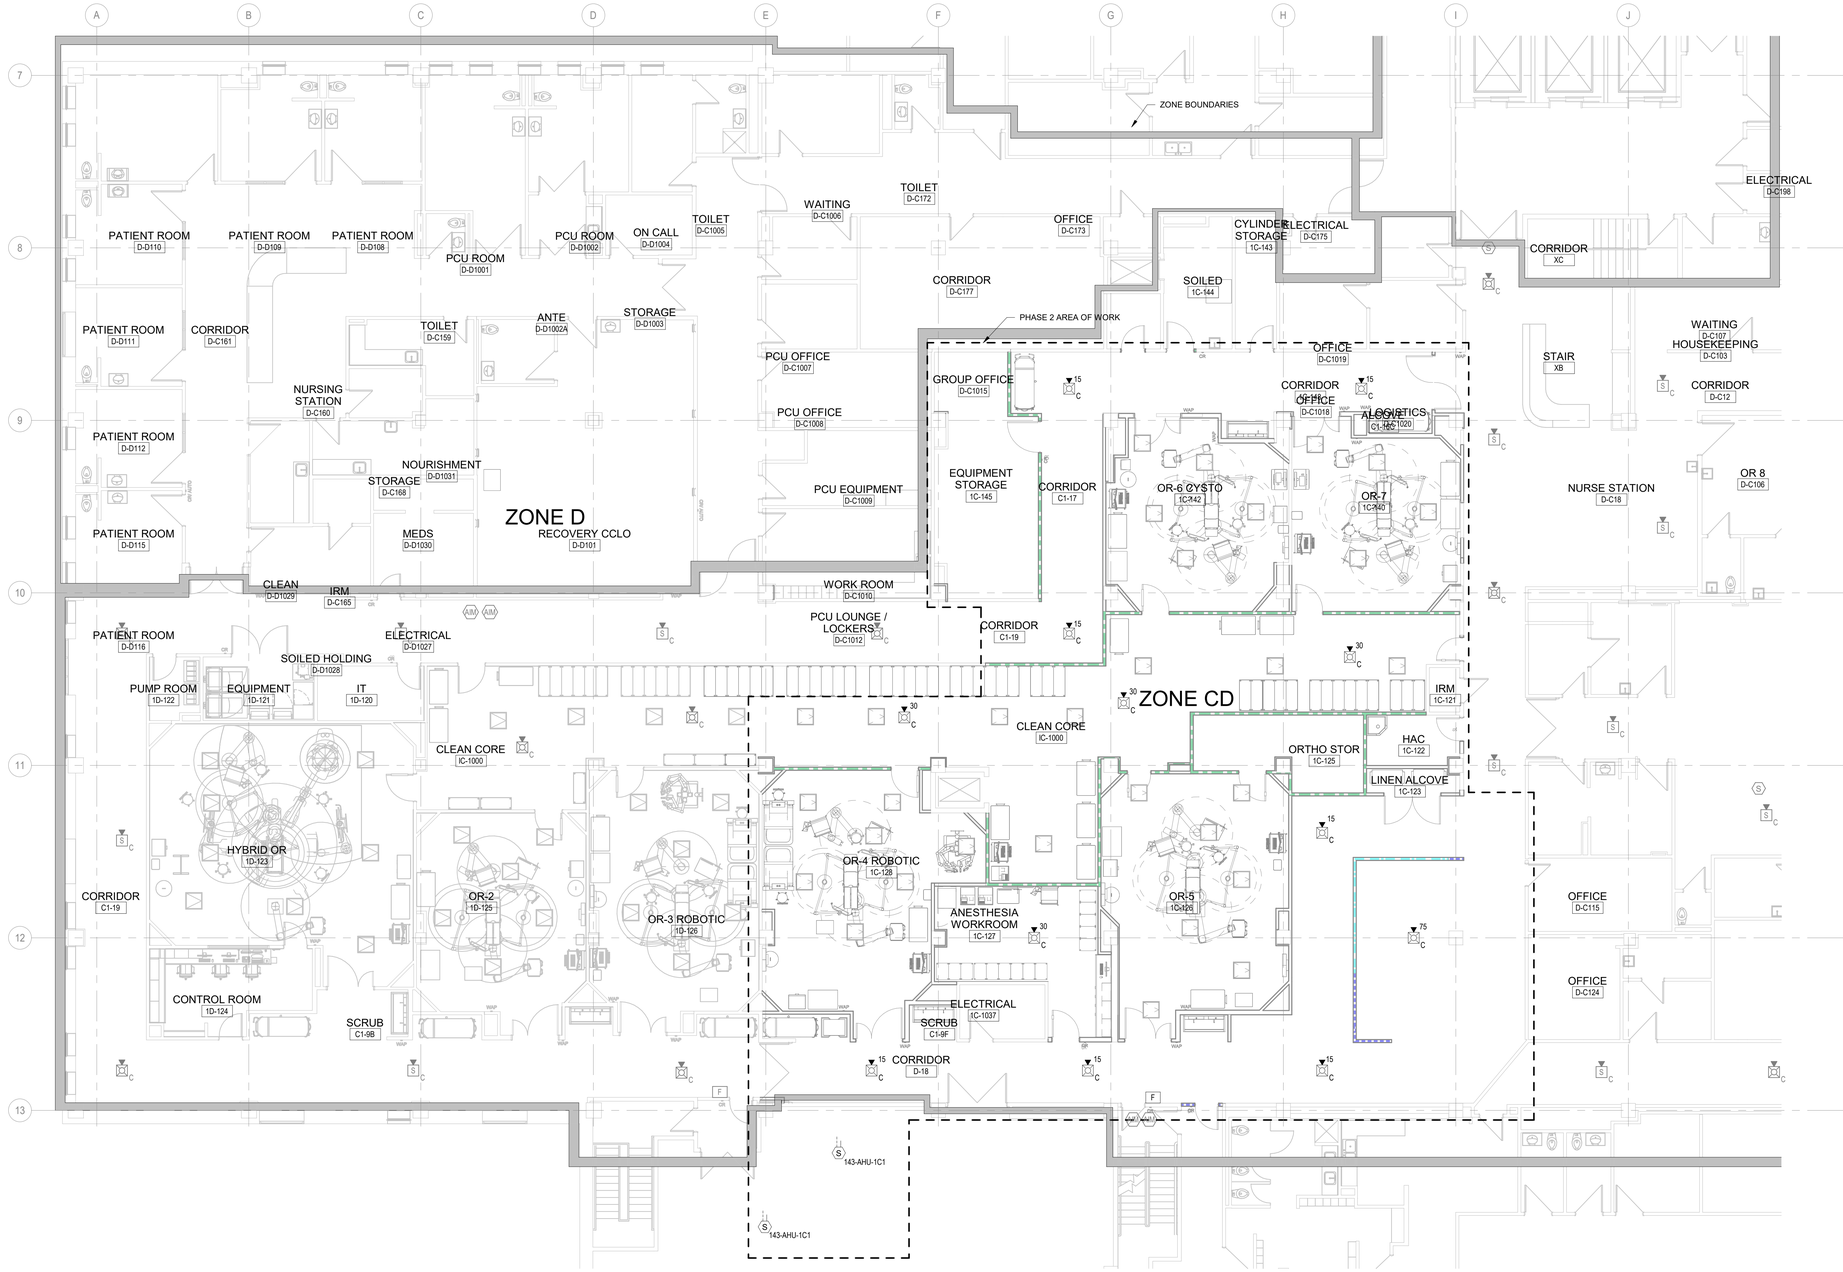

F1 FIRST FLOOR FIRE ALARM PLAN - PHASE 2

1/8" = 1'-0"

GENERAL NOTES

1. ALL NEW FIRE ALARM DEVICES MUST BE COMPATIBLE WITH THE BUILDING'S EXISTING SIMPLEX 4100U CONTROL PANEL LOCATED IN THE ENGINEERING CONTROL ROOM BD-124 ON THE BASEMENT LEVEL.
2. PROVIDE DUCT SMOKE DETECTORS FOR NEW MECHANICAL ROOM AIR HANDLING UNIT "143-RTU-1C1". PROVIDE DETECTORS IN BOTH SUPPLY AND RETURN AIR DUCTS IN ACCORDANCE WITH NFPA 90A. REFER TO AND COORDINATE WITH MECHANICAL DRAWINGS FOR EXACT LOCATIONS.
3. REFER TO GENERAL INFORMATION DRAWINGS FOR CONSTRUCTION PHASING INFORMATION.
4. ALL FIRE ALARM DEVICES, NEW AND EXISTING, SHALL BE PROGRAMMED TO MATCH THE NEW SMOKE ZONES AFTER EACH PHASE. THE NEW SMOKE ZONES BOUNDARIES SHOWN SHALL MATCH THE NEW SMOKE COMPARTMENTS SHOWN IN THE GENERAL INFORMATION DRAWINGS. ANY DISCREPANCIES SHALL BE COORDINATED WITH THE COR AND VA PERSONNEL.

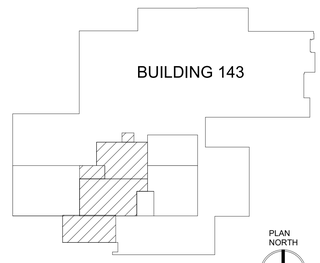

KEYPLAN

PRINTS OF THIS DRAWING SHALL NOT BE USED FOR ANY PURPOSE WHATSOEVER WITHOUT THE SEAL AND SIGNATURE OF THE PROFESSIONAL ENGINEER

Revisions: | Date:

CONSULTANT

Architecture:	Civil Engineering:	Fire & Life Safety:
PF&A DESIGN, P.C.	LABELLA ASSOCIATES	STANTON ENGINEERING SERVICES, LLC

ENGINEER OF RECORD

MILLER•REMICK
A Service-Disabled Veteran-Owned Small Business
(856) 429-4000 • Miller-Remick.com
M-R PROJECT NO. 0469-0136

STANTON ENGINEERING SERVICES PROFESSIONAL ENGINEER
PATRICK KENNETH STANTON — STATE OF WASHINGTON — 21019036 — REGISTERED PROFESSIONAL ENGINEER
12-30-2025

Office of Construction and Facilities Management

VA U.S. Department of Veterans Affairs

Drawing Title FIRE ALARM NEW WORK PLAN FIRST FLOOR PHASE 2	**Phase** BID DOCUMENTS	**Project Title** RENOVATE SURGICAL SUITE PHASE II	**VA Drawing Number** 2617
Approved by: Jon Manninen, COR	FULLY SPRINKLERED	**Project Number** 658-19-103	**Building Number** 143
		Location SALEM VA MEDICAL CENTER	**Drawing Number** P2-FA101
		Issue Date 2025-12-30 / **Checked** PJ / **Drawn** CA	

12/29/2025 4:47:01 PM

VA FORM 08 - 6231

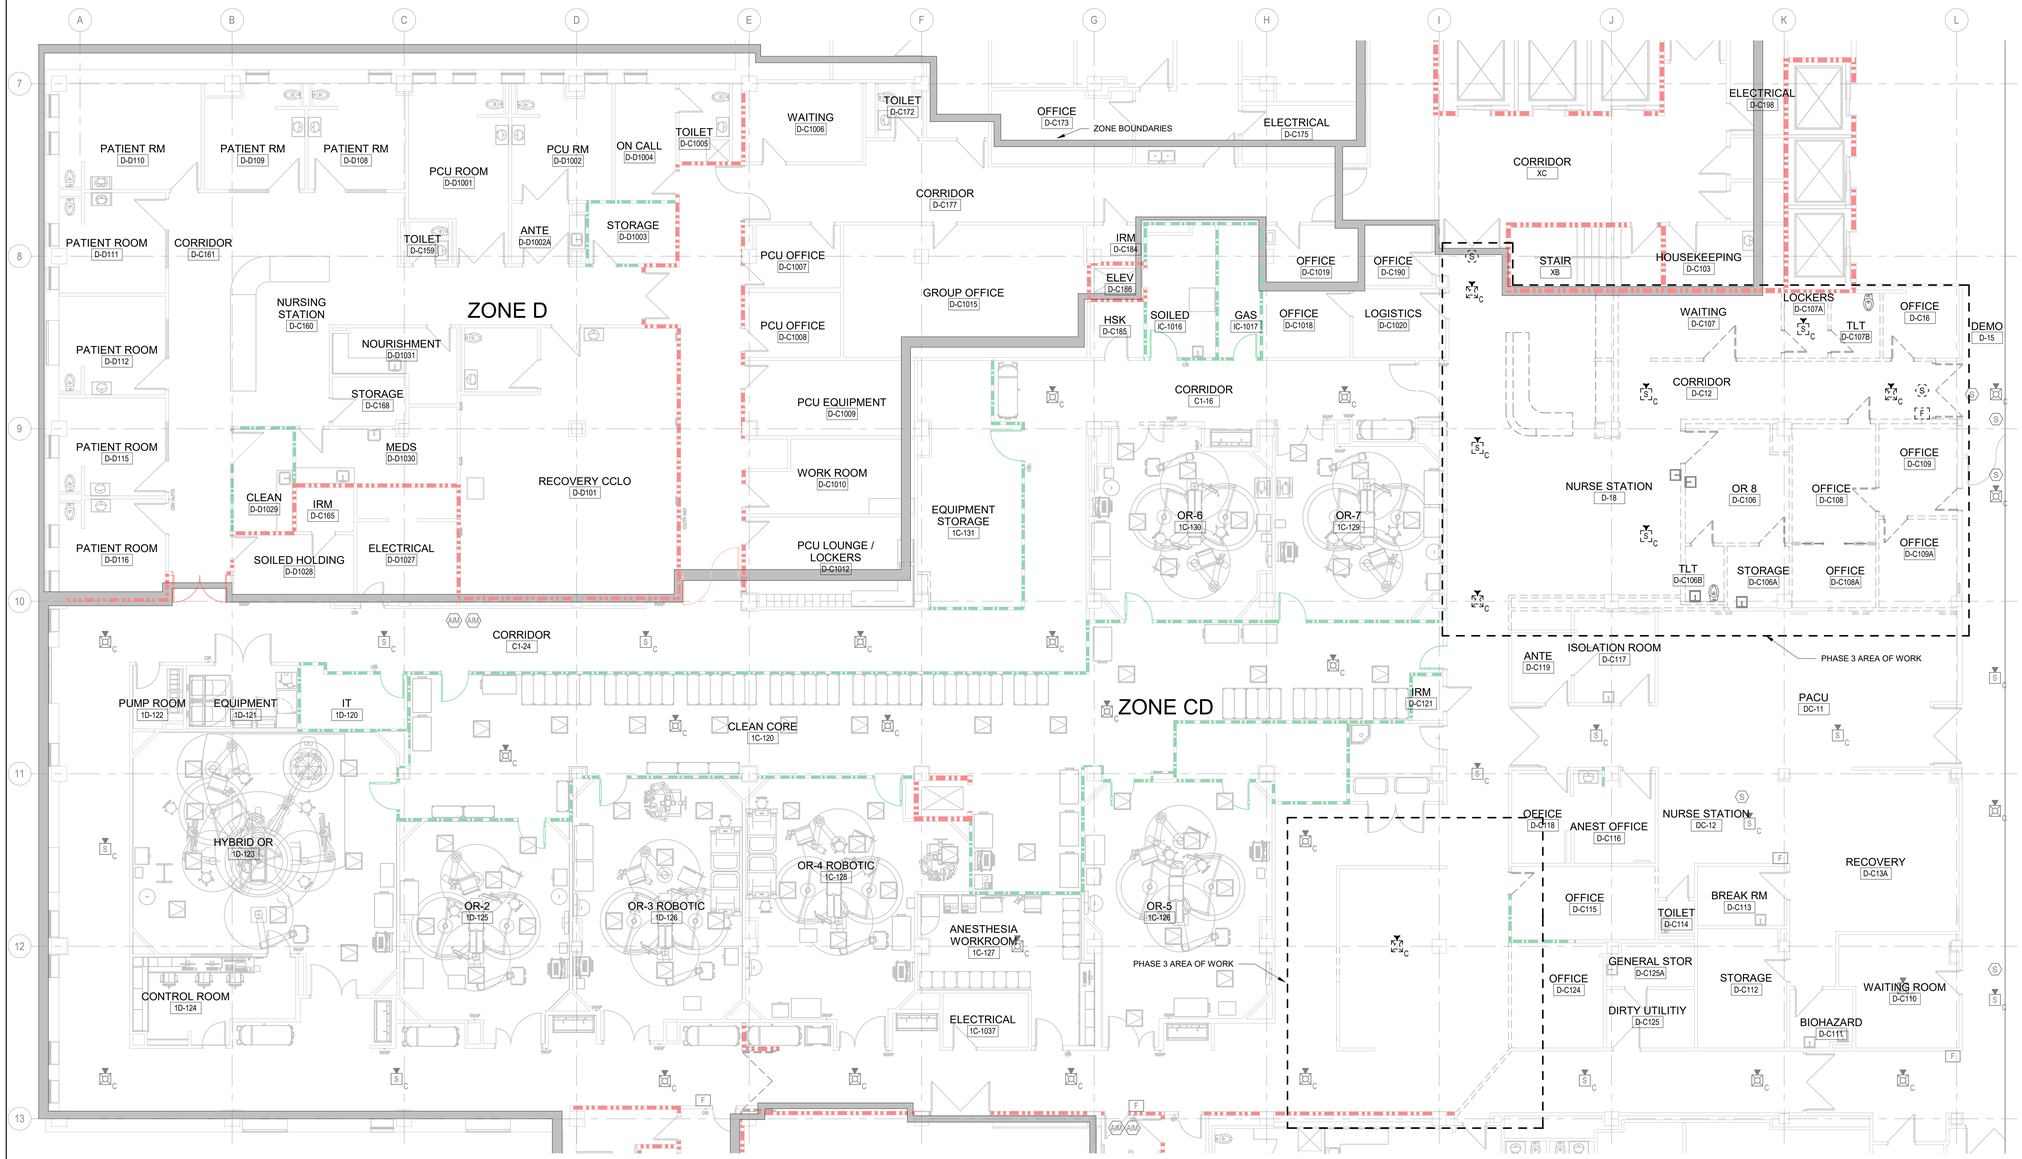

FIRST FLOOR FIRE ALARM DEMOLITION PLAN - PHASE 3

F1 1/8" = 1'-0"

GENERAL NOTES

1. DISCONNECT AND REMOVE EXISTING FIRE ALARM DEVICES INSIDE THE AREA OF WORK. REMOVE FIRE ALARM CABLING BACK TO NEXT DEVICE ON FIRE ALARM CIRCUIT THAT IS INDICATED AS EXISTING TO REMAIN, OR LOCATED OUTSIDE THE AREA OF DEMOLITION. IF NO OTHER DEVICES REMAIN ON FIRE ALARM CIRCUIT, REMOVE CABLE BACK TO SIMPLEX 4100U FIRE ALARM PANEL LOCATED IN THE ENGINEERING CONTROL ROOM BD-124 ON THE BASEMENT LEVEL.
2. CONTRACTOR SHALL COORDINATE WITH THE COR AND VA PERSONNEL PRIOR TO ANY WORK ON THE EXISTING FIRE ALARM SYSTEM.
3. EXISTING SMOKE ZONE BOUNDARIES SHOWN ARE BASED ON RECORD DOCUMENTATION AND GENERAL INFORMATION DRAWINGS. CONTRACTOR SHALL COORDINATE WITH THE COR AND VA PERSONNEL IF ANY DISCREPANCIES ARE DISCOVERED IN THE FIELD.
4. REFER TO GENERAL INFORMATION DRAWINGS FOR CONSTRUCTION PHASING INFORMATION.

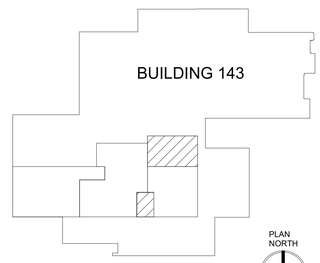

KEYPLAN

PRINTS OF THIS DRAWING SHALL NOT BE USED FOR ANY PURPOSE WHATSOEVER WITHOUT THE SEAL AND SIGNATURE OF THE PROFESSIONAL ENGINEER

Revisions: | Date:

CONSULTANT

Architecture:	Civil Engineering:	Fire & Life Safety:
PF&A DESIGN, P.C.	LABELLA ASSOCIATES	STANTON ENGINEERING SERVICES, LLC

ENGINEER OF RECORD

MILLER•REMICK
A Service-Disabled Veteran-Owned Small Business
(856) 429-4000 • Miller-Remick.com
M-R PROJECT NO. 0499-0136

STANTON ENGINEERING SERVICES PROFESSIONAL ENGINEER

PATRICK KENNETH JOHNSON STATE OF WASHINGTON 20019 REGISTERED PROFESSIONAL ENGINEER 12-30-2025

Office of Construction and Facilities Management

VA U.S. Department of Veterans Affairs

Drawing Title	FIRE ALARM DEMOLITION PLAN FIRST FLOOR PHASE 3
Approved by:	Jon Manninen, COR
Phase	BID DOCUMENTS
	FULLY SPRINKLERED
Project Title	RENOVATE SURGICAL SUITE PHASE II
Project Number	658-19-103
Location	SALEM VA MEDICAL CENTER
Issue Date	2025-12-30
Checked	PJ
Drawn	CA
VA Drawing Number	2617
Building Number	143
Drawing Number	P3-FD101

12/29/2025 4:47:30 PM

VA FORM 08 - 6231

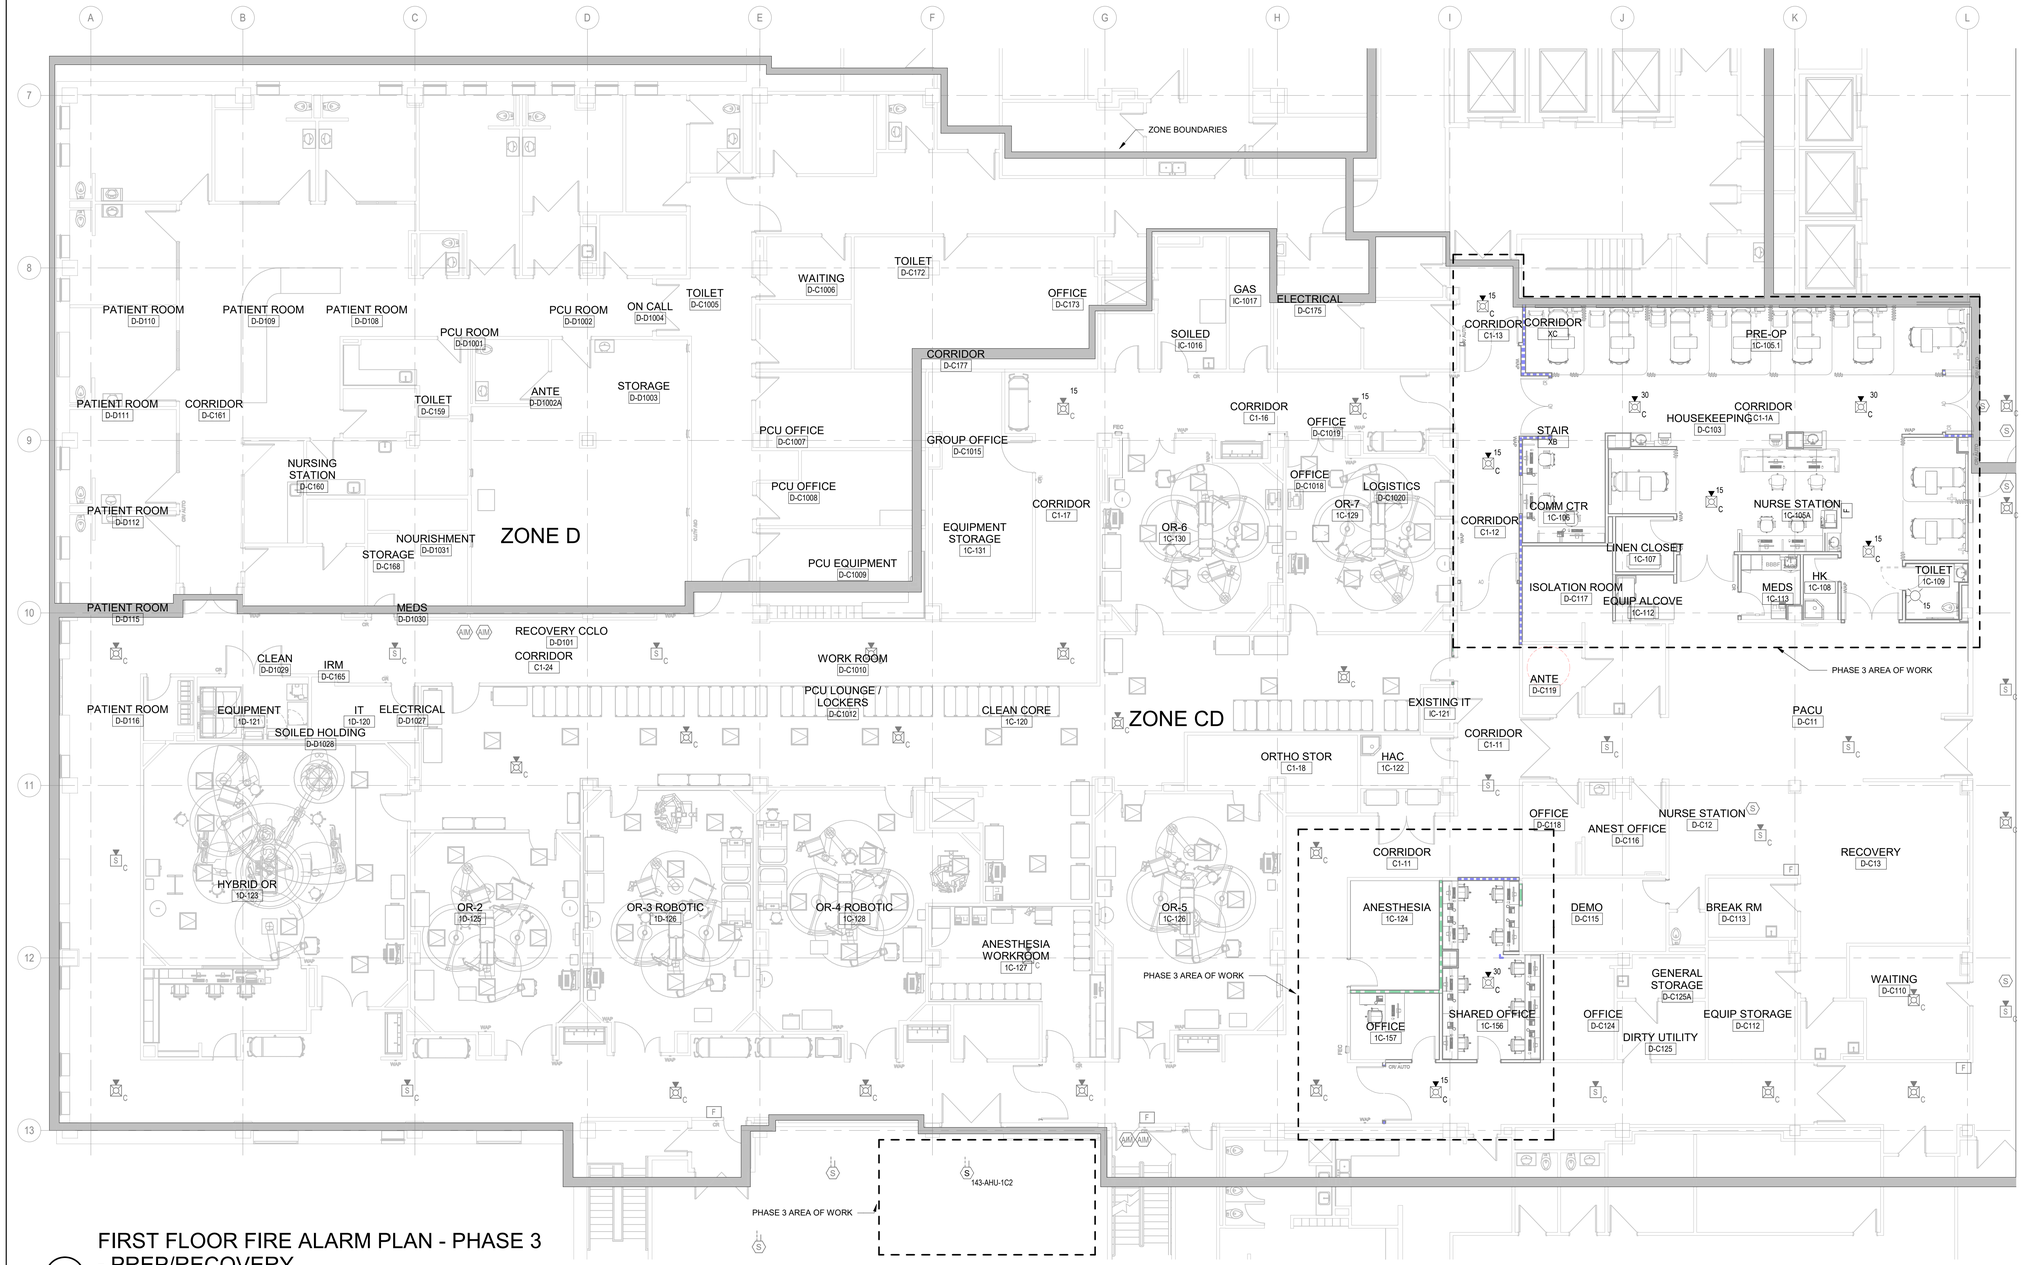

FIRST FLOOR FIRE ALARM PLAN - PHASE 3 - PREP/RECOVERY

F4 1/8" = 1'-0"

GENERAL NOTES

1. ALL NEW FIRE ALARM DEVICES MUST BE COMPATIBLE WITH THE BUILDING'S EXISTING SIMPLEX 4100U CONTROL PANEL LOCATED IN THE ENGINEERING CONTROL ROOM BD-124 ON THE BASEMENT LEVEL.
2. PROVIDE DUCT SMOKE DETECTOR FOR NEW MECHANICAL ROOM AIR HANDLING UNIT "143-RTU-1C2". PROVIDE DETECTOR SUPPLY AIR DUCTS IN ACCORDANCE WITH NFPA 90A. REFER TO AND COORDINATE WITH MECHANICAL DRAWINGS FOR EXACT LOCATIONS.
3. REFER TO GENERAL INFORMATION DRAWINGS FOR CONSTRUCTION PHASING INFORMATION.
4. ALL FIRE ALARM DEVICES, NEW AND EXISTING, SHALL BE PROGRAMMED TO MATCH THE NEW SMOKE ZONES AFTER EACH PHASE. THE NEW SMOKE ZONES BOUNDARIES SHOWN SHALL MATCH THE NEW SMOKE COMPARTMENTS SHOWN IN THE GENERAL INFORMATION DRAWINGS. ANY DISCREPANCIES SHALL BE COORDINATED WITH THE COR AND VA PERSONNEL.

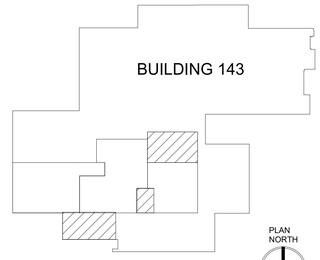

KEYPLAN

PRINTS OF THIS DRAWING SHALL NOT BE USED FOR ANY PURPOSE WHATSOEVER WITHOUT THE SEAL AND SIGNATURE OF THE PROFESSIONAL ENGINEER

Revisions: | Date:

CONSULTANT

Architecture:	Civil Engineering:	Fire & Life Safety:
PF&A DESIGN, P.C.	LABELLA ASSOCIATES	STANTON ENGINEERING SERVICES, LLC

ENGINEER OF RECORD

MILLER•REMICK
A Service-Disabled Veteran-Owned Small Business
(856) 429-4000 • Miller-Remick.com
M.R.PROJECT NO: 0499-2136

STANTON ENGINEERING SERVICES PROFESSIONAL ENGINEER

PATRICK KENNETH JOHNSON STATE OF WASHINGTON 20108 REGISTERED PROFESSIONAL ENGINEER
12-30-2025

Office of Construction and Facilities Management

VA U.S. Department of Veterans Affairs

Drawing Title	FIRE ALARM NEW WORK PLAN FIRST FLOOR PHASE 3
Approved by:	Jon Manninen, COR
Phase	BID DOCUMENTS
	FULLY SPRINKLERED
Project Title	RENOVATE SURGICAL SUITE PHASE II
Project Number	658-19-103
Location	SALEM VA MEDICAL CENTER
Issue Date	2025-12-30
Checked	PJ
Drawn	CA
VA Drawing Number	2617
Building Number	143
Drawing Number	P3-FA101

12/29/2025 4:47:25 PM

VA FORM 08 - 6231

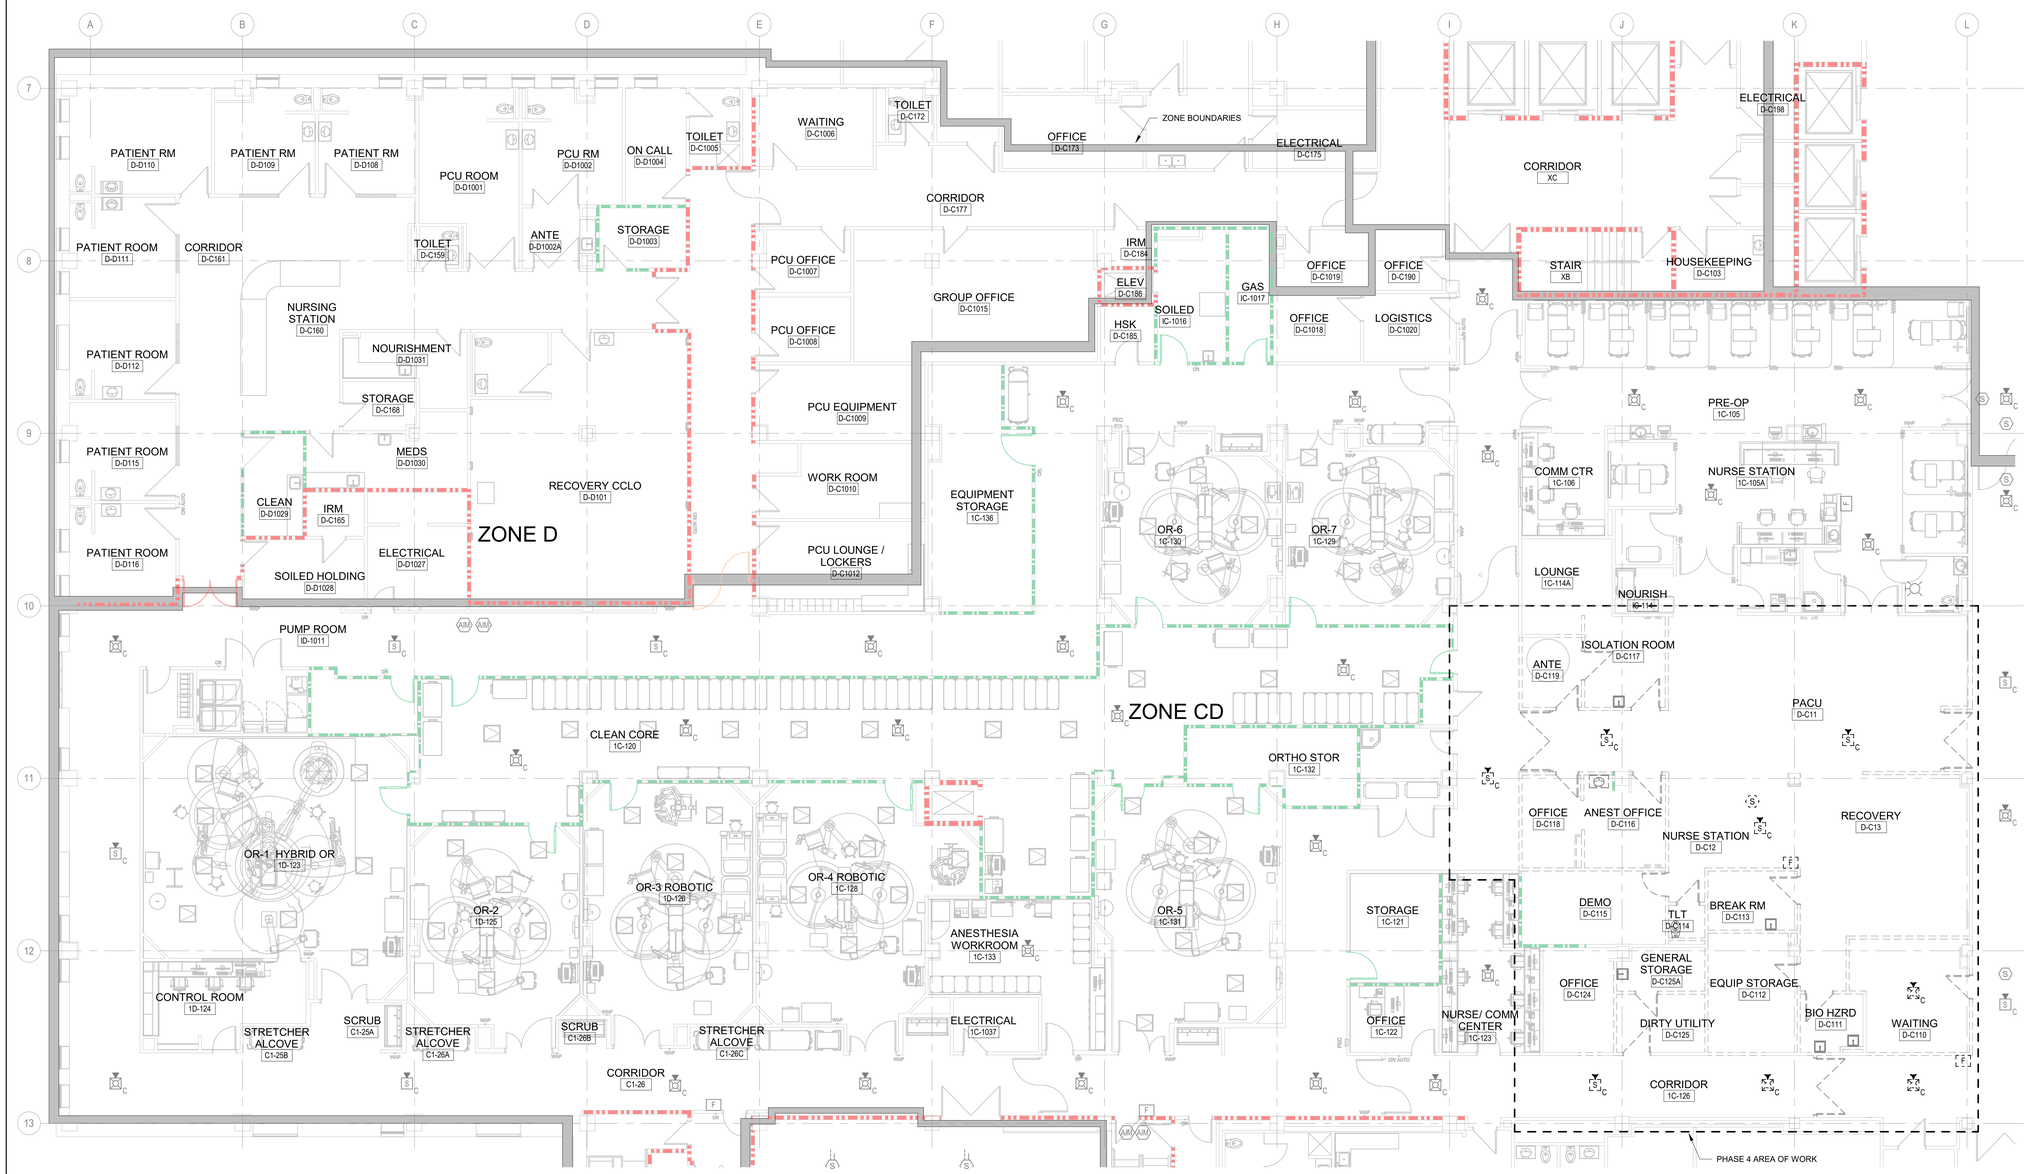

FIRST FLOOR FIRE ALARM DEMOLITION PLAN - PHASE 4

F1 1/8" = 1'-0"

GENERAL NOTES

1. DISCONNECT AND REMOVE EXISTING FIRE ALARM DEVICES INSIDE THE AREA OF WORK. REMOVE FIRE ALARM CABLING BACK TO NEXT DEVICE ON FIRE ALARM CIRCUIT THAT IS INDICATED AS EXISTING TO REMAIN, OR LOCATED OUTSIDE THE AREA OF DEMOLITION. IF NO OTHER DEVICES REMAIN ON FIRE ALARM CIRCUIT, REMOVE CABLE BACK TO SIMPLEX 4100U FIRE ALARM PANEL LOCATED IN THE ENGINEERING CONTROL ROOM BD-124 ON THE BASEMENT LEVEL.
2. CONTRACTOR SHALL COORDINATE WITH THE COR AND VA PERSONNEL PRIOR TO ANY WORK ON THE EXISTING FIRE ALARM SYSTEM.
3. EXISTING SMOKE ZONE BOUNDARIES SHOWN ARE BASED ON RECORD DOCUMENTATION AND GENERAL INFORMATION DRAWINGS. CONTRACTOR SHALL COORDINATE WITH THE COR AND VA PERSONNEL IF ANY DISCREPANCIES ARE DISCOVERED IN THE FIELD.
4. REFER TO GENERAL INFORMATION DRAWINGS FOR CONSTRUCTION PHASING INFORMATION.

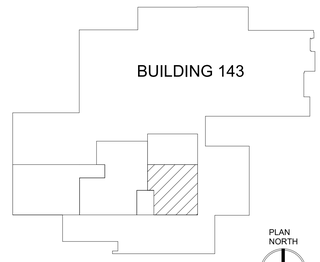

KEYPLAN

PRINTS OF THIS DRAWING SHALL NOT BE USED FOR ANY PURPOSE WHATSOEVER WITHOUT THE SEAL AND SIGNATURE OF THE PROFESSIONAL ENGINEER

Revisions: | Date:

CONSULTANT

Architecture:	Civil Engineering:	Fire & Life Safety:
PF&A DESIGN, P.C.	LABELLA ASSOCIATES	STANTON ENGINEERING SERVICES, LLC

ENGINEER OF RECORD

MILLER•REMICK
A Service-Disabled Veteran-Owned Small Business
(856) 429-4000 • Miller-Remick.com
M-R PROJECT NO. 0569-2136

STANTON ENGINEERING SERVICES PROFESSIONAL ENGINEER

PATRICK KENNETH STANTON — STATE OF WASHINGTON — REGISTERED PROFESSIONAL ENGINEER
12-30-2025

Office of Construction and Facilities Management

VA U.S. Department of Veterans Affairs

Drawing Title	FIRE ALARM DEMOLITION PLAN FIRST FLOOR PHASE 4
Approved by:	Jon Manninen, COR
Phase	BID DOCUMENTS
	FULLY SPRINKLERED
Project Title	RENOVATE SURGICAL SUITE PHASE II
Project Number	658-19-103
Location	SALEM VA MEDICAL CENTER
Issue Date	2025-12-30
Checked	PJ
Drawn	CA
VA Drawing Number	2617
Building Number	143
Drawing Number	P4-FD101

12/29/2025 4:47:55 PM

VA FORM 08 - 6231

GENERAL NOTES

1. ALL NEW FIRE ALARM DEVICES MUST BE COMPATIBLE WITH THE BUILDING'S EXISTING SIMPLEX 4100U CONTROL PANEL LOCATED IN THE ENGINEERING CONTROL ROOM BD-124 ON THE BASEMENT LEVEL.
2. REFER TO GENERAL INFORMATION DRAWINGS FOR CONSTRUCTION PHASING INFORMATION.
3. ALL FIRE ALARM DEVICES, NEW AND EXISTING, SHALL BE PROGRAMMED TO MATCH THE NEW SMOKE ZONES AFTER EACH PHASE. THE NEW SMOKE ZONES BOUNDARIES SHOWN SHALL MATCH THE NEW SMOKE COMPARTMENTS SHOWN IN THE GENERAL INFORMATION DRAWINGS. ANY DISCREPANCIES SHALL BE COORDINATED WITH THE COR AND VA PERSONNEL.

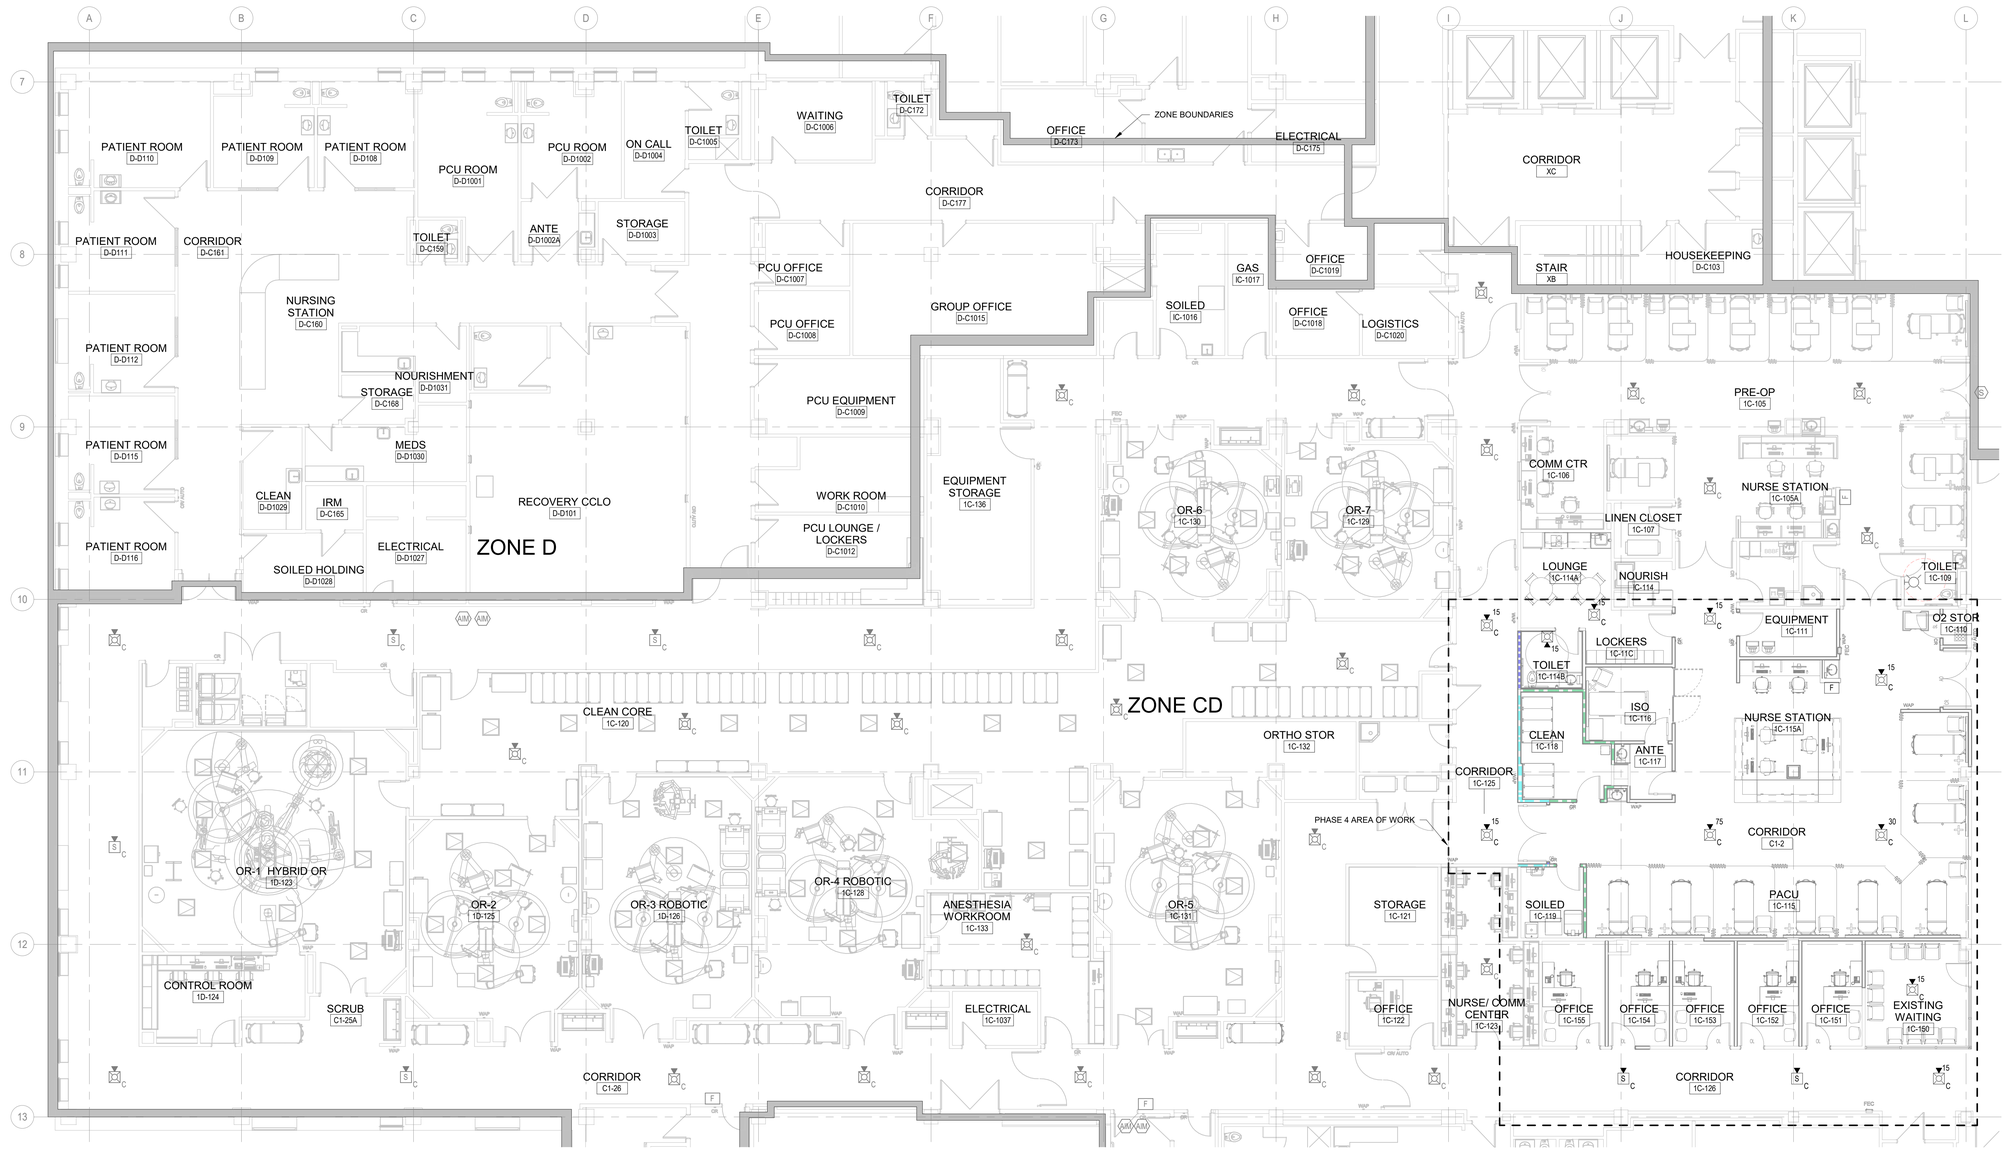

F1 FIRST FLOOR FIRE ALARM PLAN - PHASE 4

1/8" = 1'-0"

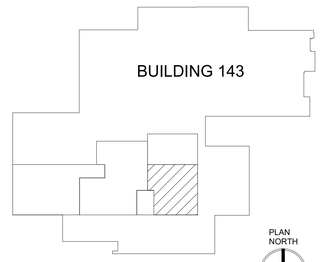

KEYPLAN

PRINTS OF THIS DRAWING SHALL NOT BE USED FOR ANY PURPOSE WHATSOEVER WITHOUT THE SEAL AND SIGNATURE OF THE PROFESSIONAL ENGINEER

Revisions: | Date:

CONSULTANT

Architecture:	Civil Engineering:	Fire & Life Safety:
PF&A DESIGN, P.C.	LABELLA ASSOCIATES	STANTON ENGINEERING SERVICES, LLC

ENGINEER OF RECORD

MILLER•REMICK
A Service-Disabled Veteran-Owned Small Business
(856) 429-6000 • Miller-Remick.com
M-R PROJECT NO: 0499-2136

STANTON ENGINEERING SERVICES PROFESSIONAL ENGINEER

PATRICK KENNETH JOHNSON STATE OF WASHINGTON 20018705 REGISTERED PROFESSIONAL ENGINEER
12-30-2025

Office of Construction and Facilities Management

VA U.S. Department of Veterans Affairs

Drawing Title	FIRE ALARM NEW WORK PLAN FIRST FLOOR PHASE 4
Approved by:	Jon Manninen, COR
Phase	BID DOCUMENTS
	FULLY SPRINKLERED
Project Title	RENOVATE SURGICAL SUITE PHASE II
Project Number	658-19-103
Location	SALEM VA MEDICAL CENTER
Issue Date	2025-12-30
Checked	PJ
Drawn	CA
VA Drawing Number	2617
Building Number	143
Drawing Number	P4-FA101

12/29/2025 4:47:48 PM

VA FORM 08 - 6231

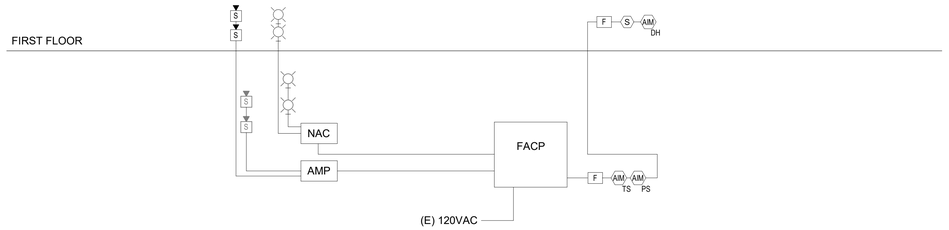

NOTE: FIRE ALARM DEVICES ARE SHOWN FOR DIAGRAMMATICAL PURPOSES ONLY AND SHALL NOT BE USED FOR QUANTIFYING NUMBER OF DEVICES. CONTRACTOR SHALL PROVIDE NEW CIRCUITS, CONDUIT, AND POWER PANELS AS NECESSARY FOR A COMPLETE, FUNCTIONAL SYSTEM.

C5 FIRE ALARM RISER DIAGRAM
NTS

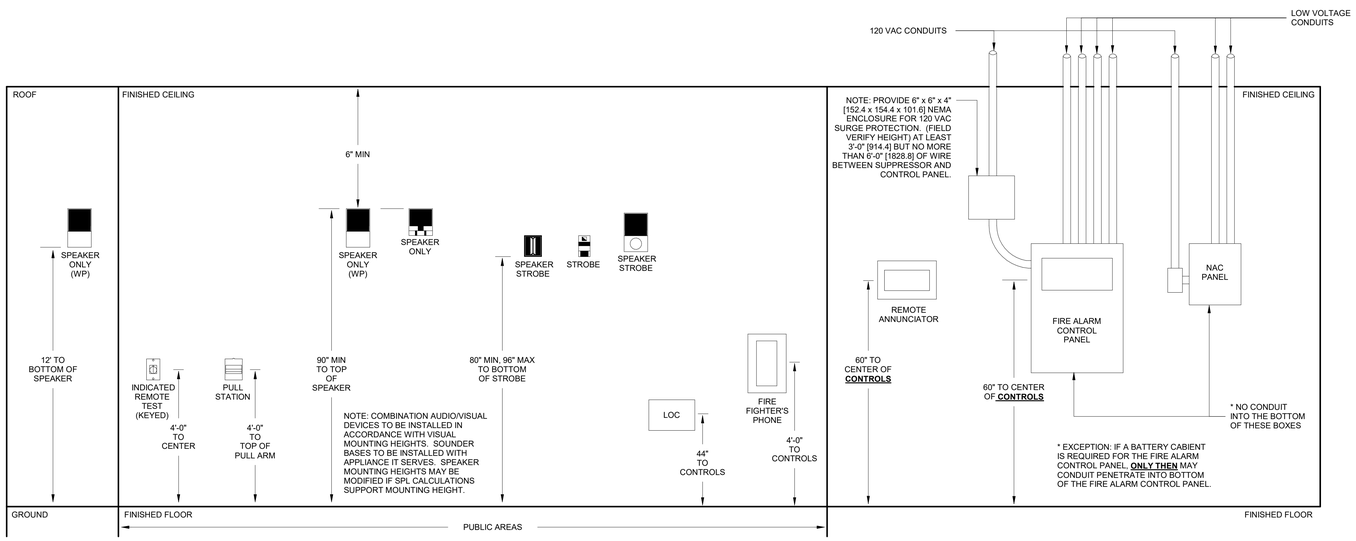

F5 FIRE ALARM WALL MOUNTING HEIGHT REQUIREMENTS
NTS

PRINTS OF THIS DRAWING SHALL NOT BE USED FOR ANY PURPOSE WHATSOEVER WITHOUT THE SEAL AND SIGNATURE OF THE PROFESSIONAL ENGINEER

Revisions:	Date:

CONSULTANT

Architecture:	Civil Engineering:	Fire & Life Safety:
PF&A DESIGN, P.C.	LABELLA ASSOCIATES	STANTON ENGINEERING SERVICES, LLC

ENGINEER OF RECORD

MILLER•REMICK
A Service-Disabled Veteran-Owned Small Business
(856) 429-4000 • Miller-Remick.com
M-R PROJECT NO. 0469-0136

STANTON ENGINEERING SERVICES PROFESSIONAL ENGINEER

PATRICK KENNETH JOHNSON STATE OF WASHINGTON 24019 REGISTERED PROFESSIONAL ENGINEER
12-30-2025

Office of Construction and Facilities Management

VA U.S. Department of Veterans Affairs

Drawing Title	FIRE ALARM DETAILS
Approved by:	Jon Manninen, COR
Phase	BID DOCUMENTS
	FULLY SPRINKLERED
Project Title	RENOVATE SURGICAL SUITE PHASE II
Project Number	658-19-103
Location	SALEM VA MEDICAL CENTER
Issue Date	2025-12-30
Checked	PJ
Drawn	CA
VA Drawing Number	2617
Building Number	143
Drawing Number	FA501

12/29/2025 4:46:28 PM

VA FORM 08 - 6231